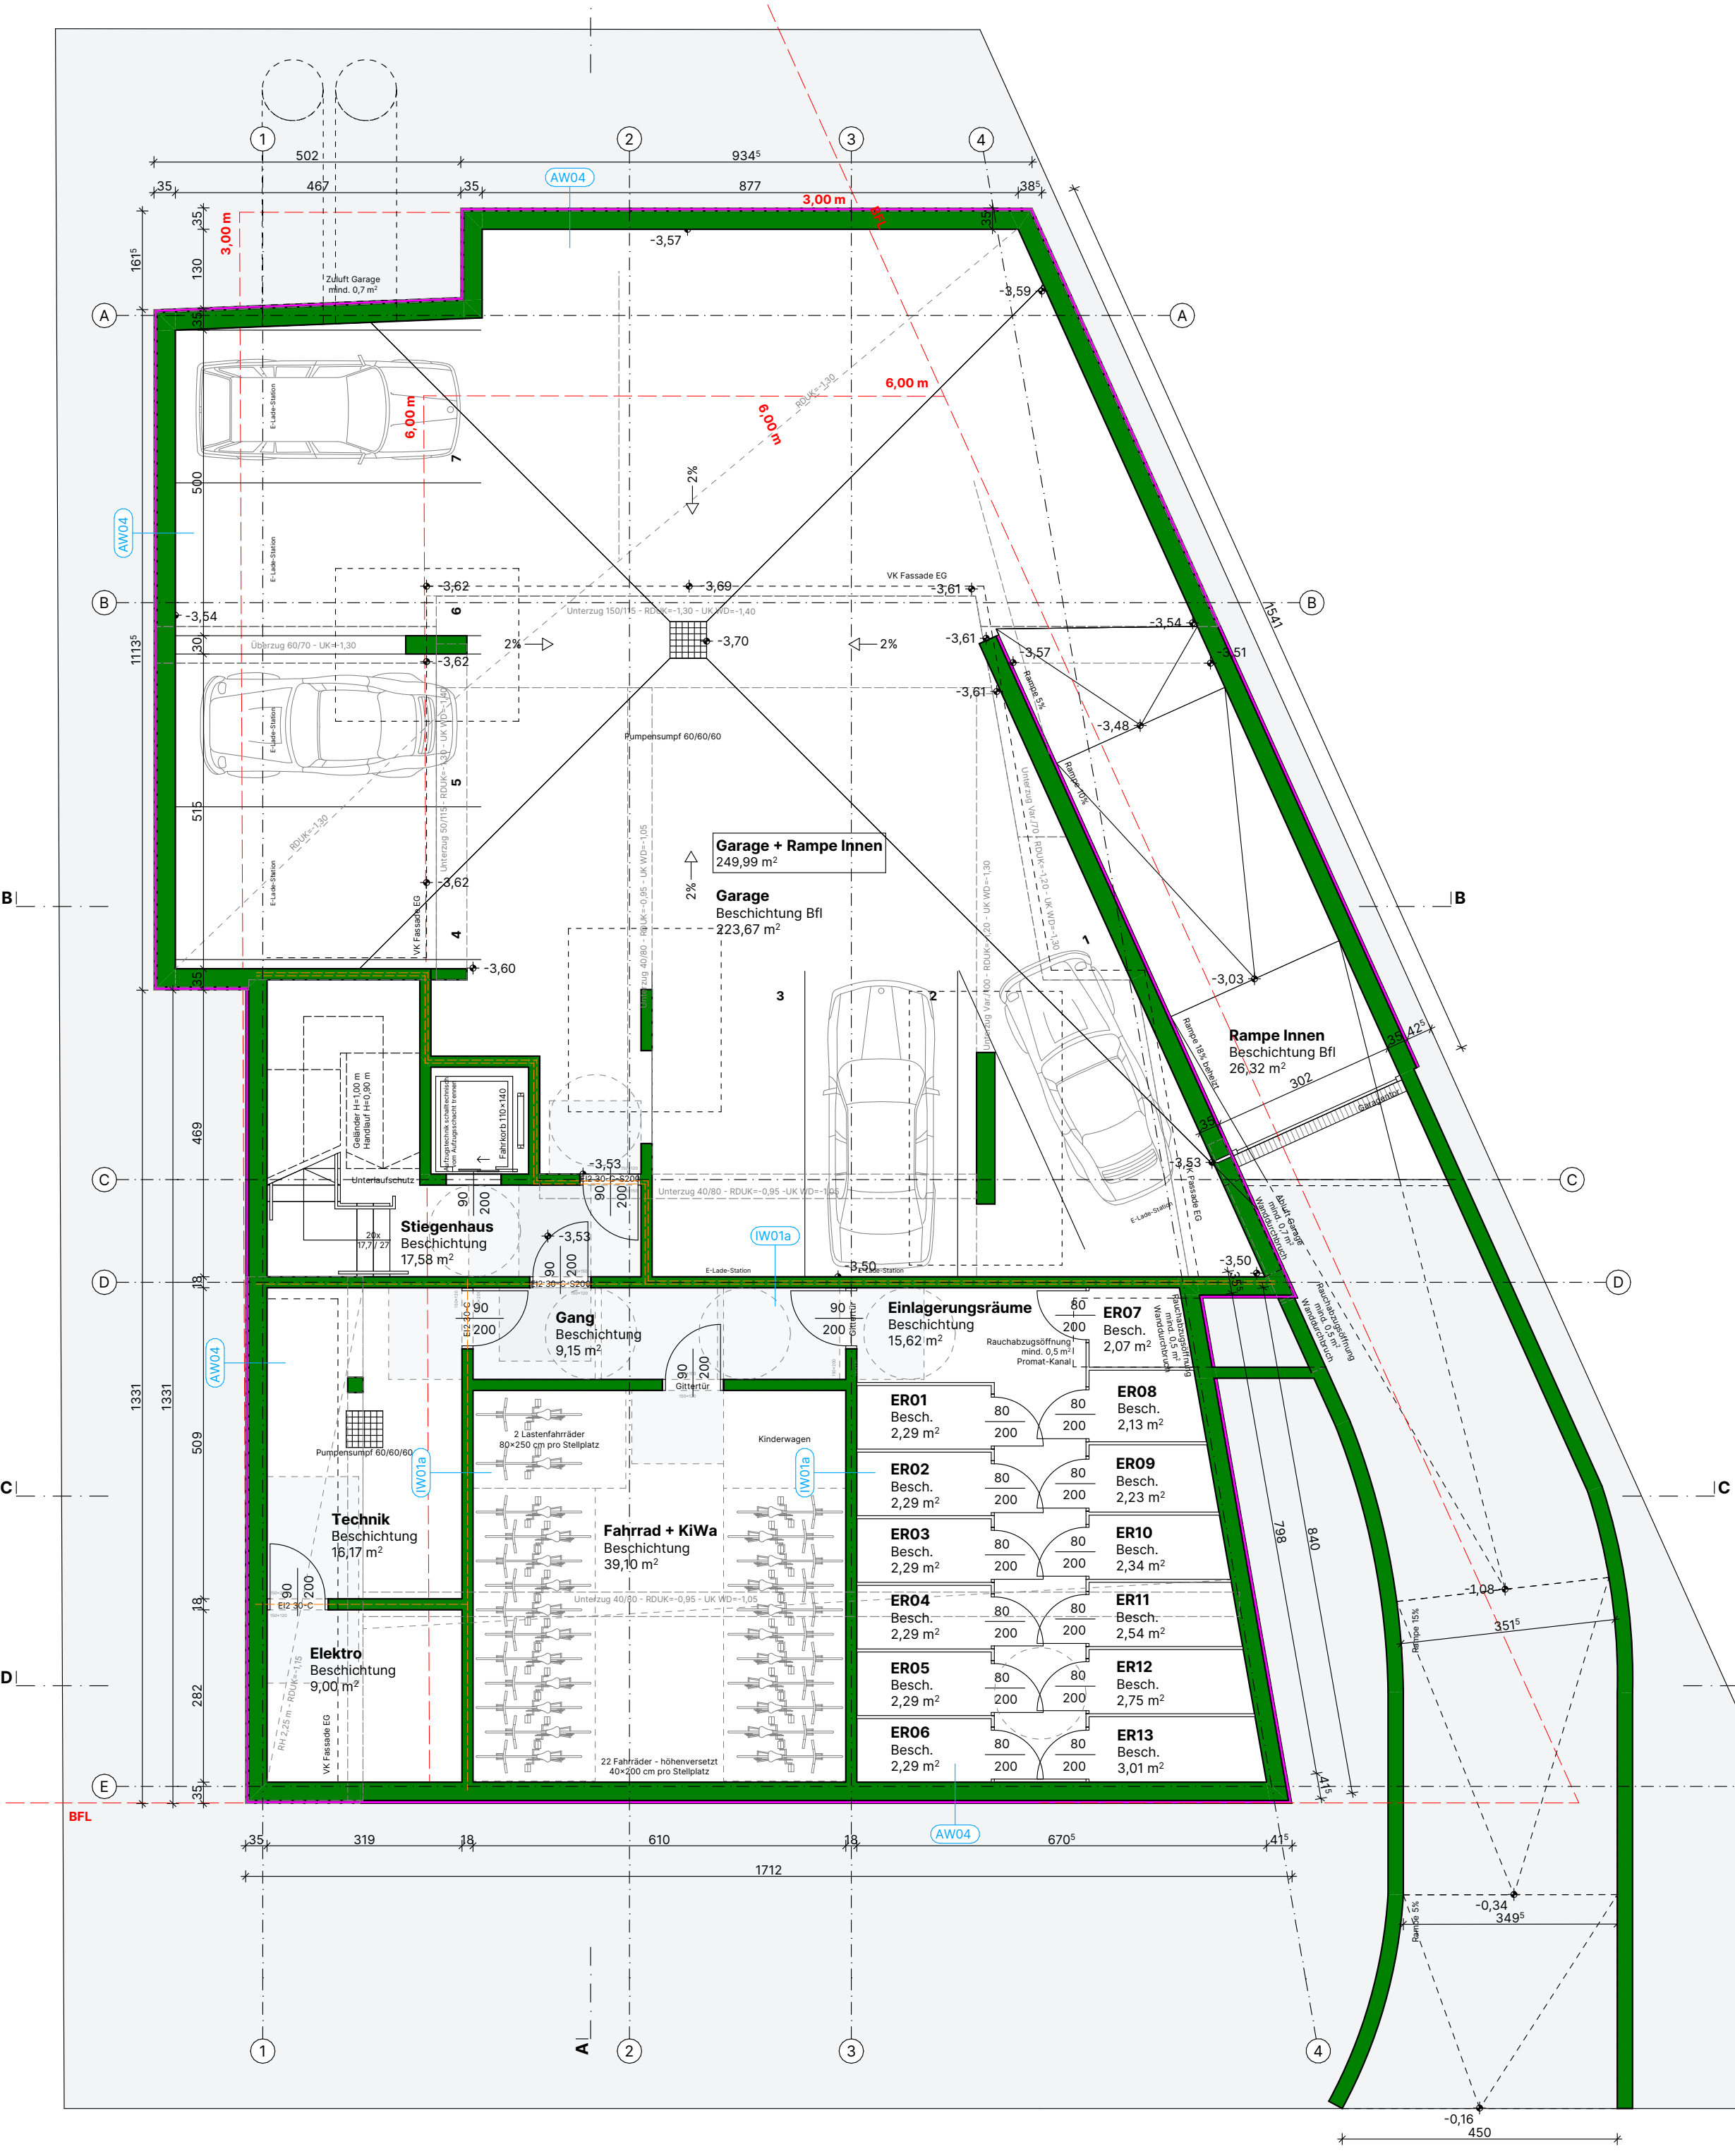

UNTERGESCHOSS M 1:100

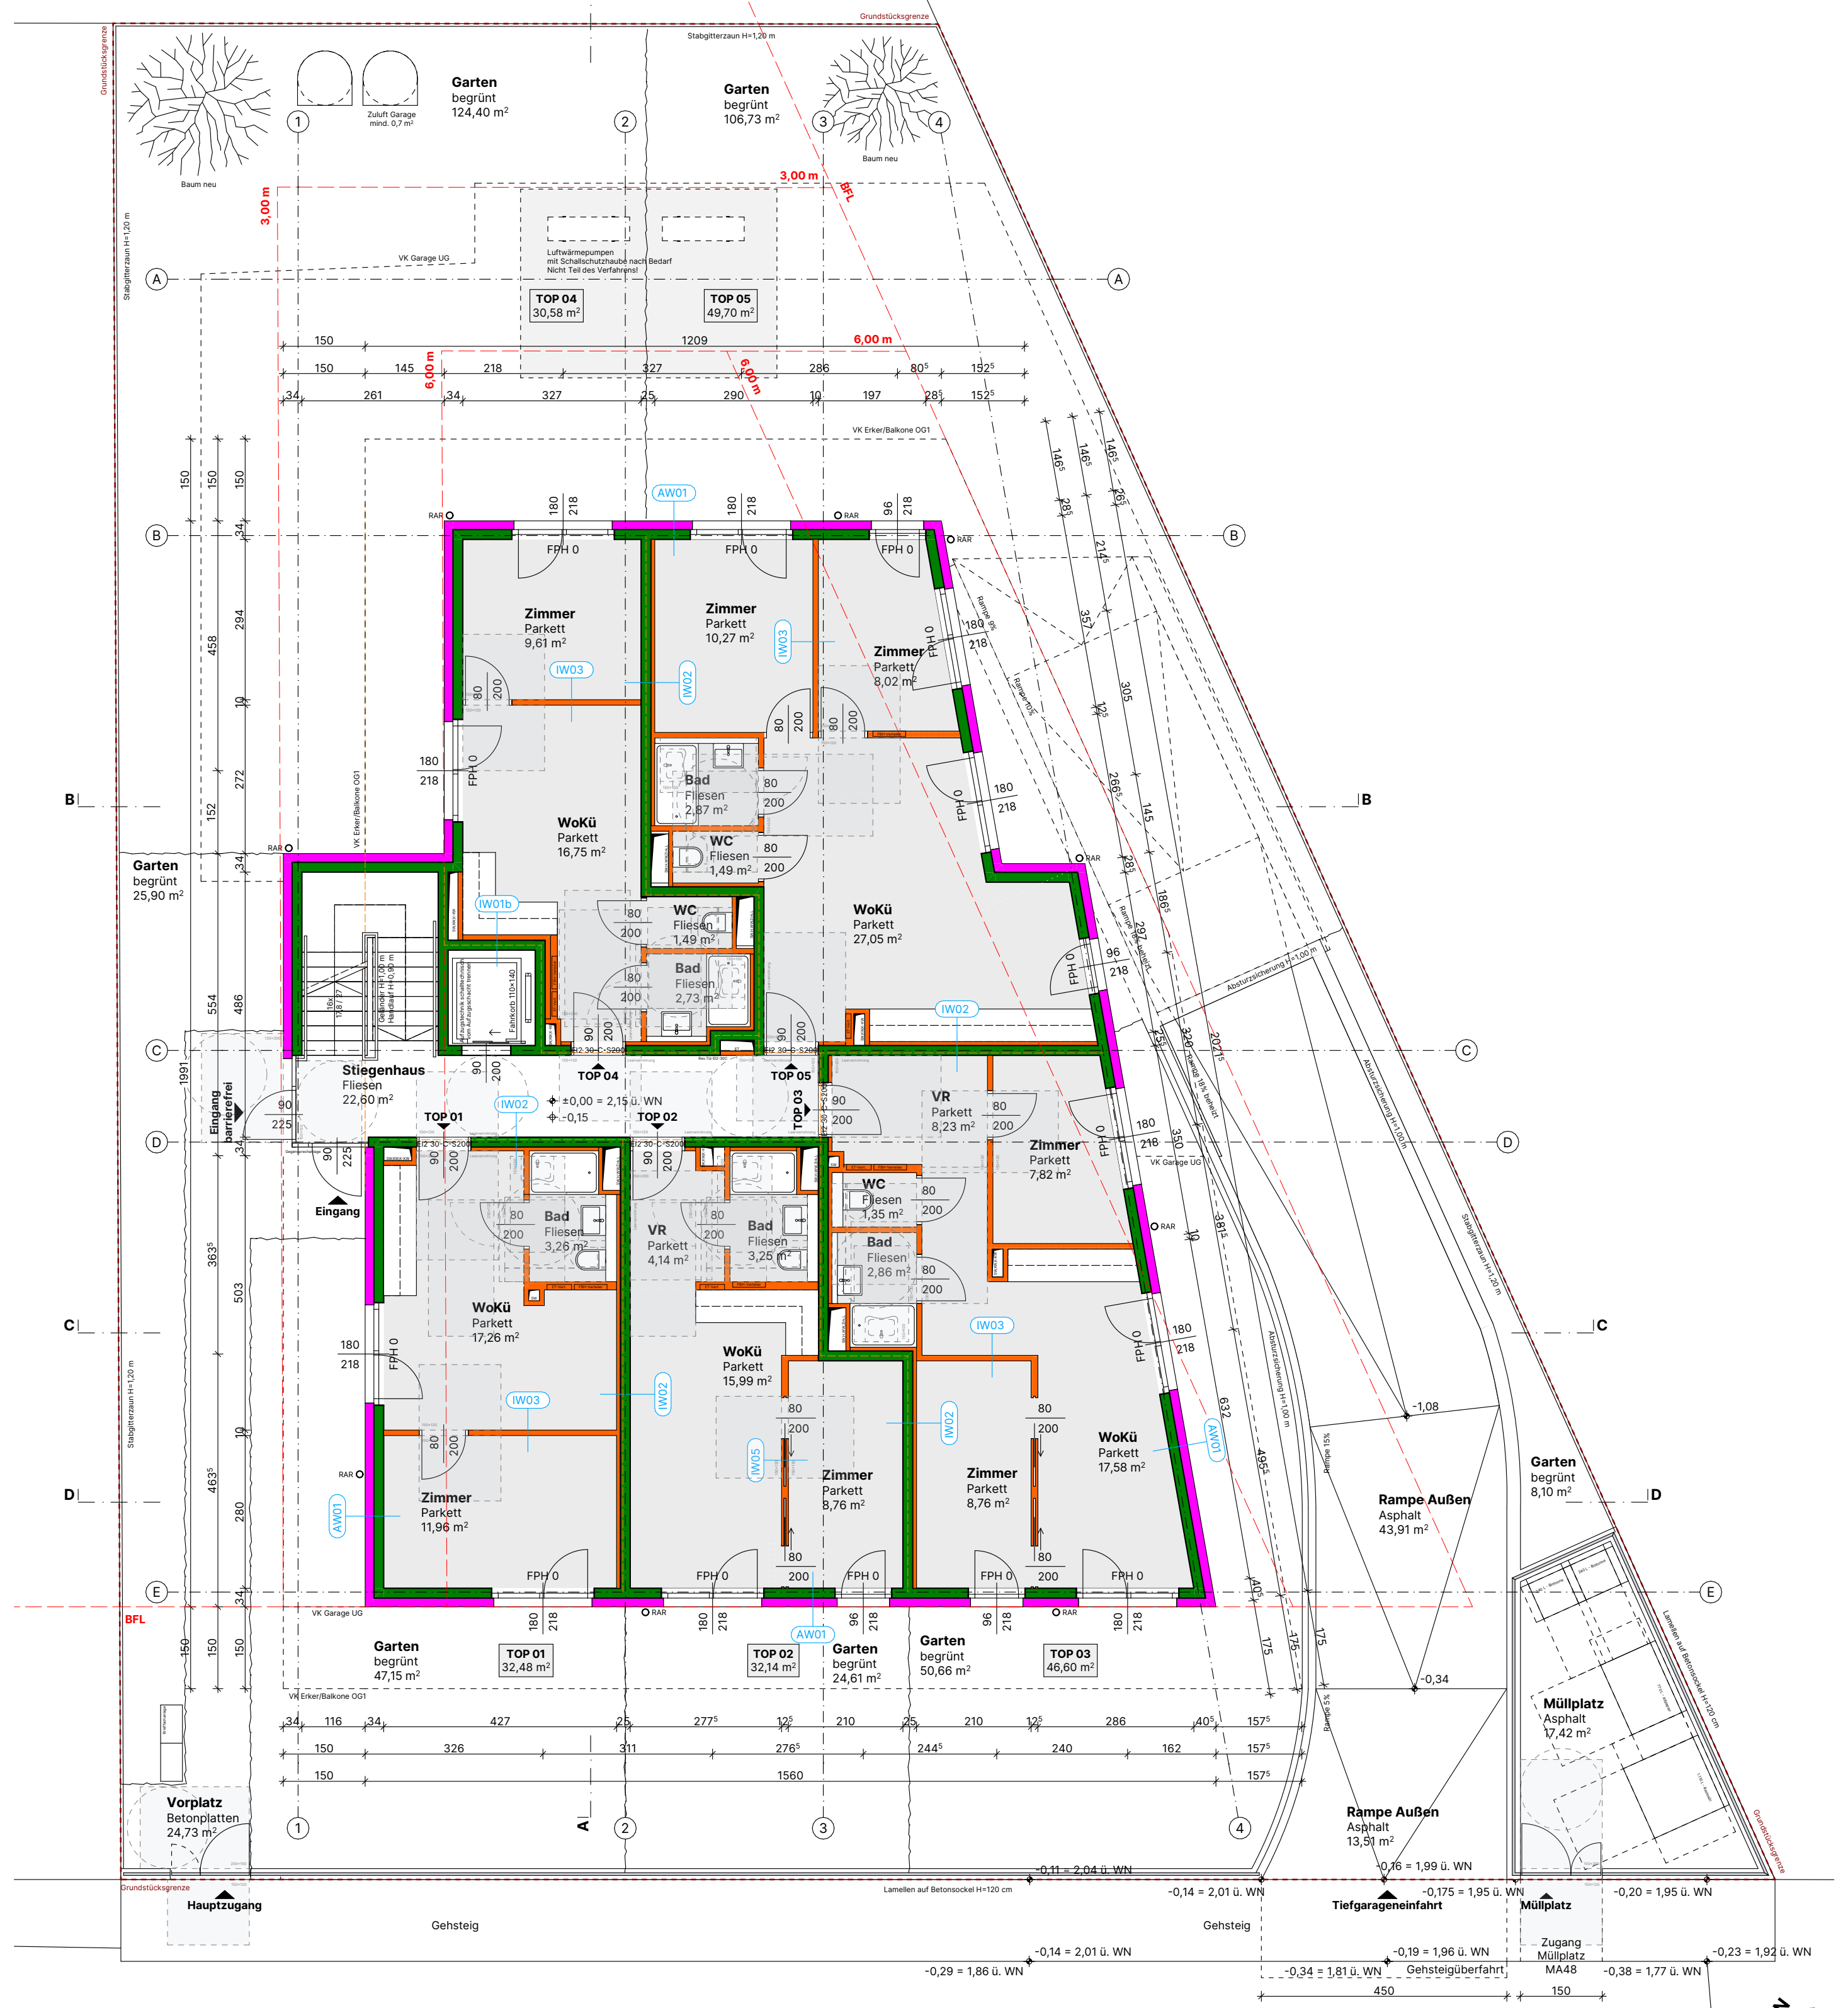

ERDGESCHOSS M 1:100

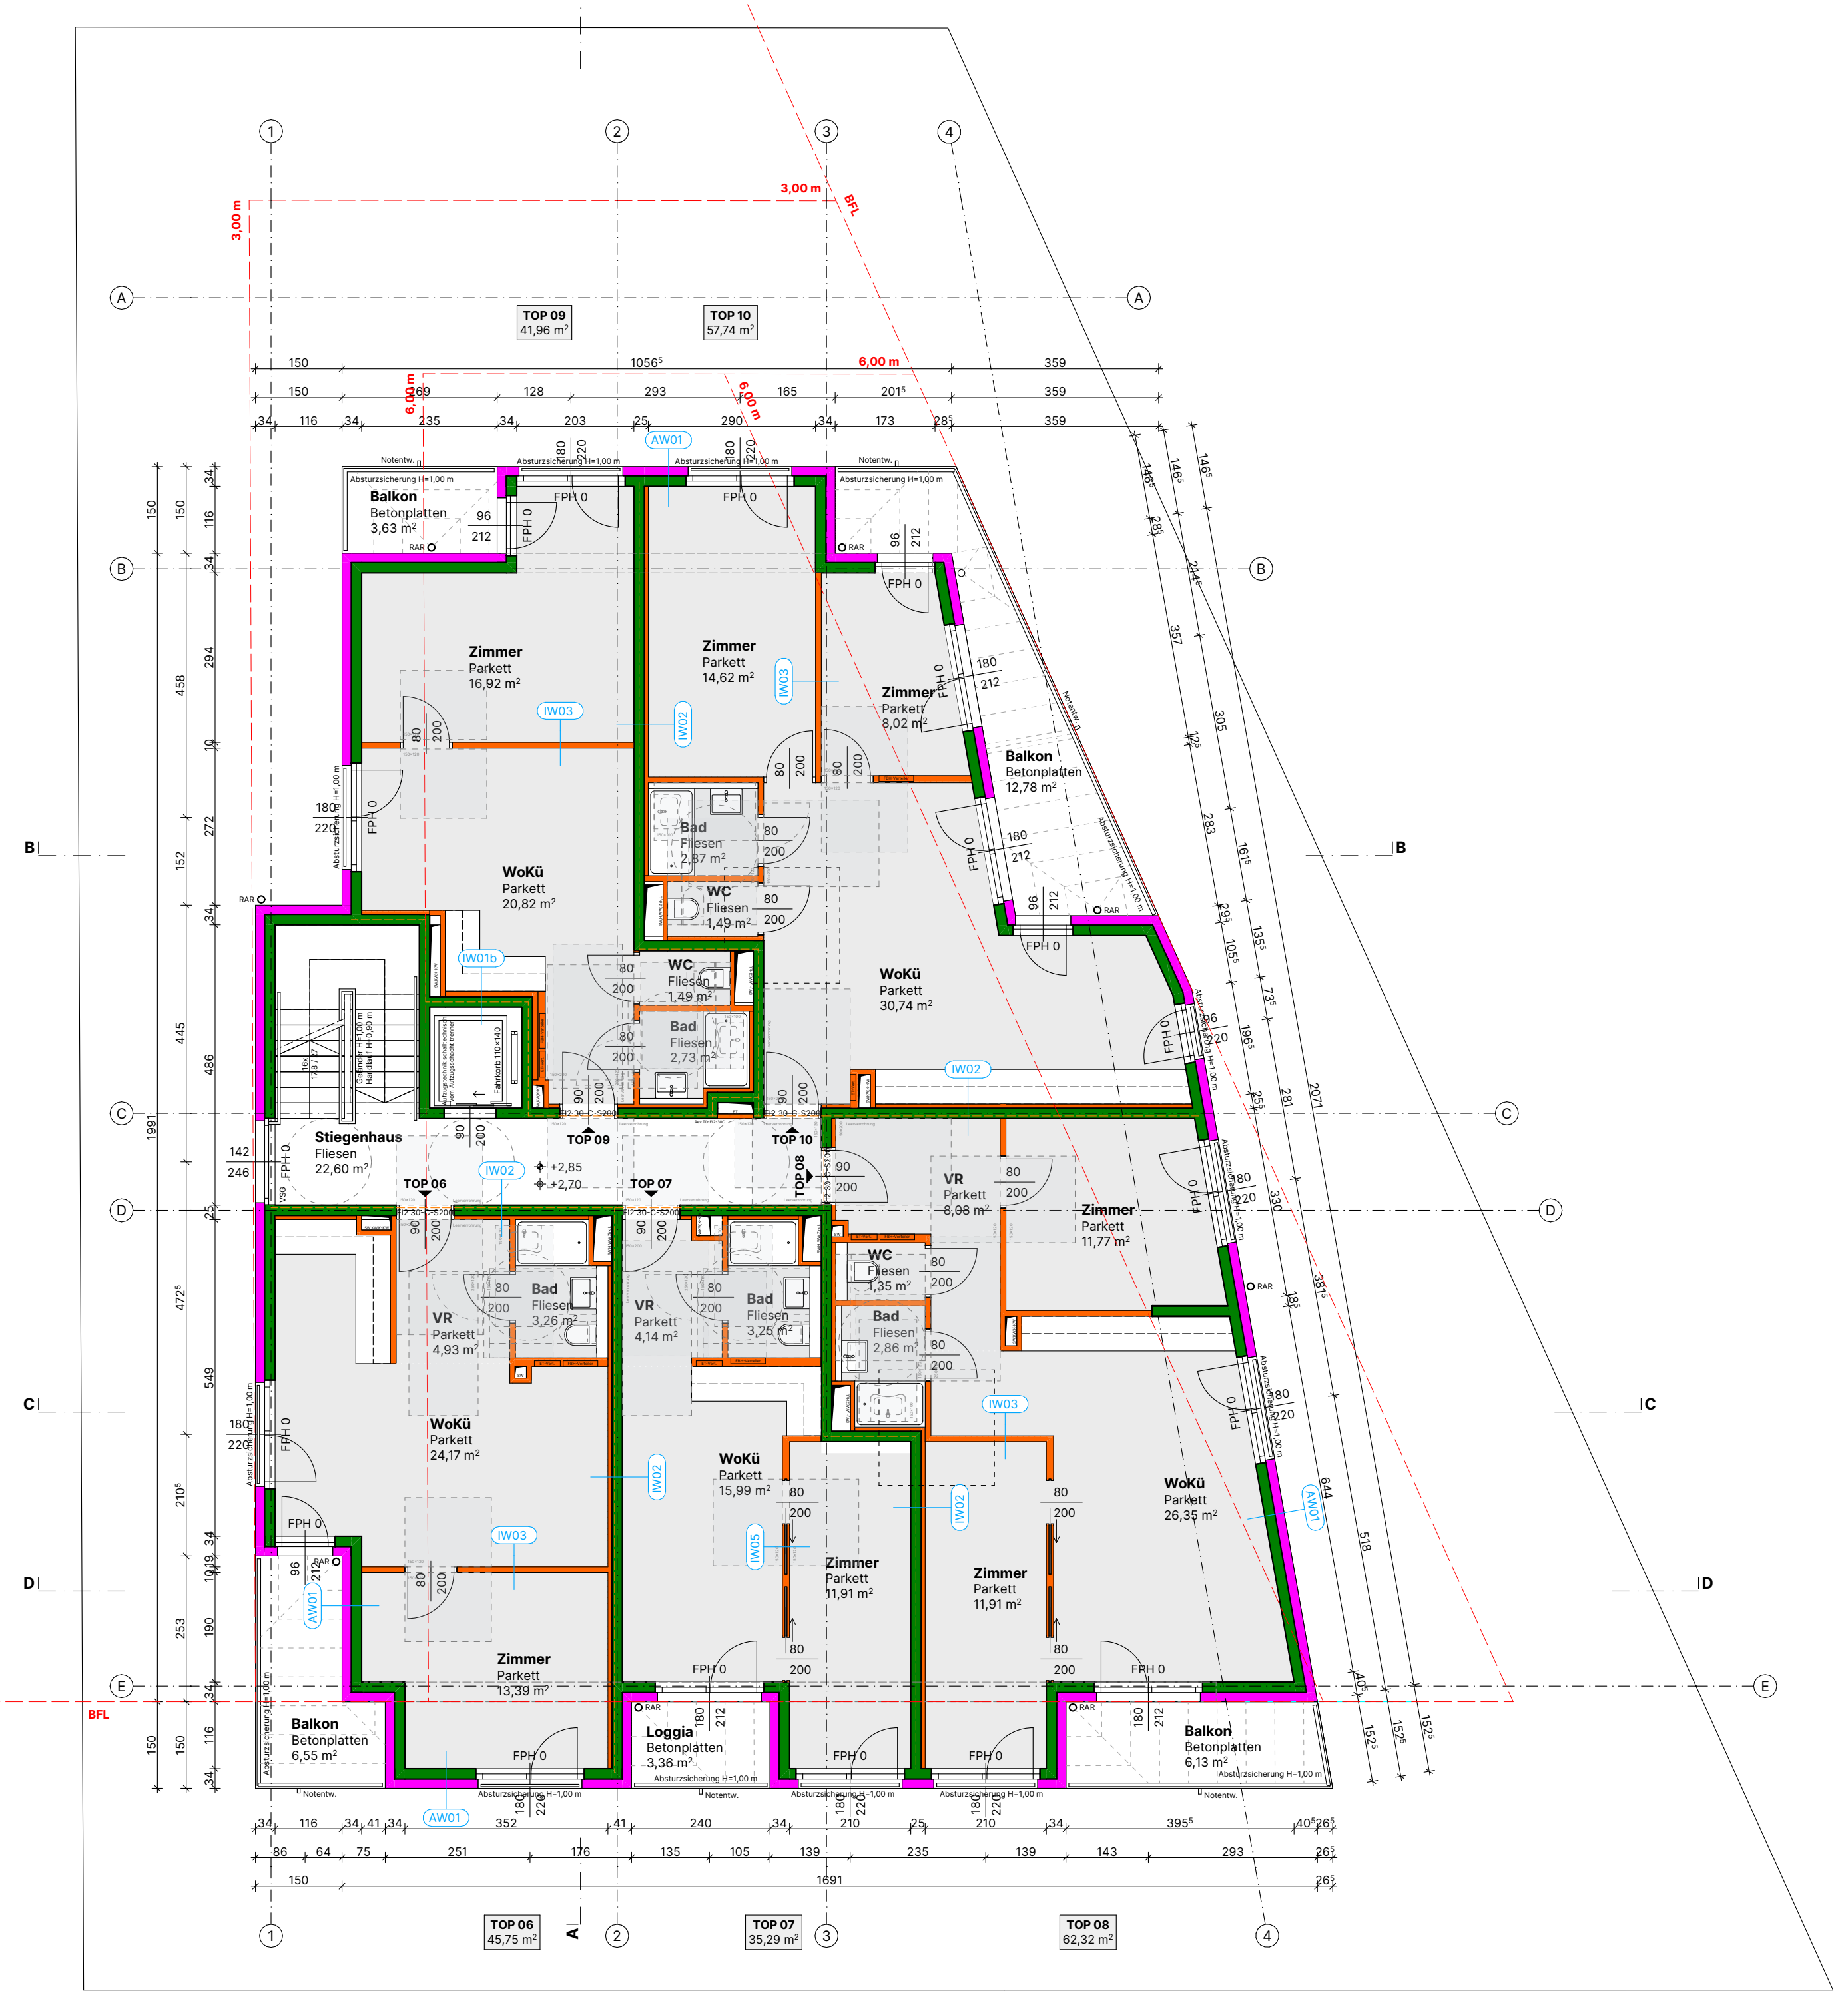

1. OBERGESCHOSS M 1:100

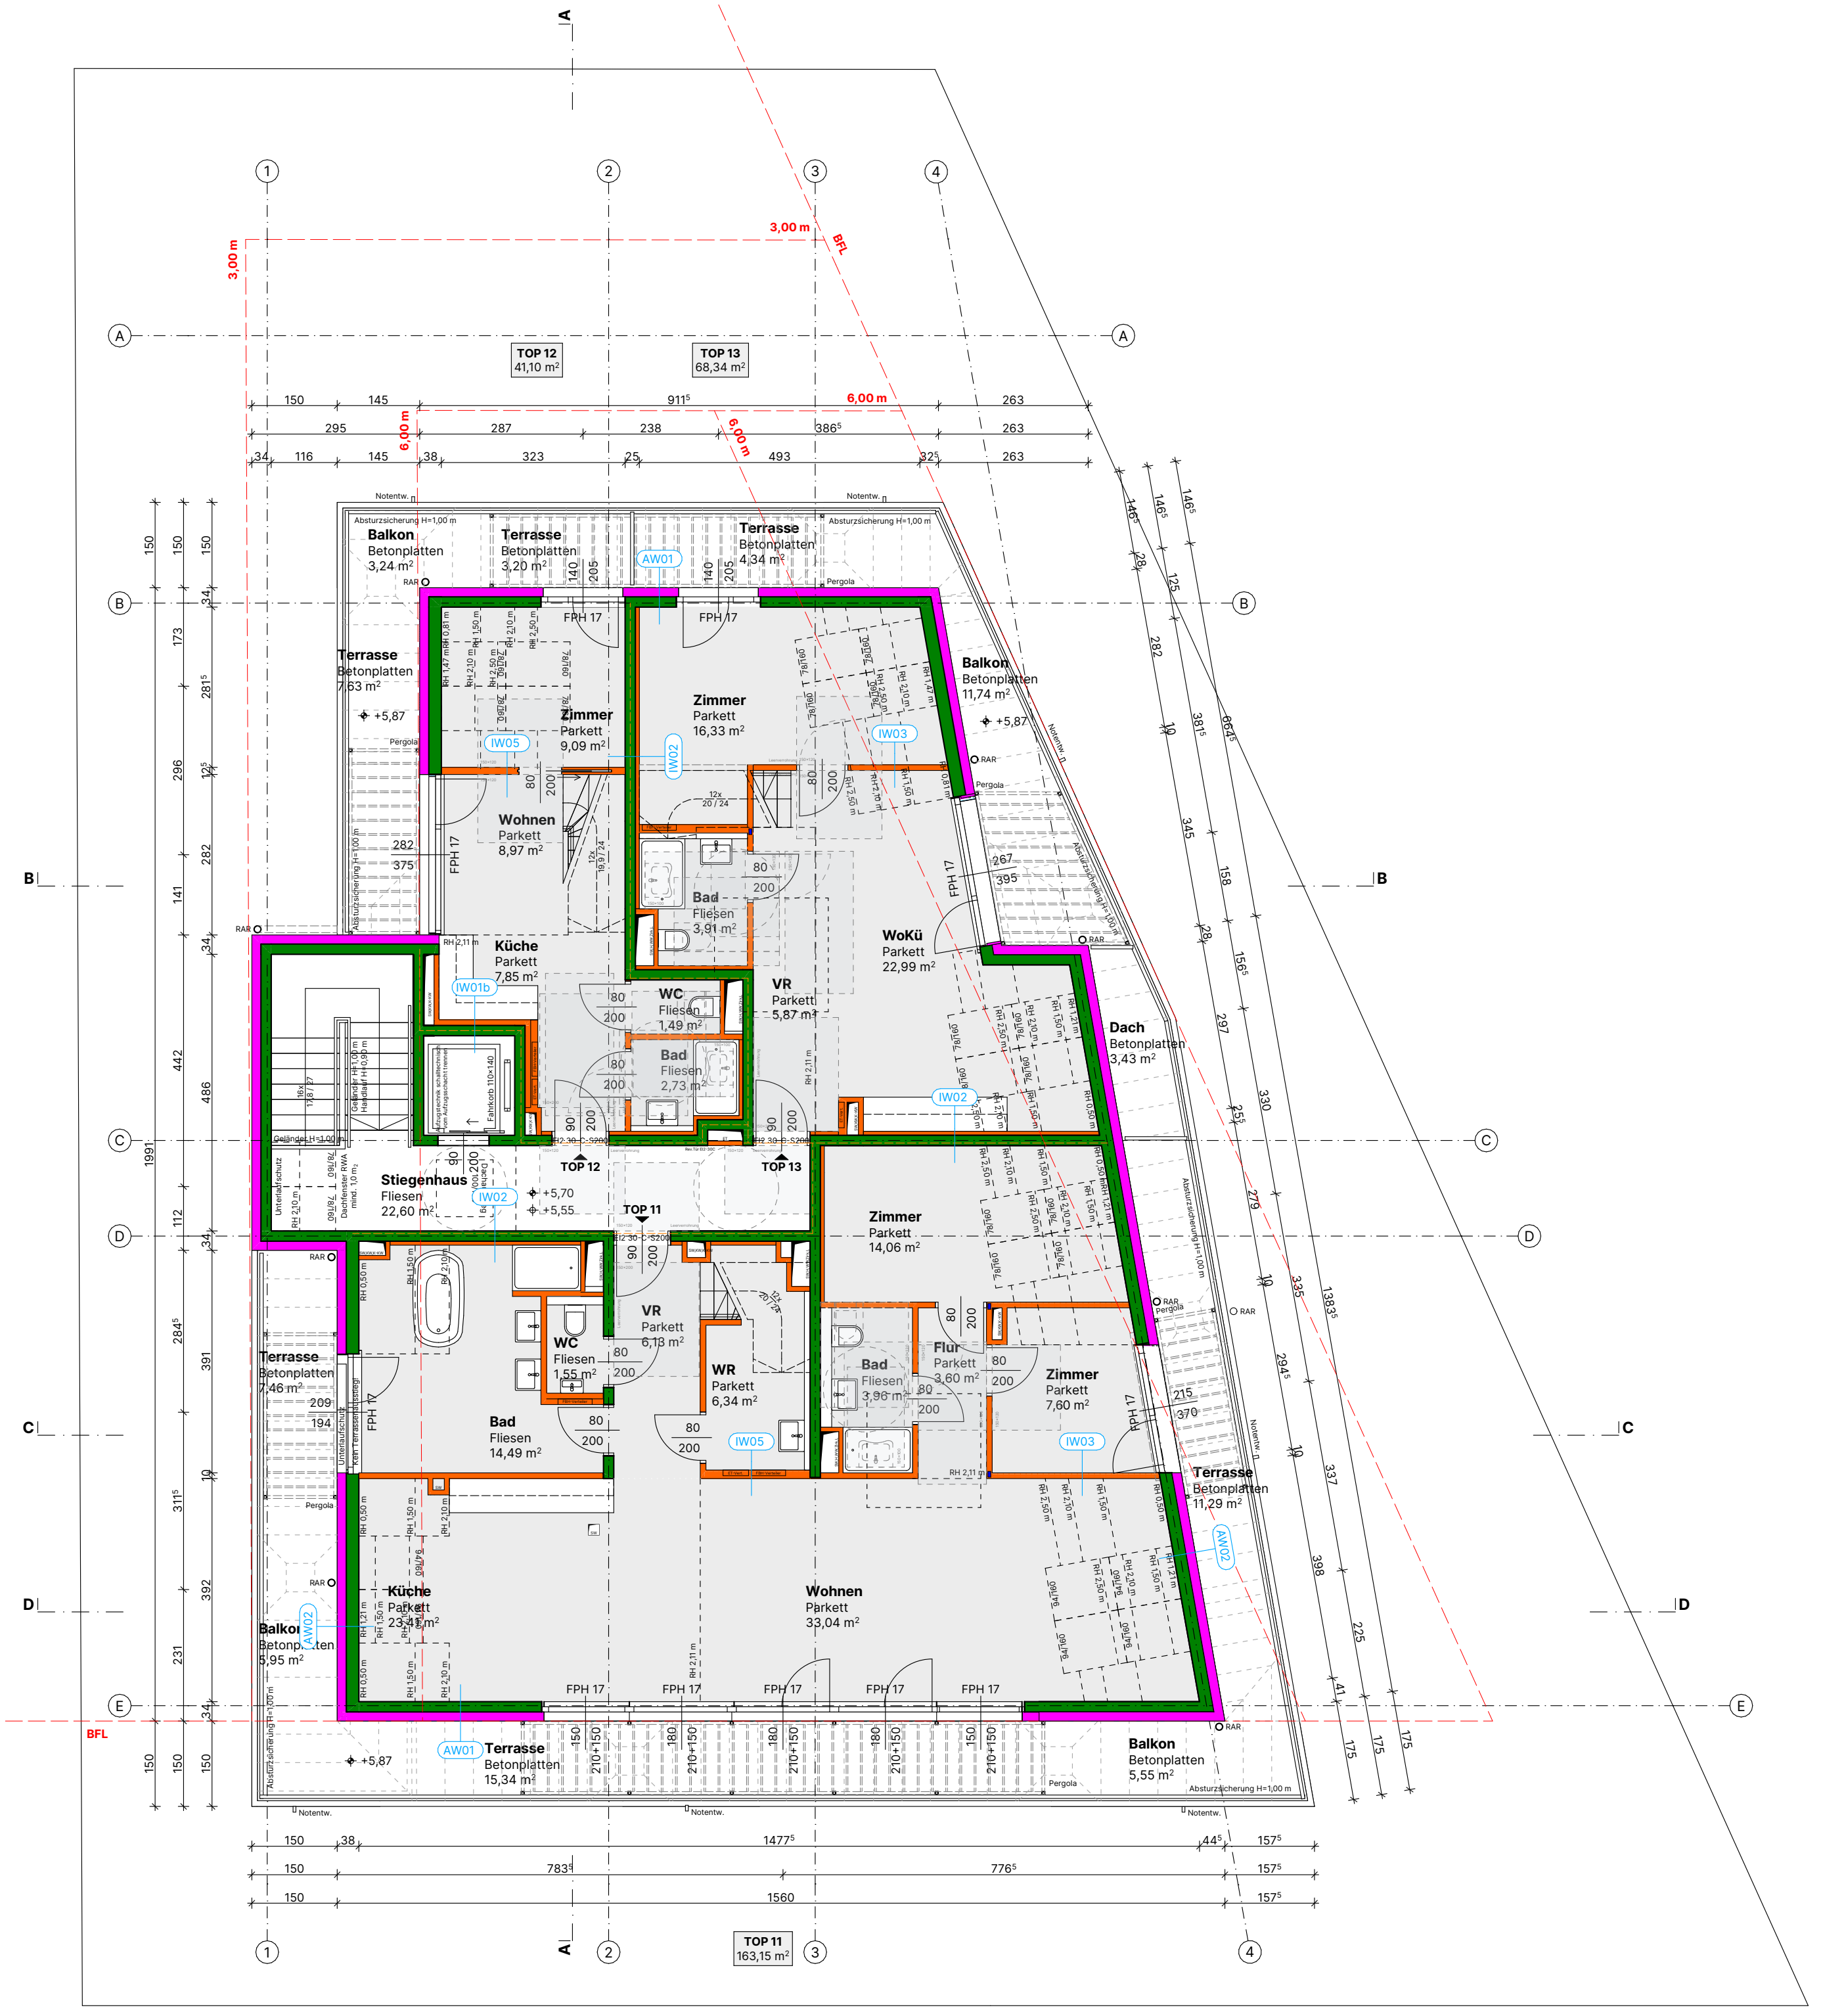

2. OBERGESCHOSS M 1:100

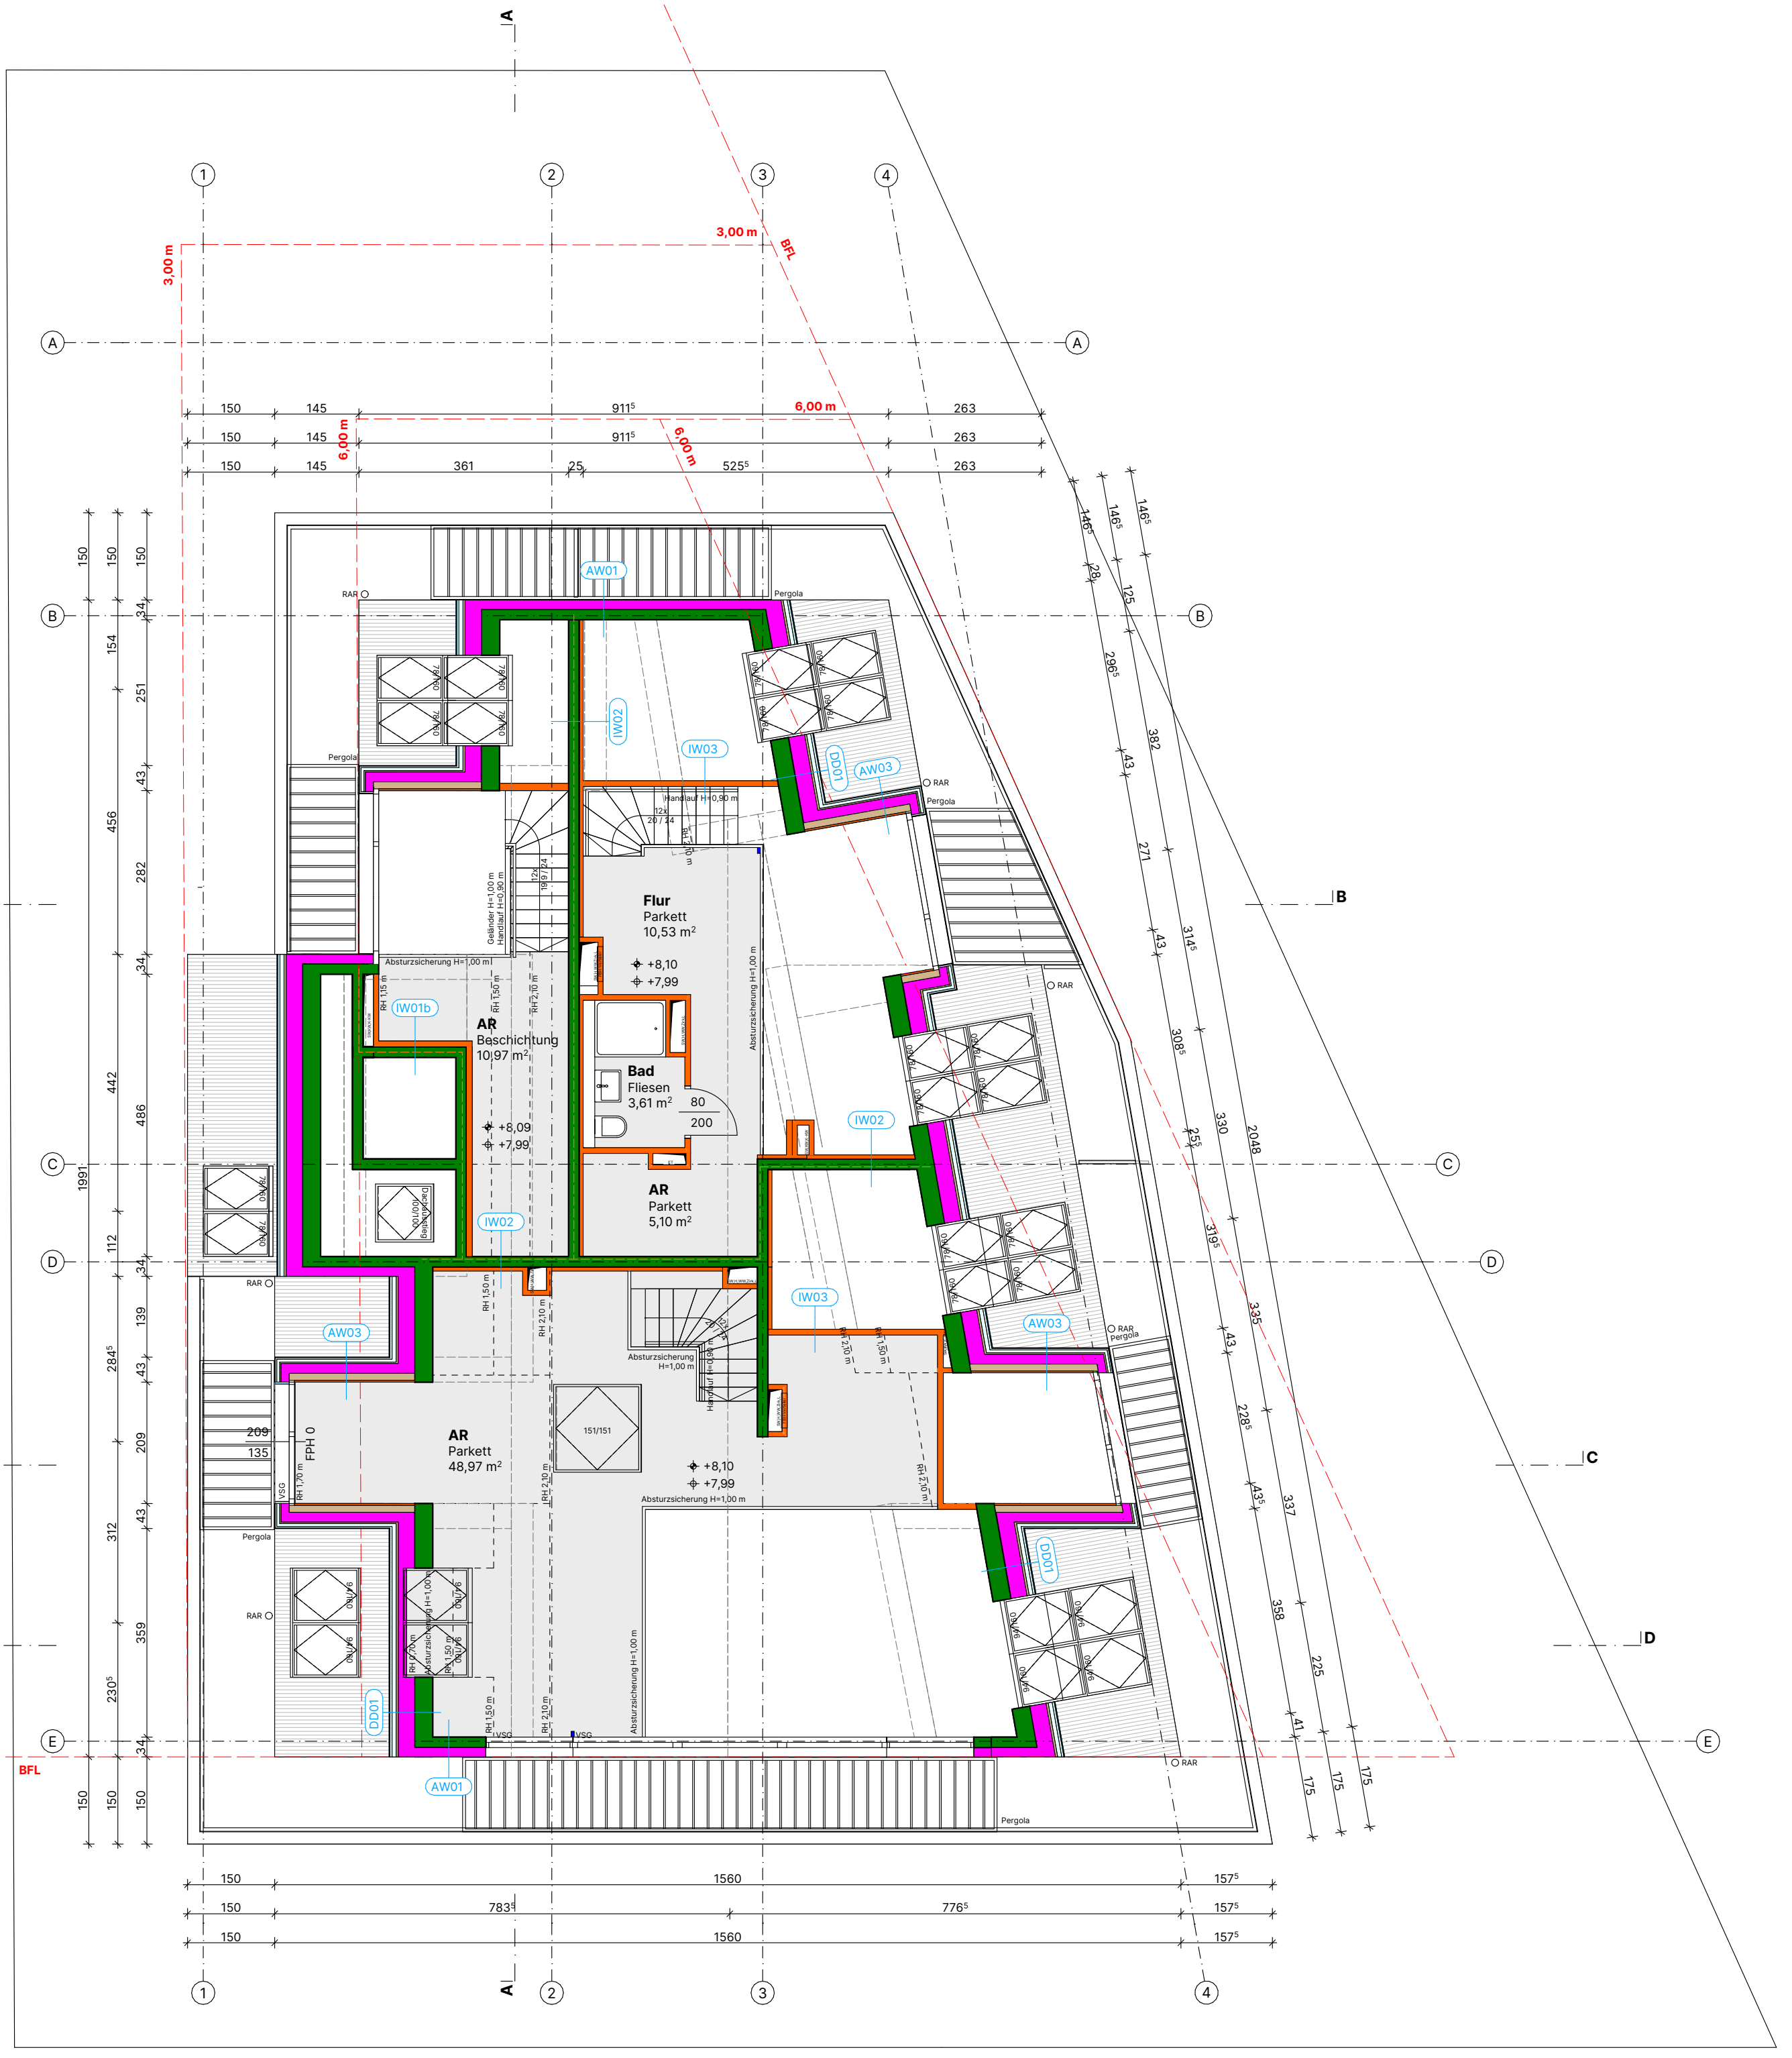

3. OBERGESCHOSS M 1:100

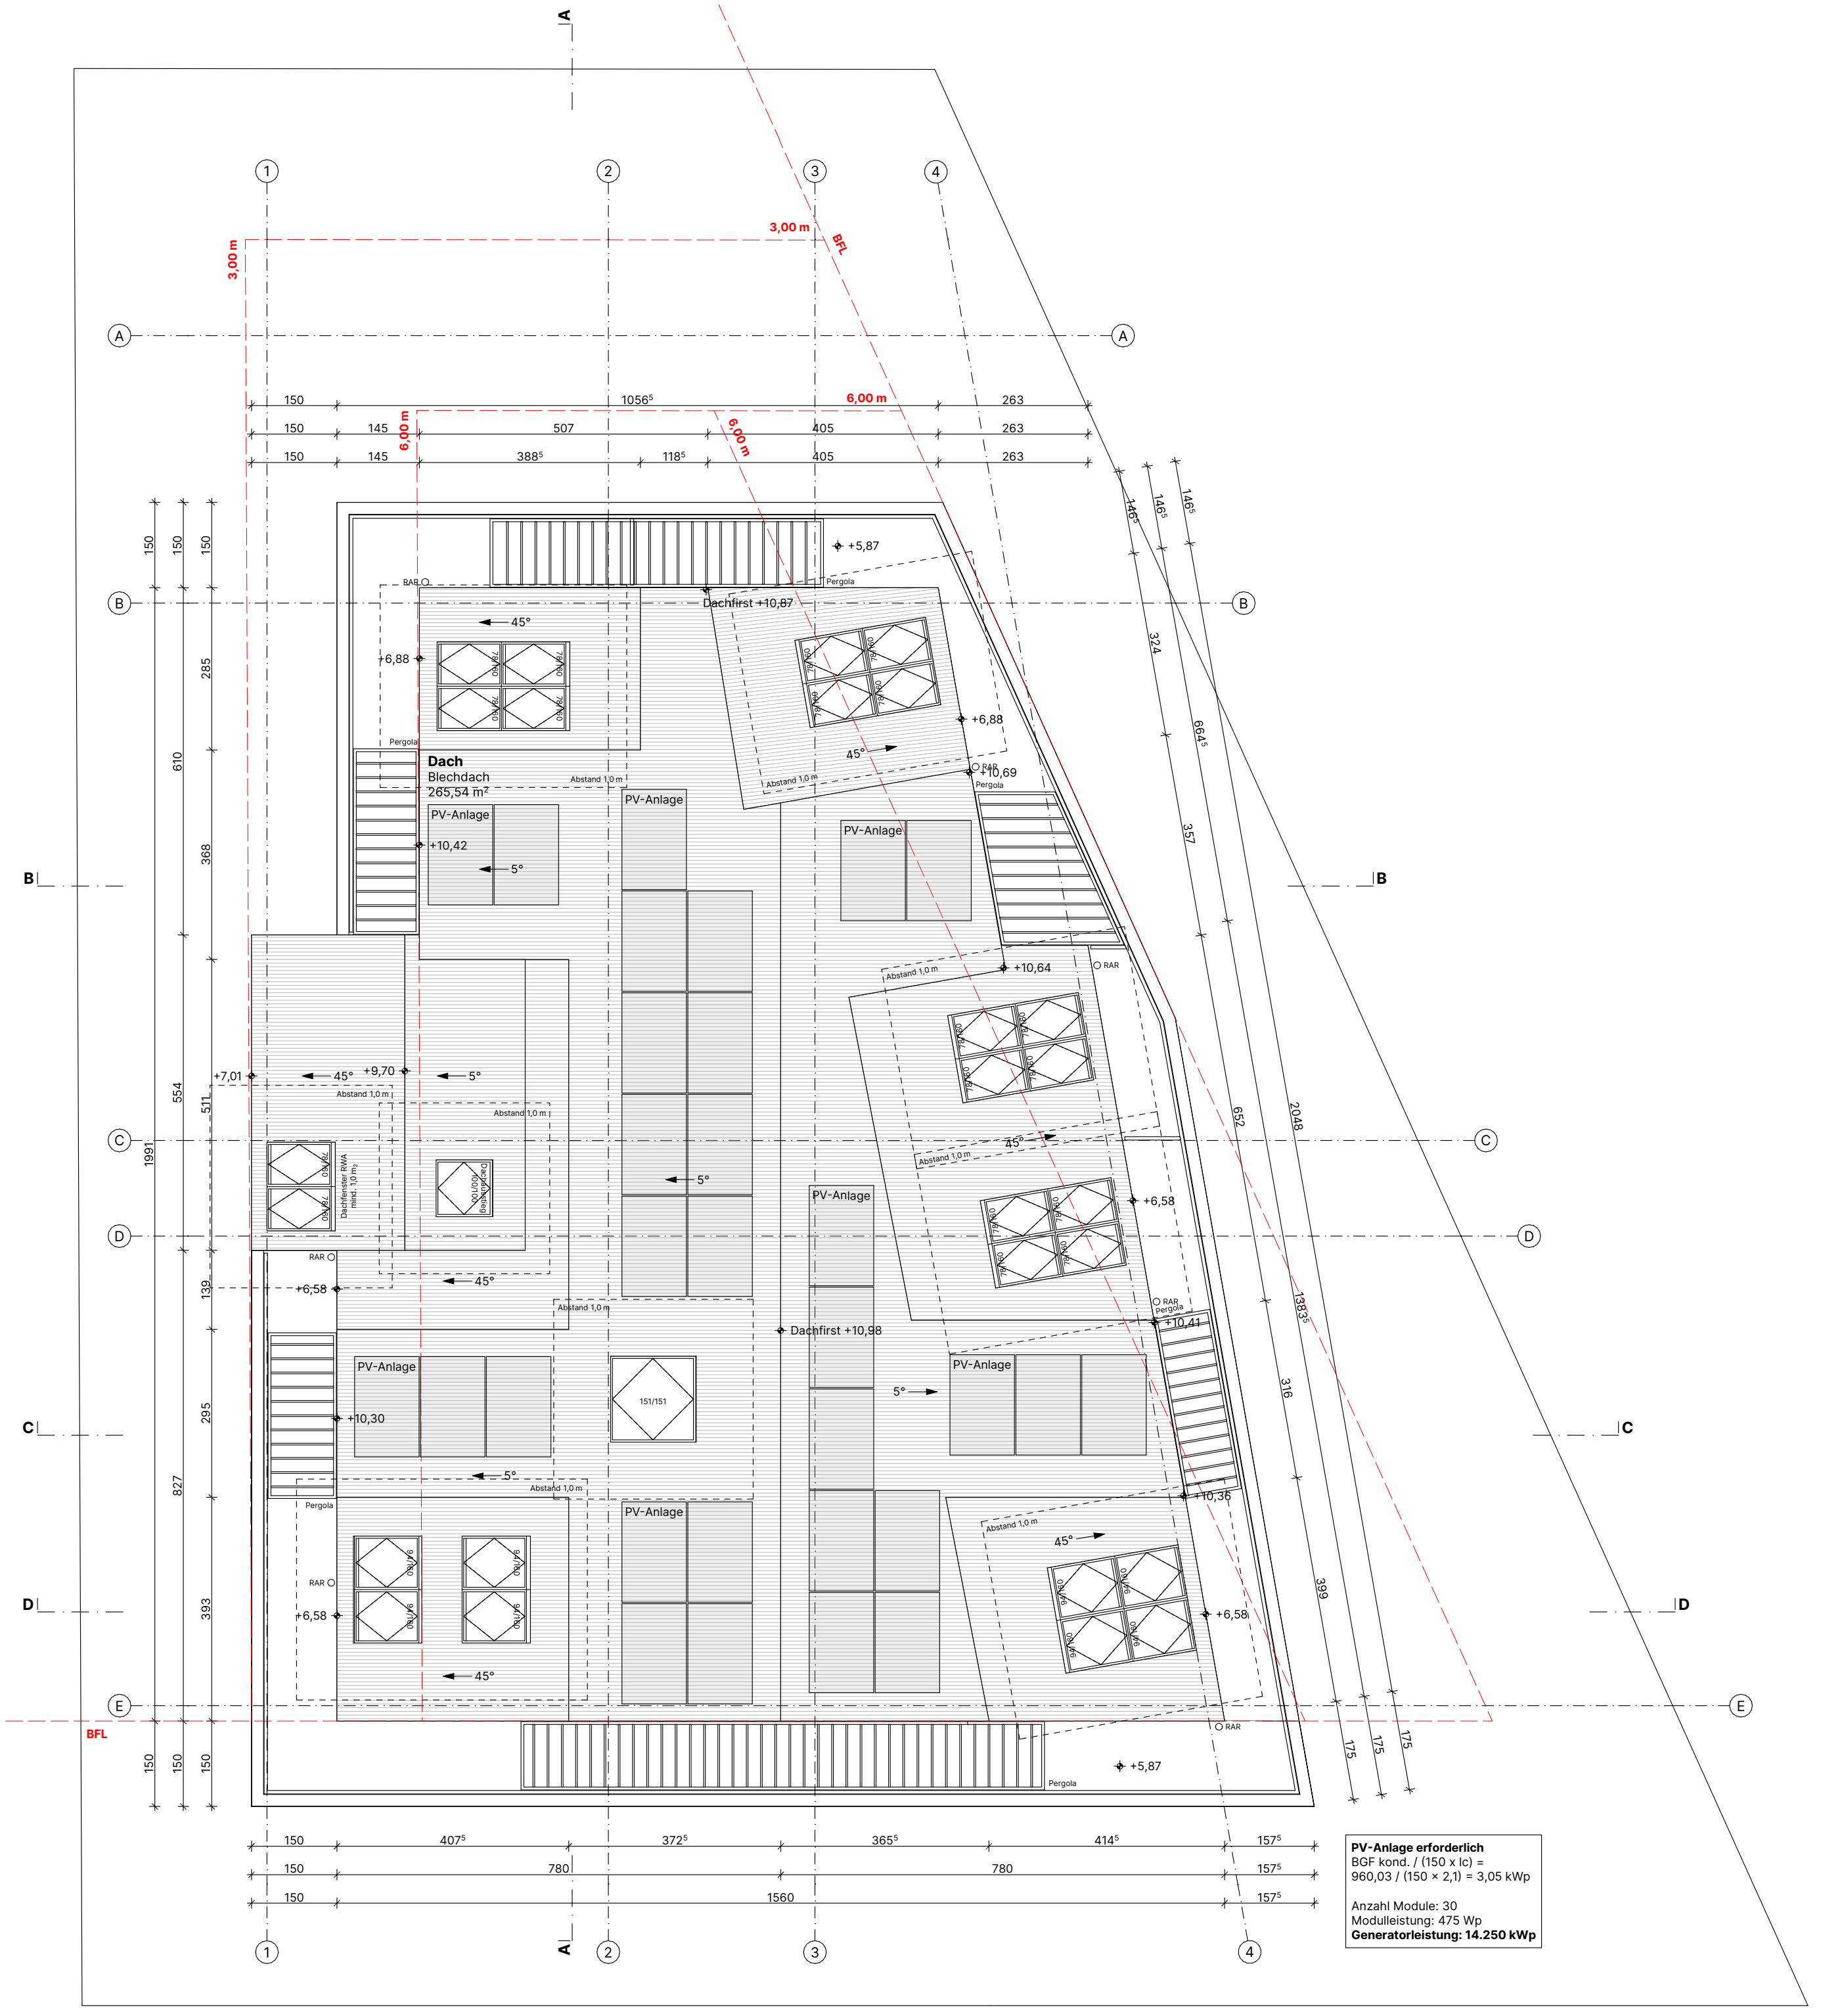

DACHDRAUFSICHT M 1:100

Wohngebäude der GK4 mit 4 oberirdischen Geschoßen und einem Fluchtniveau von ca. 8,1m

Treppenhaus der GK 4 gem. Tab. 2a der OIB-RL 2 mit 1m² Rauchabzugsöffnung an oberster Stelle gemäß TRVB 111 S.

Bei Außenwänden mit WDVS im Sockel in EPS mit einer Dämmstoffdicke > 10cm wird im Sturzbereich von Fenstern und Fenstertüren ein Brandschutzschott aus Mineralwolle mit einem seitlichen Übergriff von 30 cm und einer Höhe von 20 oder in jedem Geschoß ein umlaufendes Brandschutzschott aus Mineralwolle mit einer Höhe von 20cm ausgeführt.
Installationsschächte als Typ A oder B gemäß TRVB 110 B, im Anschluss an gesicherte Fluchtwege nur Typ A. Revisionstüren Schachttyp A zu Gängen bzw. Bauteil Stiege 2 in EI_2 30 (sonstige Bereiche Stiege 1 in EI_2 90) vierseitig angeschlagen, Durchbrüche werden EI 90 und A2 abgeschottet.

Leitungsführungen, Durchbrüche und Abschottungen gemäß TRVB 110 B.

Versperrbare Türen im Verlauf von Fluchtwegen für mehr als 40 Personen (Wohnbereiche) werden mit Notausgangsbeschlägen gem. ÖNORM EN 179 ausgestattet

Löschhilfe mit tragbaren Feuerlöschern gem. TRVB 124 F.

Alle baulichen Anlagen werden mit einer Blitzschutzanlage gem. ÖVE/ÖNORM 62305 ausgestattet.

Unterirdische innenliegende Räume werden mit einer Rauchableitungsöffnung über den Gang direkt ins Freie mit geometrischer Öffnungsfläche von 0,5m² ausgeführt.

Feuerwehraufstellflächen gem. TRVB 134 F.

LEGENDE

- 🟩 Stahlbeton
- 🟩 Beton
- 🟪 Dämmung
- 🟧 Gipskarton
- 🟦 Stahl
- - - - - Grundstücksgrenze
- — — — Widmungsgrenze
- – – – – Fluchtweg
- ======= Brandabschnitt
- - - - - - - Trennbauteil

- ±0,00 Höhenangabe Fertigmaß
- -0,16 Höhenangabe Rohbaumaß
- ±0,00 OK Fertigbau
- +2,60 UK Fertigbau
- -0,16 OK Rohbau
- +2,70 UK Rohbau

- FBDB 20/20 Fußbodendurchbruch
- DDB 20/20 Deckendurchbruch
- IW01 Aufbau
- 703 Detail

WDB	Wanddurchbruch	RAR	Regenabfallrohr
DDB	Deckendurchbruch	GelH	Geländerhöhe
FBDB	Fussbodendurchbruch	BA	Bodenablauf
OK	Oberkante	DN	Nenndurchmesser
UK	Unterkante	PT	Putztürchen
FBOK	Fussbodenoberkante (Fertigmass)	PS	Putzstück
RBOK	Fussbodenoberkante (Rohbaumass)	SEL	Strangentlüftung
FDUK/FDOK	Deckenunter/oberkante (Fertigmass)	FR	Fallrohr
RDUK/RDOK	Deckenunter/oberkante (Rohbaumass)	KS	Kanalsohle
FPH	Parapethöhe (Fertigmass)	$EI_2 30$	Brandschutztüre m.A.d. Brandwiderstandsklasse
RPH	Parapethöhe (Rohbaumass)	T30	Bestands-Brandschutztüre m.A.d. Brandwiderstandskl.
STUK	Sturzunterkante	EI30	Brandschutzwand m.A.d. Brandwiderstandsklasse
STL	Stocklichte	R30/REI30	Träger und Stütze/Verkleid. m.A.d. Brandwiderstandskl.
FOK	Fundamentoberkante	NA	Notausgang
FUK	Fundamentunterkante	DBA	Druckbelüftungsanlage
UZ	Unterzug	BSK	Brandsschutzklappe
RH	Raumhöhe (Fertigmass)	RA	Rauchabzug
FTH	Traufhöhe (Fertigmass)	BRE	Brandrauchentlüftung
FFH	Firsthöhe (Fertigmass)	RS	Rauchschürze
WOK	Wandoberkante	LÜ	Lüftung
WUK	Wandunterkante	ABL	Abluft
LiKu	Lichtkuppel	ZUL	Zuluft
LB	Lichtband	VSG	Verbund-Sicherheitsglas
		ESG	Einscheiben-Sicherheitsglas

ALLGEMEINE HINWEISE

Bei dieser Zeichnung bzw. Ausarbeitung handelt es sich um geistiges Eigentum des:der Planenden, welches somit gesetzlich geschützt ist. Jegliche Vervielfältigung, Veröffentlichung, Überarbeitung, Benutzung oder Weitergabe an Dritte in Verbindung mit einem anderen Projekt oder einer anderen Arbeit, bedarf der ausdrücklichen schriftlichen Zustimmung des:der Planenden.

Die Naturmaße sind zu nehmen und die Koten zu prüfen! Abweichungen von dargestellten Inhalten oder schriftlichen Vereinbarungen sind mit dem:der Planenden sowie der Bauleitung vor Bauausführung umgehend schriftlich mitzuteilen.

Dieser Plan ist vom ausführenden Unternahmen mit den Plänen der Tragwerksplanung und denen der Fachplanung (HKLS, Elektro, Brandschutz usw.) auf Übereinstimmungen und Vollständigkeit zu überprüfen! Etwaige Maßfehler und Unklarheiten sind dem:der Planverfasser:in sofort schriftlich mitzuteilen und abzuklären!

Die relevanten statischen Angaben sind den Statik-Plänen zu entnehmen.
Die relevanten HKLS- und Elektroangaben sind den HKLS- und Elektroplänen zu entnehmen. Die zugehörigen TGA-Bauangaben sind ebenso den jeweils zugeordneten Plänen zu entnehmen.
Erforderliche Durchführungen sind den HKLS- und Elektroplänen zu entnehmen.
Decken- und Wandaufbauten lt. Baukatalog Bauphysik.

Darstellung der Möblierung dient lediglich zur besseren Lesbarkeit der Pläne. Die Tatsächliche Möbelaufstellung kann von der planlichen Darstellung abweichen.

Alle Längenmaße sind in Zentimeter angegeben. Kote Parapet und Sturz bezieht sich auf FBOK. Alle anderen Höhenkoten beziehen sich auf Projektnull.
Fenstermaße = Architekturlichte, Türmaße = Öffnungslichte.
Höhe von Handläufen bei Stiegen 90 cm, Höhe von Absturzsicherungen mind. 100 bzw. 110 cm.

Verglasung als Absturzsicherung wird bis H=110 cm in VSG ausgeführt. Raumhohe Verglasung wird bis H=150 cm in ESG ausgeführt.

Sämtliche Rigole, Gullys usw. sind gegen Frostschäden (z. B. mit Begleitheizung) zu schützen.

Die Darstellung der Brandabschnitte und Hydranten in den Bauplänen ist symbolisch. Alle Schächte, Durchbrüche, Schlitze usw. müssen wieder verschlossen werden, sofern sie durch Brandabschnitte führen in EI90 bzw. REI90 gemäß Schachtrichtlinie (EI90). Ausführung Brandschutz lt. Brandschutzkonzept.

Schadensfolgeklasse CC2 nach ÖNORM B 1990-1

Naturmaße nehmen! Koten prüfen!

PARIE
A B C D E F

EINREICHPLAN

BAUVORHABEN
Wohnhaus Bodmergasse

ADRESSE
Bodmergasse 35, 1220 Wien

PLANINHALT
Grundrisse

PLANVERFASSER
sipa
sipa Architektur, Davor Podbregar ZT e.U.
Elizabeth-T.-Spira-Promenade 2/7 | A-1030 Wien
www.sipa-arch.com | info@sipa-arch.com | +43 664 1072040

LANGSTEMPEL

BAUWERBER
RST-Design BMG35 GmbH
Am Bahnhof 2, 1220 Wien
office@rst-design.com | +43 676 6902502

BAUFÜHRER
TBD
TBD
TBD | TBD

GRUNDEIGENTÜMER
RST-Design BMG35 GmbH
Am Bahnhof 2, 1220 Wien
office@rst-design.com | +43 676 6902502

BAUBEHÖRDE
MA37 - Gebietsgruppe Ost
Dresdner Straße 82, 1200 Wien
ost@ma37.wien.gv.at | +43 1 4000 37300

KATASTRALGEMEINDE	EINLAGEZAHL	GRUNDSTÜCK	PROJEKTNULL
01651 - Aspern	**1501**	**534/48**	**±0,00=2,15 ü.WN/158,83 ü.Adria**
PROJEKTNUMMER	PROJEKTPHASE	GEZEICHNET	PLANGRÖSSE
2607	**EINREICHUNG**	**DP**	**1260 × 841 MM**
PLANNUMMER	MASSSTAB	PLANSTAND	INDEX
2607.04.02	**1:100**	**16.10.2026**	**-**