BAUBESCHREIBUNG FÜR DAS BAUVORHABEN WOHNHAUS BODMERGASSE, BODMERGASSE 35, 1220 WIEN.

Wien, am 16. 10. 2026

Bauwerber:	RST-Design BMG35 GmbH Am Bahnhof 2, 1220 Wien
Grundeigentümer	RST-Design BMG35 GmbH Am Bahnhof 2, 1220 Wien
Adresse:	Bodmergasse 35, 1220 Wien
Grundstücksnummer:	534/48
Einlagezahl:	1501
Katastralgemeinde:	01651 - Aspern
Widmung:	Wohngebiet, Bauklasse I, max. Gebäudehöhe 6,5 m offene oder gekuppelte Bauweise

Fensterlose WCs, Bäder und Abstellräume mit Waschmaschine werden mittels Unterputzlüfter entlüftet.
Die Fortluftführung von übereinander angeordneten Sanitärräumen erfolgt über eine gemeinsame Steigleitung (Einrohrsystem) aus runden Wickelfalzrohren aus verzinktem Stahlblech bis über Dach, die Dimensionierung vom Steigleitungsdurchmesser erfolgt gemäß ÖNORM H 6036.
Einlagerungsräume, Technikräume und sonstige Nebenräume in den Allgemeinbereichen werden, soweit möglich, statisch be- und entlüftet. Ist eine statische Lüftung nicht möglich, wird der betroffene Raum mit einer mechanischen Abluftanlage ausgerüstet.
Die Dimensionierung der Garagenlüftungsanlage inkl. zugehöriger Bereiche erfolgt u.a. unter Berücksichtigung nachgeführter Normen und Richtlinien:
OIB-Richtlinie 3 Hygiene, Gesundheit du Umweltschutz
OIB-Richtlinie 2.2 Brandschutz bei Garagen, überdachten Stellplätzen und Parkdecks
ÖNORM H 6003 Lüftungstechnische Anlagen für Garagen
ÖNORM H 6029 Brandrauchverdünnungs-Anlagen (BRV-Anlagen)
ÖNORM M 9419 Kontinuierliche Überwachung der Kohlenstoffmonoxid-Konzentration in Garagen
Grundsätzlich sind Garagen gem. OIB-Richtlinie 3 (Pkt. 8.3.1) natürlich oder mechanisch so zu lüften, dass im Regelbetrieb ein Halbstundenmittelwert für Kohlenstoffmonoxid (CO) von 50 ppm nicht überschritten wird.
Gem. Pkt. 8.3.5 der OIB-Richtlinie 3 ist dieser Punkt für Garagen mit mehr als 250 m² Nutzfläche für oberirdische Geschoße und das erste unterirdische Geschoß erfüllt, wenn die Geschoße mit natürlichen Rauch- und Wärmeabzugseinrichtungen gem. Tabelle 2 der OIB-Richtlinie 2.2 ausgestattet sind.
Aufgrund dieser Definition wird keine mechanische Garagenlüftungsanlage vorgesehen.

Sanitär
Gemäß Technischer Bericht Fa. HNBT Ingenieure GmbH
Es erfolgt ein Neuanschluss an das öffentliche Versorgungsnetz der Stadt Wien. Mindestfließdrücke und Berechnungsdurchflüsse an den Zapfstellen gem. DIN 1988-300. Qualität: Hygienisch einwandfreier Zustand.
Die Warmwasserbereitung erfolgt zentral mittels heizungswasserbetriebener Durchfluss-Warmwasserbereiter (Frischwassermodul) gem. ÖNORM B 1921:2023. Als Aufstellort des Frischwassermodules dient die Technikzentrale im Untergeschoss. Das Warmwasserverteilsystem wird mit Temperaturhaltung (Zirkulation) ausgeführt. Die Energiebereitstellung erfolgt über die Wärmepumpenanlage.
Gemäß ÖNORM B1921:2023-07 wird die Anlage der vorliegenden Gebäudekategorie „Wohngebäude" in den Nutzungsbereich „A" eingeteilt.
Die Schmutzwasserentwässerung wird gemäß EN 12056-2 bzw. ÖNORM B 2501 ausgeführt.
Das anfallende Schmutzwasser wird über Einzelanschluss bzw. Sammelanschluss- und Fallleitungen sowie Hängekanäle mit natürlichem Gefälle dem Kanalsystem zugeführt.
Im Technikraum wird eine Kleinhebeanlage für die Entwässerung eines Ausgussbeckens und diverser Sicherheitsventile vorgesehen.

Entsorgung Niederschlagswässer
Die Niederschlagswässer werden auf Eigengrund versickert.

Elektrotechnik
Gemäß Technischer Bericht Fa. HNBT Ingenieure GmbH
Gegenständlicher Bericht beschreibt die Leistungen des Gewerks Elektrotechnik. Die elektrotechnische Anlage wird unter Einhaltung der OVE E 8101, elektrotechnischen Sicherheitsvorschriften der Elektrotechnikverordnung 2020 (Anhang I und II), Elektrotechnikgesetz 1992 und der TAEV sowie allen Gesetzen, Folgenormen, Bestimmungen, Vorschriften, Verordnungen und Richtlinien in der jeweils letztgültigen Fassung errichtet.

PROJEKTBESCHREIBUNG:

Geplant ist die Errichtung eines Wohngebäudes mit insgesamt 13 Wohneinheiten. Das Gebäude umfasst ein Erdgeschoss, drei Obergeschosse sowie ein Untergeschoss. Das Satteldach beginnt ab dem 2. Obergeschoss. Die Wohnungen im 2. und 3. Obergeschoss sind als Maisonettewohnungen konzipiert, wobei die Erschließung über das 2. Obergeschoss erfolgt und das 3. Obergeschoss ausschließlich über wohnungsinterne Treppen zugänglich ist.
Die Haupterschließung des Gebäudes erfolgt über ein innenliegendes Stiegenhaus mit Aufzug, welches bis zum 2. Obergeschoss führt. Sowohl der Hauptzugang zum Gebäude als auch die Zufahrt zur Tiefgarage erfolgen über die Bodmergasse.
Insgesamt werden 13 Wohnungen errichtet. Die Wohnungen im Erdgeschoss verfügen über private Eigengärten, während den Wohnungen in den Obergeschossen private Freiflächen in Form von Balkonen, Loggien oder Terrassen zugeordnet sind.
Im Untergeschoss befinden sich Technikräume, Einlagerungsräume sowie ein Fahrradraum. Die Tiefgarage verfügt über insgesamt 7 PKW-Stellplätze.

Statik
Gemäß Vorstatik Fa. petz zt-gmbh
In der Bodmergasse 1220 Wien soll eine neue Wohnhausanlage errichtet werden. In dieser Vorstatik wird die Vorbemessung aller wichtigen Tragelementen vorgenommen.
Das Bauwerk ist in die Schadensfolgeklasse CC2 nach ÖN B1990-1 Tabelle B.1 einzuordnen.
Das Gebäude besteht aus einer Tiefgarage und vier oberirdischen Geschossen: Erdgeschoss (EG), 1. Obergeschoss (OG1), 2. Obergeschoss (OG2) und einem Galeriegeschoss (GG). Das Gebäude ist in Massivbauweise in Stahlbeton konzipiert, teilweise in Ortbeton und teilweise in Fertigteilbauweise (Hohlwände und Elementdecken). Über dem 2. Obergeschoss und dem Galeriegeschoss ist ein Sargdeckel konzipiert.

Gründung UG
Bodenplatte h=25-40cm mit Vouten h=bis zu 90cm Gesamtstärke laut Kapitel 3 C25/30 B2; Bewehrungsgehalt 100kg/m³
OK im Gefälle; Abdichtung als „Schwarze Wanne" gegen GW
Unter der Bodenplatte XPS TOP 30; bis. zu 20% der Fläche TOP 50

Wände UG
STB-Außenwände erdberührt t=25 teilw. 30 cm als Ortbeton C25/30 B2; Bewehrungsgehalt 110kg/m³
STB-Innenwände t=18 cm als Hohlwände; bis zu 30% als Ortbeton C25/30 XC1; Bewehrungsgehalt 90kg/m³

Stützen UG
Ortbetonstützen in verschiedenen Abmessungen laut Kapitel 3 C50/60 B3; Bewehrungsgehalt 200kg/m³

Wände uns Stützen EG-GG
STB-Wände t=18 cm als Hohlwände; bis zu 30% als Ortbeton C30/37 XC1; Bewehrungsgehalt 90kg/m³
Stahlstützen Formrohr 100x50x4 S235 im GG

STB-Decken und Träger
Decke und Träger über UG1 laut Kapitel 3; C40/50 B2; Bewehrungsgehalt: Decke 110kg/m³; Träger 250kg/m³ in den Außenbereichen OK im Gefälle
Regeldecke h=18cm mit Vouten h=18+4cm laut Kapitel 3 als Elementdecke; bis zu 25% als Ortbeton C30/37, teilw. C40/50 XC1 (Decke ü. 1. und 2.OG) ; Bewehrungsgehalt 100kg/m³
Sargdeckel h=22cm laut Kapitel 3

Energieversorgung
Gemäß Technischer Bericht Fa. HNBT Ingenieure GmbH
Die Versorgung des Objektes mit elektrischer Energie erfolgt aus dem Niederspannungsnetz des örtlichen Netzbetreibers (Wiener Netze).
Die Niederspannungshauptverteilung (NSHV) wird im 1. Untergeschoss im dafür vorgesehenen Elektrotechnikraum angeordnet.
Von der NSHV ausgehend erfolgt die Energieverteilung über einen zentralen Steigschacht. Über diesen werden die einzelnen Unterverteilungen sowie die Wohnungsverteiler sternförmig und geschossweise versorgt.

Niederspannungsverteilungsanlage
Gemäß Technischer Bericht Fa. HNBT Ingenieure GmbH
Die Niederspannungsverteiler werden entsprechend den örtlichen Gegebenheiten (z.B.: mechanische, feuchte-, temperatur- Beanspruchungen, etc.) in entsprechender Schutzart und entsprechenden Reserven

- Reserveplatz für Verteiler ca. 30%
- Rangierplatzreserve ca. 30%

ausgeführt.
In den Elektro-Verteileranlagen sind entsprechende Überspannungsschutzeinrichtungen vorgesehen:

- Niederspannungshauptverteilung TYP 1+2+3 (BSK I-IV)
- Unterverteilern TYP 2
- Endstromkreis Feinschutz TYP 3

Sämtliche Verteiler bzw. Schaltgeräte sind laienbedienbar auszuführen (gem. ÖVE Richtlinie R5).

Schutzmaßnahmen
Gemäß Technischer Bericht Fa. HNBT Ingenieure GmbH
Die Schutzmaßnahmen werden gem. den gültigen Bestimmungen (OVE E 8101, TAEV, ÖVE-Richtlinien, etc.) eingehalten.
Als Schutzmaßnahme bei indirektem Berühren wird die Nullung, mit Zusatzschutz (Fehlerstromschutzschalter mit einem Auslösenennfehlerstrom von ≤ 30mA) gem. den gültigen Vorschriften und Normen, angewendet.

Beleuchtungsanlage
Gemäß Technischer Bericht Fa. HNBT Ingenieure GmbH
Die Dimensionierung der Beleuchtungsanlage erfolgt gem. den geltenden Vorschriften und Richtlinien in der jeweiligen letztgültigen Fassung.

Erdungs-/Blitzschutzanlage, Potentialausgleich
Gemäß Technischer Bericht Fa. HNBT Ingenieure GmbH
Es wird eine Erdungs- und Blitzschutzanlage gemäß den jeweils geltenden gesetzlichen Bestimmungen sowie den einschlägigen Normen und Vorschriften - OVE E 8101, OVE E 8014 sowie der ÖVE/ÖNORM EN 62305 - in der jeweils letztgültigen Fassung vorgesehen.
Erdungsanlage:

- Erdungssystem: Fundamenterder (doppelte Erdungsanlage)
- Material: im Fundament – Stahl verzinkt D10;
  im Erdreich – Edelstahl D10 Erde Niro V4A
- Materialstärke: Durchmesser 10mm
- Verlegetiefe: mind. 0,5m

Blitzschutzanlage:

- Blitzschutzklasse: LPS III gem. Beiblatt 2 der ÖVE/ÖNORM EN 62305
- Ableitung: Unterputz
- Fangeinrichtung: vermaschte Fangleitungen und Fangstangen
- Material: Aluminium

als Hohlwände; bis zu 25% als Ortbeton C30/37 XC1; Bewehrungsgehalt 100kg/m³
Gaupe CLT 120 C3s

Loggien und Balkone
STB-Decken h=min.16cm; C30/37 B3; Bewehrungsgehalt 130kg/m³ mit Isokörbe und Schubdorne

Stiegen
STB-Fertigteile d=16cm C30/37 XC1; Bewehrungsgehalt 130kg/m³

Die genaue Konstruktion kann dem nächsten Kapitel 3 entnommen werden. Von den Bewehrungsangaben sind Abweichungen von +15% möglich.

Brandschutz
Gemäß Brandschutzbeschreibung Fa. B-LAB
Wohngebäude der GK4 mit 4 oberirdischen Geschoßen und einem Fluchtniveau von ca. 8,1m

Treppenhaus der GK 4 gem. Tab. 2a der OIB-RL 2 mit 1m² Rauchabzugsöffnung an oberster Stelle gemäß TRVB 111 S

Bei Außenwänden mit WDVS im Sockel in EPS mit einer Dämmstoffdicke > 10cm wird im Sturzbereich von Fenstern und Fenstertüren ein Brandschutzschott aus Mineralwolle mit einem seitlichen Übergriff von 30 cm und einer Höhe von 20 oder in jedem Geschoß ein umlaufendes Brandschutzschott aus Mineralwolle mit einer Höhe von 20cm ausgeführt.
Installationsschächte als Typ A oder B gemäß TRVB 110 B, im Anschluss an gesicherte Fluchtwege nur Typ A. Revisionstüren Schachttyp A zu Gängen bzw. Bauteil Stiege 2 in EI_2 30 (sonstige Bereiche Stiege 1 in EI_2 90) vierseitig angeschlagen, Durchbrüche werden EI 90 und A2 abgeschottet.

Leitungsführungen, Durchbrüche und Abschottungen gemäß TRVB 110 B.

Versperrbare Türen im Verlauf von Fluchtwegen für mehr als 40 Personen (Wohnbereiche) werden mit Notausgangsbeschlägen gem. ÖNORM EN 179 ausgestattet

Löschhilfe mit tragbaren Feuerlöschern gem. TRVB 124 F.

Alle baulichen Anlagen werden mit einer Blitzschutzanlage gem. ÖVE/ÖNORM 62305 ausgestattet.

Unterirdische innenliegende Räume werden mit einer Rauchableitungsöffnung über den Gang direkt ins Freie mit geometrischer Öffnungsfläche von 0,5m² ausgeführt.

Feuerwehraufstellflächen gem. TRVB 134 F

Heizung
Gemäß Technischer Bericht Fa. HNBT Ingenieure GmbH
Die Ermittlung der Norm-Heizlast erfolgt gemäß ÖNORM EN 12831 und ÖNORM H 7500-1.
Die Energiebereitstellung erfolgt über eine Luft/Wasser-Wärmepumpenanlage in Monoblock Bauweise.
Sämtliche Wohnungen werden mit Fußbodenheizung und Raumthermostat ausgestattet.

Lüftung
Gemäß Technischer Bericht Fa. HNBT Ingenieure GmbH
Der hygienische Mindestluftwechsel in Räumen mit Außenfenster wird durch Fensterlüftung erreicht.

- Materialstärke: Durchmesser 8mm

Der allgemeine Potentialausgleich wird gemäß OVE E 8101 bzw. TAEV in der jeweils letztgültigen Fassung ausgeführt.

Sicherheitstechnik
Gemäß Technischer Bericht Fa. HNBT Ingenieure GmbH
Die Wohnungen werden mit batteriegestützten Rauchwarnmeldern gemäß den geltenden Vorschriften und Normen (TRVB S 122) ausgestattet.

Photovoltaikanlage
Gemäß Technischer Bericht Fa. HNBT Ingenieure GmbH
Auf dem Dach des Gebäudes wird eine netzgekoppelte Aufdach-Photovoltaikanlage errichtet.
Der Wechselrichter werden im 1. Untergeschoss im Niederspannungshauptverteilungsraum untergebracht.
Die DC-Leitungen werden vom Dach über den bestehenden Steigschacht bis zum NSHV-Raum geführt und in geschlossenen Metallrohren verlegt.
Zur Erhöhung des Eigenverbrauchs wird im NSHV-Raum ein Energiespeicher errichtet. Die vorgesehenen E-Ladestationen in der Garage werden gemeinsam mit der Photovoltaikanlage und dem Energiespeicher über ein Energiemanagementsystem (EMS) gesteuert, um den Eigenverbrauchsanteil bzw. Eigennutzungsgrad der erzeugten PV-Energie zu optimieren.
Die Anlage wird sowohl auf der Gleich- als auch der Wechselspannungsseite im Niederspannungsbereich unter 1000V betrieben.
Die Photovoltaikanlage und der Energiespeicher wird im Netzparallelbetrieb (als Überschussanlage) in die NSHV-Anlage eingebunden.
Für die Photovoltaikanlage wird ein Brandschutz-Abschalteinrichtung (Not-Aus-Schalter) nach ÖVE-Richtlinie R11-1 vorgesehen.
Die Photovoltaikanlagen und deren Komponenten sind entsprechend in die Blitzschutzanlage einzubinden.
Die Zugänglichkeit zu den Photovoltaikmodulen erfolgt über einen bauseitigen Dachaufstieg einschließlich der erforderlichen Absturz- und Sicherungseinrichtungen.

Technische Daten - Photovoltaikanlage:

- Anzahl PV-Module: 31 Stück
- Leistung PV-Modul: 475 Wp
- Fläche PV-Anlage: ca. 65 m²
- Dachform: flach geneigtes Dach
- Montageart: Aufdach
- Gesamtnennleistung AC: 14,725 kWp (Generatorleistung)

Technische Daten - Energiespeicher:

- Nutzbare Kapazität: 20 kWh
- Max. Ausgangsstrom: 250 A
- Peak Ausgangsstrom: 360 A, 5 s
- Nennspannung: 51,2 V
- Spannungsbereich: 40-57,6 V
- Abmessungen (H/W/T): 1460 x 650 x 298 mm
- Gewicht: 244 kg
- Umgebungstemperatur: -10 °C bis +50°C
- Zelltechnologie: Lithium-Eisen-Phosphat-Batterie (Kobaltfrei)

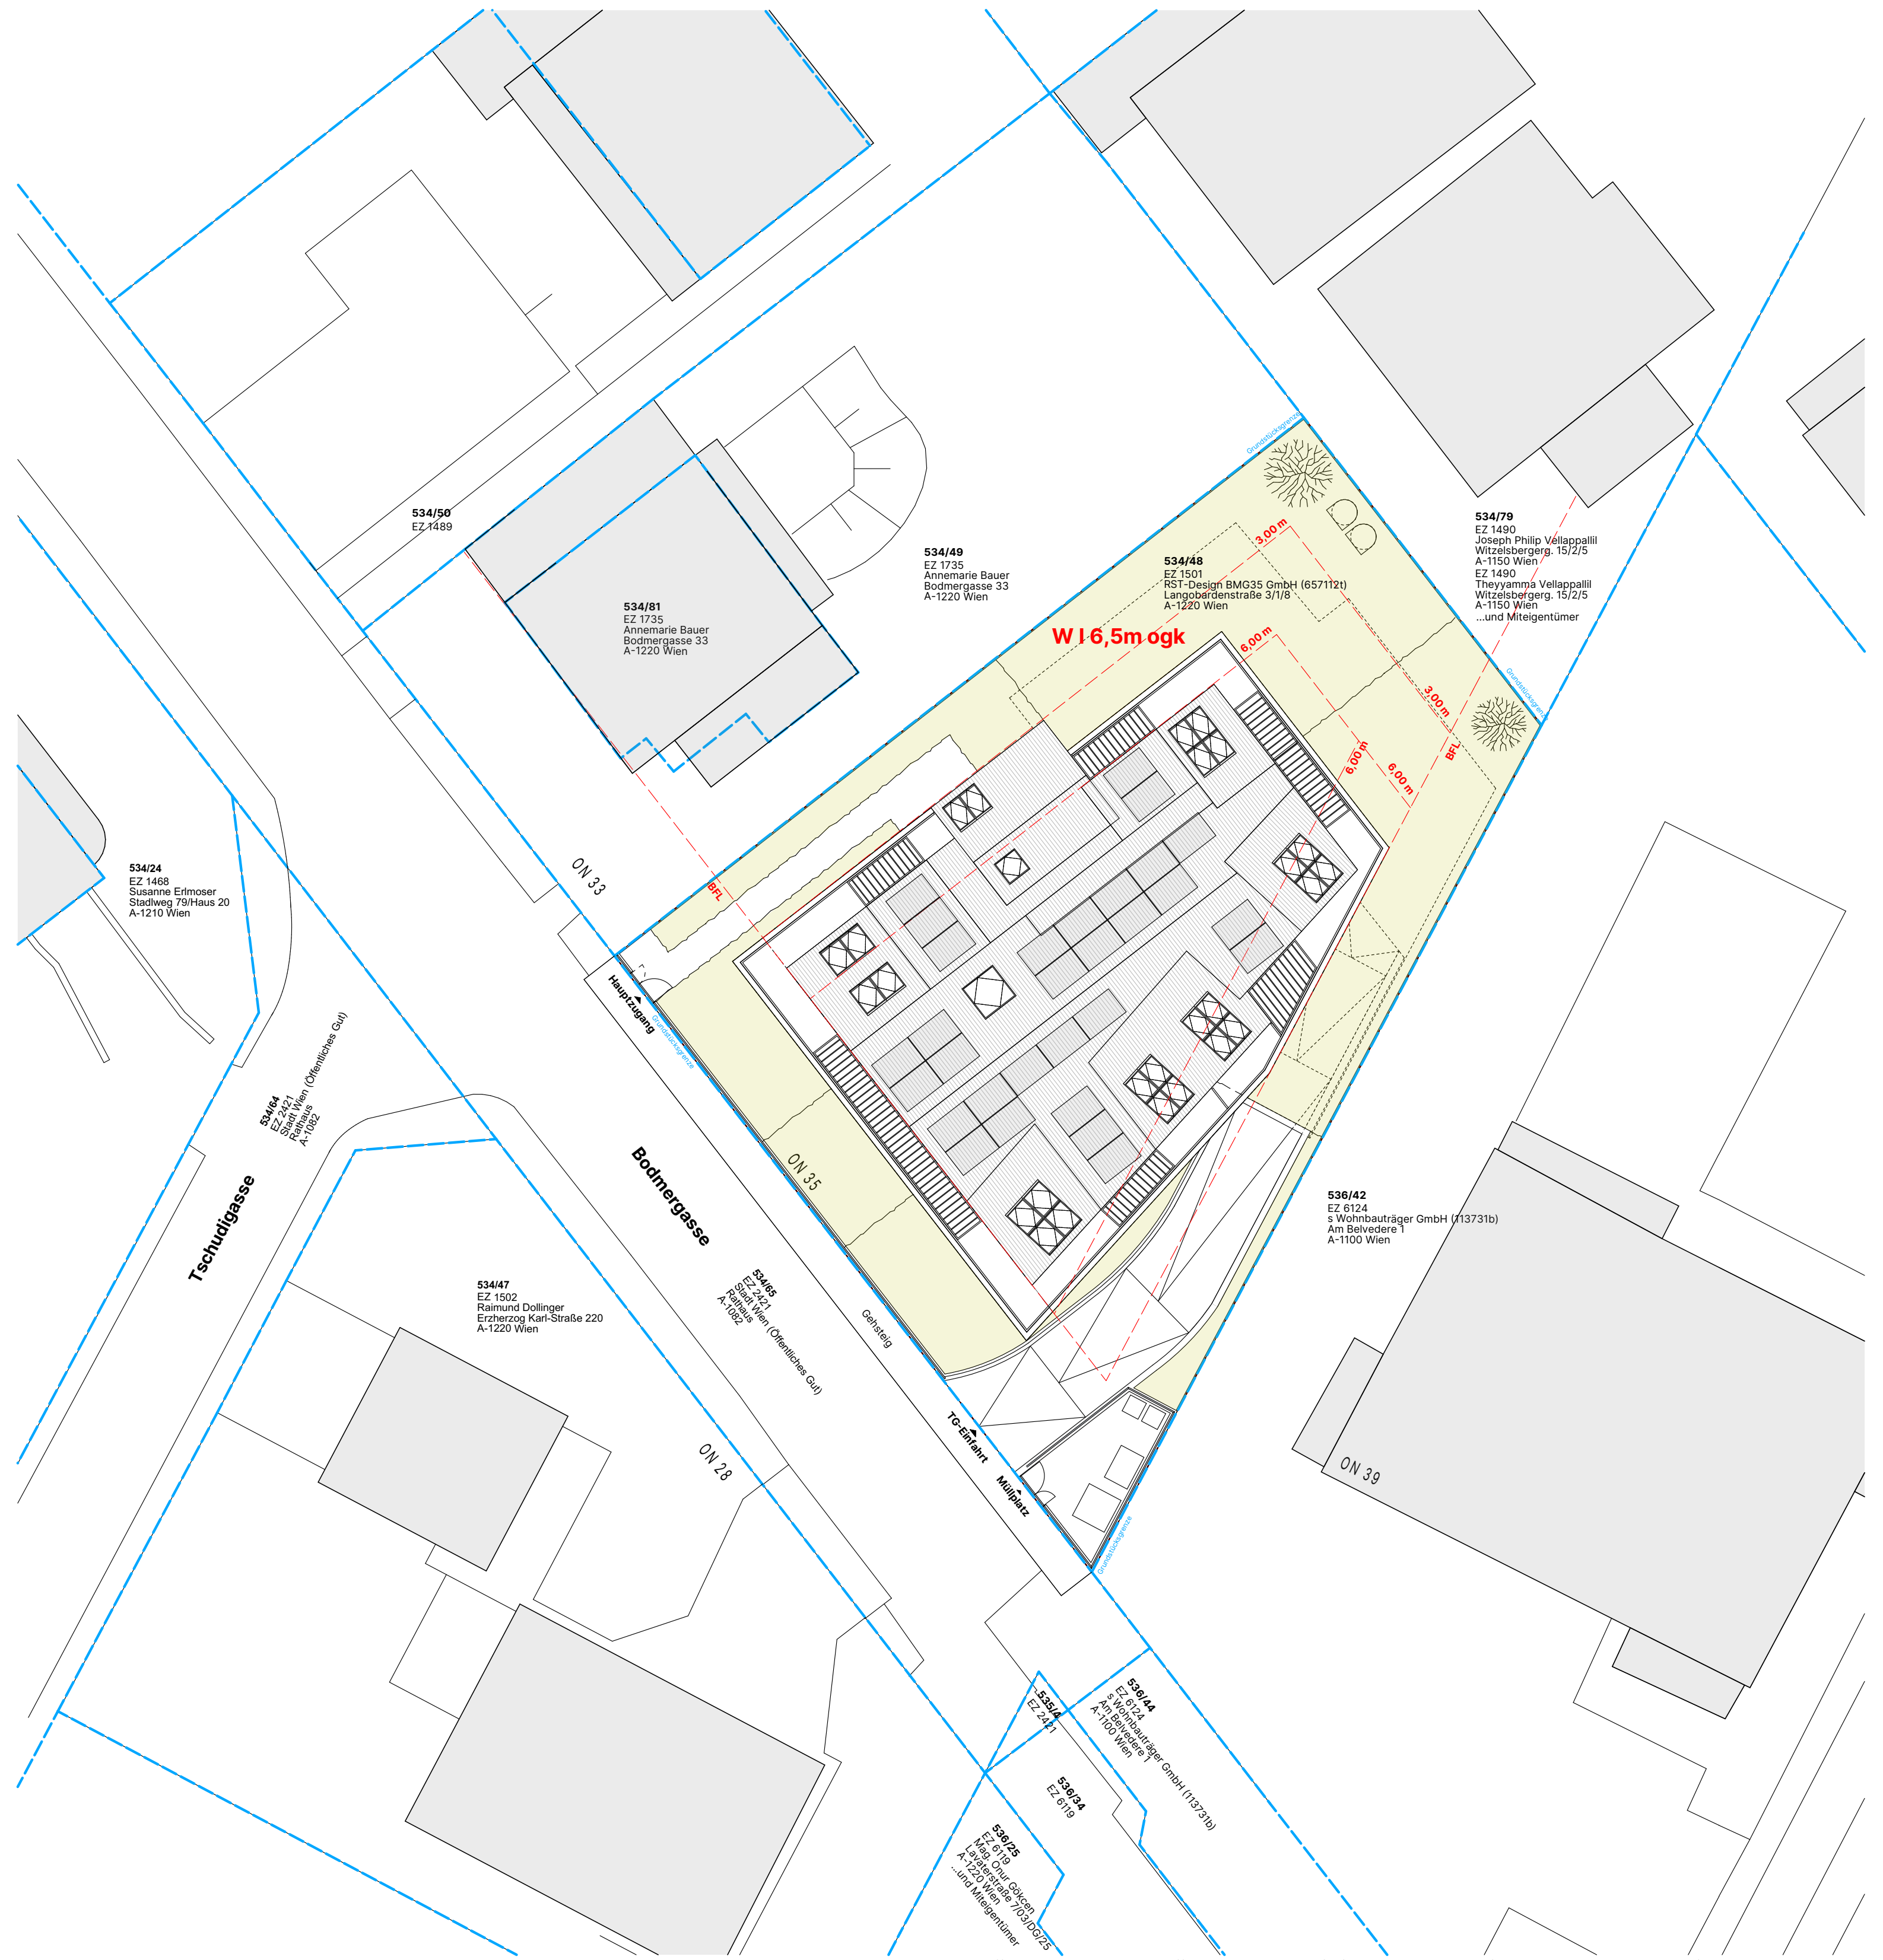

Alle Angaben gemäß Lage- und Höhenplan - Zivilgeometer Dipl.Ing. Zlatko Tokic - 11.09.2026

LAGEPLAN M 1:200

TOPOGRAFIE

TOP 01		
	Bad	3,26
	WoKü	17,26
	Zimmer	11,96
		32,48 m²
	Garten	47,15

TOP 02		
	Bad	3,25
	VR	4,14
	WoKü	15,99
	Zimmer	8,76
		32,14 m²
	Garten	24,61

TOP 03		
	Bad	2,86
	VR	8,23
	WC	1,35
	WoKü	17,58
	Zimmer	7,82
	Zimmer	8,76
		46,60 m²
	Garten	50,66

TOP 04		
	Bad	2,73
	WC	1,49
	WoKü	16,75
	Zimmer	9,61
		30,58 m²
	Garten	124,40

TOP 05		
	Bad	2,87
	WC	1,49
	WoKü	27,05
	Zimmer	8,02
	Zimmer	10,27
		49,70 m²
	Garten	106,73

TOP 06		
	Bad	3,26
	VR	4,93
	WoKü	24,17
	Zimmer	13,39
		45,75 m²
	Balkon	6,55

TOP 07		
	Bad	3,25
	VR	4,14
	WoKü	15,99
	Zimmer	11,91
		35,29 m²
	Loggia	3,36

TOP 08		
	Bad	2,86
	VR	8,08
	WC	1,35
	WoKü	26,35
	Zimmer	11,77
	Zimmer	11,91
		62,32 m²
	Balkon	6,13

TOP 09		
	Bad	2,73
	WC	1,49
	WoKü	20,82
	Zimmer	16,92
		41,96 m²
	Balkon	3,63

TOP 10		
	Bad	2,87
	WC	1,49
	WoKü	30,74
	Zimmer	8,02
	Zimmer	14,62
		57,74 m²
	Balkon	12,78

TOP 11		
	AR	48,97
	Bad	3,96
	Bad	14,49
	Flur	3,60
	Küche	23,41
	VR	6,13
	WC	1,55
	Wohnen	33,04
	WR	6,34
	Zimmer	7,60
	Zimmer	14,06
		163,15 m²
	Balkon	11,50 m²
	Terrasse	34,09 m²

TOP 12		
	AR	10,97
	Bad	2,73
	Küche	7,85
	WC	1,49
	Wohnen	8,97
	Zimmer	9,09
		41,10 m²
	Balkon	3,24 m²
	Terrasse	10,83 m²

TOP 13		
	AR	5,10
	Bad	3,61
	Bad	3,91
	Flur	10,53
	VR	5,87
	WoKü	22,99
	Zimmer	16,33
		68,34 m²
	Balkon	11,74
	Terrasse	4,34

	WNFL	**707,15 m²**

AUFBAUTEN

	Erdanliegendedecken		
ED01a	**erdanliegender Fußboden - UG**		
	Beschichtung (Bfl nach Erfordernis)		
	Bodenplatte lt. Statik, geglättet		0,3000 m
	Trennlage		
	Sauberkeitsschicht		0,1000 m
		Summe:	0,4000 m
ED01b	**erdanliegender Fußboden - UG**		
	Beschichtung (Bfl nach Erfordernis)		
	Bodenplatte lt. Statik in Gefälle (30-51 cm), geglättet		0,3000 m
	Trennlage		
	Sauberkeitsschicht		0,1000 m
		Summe:	0,4000 m
ED02	**Decke intensiv begrünt über UG**		
	Rasen / Bepflanzung		
	Substrat mind. 80 cm		
	Drainageschicht / Drainmatte gem. Freiraumplanung		
	Schutz- und Speichervlies, wasserableitend		
	XPS-G nach ÖNORM B6000		0,0500 m
	Feuchtigkeitsabdichtung		0,0100 m
	Stahlbetondecke lt. Statik in Gefälle (20-32 cm)		0,2000 m
		Summe:	0,2600 m
	Außendecken		
AD01	**Decke über Luftraum EG-OG1**		
	Bodenbelag lt. Architektur		0,0150 m
	Verbundabdichtung im Nassbereich		
	Heizestrich		0,0650 m
	PE-Folie		
	EPS-T nach ÖNORM B6000		0,0300 m
	Dampfsperre gemäß ÖNORM B3732		
	Schüttung gebunden		0,0400 m
	Stahlbetondecke lt. Statik		0,1800 m
	MW-PT		0,1600 m
	Kleber, Grundierung, Armierung, Dünnputz		0,0150 m
		Summe:	0,5050 m
AD02	**Balkon mit Isokorb - OG1**		
	Betonplatten		0,0400 m
	Stelzlager (6-13 cm)		0,1300 m
	Trittschallmatte punktuell		
	Flüssige Abdichtung, Broof(t1)		
	Stahlbetondecke lt. Statik in Gefälle (18-25 cm)		0,1800 m
	MW-PT		0,1600 m
	Kleber, Grundierung, Armierung, Dünnputz		0,0150 m
		Summe:	0,5250 m
AD03	**Balkon mit Isokorb - OG2**		
	Betonplatten		0,0400 m
	Stelzlager (3-15 cm)		0,0900 m
	Trittschallmatte punktuell		
	Abdichtung in Lagen sd < 500m, beschiefert, Broof(t1)		0,0100 m
	EPS W30 Plus Gefälledämmplatten, 2-14 cm		0,0800 m
	EPS W30 Plus Wärmedämmplatten		0,1000 m
	Dampfsperre min sd > 1500m		
	Stahlbetondecke lt. Statik		0,1800 m
	Spachtelung		
		Summe:	0,5000 m
AD04	**Terrasse - OG2**		
	Betonplatten		0,0400 m
	Stelzlager (3-15 cm)		0,0900 m
	Trittschallmatte punktuell		
	Abdichtung in Lagen sd < 500m, beschiefert, Broof(t1)		0,0100 m
	EPS W30 Plus Gefälledämmplatten, 2-14 cm		0,0800 m
	EPS W30 Plus Wärmedämmplatten		0,1000 m
	Dampfsperre min sd > 1500m		
	Stahlbetondecke lt. Statik		0,1800 m
	Spachtelung		
		Summe:	0,5000 m
	Dächer		
DD01	**Dachschräge Stahlbeton hinterlüftet - 45° Broof(t1)**		
	Blechdach		0,0100 m
	Trennlage		
	Vollholzschalung		0,0240 m
	Konterlattung - Hinterlüftung		0,0500 m
	Unterdeckbahn diffusionsoffen		
	Vollholzschalung		0,0240 m
	Vollholzsparen dazw. MW-W nach ÖNORM B6000		0,0600 m
	Vollholzsparen dazw. MW-W nach ÖNORM B6000		0,1400 m
	Dampfsperre min sd > 20m		
	Stahlbetondecke lt. Statik		0,2200 m
	Spachtelung		
		Summe:	0,5280 m
DD02	**Dachschräge Stahlbeton hinterlüftet - 5° Broof(t1)**		
	Blechdach		0,0100 m
	Trennlage		
	Vollholzschalung		0,0240 m
	Konterlattung - Hinterlüftung		0,0500 m
	Unterdeckbahn diffusionsoffen		
	Vollholzschalung		0,0240 m
	Vollholzsparen dazw. MW-W nach ÖNORM B6000		0,0600 m
	Vollholzsparen dazw. MW-W nach ÖNORM B6000		0,1400 m
	Dampfsperre min sd > 20m		
	Stahlbetondecke lt. Statik		0,2000 m
	Spachtelung		
		Summe:	0,5080 m
DD03	**Dachschräge Stahlbeton hinterlüftet - 5° Broof(t1)**		
	Blechdach		0,0100 m
	Trennlage		
	Vollholzschalung		0,0240 m
	Konterlattung - Hinterlüftung		0,0500 m
	Unterdeckbahn diffusionsoffen		
	Vollholzschalung		0,0240 m
	Vollholzsparen dazw. MW-W nach ÖNORM B6000		0,0600 m
	Vollholzsparen dazw. MW-W nach ÖNORM B6000		0,1400 m
	Dampfsperre min sd > 20m		
	Stahlbetondecke lt. Statik		0,1800 m
	Spachtelung		
		Summe:	0,4880 m
DD04	**Dachschräge Gaupe hinterlüftet - 5° Broof(t1)**		
	Blechdach		0,0100 m
	Trennlage		
	Vollholzschalung		0,0240 m
	Konterlattung - Hinterlüftung		0,0500 m
	Unterdeckbahn diffusionsoffen		
	Vollholzschalung		0,0240 m
	Vollholzsparen dazw. MW-W nach ÖNORM B6000		0,0600 m
	Vollholzsparen dazw. MW-W nach ÖNORM B6000		0,1400 m
	Dampfsperre min sd > 20m		
	Holzdecke KLH lt. Statik		0,1200 m
	Unterkonstruktion		0,0500 m
	2x GKF-Platten (1,50cm)		0,0300 m
		Summe:	0,5080 m
DD05	**Dachschräge Gaupe hinterlüftet - 5° Broof(t1)**		
	Blechdach		0,0100 m
	Trennlage		
	Vollholzschalung		0,0240 m
	Konterlattung - Hinterlüftung		0,0500 m
	Unterdeckbahn diffusionsoffen		
	Vollholzschalung		0,0240 m
	Vollholzsparen dazw. MW-W nach ÖNORM B6000		0,0600 m
	Vollholzsparen dazw. MW-W nach ÖNORM B6000		0,1400 m
	Dampfsperre min sd > 20m		
	Holzdecke KLH lt. Statik		0,1200 m
	Unterkonstruktion		0,0300 m
	2x GKF-Platten (1,50cm)		0,0300 m
		Summe:	0,4880 m
	Innendecken		
ID01	**Decke über UG /Garage**		
	Bodenbelag lt. Architektur		0,0150 m
	Verbundabdichtung im Nassbereich		
	Heizestrich		0,0650 m
	PE-Folie		
	EPS-T nach ÖNORM B6000		0,0300 m
	Dampfsperre gemäß ÖNORM B3732		
	Schüttung gebunden		0,0400 m
	Stahlbetondecke lt. Statik		0,2000 m
	Tektalan A2 SmartTec		0,1000 m
		Summe:	0,4500 m
ID02	**Trenndecke - Regelgeschoß**		
	Bodenbelag lt. Architektur		0,0150 m
	Verbundabdichtung im Nassbereich		
	Heizestrich		0,0650 m
	PE-Folie		
	EPS-T nach ÖNORM B6000		0,0300 m
	Dampfsperre gemäß ÖNORM B3732		
	Schüttung gebunden		0,0400 m
	Stahlbetondecke lt. Statik		0,1800 m
	Spachtelung		
		Summe:	0,3300 m
ID03	**Decke über OG2**		
	Bodenbelag lt. Architektur		0,0150 m
	Verbundabdichtung im Nassbereich		
	Heizestrich		0,0650 m
	PE-Folie		
	EPS-T nach ÖNORM B6000		0,0300 m
	Dampfsperre gemäß ÖNORM B3732		
	Stahlbetondecke lt. Statik		0,1800 m
	Spachtelung		
		Summe:	0,2900 m
	Außenwände		
AW01	**Außenwand WDVS (tragend)**		
	Kleber, Grundierung, Armierung, Dünnputz		0,0150 m
	EPS-F PLUS		0,1400 m
	Stahlbetonwand lt. Statik		0,1800 m
	Spachtelung		
		Summe:	0,3350 m
AW02	**Außenwand WDVS (tragend)**		
	Kleber, Grundierung, Armierung, Dünnputz		0,0150 m
	EPS-F PLUS		0,1400 m
	Stahlbetonwand lt. Statik		0,2200 m
	Spachtelung		
		Summe:	0,3750 m
AW03	**Außenwand Gaupe hinterlüftet**		
	Blechdach		0,0100 m
	Trennlage		
	Vollholzschalung		0,0240 m
	Konterlattung - Hinterlüftung		0,0500 m
	Unterdeckbahn diffusionsoffen		
	Vollholzschalung		0,0240 m
	Vollholzsparen dazw. MW-W nach ÖNORM B6000		0,1600 m
	Dampfsperre min sd > 20m		
	Holzwand KLH lt. Statik		0,1200 m
	2x GKF-Platten (1,50cm)		0,0300 m
		Summe:	0,4180 m
AW04	**erdanliegende Außenwand (tragend) - UG**		
	Noppenbahn		
	XPS TOP50 SF		0,0500 m
	Vertikale Abdichtung lt. ÖNORM B3692		
	Stahlbetonwand lt. Statik		0,3000 m
		Summe:	0,3500 m
AW05	**erdanliegende Wand - Tiefgarageneinfahrt**		
	Vertikale Abdichtung lt. ÖNORM B3692		
	Stahlbetonwand lt. Statik		0,2500 m
		Summe:	0,2500 m
	Innenwände		
IW01a	**Innenwand (tragend) - UG**		
	Stahlbetonwand lt. Statik		0,1800 m
		Summe:	0,1800 m
IW01b	**Innenwand (tragend) - Aufzugsschacht**		
	2x GKB/GKBi-Platten (1,25cm)		0,0250 m
	CW75 (freistehend) dazw. MW-W TW-KF50 nach ÖN B 6000		0,0750 m
	Stahlbetonwand lt. Statik		0,1800 m
		Summe:	0,2800 m
IW01c	**Innenwand (tragend) - UG**		
	Stahlbetonwand lt. Statik		0,2000 m
		Summe:	0,2000 m
IW01d	**Innenwand (tragend) - UG**		
	Stahlbetonwand lt. Statik		0,3000 m
		Summe:	0,3000 m
IW02	**Trennwand Wohnung/Gang u. Wohnung/Wohnung (tragend)**		
	GKB/GKBi-Platten (1,50cm)		0,0150 m
	CW50 dazw. MW-W TW-KF50 nach ÖN B 6000		0,0500 m
	Stahlbeton		0,1800 m
	Spachtelung		
		Summe:	0,2450 m
IW03	**Innenwand Leichtbau**		
	2x GKB/GKBi-Platten (1,25cm)		0,0250 m
	CW50 dazw. MW-W TW-KF50 nach ÖN B 6000		0,0500 m
	2x GKB/GKBi-Platten (1,25cm)		0,0250 m
		Summe:	0,1000 m
IW04	**Innenwand Leichtbau - anpassbarrer Wohnbau**		
	2x GKB/GKBi-Platten (1,25cm)		0,0250 m
	CW50 dazw. MW-W TW-KF50 nach ÖN B 6000		0,0500 m
	2x GKB/GKBi-Platten (1,25cm)		0,0250 m
		Summe:	0,1000 m
IW05	**Innenwand Leichtbau - Verteiler**		
	2x GKB/GKBi-Platten (1,25cm)		0,0250 m
	CW75 dazw. MW-W TW-KF50 nach ÖN B 6000		0,0750 m
	2x GKB/GKBi-Platten (1,25cm)		0,0250 m
		Summe:	0,1250 m
IW06	**Innenwand Leichtbau - Verteiler**		
	2x GKB/GKBi-Platten (1,25cm)		0,0250 m
	CW100 dazw. MW-W TW-KF50 nach ÖN B 6000		0,1000 m
	2x GKB/GKBi-Platten (1,25cm)		0,0250 m
		Summe:	0,1500 m
IW07a	**Schachtwand**		
	CW50 dazw. MW-W TW-KF50 nach ÖN B 6000		0,0500 m
	2x GKB/GKBi-Platten (1,25cm)		0,0250 m
		Summe:	0,0750 m
IW07b	**Schachtwand - Aufenthaltsraum**		
	CW50 dazw. MW-W TW-KF50 nach ÖN B 6000		0,0500 m
	3x GKB/GKBi-Platten (1,25cm)		0,0375 m
		Summe:	0,0875 m
IW08a	**Innenwand - Vorsatzschalle**		
	CW75 dazw. MW-W TW-KF50 nach ÖN B 6000		0,0750 m
	2x GKB/GKBi-Platten (1,25cm)		0,0250 m
		Summe:	0,1000 m
IW08b	**Innenwand - Vorsatzschalle**		
	CW (ins.175) dazw. MW-W TW-KF50 nach ÖN B 6000		0,1750 m
	2x GKB/GKBi-Platten (1,25cm)		0,0250 m
		Summe:	0,2000 m
IW09	**Schachtwand - EI60**		
	CW50 dazw. MW-W TW-KF50 nach ÖN B 6000		0,0500 m
	2x GKF-Platten (1,50cm)		0,0300 m
		Summe:	0,0800 m

Wohngebäude der GK4 mit 4 oberirdischen Geschoßen und einem Fluchtniveau von ca. 8,1m

Treppenhaus der GK 4 gem. Tab. 2a der OIB-RL 2 mit 1m² Rauchabzugsöffnung an oberster Stelle gemäß TRVB 111 S.

Bei Außenwänden mit WDVS im Sockel in EPS mit einer Dämmstoffdicke > 10cm wird im Sturzbereich von Fenstern und Fenstertüren ein Brandschutzschott aus Mineralwolle mit einem seitlichen Übergriff von 30 cm und einer Höhe von 20 oder in jedem Geschoß ein umlaufendes Brandschutzschott aus Mineralwolle mit einer Höhe von 20cm ausgeführt.
Installationsschächte als Typ A oder B gemäß TRVB 110 B, im Anschluss an gesicherte Fluchtwege nur Typ A. Revisionstüren Schachttyp A zu Gängen bzw. Bauteil Stiege 2 in EI_2 30 (sonstige Bereiche Stiege 1 in EI_2 90) vierseitig angeschlagen, Durchbrüche werden EI 90 und A2 abgeschottet.

Leitungsführungen, Durchbrüche und Abschottungen gemäß TRVB 110 B.

Versperrbare Türen im Verlauf von Fluchtwegen für mehr als 40 Personen (Wohnbereiche) werden mit Notausgangsbeschlägen gem. ÖNORM EN 179 ausgestattet

Löschhilfe mit tragbaren Feuerlöschern gem. TRVB 124 F.

Alle baulichen Anlagen werden mit einer Blitzschutzanlage gem. ÖVE/ÖNORM 62305 ausgestattet.

Unterirdische innenliegende Räume werden mit einer Rauchableitungsöffnung über den Gang direkt ins Freie mit geometrischer Öffnungsfläche von 0,5m² ausgeführt.

Feuerwehraufstellflächen gem. TRVB 134 F.

LEGENDE

🟩	Stahlbeton
🟩	Beton
🟪	Dämmung
🟧	Gipskarton
🟦	Stahl
- - - -	Grundstücksgrenze
— — —	Widmungsgrenze
— - —	Fluchtweg
======	Brandabschnitt
- - - - -	Trennbauteil
±0,00	Höhenangabe Fertigmaß
-0,16	Höhenangabe Rohbaumaß
±0,00	OK Fertigbau
+2,60	UK Fertigbau
-0,16	OK Rohbau
+2,70	UK Rohbau
FBDB 20/20	Fußbodendurchbruch
DDB 20/20	Deckendurchbruch
W01	Aufbau
703	Detail

WDB	Wanddurchbruch	RAR	Regenabfallrohr
DDB	Deckendurchbruch	GelH	Geländerhöhe
FBDB	Fussbodendurchbruch	BA	Bodenablauf
OK	Oberkante	DN	Nenndurchmesser
UK	Unterkante	PT	Putztürchen
FBOK	Fussbodenoberkante (Fertigmass)	PS	Putzstück
RBOK	Fussbodenoberkante (Rohbaumass)	SEL	Strangentlüftung
FDUK/FDOK	Deckenunter/oberkante (Fertigmass)	FR	Fallrohr
RDUK/RDOK	Deckenunter/oberkante (Rohbaumass)	KS	Kanalsohle
FPH	Parapethöhe (Fertigmass)	$EI_2$30	Brandschutztüre m.A.d. Brandwiderstandsklasse
RPH	Parapethöhe (Rohbaumass)	T30	Bestands-Brandschutztüre m.A.d. Brandwiderstandskl.
STUK	Sturzunterkante	EI30	Brandschutzwand m.A.d. Brandwiderstandsklasse
STL	Stocklichte	R30/REI30	Träger und Stütze/Verkleid. m.A.d. Brandwiderstandskl.
FOK	Fundamentoberkante	NA	Notausgang
FUK	Fundamentunterkante	DBA	Druckbelüftungsanlage
UZ	Unterzug	BSK	Brandsschutzklappe
RH	Raumhöhe (Fertigmass)	RA	Rauchabzug
FTH	Traufhöhe (Fertigmass)	BRE	Brandrauchentlüftung
FFH	Firsthöhe (Fertigmass)	RS	Rauchschürze
WOK	Wandoberkante	LÜ	Lüftung
WUK	Wandunterkante	ABL	Abluft
LiKu	Lichtkuppel	ZUL	Zuluft
LB	Lichtband	VSG	Verbund-Sicherheitsglas
		ESG	Einscheiben-Sicherheitsglas

ALLGEMEINE HINWEISE

Bei dieser Zeichnung bzw. Ausarbeitung handelt es sich um geistiges Eigentum des:der Planenden, welches somit gesetzlich geschützt ist. Jegliche Vervielfältigung, Veröffentlichung, Überarbeitung, Benutzung oder Weitergabe an Dritte in Verbindung mit einem anderen Projekt oder einer anderen Arbeit, bedarf der ausdrücklichen schriftlichen Zustimmung des:der Planenden.

Die Naturmaße sind zu nehmen und die Koten zu prüfen! Abweichungen von dargestellten Inhalten oder schriftlichen Vereinbarungen sind mit dem:der Planenden sowie der Bauleitung vor Bauausführung umgehend schriftlich mitzuteilen.

Dieser Plan ist vom ausführenden Unternehmen mit den Plänen der Tragwerksplanung und denen der Fachplanung (HKLS, Elektro, Brandschutz usw.) auf Übereinstimmungen und Vollständigkeit zu überprüfen! Etwaige Maßfehler und Unklarheiten sind dem:der Planverfasser:in sofort schriftlich mitzuteilen und abzuklären!

Die relevanten statischen Angaben sind den Statik-Plänen zu entnehmen.
Die relevanten HKLS- und Elektroangaben sind den HKLS- und Elektroplänen zu entnehmen. Die zugehörigen TGA-Bauangaben sind ebenso den jeweils zugeordneten Plänen zu entnehmen.
Erforderliche Durchführungen sind den HKLS- und Elektroplänen zu entnehmen.
Decken- und Wandaufbauten lt. Baukatalog Bauphysik.

Darstellung der Möblierung dient lediglich zur besseren Lesbarkeit der Pläne. Die Tatsächliche Möbelaufstellung kann von der planlichen Darstellung abweichen.

Alle Längenmaße sind in Zentimeter angegeben. Kote Parapet und Sturz bezieht sich auf FBOK. Alle anderen Höhenkoten beziehen sich auf Projektnull.
Fenstermaße = Architekturlichte, Türmaße = Öffnungslichte.
Höhe von Handläufen bei Stiegen 90 cm, Höhe von Absturzsicherungen mind. 100 bzw. 110 cm.

Verglasung als Absturzsicherung wird bis H=110 cm in VSG ausgeführt. Raumhohe Verglasung wird bis H=150 cm in ESG ausgeführt.

Sämtliche Rigole, Gullys usw. sind gegen Frostschäden (z. B. mit Begleitheizung) zu schützen.

Die Darstellung der Brandabschnitte und Hydranten in den Bauplänen ist symbolisch. Alle Schächte, Durchbrüche, Schlitze usw. müssen wieder verschlossen werden, sofern sie durch Brandabschnitte führen in EI90 bzw. REI90 gemäß Schachtrichtlinie (EI90). Ausführung Brandschutz lt. Brandschutzkonzept.

Schadensfolgeklasse CC2 nach ÖNORM B 1990-1

Naturmaße nehmen! Koten prüfen!

PARIE
A B C D E F

EINREICHPLAN

BAUVORHABEN
Wohnhaus Bodmergasse

ADRESSE
Bodmergasse 35, 1220 Wien

PLANINHALT
Lageplan, Baubeschreibung, Aufbauten, Flächenliste

PLANVERFASSER
sipa
sipa Architektur, Davor Podbregar ZT e.U.
Elizabeth-T.-Spira-Promenade 2/7 | A-1030 Wien
www.sipa-arch.com | info@sipa-arch.com | +43 664 1072040

LANGSTEMPEL

BAUWERBER	BAUFÜHRER
RST-Design BMG35 GmbH Am Bahnhof 2, 1220 Wien office@rst-design.com | +43 676 6902502	**TBD** TBD TBD | TBD
GRUNDEIGENTÜMER	**BAUBEHÖRDE**
RST-Design BMG35 GmbH Am Bahnhof 2, 1220 Wien office@rst-design.com | +43 676 6902502	**MA37 - Gebietsgruppe Ost** Dresdner Straße 82, 1200 Wien ost@ma37.wien.gv.at | +43 1 4000 37300

KATASTRALGEMEINDE	EINLAGEZAHL	GRUNDSTÜCK	PROJEKTNULL
01651 - Aspern	**1501**	**534/48**	**±0,00=2,15 ü.WN/158,83 ü.Adria**
PROJEKTNUMMER	PROJEKTPHASE	GEZEICHNET	PLANGRÖSSE
2607	**EINREICHUNG**	**DP**	**1260 × 841 MM**
PLANNUMMER	MASSSTAB	PLANSTAND	INDEX
2607.04.01	**1:1, 1:200**	**16.10.2026**	**-**