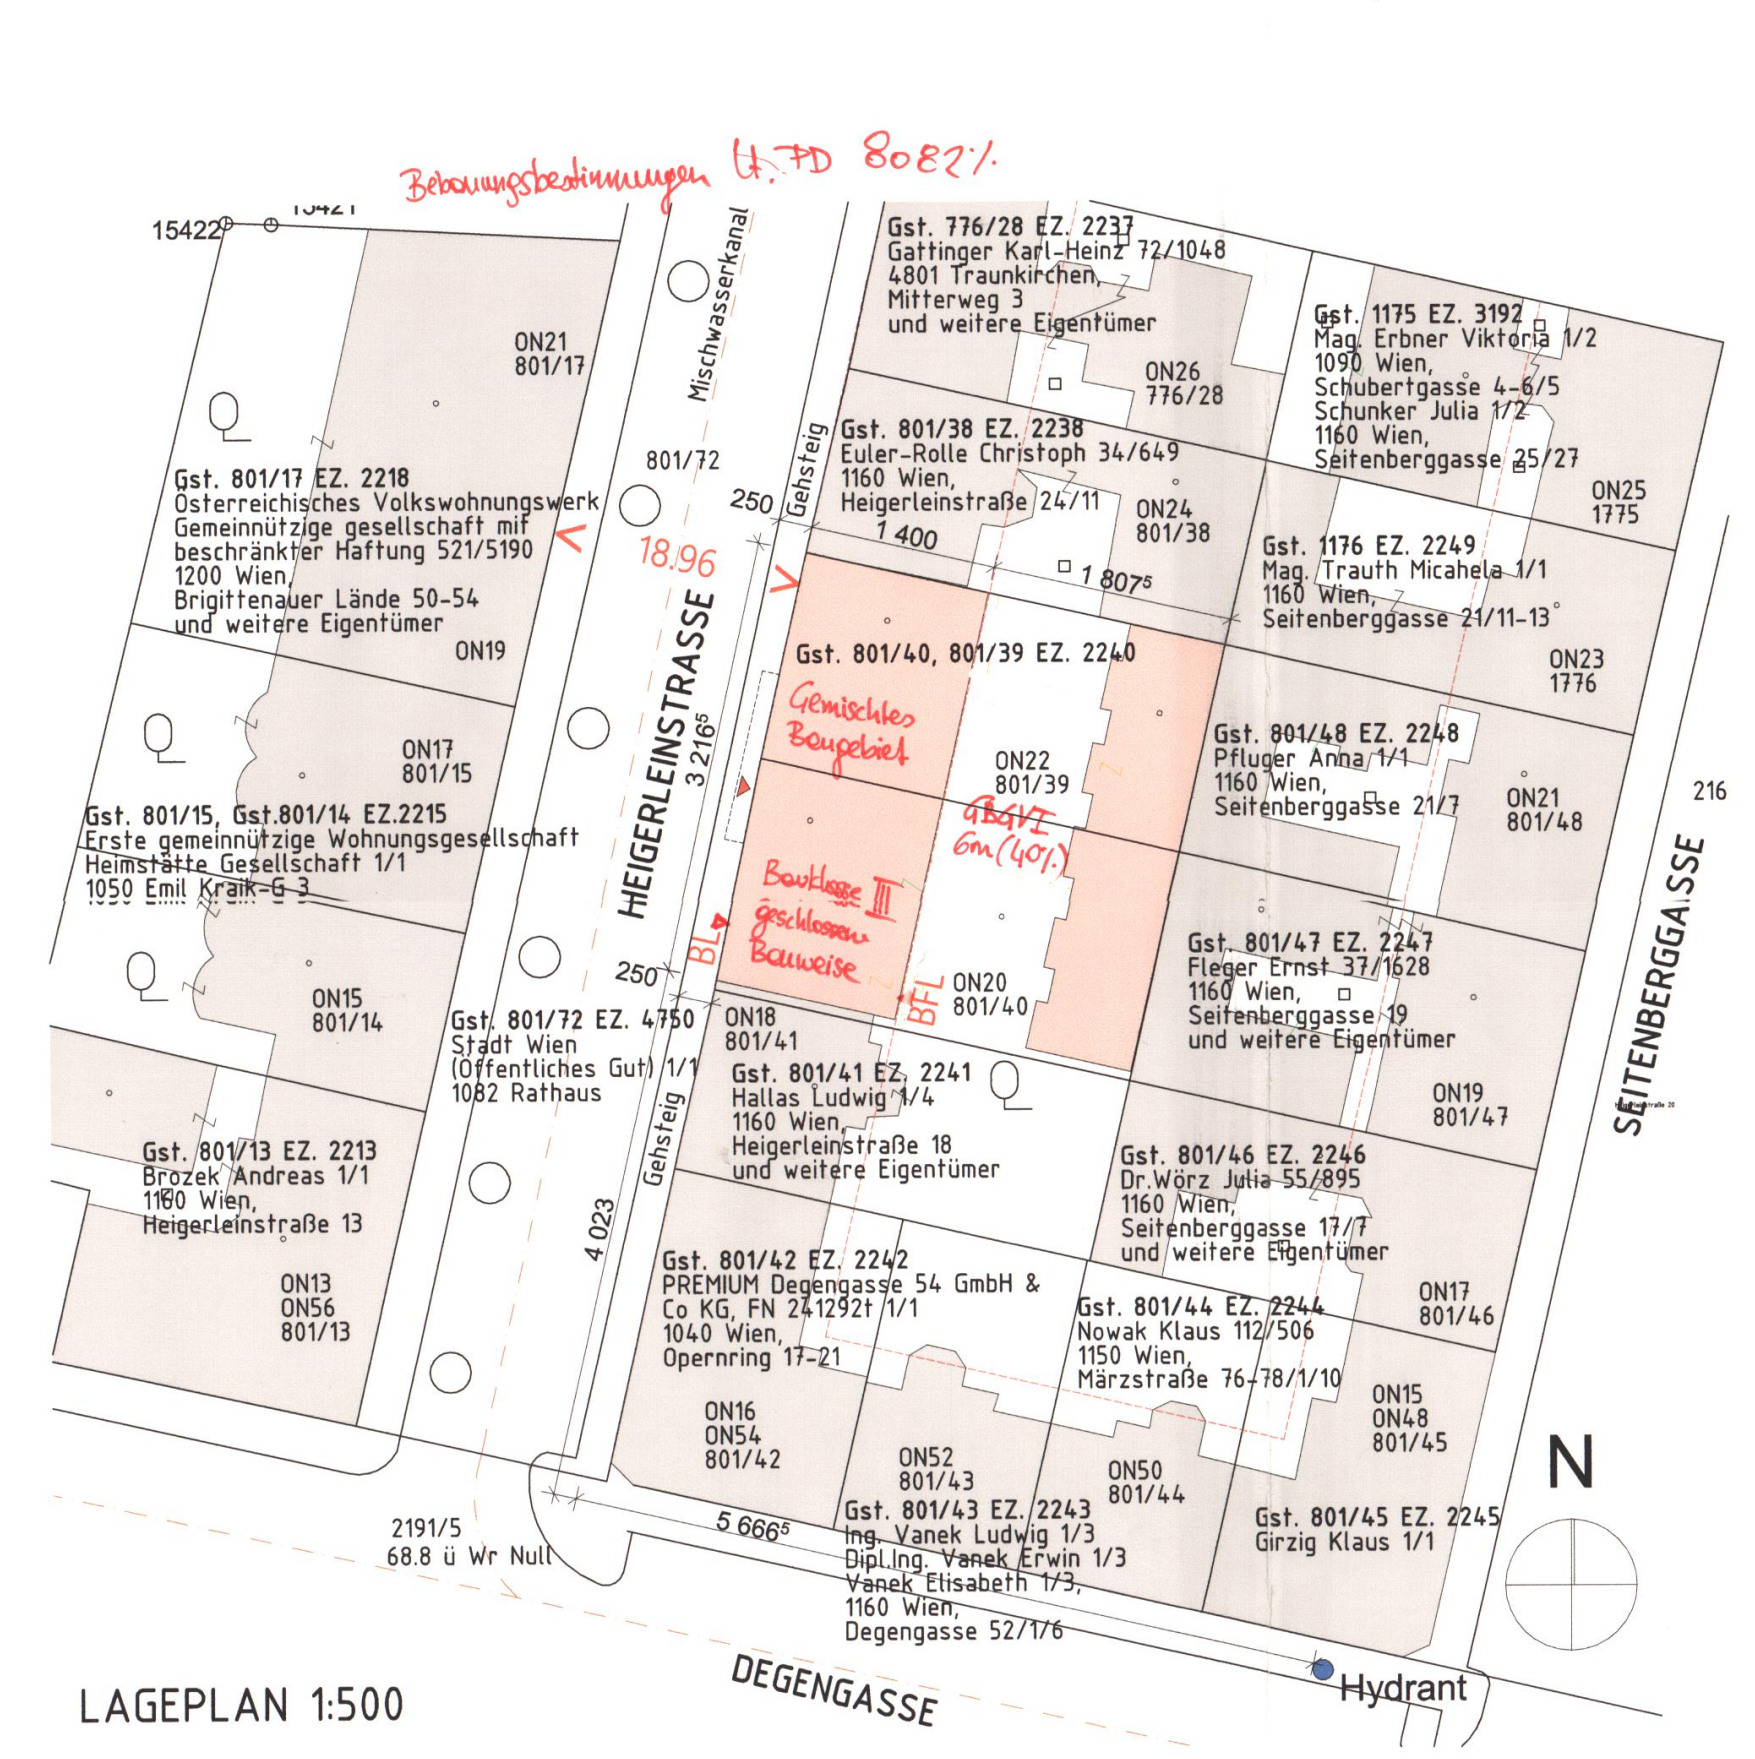

LAGEPLAN 1:500

ANRAINER:

Gst. 801/13 EZ. 2213
Brozek Andreas 1/1
1160 Wien,
Heigerleinstraße 13

Gst. 801/15, Gst.801/14 EZ.2215
Erste gemeinnützige Wohnungsgesellschaft
Heimstätte Gesellschaft 1/1
1050 Emil Kraik-G 3

Gst. 801/17 EZ. 2218
Österreichisches Volkswohnungswerk
Gemeinnützige Gesellschaft mit
beschränkter Haftung 521/5190
1200 Wien,
Brigittenauer Lände 50-54
und weitere Eigentümer siehe
Grundbuchsauszug (Beilage)

Gst. 801/72 EZ. 4750
Stadt Wien (Öffentliches Gut) 1/1
1082 Rathaus

Gst. 776/28 EZ. 2237
Gattinger Karl-Heinz 72/1048
4801 Traunkirchen,
Mitterweg 3
und weitere Eigentümer

Gst. 801/38 EZ. 2238
Euler-Rolle Christoph 34/649
1160 Wien,
Heigerleinstraße 24/11

Gst. 801/39, Gst. 801/40 EZ. 2238
Simony Immobilien GmbH & Co Phi KG (453696a)
1/1
1180 Wien,
Symonygasse 12

Gst. 801/40 EZ. 2240
Simony Immobilien GmbH & Co Phi KG (453696a)
1/1
1180 Wien,
Symonygasse 12

Gst. 801/41 EZ. 2241
Hallas Ludwig 1/4
1160 Wien,
Heigerleinstraße 18
Hallas Ludwig 1/4
1160 Wien,
Heigerleinstraße 18/5
Mag.Schlechta Andrea 1/4
1130 Wien,
Geylinggasse 27/18
Dr. Wernhart-Hallas Eisabeth
1130 Wien,
Hietzinger Hauptstraße 124/5

Gst. 801/42 EZ. 2242
PREMIUM Degengasse 54 GmbH &
Co KG, FN 241292t 1/1
1040 Wien,
Opernring 17-21

Gst. 801/43 EZ. 2243
Ing. Vanek Ludwig 1/3
Dipl.Ing. Vanek Erwin 1/3
Vanek Elisabeth 1/3,
1160 Wien,
Degengasse 52/1/6

Gst. 801/45 EZ. 2245
Girzig Klaus 1/1

Gst. 801/44 EZ. 2244
Nowak Klaus 112/506
1150 Wien,
Märzstraße 76-78/1/10

Gst. 801/46 EZ. 2246
Wörz Julia, Dr.
1160 Wien, Seitenberggasse 17/7

und weitere Eigentümer siehe
Grundbuchsauszug (Beilage)

Gst. 801/47 EZ. 2247
Fleger Ernst 37/1628
1160 Wien,
Seitenberggasse 19
und weitere Eigentümer siehe
Grundbuchsauszug (Beilage)

Gst. 801/48 EZ. 2248
Pfluger Anna 1/1
1160 Wien,
Seitenberggasse 21/7

Gst. 1176 EZ. 2249
Mag. Trauth Micahela 1/1
1160 Wien,
Seitenberggasse 21/11-13

Gst. 1175 EZ. 3192
Mag. Erbner Viktoria 1/2
1090 Wien,
Schubertgasse 4-6/5
Schunker Julia 1/2
1160 Wien,
Seitenberggasse 25/27

LEGENDE:

⬜	BESTAND		SCHMUTZWASSER	UZ	UNTERZUG
🟨	ABBRUCH		REGENWASSER	ÜZ	ÜBERZUG
🟥	NEUBAU		WASSER	AR	ABFALLROHR
			HEIZUNG	RR	REGENROHR
🟩	STAHLBETON		STROM	RSK	REGENSINKKASTEN
🟩	UNBEWEHRTER BETON		GAS	PH	PARAPETHÖHE
🟥	MAUERWERK		FERNWÄRME	STUK	STURZUNTERKANTE
🟫	HOLZ			DL	DURCHGANGSLICHTE
🟪	DÄMMUNG (HART)	DFF	DACHFLÄCHENFENSTER	OK	OBERKANTE
🟧	DÄMMUNG (WEICH)	LK	LICHTKUPPEL	UK	UNTERKANTE
▨	STAHL	VSG	VERBUND-SICHERKEITSGLAS	FOK	FUSSBODENOBERKANTE
🟦	GLAS	ESG	EINSCHEIBEN-SICHERHEITSGLAS	WD	WANDDURCHBRUCH
🟧	GIPSKARTON	BRE	BRANDRAUCHENTLÜFTUNG	DD	DECKENDURCHBRUCH

- LÜFTUNGEN DURCH FREMDE BRANDABSCHNITTE EI90 UND A2 UMMANTELT
- RESTRÄUME IM DACHGESCHOSS EI60 VON INNEN 2x GKF
- WOHNUNGSEINGANGSTÜREN AUSFÜHRUNG IN $EI_2 30$ IN WÄNDEN WELCHE ZUM STGH DURCH EINE E30-C TÜRE GETRENNTS SIND, ALLE ANDEREN WOHNUNGSEINGANGSTÜREN IN $EI_2 30$-C
- AUSWECHSLUNGEN SIND IN REI90 UND A2 AUSZUFÜHREN
- WÄRMEVERSORGUNG MITTELS 2 SOLE/WASSER WÄRMEPUMPEN, DIE NOTWENDIGE ENERGIE WIRD ÜBER TIEFENBOHRUNGEN BEREITGESTELLT.
- PHOTOVOLTAIKANLAGE IST AM FLACHDACH VORDERTRAKT AUFGESTÄNDERT
- ALLE AUSKRAGENDEN TEILE THERMISCH GETRENNT, DÄMMUNG A2
- AUSSENLIEGENDE BAUTEILE SIND THERMISCH ZU TRENNEN, DÄMMUNGEN AN GRUNDSTÜCKSGRNEZEN A2
- INTERNE TREPPEN SIND ELASTISCH ZU LAGERN
- INSTALLATIONSSCHÄCHTE IM TREPPENBERICH SIND LT. TRVB110 AUSZUFÜHREN
- BRANDVERHALTEN VON BAUPRODUKTEN GEMÄSS DEN BESTIMMUNGEN DER OIB- RICHTLINIE 2, TABELLE 1a(GK5<6 OBERIRDISCHE GESCHOSSE) SOWIE OIB-RICHTLINIE 2.2, PKT.5.2
- ALLE INNENLIEGENDEN BÄDER UND WC's LÜFTUNG ÜBER DACH
- FÜR JEDE WOHNUNG IST EIN EINLAGERUNGSRAUM VORHANDEN
- IN JEDER WOHNUNG IST EINE GEEIGNETE AUFSTELLMÖGLICHKEIT UND EIN ANSCHLUSS FÜR EINE WASCHMASCHINE UND EINE MASCHINELLE TROCKENEINRICHTUNG VORGESEHEN.
- NIEDERSCHLAGSWÄSSER UND FÄKALWÄSSER WERDEN IN DEN ÖFFENTLICHEN KANAL GELEITET
- STIEGEN UND GÄNGE KUNSTSTEINBELAG, BELAG MÜLLRAUM UND GARAGE MIND. Bfl
- GEMÄSS OIB RICHTLINIE 2, ABSATZ 3, PUNKT 11 - UNVERNETZTE RAUCHWARNMELDER IN ALLEN AUFENTHALTSRÄUMEN (AUSGEN. KÜCHEN, BEI WOHNKÜ. NICHT IM KOCHBEREICH) SOWIE BEI GÄNGEN ÜBER DIE FLUCHTWEGE VON AUFENTHALTSR. FÜHREN
- SCHADENSFOLGEKLASSE CC2 nach ÖNORM EN 1090-2 Tab. B3
- NÄCHSTE HYDRANT BIS GRUNDGRENZE: ca.115m<150m
- ALLE INNENLIEGENDE RÄUME SIND MECHANISCH ENTLÜFTET
- SCHÄCHTE WERDEN GEMÄSS WIENER INSTALLATIONSRICHTLINIE SCHACHTTYP A AUSGEFÜHRT
- AUFZUGSSCHÄCHTE SIND MIT MIND 2,5% DES SCHACHTQUERSCHNITTS ENTLÜFTET.
- FLUCHTWEGS UND ORIENTIERUNGSBELEUCHTUNG GEMÄß DEN BESTIMMUNGEN DER TRVB 102E
- DRUCKBELÜFTUNGSANLAGE GEMÄSS DEN BESTIMMUNGEN DER TRVB 112S (AUFENTHALTSKONZEPT)- AUSLÖSUNG DBA AUTOMATISCH ÜBER RAUCHMELDER ODER MANUELL MITTELS TASTER.
- FENSTER: $U_w=0{,}78W/m^2K$; $R_w=41dB$; $g=0{,}5$; $F_c=0{,}07$

± 0.00 ENTSPRICHT 70,2M ÜBER WIENER NULL

EINREICHPLAN

DOLLFUSS ARCHITEKT

PLANINHALT:
GRUNDRISSE, LAGEPLAN

Parie A [✓ B] C D E F G H I J K
Nr. [✓ 1] 2 3 4 5 6 7

BAUVORHABEN:

1160 Wien, Heigerleinstrasse 20 und 22
NEUBAU EINES MEHRFAMILIENWOHNHAUSES MIT 48 WOHNUNGEN UND EINEM REIHENHAUS (BEHERBERGUNGSSTÄTTE BESTEHEND AUS 5 ZIMMEREINHEITEN MIT INSGESAMT 10 BETTEN)
Heigerleinstraße 20-22
1160 Wien-Ottakring

GRUNDSTÜCKSNUMMER	801/39, 801/40
EINLAGEZAHL	2240
KATASTRALGEMEINDE	01405 Ottakring

GRUNDEIGENTÜMER/BAUWERBER
Simony Immobilien GmbH&Co Phi KG
Simonygasse 12
1180 Wien
PER VOLLMACHT, siehe PLANVERFASSER

BEHÖRDE **BAUFÜHRER**

Magistrat der Stadt Wien
Magistratsabteilung 37 - Baupolizei
Gebietsgruppe West, großvolumige Bauvorhaben
MA37 BAUPOLIZEI SICHER BAUEN
Stadt Wien
Zl.: MA37/1091355-2017-1
Hierauf bezieht sich der Bescheid
Für den Abteilungsleiter:
Dipl.-Ing. Weingartner
Wien, 04.01.2019

PLANVERFASSER

ARCHITEKT
DIPL.ING. GERHARD DOLLFUSS
STAATLICH BEFUGTER U. BEEIDETER ZIVILTECHNIKER
3240 MANK, BAHNHOFSTRASSE 4/4
0676/9490946 · office@dollfuss.eu

PLANINHALT	GRUNDRISSE, LAGEPLAN	
MAßSTAB	1:100,1:500	
PLANDATUM	15.12.2017	DRUCKDATUM 30.07.2018
PLANNUMMER	A2017-04-101	
PROJEKT	1160 Wien, Heigerleinstrasse 20 und 22	
CAD-FILE	A2017-04 ERPL Heigerlein 20180705.pln	

DIESER PLAN IST GEISTIGES EIGENTUM DES PLANVERFASSERS UND DARF NUR MIT DESSEN ZUSTIMMUNG WEITERGEGEBEN UND VERVIELFÄLTIGT WERDEN !
DAS VORLIEGENDE PLANDOKUMENT DIENT ALS GRUNDLAGE FÜR DIE BEHÖRDLICHE GENEHMIGUNG lt. WRBO UND STELLT KEINEN AUSFÜHRUNGSPLAN DAR!

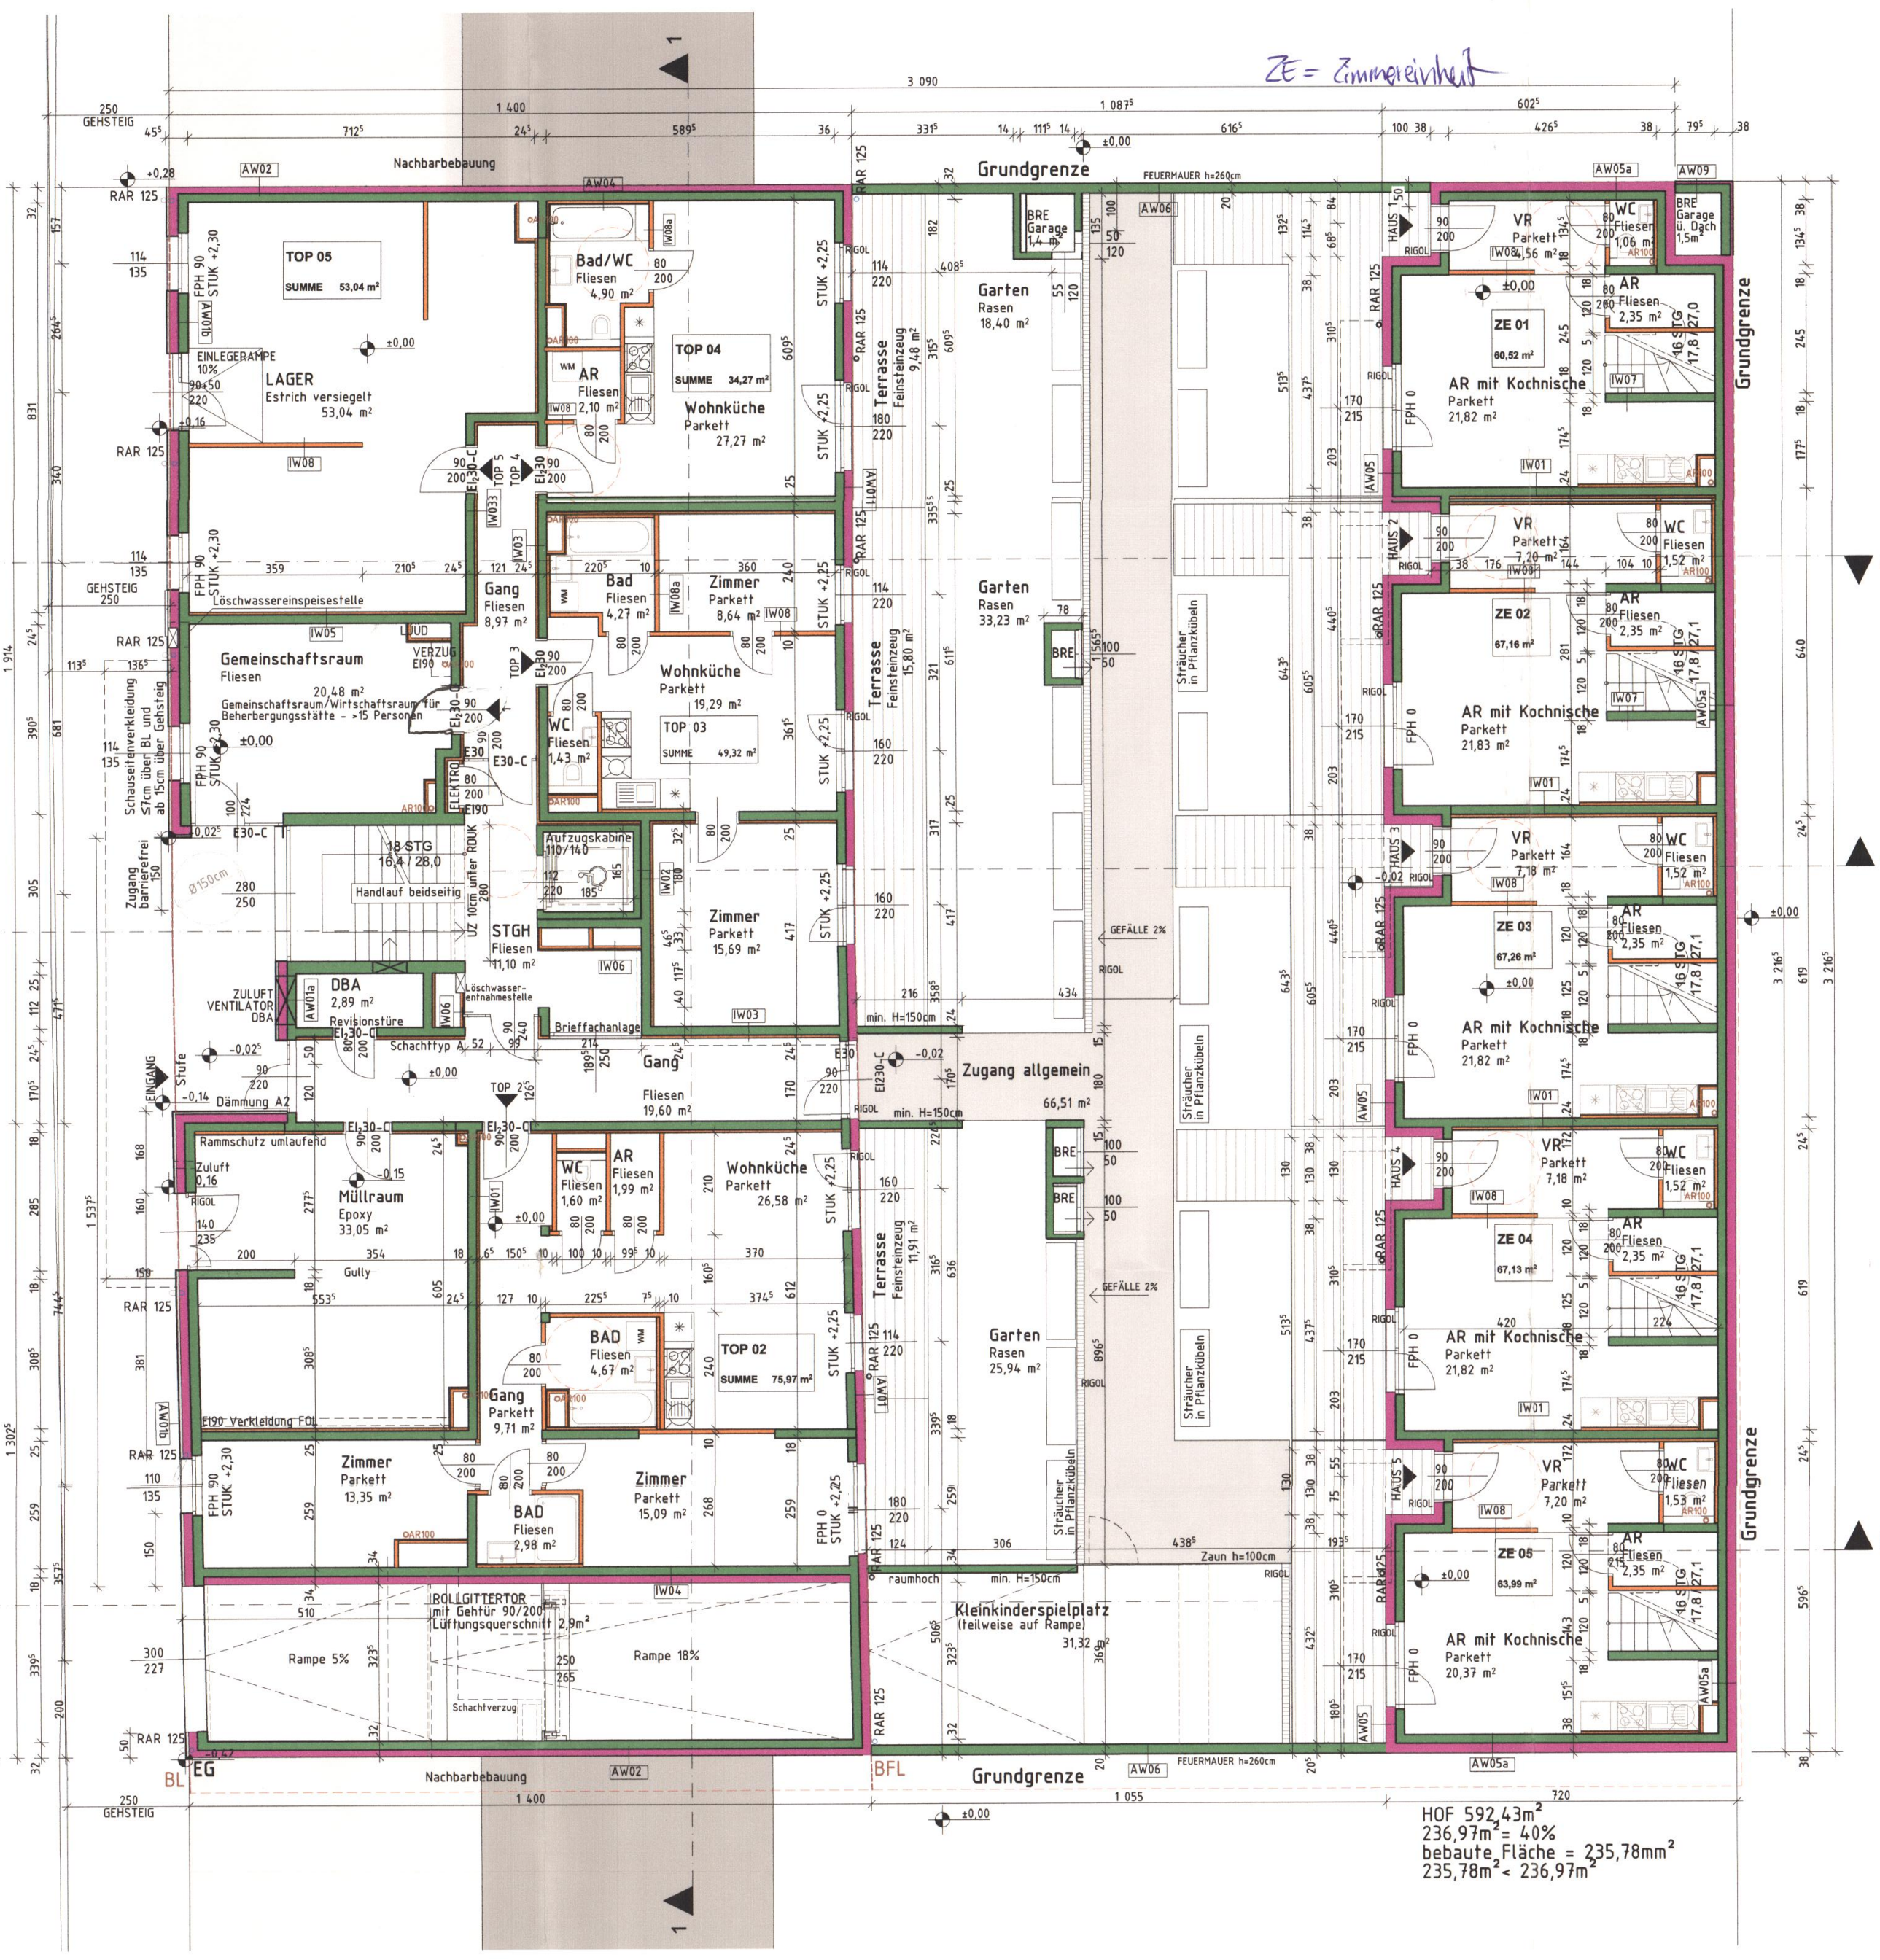

ERDGESCHOSS 1:100

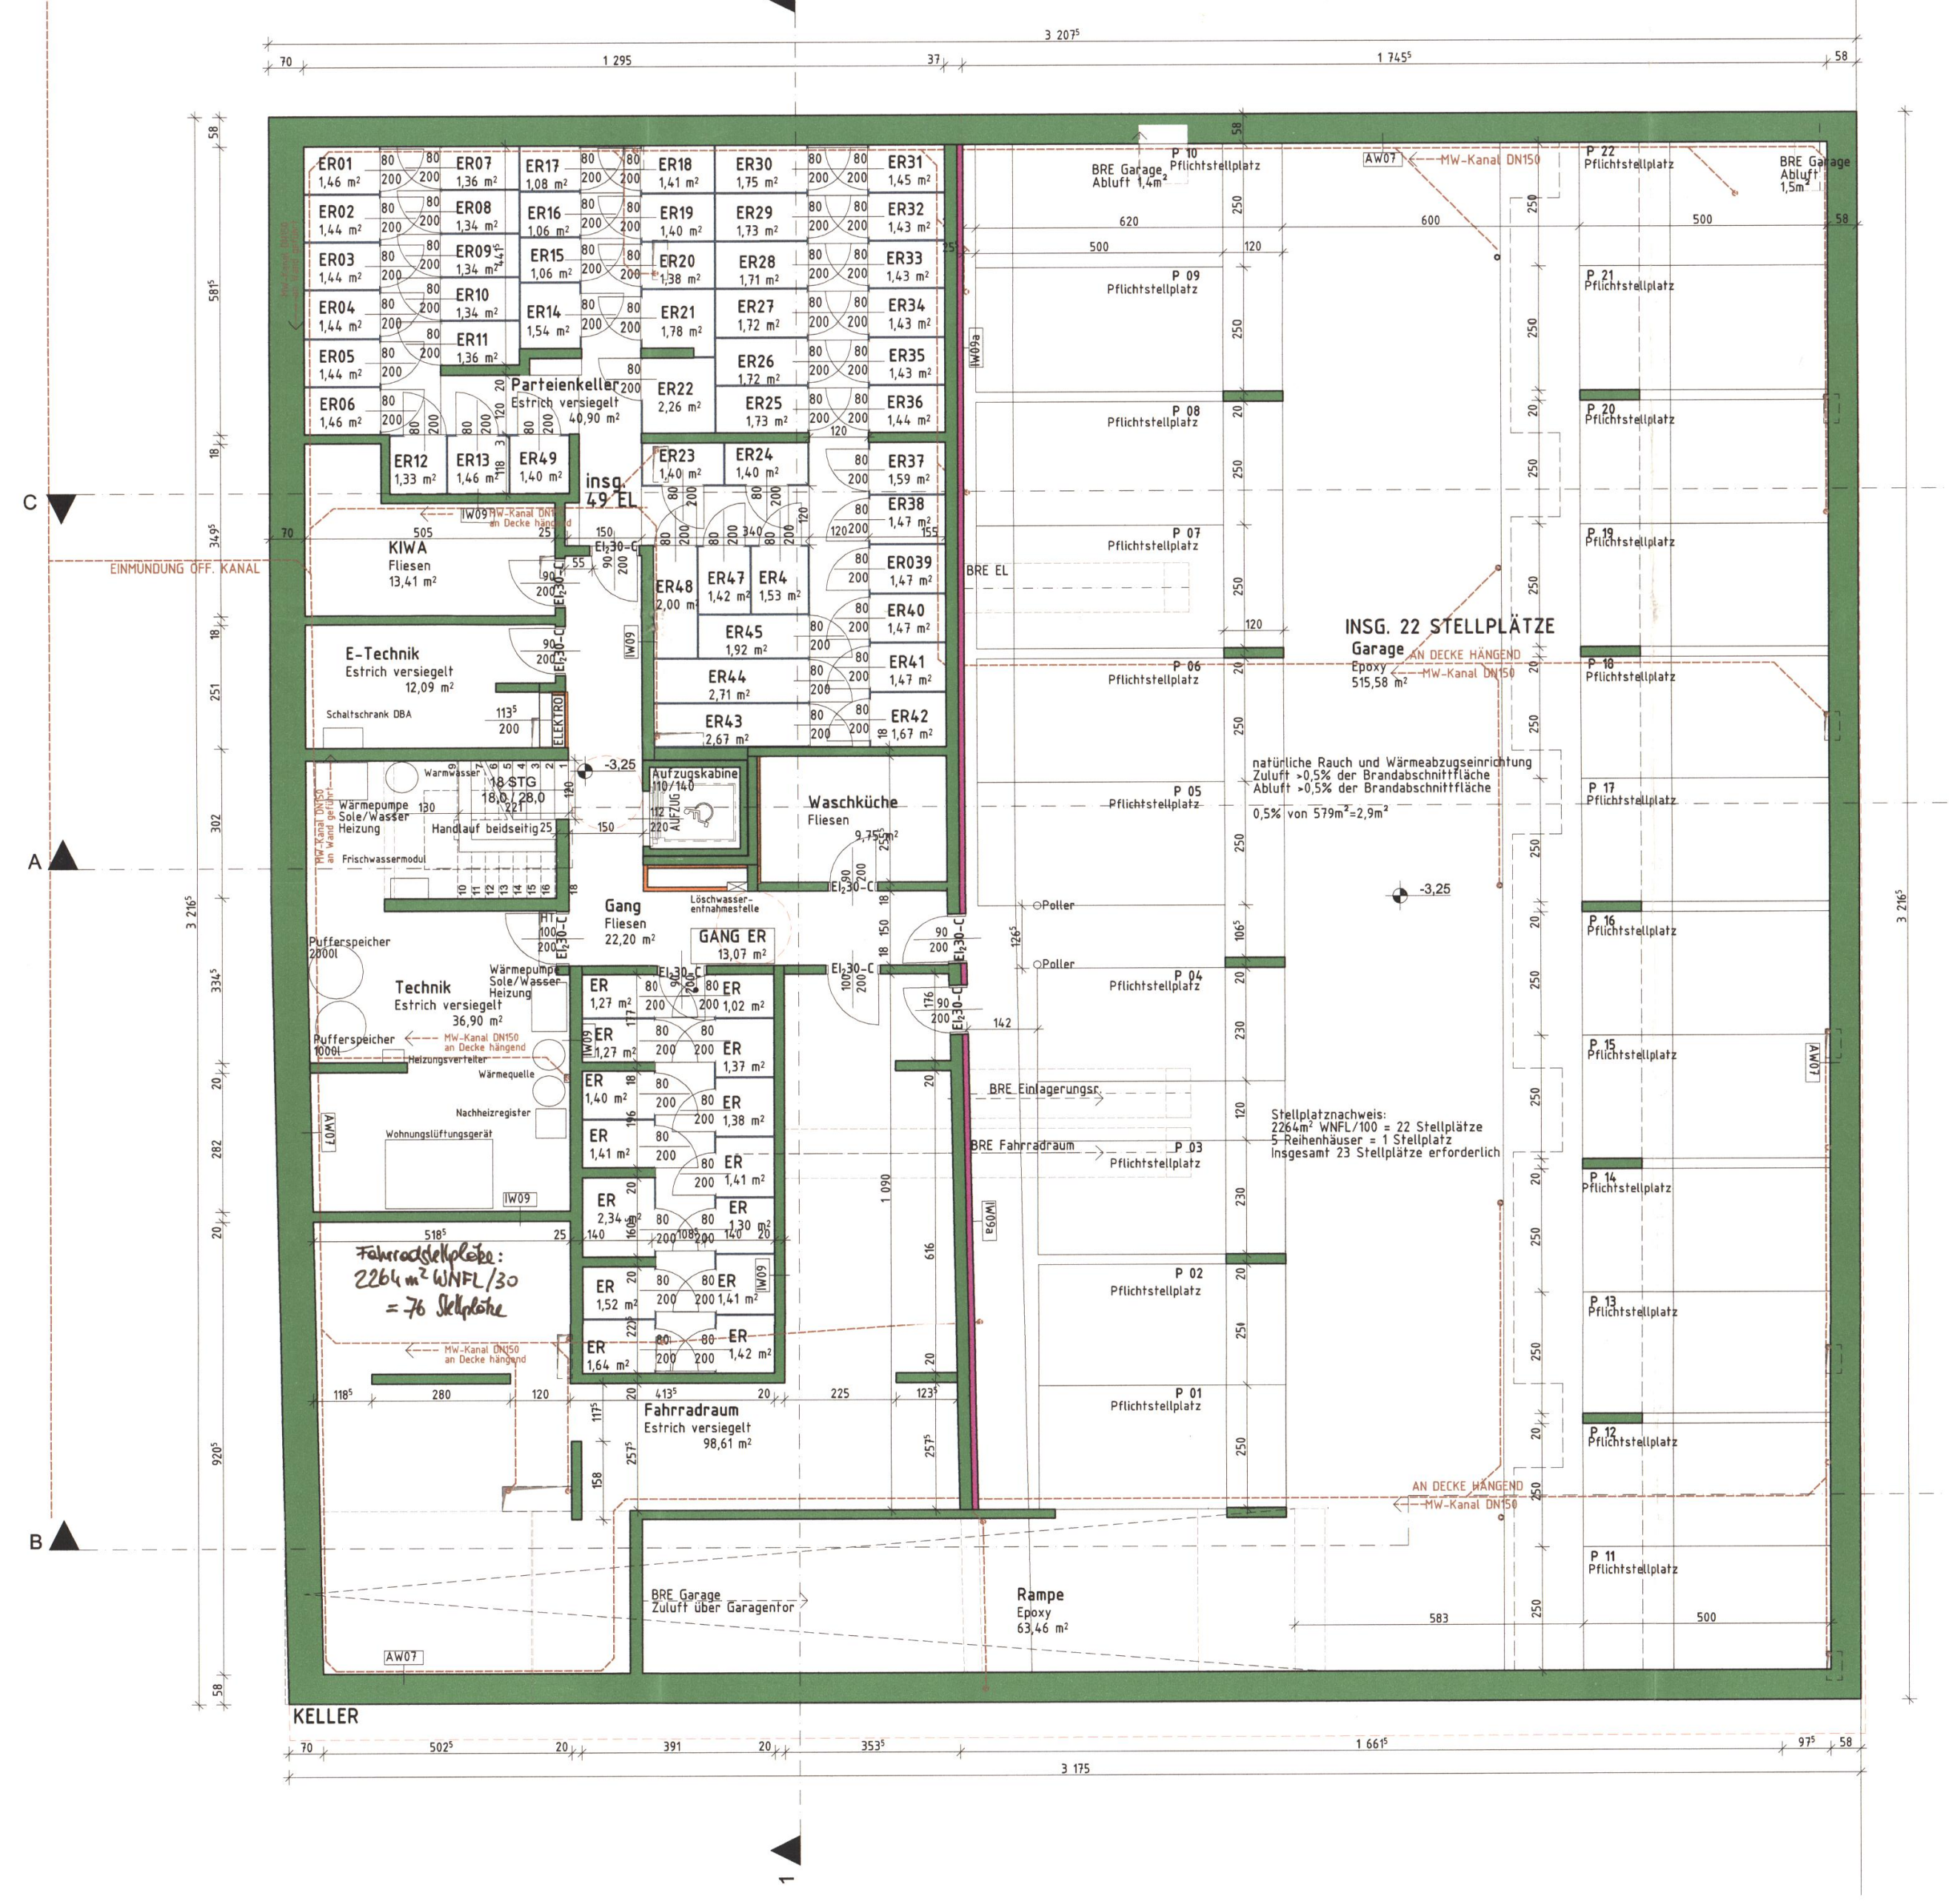

KELLERGESCHOSS

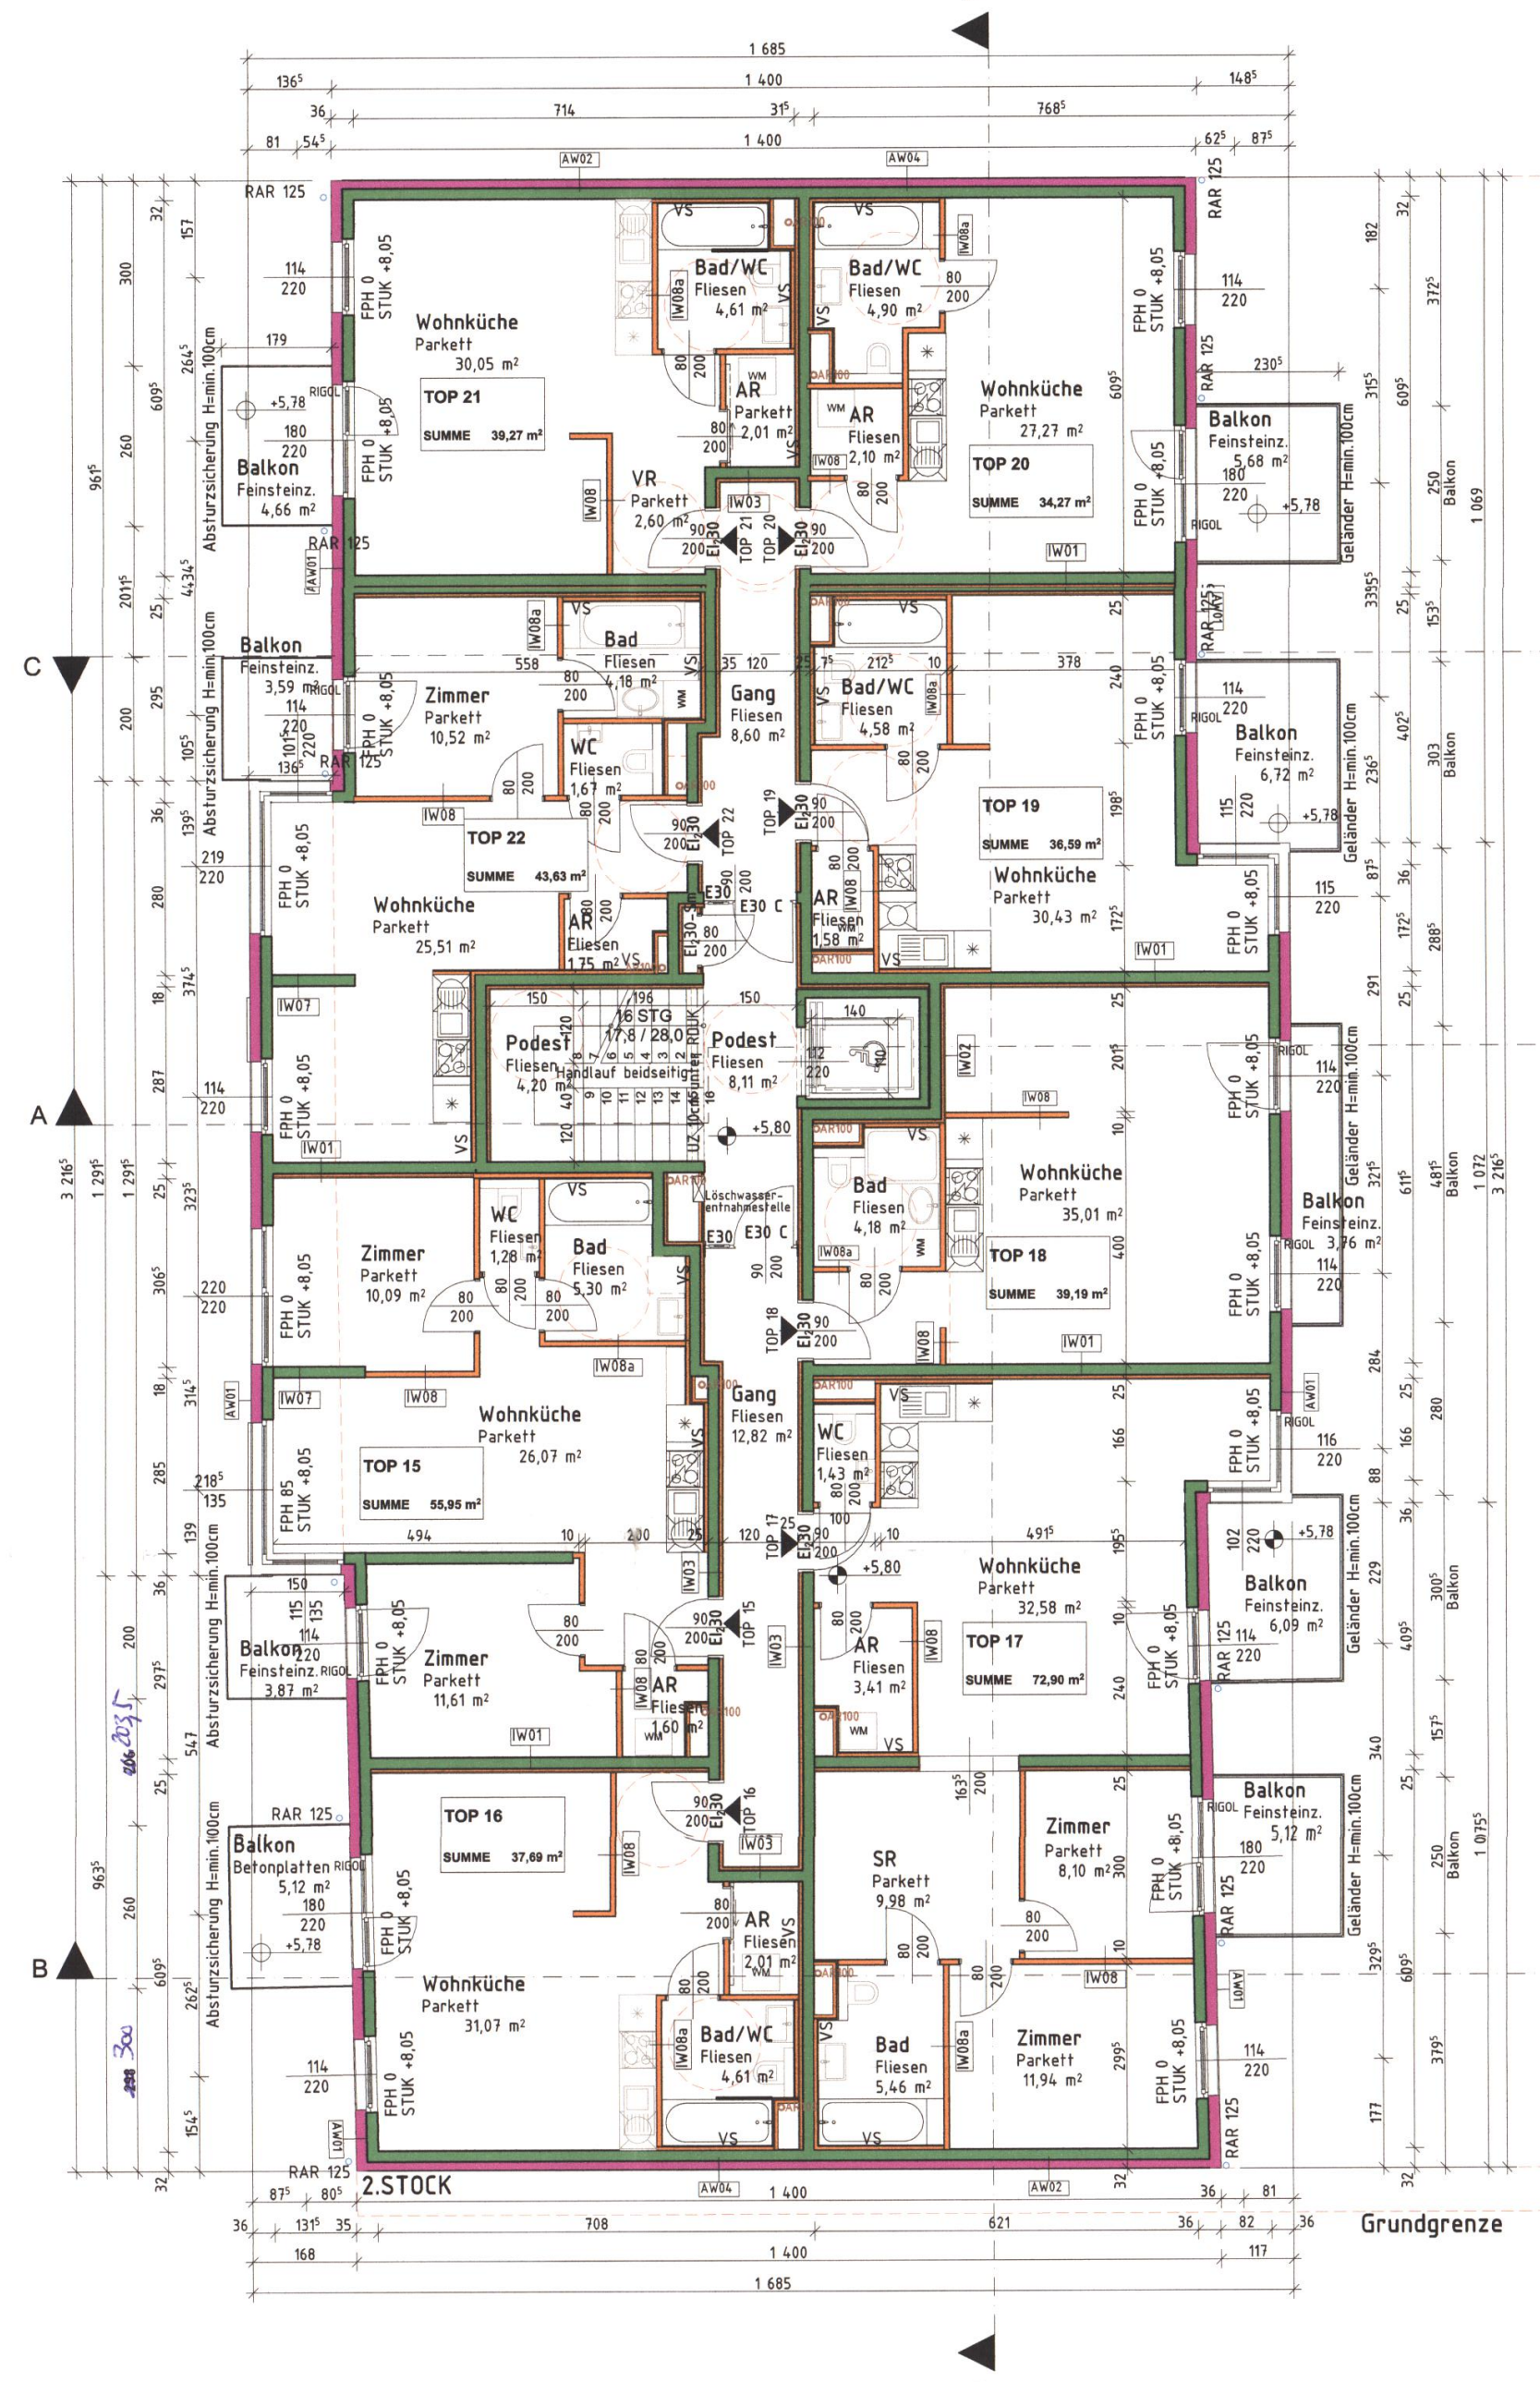

2. STOCK

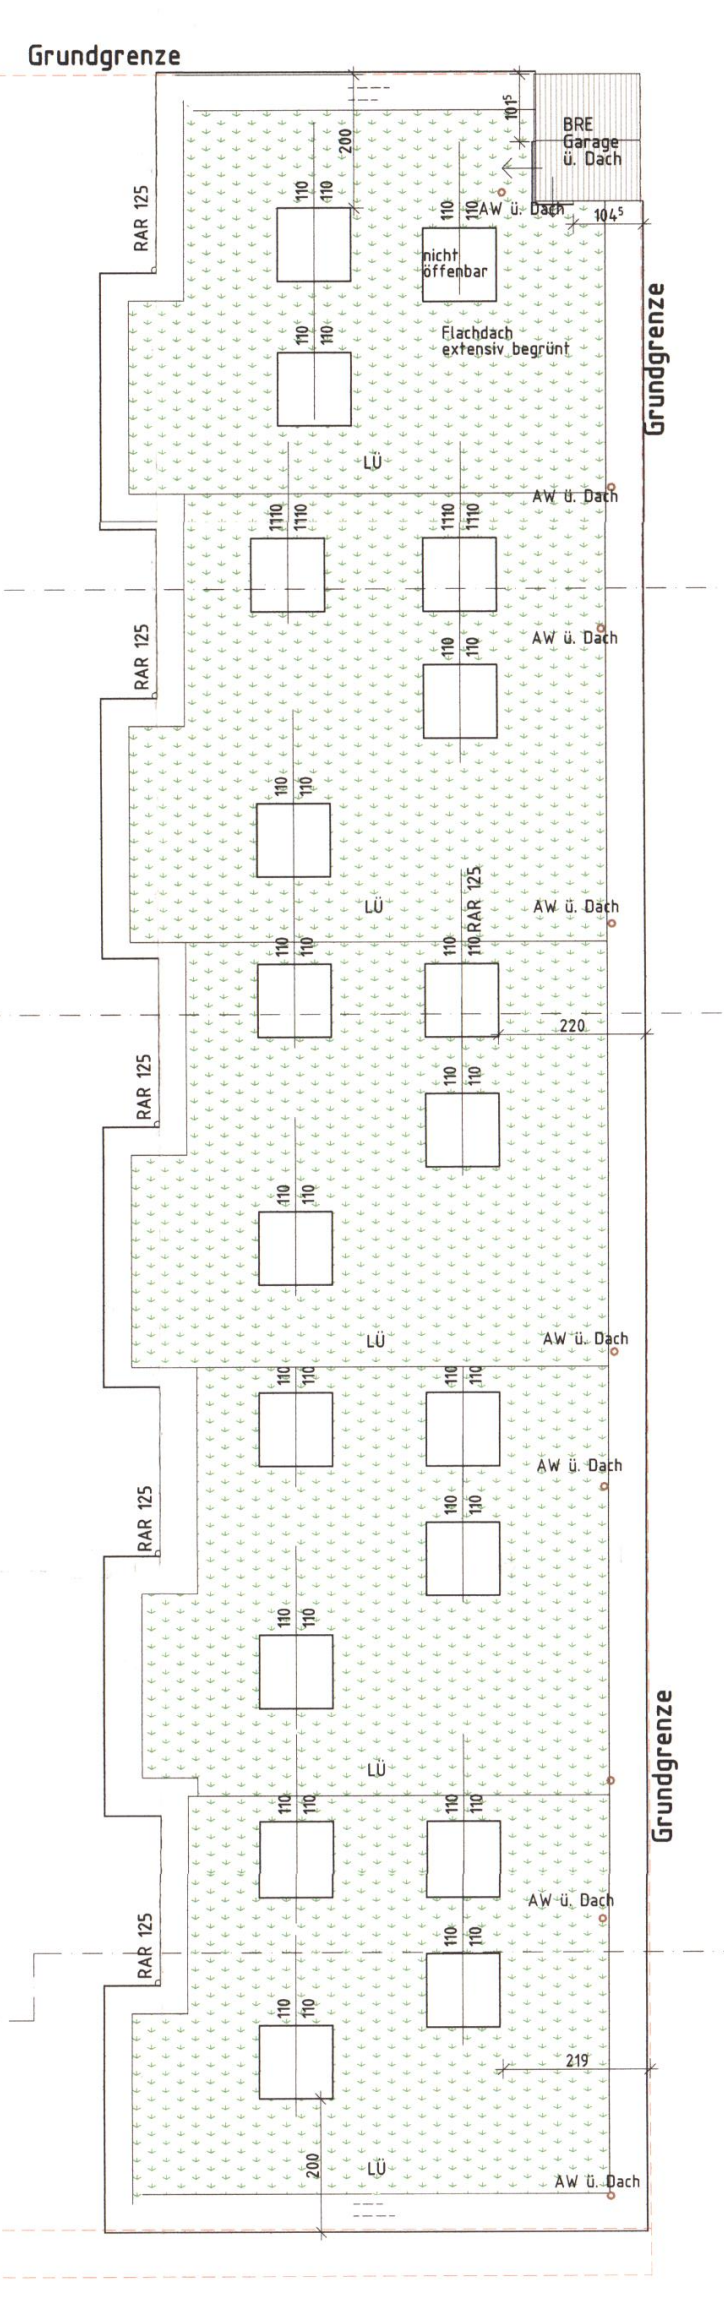

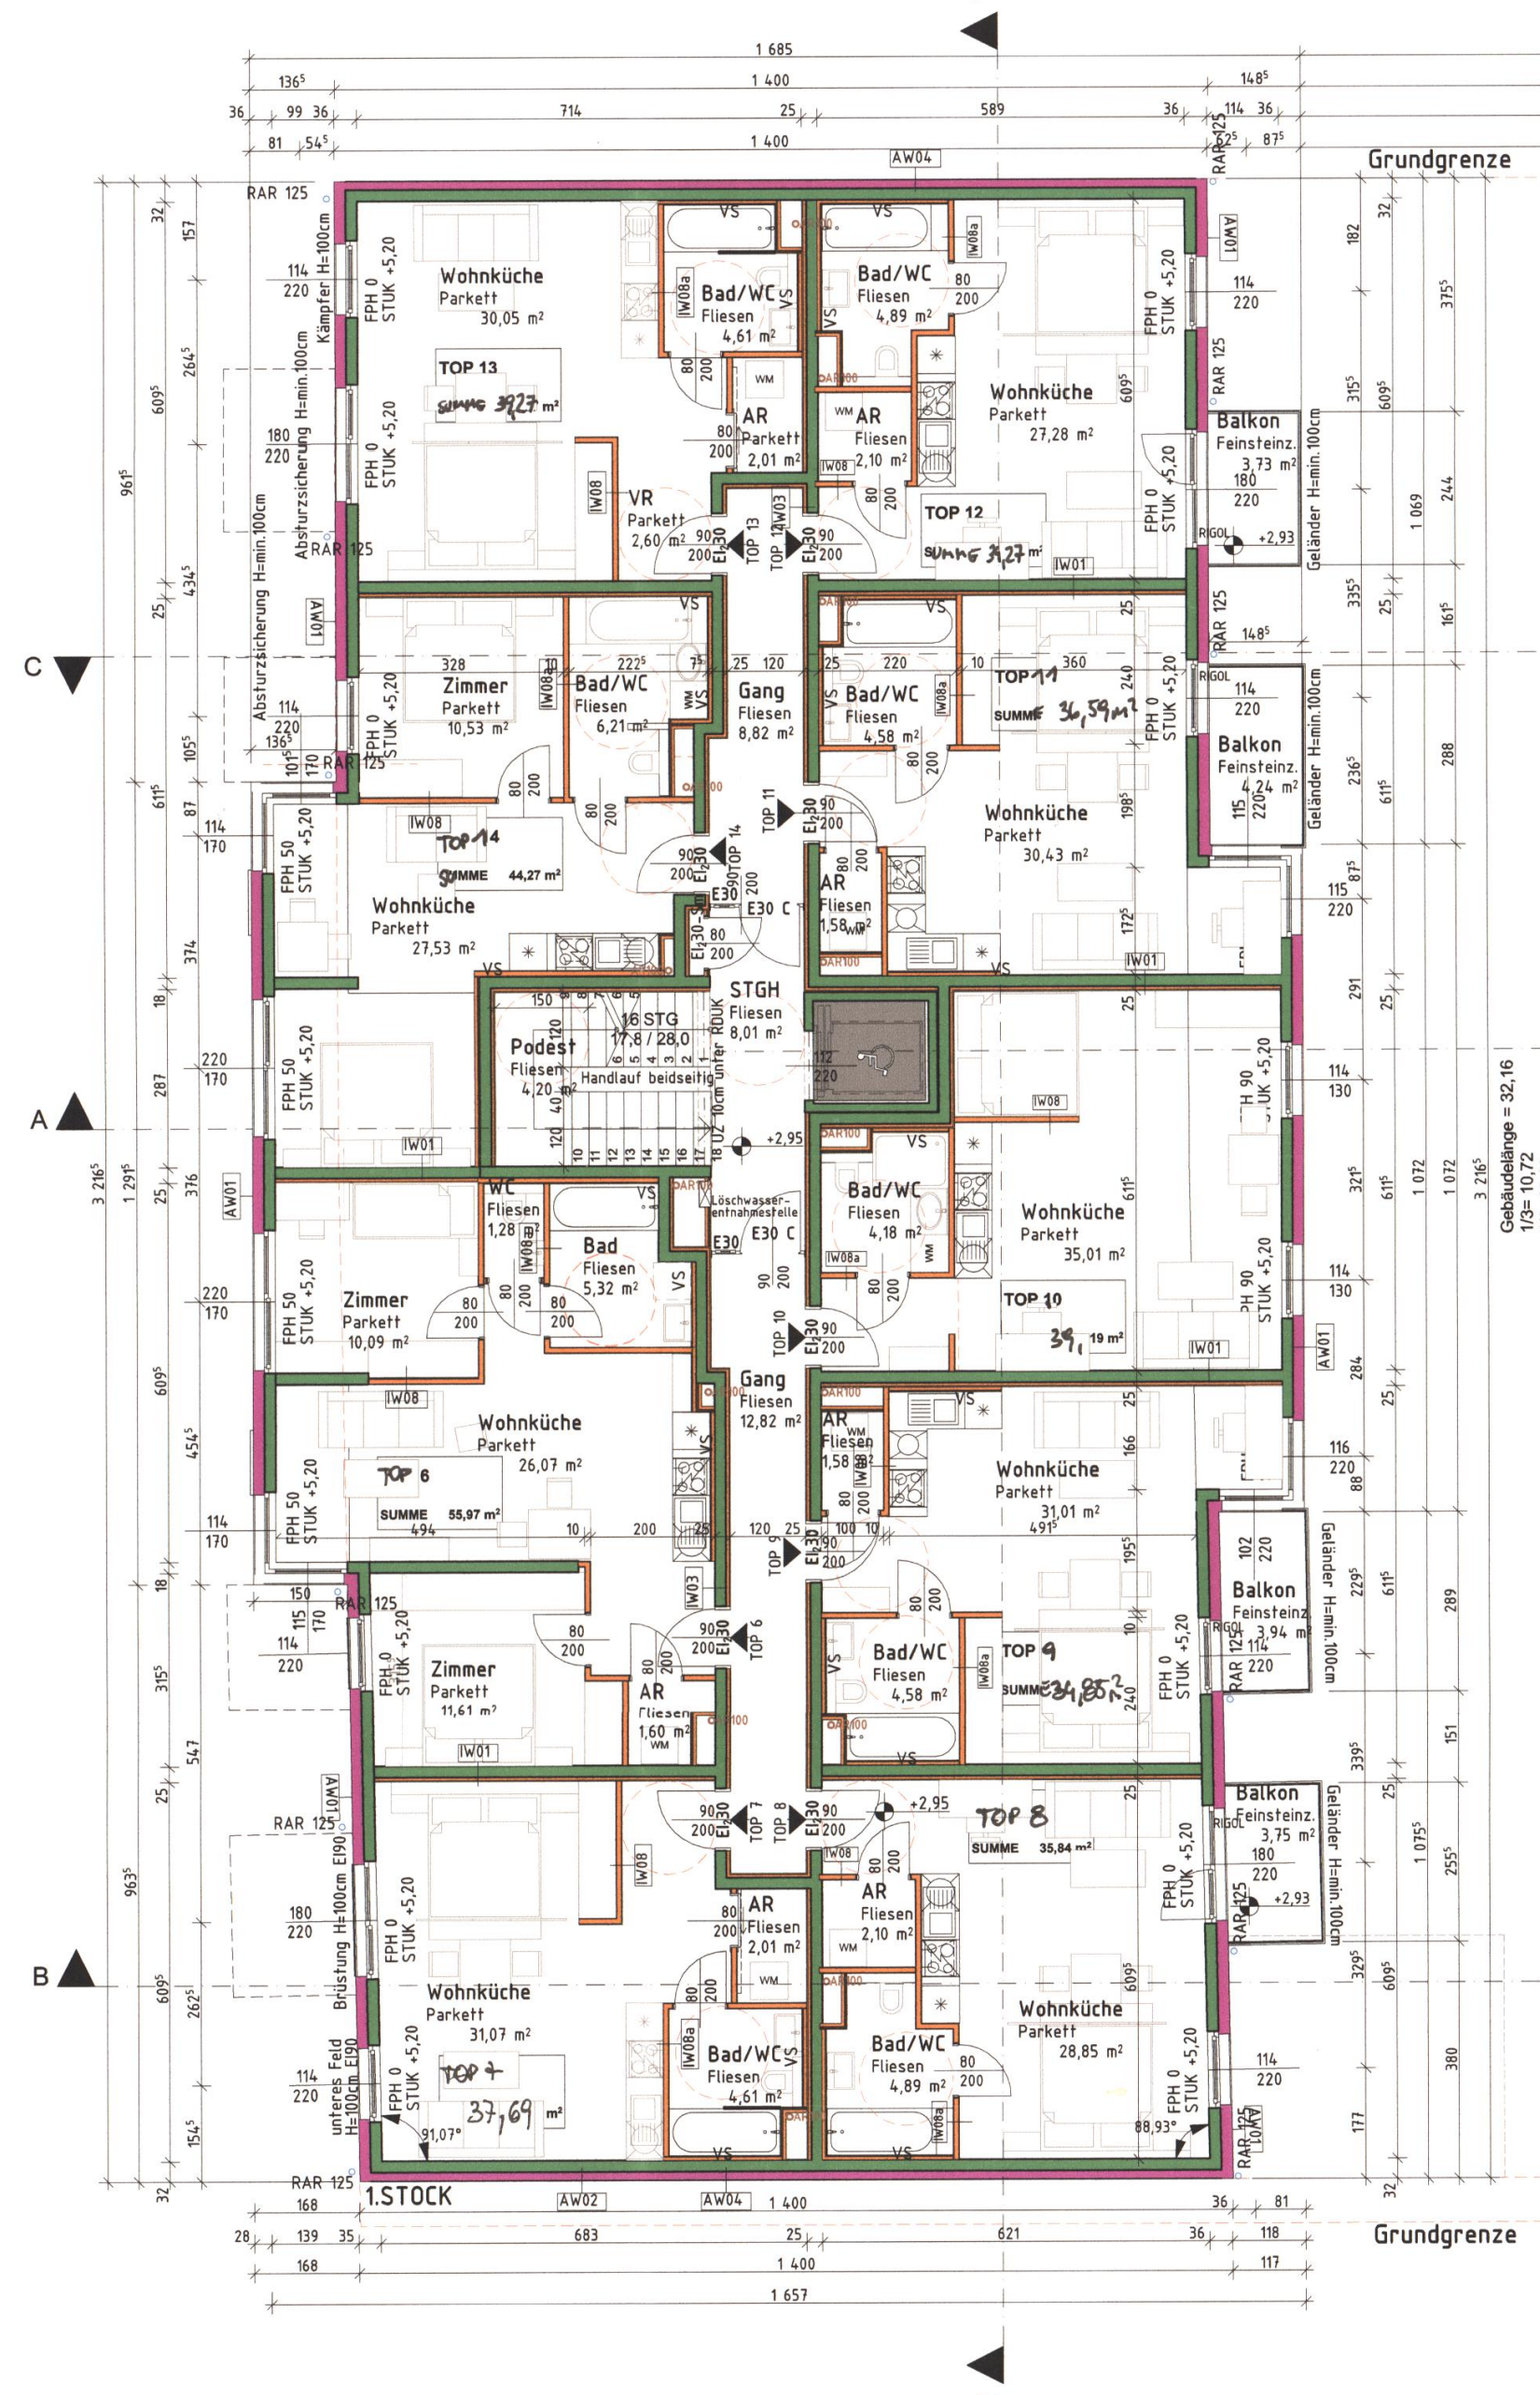

1. STOCK

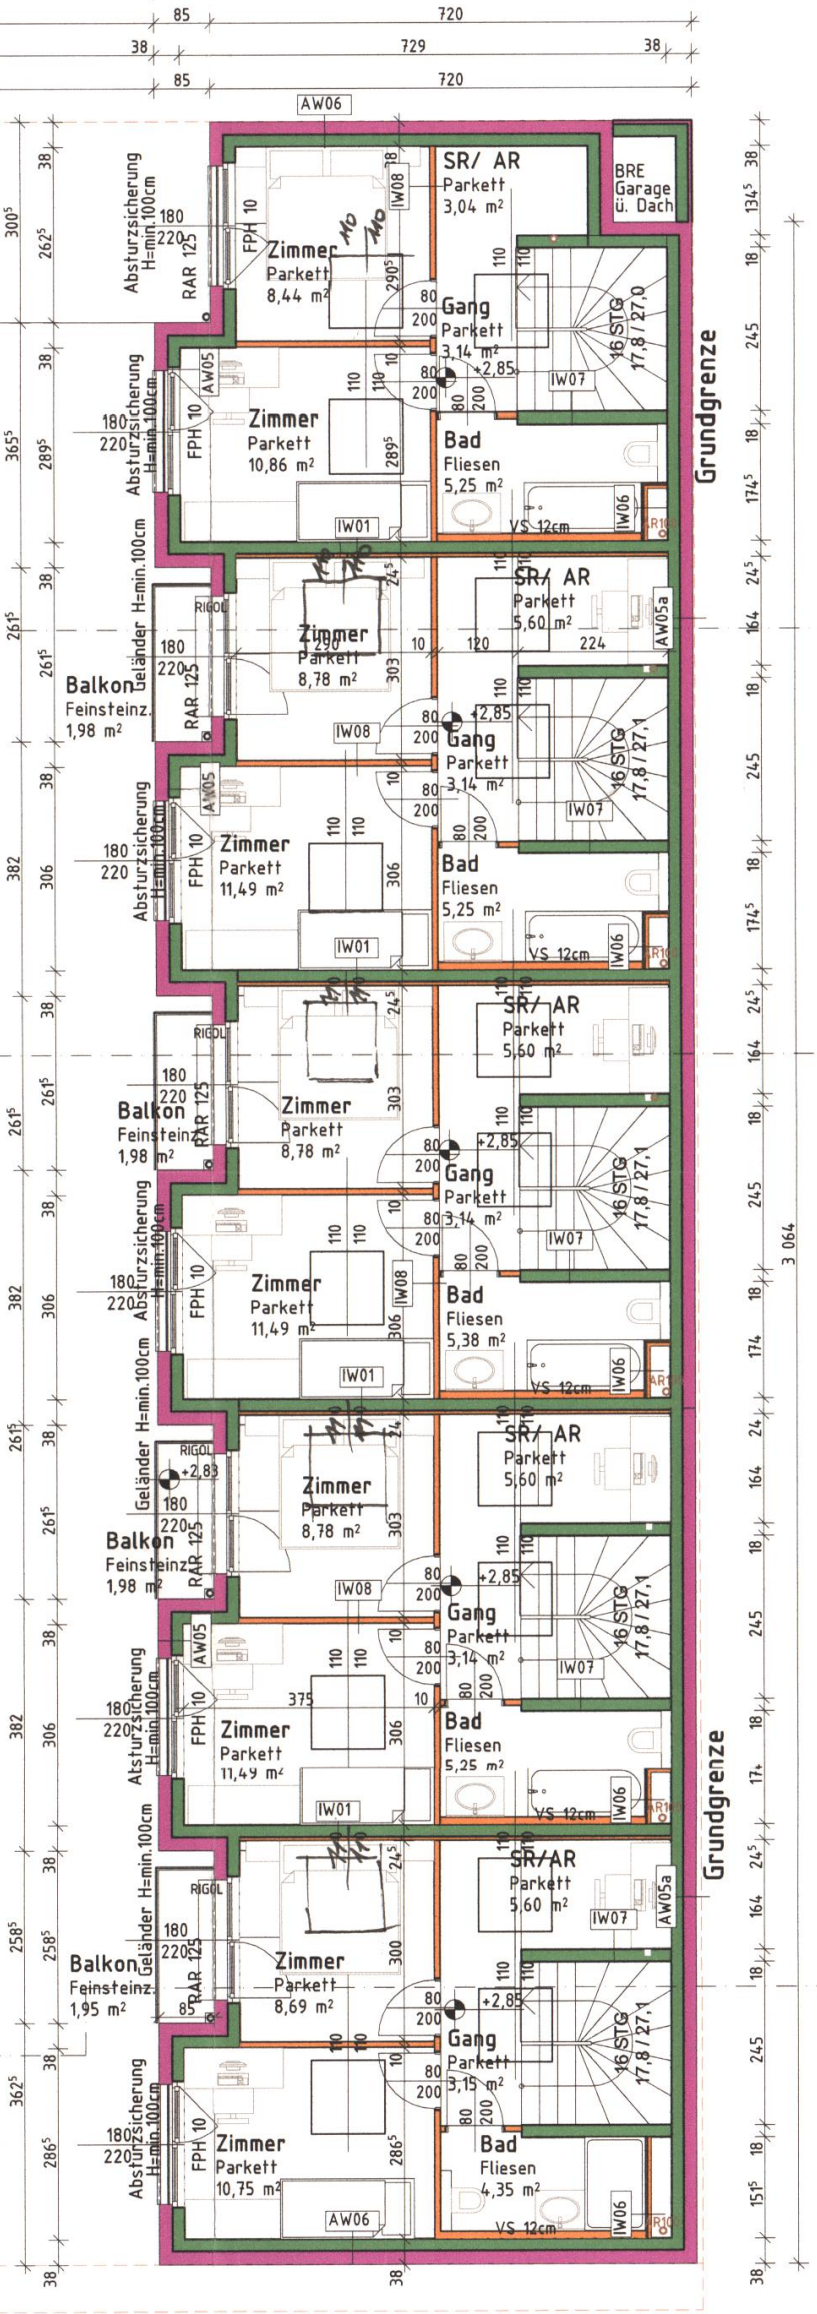

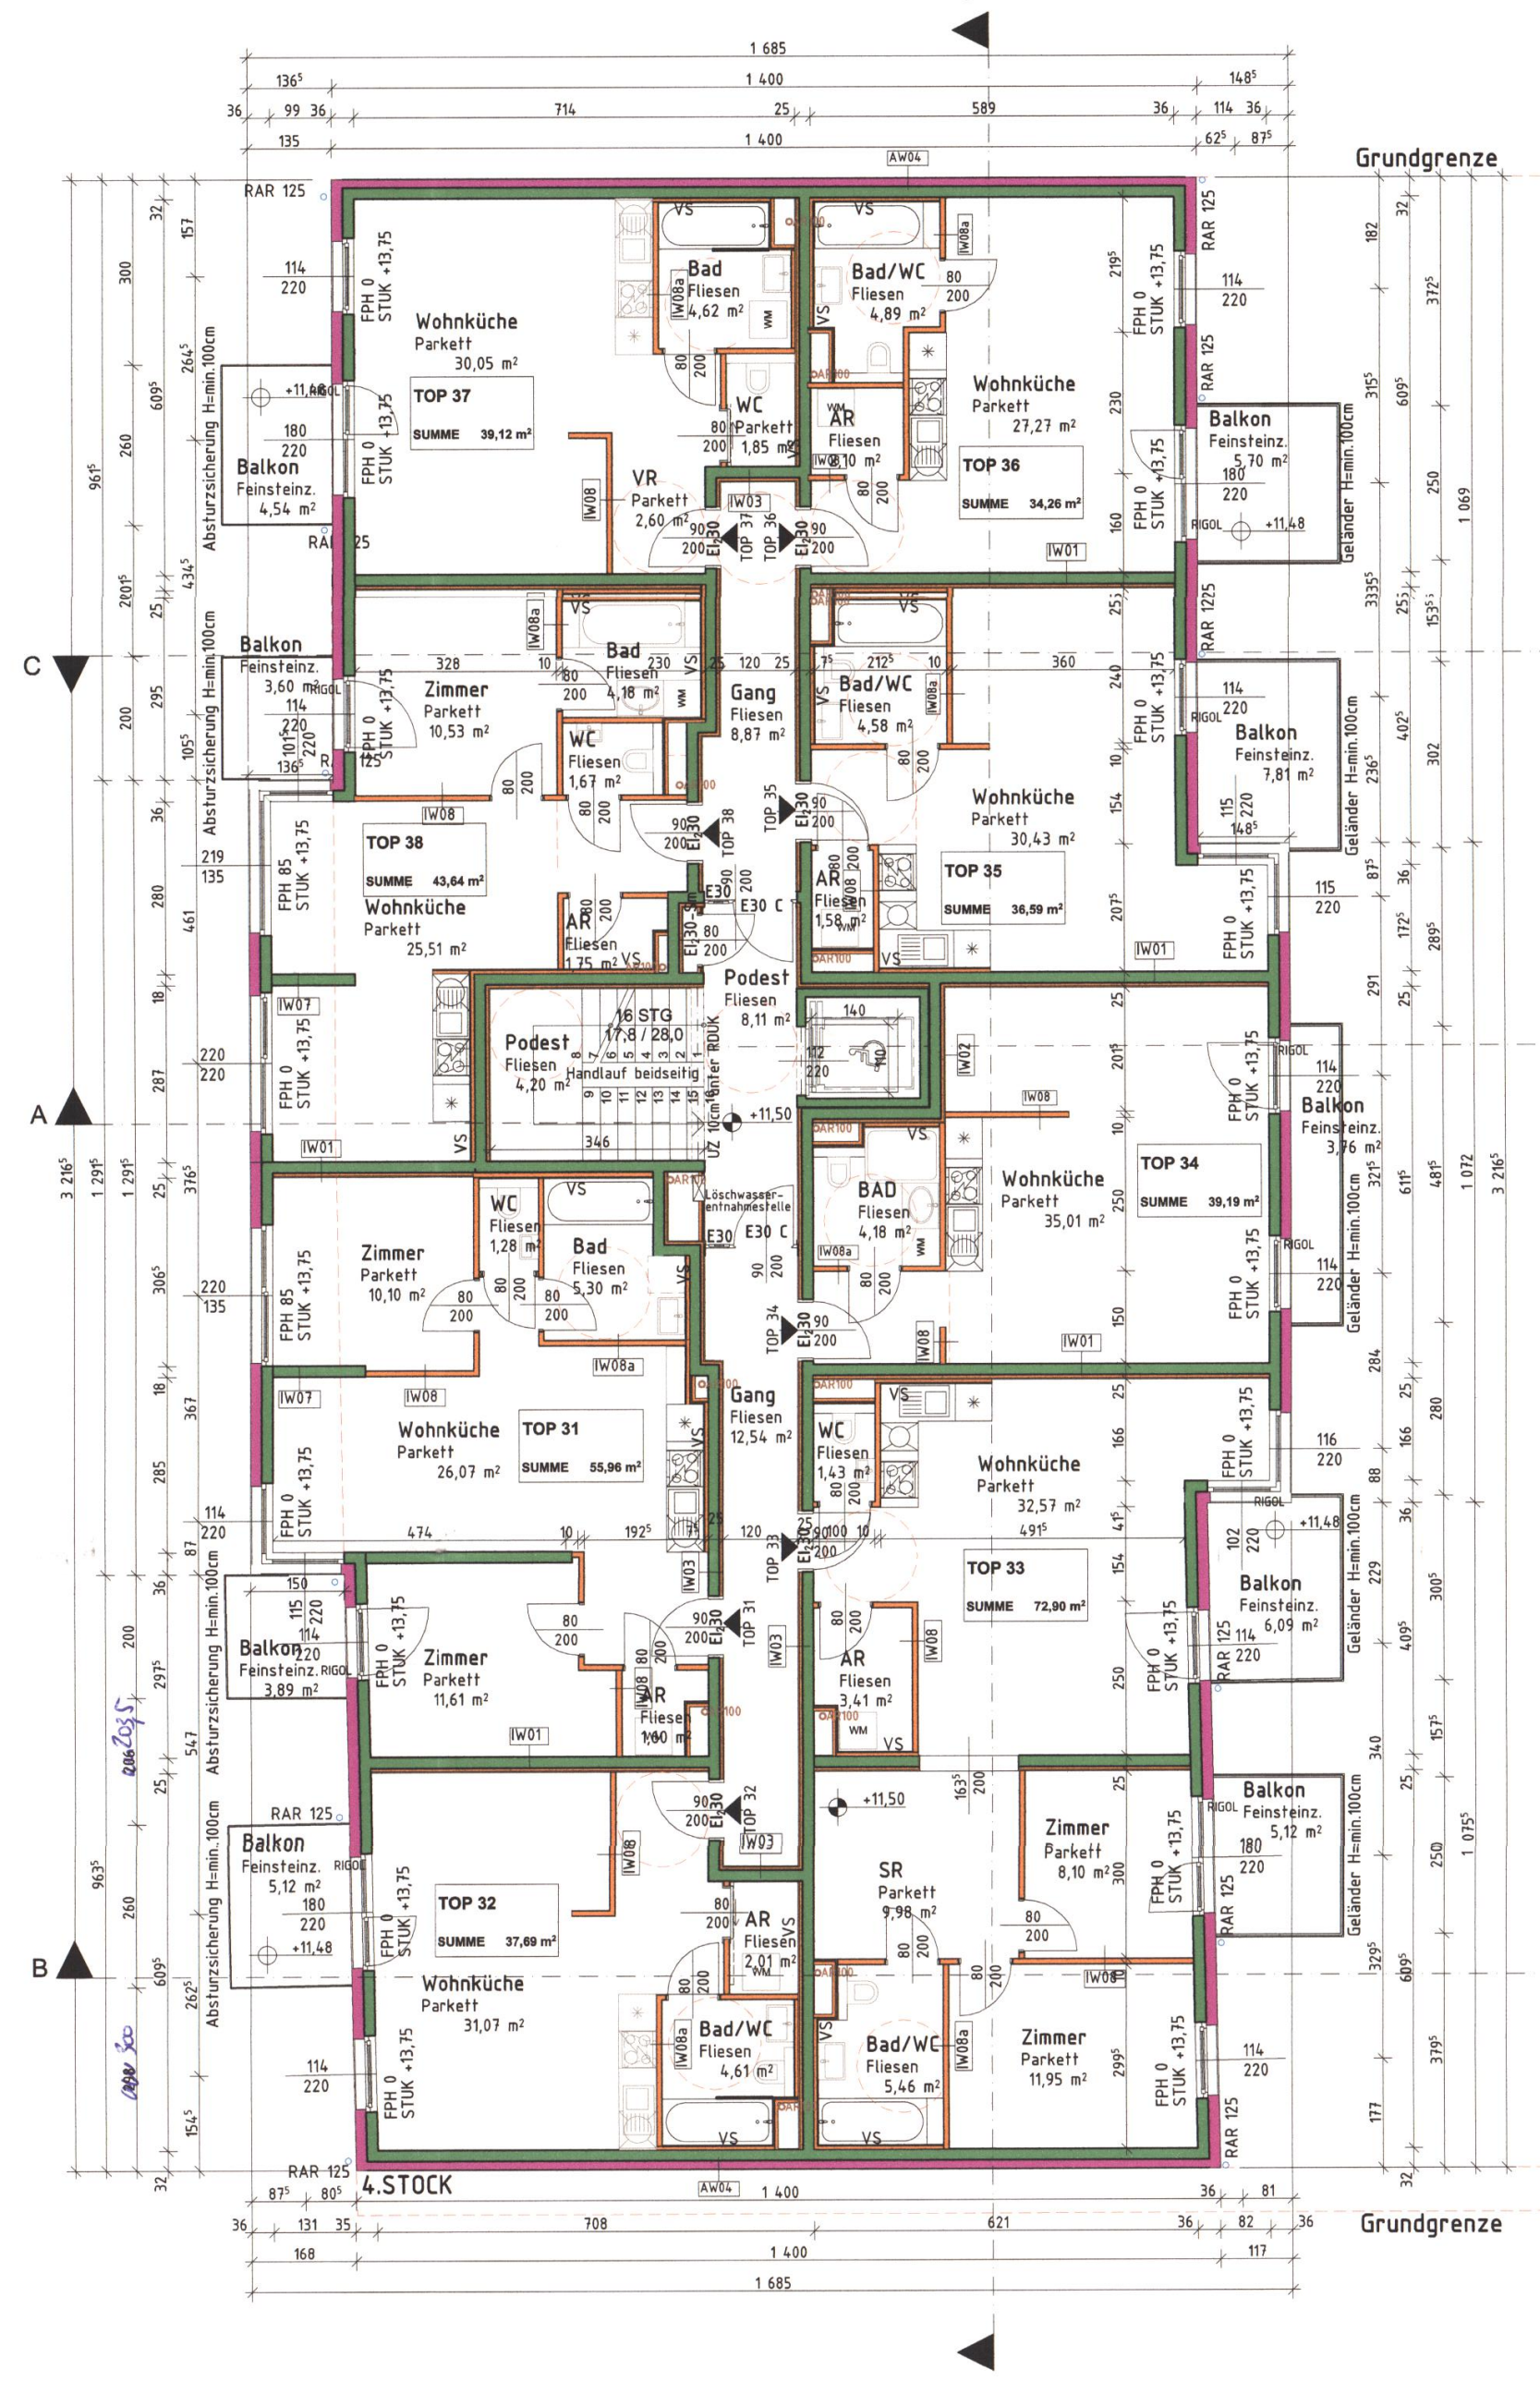

4. STOCK

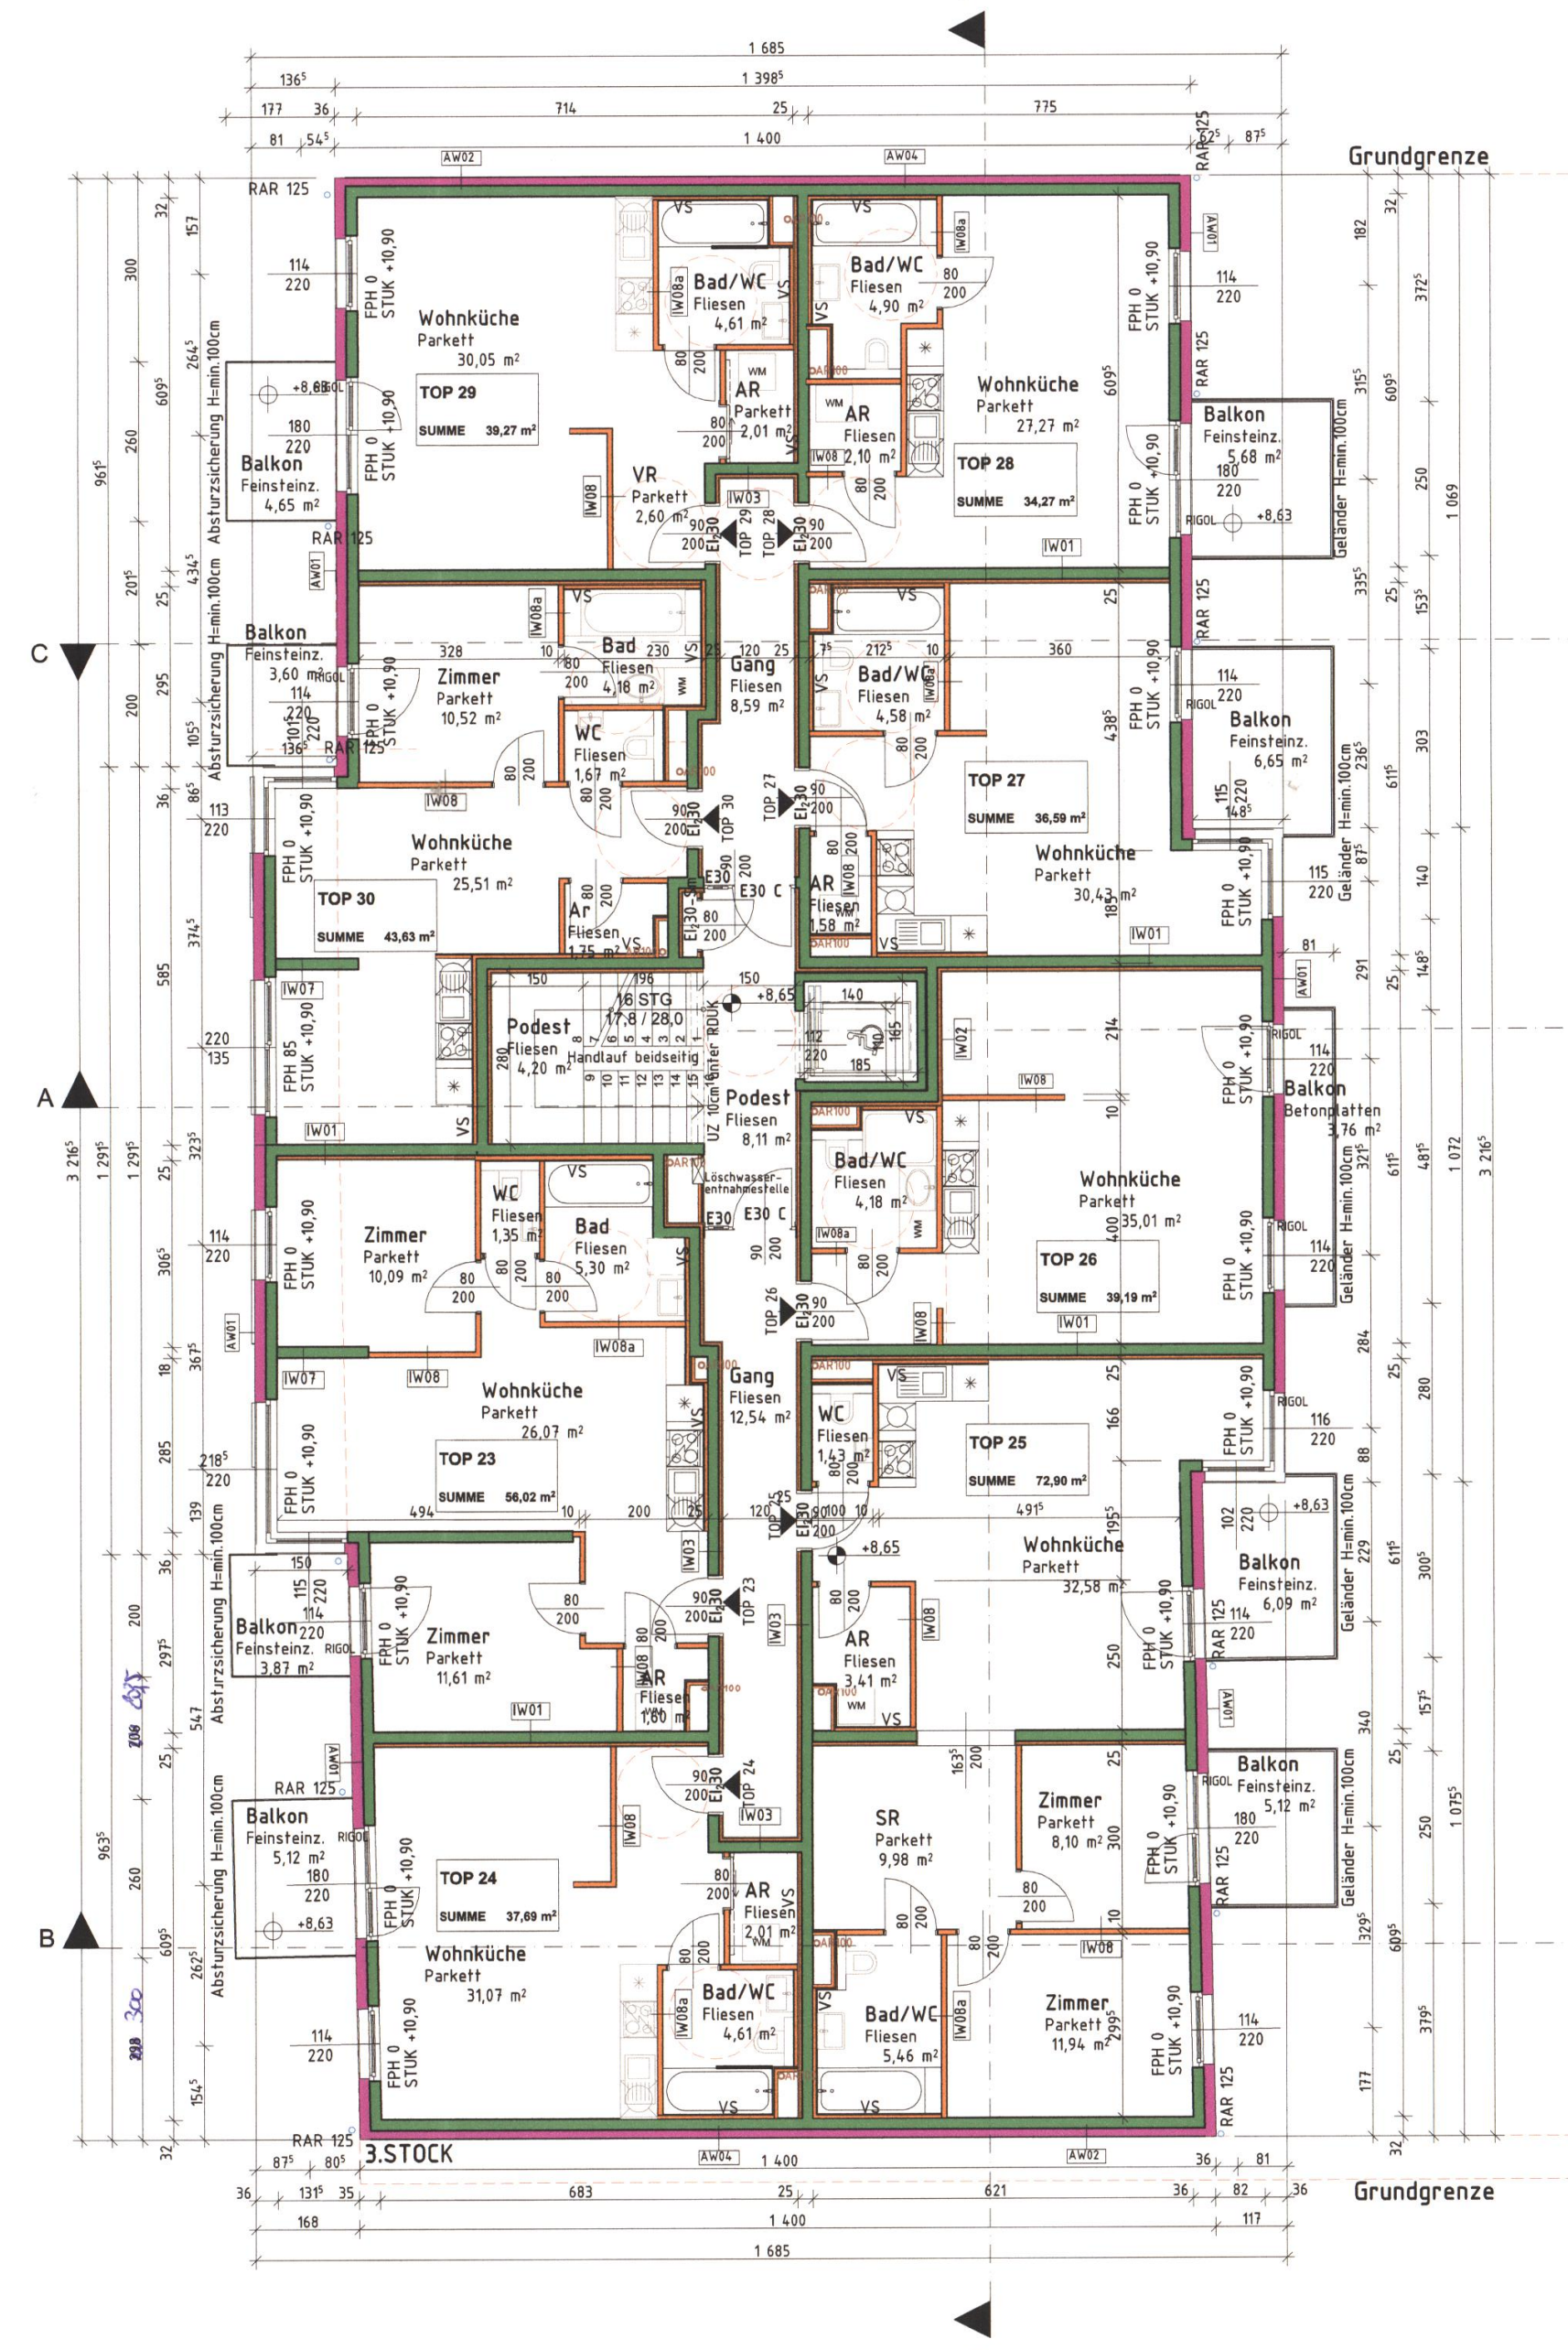

3. STOCK

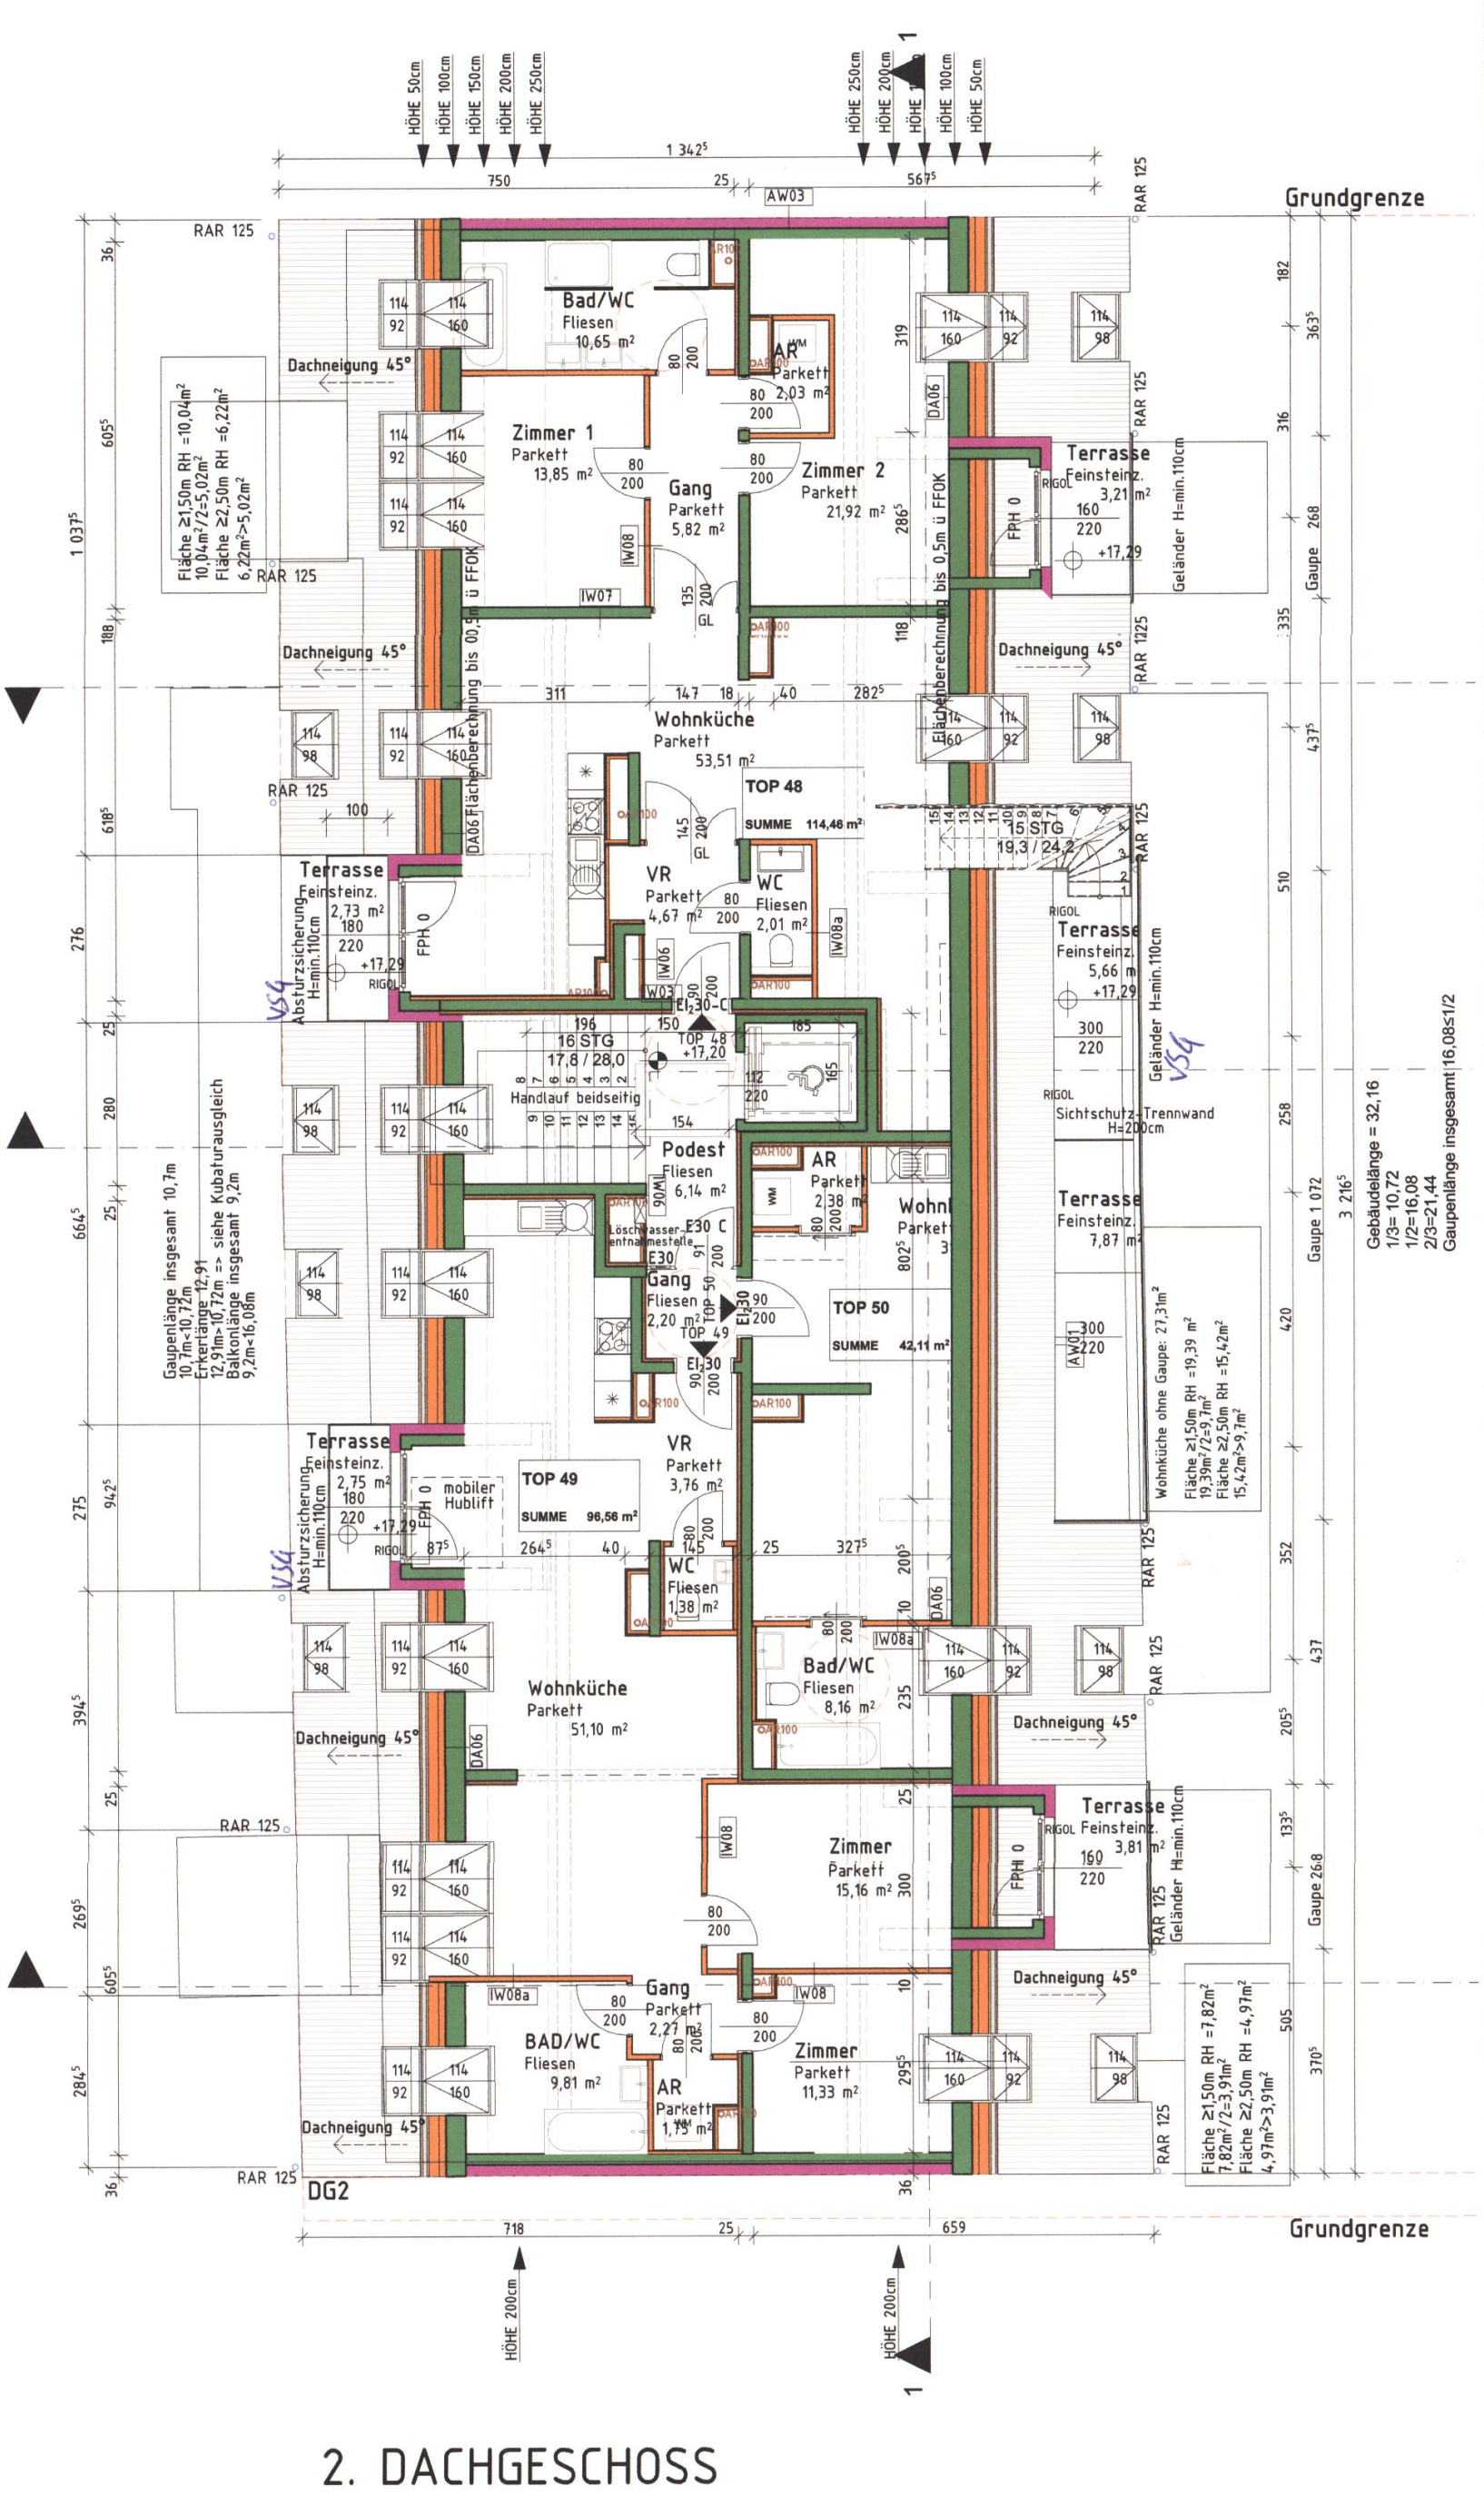

2. DACHGESCHOSS

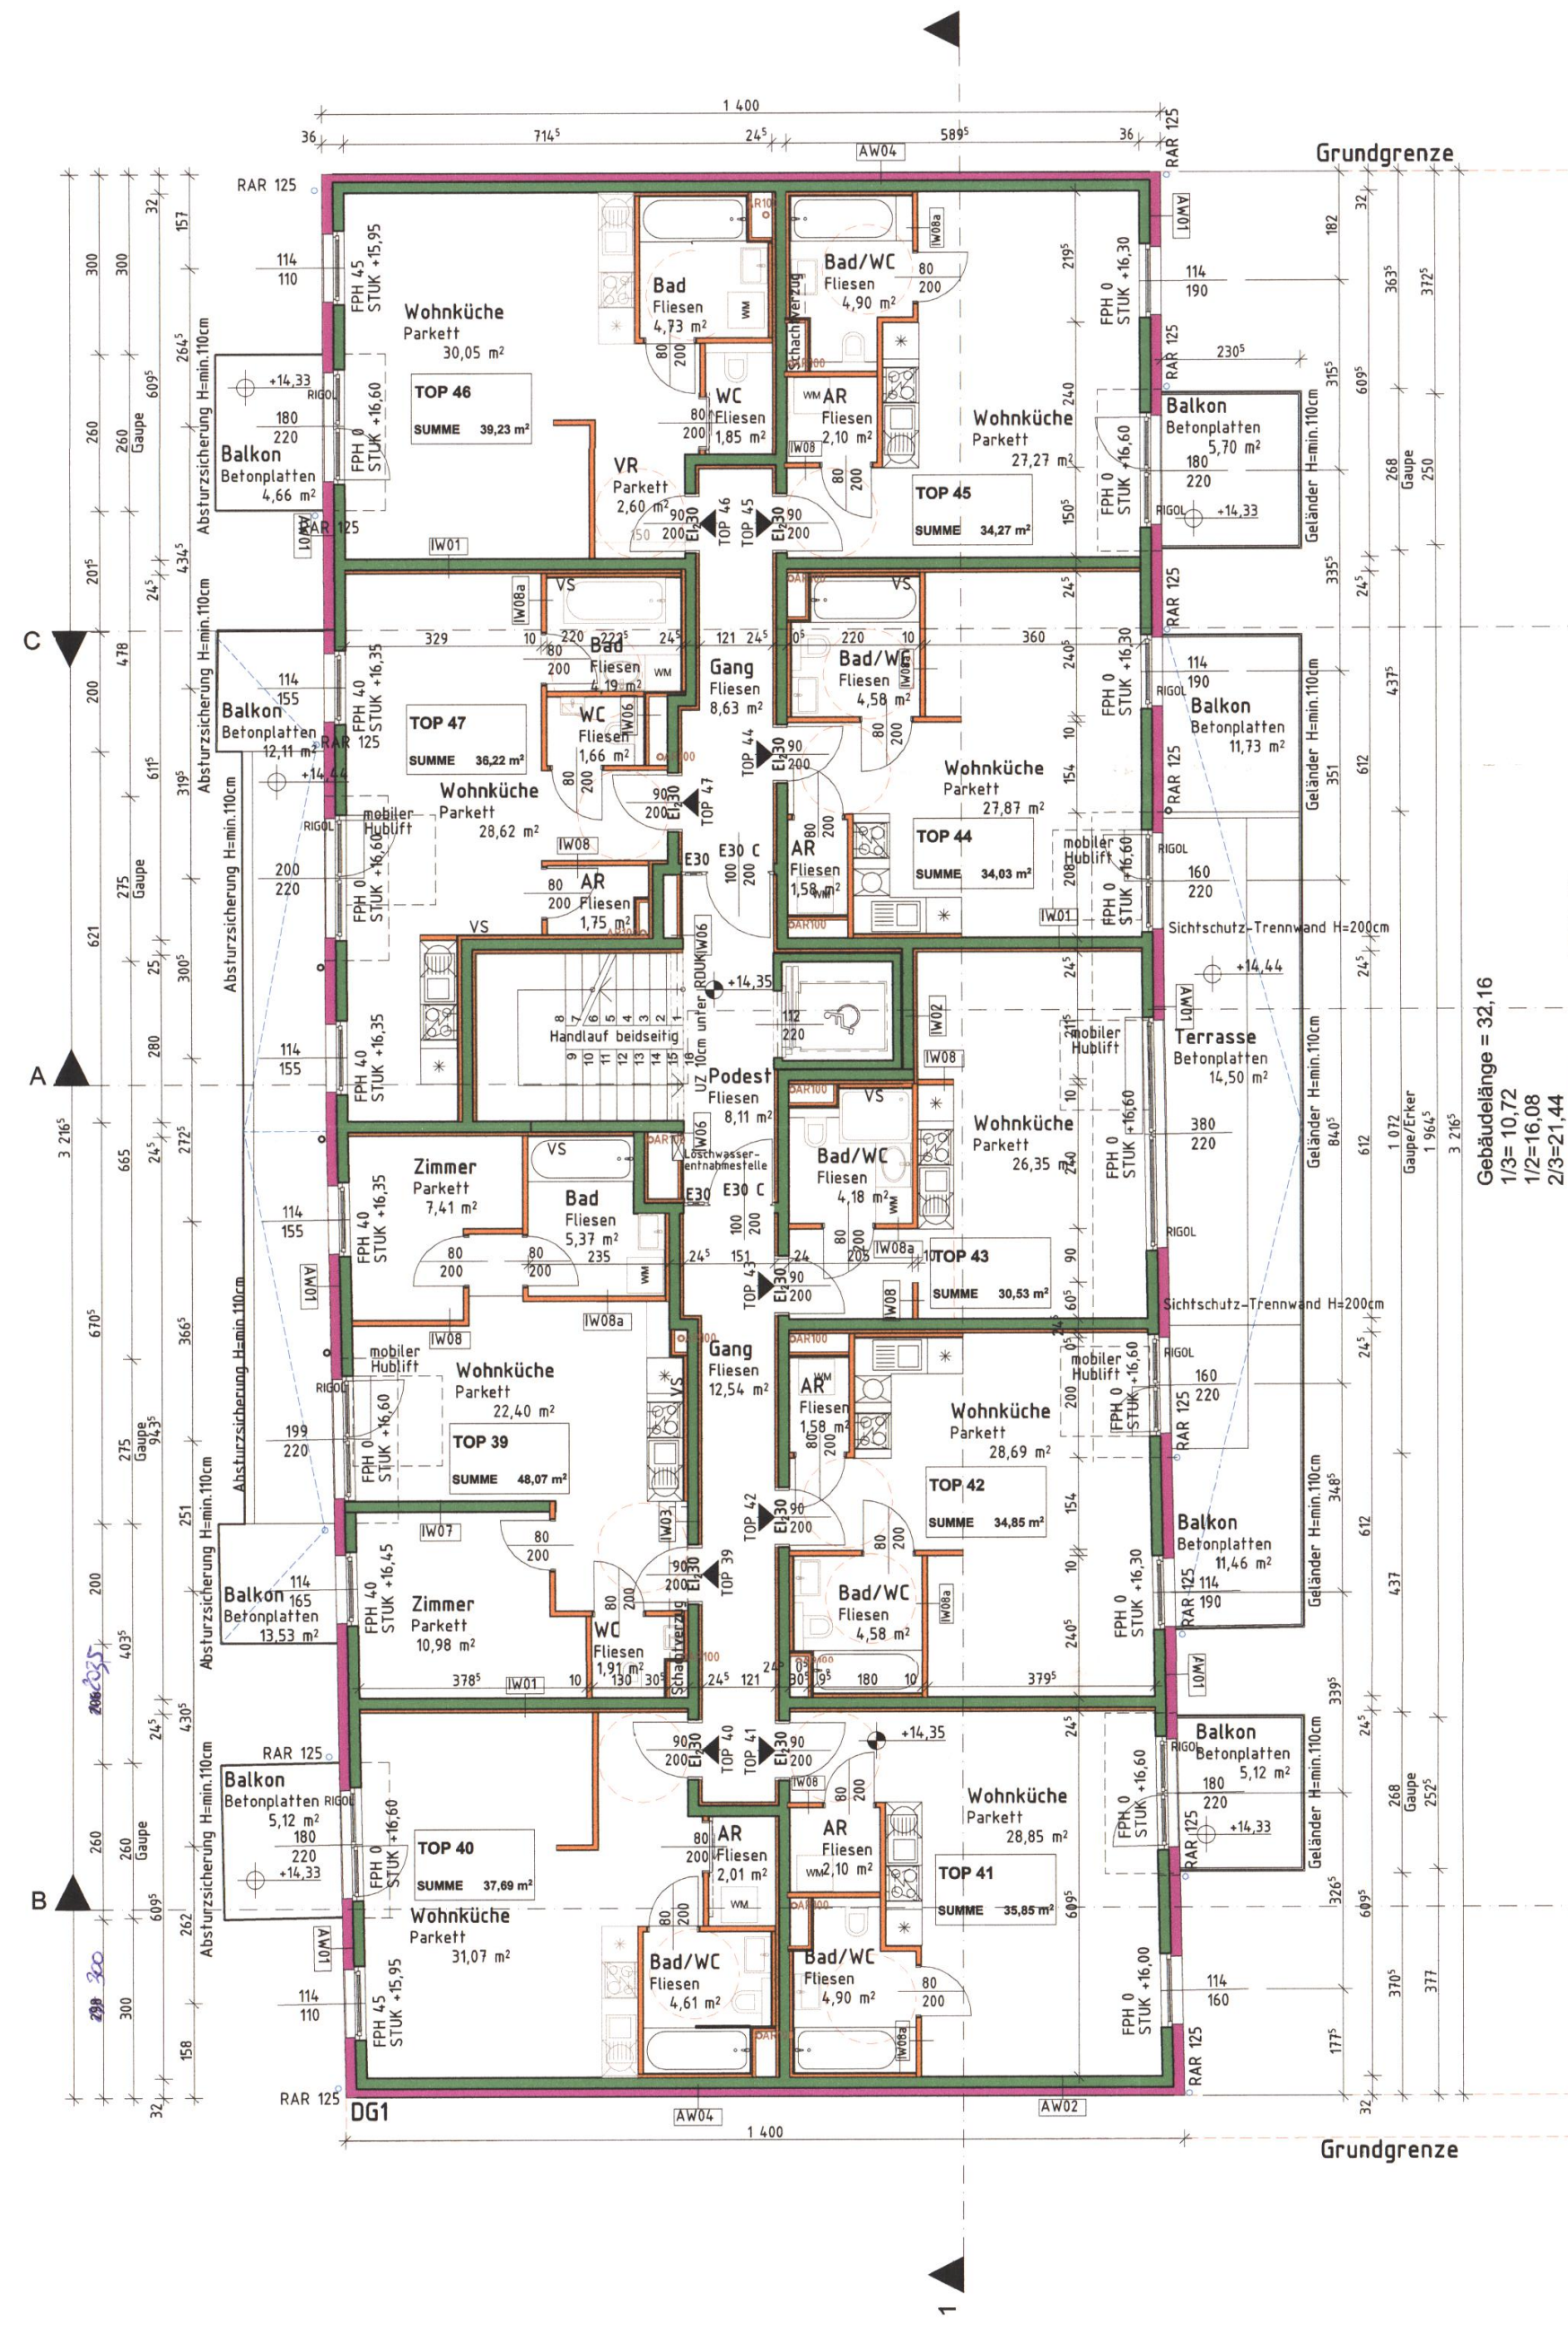

1. DACHGESCHOSS

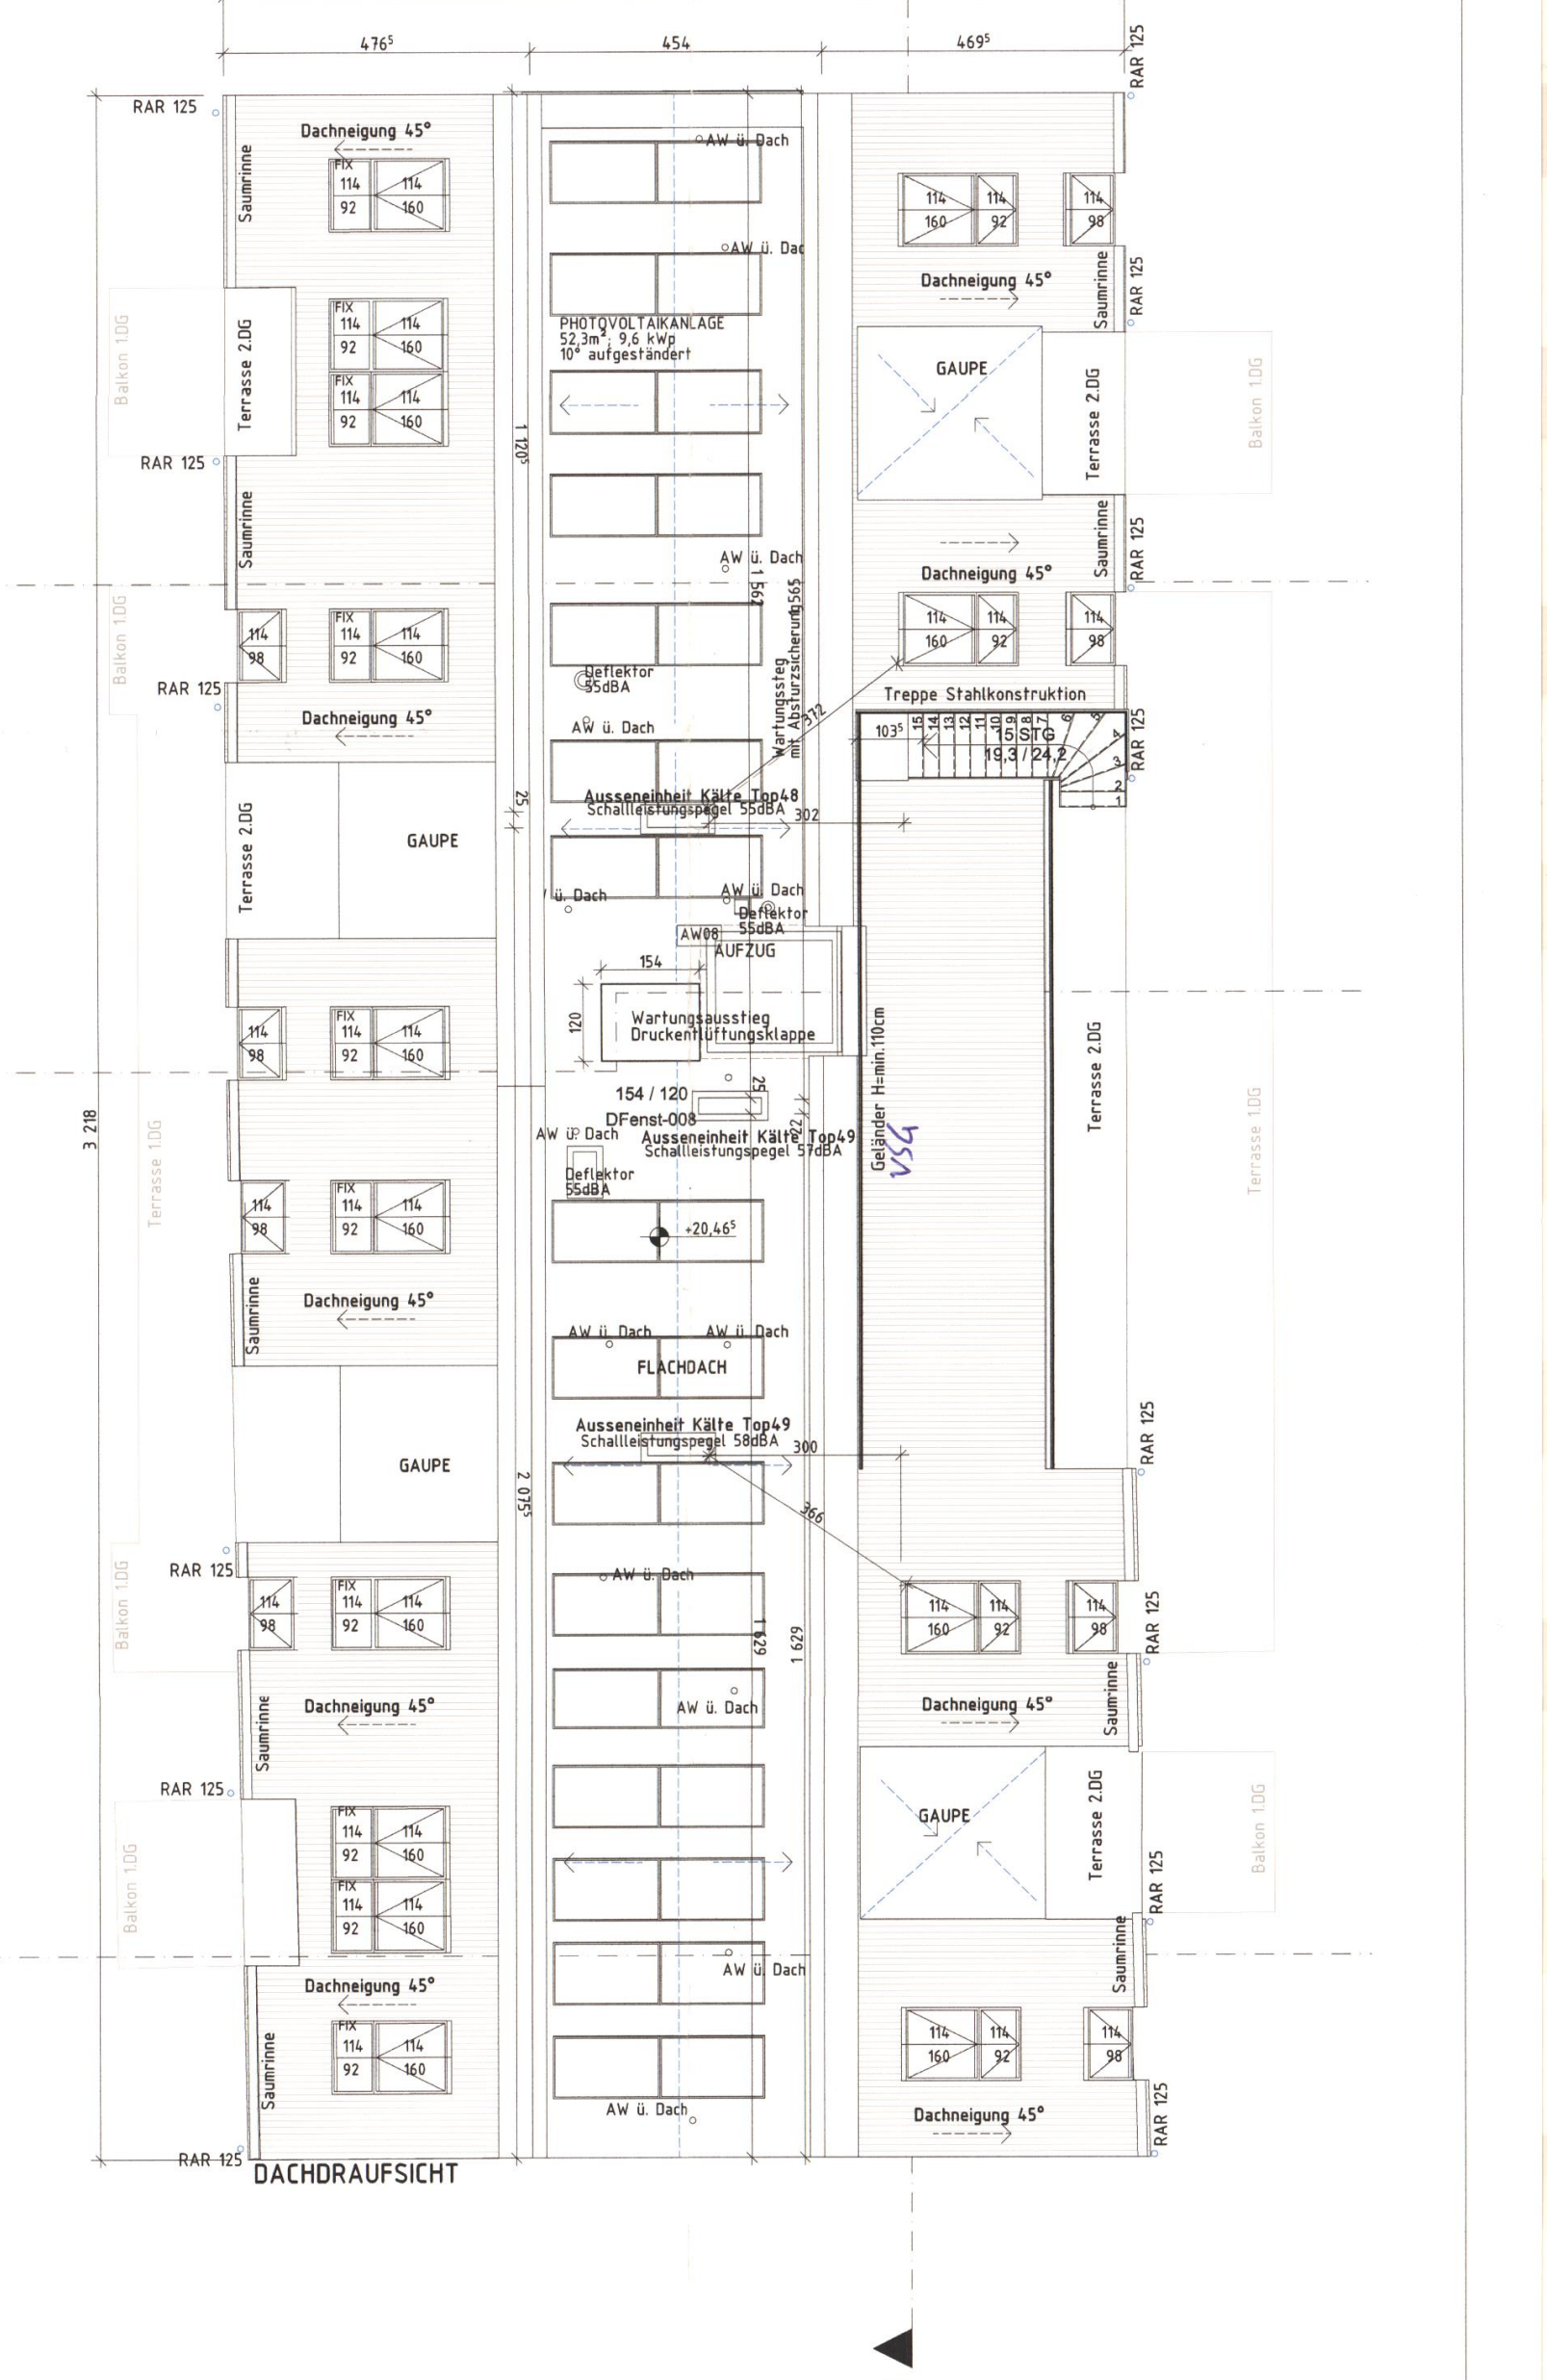

DACHRAUFSICHT

BAUTEILKATALOG WÄNDE / DECKEN / DÄCHER / FUSSBÖDEN

AUSSENWÄNDE

AW01		**Aussenwand Strassentrakt**	
		Außenputz	0,20 cm
		Grundbeschichtung	0,10 cm
		Glasarmierung	0,10 cm
		Mineralischer Klebe- und Armierungsmörtel	0,20 cm
	A2	Dämmung	18,00 cm
		Mineralischer Klebe- und Armierungsmörtel	0,40 cm
		Stahlbeton lt. Statik (2400kg/m³)	18,00 cm
		Innenspachtelung	0,20 cm
AW01a		**Aussenwand Strassentrakt 18cm STB + Schauseitenverkleidung**	
		Fassadenplatten	0,80 cm
		Untrkonstruktion/ Hinterlüftung	5,00 cm
		Winddichte Folie	0,06 cm
	A2	Dämmung	18,00 cm
		Mineralischer Klebe- und Armierungsmörtel	0,40 cm
		Stahlbeton lt. Statik (2400kg/m³)	18,00 cm
		Innenspachtelung	0,20 cm
AW01b		**Aussenwand Strassentrakt 20cm STB + Schauseitenverkleidung**	
		Fassadenplatten	0,80 cm
		Untrkonstruktion/ Hinterlüftung	5,00 cm
		Winddichte Folie	0,06 cm
	A2	Dämmung	18,00 cm
		Mineralischer Klebe- und Armierungsmörtel	0,40 cm
		Stahlbeton lt. Statik (2400kg/m³)	20,00 cm
		Innenspachtelung	0,20 cm
AW02		**Feuermauer angebaut Straßentrakt**	
	A2	Dämmung	14,00 cm
		Stahlbeton lt. Statik (2400kg/m³)	18,00 cm
		Innenspachtelung	0,20 cm
AW03		**Feuermauer im Außenbereich Straßentrakt**	
		Außenputz	0,20 cm
		Grundbeschichtung	0,10 cm
		Glasarmierung	0,10 cm
		Mineralischer Klebe- und Armierungsmörtel	0,20 cm
	A2	Dämmung	18,00 cm
		Mineralischer Klebe- und Armierungsmörtel	0,40 cm
		Stahlbeton lt. Statik (2400kg/m³)	18,00 cm
		Innenspachtelung	0,20 cm
AW04		**Feuermauer angebaut mit VS Straßentrakt**	
	A2	Dämmung	14,00 cm
		Stahlbeton lt. Statik (2400kg/m³)	18,00 cm
		CW-Profil	7,50 cm
		2x1,25 GK-Platte	2,50 cm
AW05		**Aussenwand Hoftrakt**	
		Außenputz	0,20 cm
		Grundbeschichtung	0,10 cm
		Glasarmierung	0,10 cm
		Mineralischer Klebe- und Armierungsmörtel	0,20 cm
	A2	Dämmung	20,00 cm
		Mineralischer Klebe- und Armierungsmörtel	0,40 cm
		Stahlbeton lt. Statik (2400kg/m³)	18,00 cm
		Innenspachtelung	0,20 cm
AW05a		**Feuermauer im Außenbereich Hoftrakt**	
		Außenputz	0,20 cm
		Grundbeschichtung	0,10 cm
		Glasarmierung	0,10 cm
		Mineralischer Klebe- und Armierungsmörtel	0,20 cm
		Dämmung	20,00 cm
		Mineralischer Klebe- und Armierungsmörtel	0,40 cm
		Stahlbeton lt. Statik (2400kg/m³)	18,00 cm
		Innenspachtelung	0,20 cm
AW06		**Wand an der Grundgrenze**	
		Stahlbeton lt. Statik (2400kg/m³)	20,00 cm
AW07		**Außenwand Keller**	
		Bohrpfahlwand Bohfahlwand	58,00 cm
AW08		**Außenwand Aufzug über Dach**	
		Außenputz	0,20 cm
		Grundbeschichtung	0,10 cm
		Glasarmierung	0,10 cm
		Mineralischer Klebe- und Armierungsmörtel	0,20 cm
		Dämmung	10,00 cm
		Mineralischer Klebe- und Armierungsmörtel	0,40 cm
		Stahlbeton lt. Statik (2400kg/m³)	14,00 cm

INNENWÄNDE

IW01		**Trennwand STB zw. Wohnungen**	
		Gipskartonplatte	1,25 cm
		CW-Profil	5,00 cm
	A2	dazw. Mineralwolle	
		Stahlbeton lt. Statik (2400kg/m³)	18,00 cm
		Innenspachelung	0,20 cm
IW01a		**Trennwand STB zw. Wohnungen + Installation**	
		2x1,25 Gipskartonplatten	2,50 cm
		CW-Profil für Installationen	7,50 cm
		Bauplatte	1,25 cm
		CW-Profil dazw. Dämmung	5,00 cm
		Stahlbeton lt. Statik (2400kg/m³)	18,00 cm
		Innenspachtelung	0,20 cm
IW02		**Trennwand STB zw. Wohnung u. Aufzug**	
		Stahlbeton lt. Statik (2400kg/m³)	18,0 cm
		Trennfugenplatte	5,00 cm
		Stahlbeton lt. Statik (2400kg/m³)	18,00 cm
		CW-Profil	5,00 cm
	A2	dazw. Mineralwolle	
		Gipskartonplatte	1,25 cm
IW03		**Trennwand zw. Wohnung u. Gang**	
		Gipskartonplatte	1,25 cm
		PE-Folie	0,02 cm
		CW-Profil dazw. Dämmung	5,00 cm
		Stahlbeton lt. Statik (2400kg/m³)	18,00 cm
		Innenspachtelung	0,20 cm
IW04		**Trennwand zw. Wohnung u. Einfahrt**	
		Außenputz	0,20 cm
		Grundbeschichtung	0,10 cm
		Glasarmierung	0,10 cm
		Mineralischer Klebe- und Armierungsmörtel	0,20 cm
		Dämmung	16,00 cm
		Mineralischer Klebe- und Armierungsmörtel	0,40 cm
		Stahlbeton lt. Statik (2400kg/m³)	18,00 cm
		Innenspachtelung	0,20 cm
IW05		**Trennwand zw. Wohnung u. Müllraum**	
		Gipskartonplatte	1,25 cm
		PE-Folie	0,02 cm
	A2	CW-Profil dazw. Dämmung	5,00 cm
		Stahlbeton lt. Statik (2400kg/m³)	18,00 cm
		Innenspachtelung	0,20 cm
IW06		**Schachtwand**	
	EI90	3x1,5 GKF	4,50 cm
	A2	CW-Profil dazw. Dämmung	5,00 cm
IW07		**Scheidewand tragend**	
		Innenspachtelung	0,20 cm
		Stahlbeton lt. Statik	18,00 cm
		Innenspachtelung	0,20 cm
IW08		**Scheidewand**	
		Gipskartonplatte	1,25 cm
		CW-Profil dazw. Dämmung	7,50 cm
		Gipskartonplatte	1,25 cm
IW08a		**Scheidewand Bad+WC**	
		Gipskartonplatte	1,25 cm
		Hygrodiode	
		CW-Profil dazw. Dämmung	7,50 cm
		Gipskartonplatte	1,25 cm
IW09		**Innenwand Keller**	
		Stahlbeton lt. Statik (2400kg/m³)	18,00 - 25,00 cm
IW09a		**Innenwand Keller gedämmt**	
		Stahlbeton lt. Statik (2400kg/m³)	25,00 cm
	A2	Dämmung	12,00 cm

DECKENAUFBAUTEN

Dächer

DA01		**Terrasse über Tiefgarage**	
		Belag	2,00 cm
		Splittbett	3,00 cm
		Tragschicht	18,00 cm
		Schutzvlies	0,20 cm
		Abdichtung wurzelfest	0,50 cm
		Abdichtung 2-lagig	1,00 cm
		Gefälledämmung	8,00 cm im Mittel
		Stahlbetondecke lt. Statik (2400kg/m³)	35-65 cm
DA02		**Gründach über Tiefgarage**	
		Pflanzsubstrat für Gründach	20,00 cm
		Filtervlies	0,02 cm
		Drainageplatte	3,00 cm
		Schutzvlies	0,20 cm
		Abdichtung wurzelfest	0,50 cm
		Abdichtung 2-lagig	1,00 cm
		Gefälledämmung	8,00 cm im Mittel
		Stahlbetondecke lt. Statik (2400kg/m³)	35-65 cm
DA03		**Kinderplatz über Rampe der Tiefgarage**	
		Fallschutzplatten	4,00 cm
		Splittbett	4,00 cm
		Schutzvlies	0,02 cm
		Abdichtung	1,00 cm
		Dämmung	8,00 cm
		Abdichtung 2-lagig	1,00 cm
		Voranstrich	
		Stahlbetondecke lt. Statik (2400kg/m³)	35-65 cm
DA04		**Gehweg über Tiefgarage**	
		Asphalt	3,00 cm
		Bodenestrich bewehrt	6,00 cm
		Trennlage	
		Tragschicht	14,00 cm
		Schutzvlies	0,20 cm
		Abdichtung wurzelfest	0,50 cm
		Abdichtung 2-lagig	1,00 cm
		Gefälledämmung	8,00 cm im Mittel
		Stahlbetondecke lt. Statik (2400kg/m³)	35-65 cm
DA05		**Terrasse über Wohnung u. Gaupen**	
		Estrichplatten in Splittbett	5,00 cm
		Schutzvlies	0,20 cm
		Abdichtung 2-lagig	1,00 cm
		Gefälledämmung mit 2% Gefälle	20,00 cm im Mittel
		Dampfbremse mit Voranstrich	0,10 cm
		Stahlbetondecke lt. Statik (2400kg/m³)	20,00 cm
		Innenspachtelung	0,20 cm
DA06		**Dachschräge Beton**	
		Blechdeckung	
		Trennlage	0,20 cm
		Vollholzschalung	2,40 cm
		Konterlattung / Hinterlüftung	5,00 cm
		Unterdeckbahn / Winddichtung	0,10 cm
		Vollholzschalung	2,50 cm
	A2	Sparren 8x12cm dazw. Dämmung	12,00 cm
	A2	Lattung 8x8cm dazw. Dämmung	8,00 cm
		Dampfbremse	0,04 cm
		Stahlbetondecke lt. Statik (2400kg/m³)	23,00 cm
		Innenspachtelung	0,20 cm
DA07		**Flachdach begrünt**	
		Pflanzsubstrat für Gründach	11,00 cm
		Filtervlies	0,02 cm
		Drainageplatte	3,00 cm
		Gummigranulatplatte	1,00 cm
		Abdichtung 2-lagig	1,00 cm
		Gefälledämmung mit 2% Gefälle	ca.25 cm im Mittel
		Dampfbremse	0,05 cm
		Stahlbetondecke lt. Statik (2400kg/m³)	20,00 cm
		Innenspachtelung	0,02 cm
DA08		**Flachdach über Aufzug**	
		Kies	5,00 cm
		Schutzvlies	0,20 cm
		Abdichtung 2-lagig	1,00 cm
		Dämmung	28,00 cm
		Abdichtung 2-lagig	1,00 cm
		Dampfbremse mit Voranstrich	0,10 cm
		Stahlbetondecke lt. Statik (2400kg/m³)	20,00 cm
DA09		**Gaupendach**	
		Estrichplatten im Splittbett	5,00 cm
		Schutzvlies	0,20 cm
		Abdichtung 2-lagig	1,00 cm
		Gefälledämmung mit 2% Gefälle	20,00 cm im Mittel
		Dampfbremse mit Voranstrich	0,10 cm
		Stahlbetondecke lt. Statik (2400kg/m³)	20,00 cm
		Innenspachtelung	0,20 cm
DA10		**Balkon - thermisch getrennt mit Isokorb**	
		Belag für Außenbereich	2,00 cm
		Splittbett mit Gegengefälle	4,00 cm
		Schutzvlies	0,50 cm
		Abdichtung 2-lagig	1,00 cm
		Stahlbetonplatte mit 2% Gefälle	16,00 cm

Zwischendecken

DE01		**Boden Tiefgarage**	
		Epoxybeschichtung	cm
		Grundierung	0,50 cm
		Fundamentplatte aus Dichtbeton im Gefälle lt. Statik	60,00 cm
		Gleitschchicht + Vlies	0,50 cm
		XPS	5,00 cm
		Sauberkeitsschicht	5,00 cm
		Folie	0,02 cm
DE02		**Boden Keller / Nebenräume**	
		Estrich/ Beschichtung	cm
		Abdichtung	0,50 cm
		Fundamentplatte aus Dichtbeton lt. Statik	40,00 cm
		Gleitschchicht+Vlies	0,50 cm
		XPS	5,00 cm
		Sauberkeitsschicht	5,00 cm
		Folie	0,02 cm
DE03		**Tiefgaragenrampe**	
		Epoxybeschichtung	cm
		Grundierung	0,50 cm
		Abdichtung	1,00 cm
		Stahlbetonplate lt. Statik	20,00 cm
DE04		**Decke Apartment's über Tiefgarage**	
		Bodenbelag	1,00 cm
		Heizestrich	7,00 cm
		Folie	0,01 cm
		Trittschalldämmung	3,00 cm
		Folie	0,01 cm
	A2	Dämmung	10,00 cm
		Schüttdämmstoff	9,00 cm
		Stahlbetondecke lt. Statik (2400kg/m³)	35-60 cm
		Dämmung	16,00 cm
DE05		**Decke Müllraum über Tiefgarage**	
		Gußasphalt	
		Abdichtung	
		Gefällebeton	ca. 5,00 cm
		Stahlbetondecke lt. Statik (2400kg/m³)	35,00 cm
	A2	Dämmung	16,00 cm
DE06		**Decke Stiegenhaus / Gang über Tiefgarage**	
		Bodenbelag	1,00 cm
		Estrich	7,00 cm
		Folie	0,01 cm
		Trittschalldämmung	3,00 cm
		Folie	0,01 cm
		Schüttdämmstoff	4,00 cm
		Stahlbetondecke lt. Statik (2400kg/m³)	35,00 cm
		Dampfbremse	0,01 cm
		Mineralischer Klebe- und Armierungsmörtel	0,40 cm
	A2	Dämmung	16,00 cm
		Innenspachtelung	0,20 cm
DE07		**Stiegenpodest**	
		Bodenbelag	1,00 cm
		Estrich	5,00 cm
		Folie	0,02 cm
		Trittschalldämmung	3,00 cm
		Folie	0,02 cm
		Schüttdämmstoff	3,50 cm
		Stahlbetondecke lt. Statik (2400kg/m³)	20,00 cm
		Innenspachtelung	0,20 cm
DE08		**Betonstiege**	
		Belag	1,00 cm
		Betonfertigteile lt. Statik	18,00 cm
DE09		**Regelgeschoßdecke Wohnung**	
		Bodenbelag	1,00 cm
		Heizestrich	7,00 cm
		Folie	0,01 cm
		Trittschalldämmung	3,00 cm
		Folie	0,01 cm
		Schüttdämmstoff	4,00 cm
		Stahlbetondecke lt. Statik (2400kg/m³)	20,00 cm
		Innenspachtelung	0,20 cm
DE09a		**Regelgeschoßdecke Unterseite gedämmt**	
		Bodenbelag	1,00 cm
		Heizestrich	7,00 cm
		Folie	0,01 cm
		Trittschalldämmung	3,00 cm
		Folie	0,01 cm
		Schüttdämmstoff	4,00 cm
		Stahlbetondecke lt. Statik (2400kg/m³)	20,00 cm
		Dämmung	16,00 cm
		Innenspachtelung	0,20 cm
DE10		**Regelgeschoßdecke Stiegenhaus / Gang**	
		Bodenbelag	1,00 cm
		Estrich	7,00 cm
		Folie	0,02 cm
		Trittschalldämmung	3,00 cm
		Folie	0,01 cm
		Schüttdämmstoff	4,00 cm
		Stahlbetondecke lt. Statik (2400kg/m³)	20,00 cm
		Innenspachtelung	0,20 cm
DE11		**Decke Wohnung über Außenluft**	
		Bodenbelag	1,00 cm
		Heizestrich	7,00 cm
		Folie	0,01 cm
		Trittschalldämmung	3,00 cm
		Folie	0,01 cm
		Schüttdämmstoff	4,00 cm
		Stahlbetondecke lt. Statik (2400kg/m³)	20,00 cm
		Dampfbremse	0,01 cm
		Mineralischer Klebe- und Armierungsmörtel	0,40 cm
	A2	Dämmung	16,00 cm
		Mineralischer Klebe- und Armierungsmörtel	0,20 cm
		Glasarmierung	0,10 cm
		Grundbeschichtung	0,10 cm
		Außenputz	0,20 cm
DE12		**Decke Wohnung über unbeheizten Räumen**	
		Bodenbelag	1,00 cm
		Heizestrich	7,00 cm
		Folie	0,01 cm
		Trittschalldämmung	3,00 cm
		Folie	0,01 cm
		Schüttdämmstoff	4,00 cm
		Stahlbetondecke lt. Statik (2400kg/m³)	20,00 cm
		Dampfbremse	0,01 cm
		Mineralischer Klebe- und Armierungsmörtel	0,40 cm
		Dämmung	16,00 cm
		Innenspachtelung	0,20 cm