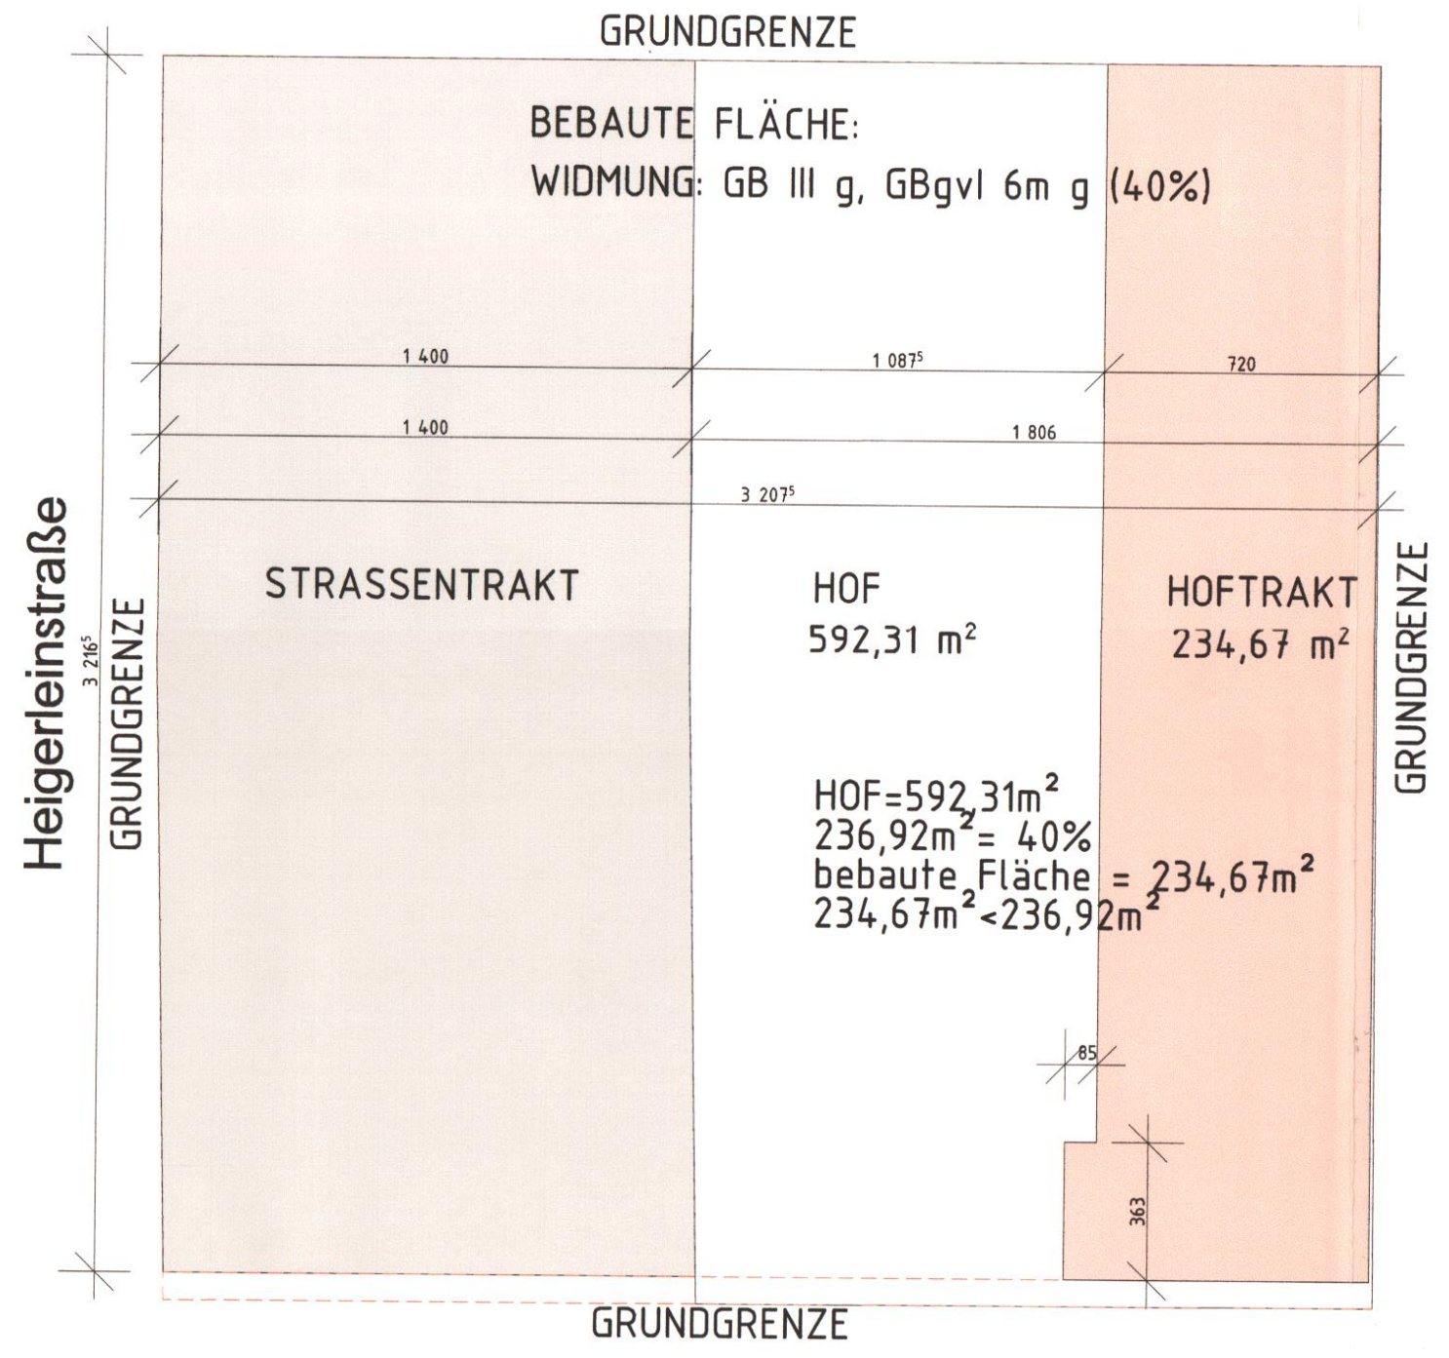

BERECHNUNG BEBAUTE FLÄCHE

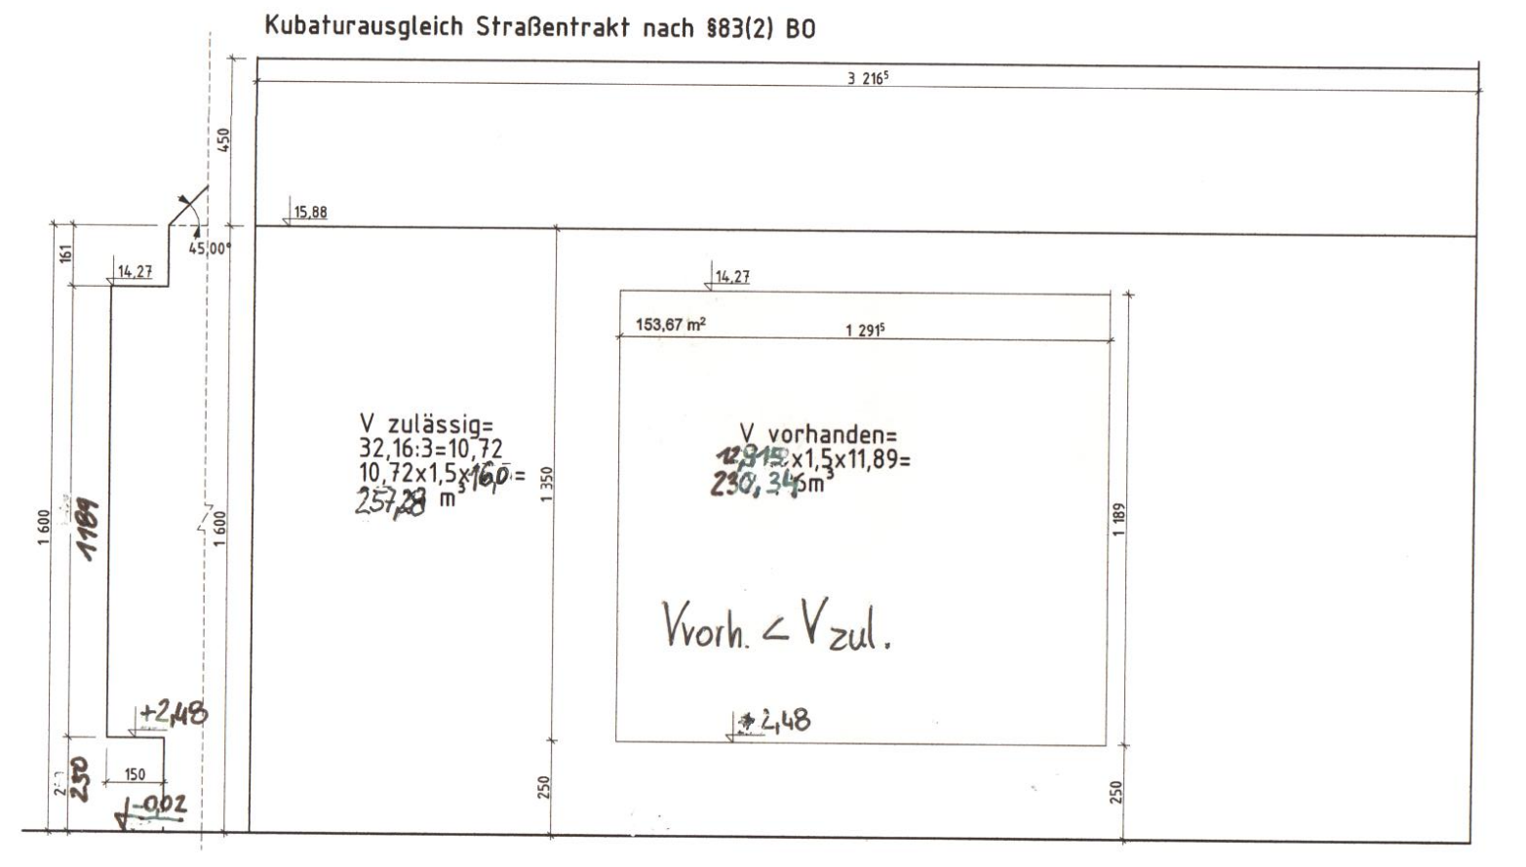

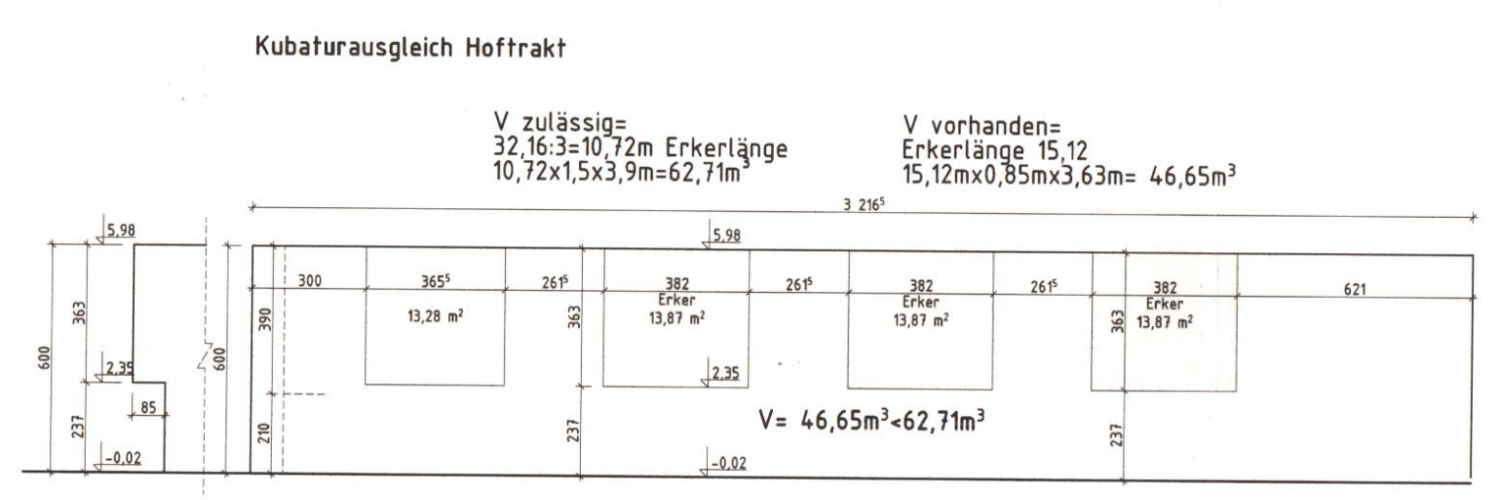

KUBATURAUSGLEICH

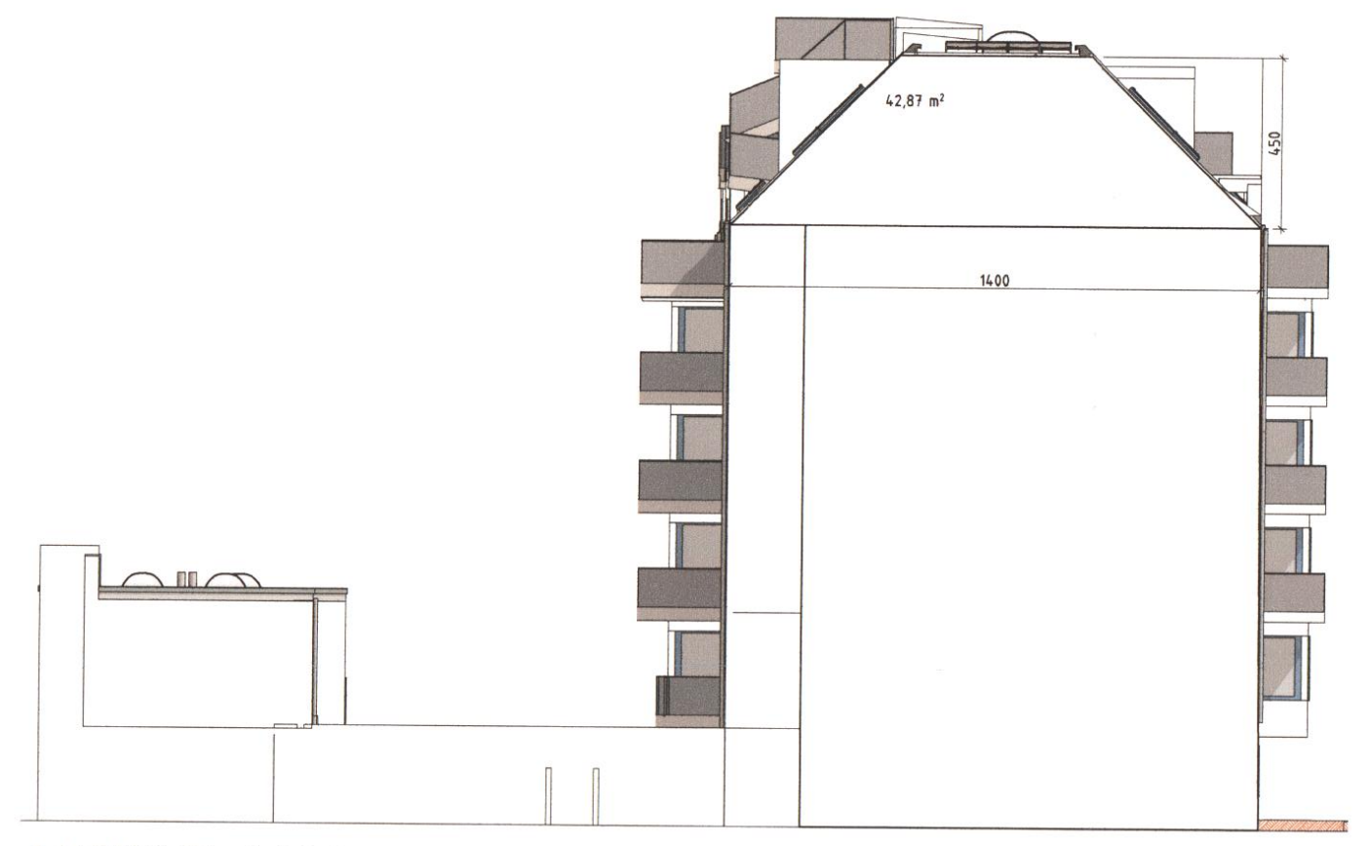

ANSICHT 1:200
BERECHNUNG GIEBELFLÄCHE

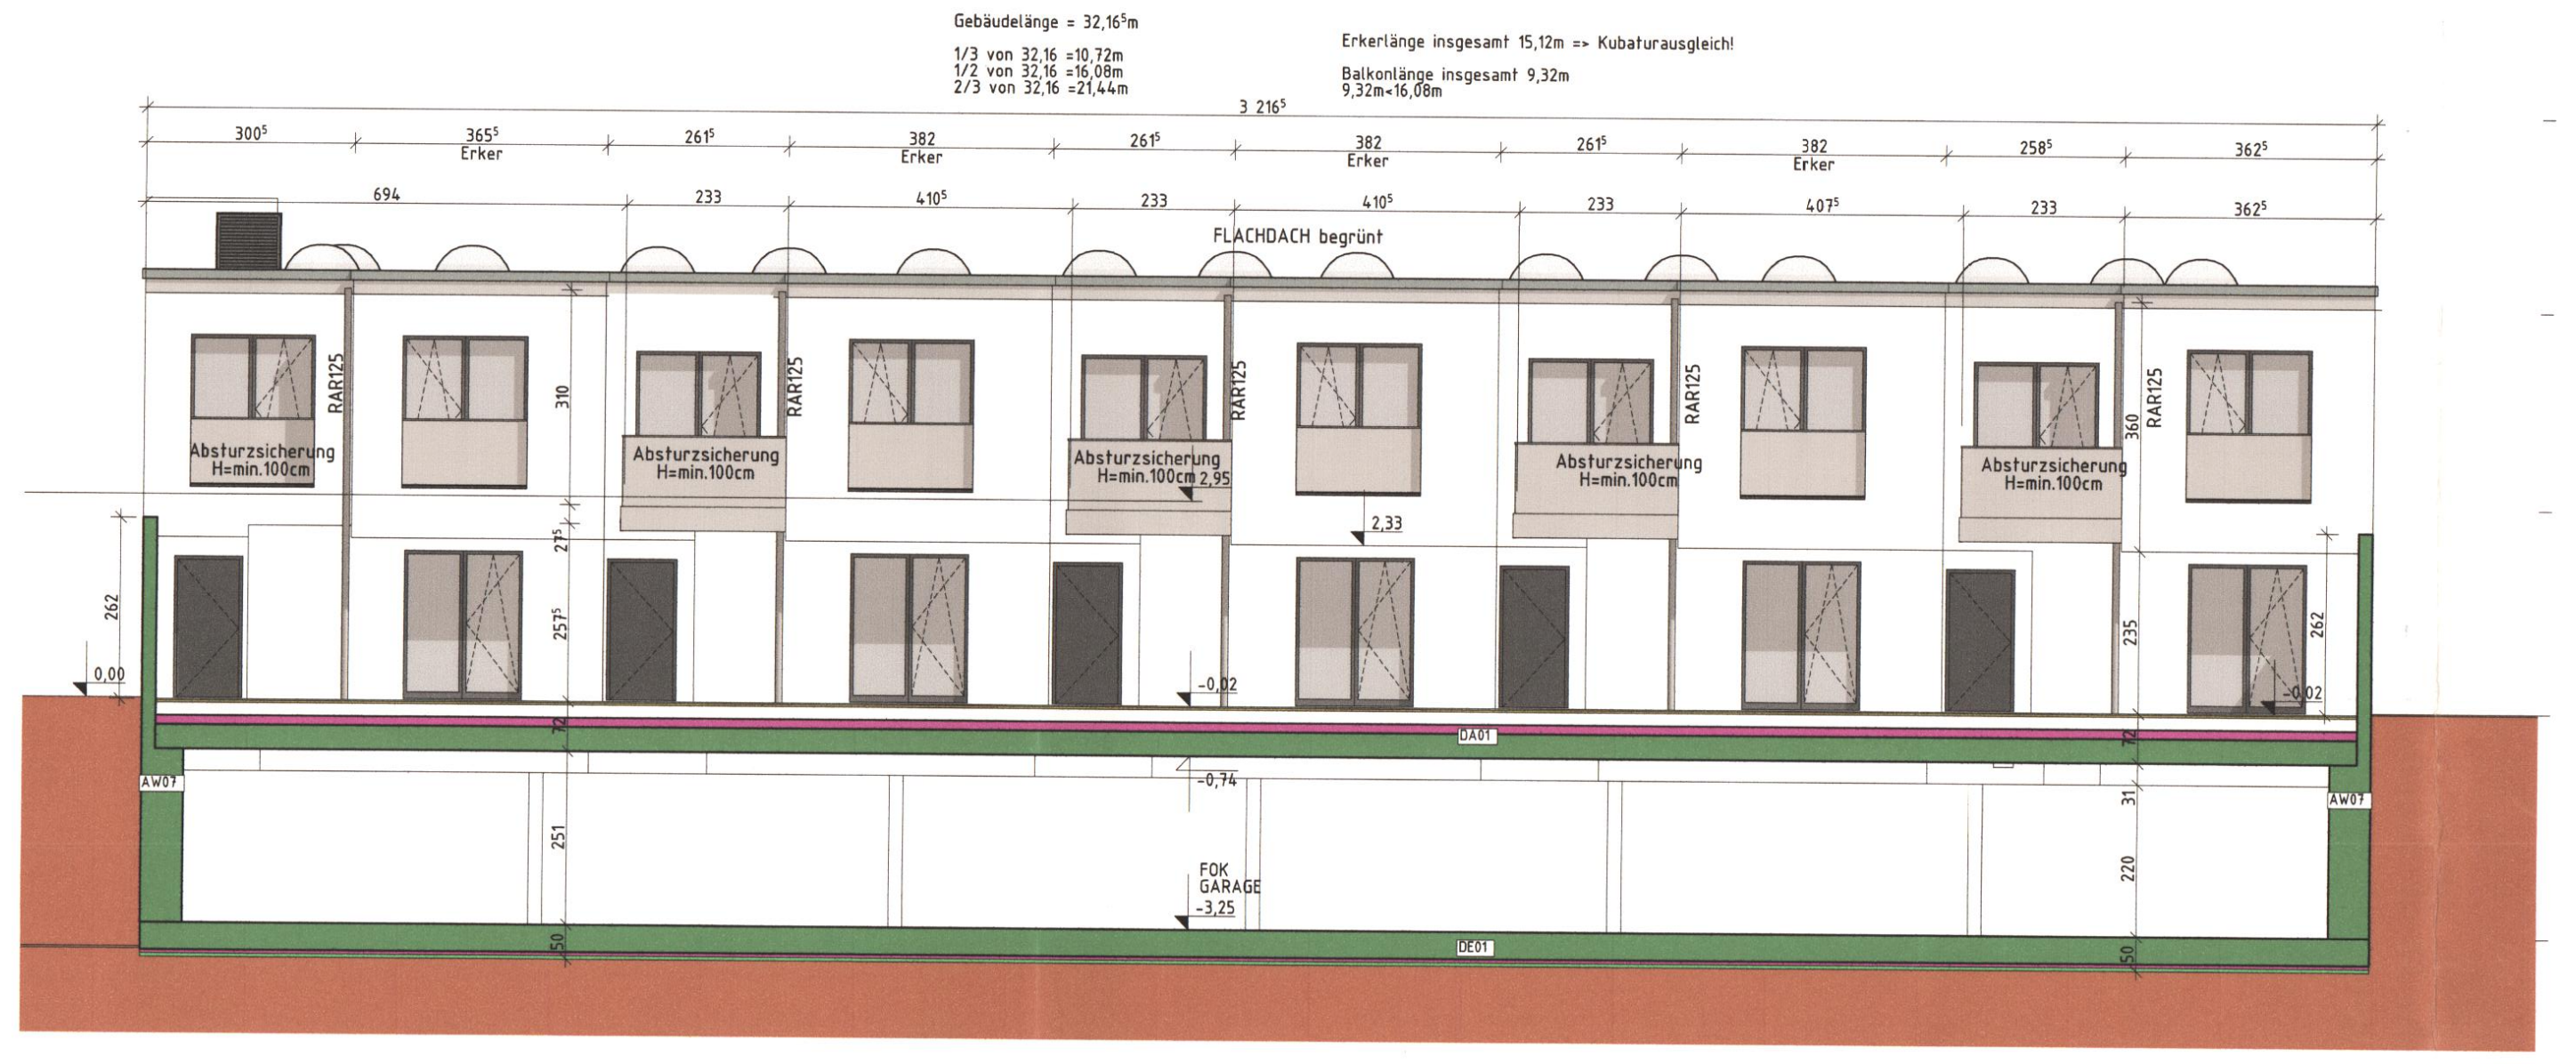

HOFTRAKT. WESTANSICHT 1:100

VISUALISIERUNGEN DIENEN LEDIGLICH ZUR BESSEREN DARSTELLUNG DES ENTWURFS UND SIND FÜR DIE EINREICHUNG NICHT RELEVANT.

STELLPLATZNACHWEIS: 2264m² WOHNNUTZFLÄCHE = 22 STELLPLÄTZE
5 REIHENHÄUSER = 1 STELLPLATZ
INSGESAMT 23 STELLPLÄTZE
22 STELLPLÄTZE VORHANDEN

FAHRRAD-STELLPLATZNACHWEIS: 2264m² WOHNNUTZFLÄCHE / 30m²
min. 75 FAHRRADABSTELLPLÄTZE

BETTENANZAHL: INSGESAMT 5 REIHENHÄUSER (BEHERBERGUNGSBETRIEB)
2 BETTEN PRO BETRIEBSEINHEIT
INSGESAMT 10 BETTEN

LEGENDE:

☐	BESTAND		SCHMUTZWASSER	UZ	UNTERZUG		
🟧	ABBRUCH		REGENWASSER	ÜZ	ÜBERZUG		
🟥	NEUBAU		WASSER	AR	ABFALLROHR		
			HEIZUNG	RR	REGENROHR		
🟩	STAHLBETON		STROM	RSK	REGENSINKKASTEN		
🟩	UNBEWEHRTER BETON		GAS	PH	PARAPETHÖHE		
🟥	MAUERWERK		FERNWÄRME	STUK	STURZUNTERKANTE		
🟫	HOLZ			DL	DURCHGANGSLICHTE		
🟪	DÄMMUNG (HART)	DFF	DACHFLÄCHENFENSTER	OK	OBERKANTE		
🟧	DÄMMUNG (WEICH)	LK	LICHTKUPPEL	UK	UNTERKANTE		
▨	STAHL	VSG	VERBUND-SICHERHEITSGLAS	FOK	FUSSBODENOBERKANTE		
🟦	GLAS	ESG	EINSCHEIBEN-SICHERHEITSGLAS	WD	WANDDURCHBRUCH		
🟥	GIPSKARTON	BRE	BRANDRAUCHENTLÜFTUNG	DD	DECKENDURCHBRUCH		

- LÜFTUNGEN DURCH FREMDE BRANDABSCHNITTE EI90 UND A2 UMMANTELT
- RESTRÄUME IM DACHGESCHOSS EI60 VON INNEN 2x GKF
- WOHNUNGSEINGANGSTÜREN AUSFÜHRUNG IN EI$_2$30 IN WÄNDEN WELCHE ZUM STGH DURCH EINE E30-C TÜRE GETRENNTS SIND, ALLE ANDEREN WOHNUNGSEINGANGSTÜREN IN EI$_2$30-C
- AUSWECHSLUNGEN SIND IN REI90 UND A2 AUSZUFÜHREN
- WÄRMEVERSORGUNG MITTELS 2 SOLE/WASSER WÄRMEPUMPEN, DIE NOTWENDIGE ENERGIE WIRD ÜBER TIEFENBOHRUNGEN BEREITGESTELLT.
- PHOTOVOLTAIKANLAGE IST AM FLACHDACH VORDERTRAKT AUFGESTÄNDERT
- ALLE AUSKRAGENDEN TEILE THERMISCH GETRENNT, DÄMMUNG A2
- AUSSENLIEGENDE BAUTEILE SIND THERMISCH ZU TRENNEN, DÄMMUNGEN AN GRUNDSTÜCKSGRNEZEN A2
- INTERNE TREPPEN SIND ELASTISCH ZU LAGERN
- INSTALLATIONSSCHÄCHTE IM TREPPENBERICH SIND LT. TRVB110 AUSZUFÜHREN
- BRANDVERHALTEN VON BAUPRODUKTEN GEMÄSS DEN BESTIMMUNGEN DER OIB- RICHTLINIE 2, TABELLE 1a(GK5<6 OBERIRDISCHE GESCHOSSE) SOWIE OIB-RICHTLINIE 2.2, PKT.5.2
- ALLE INNENLIEGENDEN BÄDER UND WC's LÜFTUNG ÜBER DACH
- FÜR JEDE WOHNUNG IST EIN EINLAGERUNGSRAUM VORHANDEN
- IN JEDER WOHNUNG IST EINE GEEIGNETE AUFSTELLMÖGLICHKEIT UND EIN ANSCHLUSS FÜR EINE WASCHMASCHINE UND EINE MASCHINELLE TROCKENEINRICHTUNG VORGESEHEN.
- NIEDERSCHLAGSWÄSSER UND FÄKALWÄSSER WERDEN IN DEN ÖFFENTLICHEN KANAL GELEITET
- STIEGEN UND GÄNGE KUNSTSTEINBELAG, BELAG MÜLLRAUM UND GARAGE MIND. Bfl
- GEMÄSS OIB RICHTLINIE 2, ABSATZ 3, PUNKT 11 - UNVERNETZTE RAUCHWARNMELDER IN ALLEN AUFENTHALTSRÄUMEN (AUSGEN. KÜCHEN, BEI WOHNKÜ. NICHT IM KOCHBEREICH) SOWIE BEI GÄNGEN ÜBER DIE FLUCHTWEGE VON AUFENTHALTSR. FÜHREN
- SCHADENSFOLGEKLASSE CC2 nach ÖNORM EN 1090-2 Tab. B3
- NÄCHSTE HYDRANT BIS GRUNDGRENZE: ca.115m<150m
- ALLE INNENLIEGENDE RÄUME SIND MECHANISCH ENTLÜFTET
- SCHÄCHTE WERDEN GEMÄSS WIENER INSTALLATIONSRICHTLINIE SCHACHTTYP A AUSGEFÜHRT
- AUFZUGSSCHÄCHTE SIND MIT MIND 2,5% DES SCHACHTQUERSCHNITTS ENTLÜFTET.
- FLUCHTWEGS UND ORIENTIERUNGSBELEUCHTUNG GEMÄß DEN BESTIMMUNGEN DER TRVB 102E
- DRUCKBELÜFTUNGSANLAGE GEMÄSS DEN BESTIMMUNGEN DER TRVB 112S (AUFENTHALTSKONZEPT)- AUSLÖSUNG DBA AUTOMATISCH ÜBER RAUCHMELDER ODER MANUELL MITTELS TASTER.
- FENSTER: Uw=0,78W/m²K; Rw=41dB; g=0,5; Fc=0,07

± 0.00 ENTSPRICHT 70,2M ÜBER WIENER NULL

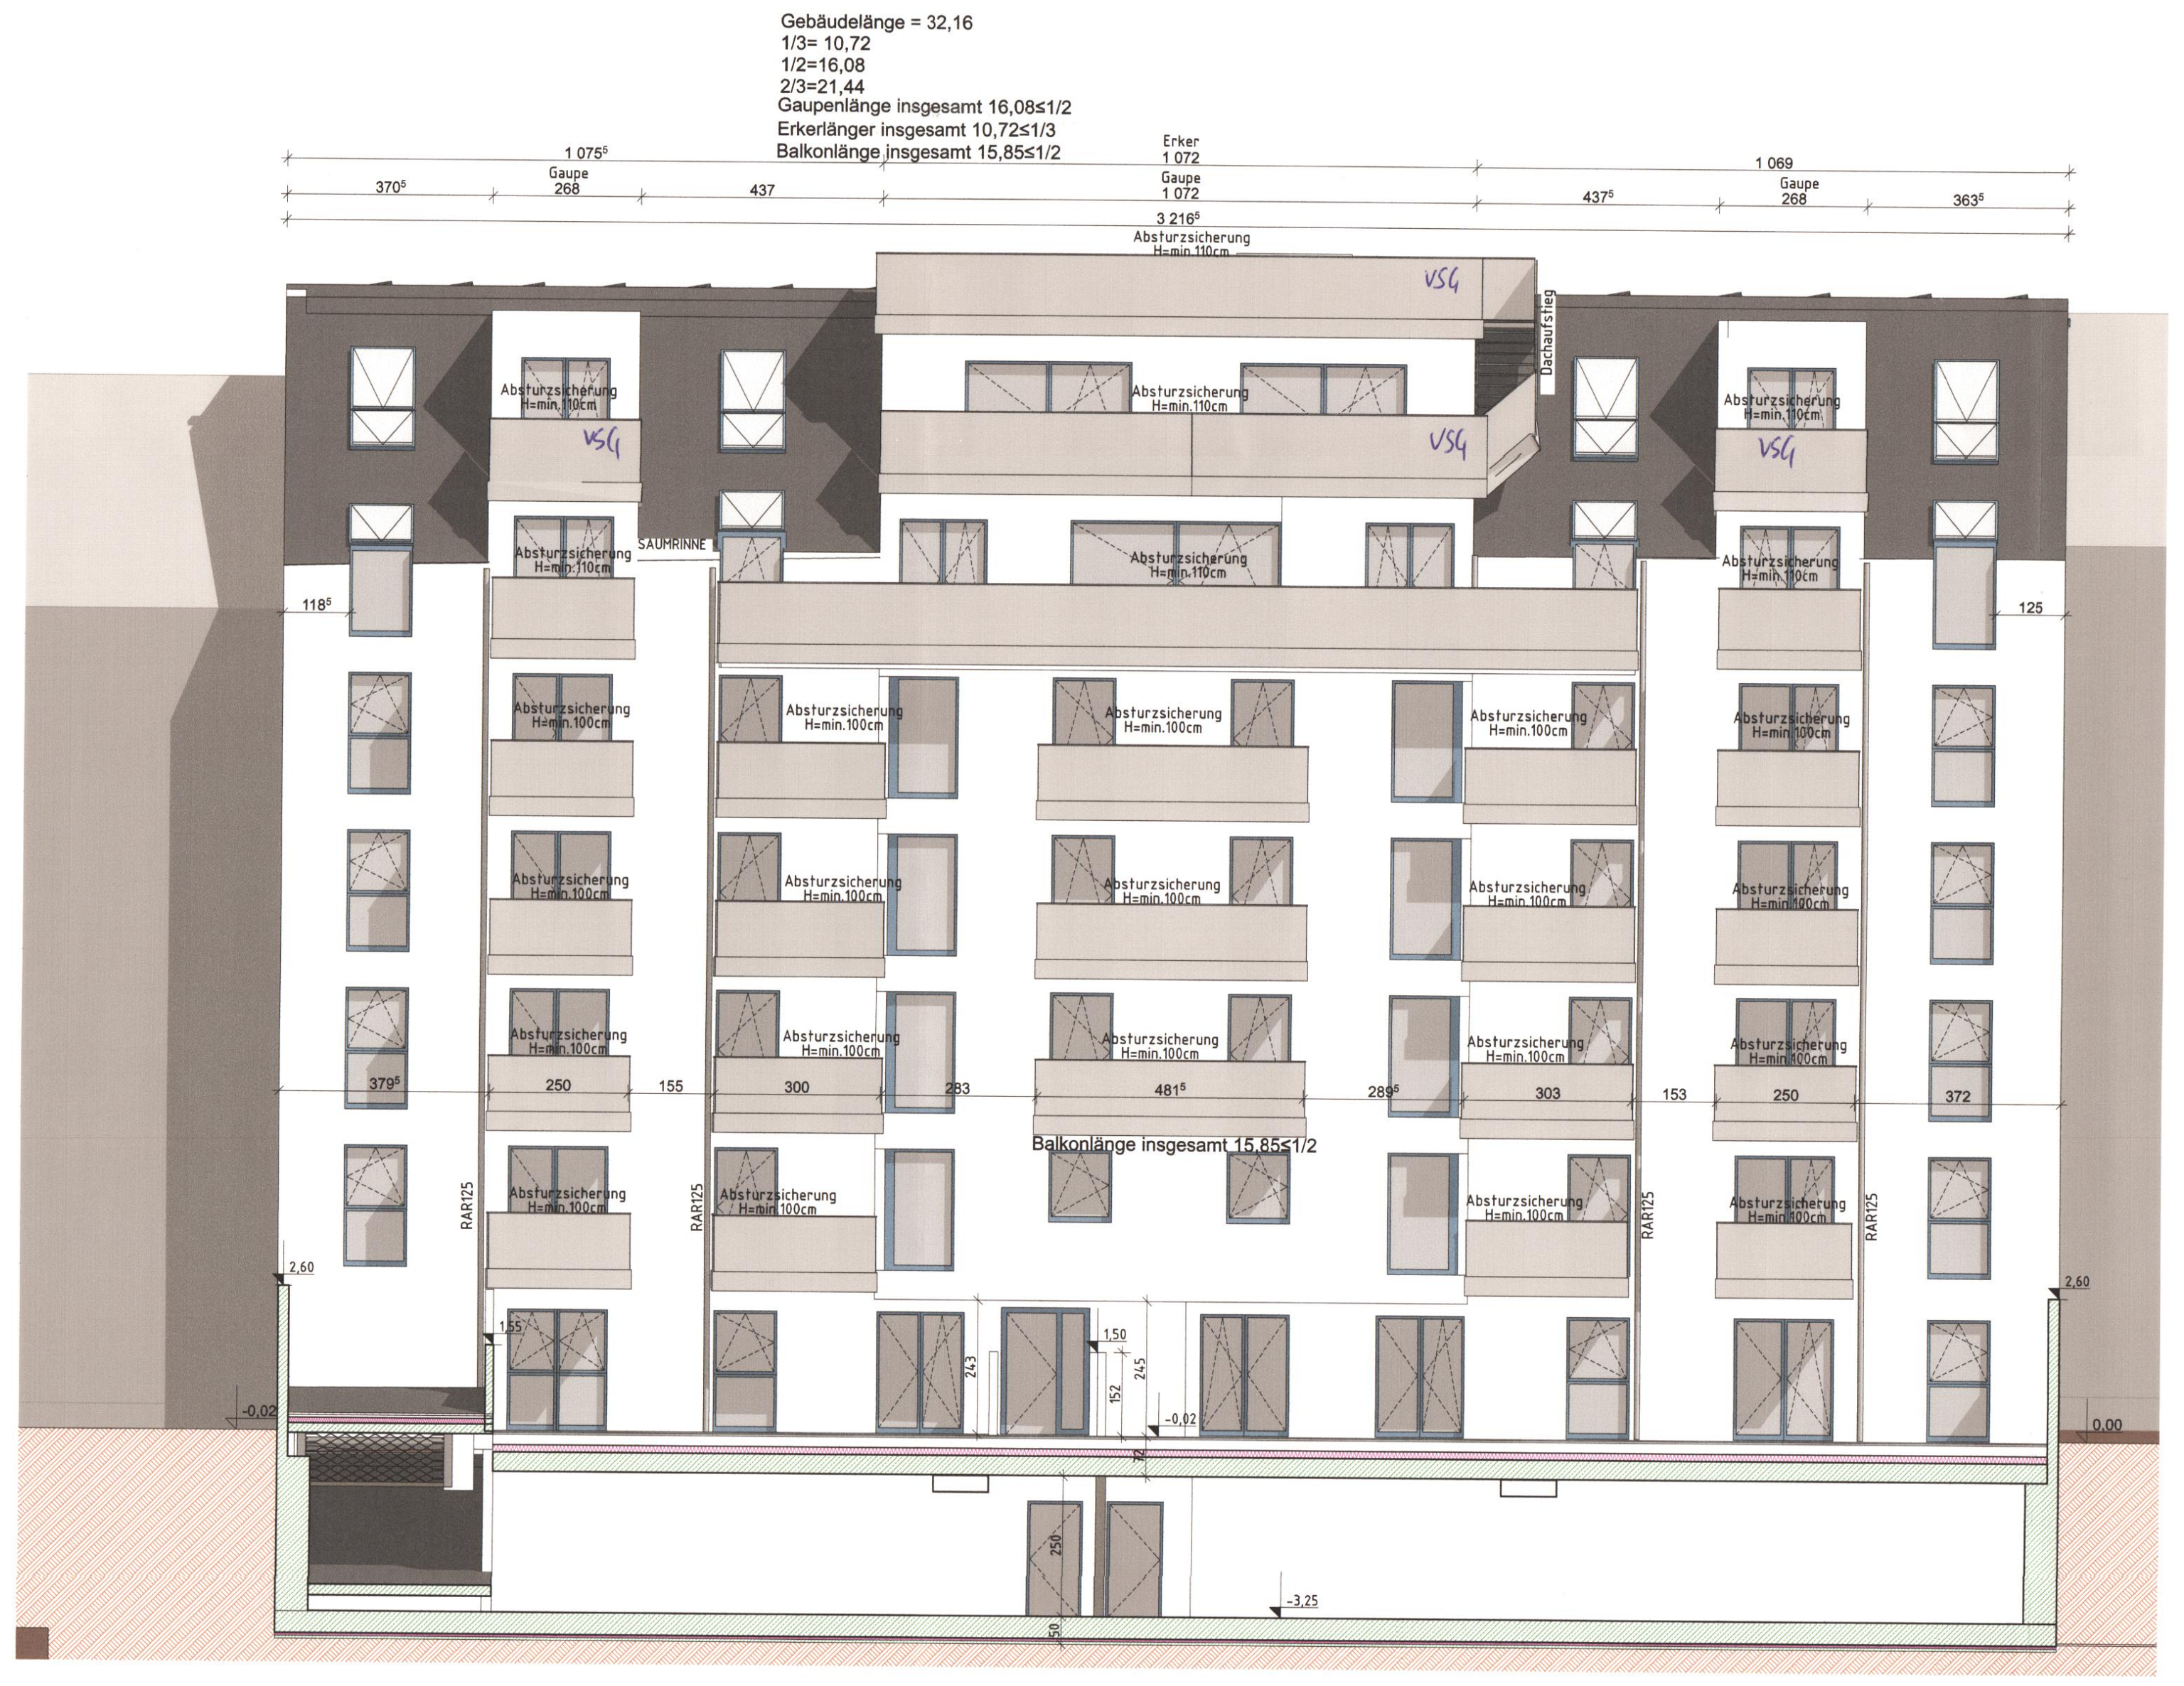
Gebäudelänge = 32,16
1/3= 10,72
1/2=16,08
2/3=21,44
Gaupenlänge insgesamt 16,08≤1/2
Erkerlänger insgesamt 10,72≤1/3
Balkonlänge insgesamt 15,85≤1/2
Erker
Gaupe
Absturzsicherung
VSG
Balkonlänge insgesamt 15,85≤1/2
RAR125

STRASSENTRAKT. OSTANSICHT 1:100

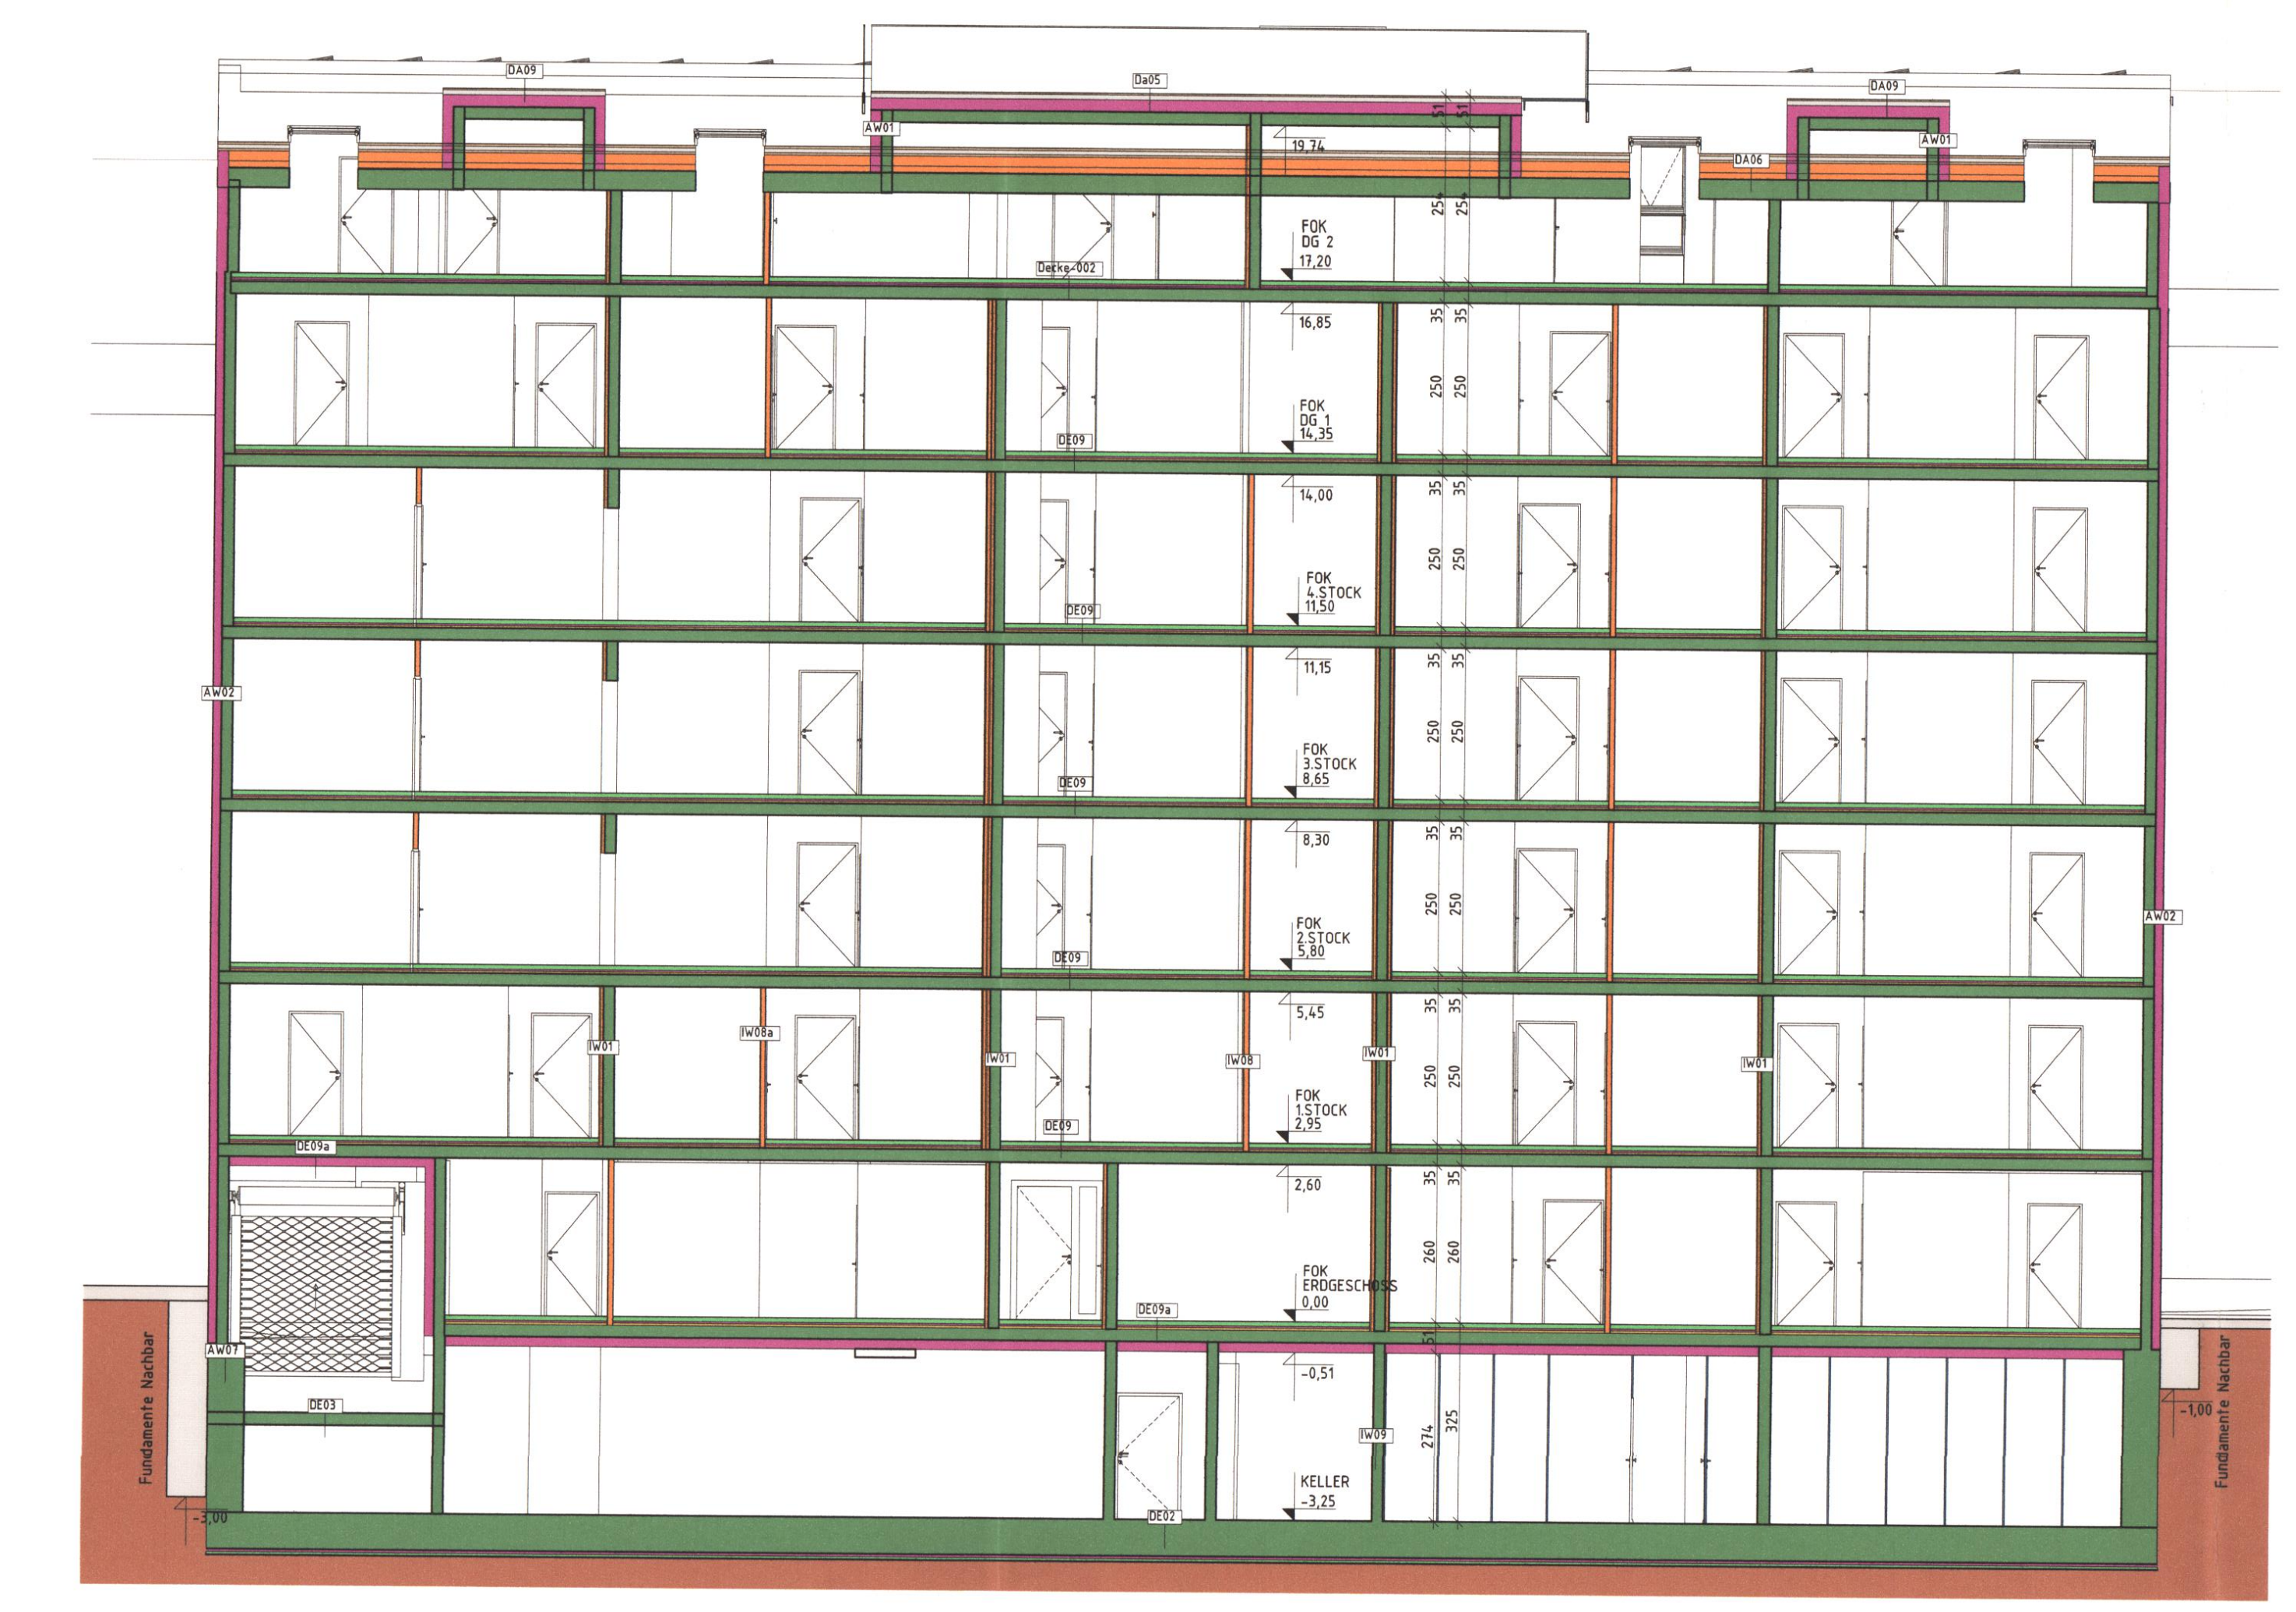

SCHNITT 1-1 1:100

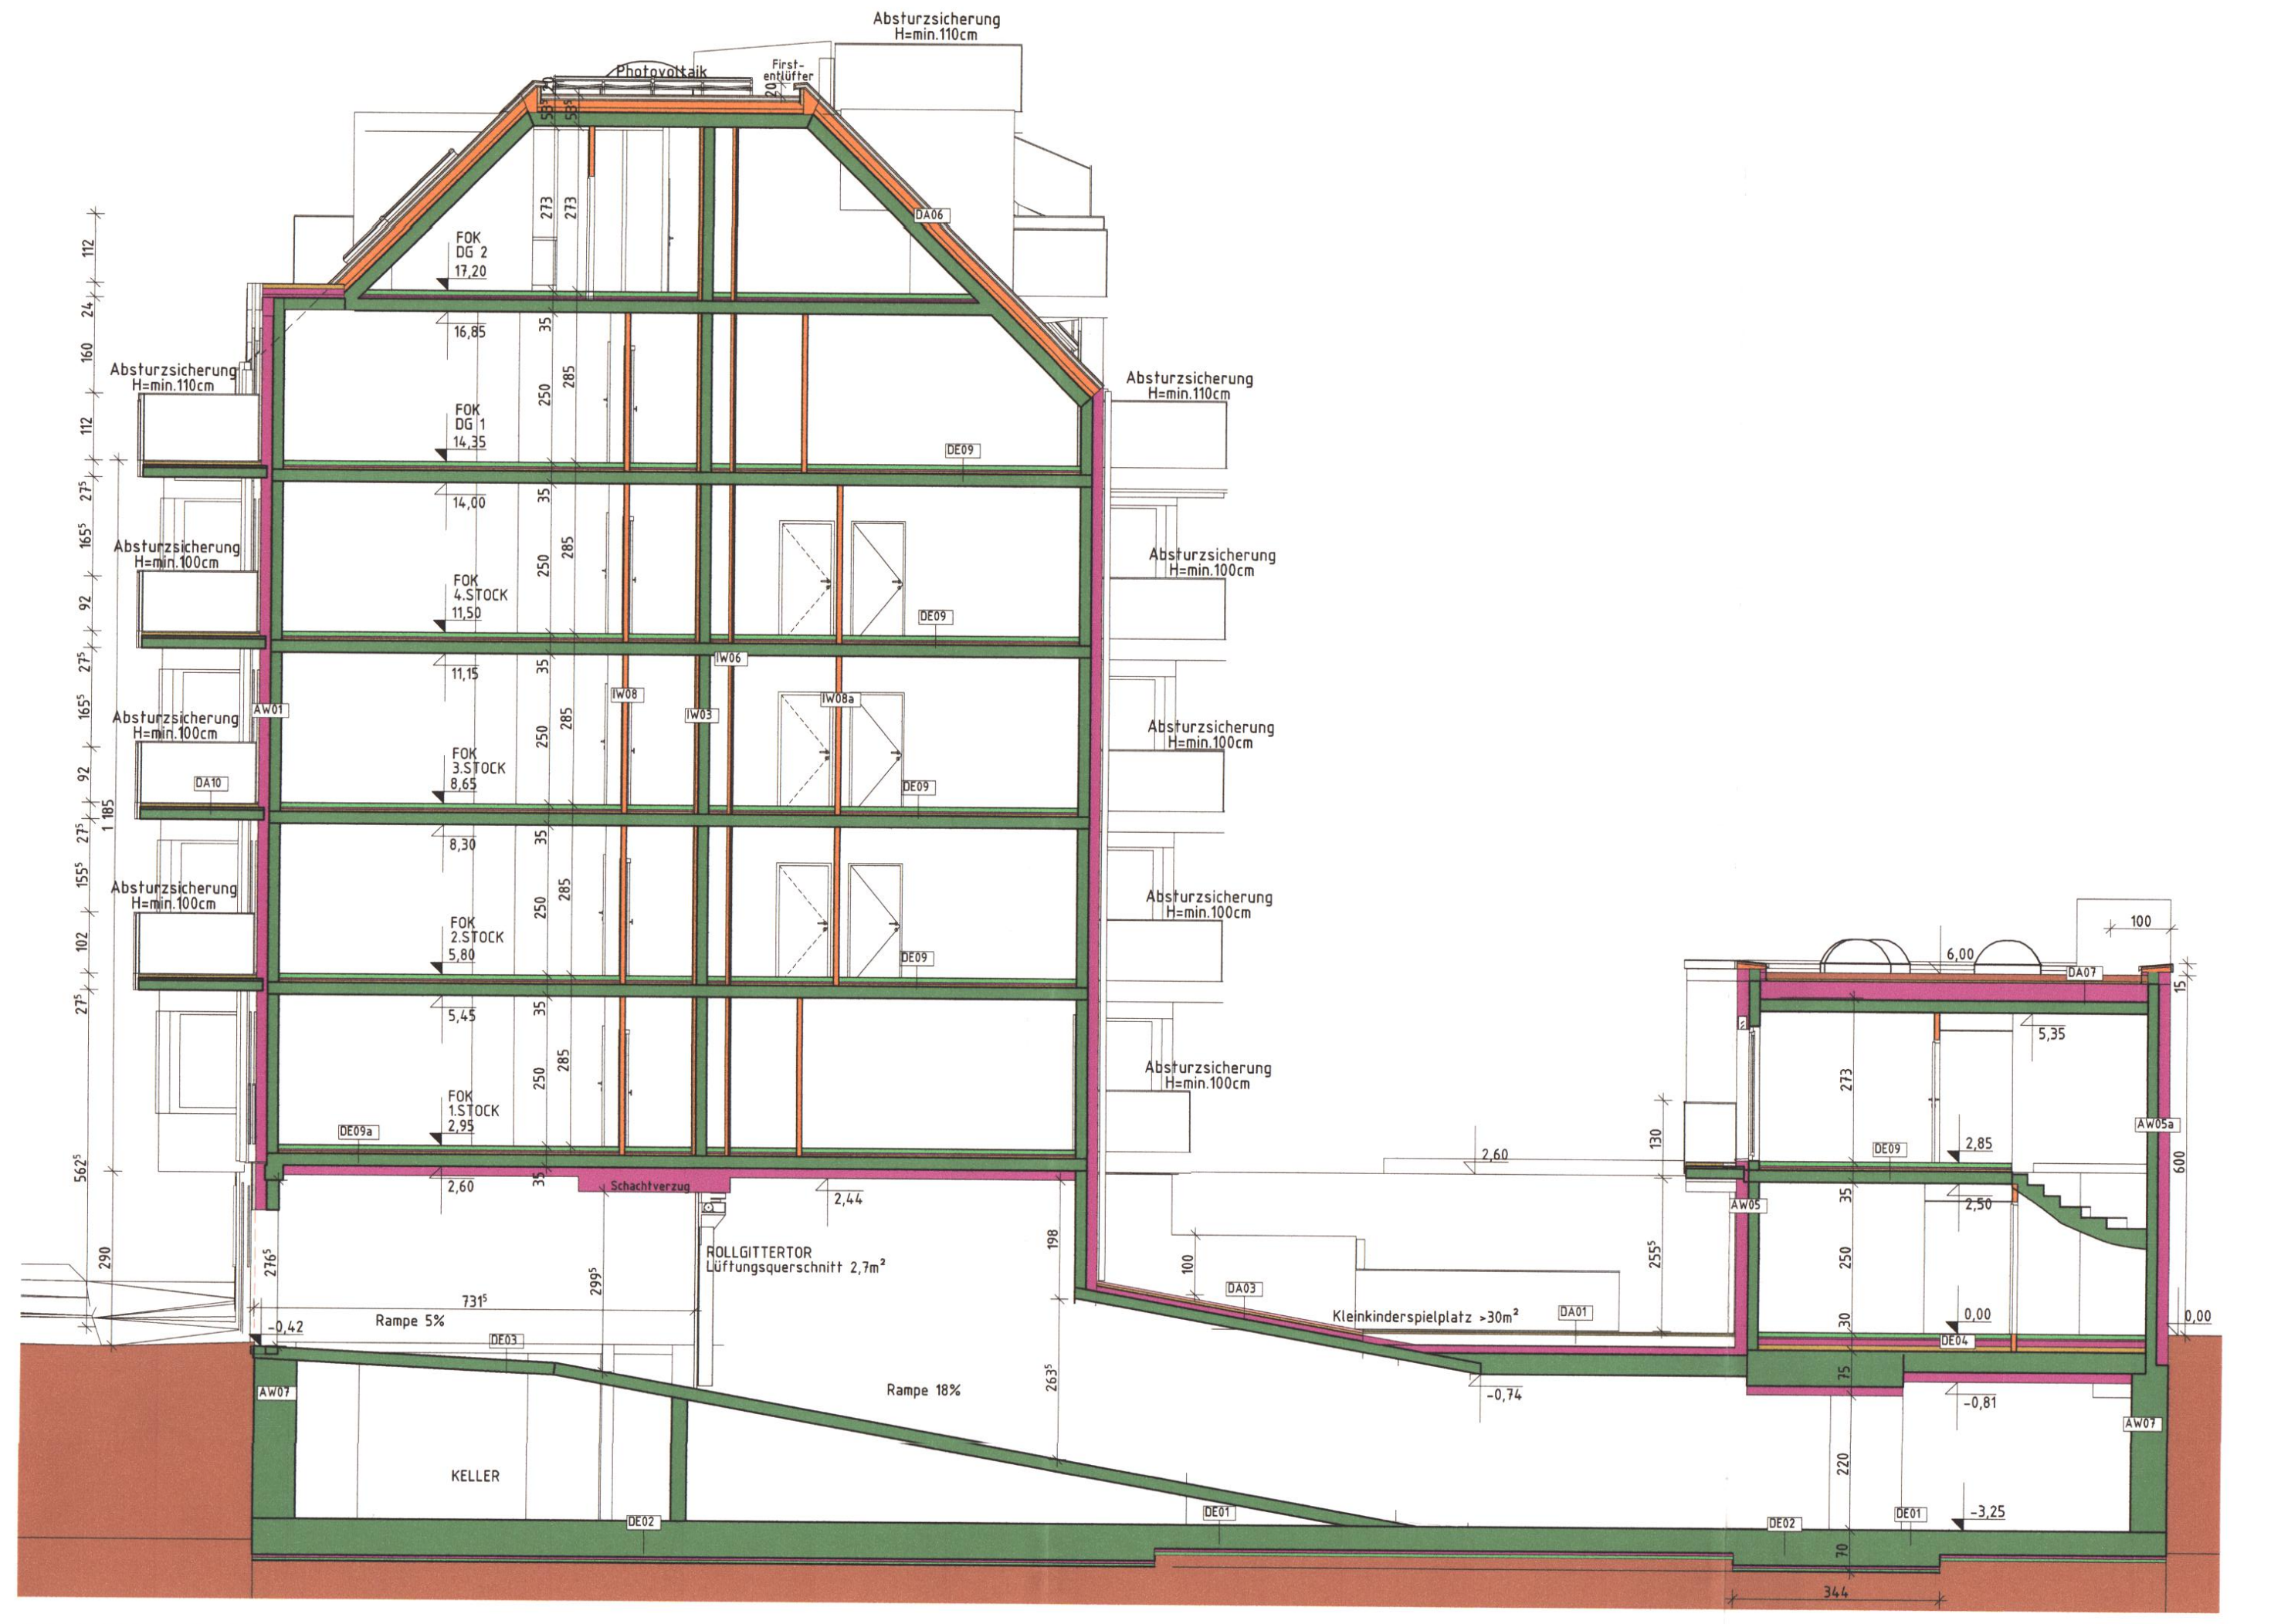

SCHNITT B-B

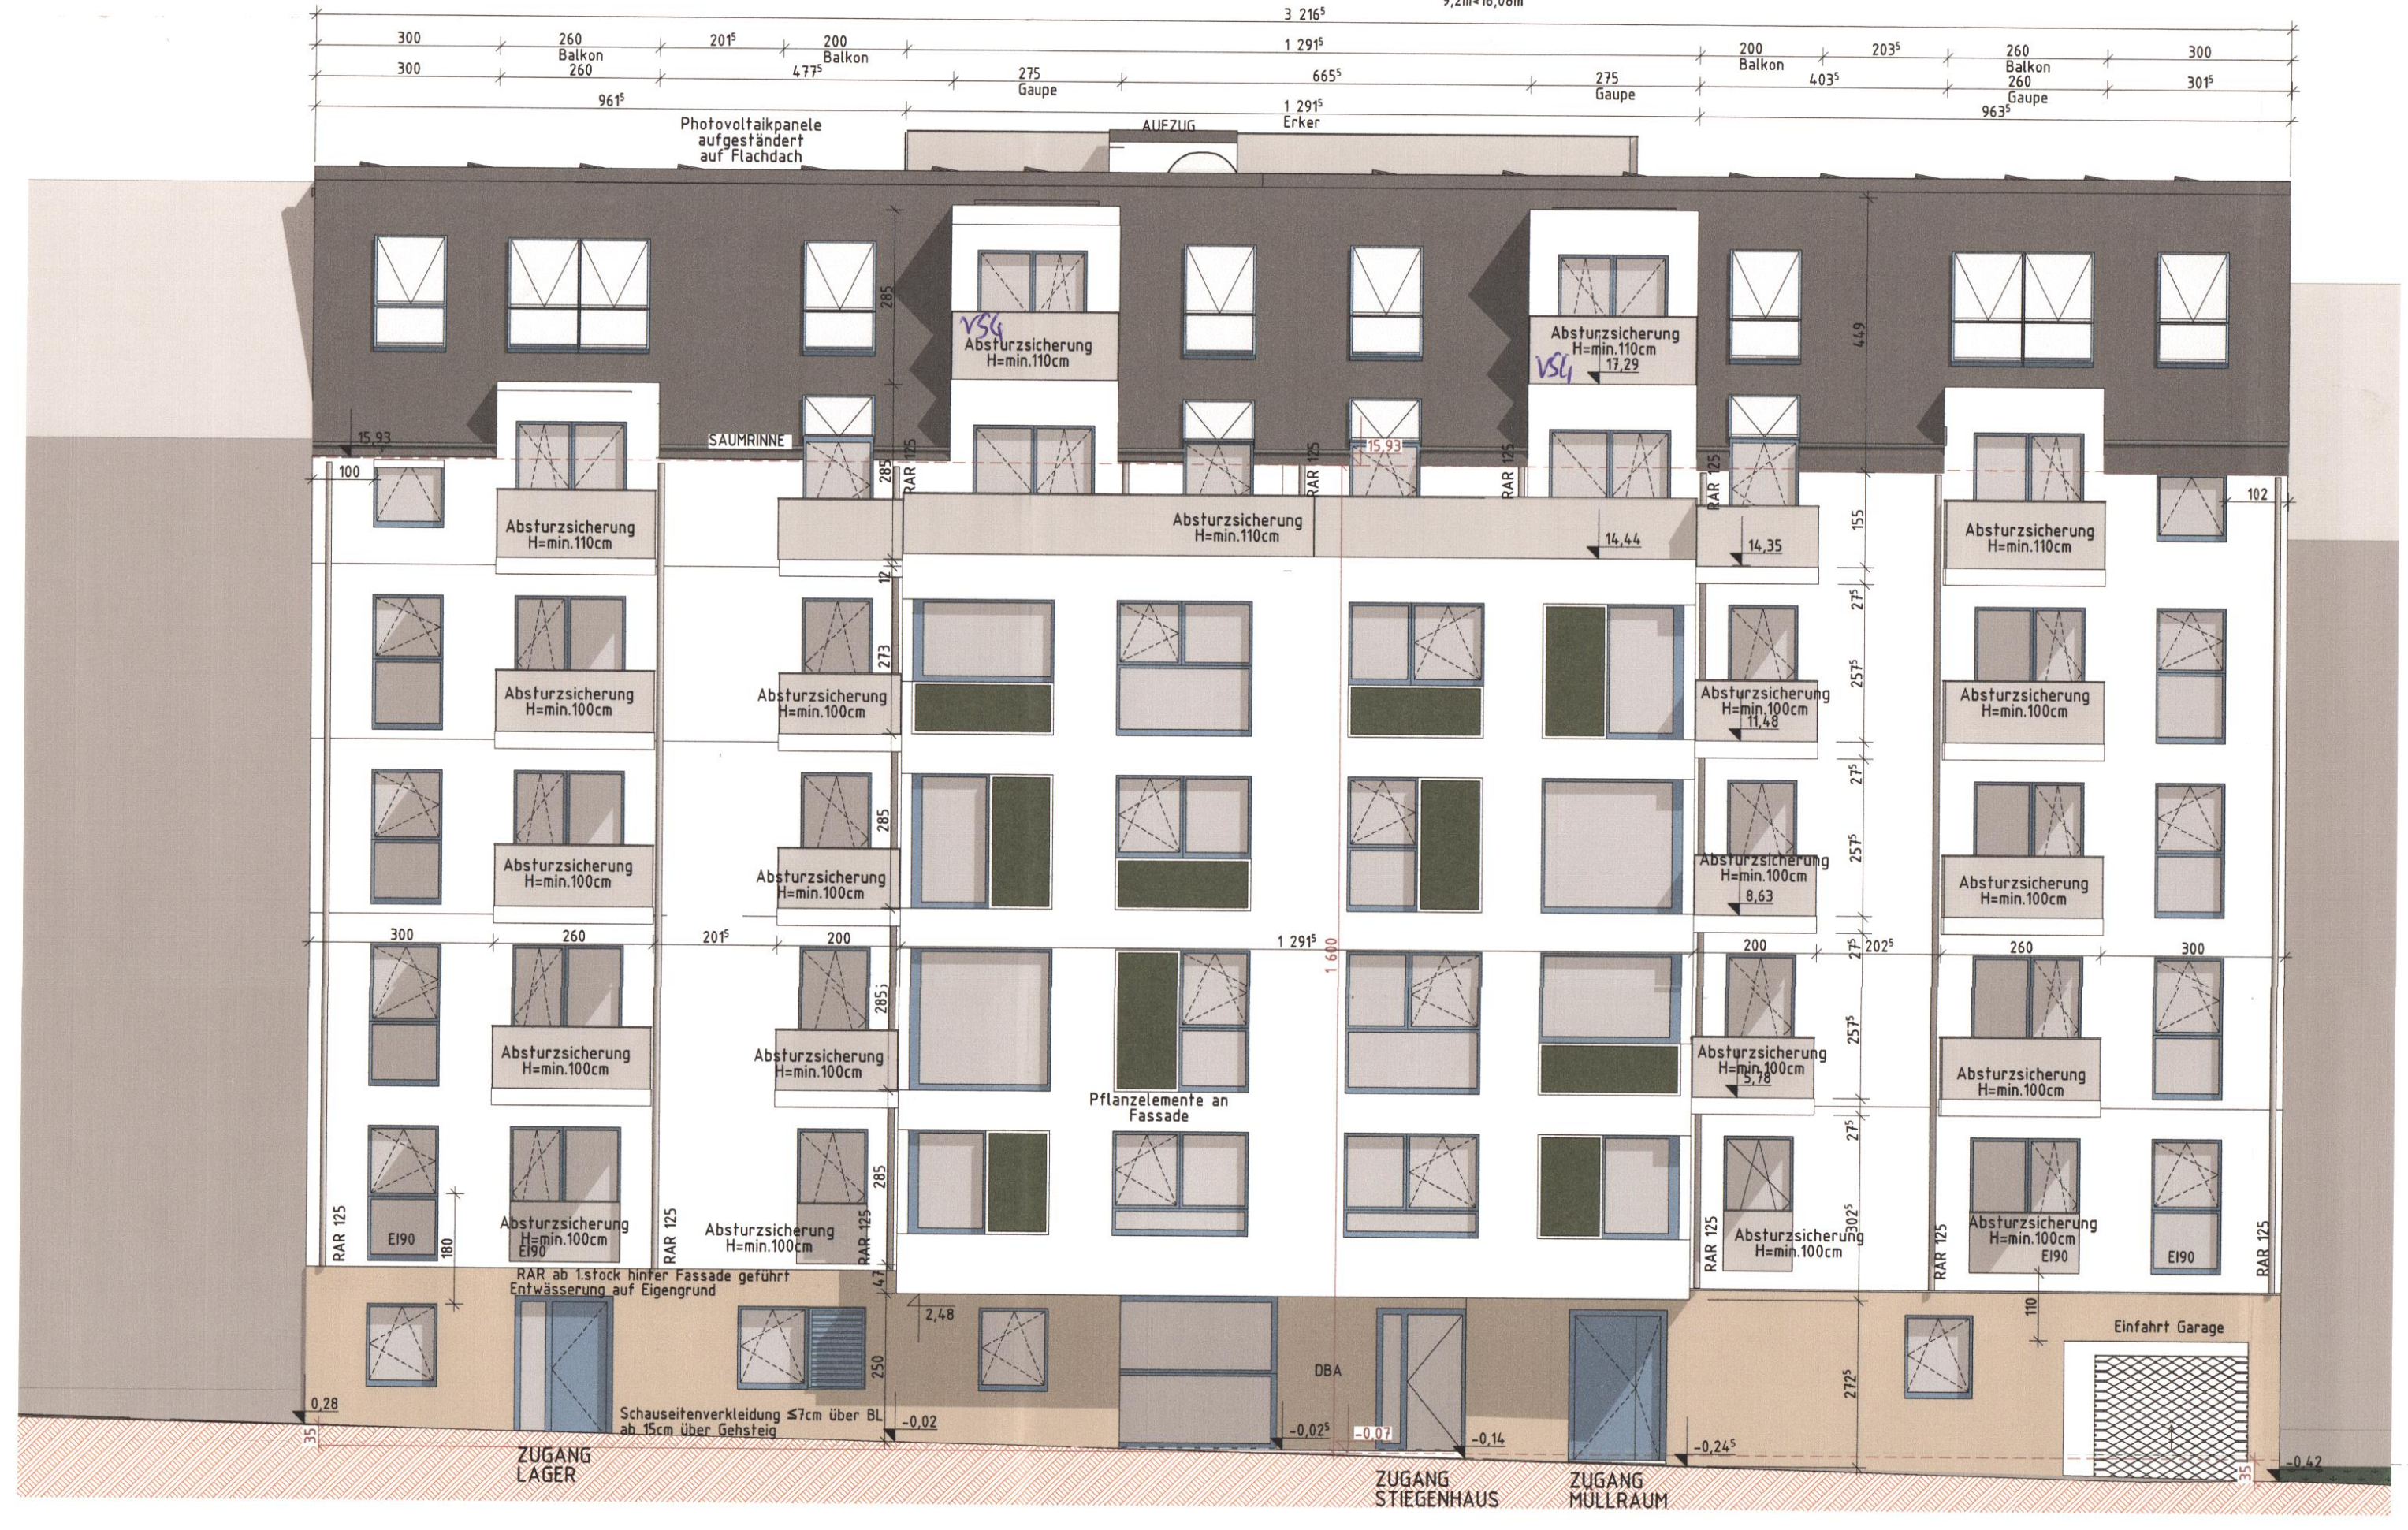

STRASSENTRAKT. WESTANSICHT HEIGERLEINSTRASSE 1:100

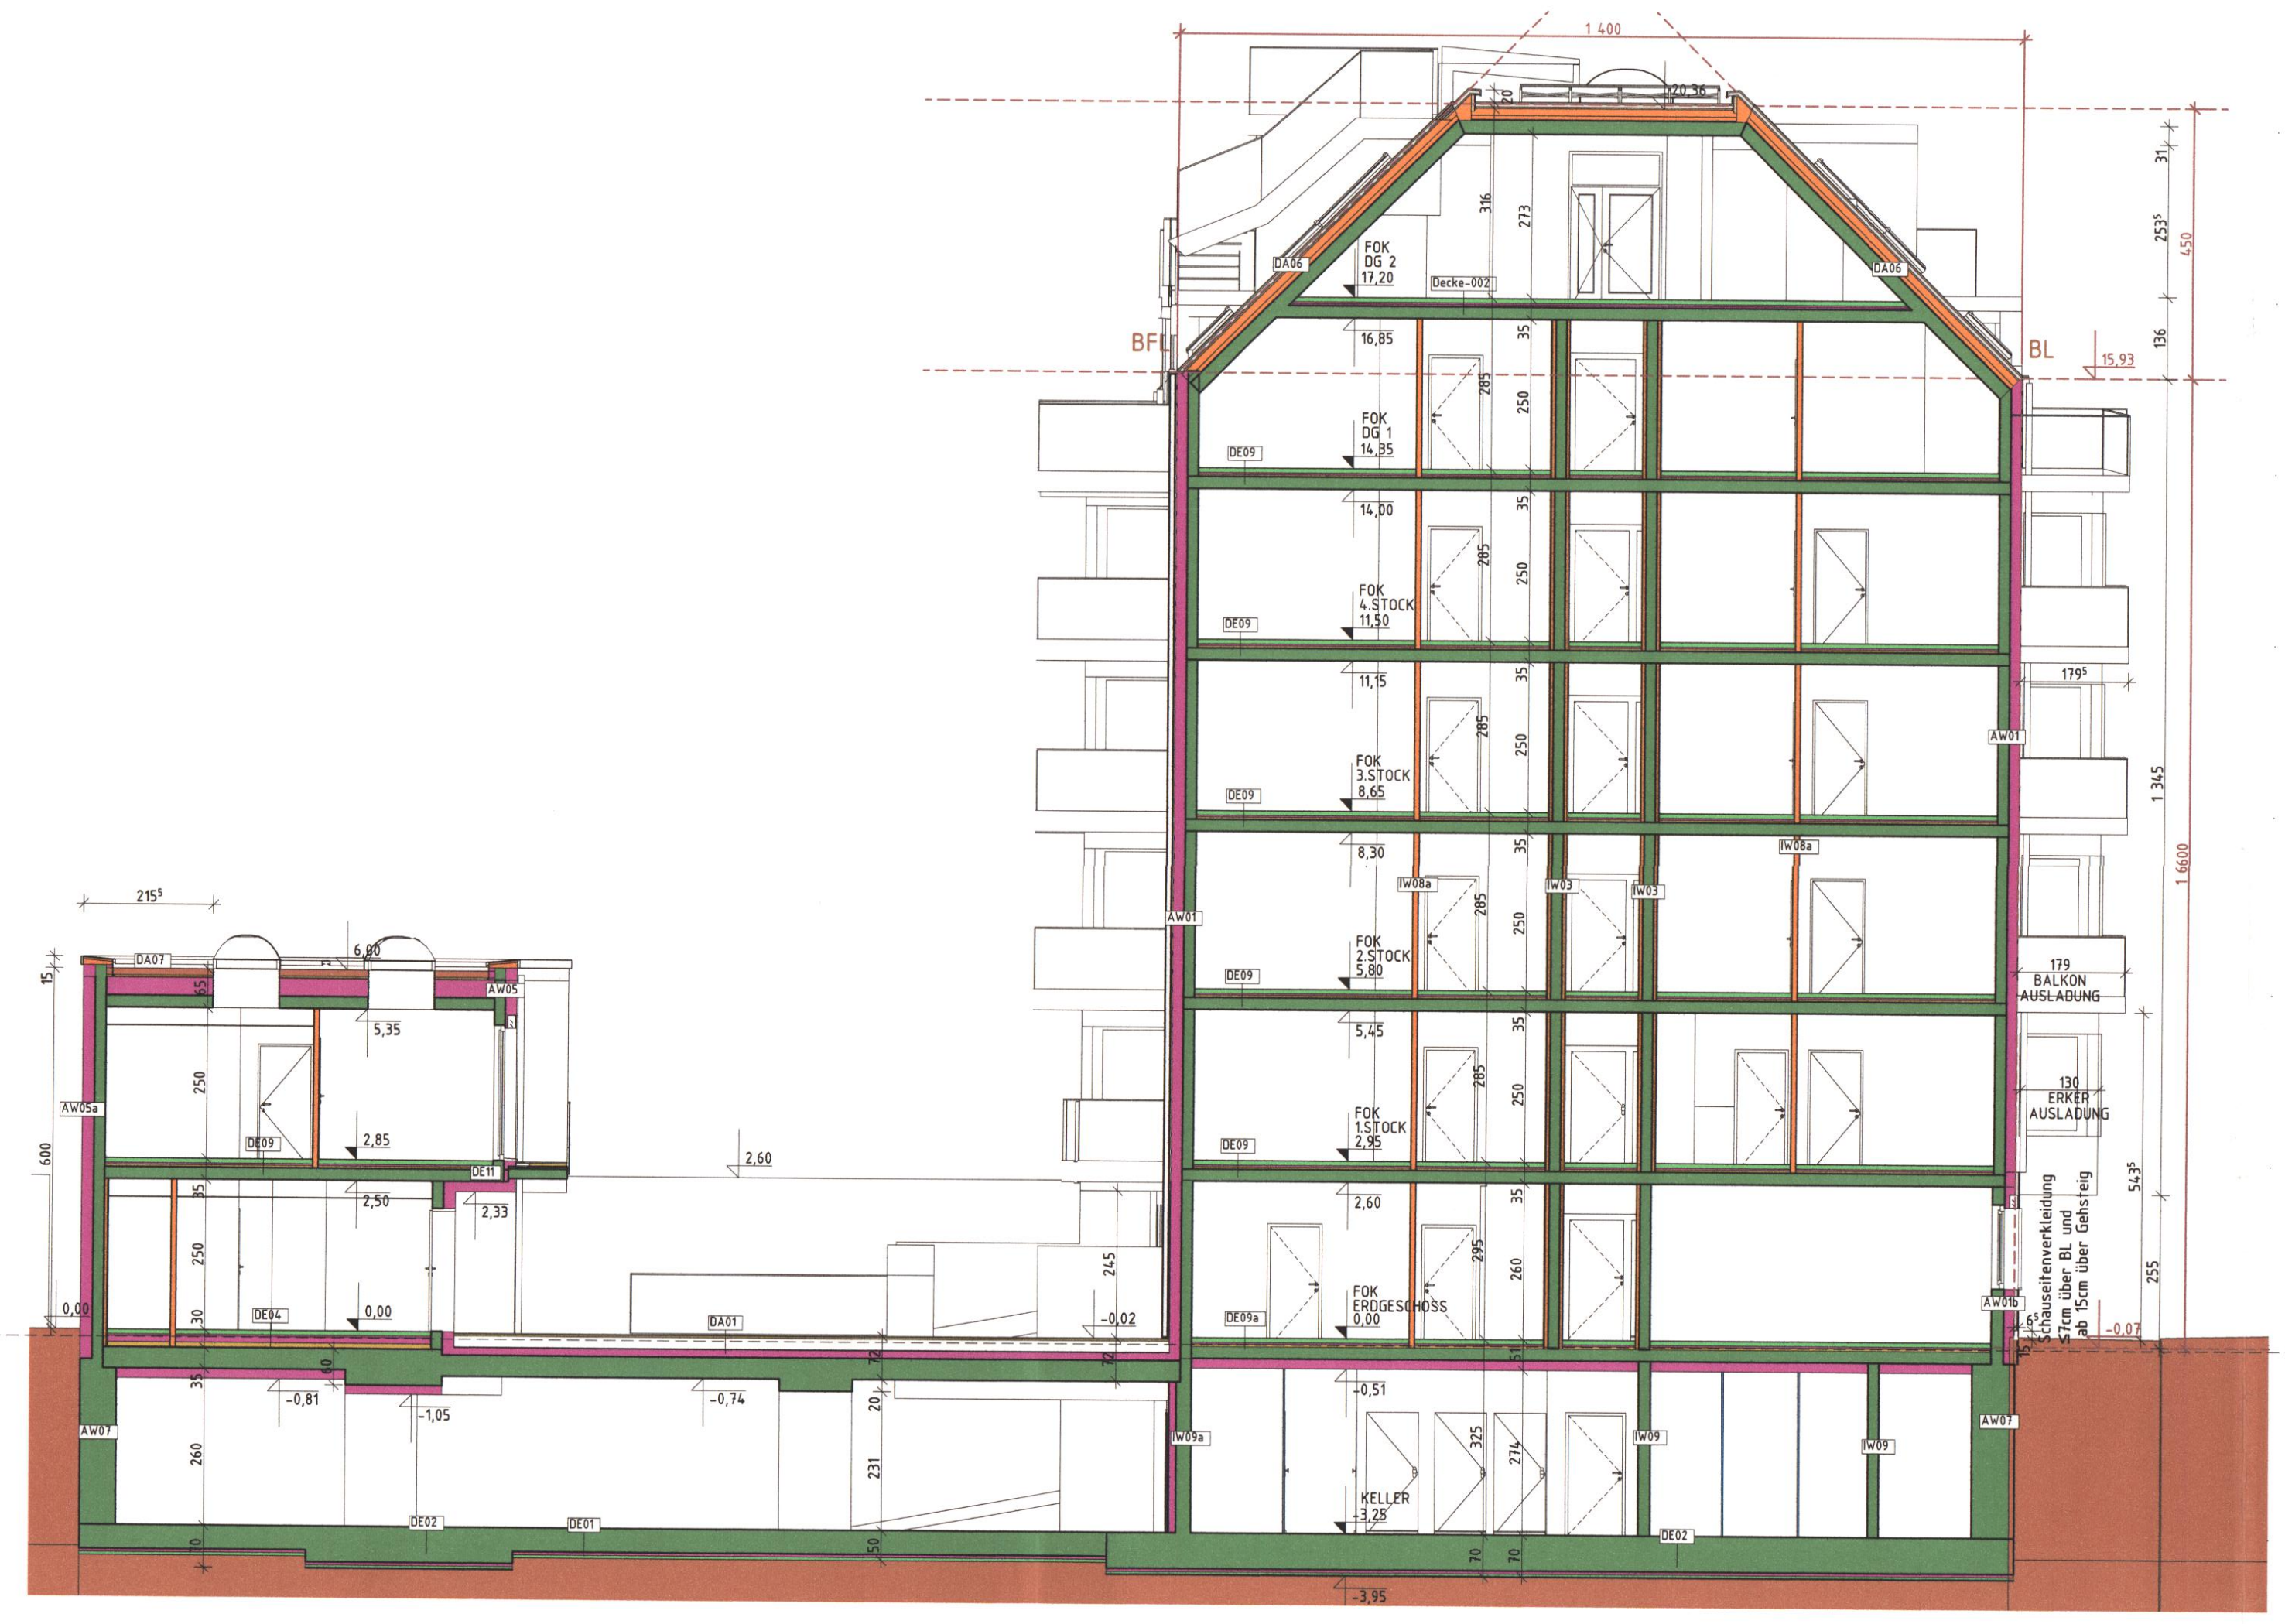

SCHNITT C-C 1:100

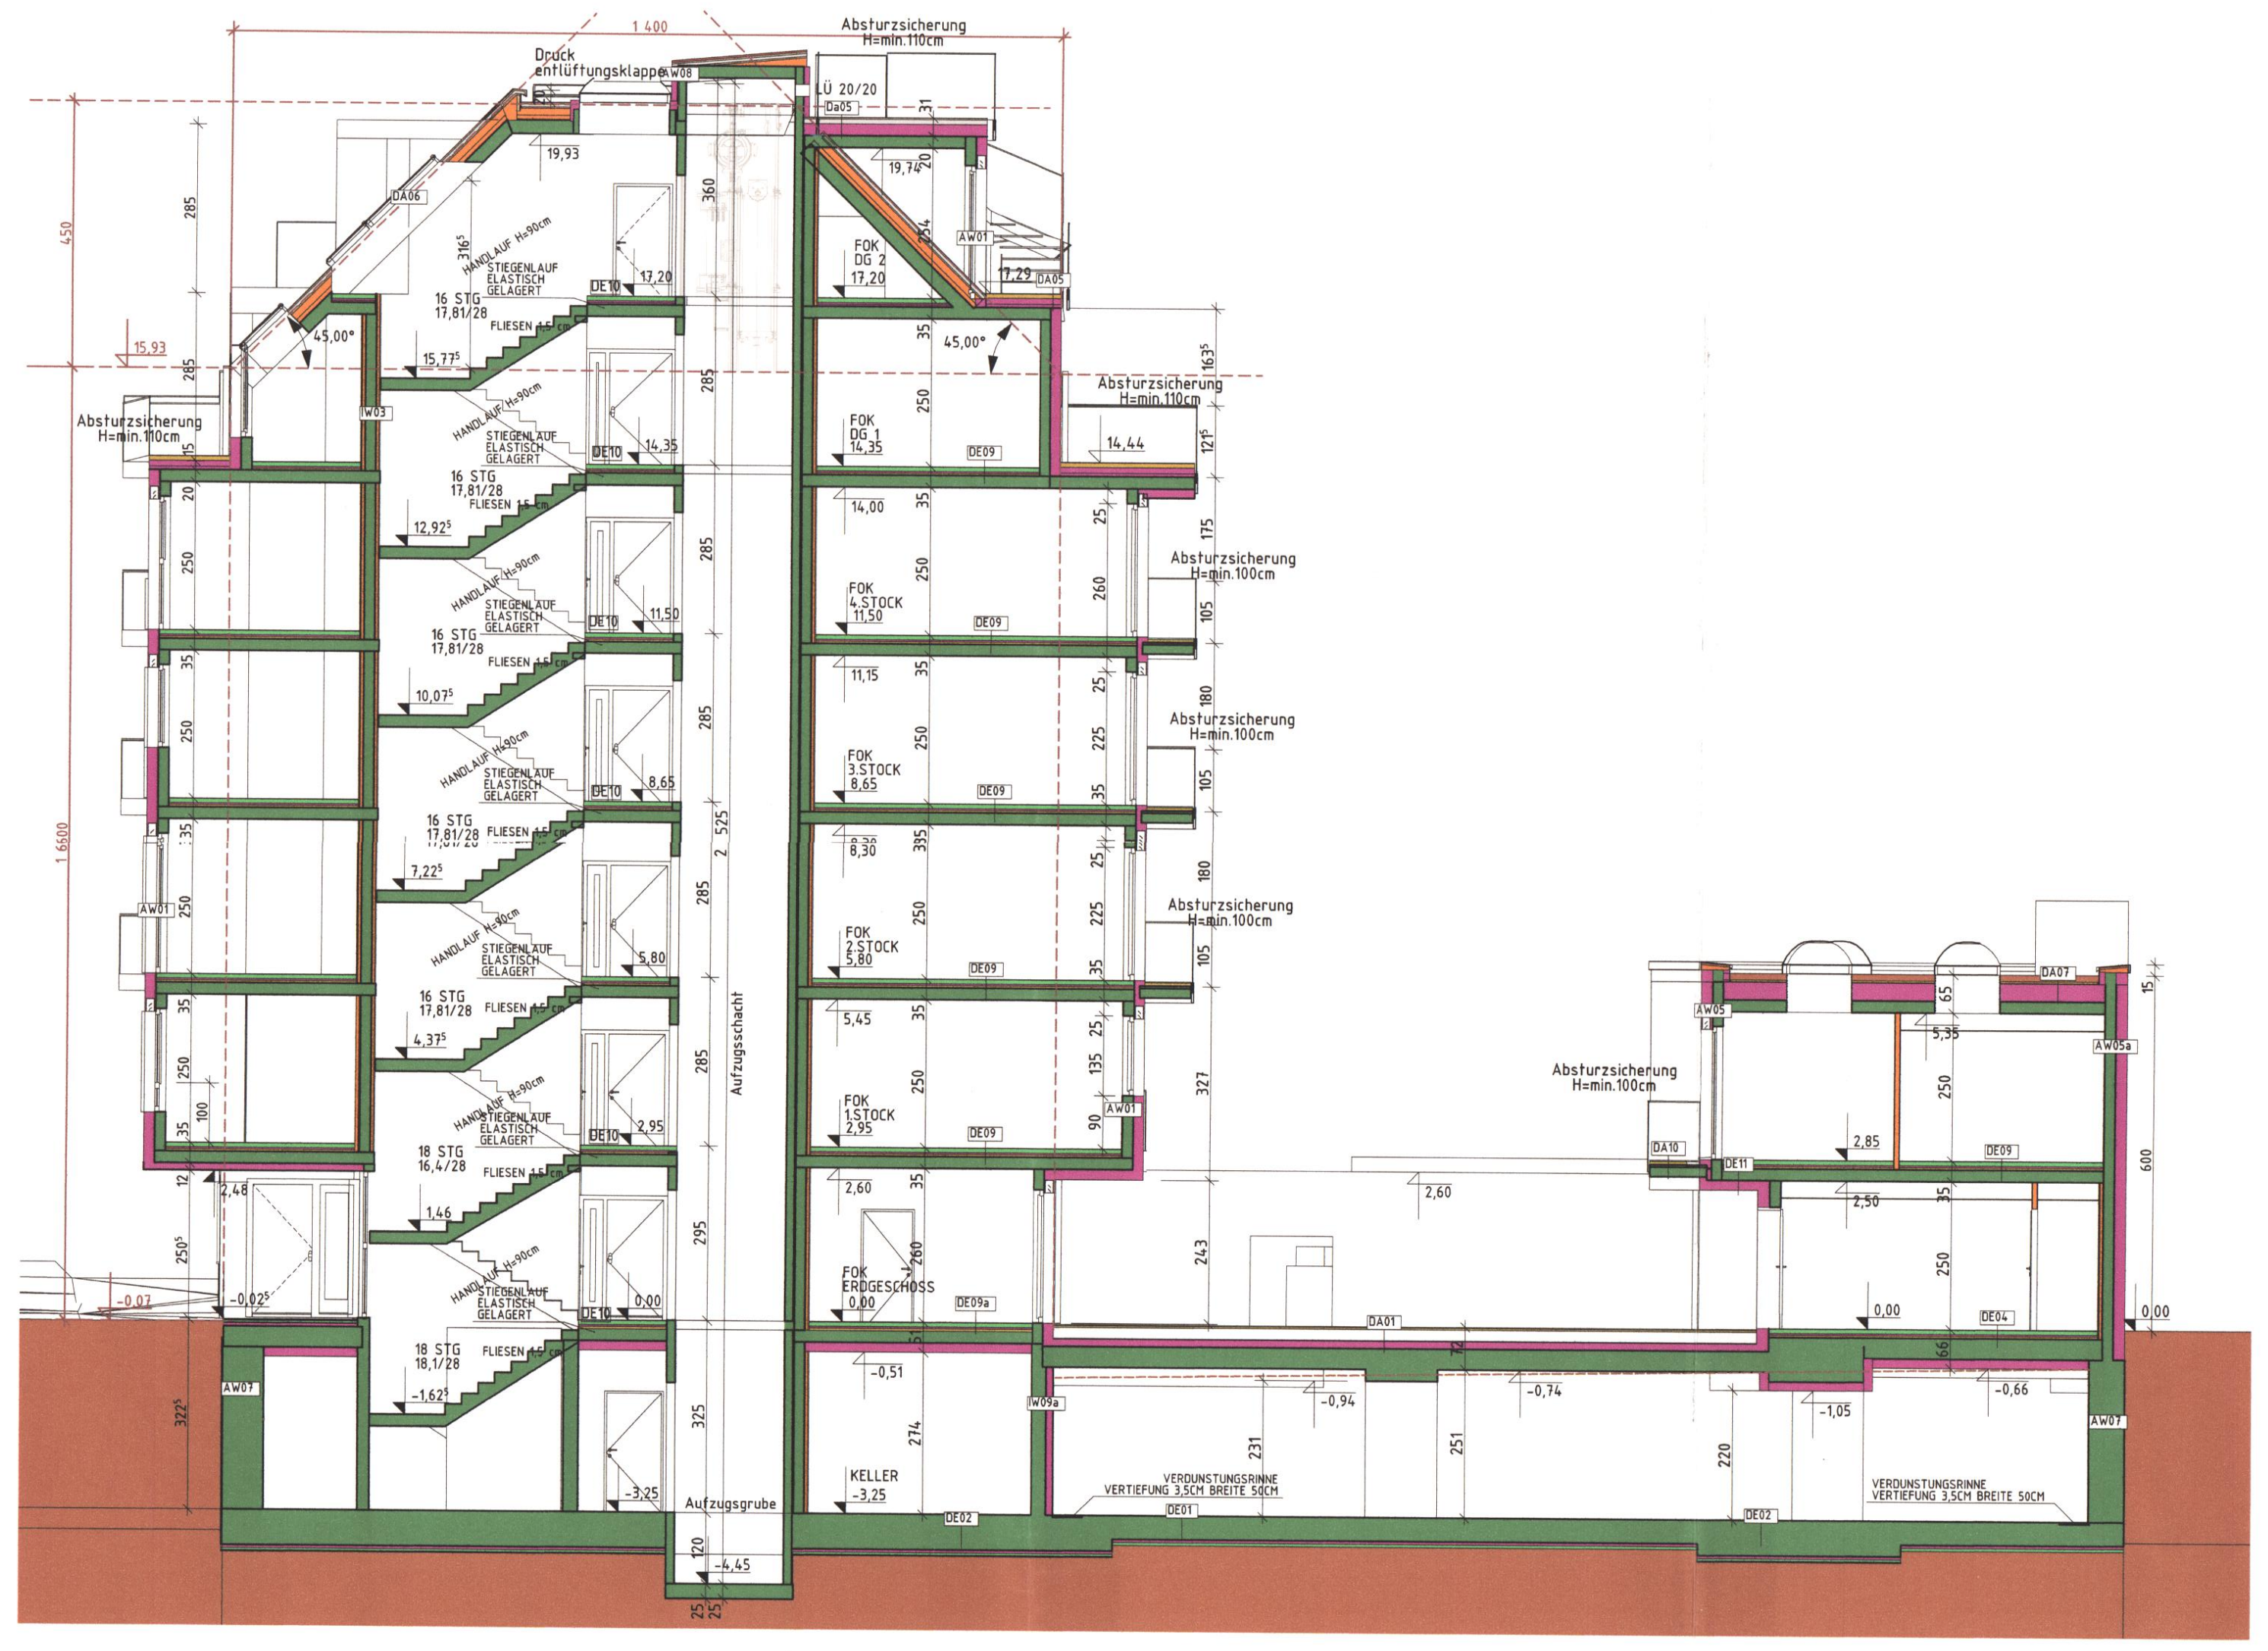

SCHNITT A-A

EINREICHPLAN

DOLLFUSS ARCHITEKT

PLANINHALT: SCHNITTE, ANSICHTEN

Parie A [✓ B] C D E F G H I J K
Nr. 1 [✓ 2] 3 4 5 6 7

BAUVORHABEN:

1160 Wien, Heigerleinstrasse 20 und 22
NEUBAU EINES MEHRFAMILIENWOHNHAUSES MIT 48 WOHNUNGEN UND EINEM REIHENHAUS (BEHERBERGUNGSSTÄTTE BESTEHEND AUS 5 ZIMMEREINHEITEN MIT INSGESAMT 10 BETTEN)
Heigerleinstraße 20-22
1160 Wien-Ottakring

GRUNDSTÜCKSNUMMER	801/39, 801/40
EINLAGEZAHL	2240
KATASTRALGEMEINDE	01405 Ottakring

GRUNDEIGENTÜMER/BAUWERBER

Simony Immobilien GmbH&Co Phi KG
Simonygasse 12
1180 Wien PER VOLLMACHT; SIEHE PLANVERFASSER

BEHÖRDE

BAUFÜHRER

Magistrat der Stadt Wien
Magistratsabteilung 37 - Baupolizei
Gebietsgruppe West, großvolumige Bauvorhaben
MA37 BAUPOLIZEI SICHER BAUEN
Zl.: MA37/1091355-2017-1
Hierauf bezieht sich der Bescheid
Für den Abteilungsleiter:
Dipl.-Ing. Weingartner
Wien, 04.01.2019

PLANVERFASSER

ARCHITEKT
DIPL.ING. GERHARD DOLLFUSS
STAATLICH BEFUGTER U. BEEIDETER ZIVILTECHNIKER
3240 MANK, BAHNHOFSTRASSE 4/4
0676/9490946 · office@dollfuss.eu

PLANINHALT	SCHNITTE, ANSICHTEN
MAßSTAB	1:100,1:200
PLANDATUM	15.12.2017
PLANNUMMER	A2017-04-101
PROJEKT	1160 Wien, Heigerleinstrasse 20 und 22
CAD-FILE	A2017-04 ERPL Heigerlein 20180705.pln

DRUCKDATUM 30.07.2018

DIESER PLAN IST GEISTIGES EIGENTUM DES PLANVERFASSERS UND DARF NUR MIT DESSEN ZUSTIMMUNG WEITERGEGEBEN UND VERVIELFÄLTIGT WERDEN ! DAS VORLIEGENDE PLANDOKUMENT DIENT ALS GRUNDLAGE FÜR DIE BEHÖRDLICHE GENEHMIGUNG lt. WRBO UND STELLT KEINEN AUSFÜHRUNGSPLAN DAR!