Bebauungsbestimmungen lt. PD 8082

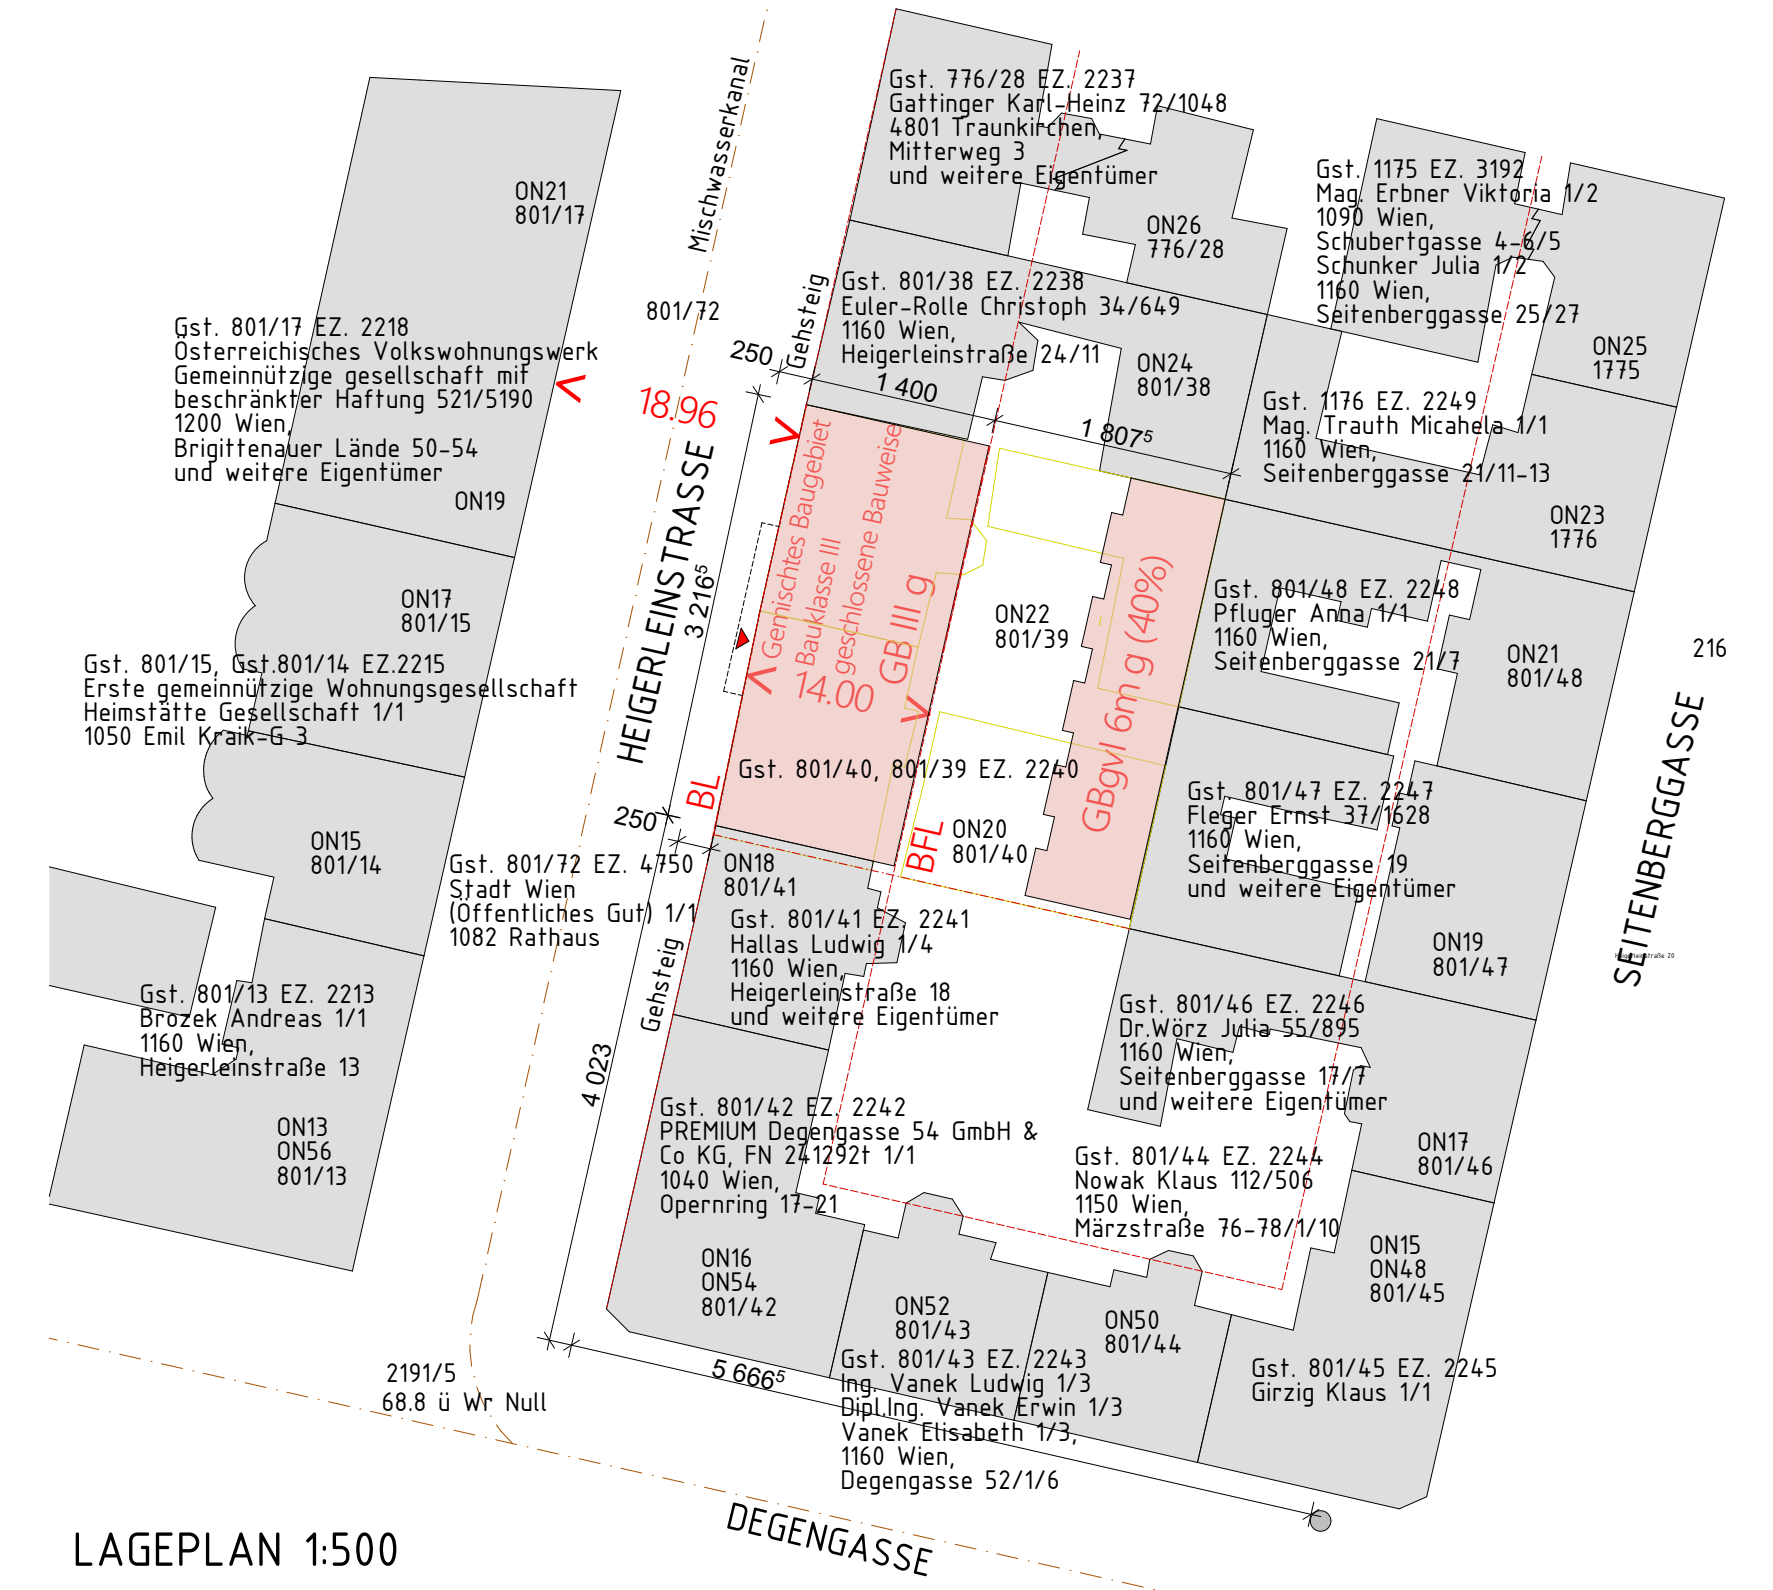

LAGEPLAN 1:500

ANRAINER:

Gst. 801/13 EZ. 2213
Brozek Andreas 1/1
1160 Wien,
Heigerleinstraße 13

Gst. 801/15, Gst.801/14 EZ.2215
Erste gemeinnützige Wohnungsgesellschaft
Heimstätte Gesellschaft 1/1
1050 Emil Kraik-G 3

Gst. 801/17 EZ. 2218
Österreichisches Volkswohnungswerk
Gemeinnützige Gesellschaft mit
beschränkter Haftung 521/5190
1200 Wien,
Brigittenauer Lände 50-54
und weitere Eigentümer siehe
Grundbuchsauszug (Beilage)

Gst. 801/72 EZ. 4750
Stadt Wien (Öffentliches Gut) 1/1
1082 Rathaus

Gst. 776/28 EZ. 2237
Gattinger Karl-Heinz 72/1048
4801 Traunkirchen,
Mitterweg 3
und weitere Eigentümer

Gst. 801/38 EZ. 2238
Euler-Rolle Christoph 34/649
1160 Wien,
Heigerleinstraße 24/11

Gst. 801/39, Gst. 801/40 EZ. 2238
Simony Immobilien GmbH & Co Phi KG (453696a)
1/1
1180 Wien,
Symonygasse 12

Gst. 801/40 EZ. 2240
Simony Immobilien GmbH & Co Phi KG (453696a)
1/1
1180 Wien,
Symonygasse 12

Gst. 801/41 EZ. 2241
Hallas Ludwig 1/4
1160 Wien,
Heigerleinstraße 18
Hallas Ludwig 1/4
1160 Wien,
Heigerleinstraße 18/5
Mag.Schlechta Andrea 1/4
1130 Wien,
Geylinggasse 27/18
Dr. Wernhart-Hallas Eisabeth
1130 Wien,
Hietzinger Hauptstraße 124/5

Gst. 801/42 EZ. 2242
PREMIUM Degengasse 54 GmbH &
Co KG, FN 241292t 1/1
1040 Wien,
Opernring 17-21

Gst. 801/43 EZ. 2243
Ing. Vanek Ludwig 1/3
Dipl.Ing. Vanek Erwin 1/3
Vanek Elisabeth 1/3,
1160 Wien,
Degengasse 52/1/6

Gst. 801/45 EZ. 2245
Girzig Klaus 1/1

Gst. 801/44 EZ. 2244
Nowak Klaus 112/506
1150 Wien,
Märzstraße 76-78/1/10

Gst. 801/46 EZ. 2246
Wörz Julia, Dr.
1160 Wien, Seitenberggasse 17/7

und weitere Eigentümer siehe
Grundbuchsauszug (Beilage)

Gst. 801/47 EZ. 2247
Fleger Ernst 37/1628
1160 Wien,
Seitenberggasse 19
und weitere Eigentümer siehe
Grundbuchsauszug (Beilage)

Gst. 801/48 EZ. 2248
Pfluger Anna 1/1
1160 Wien,
Seitenberggasse 21/7

Gst. 1176 EZ. 2249
Mag. Trauth Micahela 1/1
1160 Wien,
Seitenberggasse 21/11-13

Gst. 1175 EZ. 3192
Mag. Erbner Viktoria 1/2
1090 Wien,
Schubertgasse 4-6/5
Schunker Julia 1/2
1160 Wien,
Seitenberggasse 25/27

LEGENDE:

■	BESTAND	—	SCHMUTZWASSER	UZ	UNTERZUG
■	ABBRUCH	—	REGENWASSER	ÜZ	ÜBERZUG
■	NEUBAU	—	WASSER	AR	ABFALLROHR
		—	HEIZUNG	RR	REGENROHR
■	STAHLBETON	—	STROM	RSK	REGENSINKKASTEN
■	UNBEWEHRTER BETON	—	GAS	PH	PARAPETHÖHE
■	MAUERWERK	—	FERNWÄRME	STUK	STURZUNTERKANTE
■	HOLZ			DL	DURCHGANGSLICHTE
■	DÄMMUNG (HART)	DFF	DACHFLÄCHENFENSTER	OK	OBERKANTE
■	DÄMMUNG (WEICH)	LK	LICHTKUPPEL	UK	UNTERKANTE
▨	STAHL	VSG	VERBUND-SICHERHEITSGLAS	FOK	FUSSBODENOBERKANTE
■	GLAS	ESG	EINSCHEIBEN-SICHERHEITSGLAS	WD	WANDDURCHBRUCH
■	GIPSKARTON	BRE	BRANDRAUCHENTLÜFTUNG	DD	DECKENDURCHBRUCH

- LÜFTUNGEN DURCH FREMDE BRANDABSCHNITTE EI90 UND A2 UMMANTELT
- RESTRÄUME IM DACHGESCHOSS EI60 VON INNEN 2x GKF
- WOHNUNGSEINGANGSTÜREN $EI_2$30
- AUSWECHSLUNGEN REI90 UMMANTELT
- HEIZUNGSSYSTEM: WÄRMEPUMPE
- PHOTOVOLTAIKANLAGE IST AM FLACHDACH VORDERTRAKT AUFGESTÄNDERT
- ALLE AUSKRAGENDEN TEILE THERMISCH GETRENNT
- ALLE INNENLIEGENDEN BÄDER UND WC's LÜFTUNG ÜBER DACH
- FÜR JEDE WOHNUNG IST EIN EINLAGERUNGSRAUM VORHANDEN
- IN JEDER WOHNUNG IST EINE GEEIGNETE AUFSTELLMÖGLICHKEIT UND EIN ANSCHLUSS FÜR EINE WASCHMASCHINE UND EINE MASCHINELLE TROCKENEINRICHTUNG VORGESEHEN.
- NIEDERSCHLAGSWÄSSER UND FÄKALWÄSSER WERDEN IN DEN ÖFFENTLICHEN KANAL GELEITET
- STIEGEN UND GÄNGE KUNSTSTEINBELAG, BELAG MÜLLRAUM UND GARAGE MIND. Bfl
- GEMÄSS OIB RICHTLINIE 2, ABSATZ 3, PUNKT 11 - UNVERNETZTE RAUCHWARNMELDER IN ALLEN AUFENTHALTSRÄUMEN (AUSGEN. KÜCHEN, BEI WOHNKÜ. NICHT IM KOCHBEREICH) SOWIE BEI GÄNGEN ÜBER DIE FLUCHTWEGE VON AUFENTHALTSR. FÜHREN
- SCHADENSFOLGEKLASSE CC2 nach ÖNORM EN 1090-2 Tab. B3
- NÄCHSTE HYDRANT BIS GRUNDGRENZE: ca.115m<150m
- ALLE INNENLIEGENDE RÄUME SIND MECHANISCH ENTLÜFTET
- SCHÄCHTE WERDEN GEMÄSS WIENER INSTALLATIONSRICHTLINIE SCHACHTTYP A AUSGEFÜHRT
- AUFZUGSSCHÄCHTE SIND MIT MIND 2,5% DES SCHACHTQUERSCHNITTS ENTLÜFTET.
- FLUCHTWEGS UND ORIENTIERUNGSBELEUCHTUNG GEMÄß DEN BESTIMMUNGEN DER TRVB 102E
- DRUCKBELÜFTUNGSANLAGE GEMÄSS DEN BESTIMMUNGEN DER TRVB 112S (AUFENTHALTSKONZEPT)

± 0.00 ENTSPRICHT 70,12M ÜBER WIENER NULL
± 0.00 ENTSPRICHT 70,20M ÜBER WIENER NULL

DOLL
FUSS
ARCHITEKT

AUSWECHSLUNGSPLAN

PLANINHALT:
GRUNDRISSE, LAGEPLAN

Parie	A	B	C	D	E	F	G	H	I	J	K
Nr.	1	2	3	4	5	6	7				

BAUVORHABEN:

1160 Wien, Heigerleinstrasse 20 und 22

ABBRUCH BESTANDSGEBÄUDE UND NEUBAU EINES MEHRFAMILIENWOHNHAUSES MIT 44 WOHNUNGEN UND 5 REIHENHÄUSERN (BEHERBERGUNGSBETRIEB MIT 5 BETRIEBSEINHEITEN UND 10 BETTEN)
Heigerleinstraße 20-22
1160 Wien-Ottakring

GRUNDSTÜCKSNUMMER	801/39, 801/40
EINLAGEZAHL	2240
KATASTRALGEMEINDE	01405 Ottakring

GRUNDEIGENTÜMER/BAUWERBER

~~Simony Immobilien GmbH&Co Phi KG~~
~~Simonygasse 12~~
~~1180 Wien~~

HEIGE20 Projekt GmbH & Co KG
Sterngasse 11/4B
1010 Wien

BEHÖRDE

BAUFÜHRER
Auböck Bau GmbH
Drosselstraße 36
A-4470 Enns

PLANVERFASSER

ARCHITEKT
DIPL.ING. GERHARD DOLLFUSS
STAATLICH BEFUGTER U. BEEIDETER ZIVILTECHNIKER
3240 MANK, BAHNHOFSTRASSE 4/4
0676/9490946 · office@dollfuss.eu

PLANINHALT	GRUNDRISSE, LAGEPLAN
MAßSTAB	1:100,1:500
PLANDATUM	02.10.2020 DRUCKDATUM 15.12.2020
PLANNUMMER	A2017-04-201
PROJEKT	1160 Wien, Heigerleinstrasse 20 und 22
CAD-FILE	A2017-04_Heigerlein_ASW_20200102.pln

DIESER PLAN IST GEISTIGES EIGENTUM DES PLANVERFASSERS UND DARF NUR MIT DESSEN ZUSTIMMUNG WEITERGEGEBEN UND VERVIELFÄLTIGT WERDEN !
DAS VORLIEGENDE PLANDOKUMENT DIENT ALS GRUNDLAGE FÜR DIE BEHÖRDLICHE GENEHMIGUNG lt. WRBO UND STELLT KEINEN AUSFÜHRUNGSPLAN DAR!

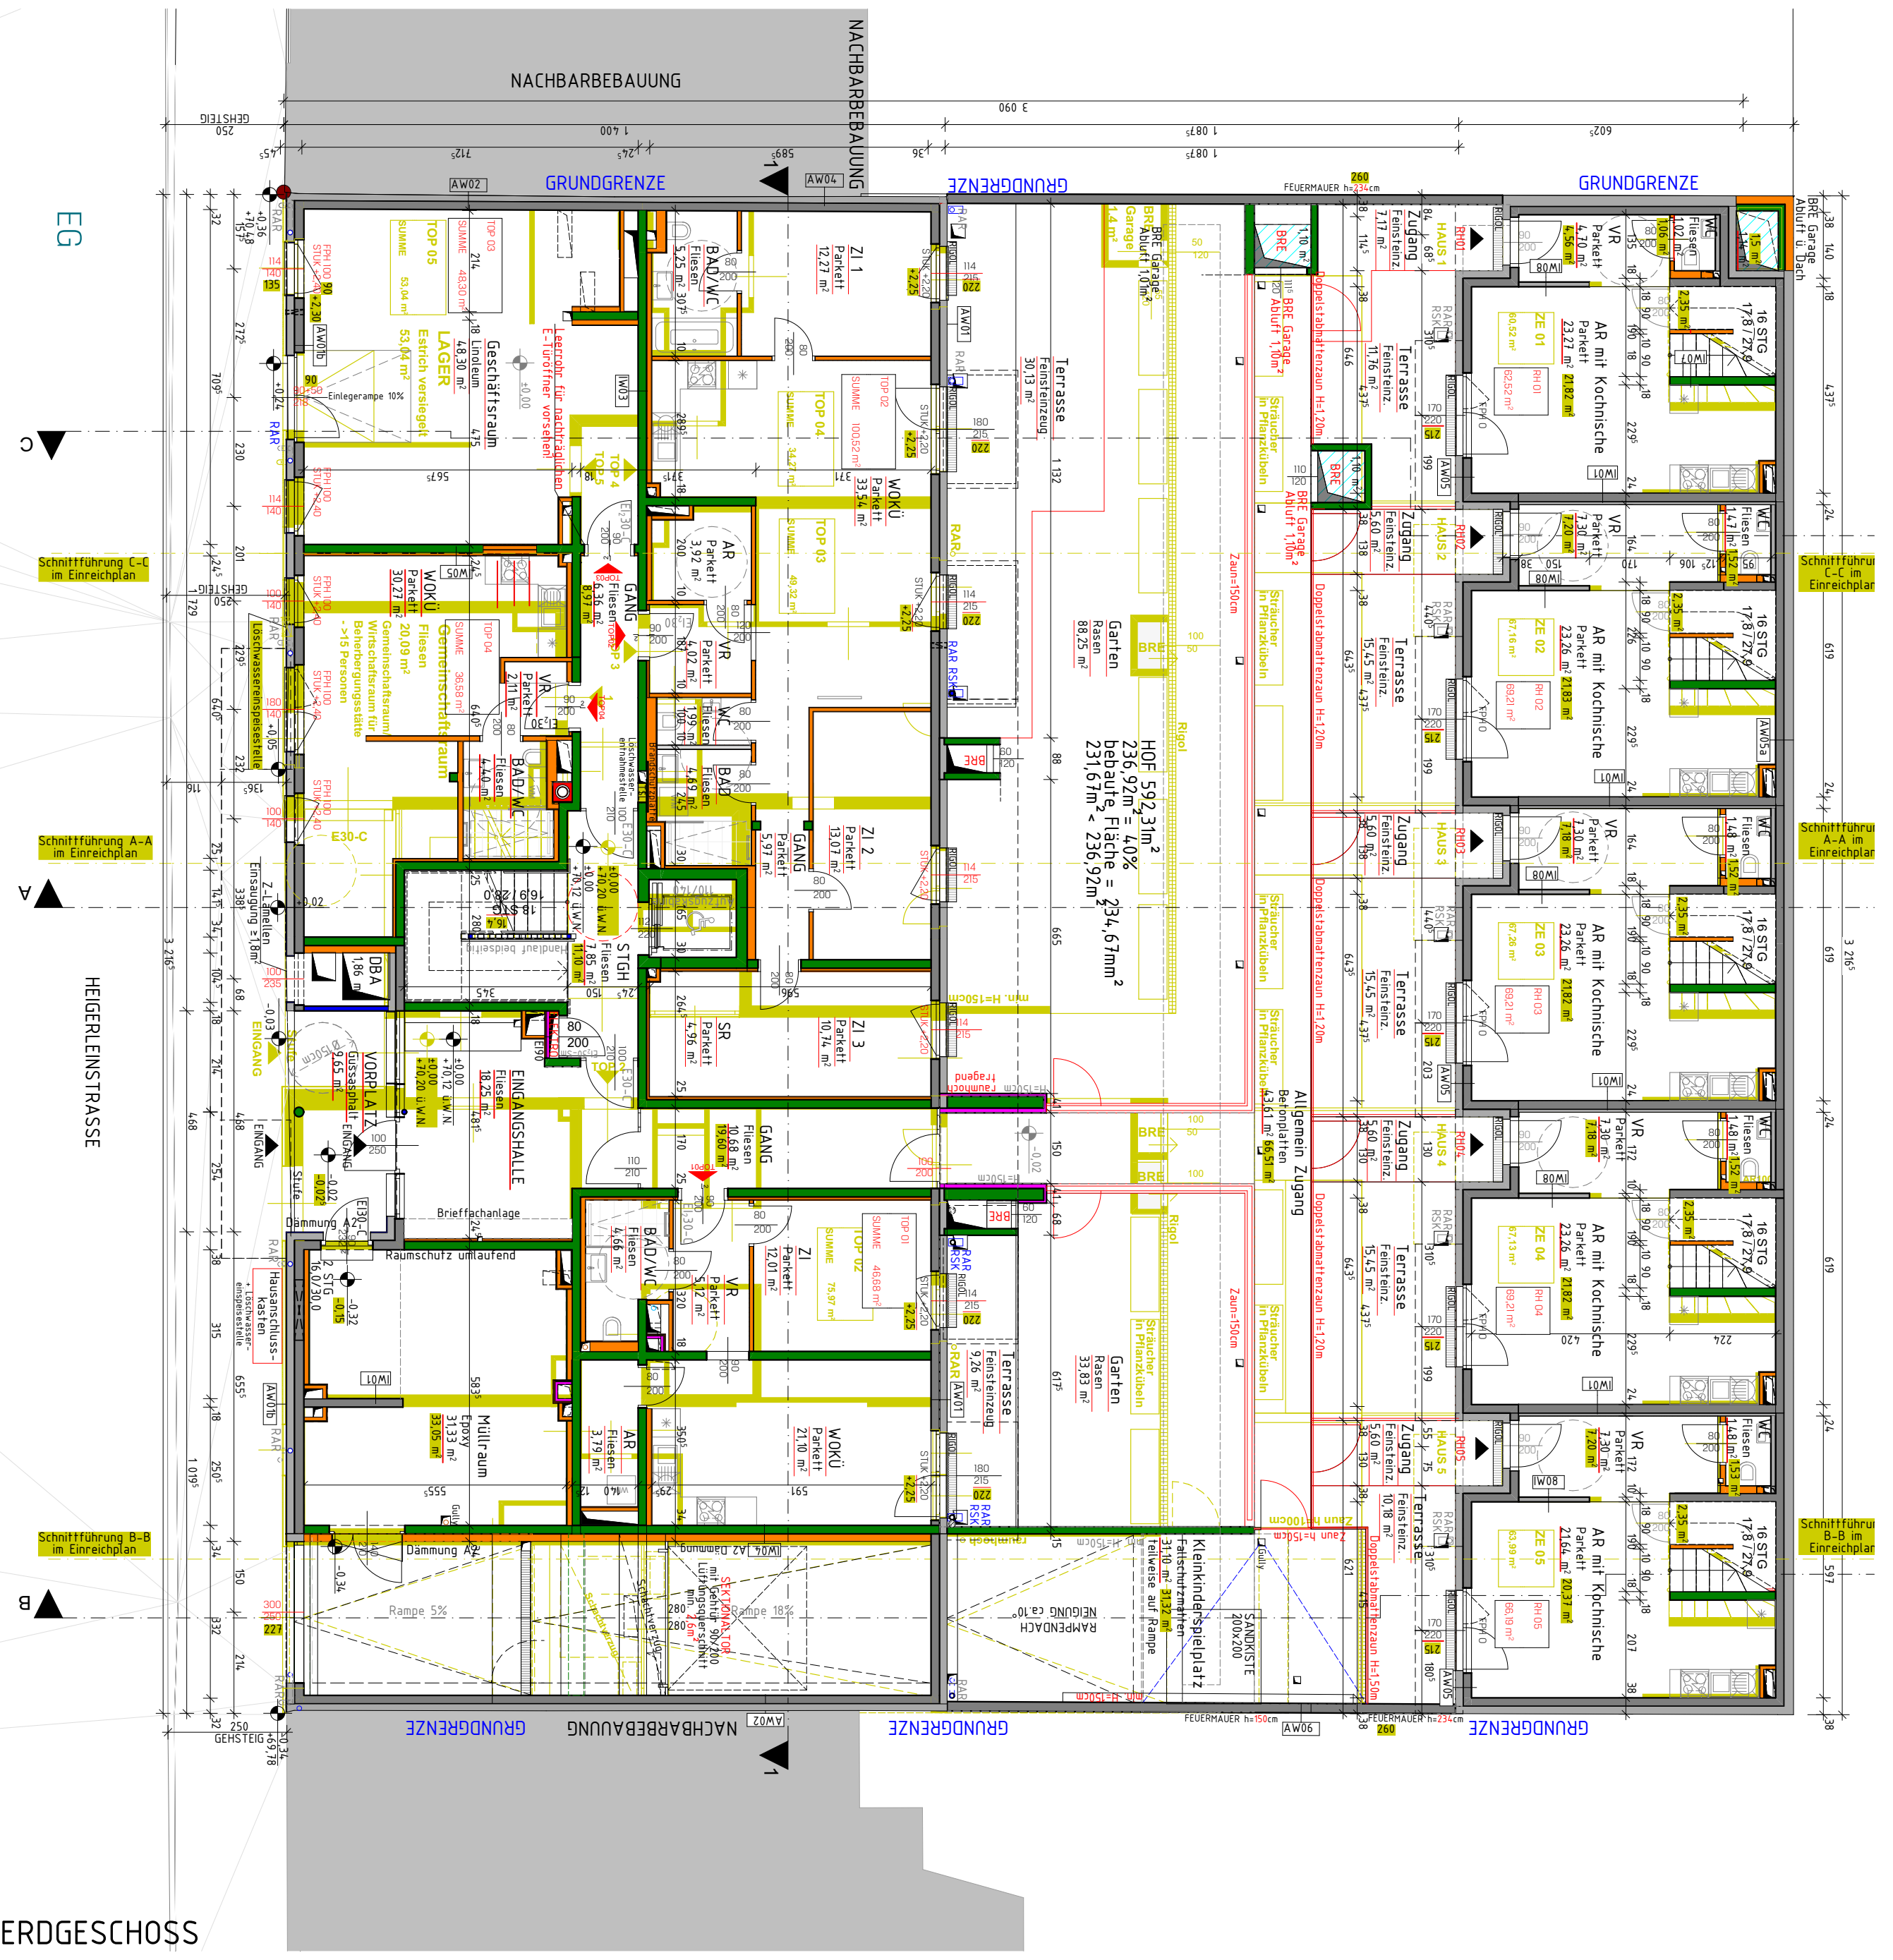

ERDGESCHOSS

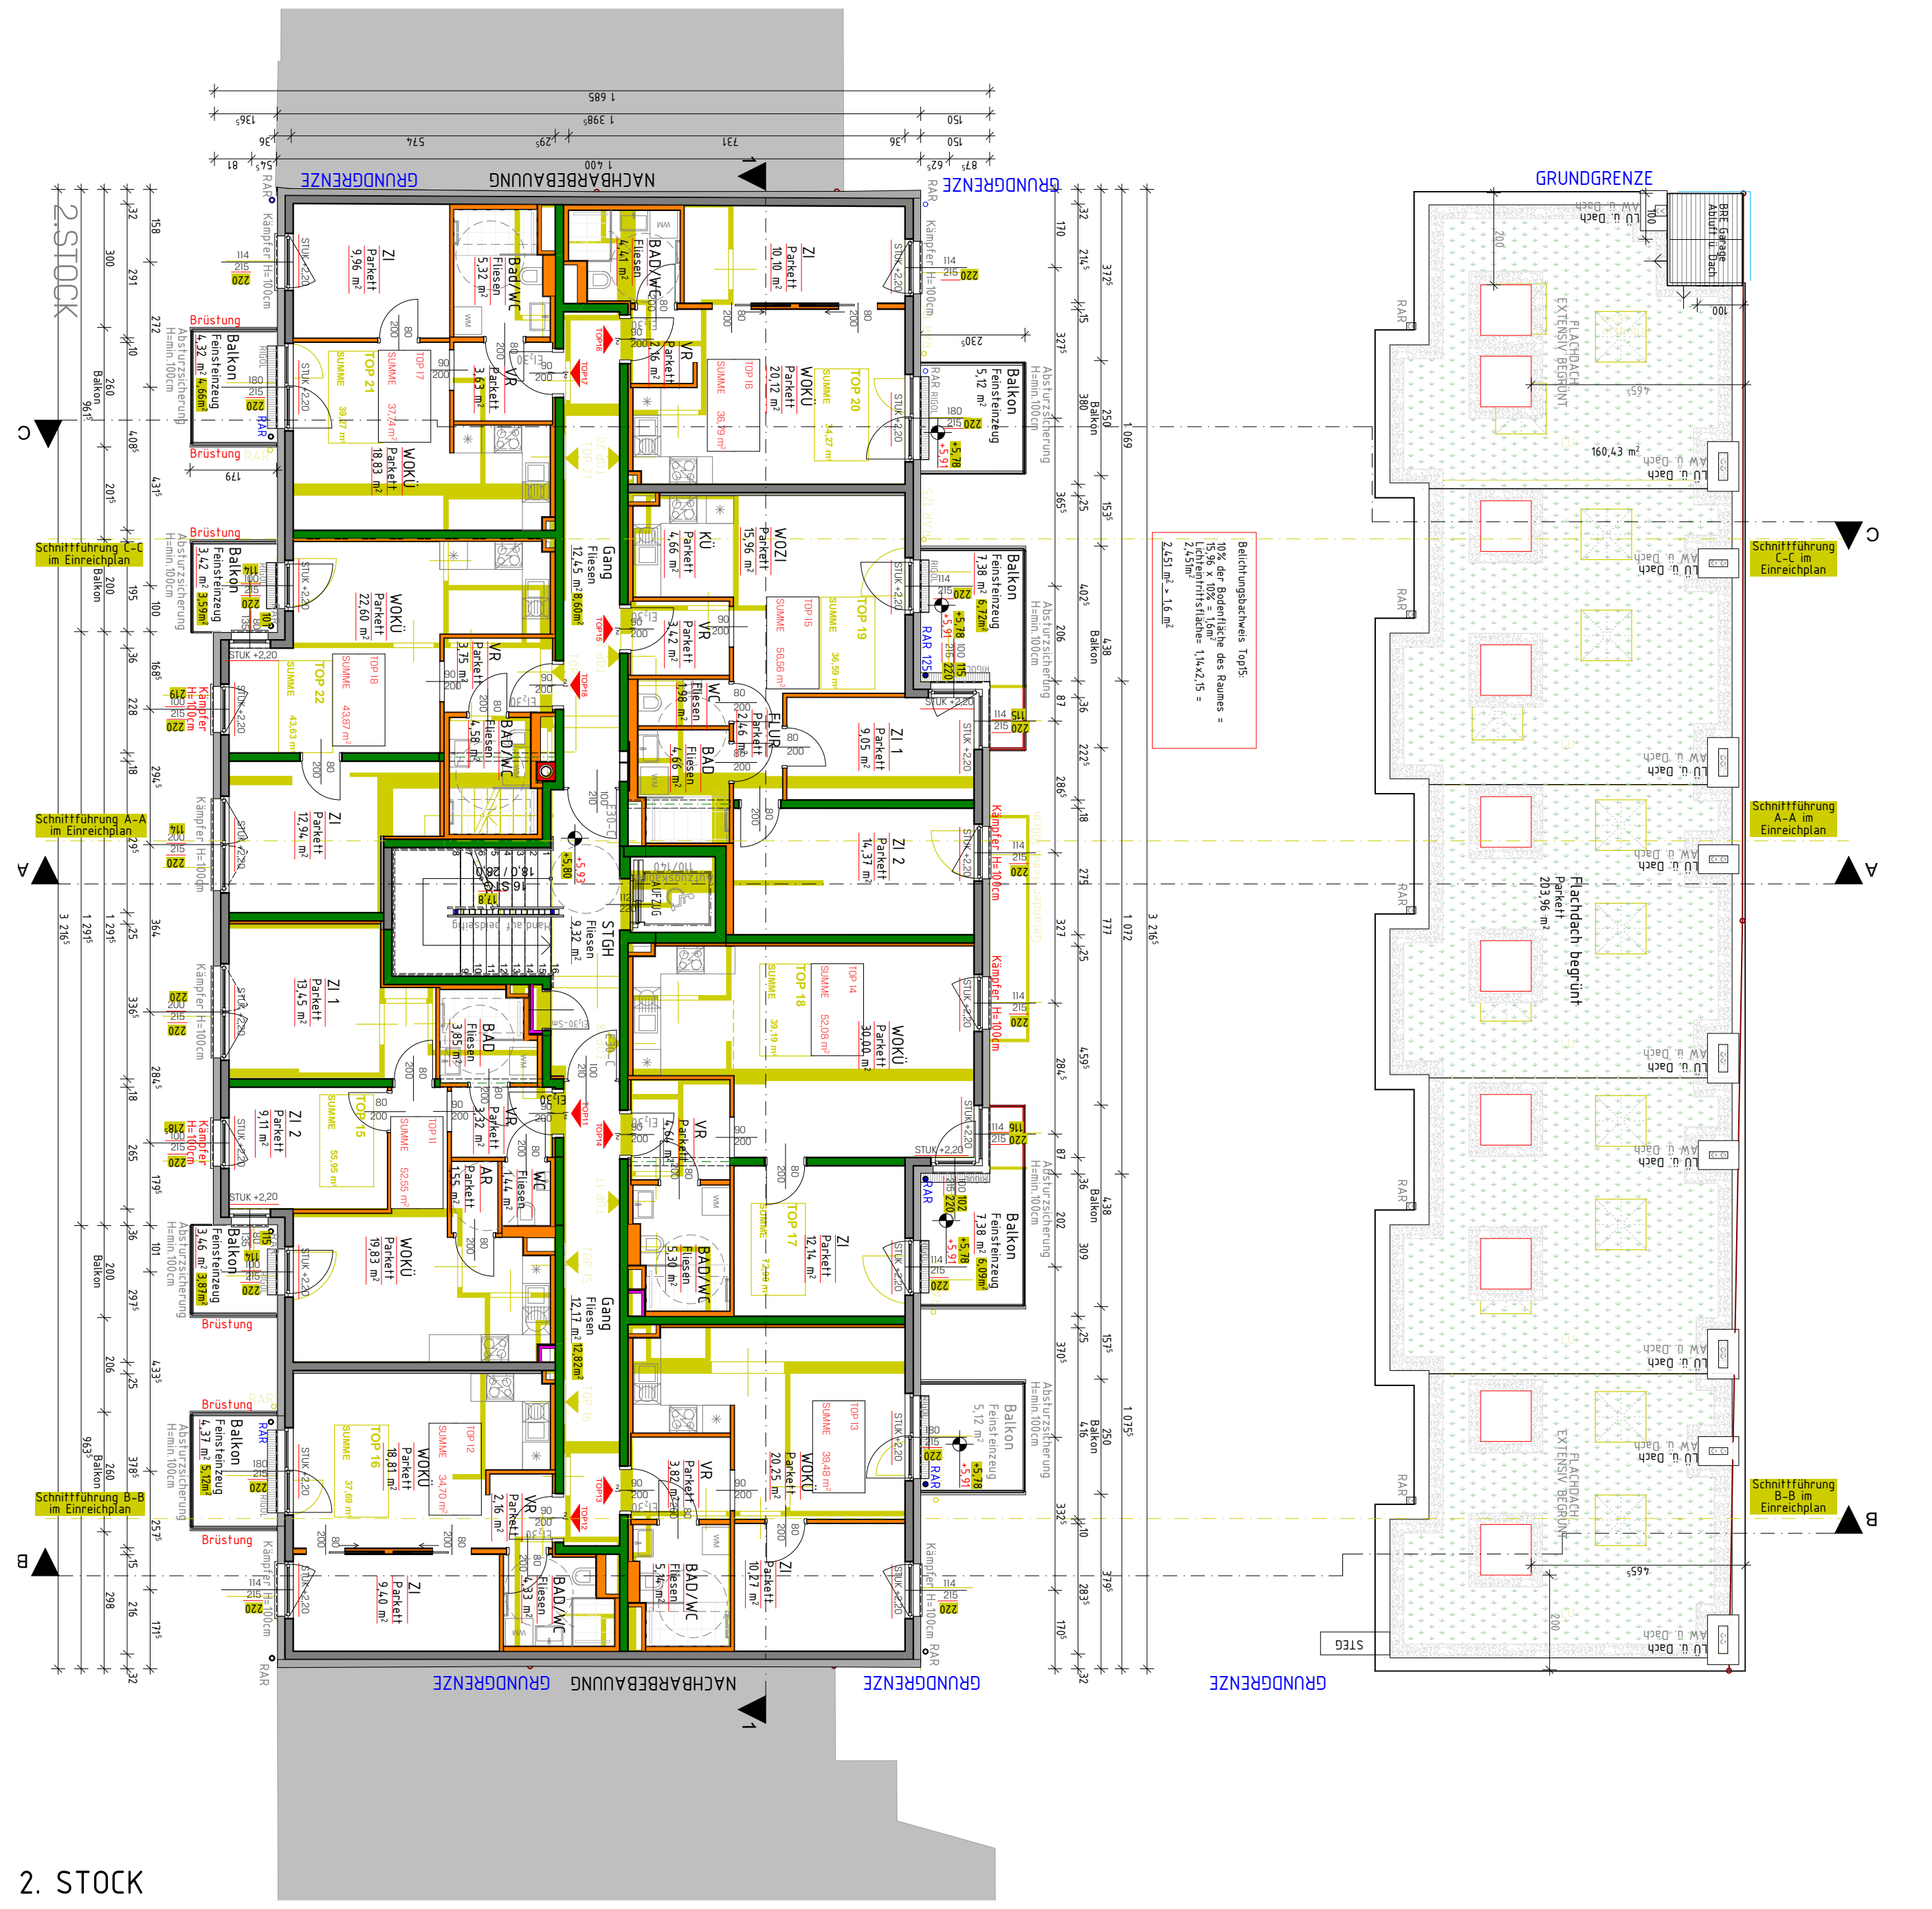

2. STOCK

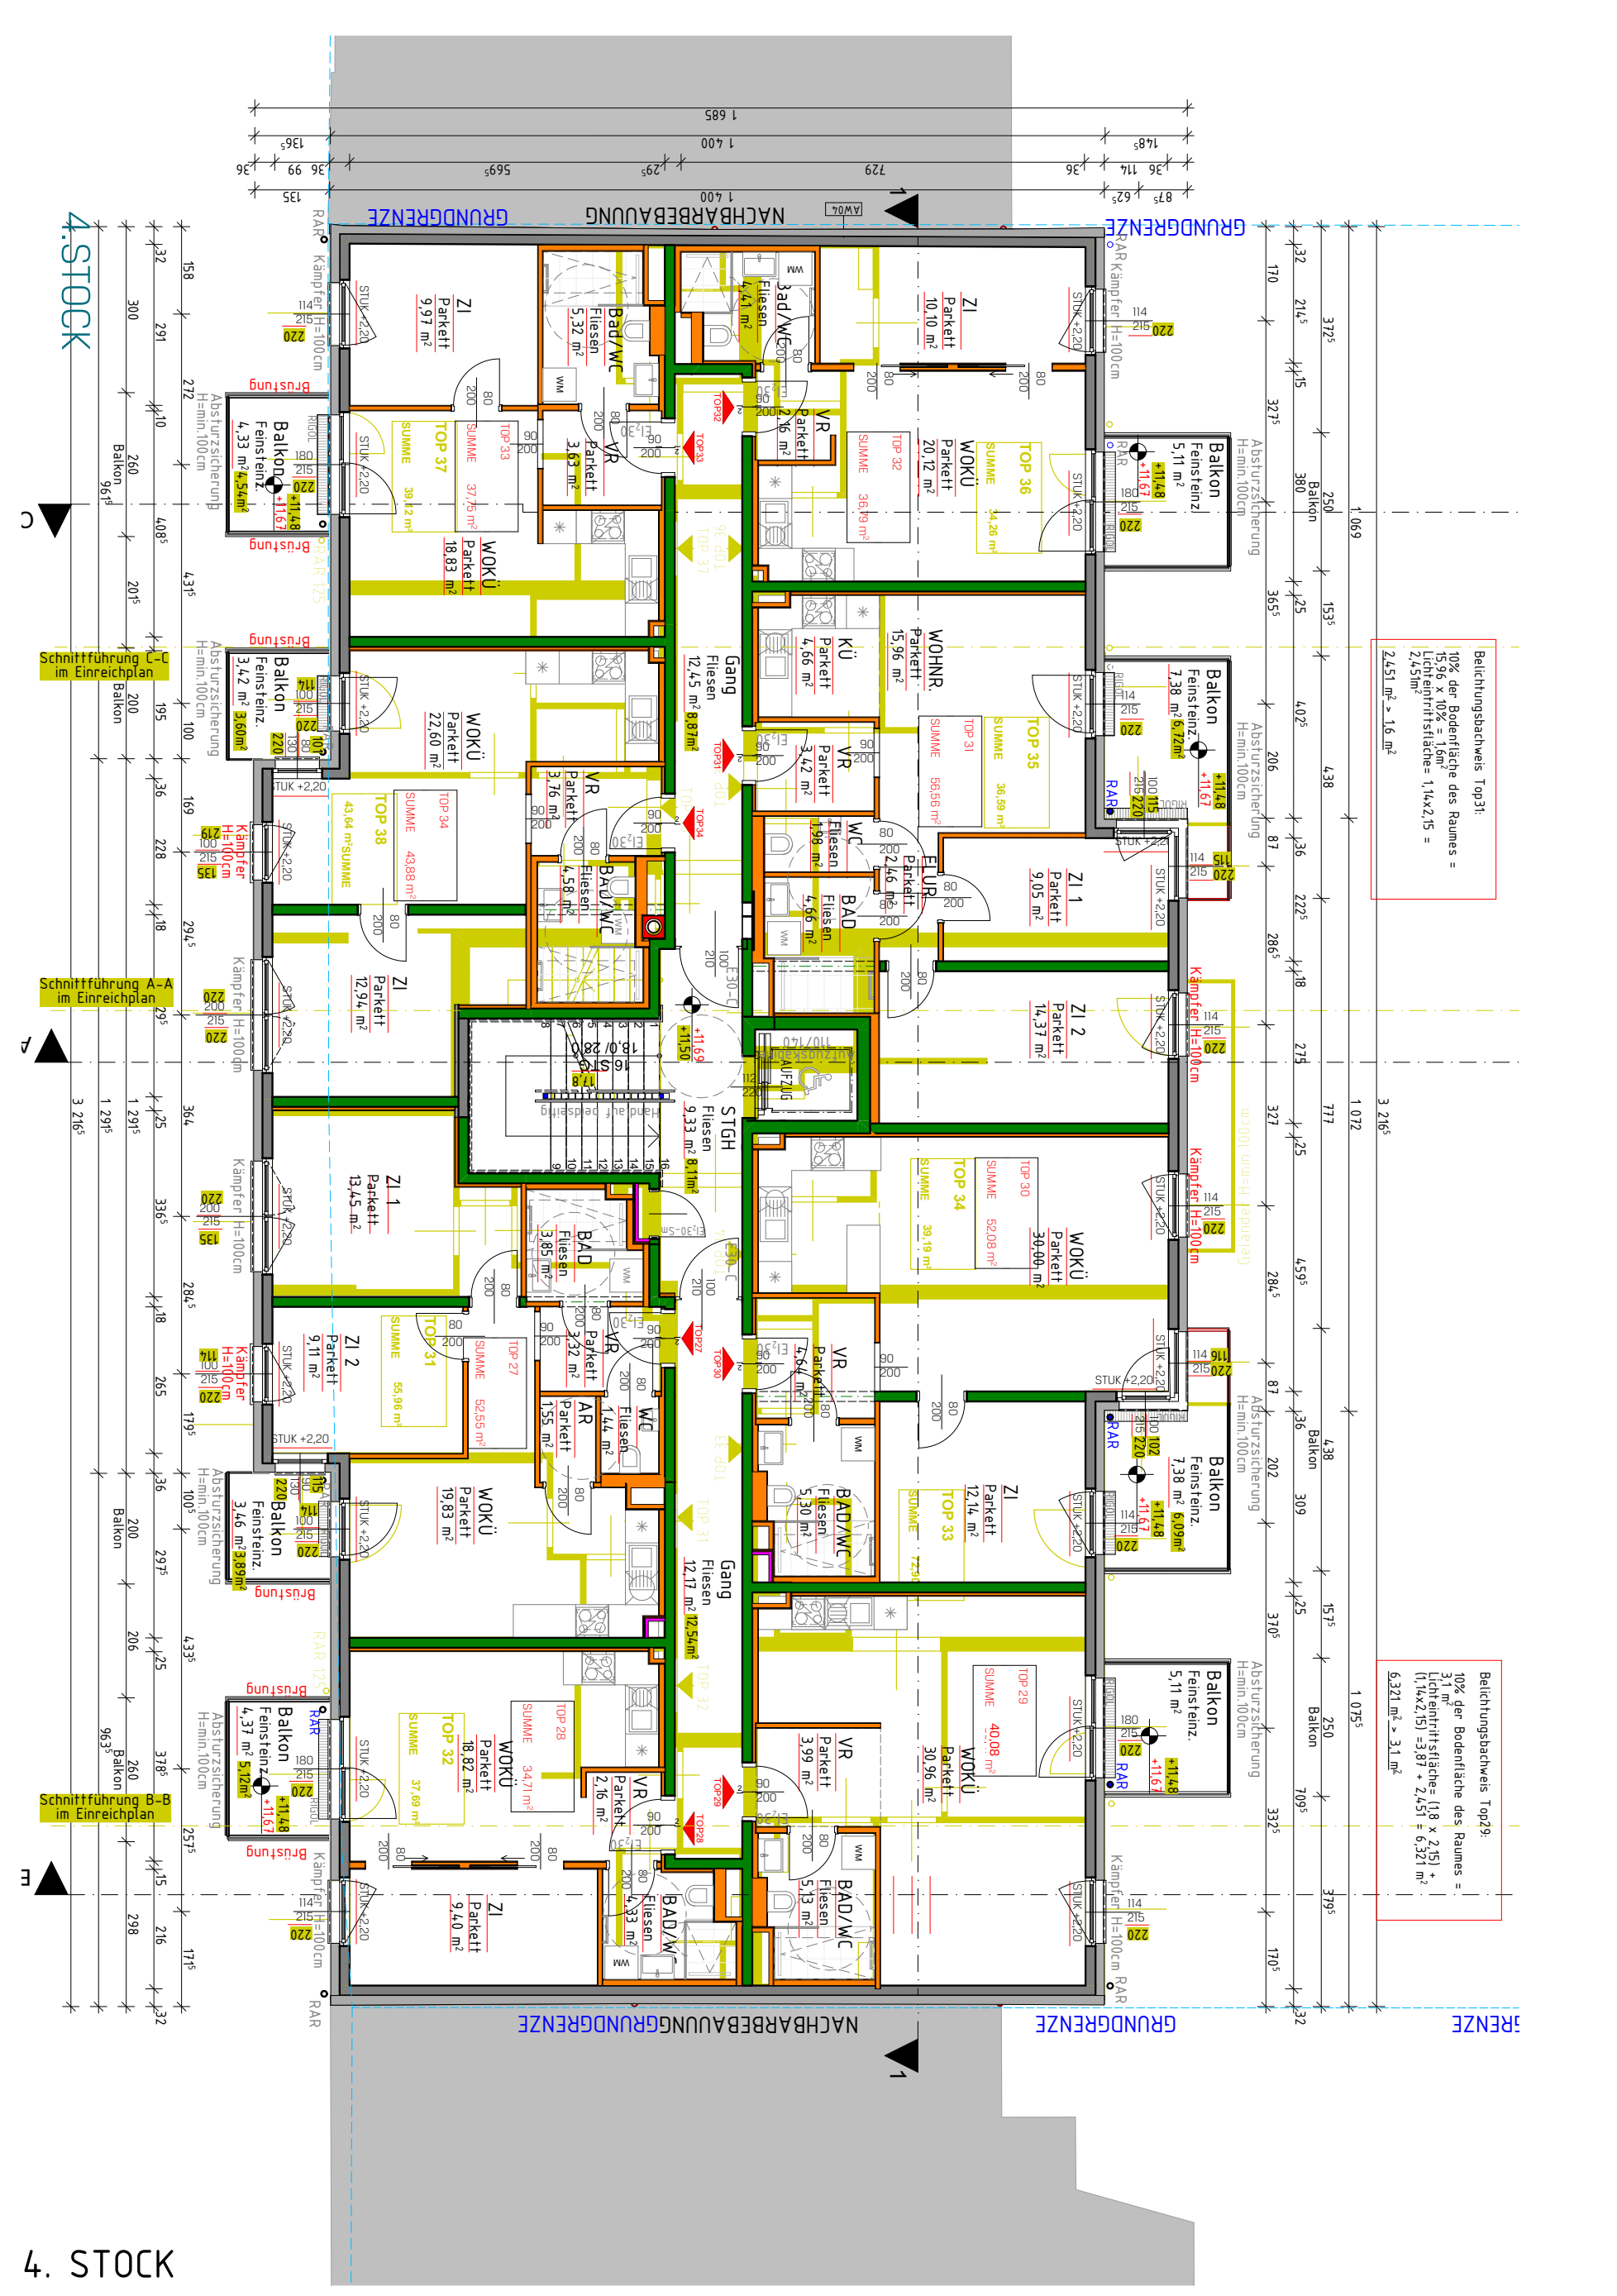

4. STOCK

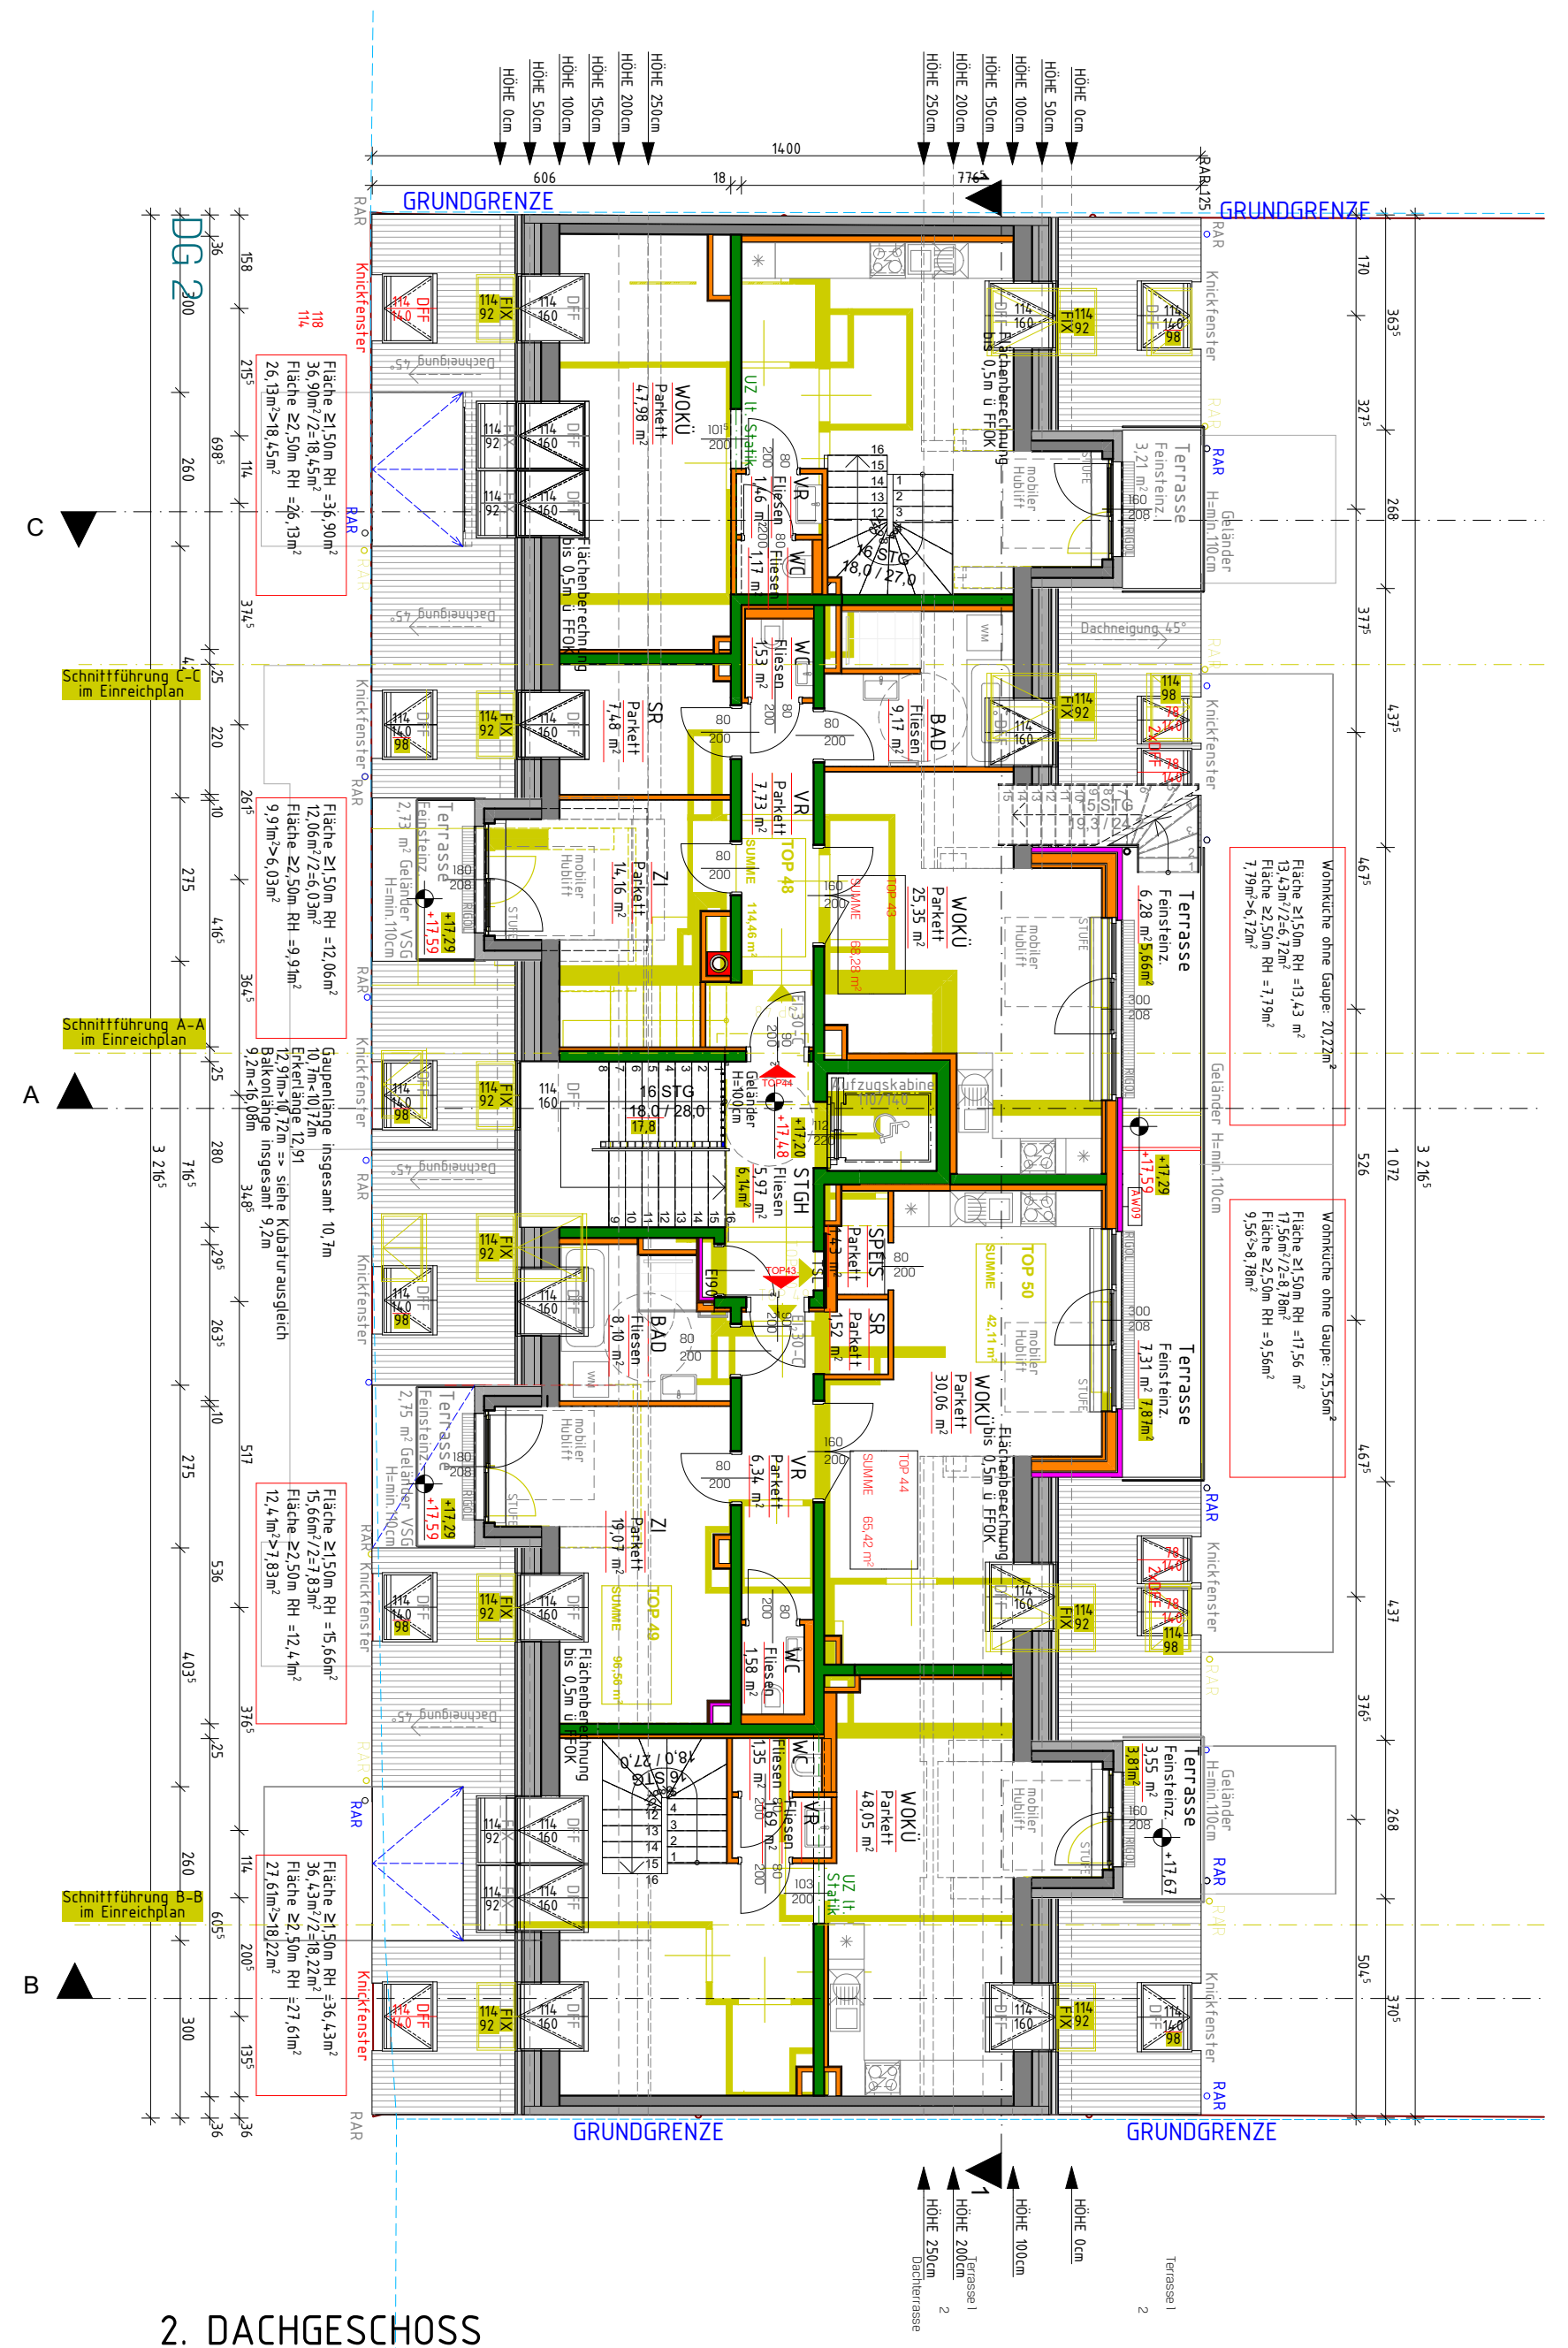

2. DACHGESCHOSS

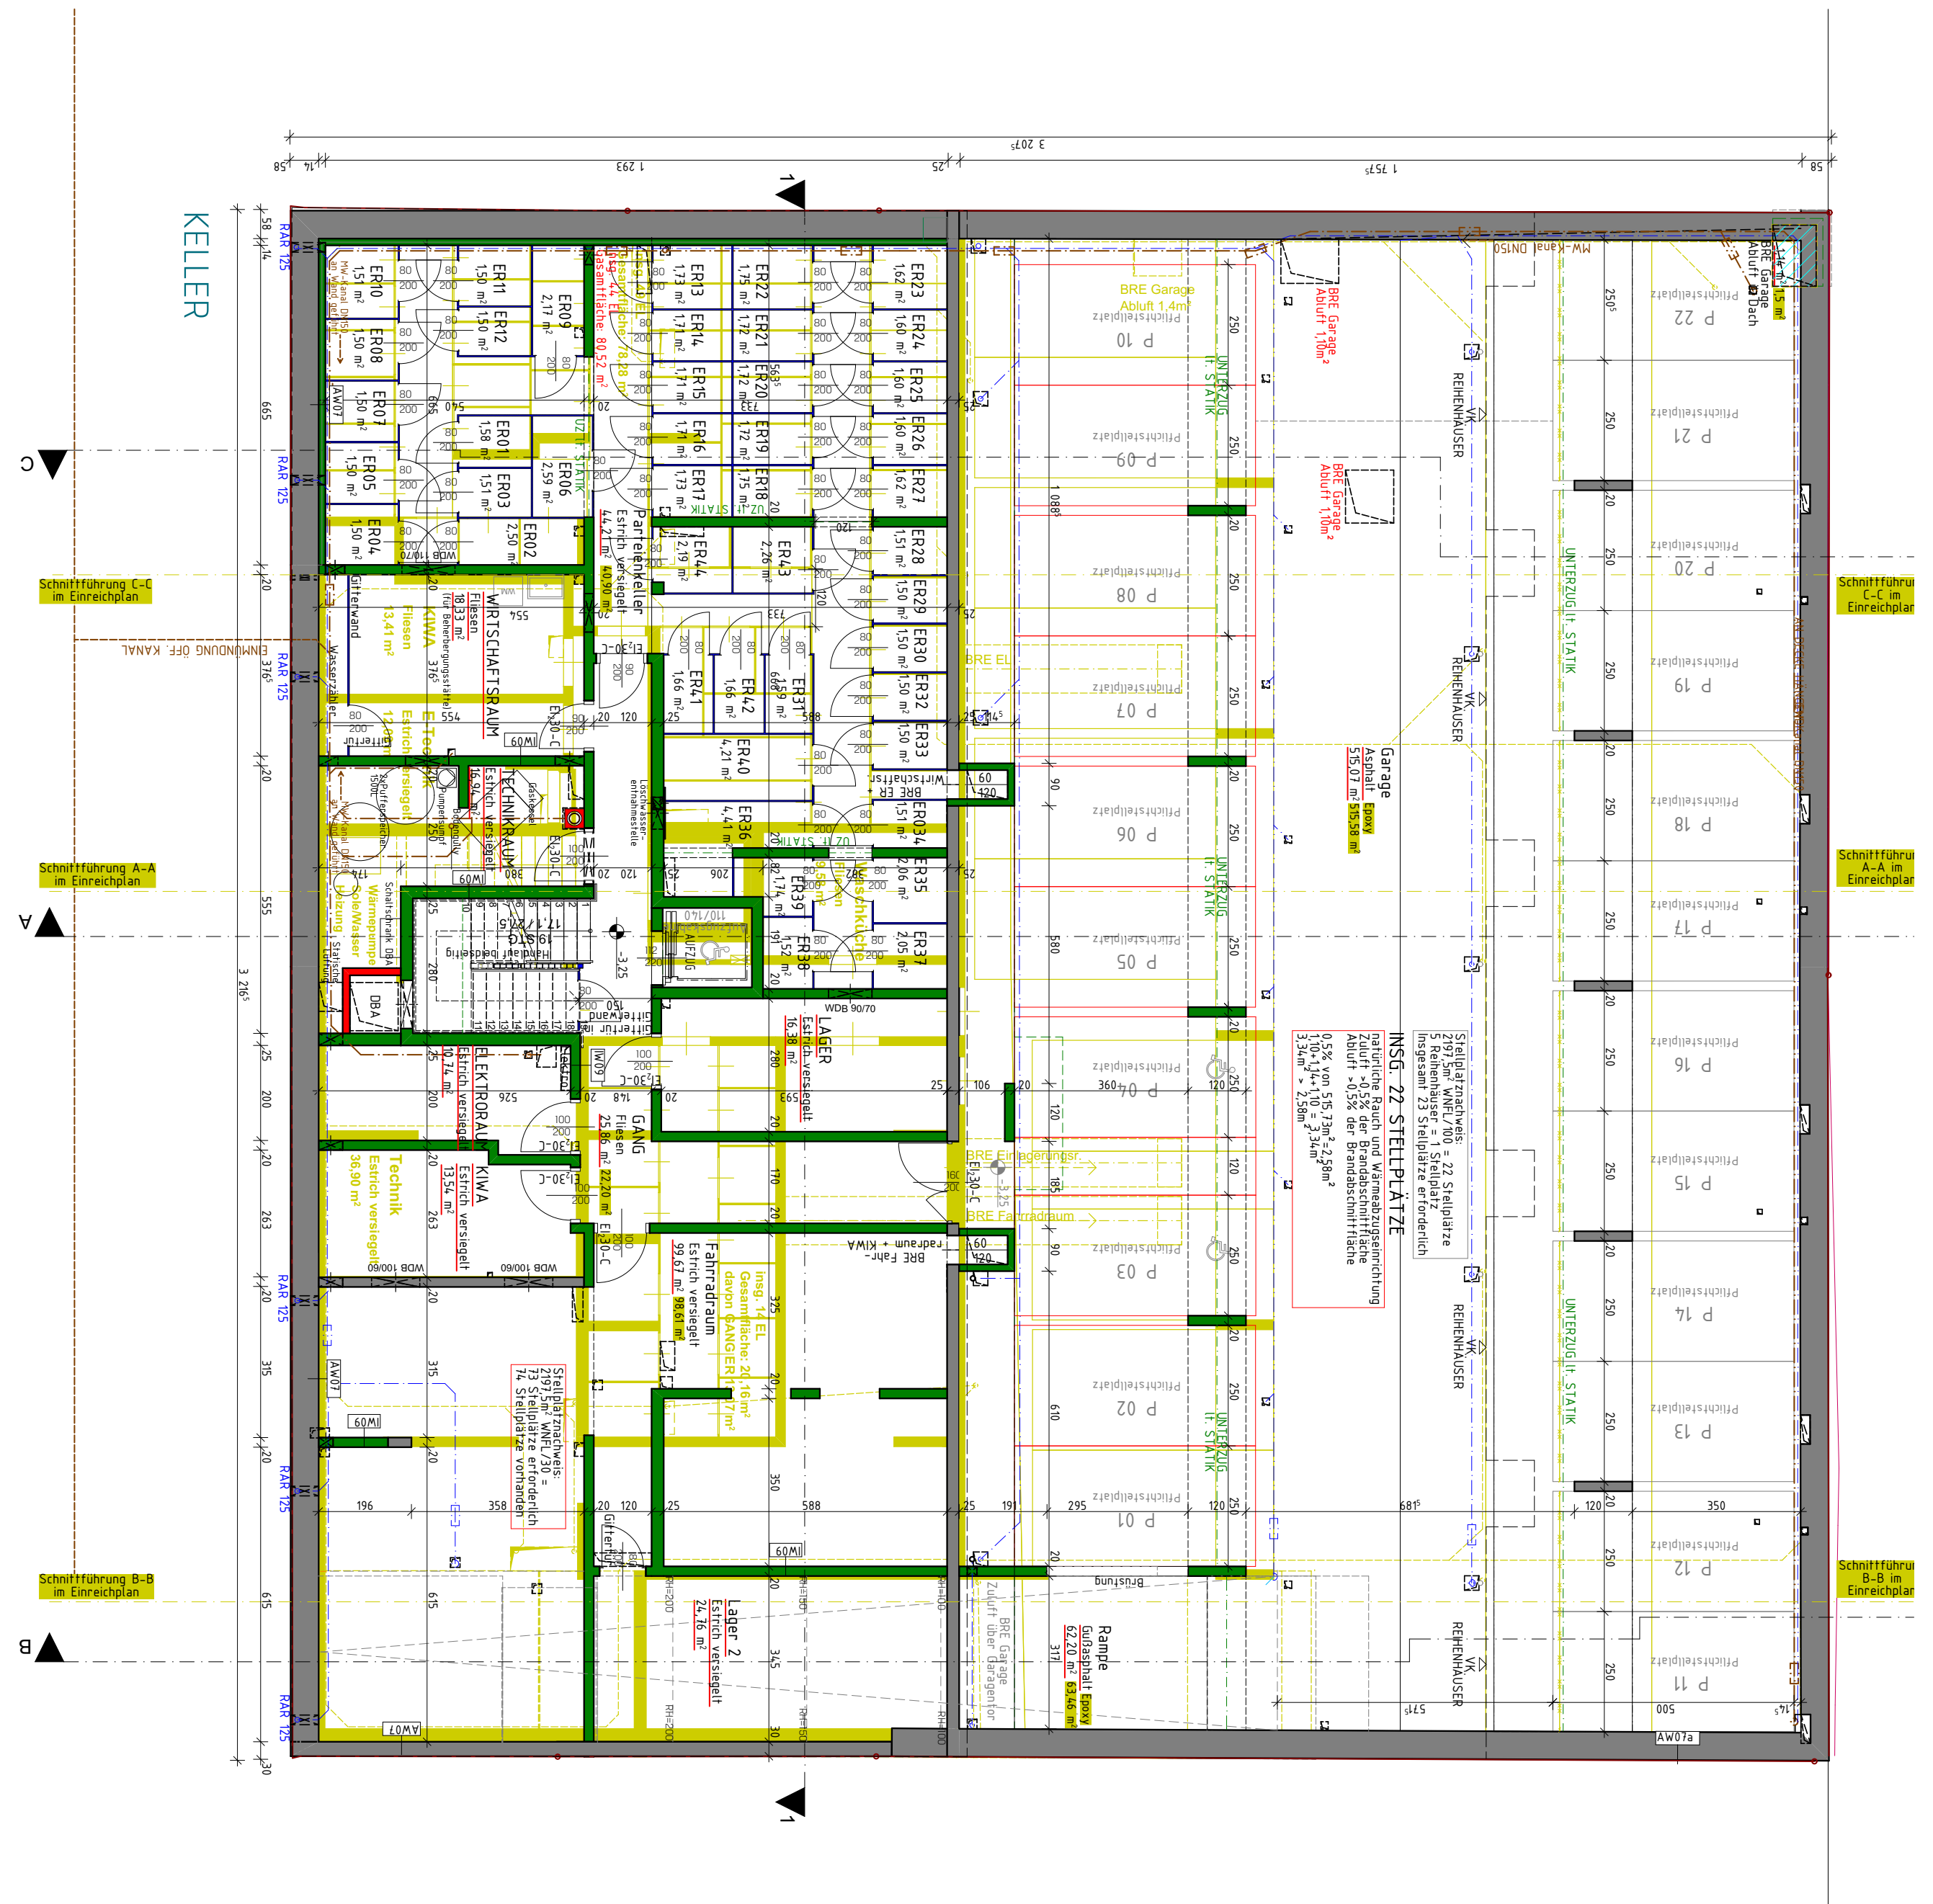

KELLERGESCHOSS

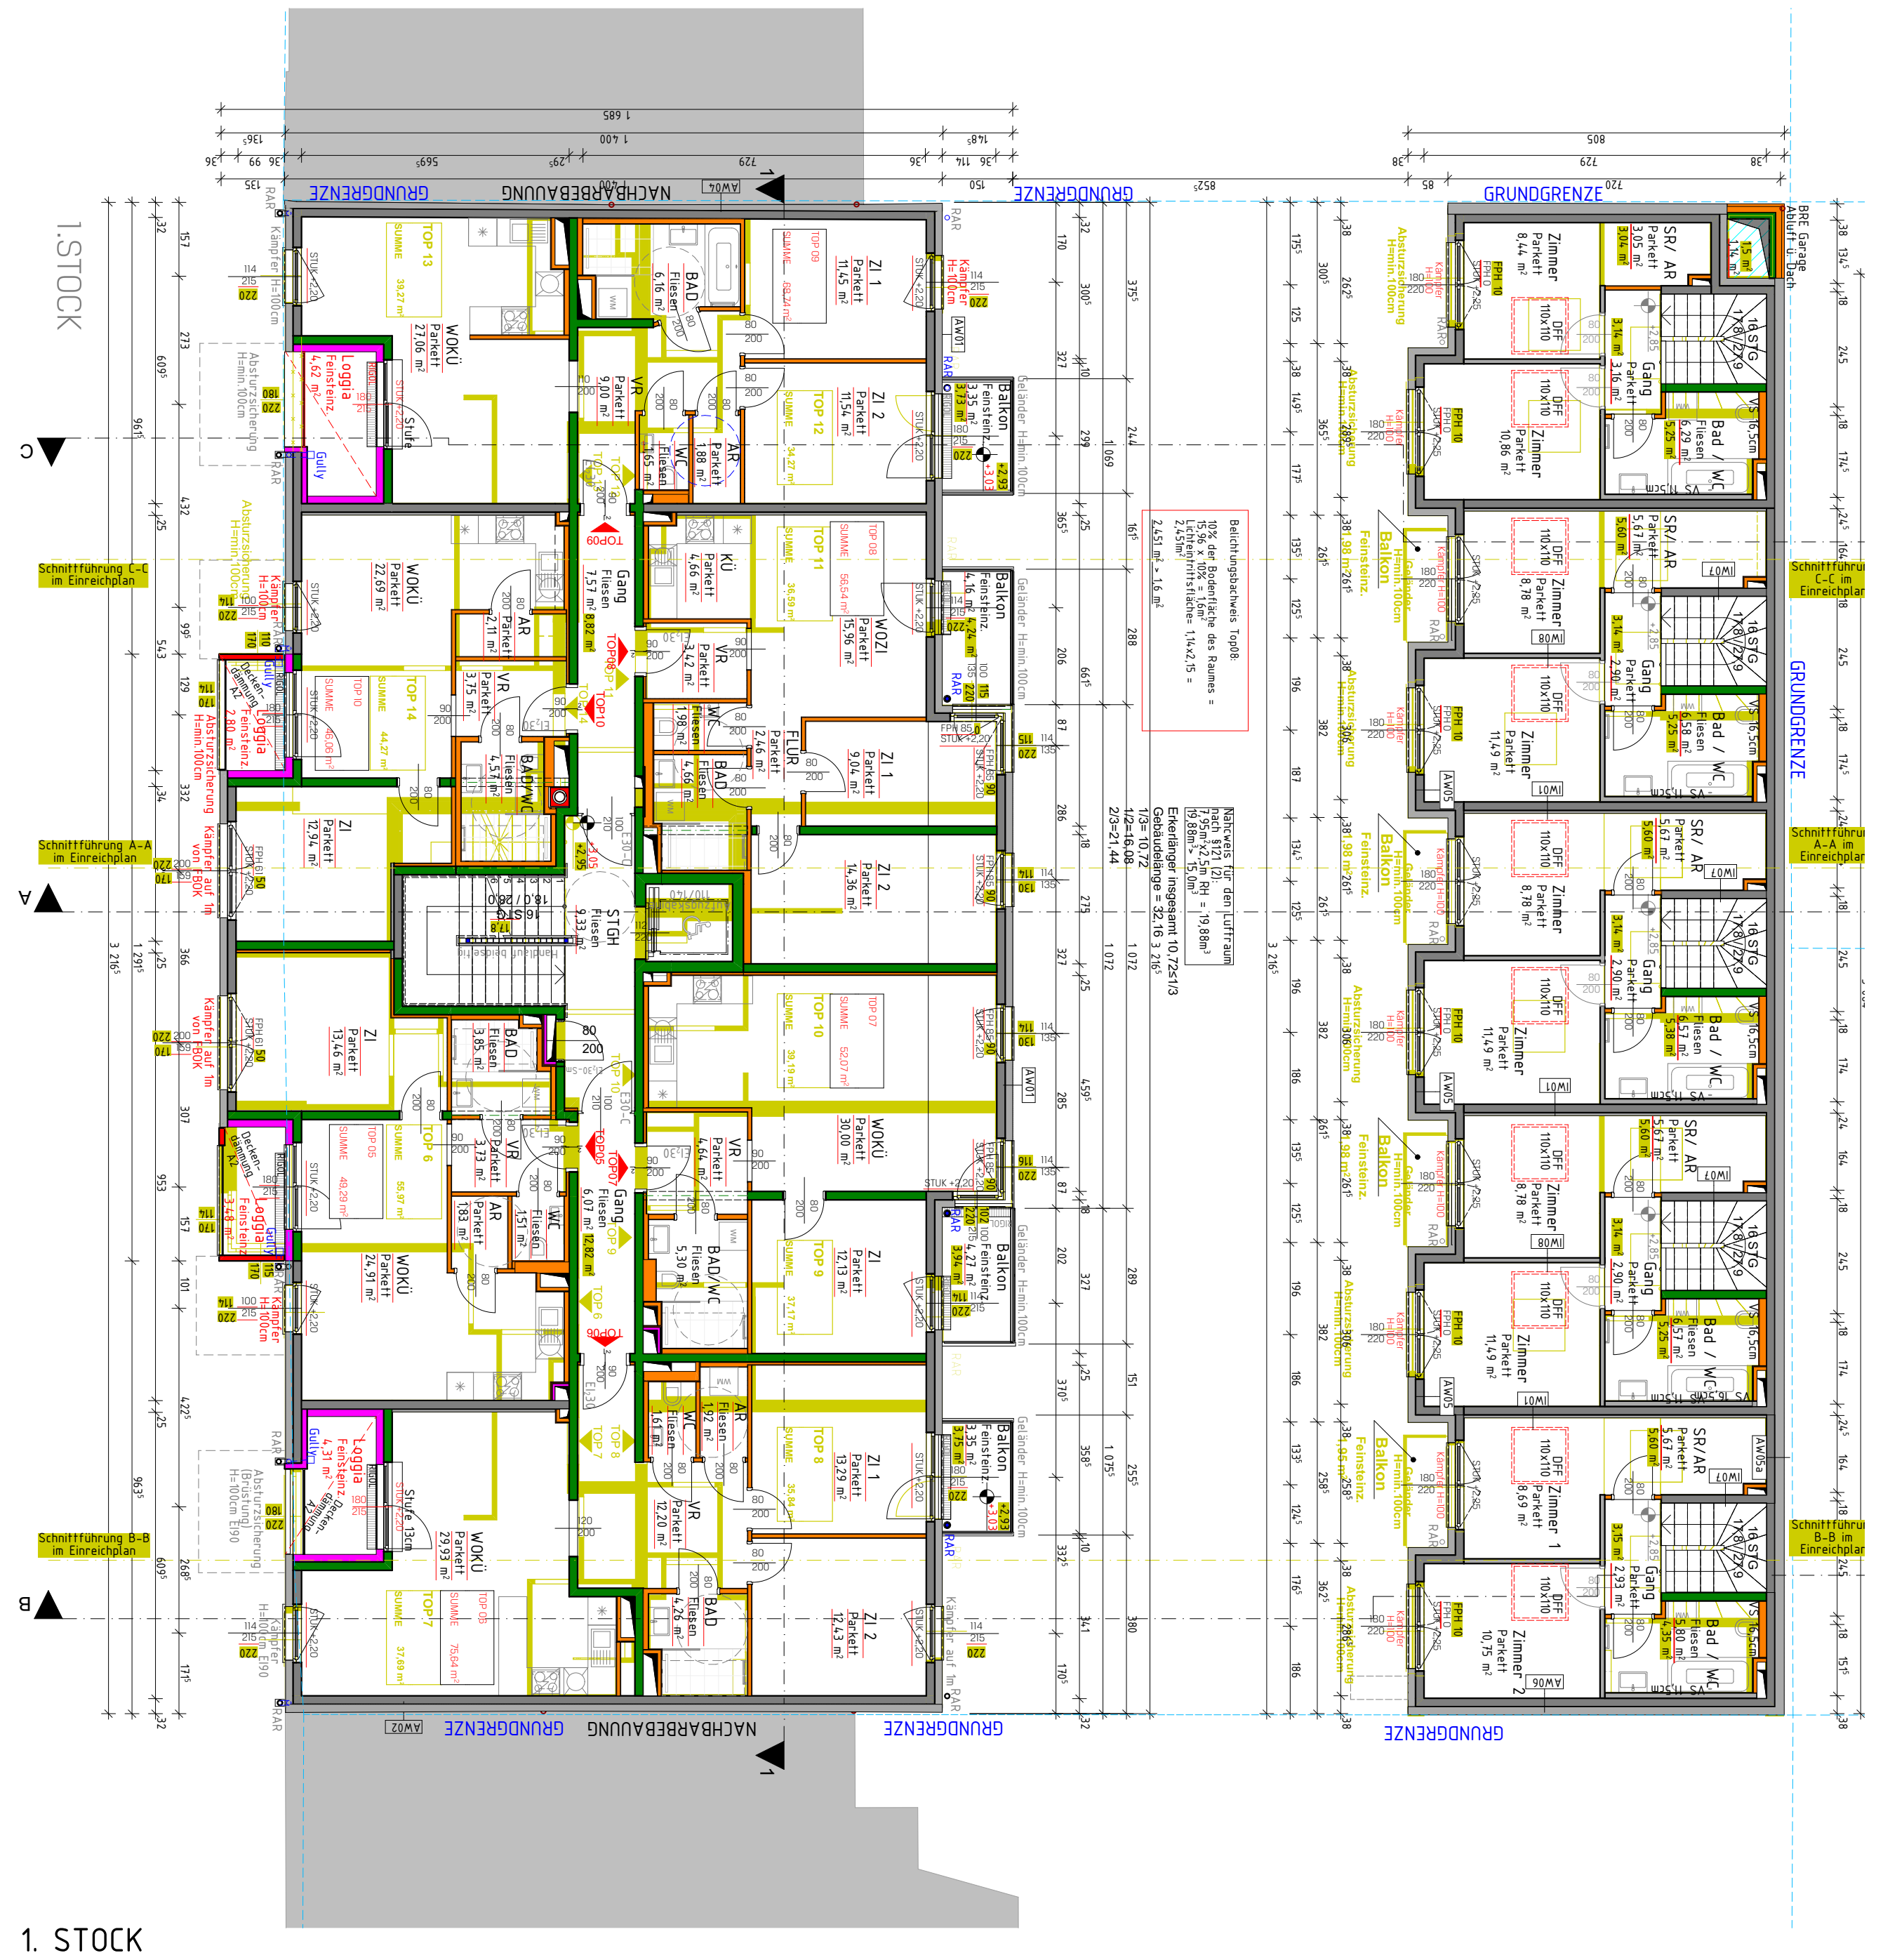

1. STOCK

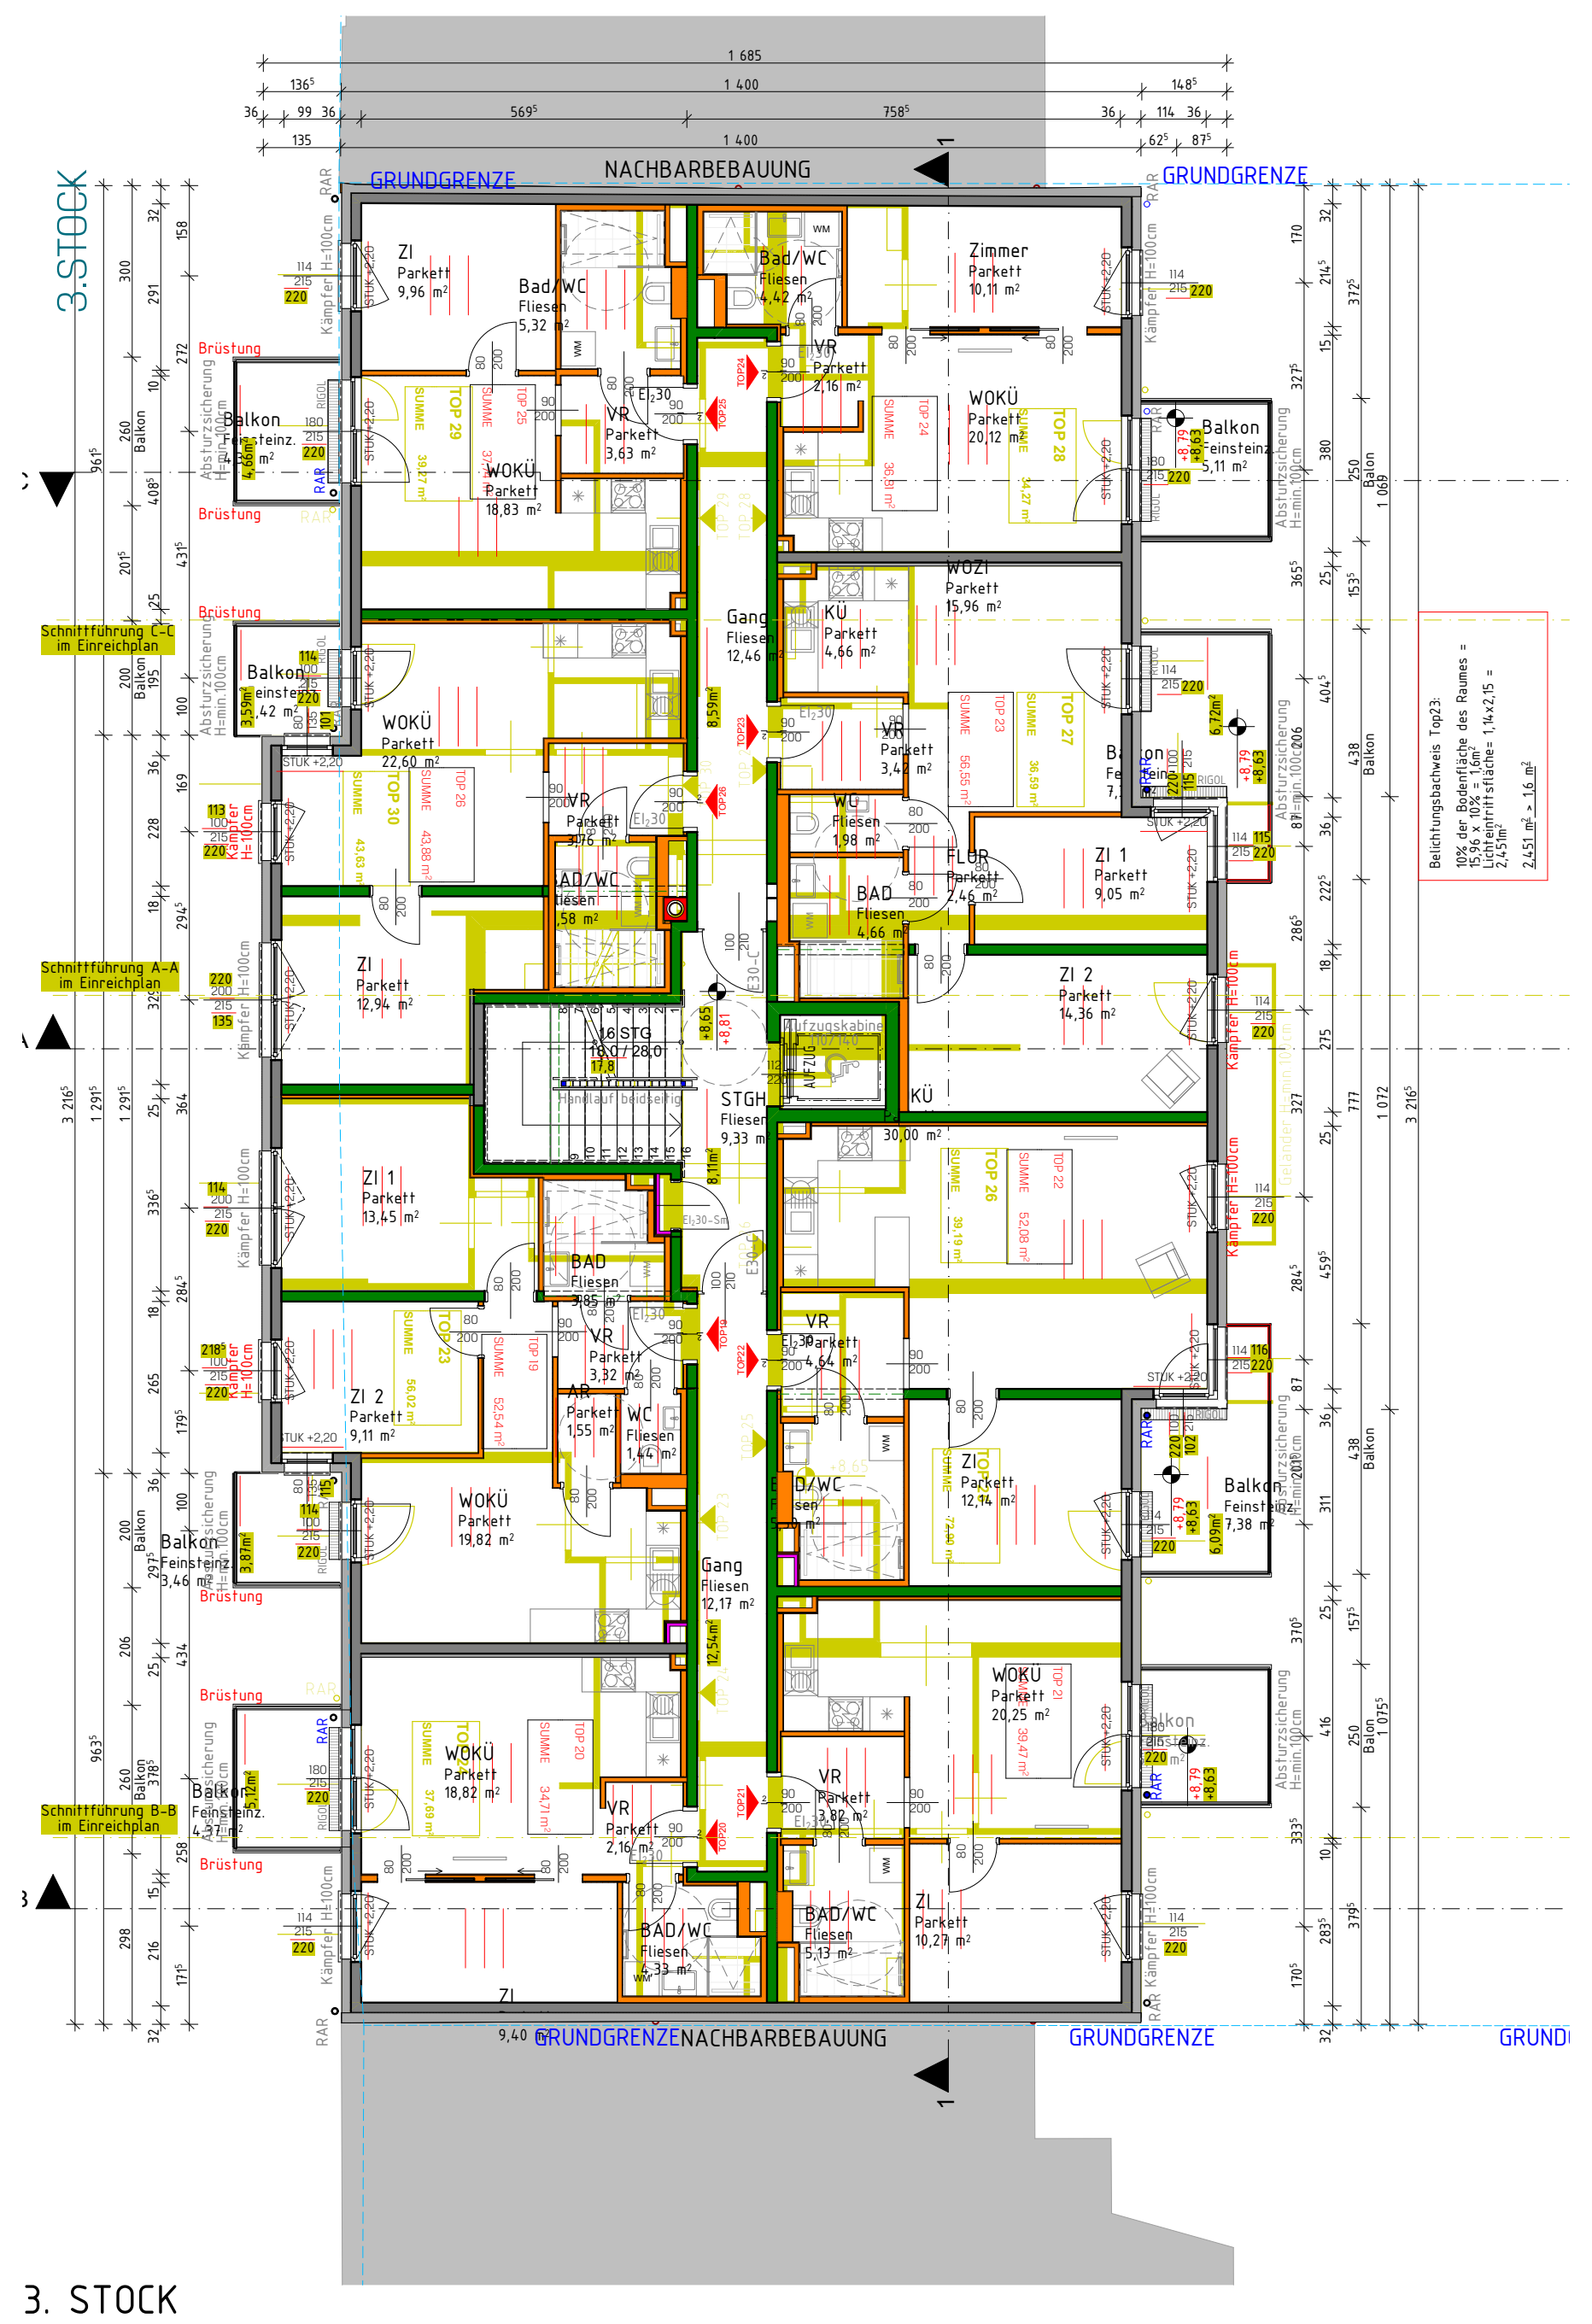

3. STOCK

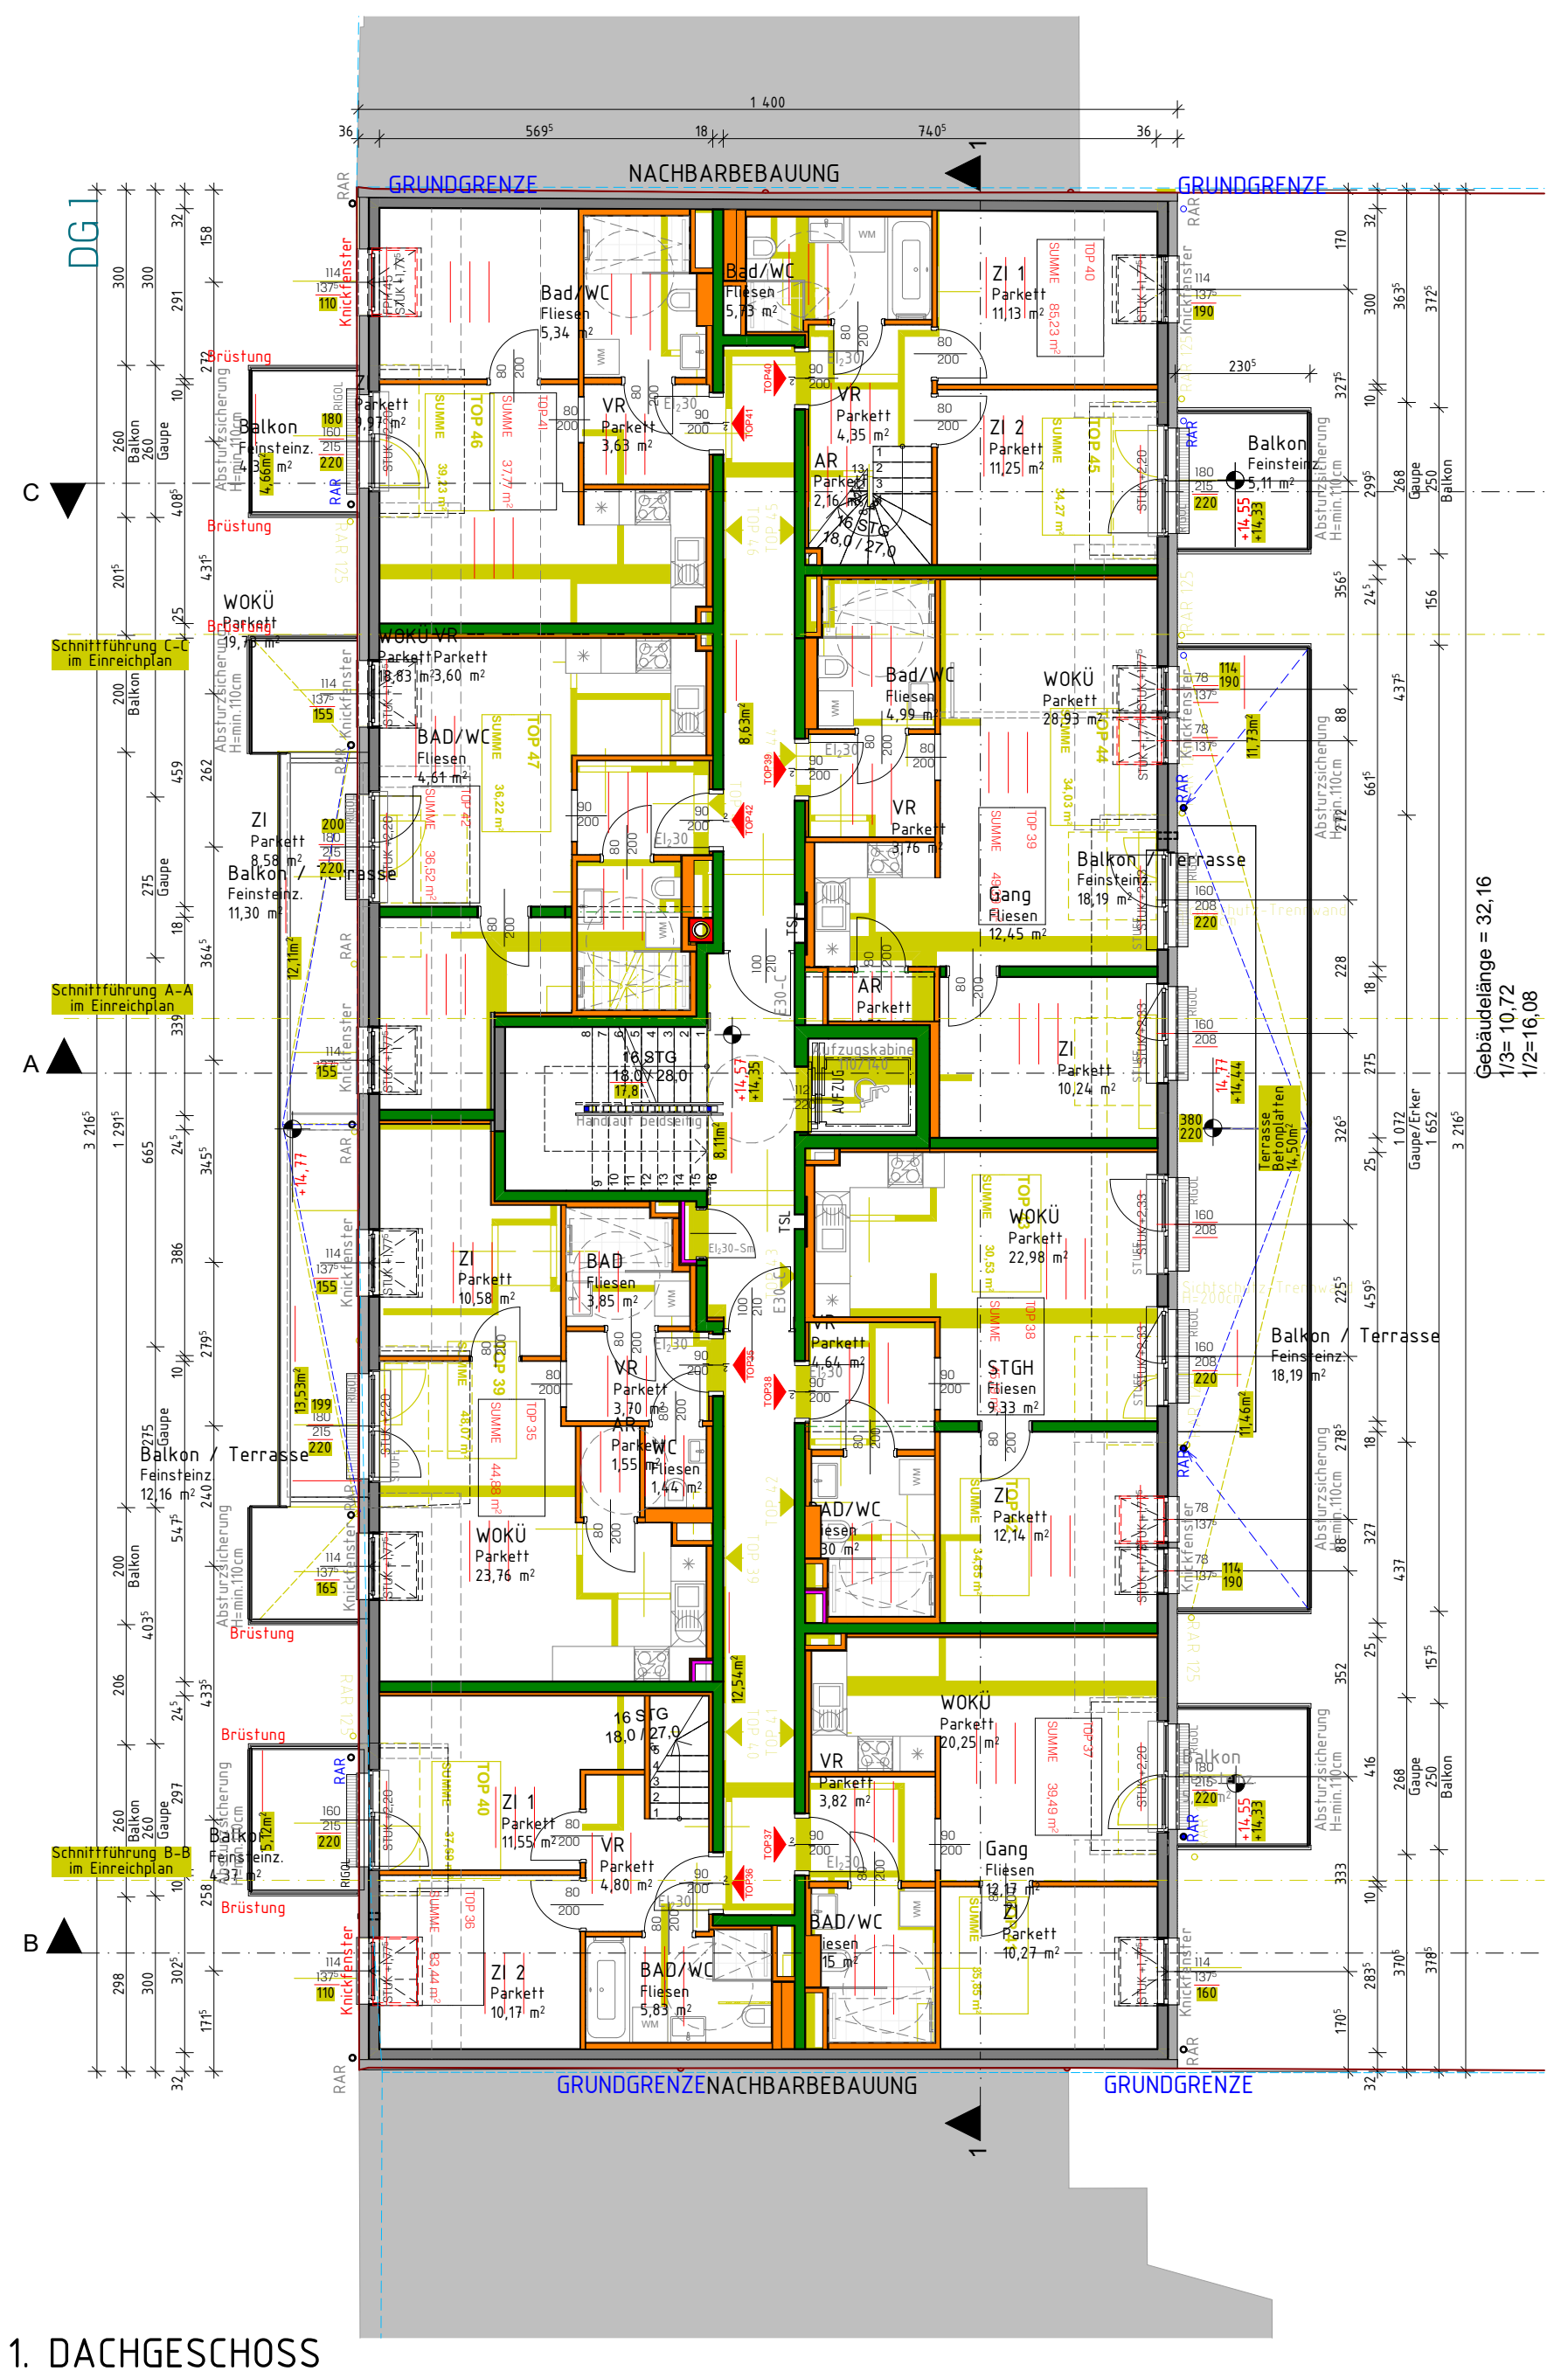

1. DACHGESCHOSS

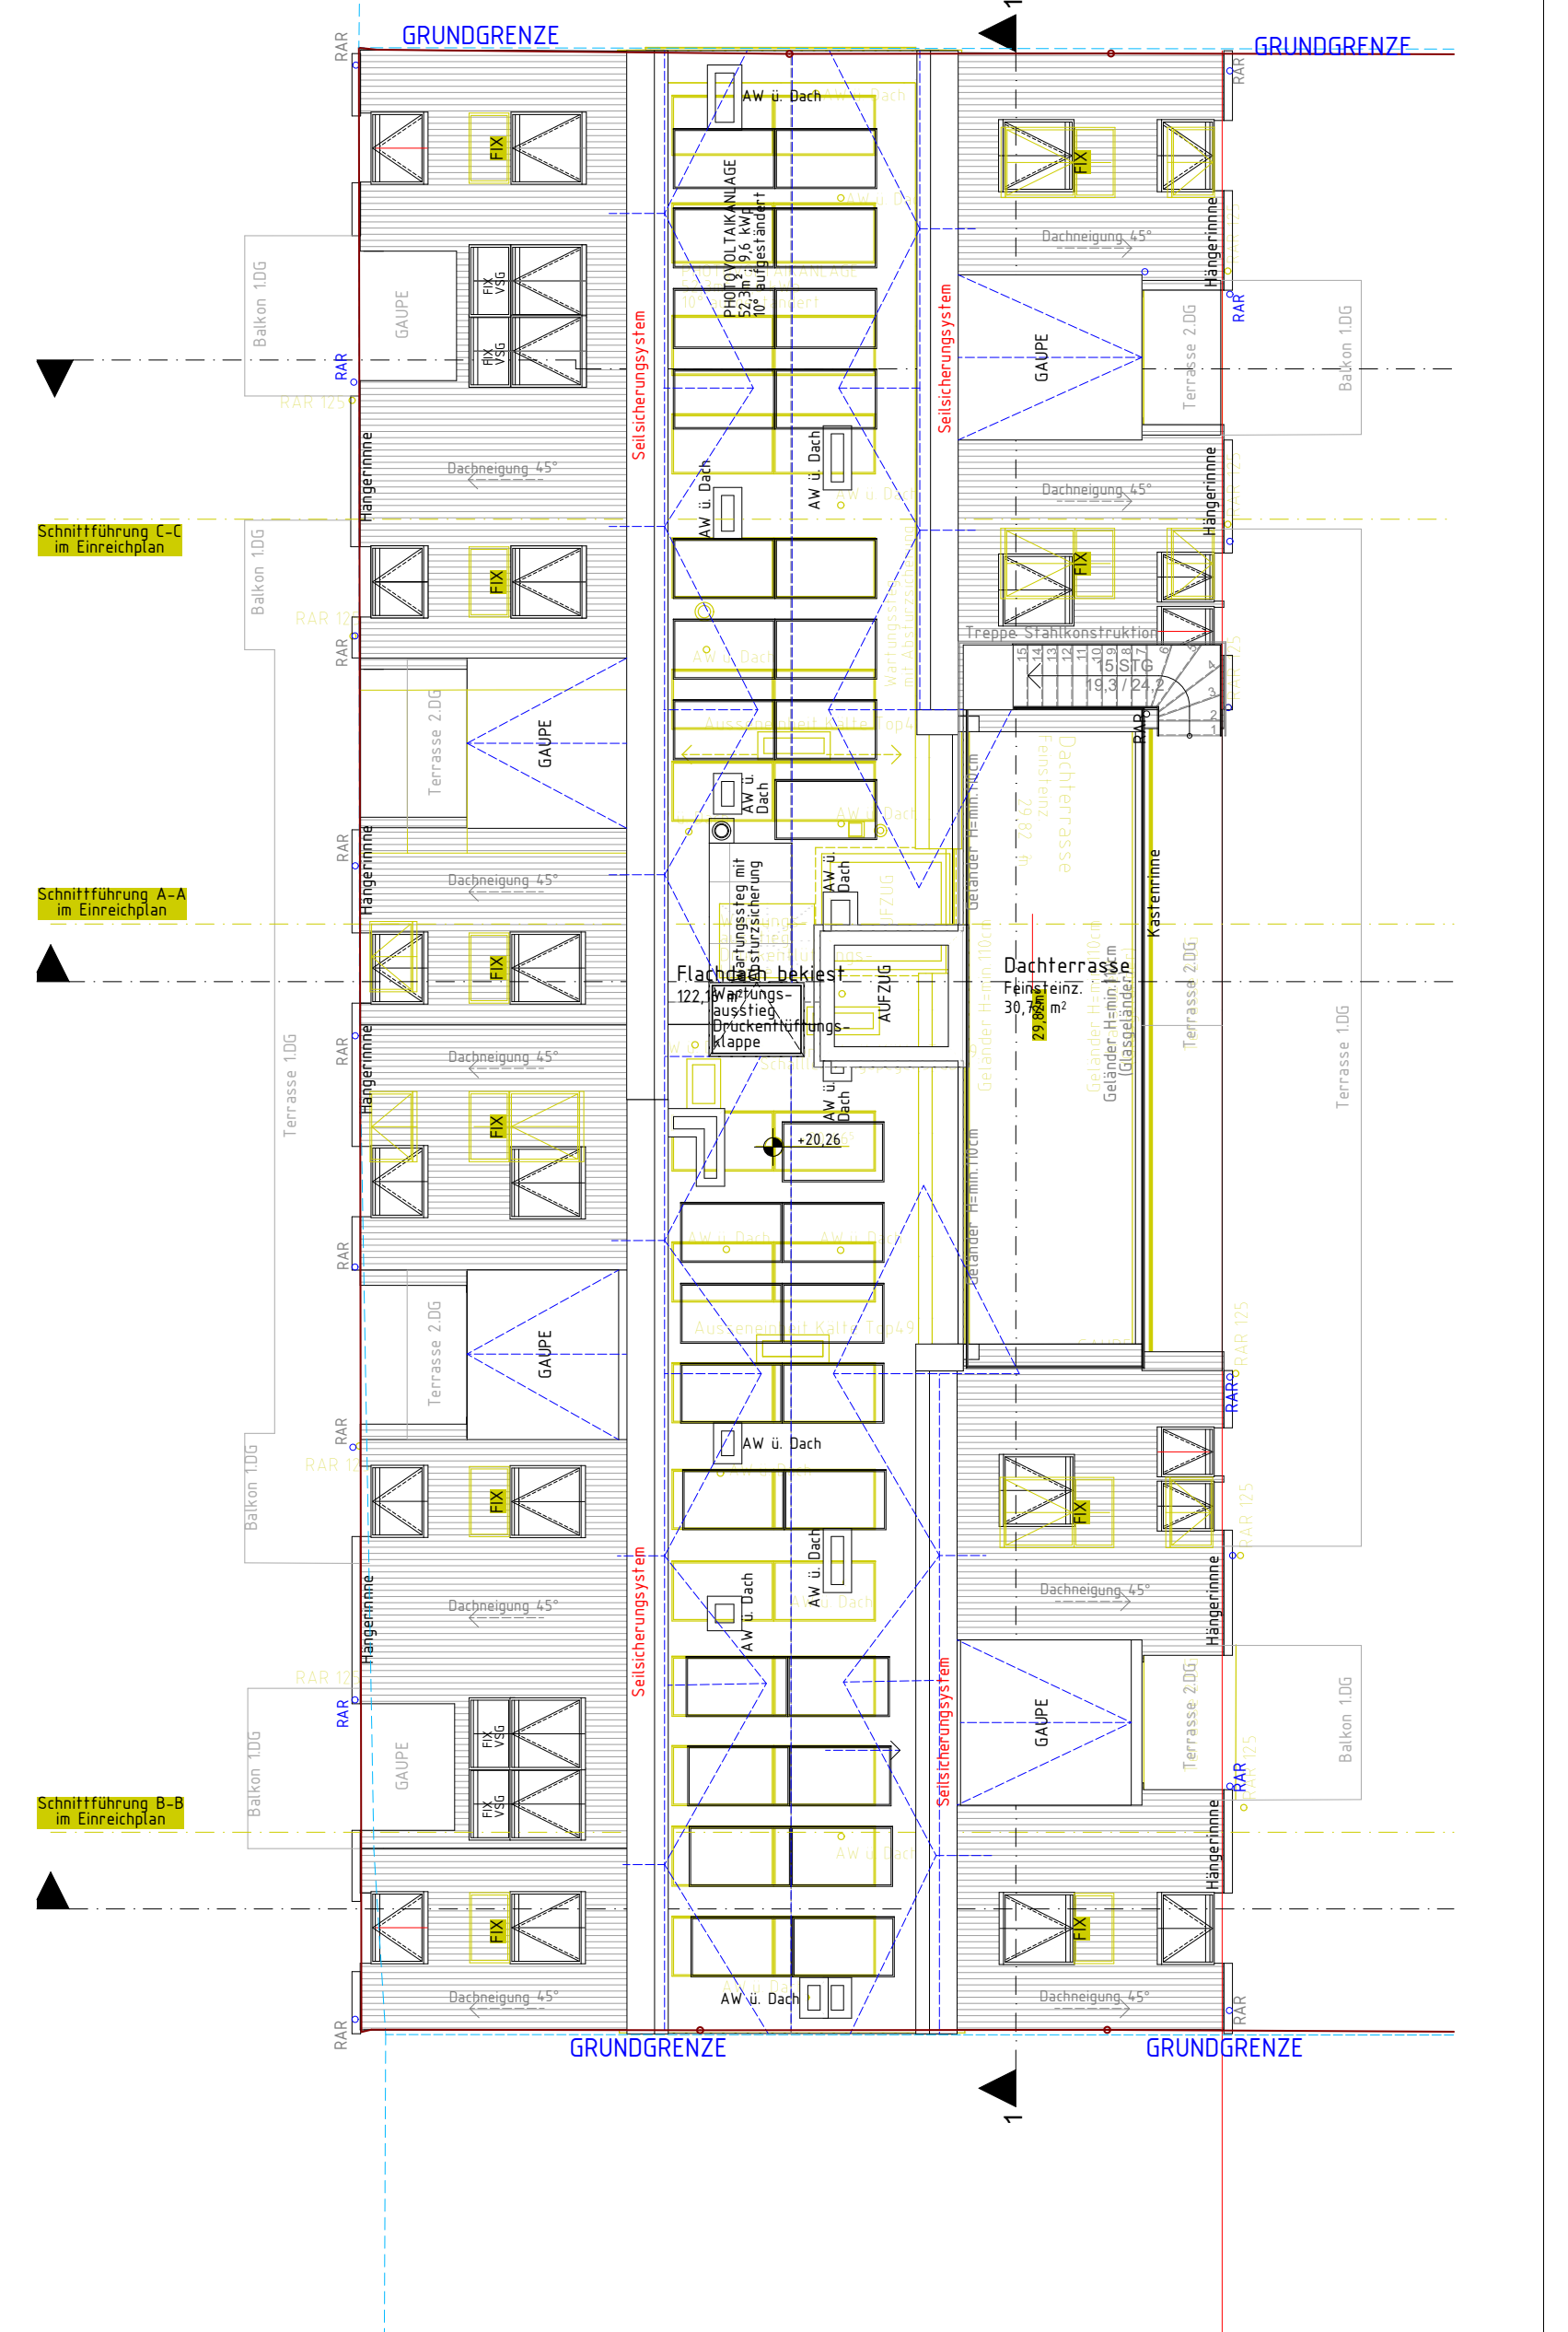

DACHDRAUFSICHT

AUFBAUTEN

AUSSENWÄNDE

AW01 Aussenwand Strassentrakt

Außenputz	0,20 cm
Grundbeschichtung	0,10 cm
Glasarmierung	0,10 cm
Mineralischer Klebe- und Armierungsmörtel	0,20 cm
Dämmung A2	18,00 cm
Mineralischer Klebe- und Armierungsmörtel	0,40 cm
Stahlbeton lt. Statik (2400kg/m^3)	18,00 cm
Innenspachtelung	0,20 cm
Gesamtaufbau	ca.37,2cm

AW01a Aussenwand Strassentrakt + Schauseitenverkleidung

Fassadenplatten (HardTop Baumit)	~~0,80 cm~~
~~Unterkonstrukton/ Hinterlüftung~~	~~5,00 cm~~
~~Winddichte Folie~~	~~0,06 cm~~
Dämmung A2	18,00 cm
Mineralischer Klebe- und Armierungsmörtel	0,40 cm
Stahlbeton lt. Statik (2400kg/m^3)	18,00-20,00 cm
Innenspachtelung	0,20 cm
Gesamtaufbau	ca.42,5cm

AW02 Feuermauer angebaut

Dämmung Steinwolle A2	14,00 cm
Stahlbeton lt. Statik (2400kg/m^3)	18,00 cm
Innenspachtelung	0,20 cm
Gesamtaufbau	ca.34,2cm

AW03 Feuermauer an der Grundgrenze (n. angebaut)

Außenputz	0,20 cm
Grundbeschichtung	0,10 cm
Glasarmierung	0,10 cm
Mineralischer Klebe- und Armierungsmörtel	0,20 cm
Dämmung Steinwolle A2	18,00 cm
Mineralischer Klebe- und Armierungsmörtel	0,40 cm
Stahlbeton lt. Statik (2400kg/m^3)	18,00 cm
Innenspachtelung	0,20 cm
Gesamtaufbau	ca.37,2cm

AW05 Aussenwand Hoftrakt

Außenputz	0,20 cm
Grundbeschichtung	0,10 cm
Glasarmierung	0,10 cm
Mineralischer Klebe- und Armierungsmörtel	0,20 cm
Dämmung	18,00 cm
Mineralischer Klebe- und Armierungsmörtel	0,40 cm
Stahlbeton lt. Statik (2400kg/m^3)	18,00 cm
Innenspachtelung	0,20 cm
Gesamtaufbau	ca.39,2cm

AW06 Stützwand an der Grundgrenze

Stahlbeton lt. Statik (2400kg/m^3)	20,00 cm
Gesamtaufbau	ca.20,0cm

AW07 Außenwand Keller

Pfahlwand aus Stahlbeton lt. Statik (2400kg/m^3)	58,00 cm
Gesamtaufbau	ca.58,0cm

AW07a Außenwand Keller + VS

Pfahlwand aus Stahlbeton lt. Statik (2400kg/m^3)	58,00 cm
Stahlbeton VS	14,00 cm
Gesamtaufbau	ca.72,0cm

AW08 Außenwand Aufzug über Dach

Außenputz	0,20 cm
Grundbeschichtung	0,10 cm
Glasarmierung	0,10 cm
Mineralischer Klebe- und Armierungsmörtel	0,20 cm
Dämmung	10,00 cm
Mineralischer Klebe- und Armierungsmörtel	0,40 cm
Stahlbeton lt. Statik (2400kg/m^3)	14,00 cm
Gesamtaufbau	ca.25,0cm

AW09 Außenwand Gaupe Hoftrakt

Außenputz	0,20 cm
Grundbeschichtung	0,10 cm
Glasarmierung	0,10 cm
Mineralischer Klebe- und Armierungsmörtel	0,20 cm
Dämmung	8,00 cm
Schalung	2,50 cm
Holzriegelkonstruktion dazw. Dämmung	16,00 cm
Schalung	2,50 cm
Instalationsebene gedämmt	5,00 cm
GK-Platte	1,50 cm
Gesamtaufbau	ca.36,1cm

INNENWÄNDE

IW01 Trennwand STB zw. Wohnungen

1xGipskartonplatte	1,25 cm
CW-Profil dazw. Mineralwolle	min. 5,00 cm
Stahlbeton lt. Statik (2400kg/m^3)	18,00 cm
Spachelung	0,20 cm
Gesamtaufbau	24,5 cm

IW01a Trennwand STB zw. Wohnungen + Installation

1x1,25 Gipskartonplatten	1,50 cm
CW-Profil dazw. Dämmung A2	min. 10,00cm
Stahlbeton lt. Statik (2400kg/m^3)	18,00 cm
Innenspachtelung	0,20 cm
Gesamtaufbau	34,5 cm

IW02 entfällt = IW01 gleich

IW03 Trennwand zw. Wohnung u. Gang

1xGipskartonplatte	1,25 cm
PE-Folie	0,02 cm
CW-Profil dazw. Dämmung	5,00 cm
Stahlbeton lt. Statik (2400kg/m^3)	18,00 cm
Innenspachtelung	0,20 cm
Gesamtaufbau	24,5 cm

IW04 Trennwand zw. Wohnung u. Einfahrt

Außenputz	0,20 cm
Grundbeschichtung	0,10 cm
Glasarmierung	0,10 cm
Mineralischer Klebe- und Armierungsmörtel	0,20 cm
Dämmung Steinwolle A2	16,00 cm
Mineralischer Klebe- und Armierungsmörtel	0,40 cm
Stahlbeton lt. Statik (2400kg/m^3)	18,00 cm
Innenspachtelung	0,20 cm
Gesamtaufbau	35,2 cm

IW05 Trennwand zw. Wohnung u. Müllraum

Gipskartonplatte	1,25 cm
PE-Folie	0,02 cm
CW-Profil dazw. Dämmung	5,00 cm
Stahlbeton lt. Statik (2400kg/m^3)	18,00 cm
Innenspachtelung	0,20 cm
Gesamtaufbau	24,5 cm

IW06 Schachtwand EI90

EI90 3x1,5 GKF-Platten	4,50 cm
CW-Profil dazw. Dämmung	5,00 cm
Gesamtaufbau	9,5 cm

IW07 Scheidewand tragend

Innenspachtelung	0,20 cm
Stahlbeton lt. Statik	18,00 cm
Innenspachtelung	0,20 cm
Gesamtaufbau	18,4 cm

IW08 Scheidewand

Gipskartonplatte	1,25 cm
CW-Profil dazw. Dämmung	7,50 cm
Gipskartonplatte	1,25 cm
Gesamtaufbau	10,0 cm

IW08a Scheidewand Bad+WC

Gipskartonplatte	1,25 cm
Hygrodiode	
CW-Profil dazw. Dämmung	7,50 cm
Gipskartonplatte	1,25 cm
Gesamtaufbau	10,0 cm

IW09 Innenwand Keller

Stahlbeton lt. Statik (2400kg/m^3)	18,00 - 25,00cn
Gesamtaufbau	18,00 - 25,00cn

Vorsatzschale 7,5cm

Gipskartonplatte	1,25 cm
CW-Profil dazw. Dämmung (lt. HAT)	7,50 - 20,00 cm
Gesamtaufbau	7,55 cm

DECKENAUFBAUTEN

Dächer

DA01 Terrasse über Tiefgarage

Belag	2,00 cm
Splittbett	3,00 cm
Tragschicht	18,00 cm
Schutzvlies	0,20 cm
Abdichtung wurzelfest	0,50 cm
Abdichtung 2-lagig	1,00 cm
Gefällebeton	8,00 c i.M.
Stahlbetondecke lt. Statik (2400kg/m^3)	35-65 cm
Gesamtaufbau	32,7 cm

DA02 Gründach über Tiefgarage

Pflanzsubstrat für Gründach	20,00 cm
Filtervlies	0,02 cm
Drainageplatte	3,00 cm
Schutzvlies	0,20 cm
Abdichtung wurzelfest	0,50 cm
Abdichtung 2-lagig	1,00 cm
Gefällebeton	8,00 cm i.M.
Stahlbetondecke lt. Statik (2400kg/m^3)	35-65 cm
Gesamtaufbau	32,7 cm

DA03 Kinderplatz über Rampe der Tiefgarage

Fallschuzplatten	4,00 cm
Splittbett	4,00 cm
Schutzvlies	0,02 cm
Abdichtung 2-lagig	1,00 cm
Gefällebeton	8,00 cm i i.M.
Stahlbetondecke lt. Statik (2400kg/m^3)	35-65 cm
Gesamtaufbau	18,0 cm

DA04 Gehweg über Tiefgarage

Estrichplatten	4,00 cm
Splittbett	4,00 cm
Tragschicht	14,00 cm
Schutzvlies	0,20 cm
Abdichtung wurzelfest	0,50 cm
Abdichtung 2-lagig	1,00 cm
Gefällebeton	8,00 cm i.M.
Stahlbetondecke lt. Statik (2400kg/m^3)	35-65 cm
Gesamtaufbau	32,7 cm

DA05 Terrasse über Wohnung u. Gaupen

Belag für Außenbereich	2,00 cm
Kies	3,00 cm
Schutzvlies	0,20 cm
Abdichtung 2-lagig	1,00 cm
Gefälledämmung mit 2% Gefälle	20,00 cm i.M.
Dampfbremse mit Voranstrich	0,10 cm
Stahlbetondecke lt. Statik (2400kg/m^3)	20,00 cm
Innenspachtelung	0,20 cm
Gesamtaufbau	46,5 cm i.M.

DA06 Dachschräge Beton

Blechdeckung	
Trennlage	0,20 cm
Vollholzschalung	2,40 cm
Konterlattung / Hinterlüftung	5,00 cm
Unterdeckbahn / Winddichtung	0,10 cm
Vollholzschalung	2,50 cm
Sparren 8x12cm dazw. Dämmung A2	12,00 cm
Lattung 8x8cm dazw. Dämmung A2	8,00 cm
Dampfbremse	0,04 cm
Stahlbetondecke lt. Statik (2400kg/m^3)	23,00 cm
Innenspachtelung	0,20 cm
Gesamtaufbau	53,4 cm

DA07 Flachdach begrünt

Pflanzsubstrat für Gründach	11,00 cm
Filtervlies	0,02 cm
Drainageplatte	3,00 cm
Gummigranulatplatte	1,00 cm
Abdichtung 2-lagig	1,00 cm
Gefälledämmung mit 2% Gefälle	20,00 cm i.M.
Dampfbremse	0,05 cm
Stahlbetondecke lt. Statik (2400kg/m^3)	20,00 cm
Innenspachtelung	0,02 cm
Gesamtaufbau	76,1 cm

~~**DA08 Flachdach über Aufzug**~~

DA08 Dach 5° über Aufzug

Blechdeckung	
Lattung	2,40 cm
Konterlattung / Hinterlüftung	5,00 cm
Unterdeckbahn / Winddichtung	0,10 cm
Schalung	2,40 cm
Dämmkeil 5°	
Dampfbremse mit Voranstrich	0,10 cm
Stahlbetondecke lt. Statik (2400kg/m^3)	20,00 cm
Gesamtaufbau	53,3 cm

DA09 Gaupendach

Kies	8,00 cm
Schutzvlies	0,20 cm
Abdichtung 2-lagig	1,00 cm
Dämmung mit 2% Gefälle	20,00 cm i.M.
Dampfbremse mit Voranstrich	0,04 cm
Stahlbetondecke lt. Statik (2400kg/m^3)	20,00 cm
Innenspachtelung	0,20 cm
Gesamtaufbau	51,4 cm i.M.

DA10 Balkon - thermisch getrennt mit Isokorb

Belag für Außenbereich	2,00 cm
Splittbett mit Gegengefälle	4,00 cm
Schutzvlies	0,50 cm
Abdichtung 2-lagig	1,00 cm
Stahlbetonplatte mit 2% Gefällle	16,00 cm
Gesamtaufbau	23,5 cm

Zwischendecken

DE01 Boden Tiefgarage

Asphalt	2,00 cm
faserbewerter Unterbeton	15,00 cm
Trennlage	0,02 cm
Tragender Boden im Gefälle	
Gesamtaufbau	17,02 cm

DE02 Boden Keller / Nebenräume

Fliesen/ Estrich beschichtet	1,50 cm
Abdichtung	0,50 cm
Estrich	5,00 cm
Fundamentplatte aus Dichtbeton lt. Statik	40,00 cm
Gleitschchicht+Vlies	0,50 cm
Sauberkeitsschicht	5,00 cm
Folie	0,02 cm
Gesamtaufbau	46,0 cm

DE03 Tiefgaragenrampe

Gußspahlt	2,00 cm
Grundierung	0,50 cm
Abdichtung	1,00 cm
Stahlbetonplate lt. Statik	40,00 cm
Gesamtaufbau	41,5 cm

DE04 Decke Wohnung über Tiefgarage

Bodenbelag	1,00 cm
Heizestrich	7,00 cm
Folie	0,01 cm
Trittschalldämmung	3,00 cm
Folie	0,01 cm
Schüttdämmstoff	4,00 cm
Stahlbetondecke lt. Statik (2400kg/m^3)	20,00 cm
Dämmung Steinwolle A2	16,00 cm
Gesamtaufbau	51,0 cm

DE04a Decke Apartment's über Tiefgarage

Bodenbelag	1,00 cm
Heizestrich	7,00 cm
Folie	0,01 cm
Trittschalldämmung	3,00 cm
Folie	0,01 cm
Dämmung	10,00 cm
Schüttdämmstoff	9,00 cm
Stahlbetondecke lt. Statik (2400kg/m^3)	35-60 cm
Dämmung Steinwolle A2	16,00 cm
Gesamtaufbau	46,0 cm

DE05 Decke Müllraum über Tiefgarage

Epoxy	2,00 cm
Estrich	5,50 cm
Abdichtung	1,00 cm
Gefällebeton	min. 5,00 cm
Stahlbetondecke lt. Statik (2400kg/m^3)	20,00 cm
Gesamtaufbau	47,5 cm

DE06 Decke Stiegenhaus / Gang über Tiefgarage

Bodenbelag	1,00 cm
Estrich	7,00 cm
Folie	0,01 cm
Trittschalldämmung	3,00 cm
Folie	0,01 cm
Schüttdämmstoff	4,00 cm
Stahlbetondecke lt. Statik (2400kg/m^3)	20,00 cm
Dampfbremse	0,01 cm
Mineralischer Klebe- und Armierungsmörtel	0,40 cm
Dämmung Steinwolle A2	16,00 cm
Gesamtaufbau	51,6 cm

DE07 Stiegenpodest

Bodenbelag	1,00 cm
Estrich	5,50 cm
Folie	0,02 cm
Trittschalldämmung	3,00 cm
Folie	0,02 cm
Schüttdämmstoff	3,50 cm
Stahlbetondecke lt. Statik (2400kg/m^3)	20,00 cm
Innenspachtelung	0,20 cm
Gesamtaufbau	33,2 cm

DE08 Betonstiege

Belag	1,50 cm
Betonfertigteile lt. Statik	18,00 cm

DE09 Regelgeschoßdecke Wohnung

Bodenbelag	1,00 cm
Heizestrich	7,00 cm
Folie	0,01 cm
Trittschalldämmung	3,00 cm
Folie	0,01 cm
Schüttdämmstoff	4,00 cm
Stahlbetondecke lt. Statik (2400kg/m^3)	20,00 cm
Innenspachtelung	0,20 cm
Gesamtaufbau	35,2 cm

DE10 Regelgeschoßdecke Stiegenhaus / Gang

Bodenbelag	1,00 cm
Estrich	7,00 cm
Folie	0,02 cm
Trittschalldämmung	3,00 cm
Folie	0,01 cm
Schüttdämmstoff	4,00 cm
Stahlbetondecke lt. Statik (2400kg/m^3)	20,00 cm
Innenspachtelung	0,20 cm
Gesamtaufbau	35,2 cm

DE11 Decke Wohnung über Außenluft

Bodenbelag	1,00 cm
Heitestrich	7,00 cm
Folie	0,01 cm
Trittschalldämmung	3,00 cm
Folie	0,01 cm
Schüttdämmstoff	4,00 cm
Stahlbetondecke lt. Statik (2400kg/m^3)	20,00 cm
Dampfbremse	0,01 cm
Mineralischer Klebe- und Armierungsmörtel	0,40 cm
Dämmung Steinwolle A2	16,00 cm
Mineralischer Klebe- und Armierungsmörtel	0,20 cm
Glasarmierung	0,10 cm
Grundbeschichtung	0,10 cm
Außenputz	0,20 cm
Gesamtaufbau	52,0 cm

DE12 Decke Wohnung über unbeheizte Räume

Bodenbelag	1,00 cm
Heitestrich	7,00 cm
Folie	0,01 cm
Trittschalldämmung	3,00 cm
Folie	0,01 cm
Schüttdämmstoff	4,00 cm
Stahlbetondecke lt. Statik (2400kg/m^3)	20,00 cm
Dampfbremse	0,01 cm
Mineralischer Klebe- und Armierungsmörtel	0,40 cm
Dämmung	16,00 cm
Innenspachtelung	0,20 cm
Gesamtaufbau	51,6 cm