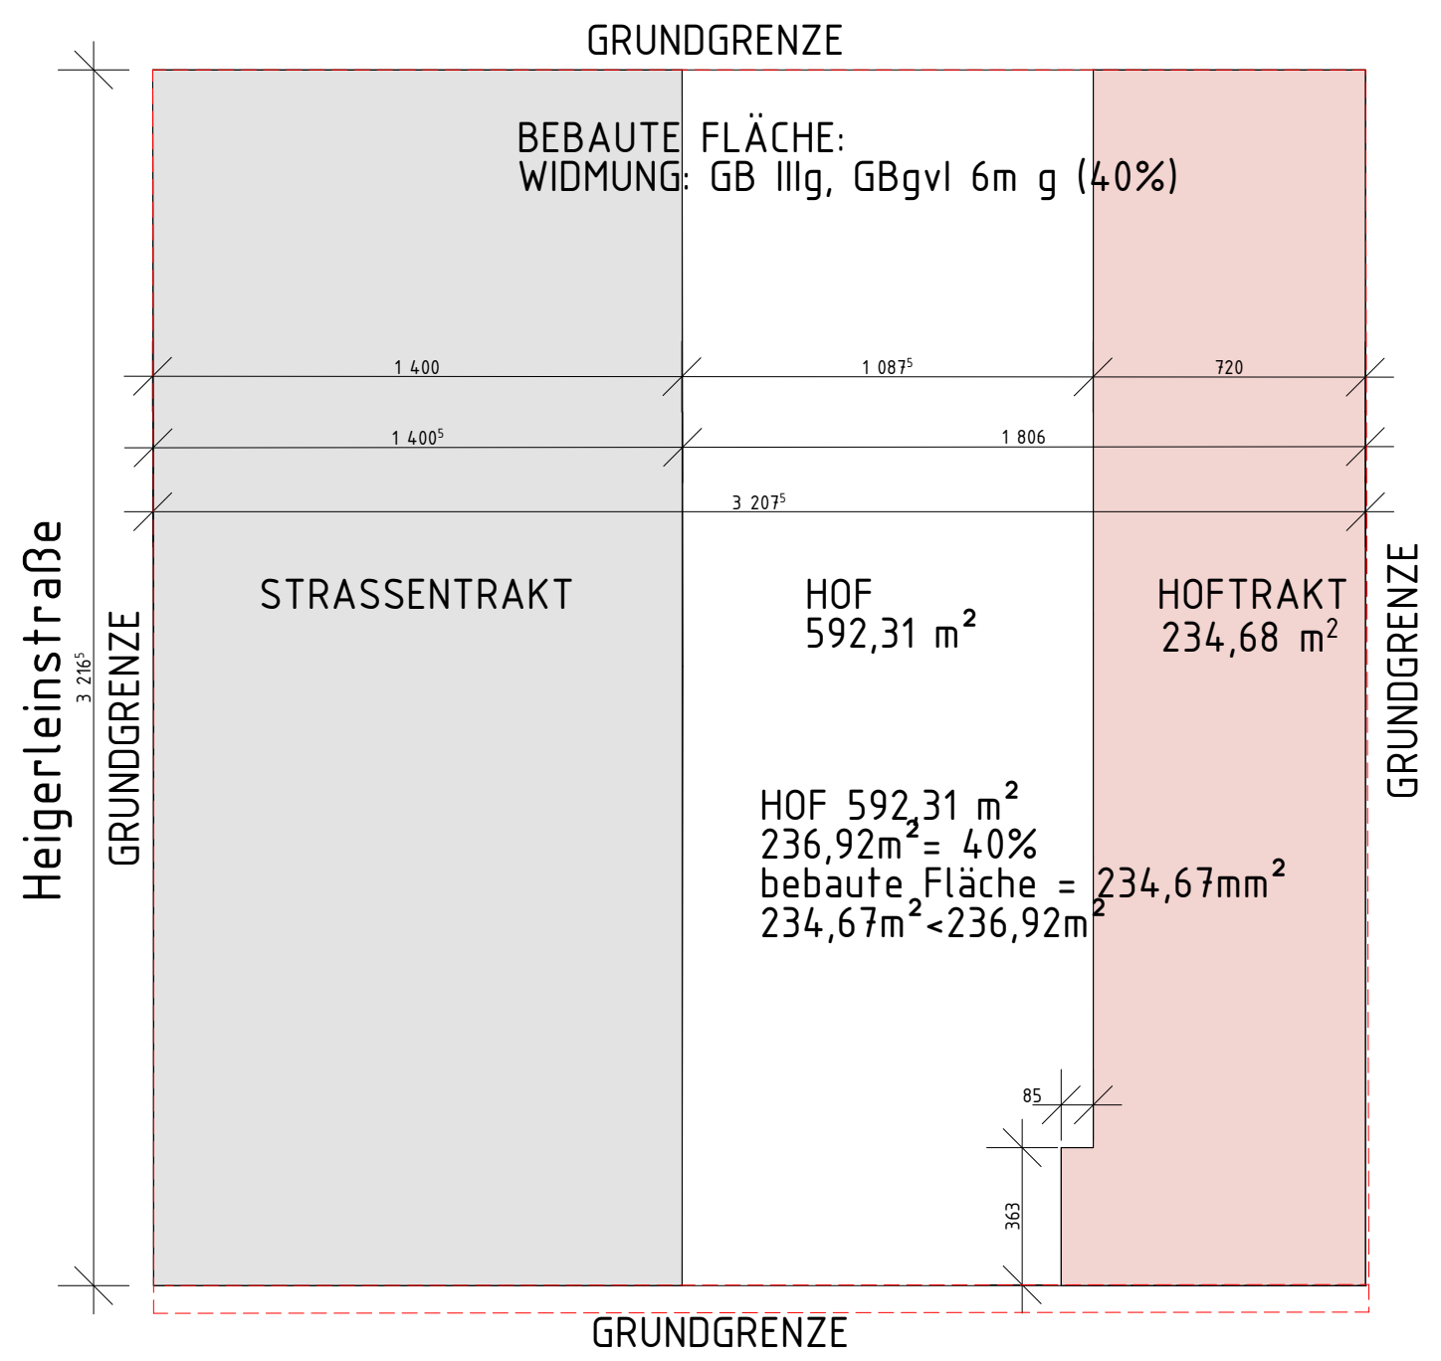
GRUNDGRENZE
BEBAUTE FLÄCHE:
WIDMUNG: GB IIIg, GBgvl 6m g (40%)
1 400
1 087⁵
720
1 400⁵
1 806
3 207⁵
Heigerleinstraße
3 216⁵
GRUNDGRENZE
STRASSENTRAKT
HOF
592,31 m²
HOFTRAKT
234,68 m²
GRUNDGRENZE
HOF 592,31 m²
236,92m² = 40%
bebaute Fläche = 234,67mm²
234,67m²<236,92m²
85
363
GRUNDGRENZE

STELLPLATZNACHWEIS: 2197,5m² WOHNNUTZFLÄCHE = 22 STELLPLÄTZE
5 REIHENHÄUSER = 1 STELLPLATZ
INSGESAMT 23 STELLPLÄTZE
22 STELLPLÄTZE VORHANDEN

FAHRRAD-STELLPLATZNACHWEIS: 2197,5m² WOHNNUTZFLÄCHE / 30m²
min. 73 FAHRRADABSTELLPLÄTZE

BETTENANZAHL: INSGESAMT 5 REIHENHÄUSER (BEHERBERGUNGSBETRIEB)
2 BETTEN PRO BETRIEBSEINHEIT
INSGESAMT 10 BETTEN

LEGENDE:

▨	BESTAND	—	SCHMUTZWASSER	UZ	UNTERZUG
▨	ABBRUCH	—	REGENWASSER	ÜZ	ÜBERZUG
🟥	NEUBAU	—	WASSER	AR	ABFALLROHR
		—	HEIZUNG	RR	REGENROHR
🟩	STAHLBETON	—	STROM	RSK	REGENSINKKASTEN
🟩	UNBEWEHRTER BETON	—	GAS	PH	PARAPETHÖHE
🟥	MAUERWERK	—	FERNWÄRME	STUK	STURZUNTERKANTE
▨	HOLZ			DL	DURCHGANGSLICHTE
▨	DÄMMUNG (HART)	DFF	DACHFLÄCHENFENSTER	OK	OBERKANTE
▨	DÄMMUNG (WEICH)	LK	LICHTKUPPEL	UK	UNTERKANTE
▨	STAHL	VSG	VERBUND-SICHERKEITSGLAS	FOK	FUSSBODENOBERKANTE
▨	GLAS	ESG	EINSCHEIBEN-SICHERHEITSGLAS	WD	WANDDURCHBRUCH
▨	GIPSKARTON	BRE	BRANDRAUCHENTLÜFTUNG	DD	DECKENDURCHBRUCH

- LÜFTUNGEN DURCH FREMDE BRANDABSCHNITTE EI90 UND A2 UMMANTELT
- RESTRÄUME IM DACHGESCHOSS EI60 VON INNEN 2x GKF
- WOHNUNGSEINGANGSTÜREN EI_2-30
- AUSWECHSLUNGEN REI90 UMMANTELT
- HEIZUNGSSYSTEM: WÄRMEPUMPE
- PHOTOVOLTAIKANLAGE IST AM FLACHDACH VORDERTRAKT AUFGESTÄNDERT
- ALLE AUSKRAGENDEN TEILE THERMISCH GETRENNT
- ALLE INNENLIEGENDEN BÄDER UND WC's LÜFTUNG ÜBER DACH
- FÜR JEDE WOHNUNG IST EIN EINLAGERUNGSRAUM VORHANDEN
- IN JEDER WOHNUNG IST EINE GEEIGNETE AUFSTELLMÖGLICHKEIT UND EIN ANSCHLUSS FÜR EINE WASCHMASCHINE UND EINE MASCHINELLE TROCKENEINRICHTUNG VORGESEHEN.
- NIEDERSCHLAGSWÄSSER UND FÄKALWÄSSER WERDEN IN DEN ÖFFENTLICHEN KANAL GELEITET
- STIEGEN UND GÄNGE KUNSTSTEINBELAG, BELAG MÜLLRAUM UND GARAGE MIND. Bfl
- GEMÄSS OIB RICHTLINIE 2, ABSATZ 3, PUNKT 11 - UNVERNETZTE RAUCHWARNMELDER IN ALLEN AUFENTHALTSRÄUMEN (AUSGEN. KÜCHEN, BEI WOHNKÜ. NICHT IM KOCHBEREICH) SOWIE BEI GÄNGEN ÜBER DIE FLUCHTWEGE VON AUFENTHALTSR. FÜHREN
- SCHADENSFOLGEKLASSE CC2 nach ÖNORM EN 1090-2 Tab. B3
- NÄCHSTE HYDRANT BIS GRUNDGRENZE: ca.115m<150m
- ALLE INNENLIEGENDE RÄUME SIND MECHANISCH ENTLÜFTET
- SCHÄCHTE WERDEN GEMÄSS WIENER INSTALLATIONSRICHTLINIE SCHACHTTYP A AUSGEFÜHRT
- AUFZUGSSCHÄCHTE SIND MIT MIND 2,5% DES SCHACHTQUERSCHNITTS ENTLÜFTET.
- FLUCHTWEGS UND ORIENTIERUNGSBELEUCHTUNG GEMÄß DEN BESTIMMUNGEN DER TRVB 102E
- DRUCKBELÜFTUNGSANLAGE GEMÄSS DEN BESTIMMUNGEN DER TRVB 112S (AUFENTHALTSKONZEPT)

± 0.00 ENTSPRICHT 70,12M ÜBER WIENER NULL
± 0.00 ENTSPRICHT 70,20M ÜBER WIENER NULL

DOLL FUSS ARCHITEKT

AUSWECHSLUNGSPLAN

PLANINHALT:
SCHNITTE, ANSICHTEN

Parie A B C D E F G H I J K
Nr. 1 2 3 4 5 6 7

BAUVORHABEN:

1160 Wien, Heigerleinstrasse 20 und 22

ABBRUCH BESTANDSGEBÄUDE UND NEUBAU EINES MEHRFAMILIENWOHNHAUSES MIT 44 WOHNUNGEN UND 5 REIHENHÄUSERN (BEHERBERGUNGSBETRIEB MIT 5 BETRIEBSEINHEITEN UND 10 BETTEN)
Heigerleinstraße 20-22
1160 Wien-Ottakring

GRUNDSTÜCKSNUMMER	801/39, 801/40
EINLAGEZAHL	2240
KATASTRALGEMEINDE	01405 Ottakring

GRUNDEIGENTÜMER/BAUWERBER

~~Simony Immobilien GmbH&Co Phi KG~~
~~Simonygasse 12~~
~~1180 Wien~~

HEIGE20 Projekt GmbH & Co KG
Sterngasse 11/4B
1010 Wien

BEHÖRDE

BAUFÜHRER
Auböck Bau GmbH
Drosselstraße 36
A-4470 Enns

PLANVERFASSER

ARCHITEKT
DIPL.ING. GERHARD DOLLFUSS
STAATLICH BEFUGTER U. BEEIDETER ZIVILTECHNIKER
3240 MANK, BAHNHOFSTRASSE 4/4
0676/9490946 · office@dollfuss.eu

PLANINHALT	SCHNITTE, ANSICHTEN
MAßSTAB	1:100,1:200
PLANDATUM	02.10.2020 DRUCKDATUM 15.12.2020
PLANNUMMER	A2017-04-201
PROJEKT	1160 Wien, Heigerleinstrasse 20 und 22
CAD-FILE	A2017-04_Heigerlein_ASW_20200102.pln

DIESER PLAN IST GEISTIGES EIGENTUM DES PLANVERFASSERS UND DARF NUR MIT DESSEN ZUSTIMMUNG WEITERGEGEBEN UND VERVIELFÄLTIGT WERDEN !
DAS VORLIEGENDE PLANDOKUMENT DIENT ALS GRUNDLAGE FÜR DIE BEHÖRDLICHE GENEHMIGUNG lt. WRBO UND STELLT KEINEN AUSFÜHRUNGSPLAN DAR!

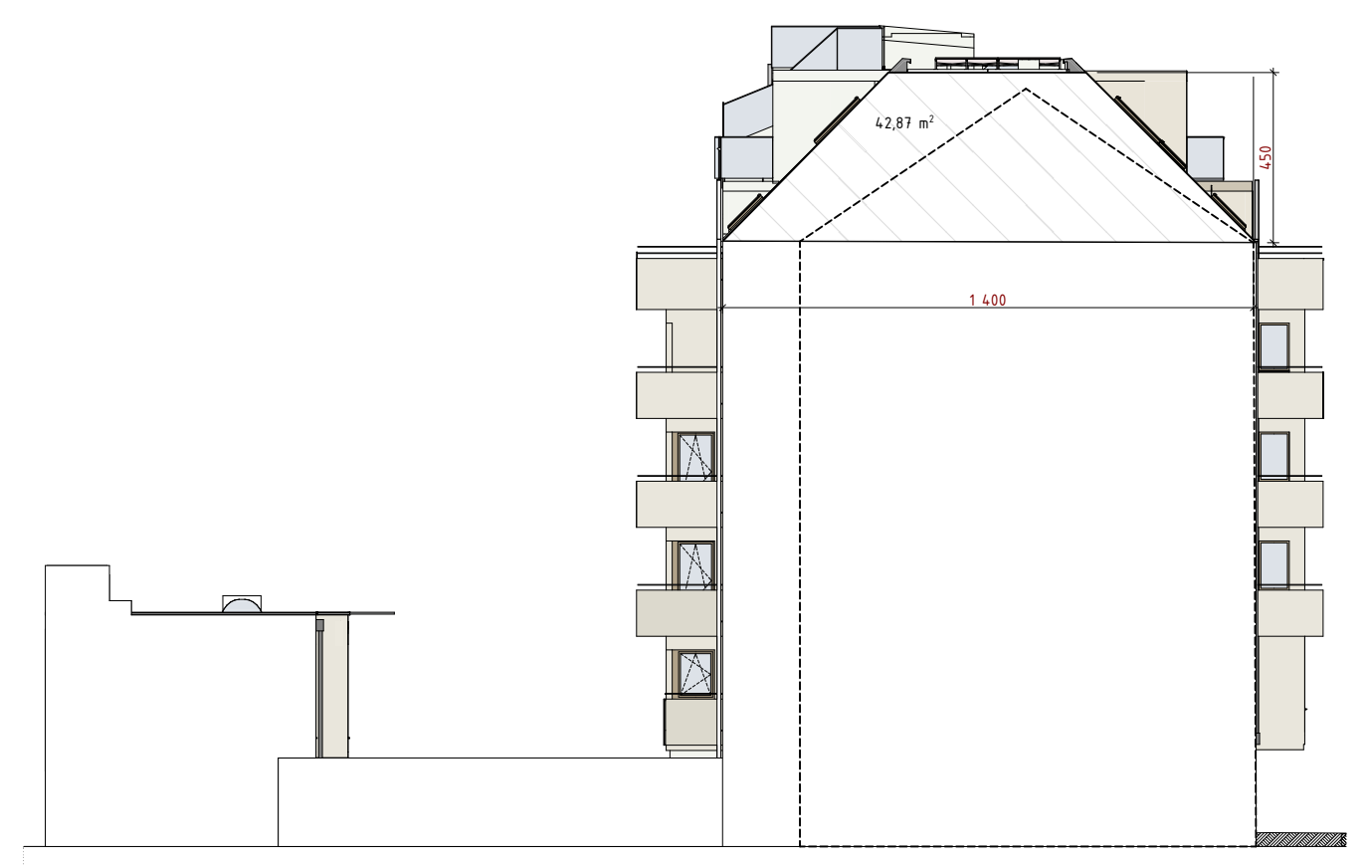

ANSICHT 1:200
GIEBELFLÄCHE

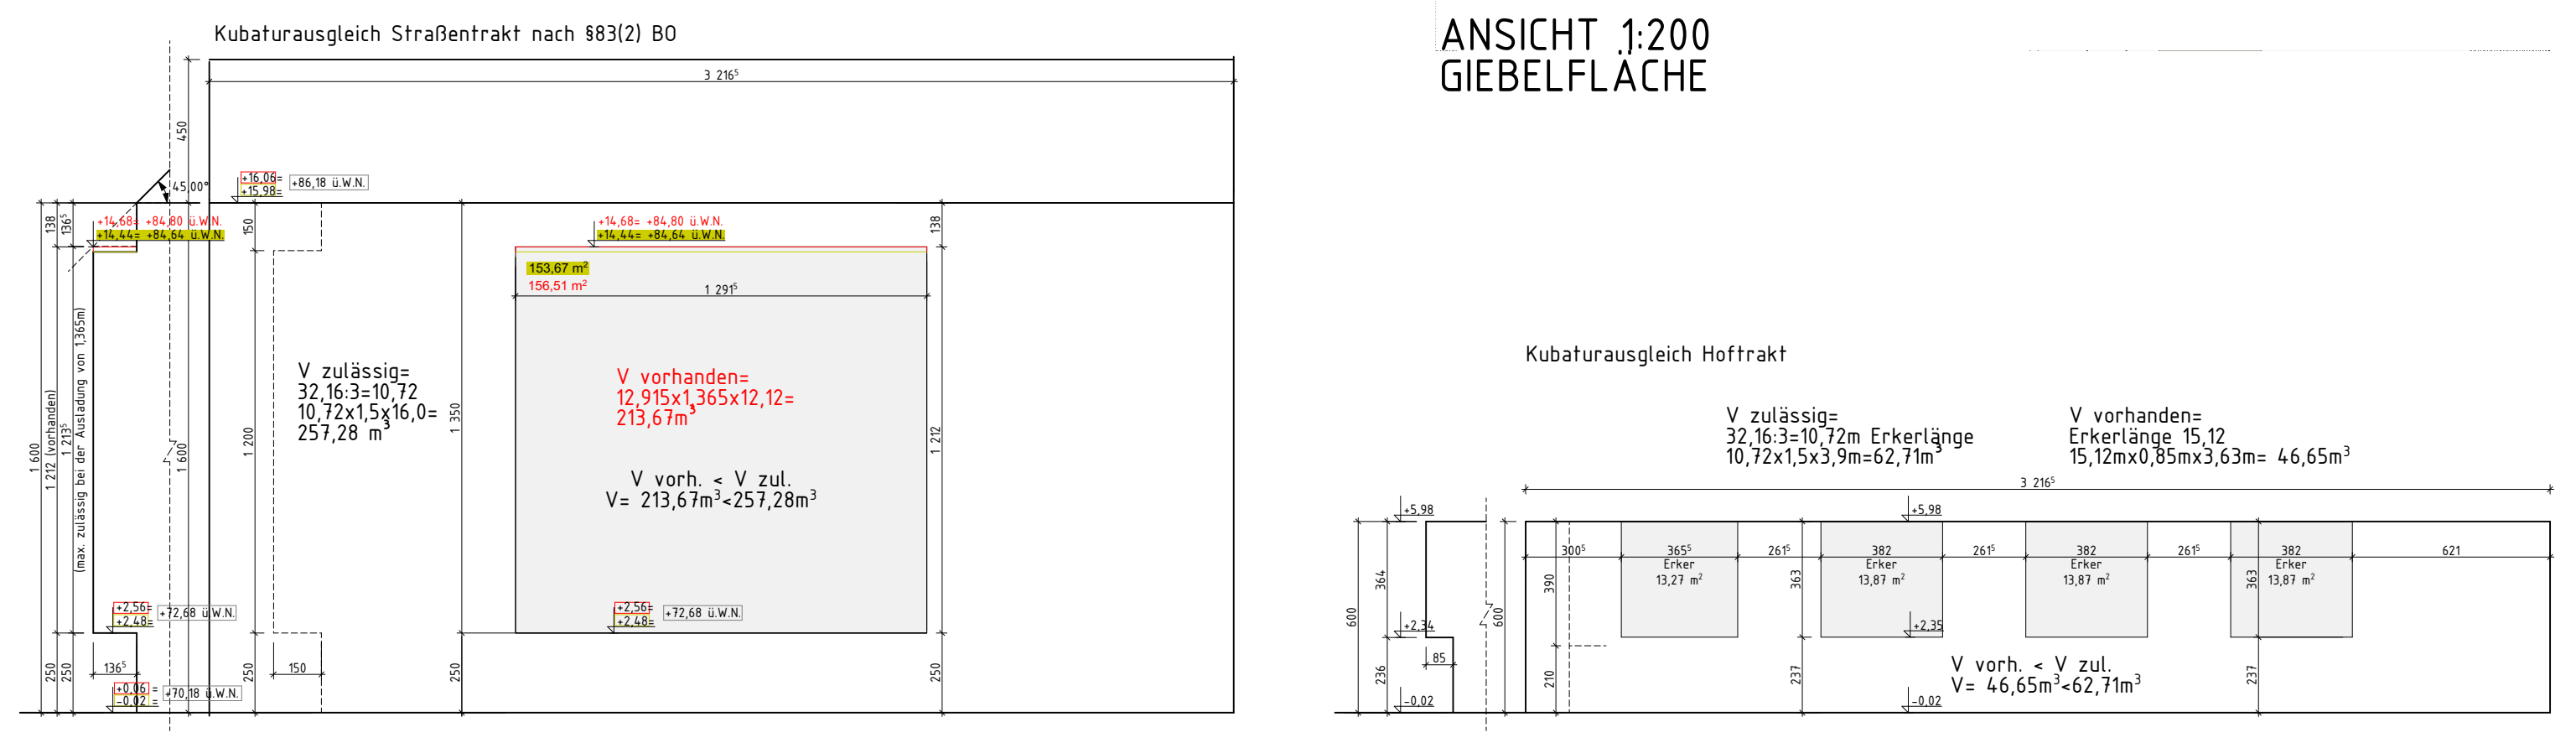
Kubaturausgleich Straßentrakt nach §83(2) BO
3 216⁵
V zulässig=
32,16:3=10,72
10,72x1,5x16,0=
257,28 m³
V vorhanden=
12,915x1,365x12,12=
213,67m³
V vorh. < V zul.
V= 213,67m³<257,28m³
153,67 m²
156,51 m²
1 291⁵
+14,68= +84,80 ü.W.N.
+14,44= +84,64 ü.W.N.
+16,06=
+15,98=
+86,18 ü.W.N.
+2,56=
+2,48=
+72,68 ü.W.N.
+0,06=
-0,02=
+70,18 ü.W.N.
(max. zulässig bei der Ausladung von 1,365m)
Kubaturausgleich Hoftrakt
V zulässig=
32,16:3=10,72m Erkerlänge
10,72x1,5x3,9m=62,71m³
V vorhanden=
Erkerlänge 15,12
15,12mx0,85mx3,63m= 46,65m³
3 216⁵
Erker 13,27 m²
Erker 13,87 m²
Erker 13,87 m²
Erker 13,87 m²
V vorh. < V zul.
V= 46,65m³<62,71m³

KUBATURAUSGLEICH

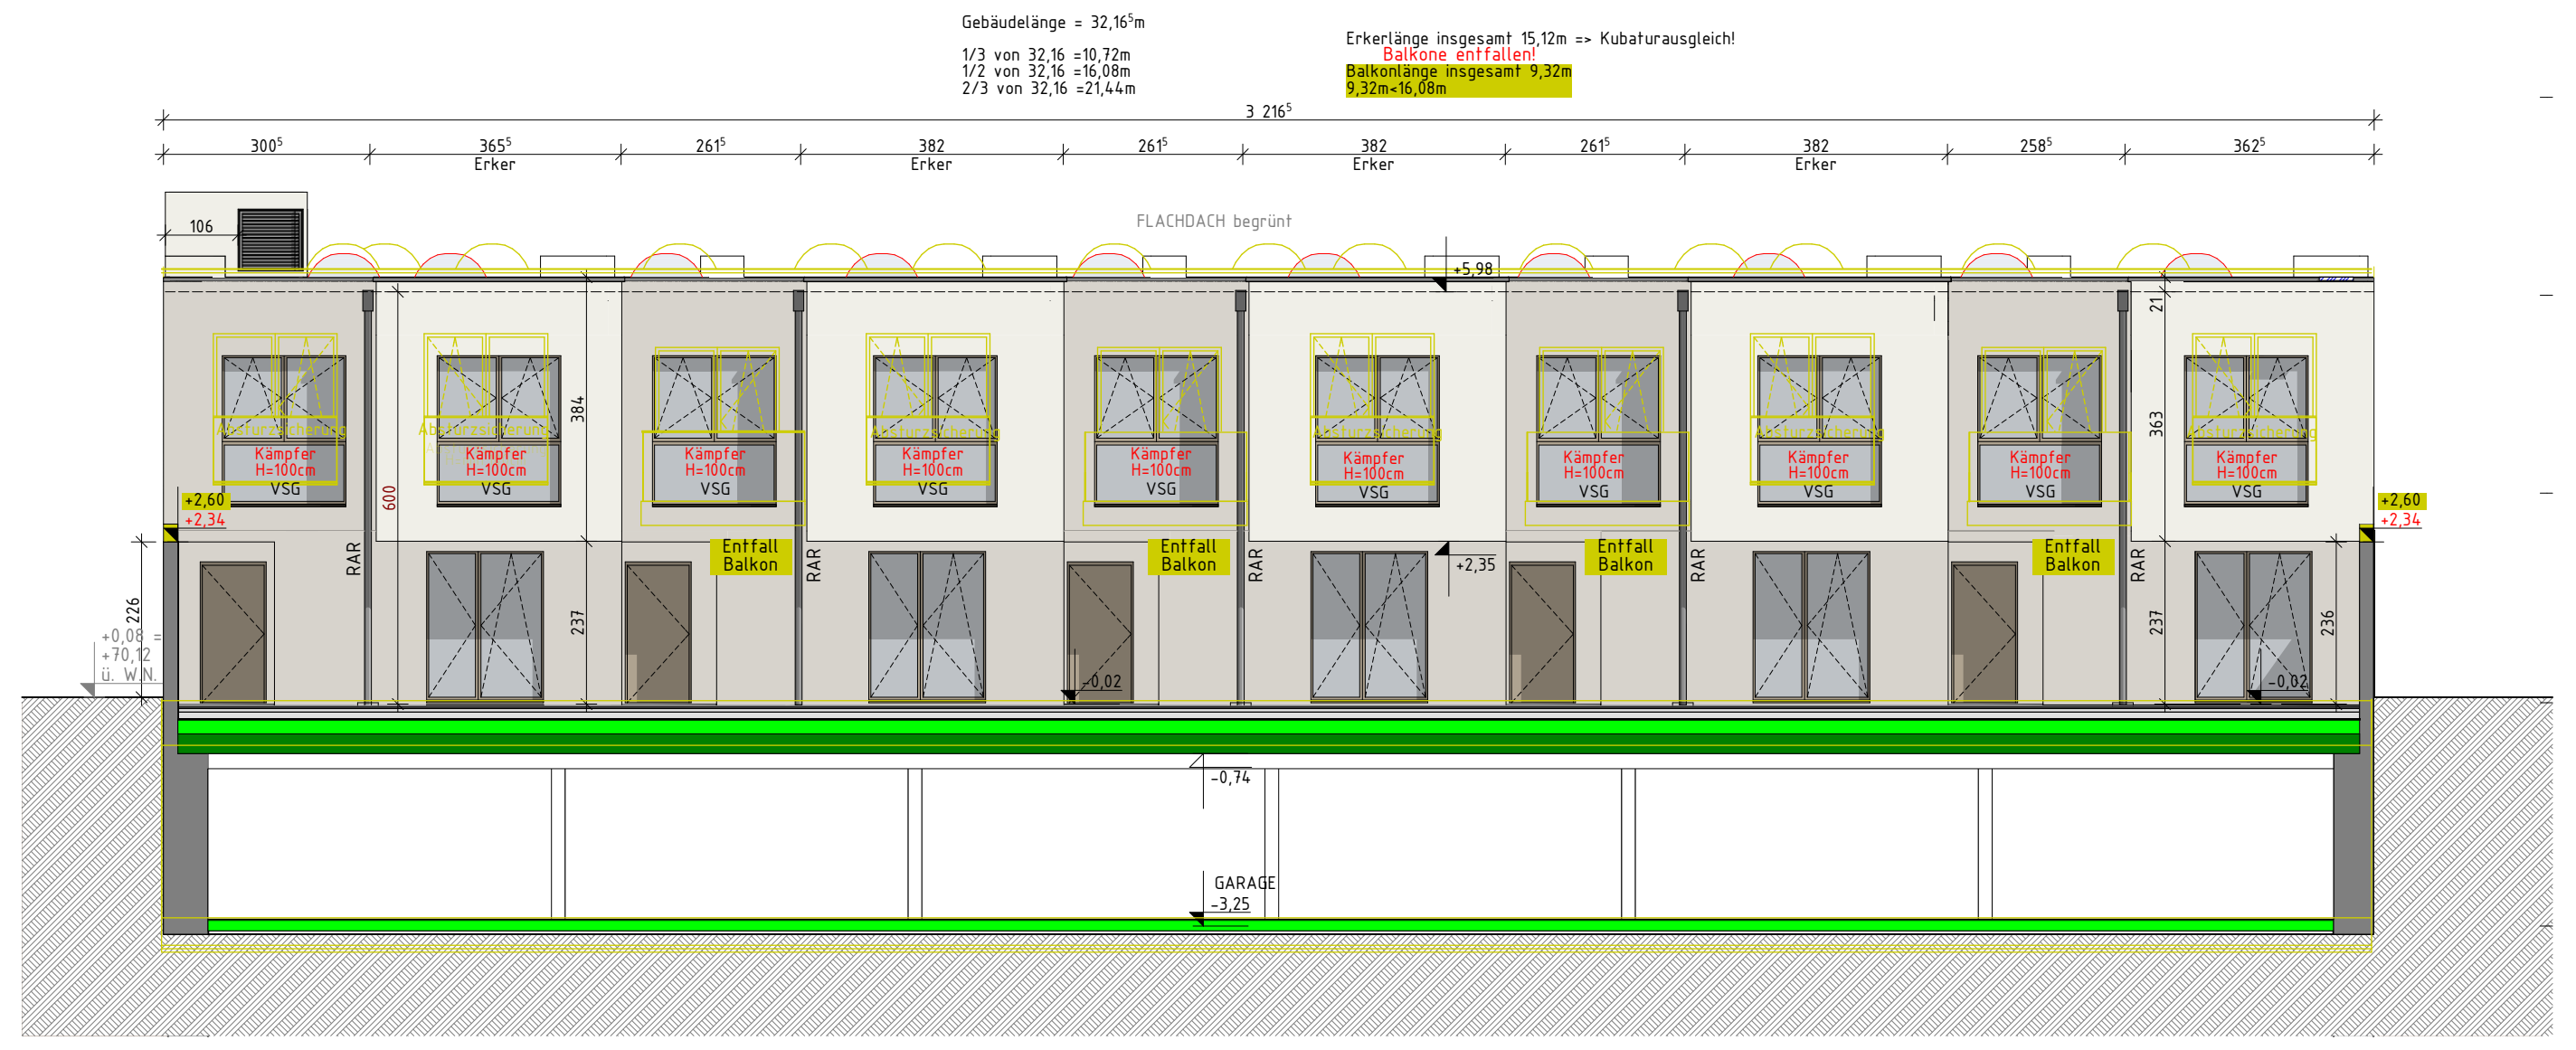
Gebäudelänge = 32,16⁵m
1/3 von 32,16 =10,72m
1/2 von 32,16 =16,08m
2/3 von 32,16 =21,44m
Erkerlänge insgesamt 15,12m => Kubaturausgleich!
Balkone entfallen!
Balkonlänge insgesamt 9,32m
9,32m<16,08m
3 216⁵
382 Erker
261⁵
FLACHDACH begrünt
+5,98

HOFTRAKT. WESTANSICHT

VISUALISIERUNGEN DIENEN LEDIGLICH ZUR BESSEREN DARSTELLUNG DES ENTWURFS UND SIND FÜR DIE EINREICHUNG NICHT RELEVANT:

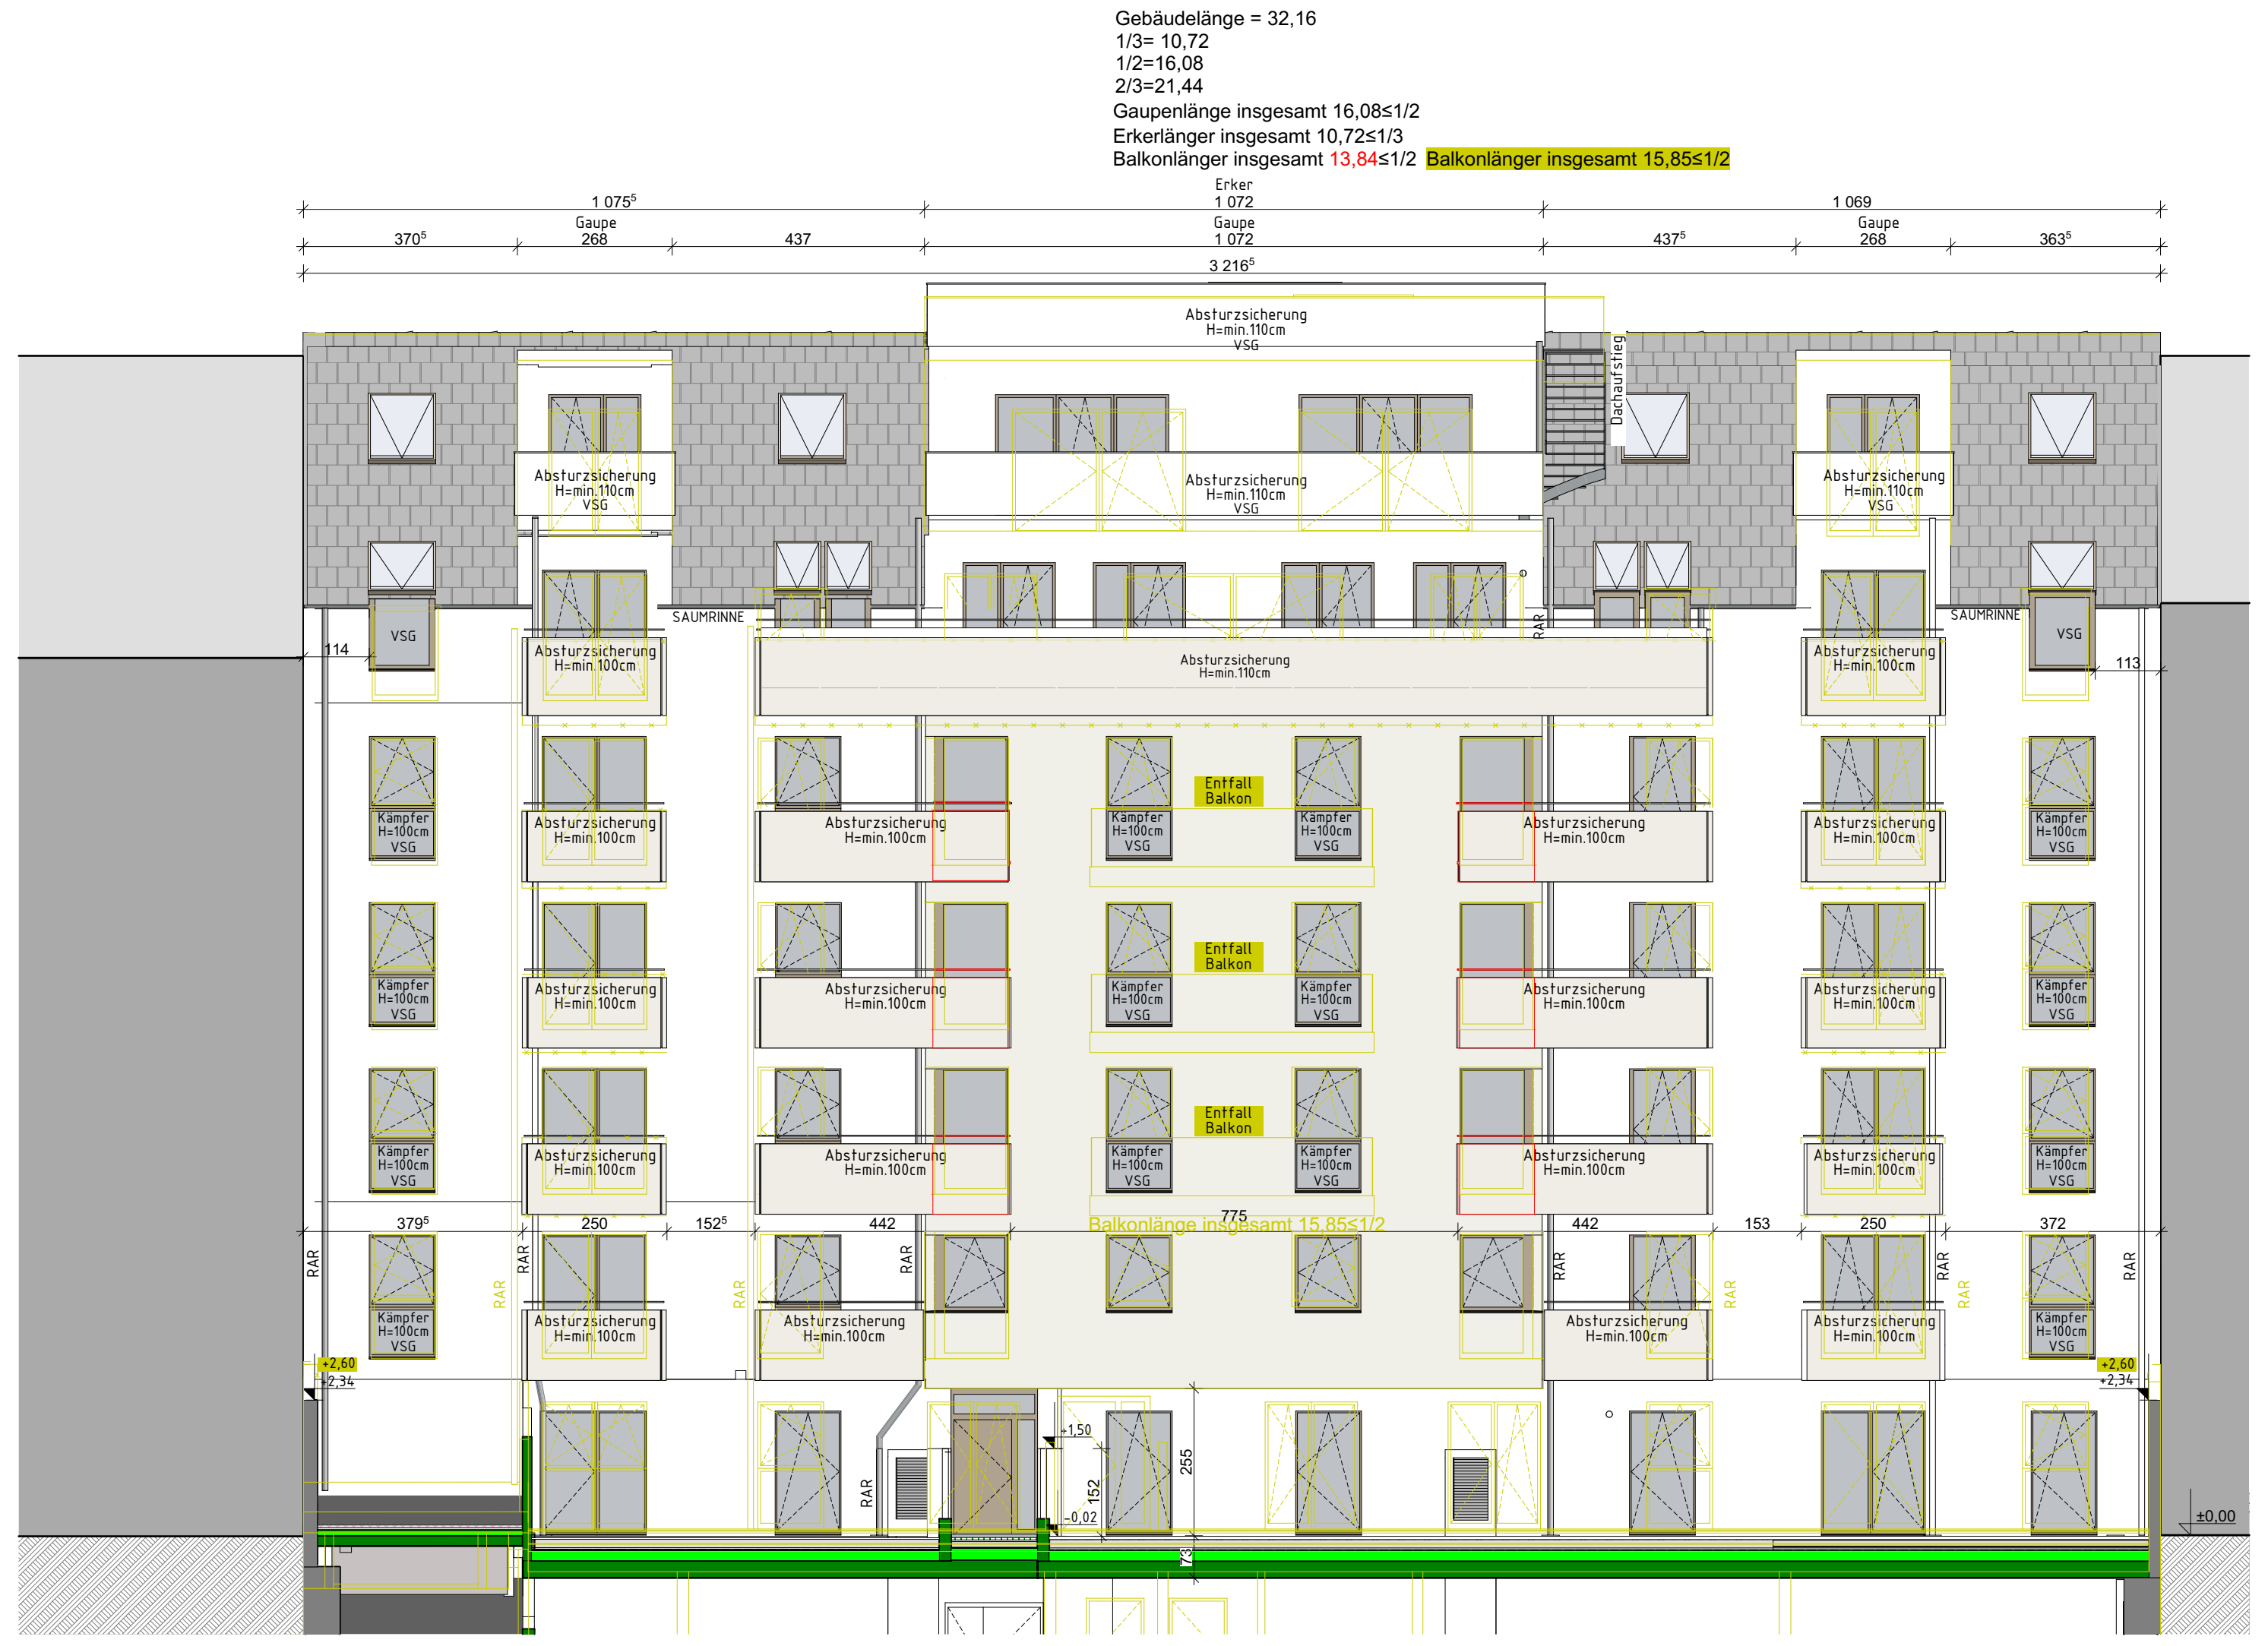
Gebäudelänge = 32,16
1/3= 10,72
1/2=16,08
2/3=21,44
Gaupenlänge insgesamt 16,08≤1/2
Erkerlänger insgesamt 10,72≤1/3
Balkonlänger insgesamt 13,84≤1/2
Balkonlänger insgesamt 15,85≤1/2
Erker
1 072
Gaupe
1 072
3 216⁵
437⁵
1 069
Gaupe
268
Absturzsicherung
H=min.110cm
VSG
Dachaufstieg

STRASSENTRAKT. OSTANSICHT

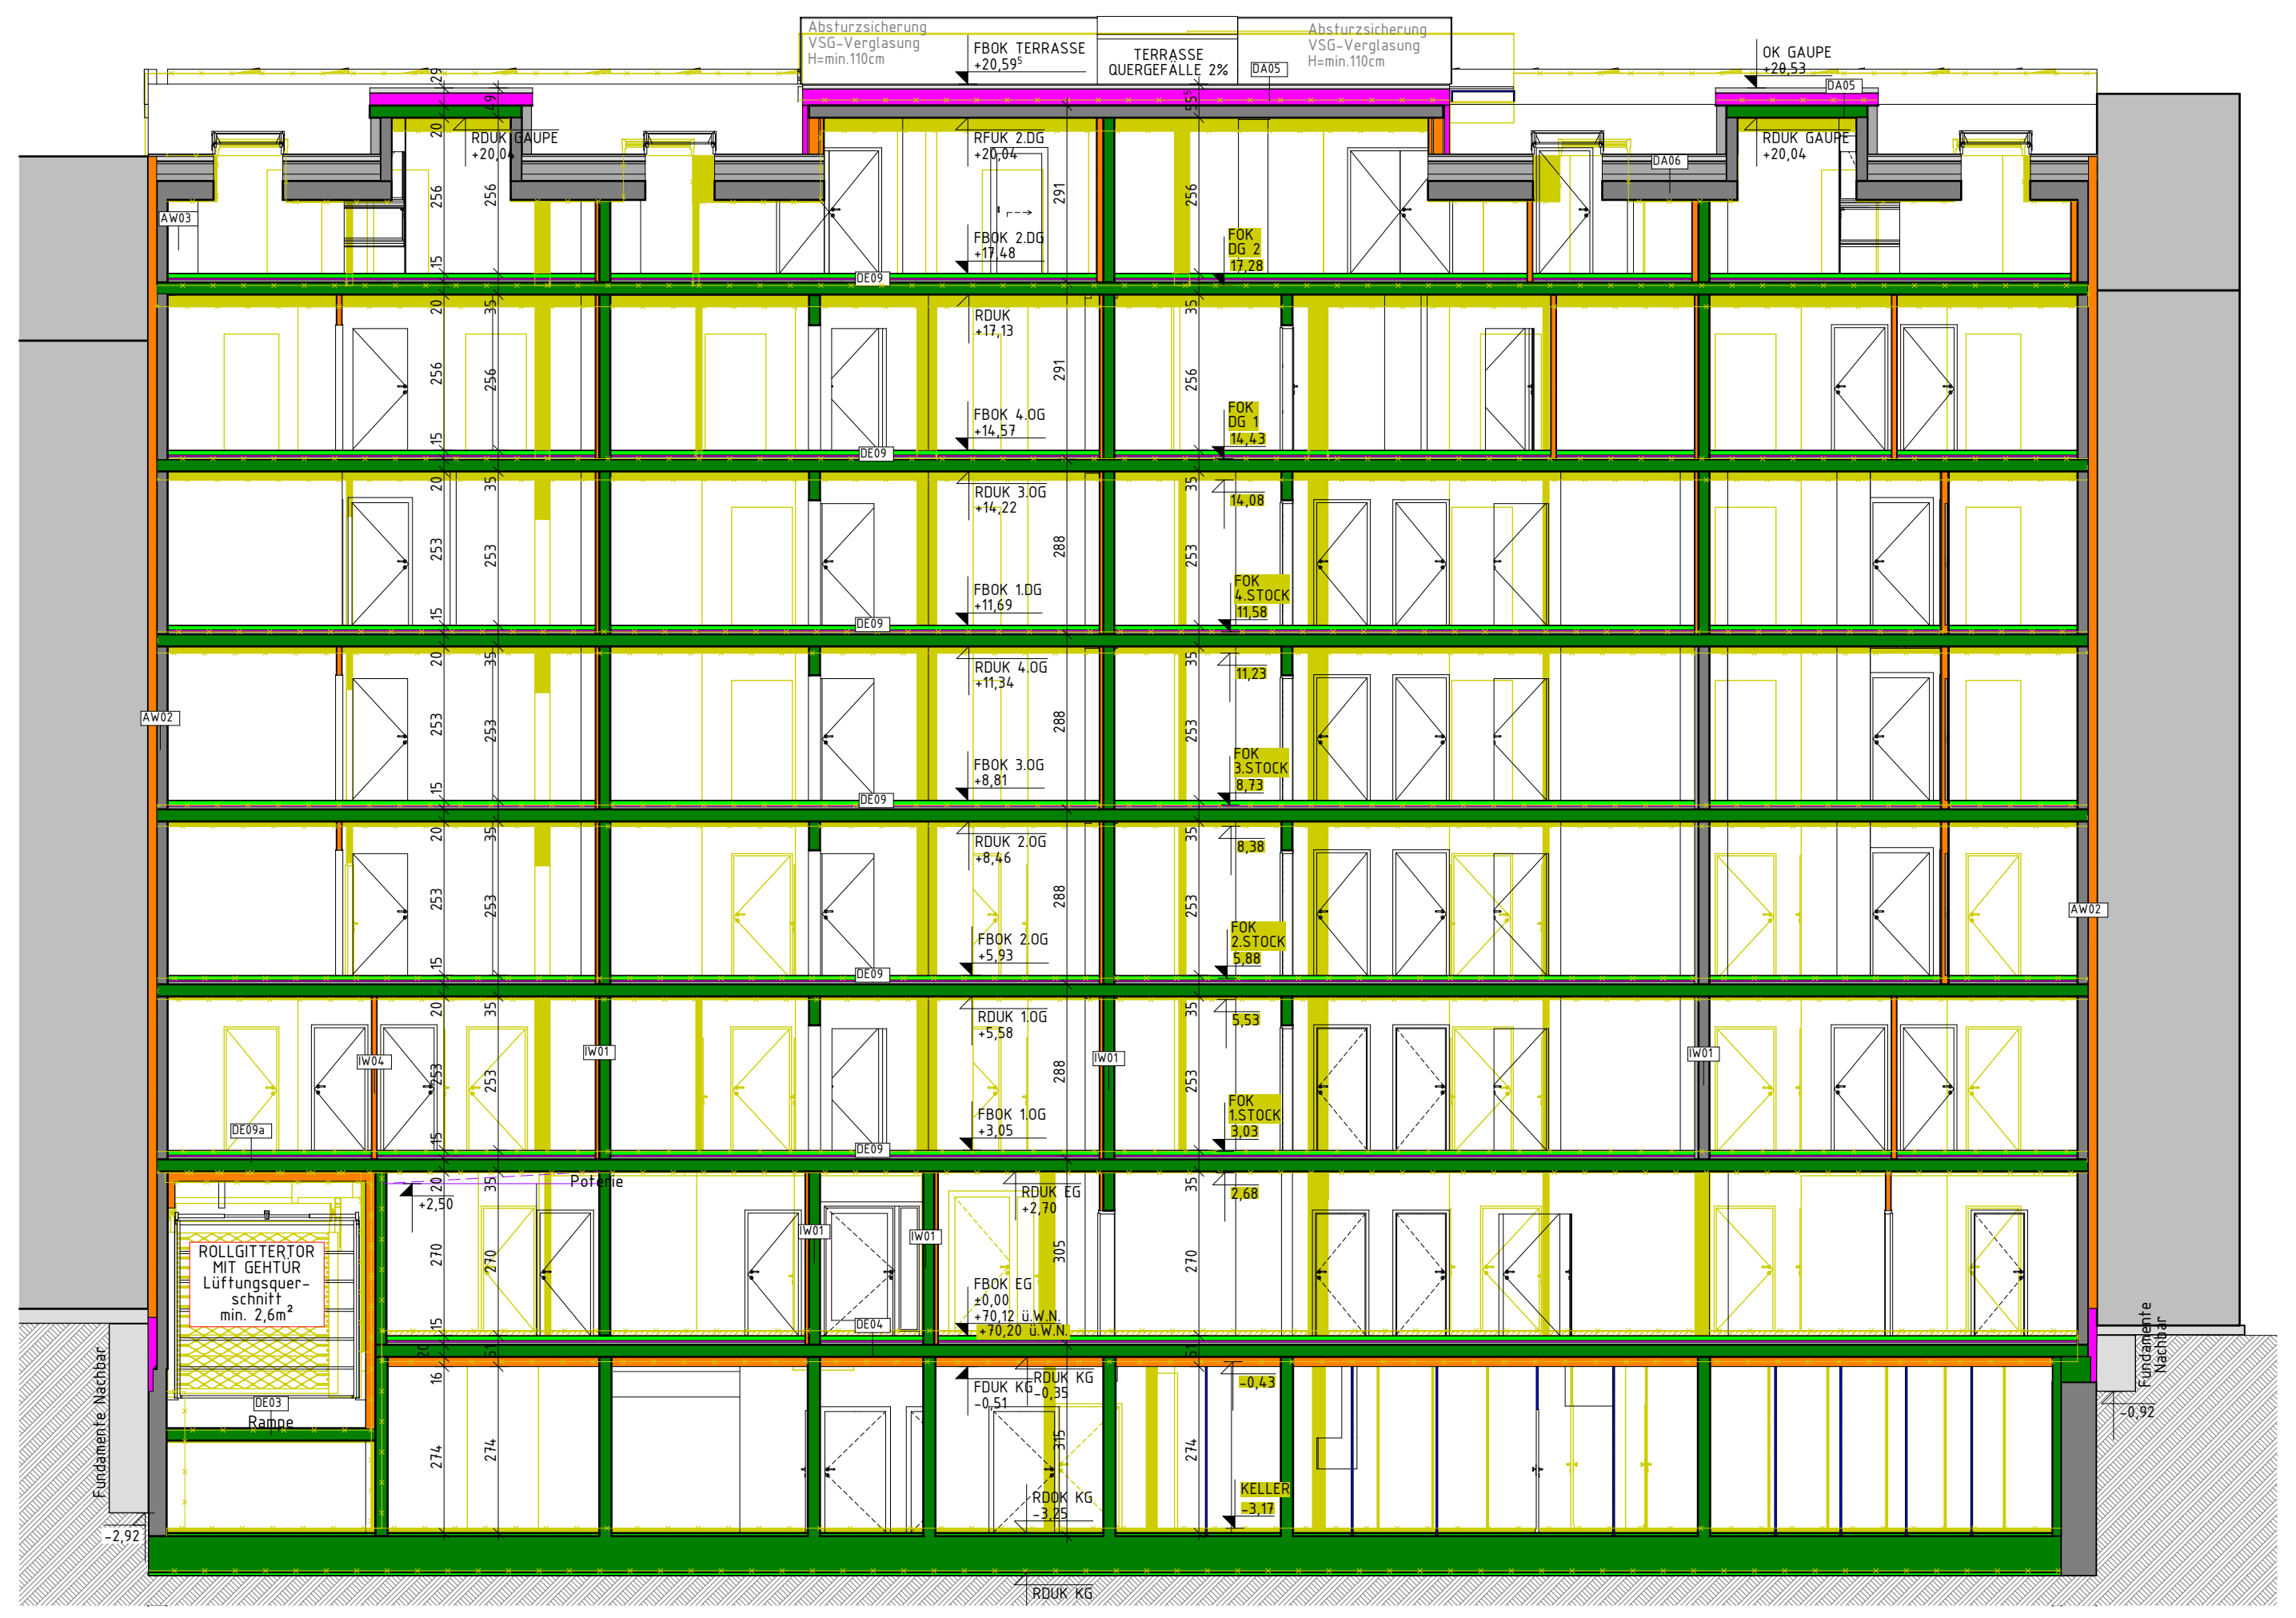

SCHNITT 1-1

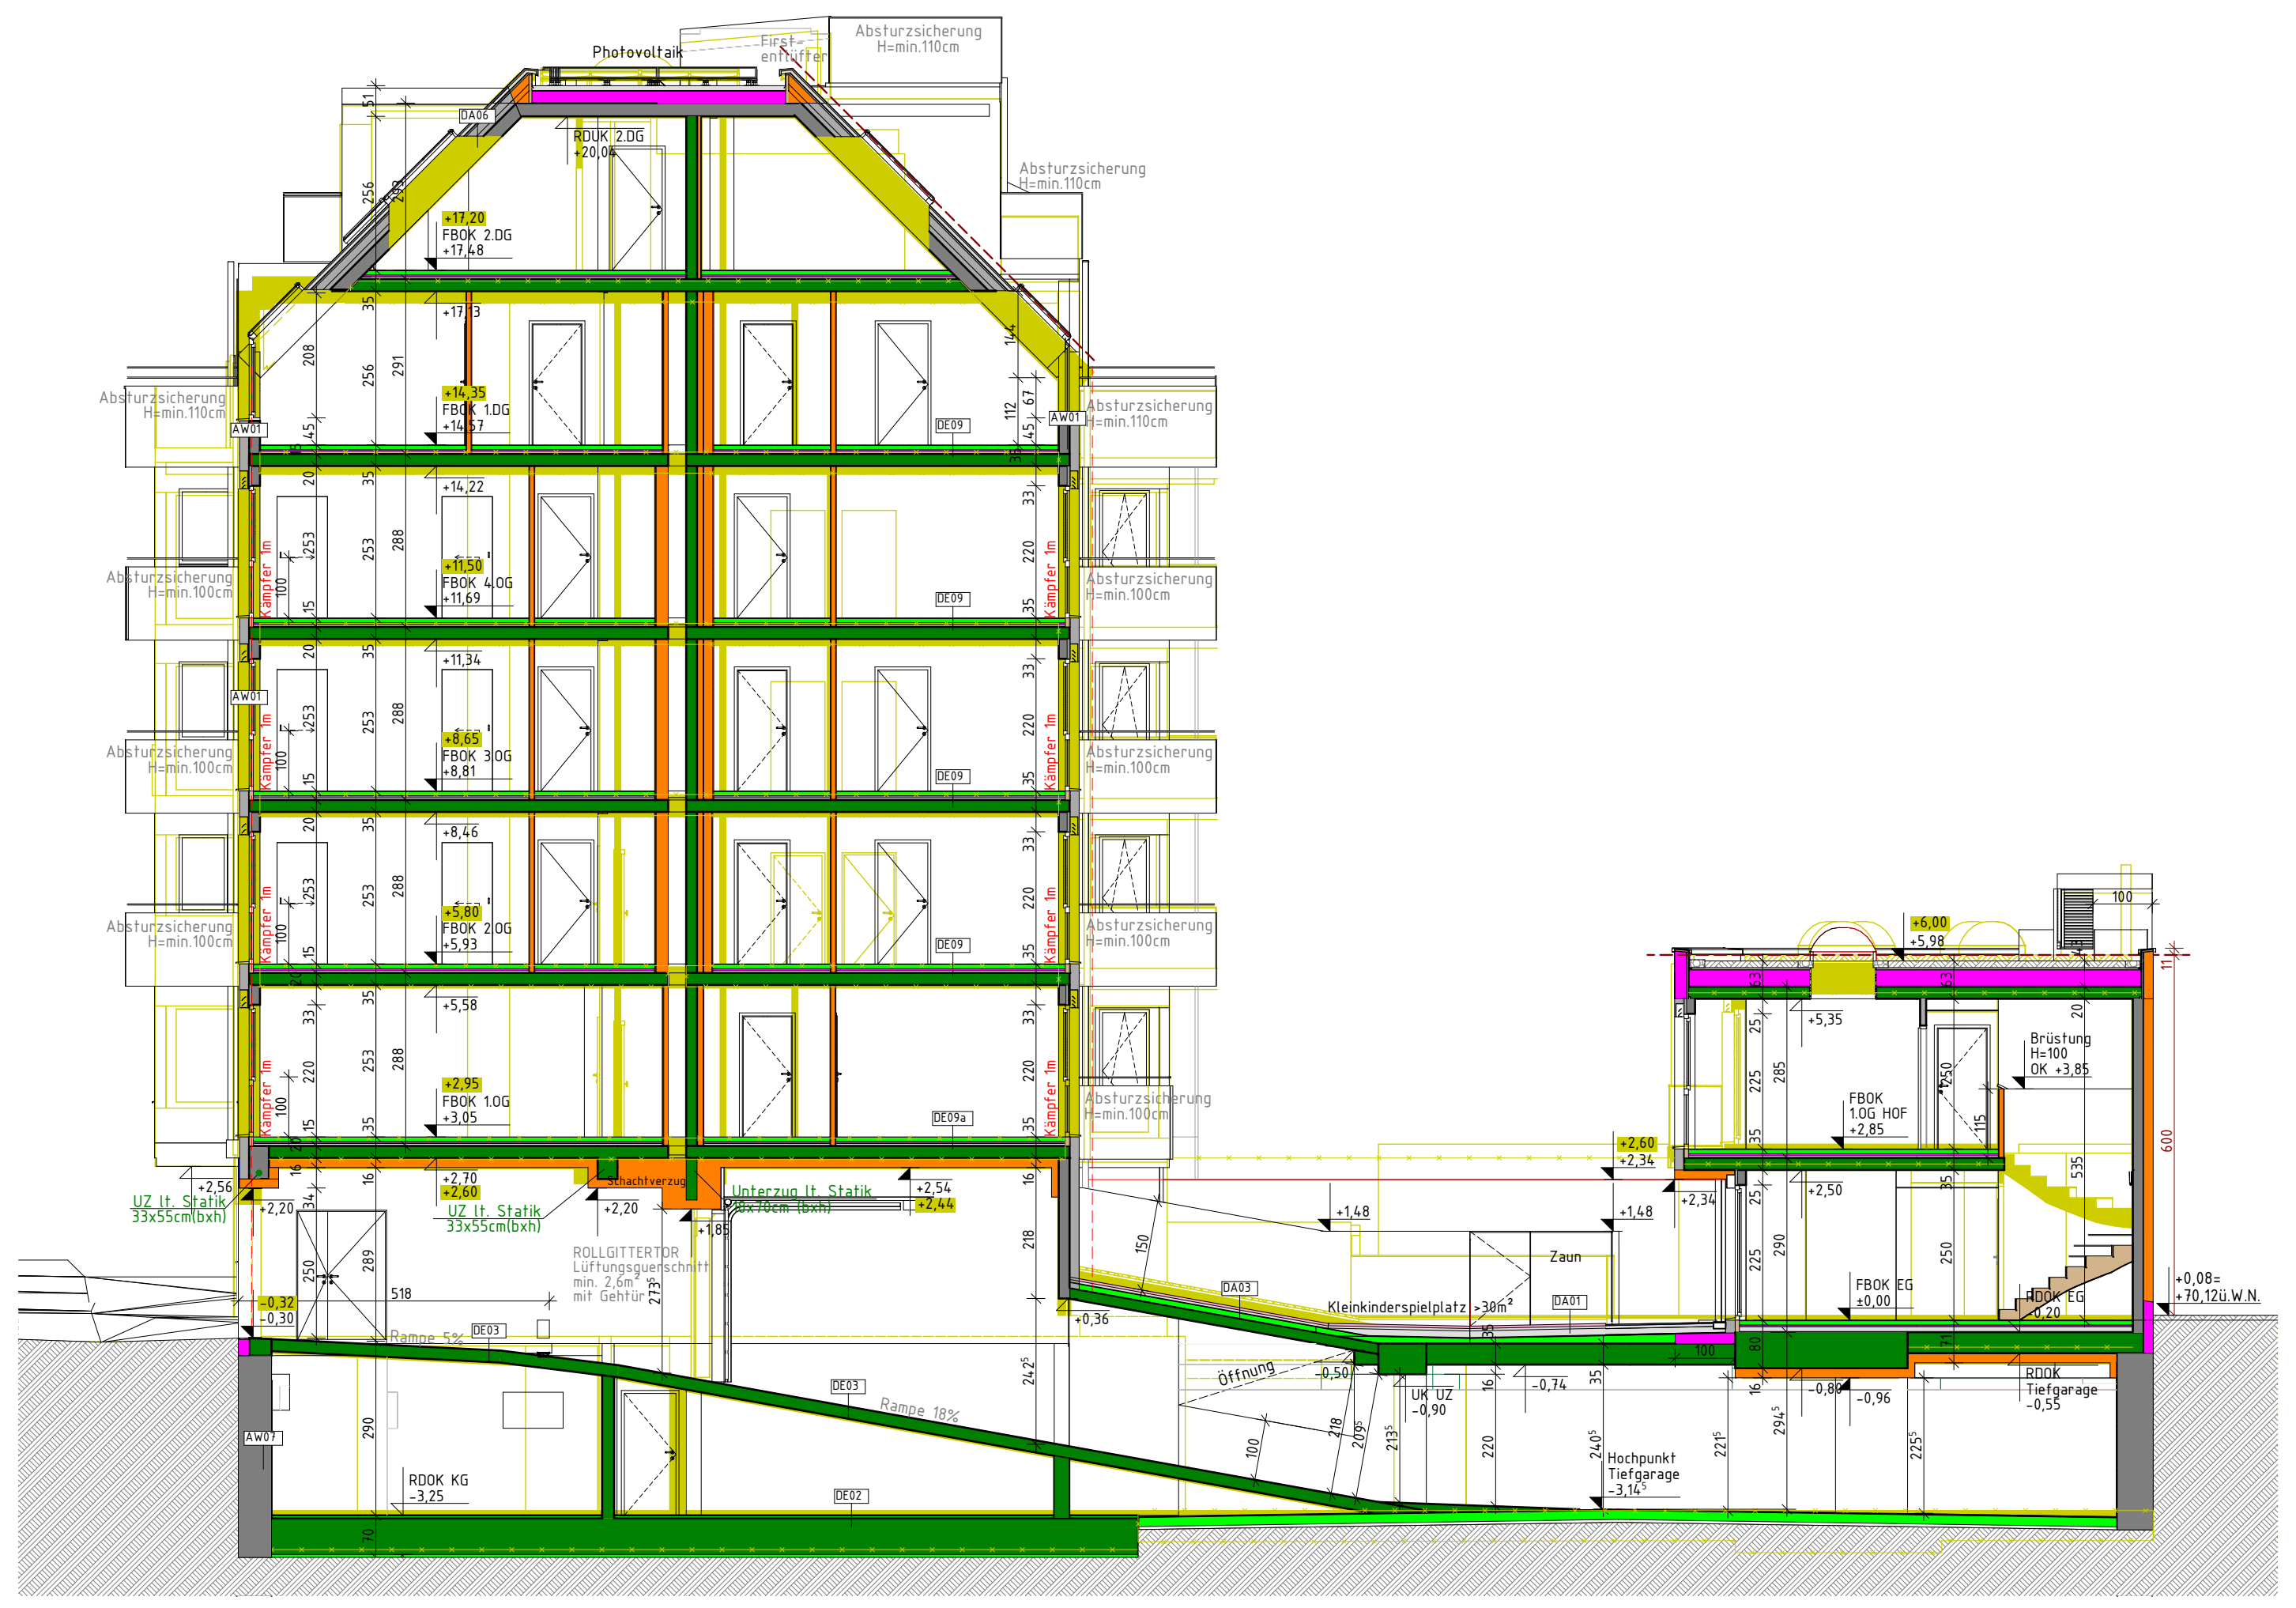

SCHNITT B-B

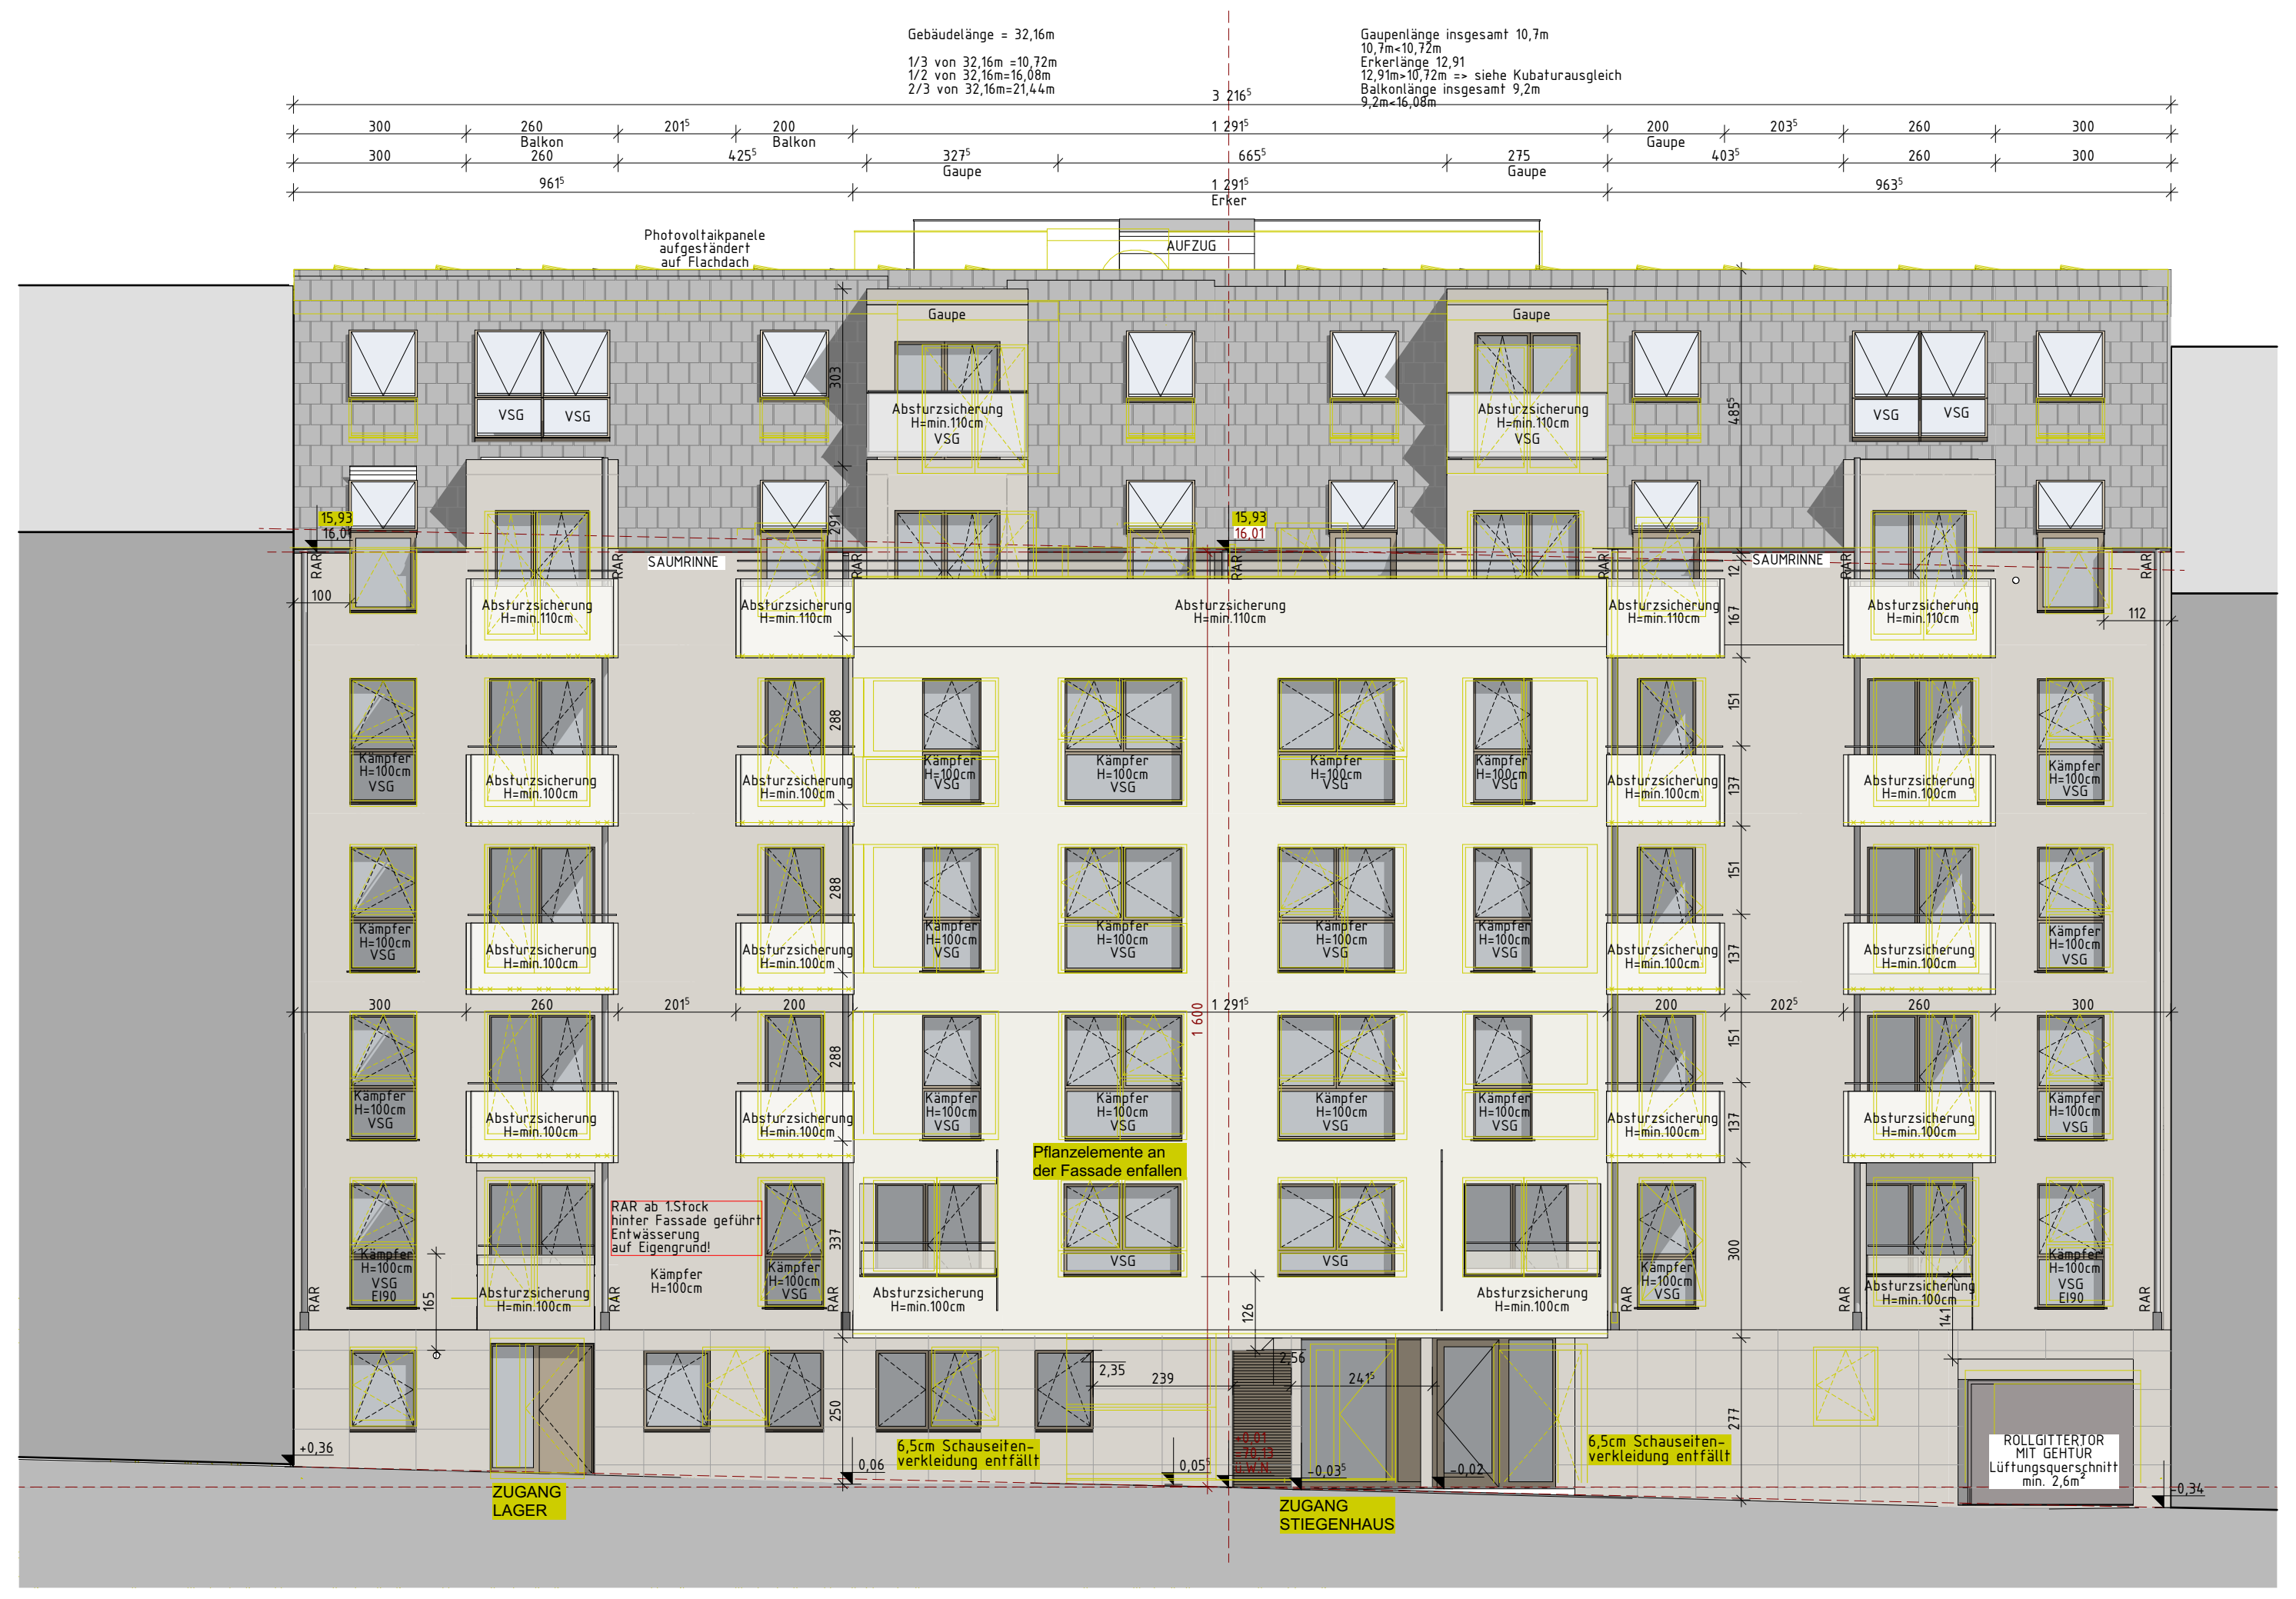
Gebäudelänge = 32,16m
1/3 von 32,16m =10,72m
1/2 von 32,16m=16,08m
2/3 von 32,16m=21,44m
Gaupenlänge insgesamt 10,7m
10,7m<10,72m
Erkerlänge 12,91
12,91m>10,72m => siehe Kubaturausgleich
Balkonlänge insgesamt 9,2m
9,2m<16,08m
3 216⁵
200 Balkon
1 291⁵
200 Gaupe
203⁵
425⁵
327⁵ Gaupe
665⁵
275 Gaupe
403⁵
1 291⁵ Erker
AUFZUG
Gaupe
Gaupe
ZUGANG LAGER
ZUGANG STIEGENHAUS

STRASSENTRAKT. WESTANSICHT HEIGERLEINSTRASSE

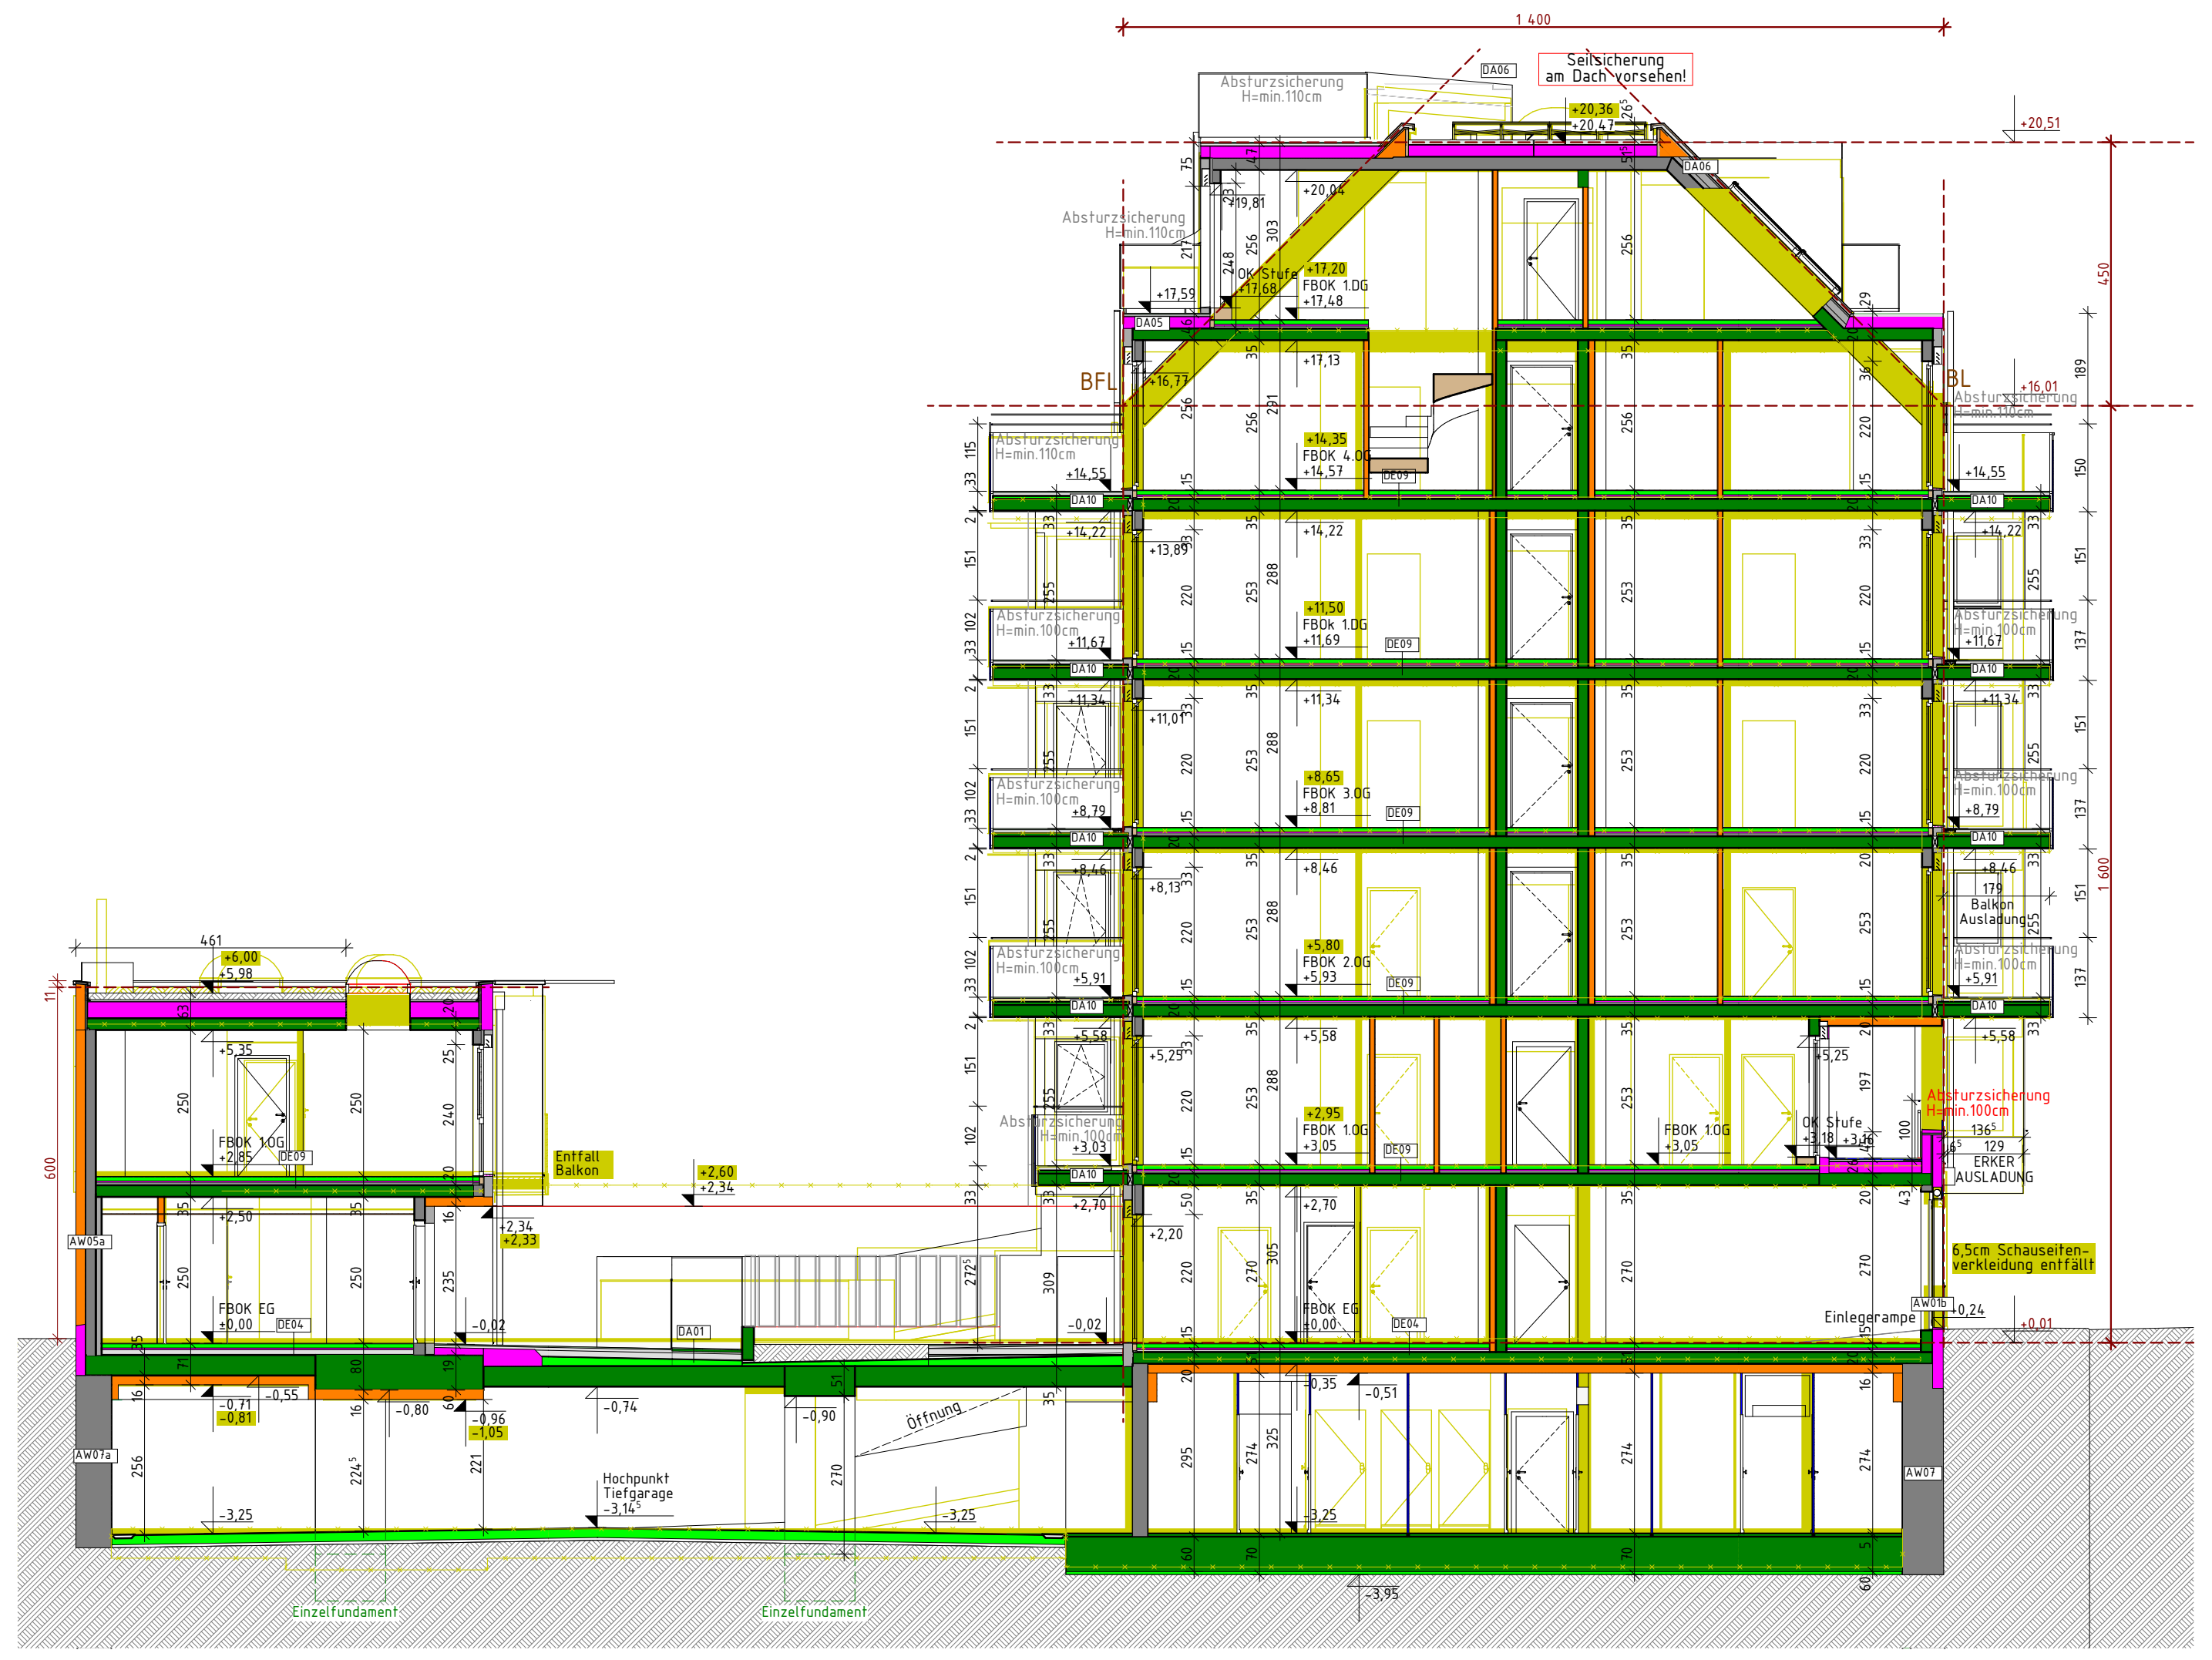

SCHNITT C-C

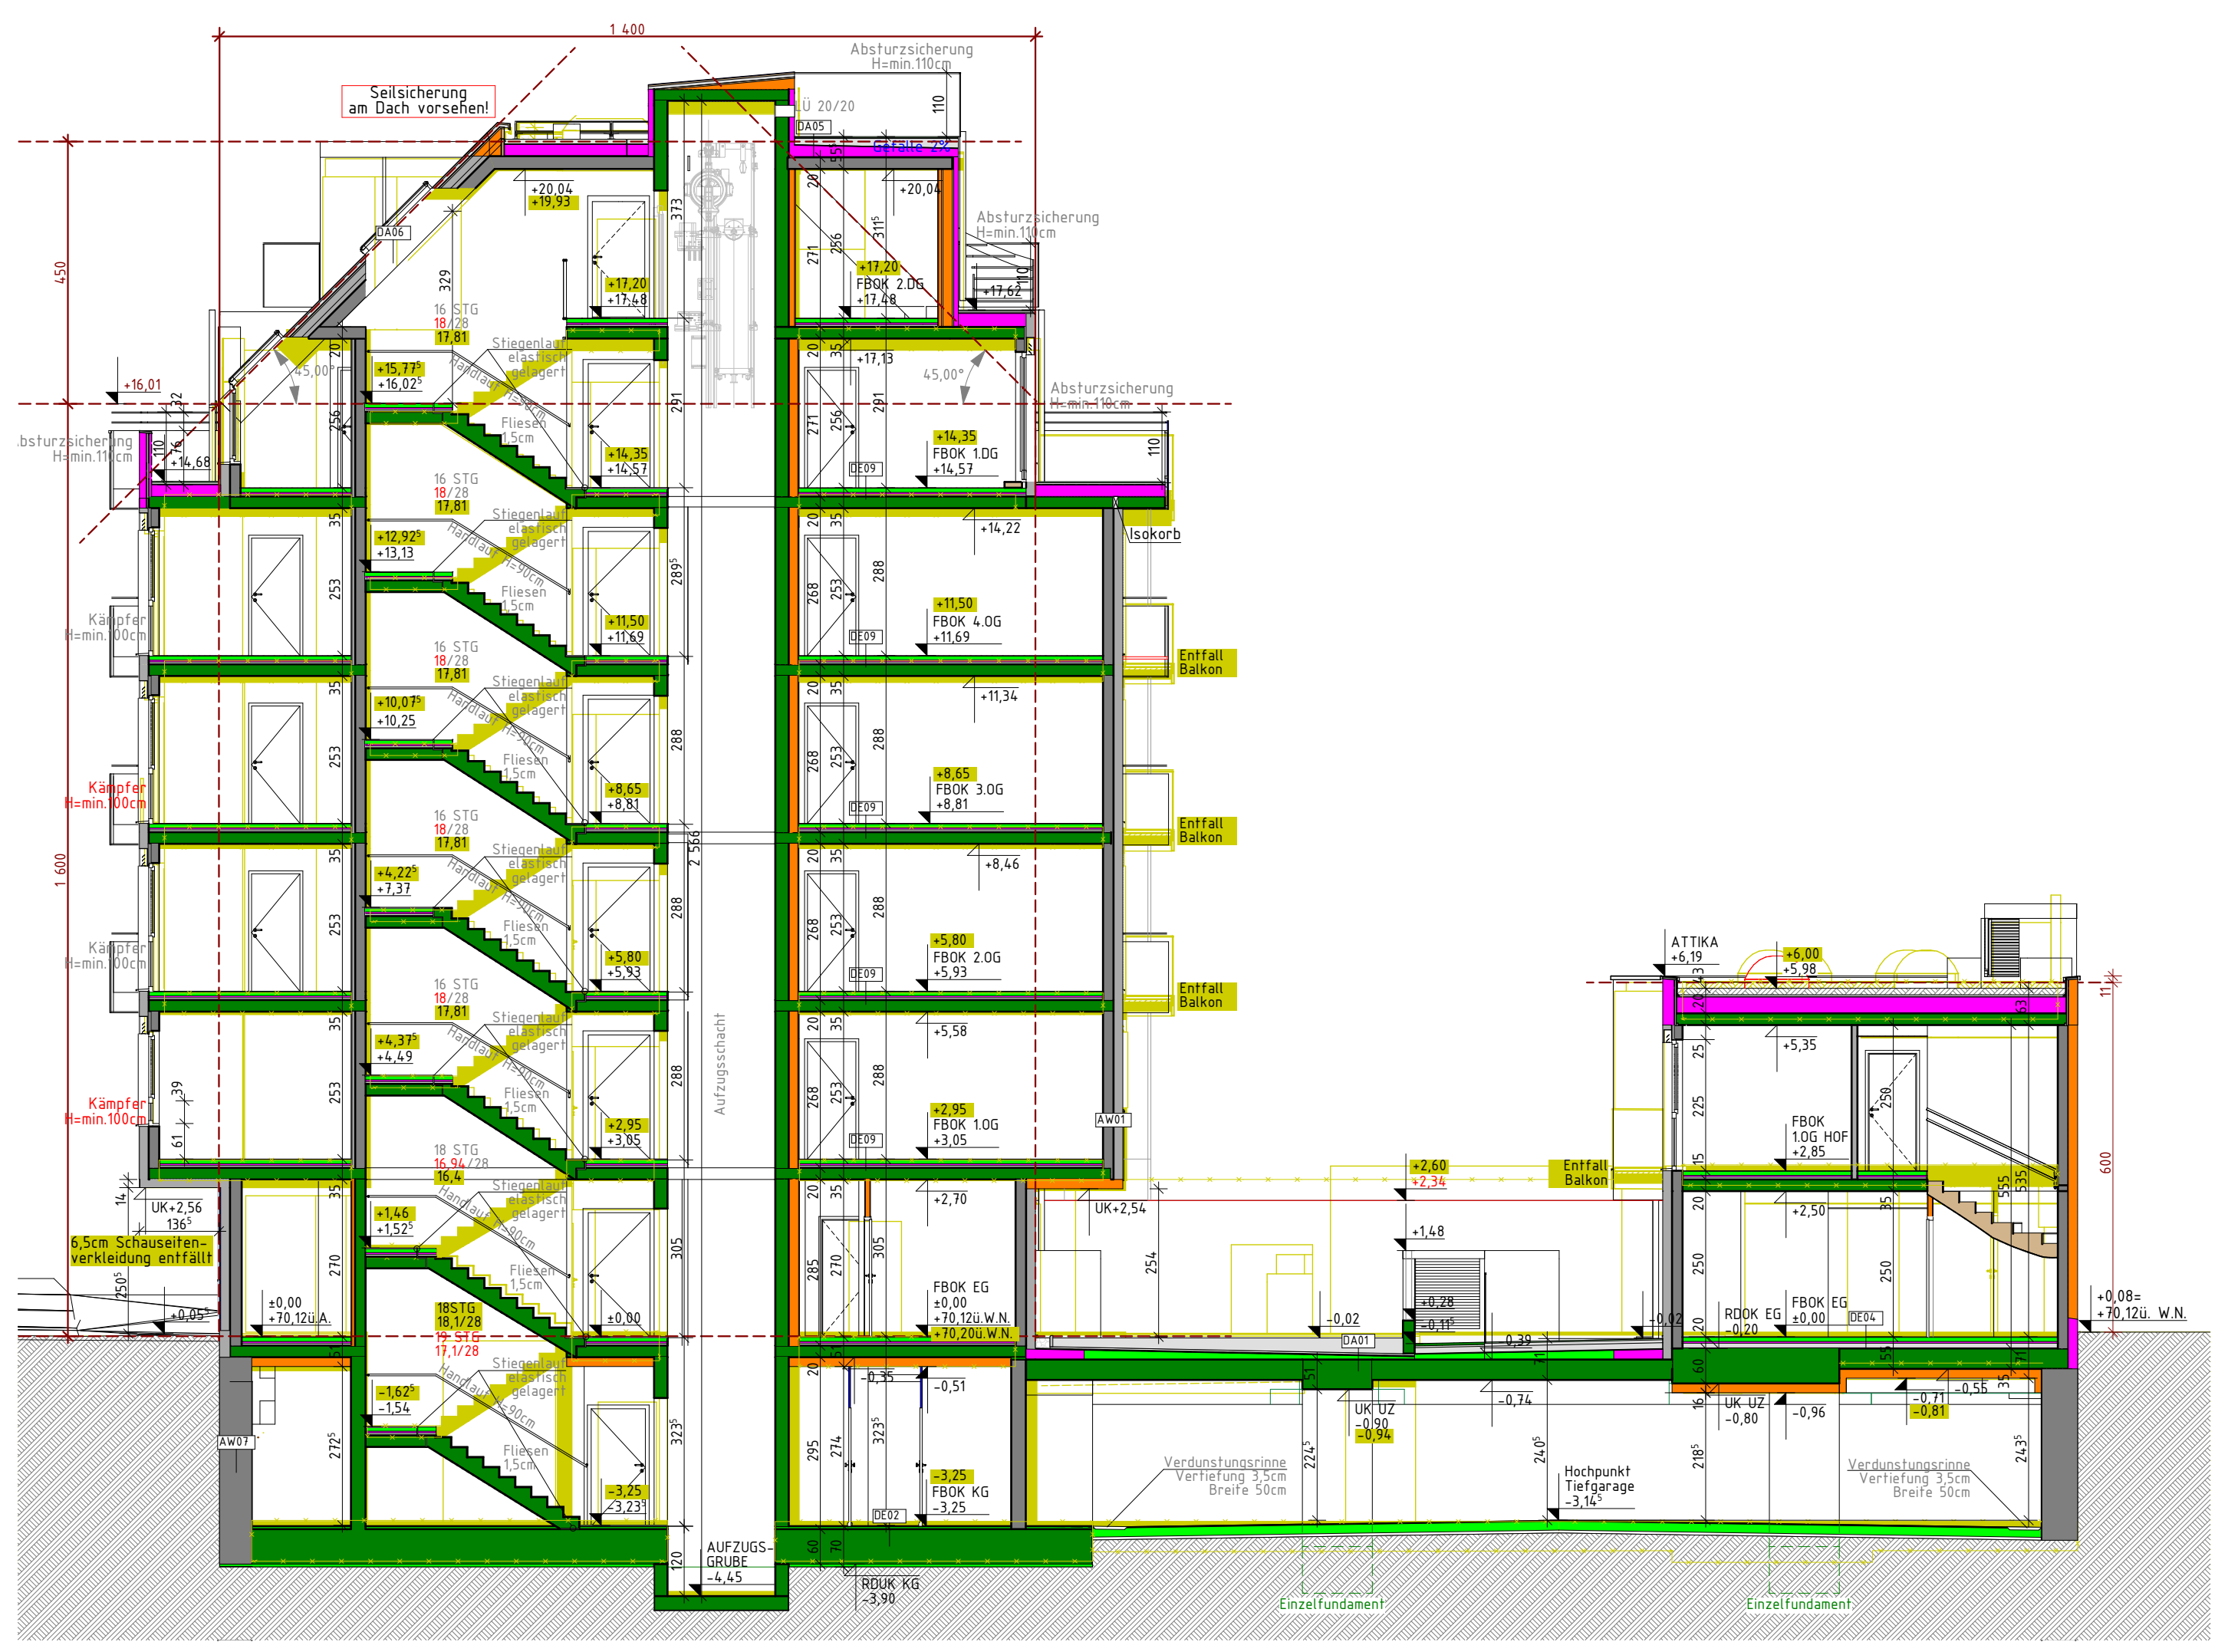

SCHNITT A-A