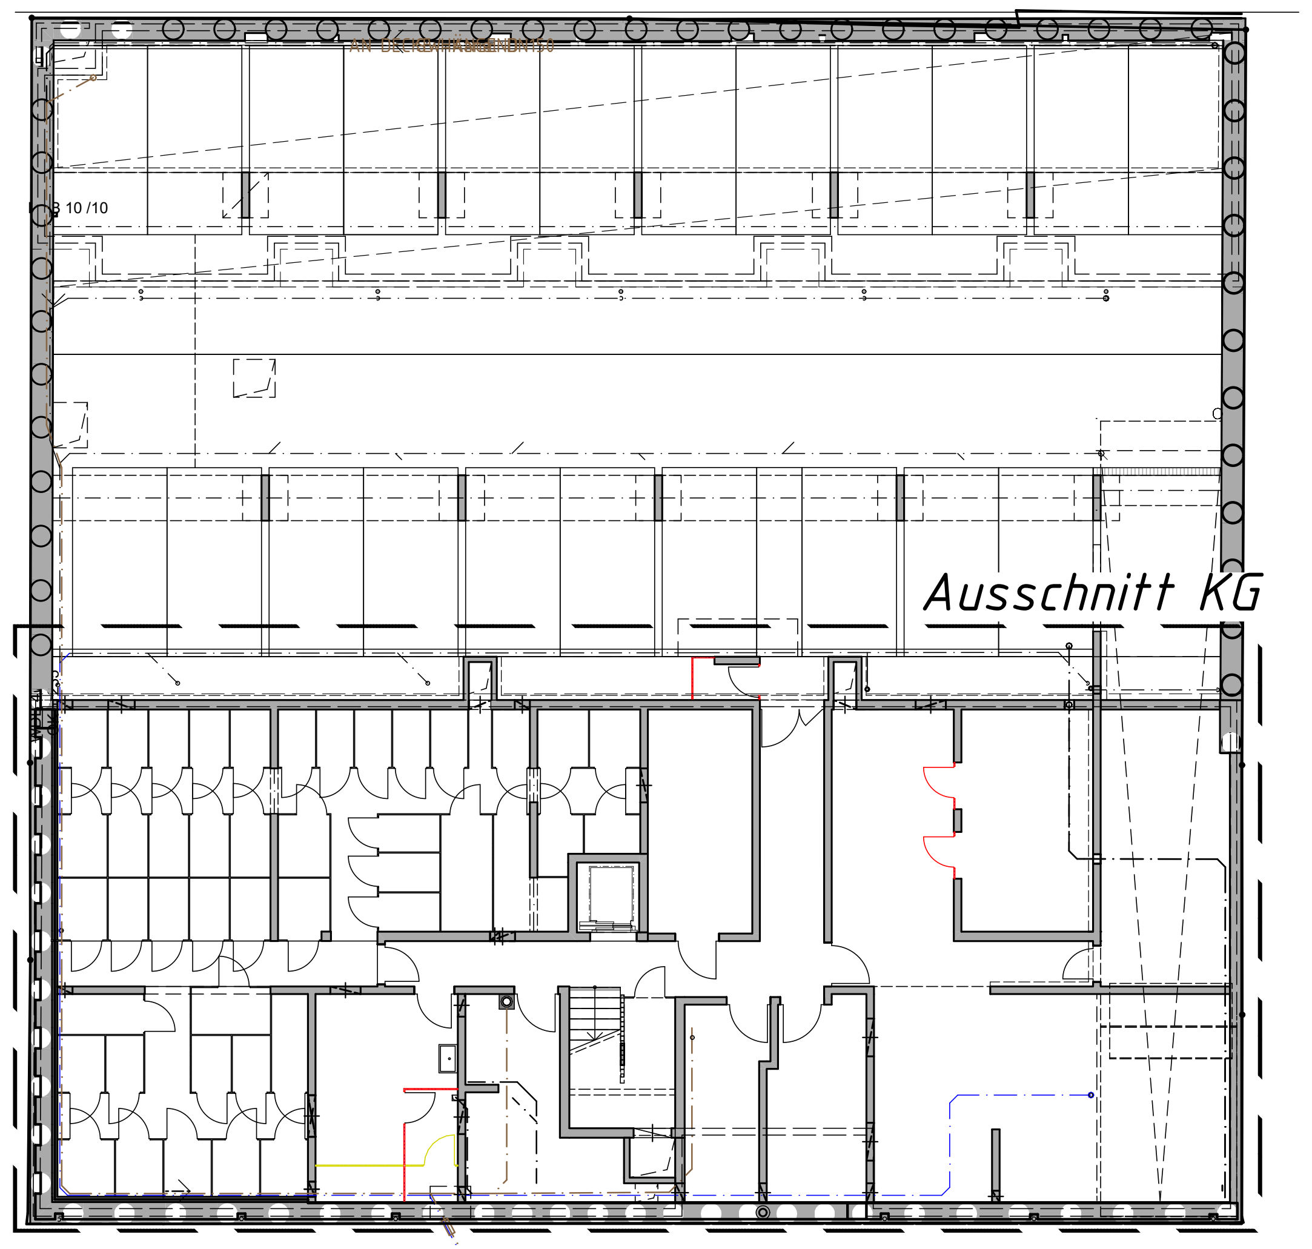

KELLERGESCHOSS ÜBERSICHT M1:200

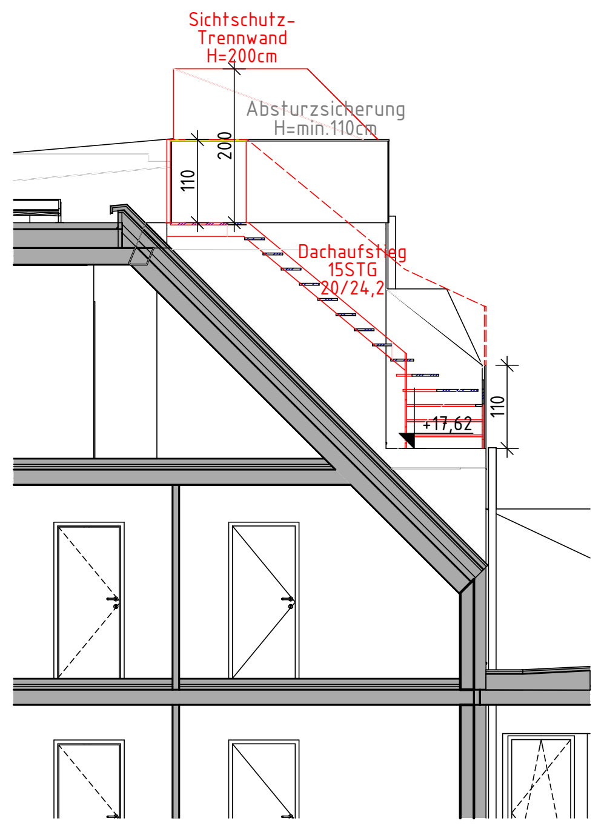

SCHNITT D-D M1:100

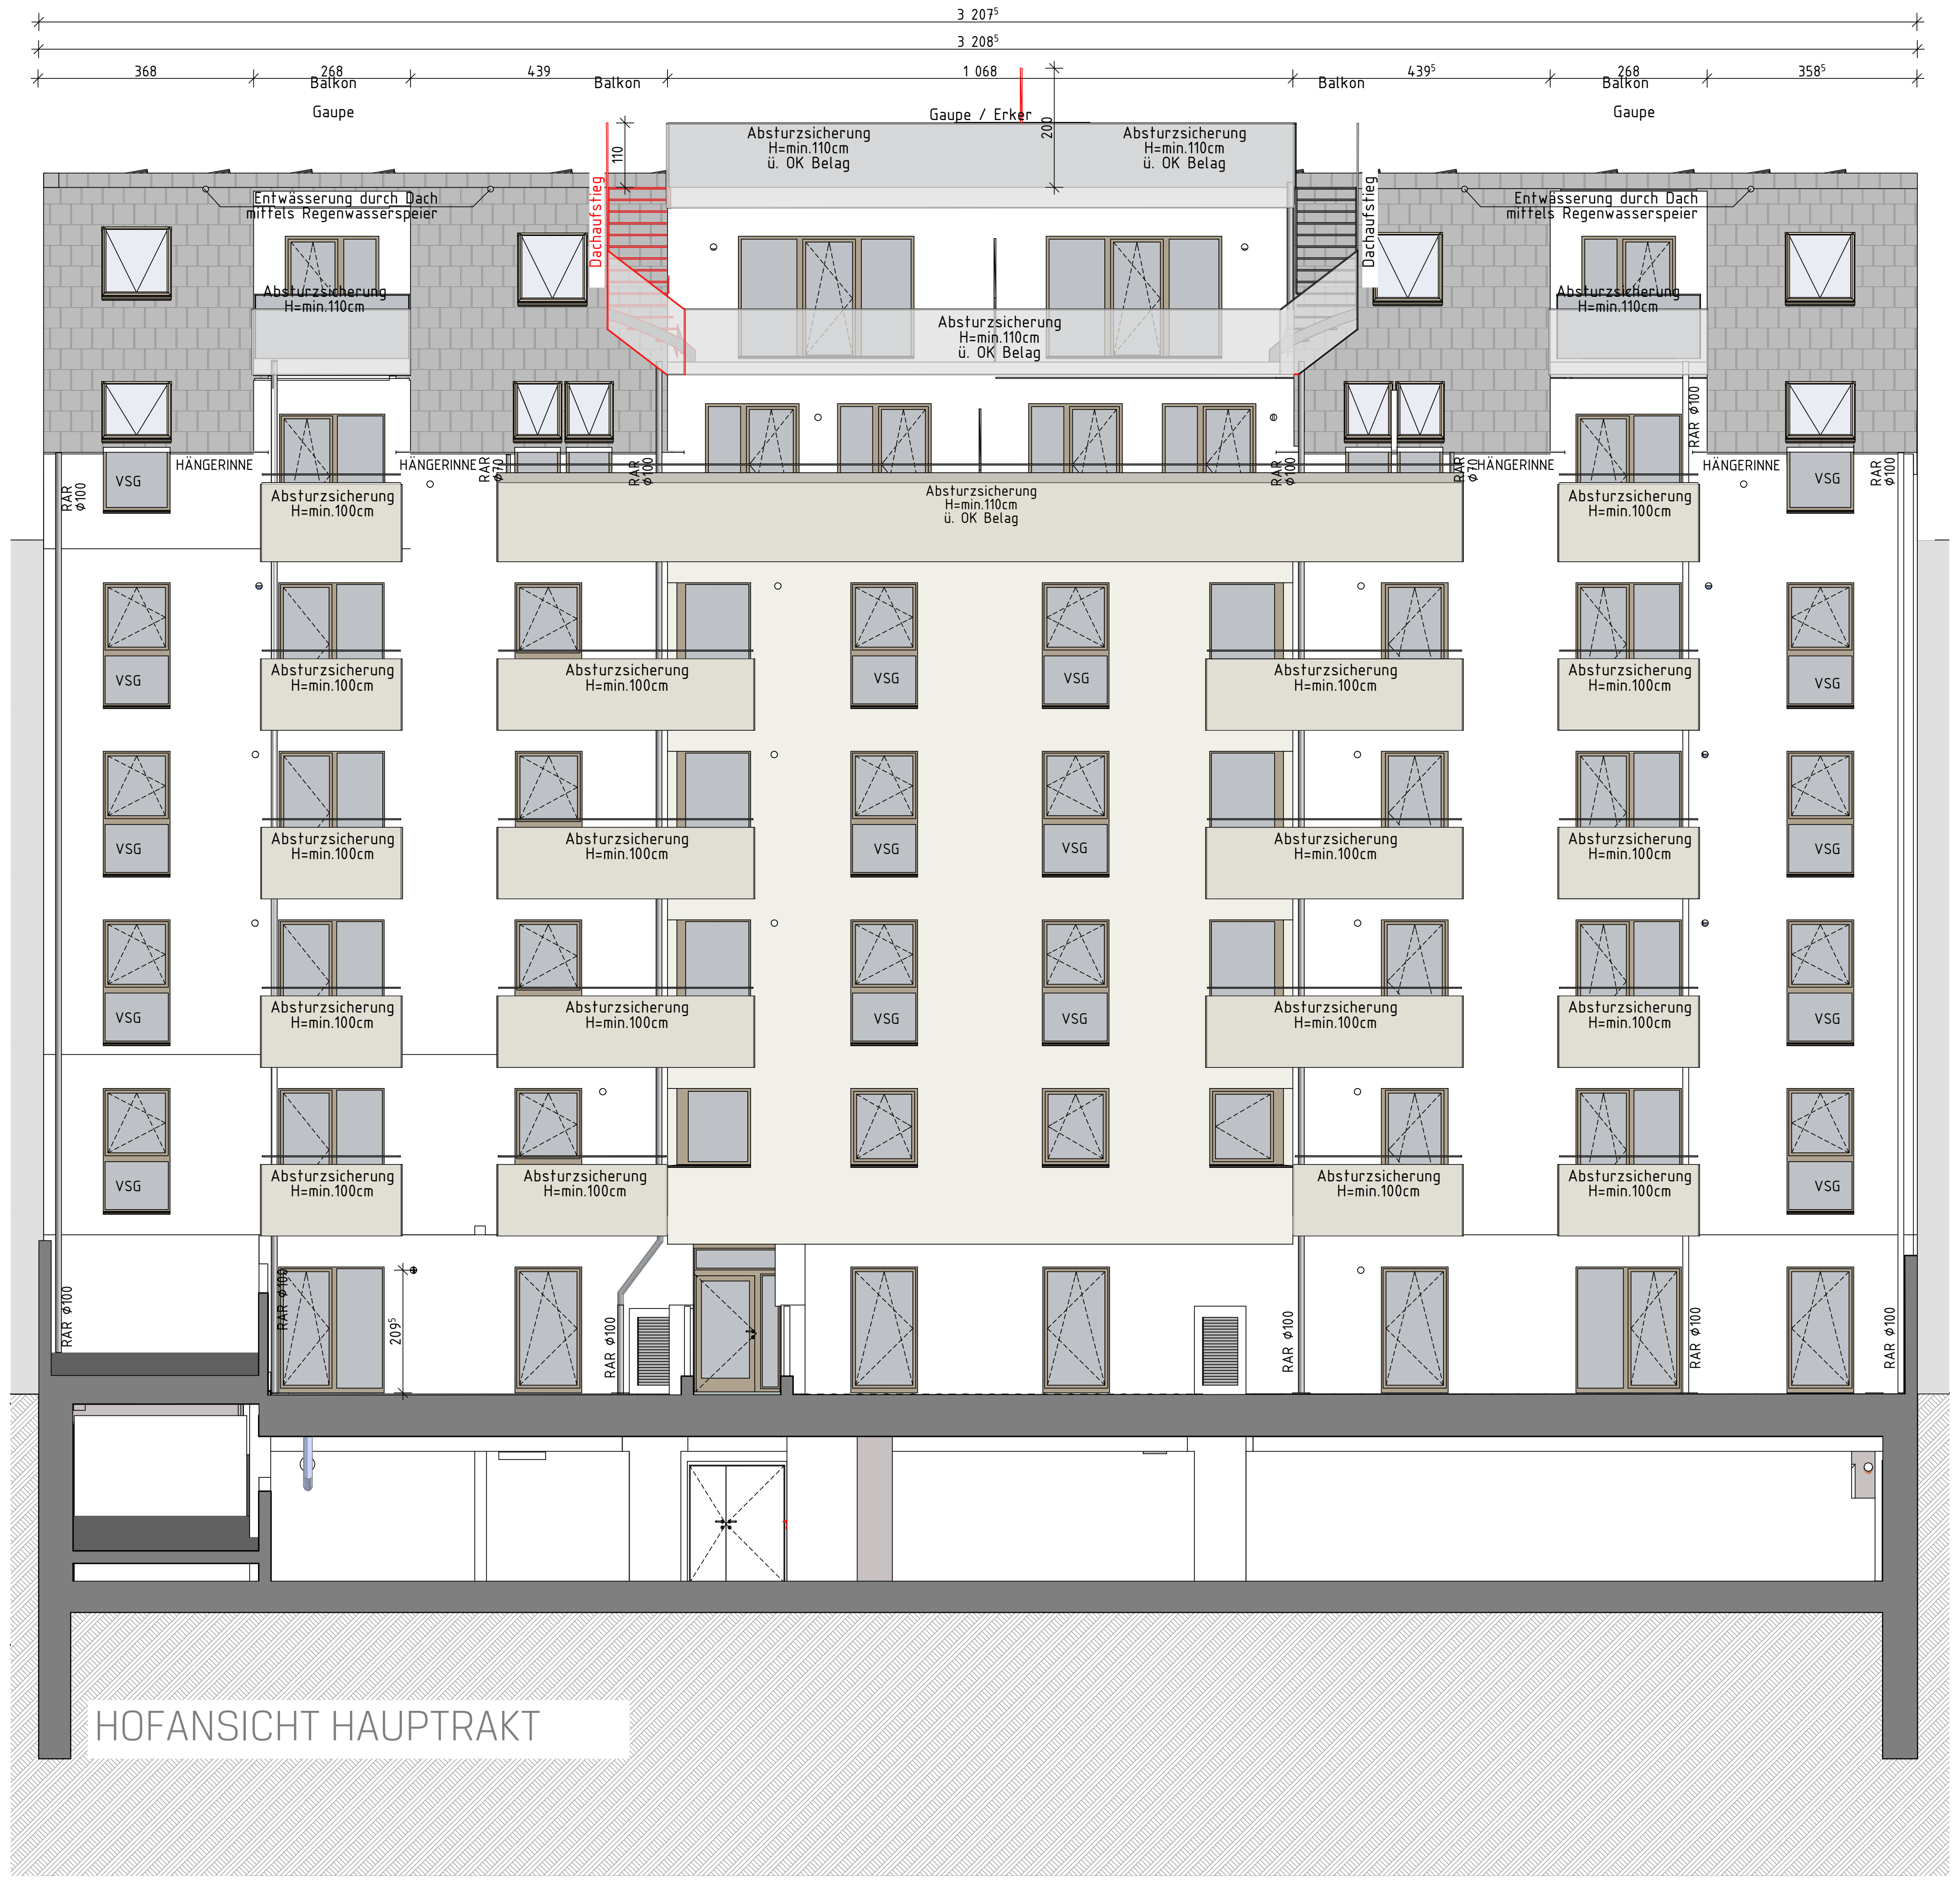
Balkon
Gaupe
Gaupe / Erker
Absturzsicherung H=min.110cm ü. OK Belag
Entwasserung durch Dach mittels Regenwasserspeier
Absturzsicherung H=min.110cm
Dachaufstieg
HÄNGERINNE
Absturzsicherung H=min.100cm
VSG
RAR ø100
HOFANSICHT HAUPTRAKT

HOFANSICHT M1:100

LEGENDE:

⬜	BESTAND	—	SCHMUTZWASSER	UZ	UNTERZUG
🟨	ABBRUCH	—	REGENWASSER	ÜZ	ÜBERZUG
🟥	NEUBAU	—	WASSER	AR	ABFALLROHR
		—	HEIZUNG	RR	REGENROHR
🟩	STAHLBETON	—	STROM	RSK	REGENSINKKASTEN
🟩	UNBEWEHRTER BETON	—	GAS	PH	PARAPETHÖHE
🟥	MAUERWERK	—	FERNWÄRME	STUK	STURZUNTERKANTE
🟫	HOLZ			DL	DURCHGANGSLICHTE
🟪	DÄMMUNG (HART)	DFF	DACHFLÄCHENFENSTER	OK	OBERKANTE
🟧	DÄMMUNG (WEICH)	LK	LICHTKUPPEL	UK	UNTERKANTE
▨	STAHL	VSG	VERBUND-SICHERKEITSGLAS	FOK	FUSSBODENOBERKANTE
🟦	GLAS	ESG	EINSCHEIBEN-SICHERHEITSGLAS	WD	WANDDURCHBRUCH
🟧	GIPSKARTON	BRE	BRANDRAUCHENTLÜFTUNG	DD	DECKENDURCHBRUCH

- LÜFTUNGEN DURCH FREMDE BRANDABSCHNITTE EI90 UND A2 UMMANTELT
- RESTRÄUME IM DACHGESCHOSS EI60 VON INNEN 2x GKF
- WOHNUNGSEINGANGSTÜREN EI_2-30
- AUSWECHSLUNGEN REI90 UMMANTELT
- HEIZUNGSSYSTEM: WÄRMEPUMPE
- PHOTOVOLTAIKANLAGE IST AM FLACHDACH VORDERTRAKT AUFGESTÄNDERT
- ALLE AUSKRAGENDEN TEILE THERMISCH GETRENNT
- ALLE INNENLIEGENDEN BÄDER UND WC's LÜFTUNG ÜBER DACH
- FÜR JEDE WOHNUNG IST EIN EINLAGERUNGSRAUM VORHANDEN
- IN JEDER WOHNUNG IST EINE GEEIGNETE AUFSTELLMÖGLICHKEIT UND EIN ANSCHLUSS FÜR EINE WASCHMASCHINE UND EINE MASCHINELLE TROCKENEINRICHTUNG VORGESEHEN.
- NIEDERSCHLAGSWÄSSER UND FÄKALWÄSSER WERDEN IN DEN ÖFFENTLICHEN KANAL GELEITET
- STIEGEN UND GÄNGE KUNSTSTEINBELAG, BELAG MÜLLRAUM UND GARAGE MIND. Bfl
- GEMÄSS OIB RICHTLINIE 2, ABSATZ 3, PUNKT 11 - UNVERNETZTE RAUCHWARNMELDER IN ALLEN AUFENTHALTSRÄUMEN (AUSGEN. KÜCHEN, BEI WOHNKÜ. NICHT IM KOCHBEREICH) SOWIE BEI GÄNGEN ÜBER DIE FLUCHTWEGE VON AUFENTHALTSR. FÜHREN
- SCHADENSFOLGEKLASSE CC2 nach ÖNORM EN 1090-2 Tab. B3
- NÄCHSTE HYDRANT BIS GRUNDGRENZE: ca.115m<150m
- ALLE INNENLIEGENDE RÄUME SIND MECHANISCH ENTLÜFTET
- SCHÄCHTE WERDEN GEMÄSS WIENER INSTALLATIONSRICHTLINIE SCHACHTTYP A AUSGEFÜHRT
- AUFZUGSSCHÄCHTE SIND MIT MIND 2,5% DES SCHACHTQUERSCHNITTS ENTLÜFTET.
- FLUCHTWEGS UND ORIENTIERUNGSBELEUCHTUNG GEMÄß DEN BESTIMMUNGEN DER TRVB 102E
- DRUCKBELÜFTUNGSANLAGE GEMÄSS DEN BESTIMMUNGEN DER TRVB 112S (AUFENTHALTSKONZEPT)

± 0.00 ENTSPRICHT 70,12M ÜBER WIENER NULL

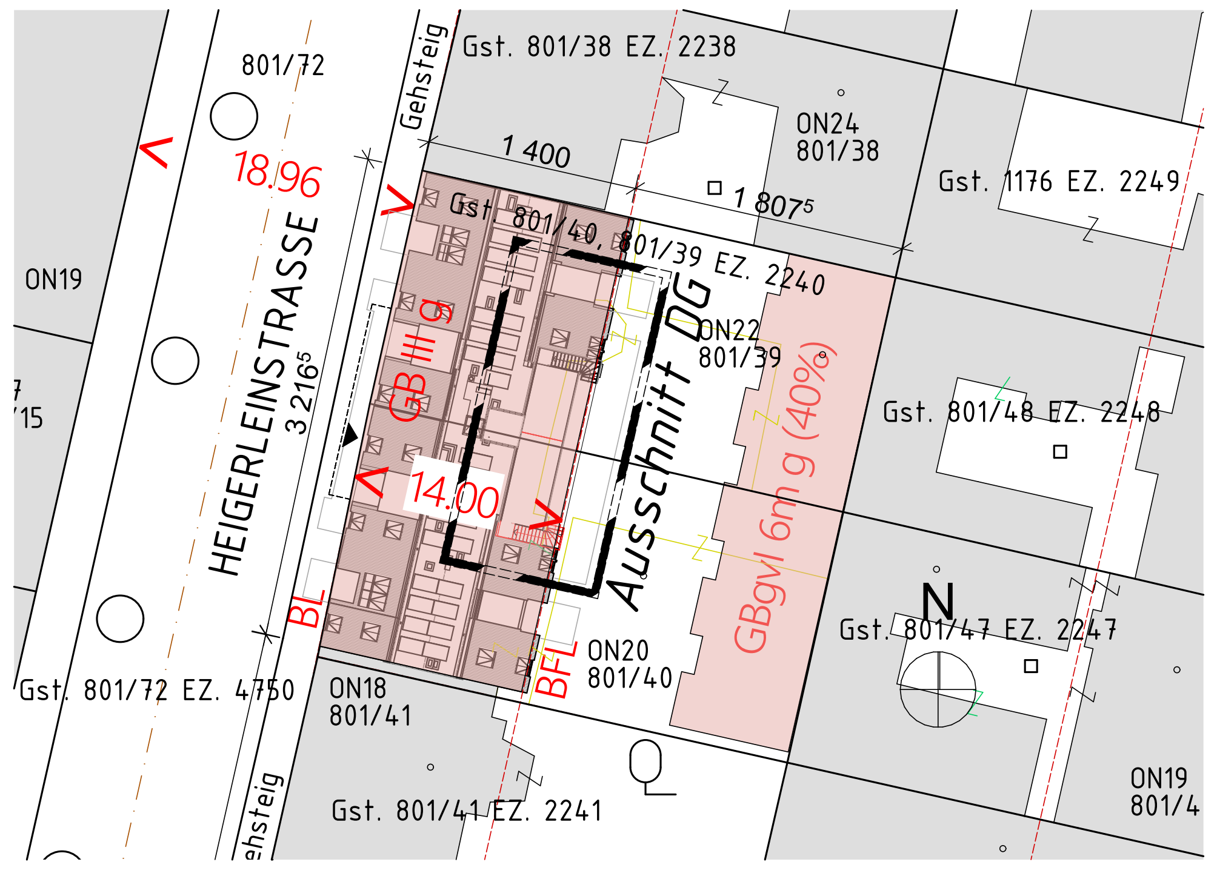

LAGEPLAN M1:500

ANRAINER:

Gst. 801/13 EZ. 2213
Brozek Andreas 1/1
1160 Wien,
Heigerleinstraße 13

Gst. 801/15, Gst.801/14 EZ.2215
Erste gemeinnützige Wohnungsgesellschaft
Heimstätte Gesellschaft 1/1
1050 Emil Kraik-G 3

Gst. 801/17 EZ. 2218
Österreichisches Volkswohnungswerk
Gemeinnützige Gesellschaft mit
beschränkter Haftung 521/5190
1200 Wien,
Brigittenauer Lände 50-54
und weitere Eigentümer siehe
Grundbuchsauszug (Beilage)

Gst. 801/72 EZ. 4750
Stadt Wien (Öffentliches Gut) 1/1
1082 Rathaus

Gst. 776/28 EZ. 2237
Gattinger Karl-Heinz 72/1048
4801 Traunkirchen,
Mitterweg 3
und weitere Eigentümer

Gst. 801/38 EZ. 2238
Euler-Rolle Christoph 34/649
1160 Wien,
Heigerleinstraße 24/11

Gst. 801/39, Gst. 801/40 EZ. 2238
Simony Immobilien GmbH & Co Phi KG (453696a)
1/1
1180 Wien,
Symonygasse 12

Gst. 801/40 EZ. 2240
Simony Immobilien GmbH & Co Phi KG (453696a)
1/1
1180 Wien,
Symonygasse 12

Gst. 801/41 EZ. 2241
Hallas Ludwig 1/4
1160 Wien,
Heigerleinstraße 18
Hallas Ludwig 1/4
1160 Wien,
Heigerleinstraße 18/5
Mag.Schlechta Andrea 1/4
1130 Wien,
Geylinggasse 27/18
Dr. Wernhart-Hallas Eisabeth
1130 Wien,
Hietzinger Hauptstraße 124/5

Gst. 801/42 EZ. 2242
PREMIUM Degengasse 54 GmbH &
Co KG, FN 241292t 1/1
1040 Wien,
Opernring 17-21

Gst. 801/43 EZ. 2243
Ing. Vanek Ludwig 1/3
Dipl.Ing. Vanek Erwin 1/3
Vanek Elisabeth 1/3,
1160 Wien,
Degengasse 52/1/6

Gst. 801/45 EZ. 2245
Girzig Klaus 1/1

Gst. 801/44 EZ. 2244
Nowak Klaus 112/506
1150 Wien,
Märzstraße 76-78/1/10

Gst. 801/46 EZ. 2246
Wörz Julia, Dr.
1160 Wien, Seitenberggasse 17/7

und weitere Eigentümer siehe
Grundbuchsauszug (Beilage)

Gst. 801/47 EZ. 2247
Fleger Ernst 37/1628
1160 Wien,
Seitenberggasse 19
und weitere Eigentümer siehe
Grundbuchsauszug (Beilage)

Gst. 801/48 EZ. 2248
Pfluger Anna 1/1
1160 Wien,
Seitenberggasse 21/7

Gst. 1176 EZ. 2249
Mag. Trauth Micahela 1/1
1160 Wien,
Seitenberggasse 21/11-13

Gst. 1175 EZ. 3192
Mag. Erbner Viktoria 1/2
1090 Wien,
Schubertgasse 4-6/5
Schunker Julia 1/2
1160 Wien,
Seitenberggasse 25/27

DOLL
FUSS
ARCHITEKT

2.AUSWECHSLUNGSPLAN

PLANINHALT:	Parie	A	B	C	D	E	F	G	H	I	J	K
2. AUSWECHSLUNGSPLAN	Nr.	1	2	3	4	5	6	7				

BAUVORHABEN:

1160 Wien, Heigerleinstrasse 20

ÜBER DIE ERGÄNZUNG DER 2. STAHLSTIEGE AUF DIE DACHTERRASSE UND ÄNDERUNG DER RAUMORDNUNG IM KELLERGESCHOSS

Heigerleinstraße 20
1160 Wien-Ottakring

GRUNDSTÜCKSNUMMER	801/39, 801/40
EINLAGEZAHL	2240
KATASTRALGEMEINDE	01405 Ottakring

GRUNDEIGENTÜMER/BAUWERBER

HEIGE20 Projekt GmbH & Co KG
Sterngasse 11/4B
1010 Wien

BEHÖRDE

BAUFÜHRER

Auböck Bau GmbH
Drosselstraße 36
A-4470 Enns

PLANVERFASSER

ARCHITEKT
DIPL.ING. GERHARD DOLLFUSS
STAATLICH BEFUGTER U. BEEIDETER ZIVILTECHNIKER
3240 MANK, BAHNHOFSTRASSE 4/4
0676/9490946 · office@dollfuss.eu

PLANINHALT	GRUNDRISSE, LAGEPLAN, SCHNITT, ANSICHT	
MAßSTAB		
PLANDATUM	12.08.2021	DRUCKDATUM 17.08.2021
PLANNUMMER	A2017-04-202	
PROJEKT	1160 Wien, Heigerleinstrasse 20	
CAD-FILE	A2017-04_Heigerlein_2.AWPL_20210812.pln	

DIESER PLAN IST GEISTIGES EIGENTUM DES PLANVERFASSERS UND DARF NUR MIT DESSEN ZUSTIMMUNG WEITERGEGEBEN UND VERVIELFÄLTIGT WERDEN !
DAS VORLIEGENDE PLANDOKUMENT DIENT ALS GRUNDLAGE FÜR DIE BEHÖRDLICHE GENEHMIGUNG lt. WRBO UND STELLT KEINEN AUSFÜHRUNGSPLAN DAR!

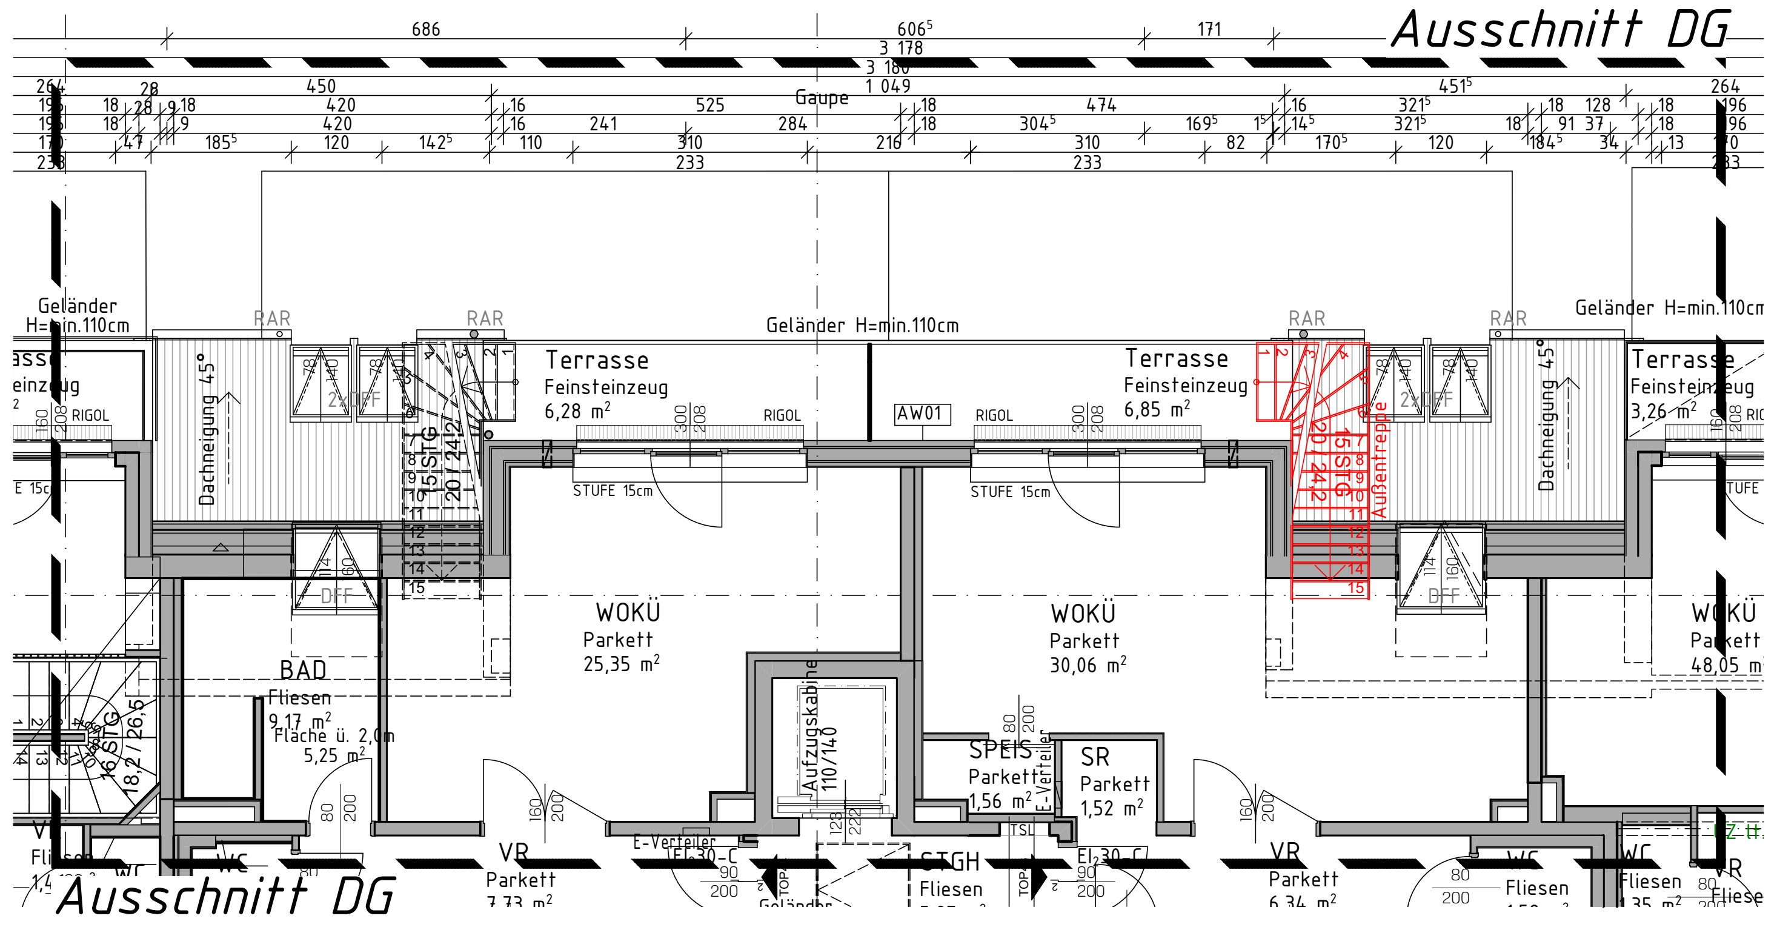

2. DACHGESCHOSS M1:100

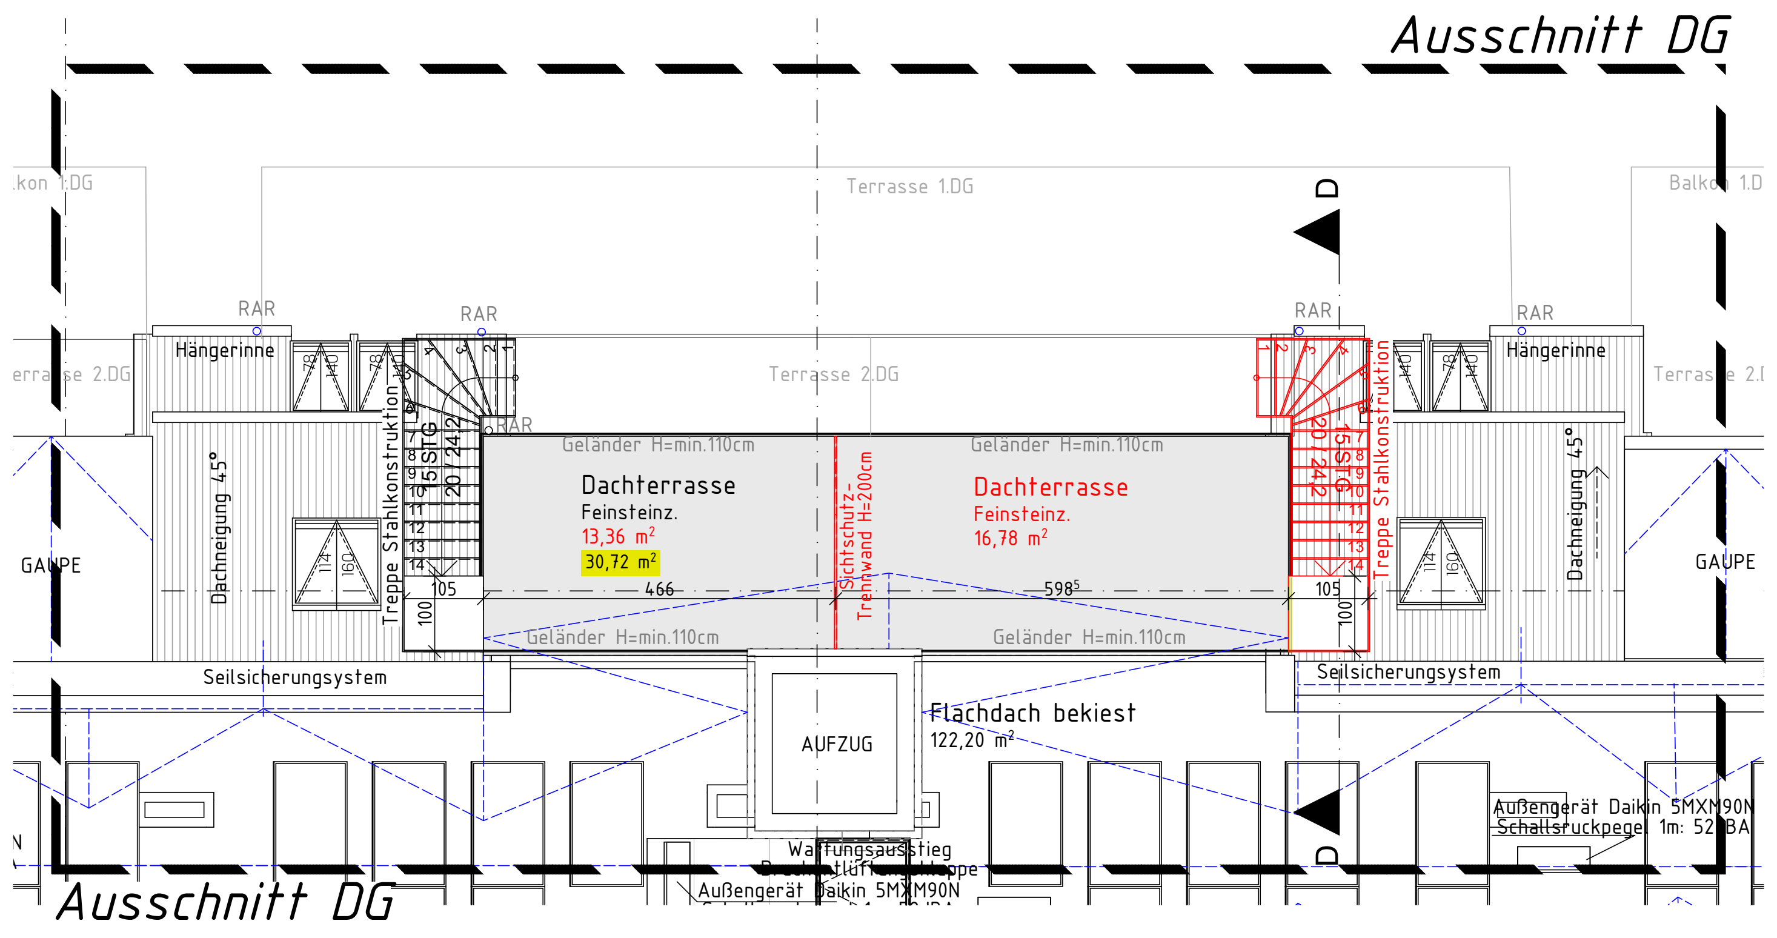

DACHDRAUFSICHT M1:100

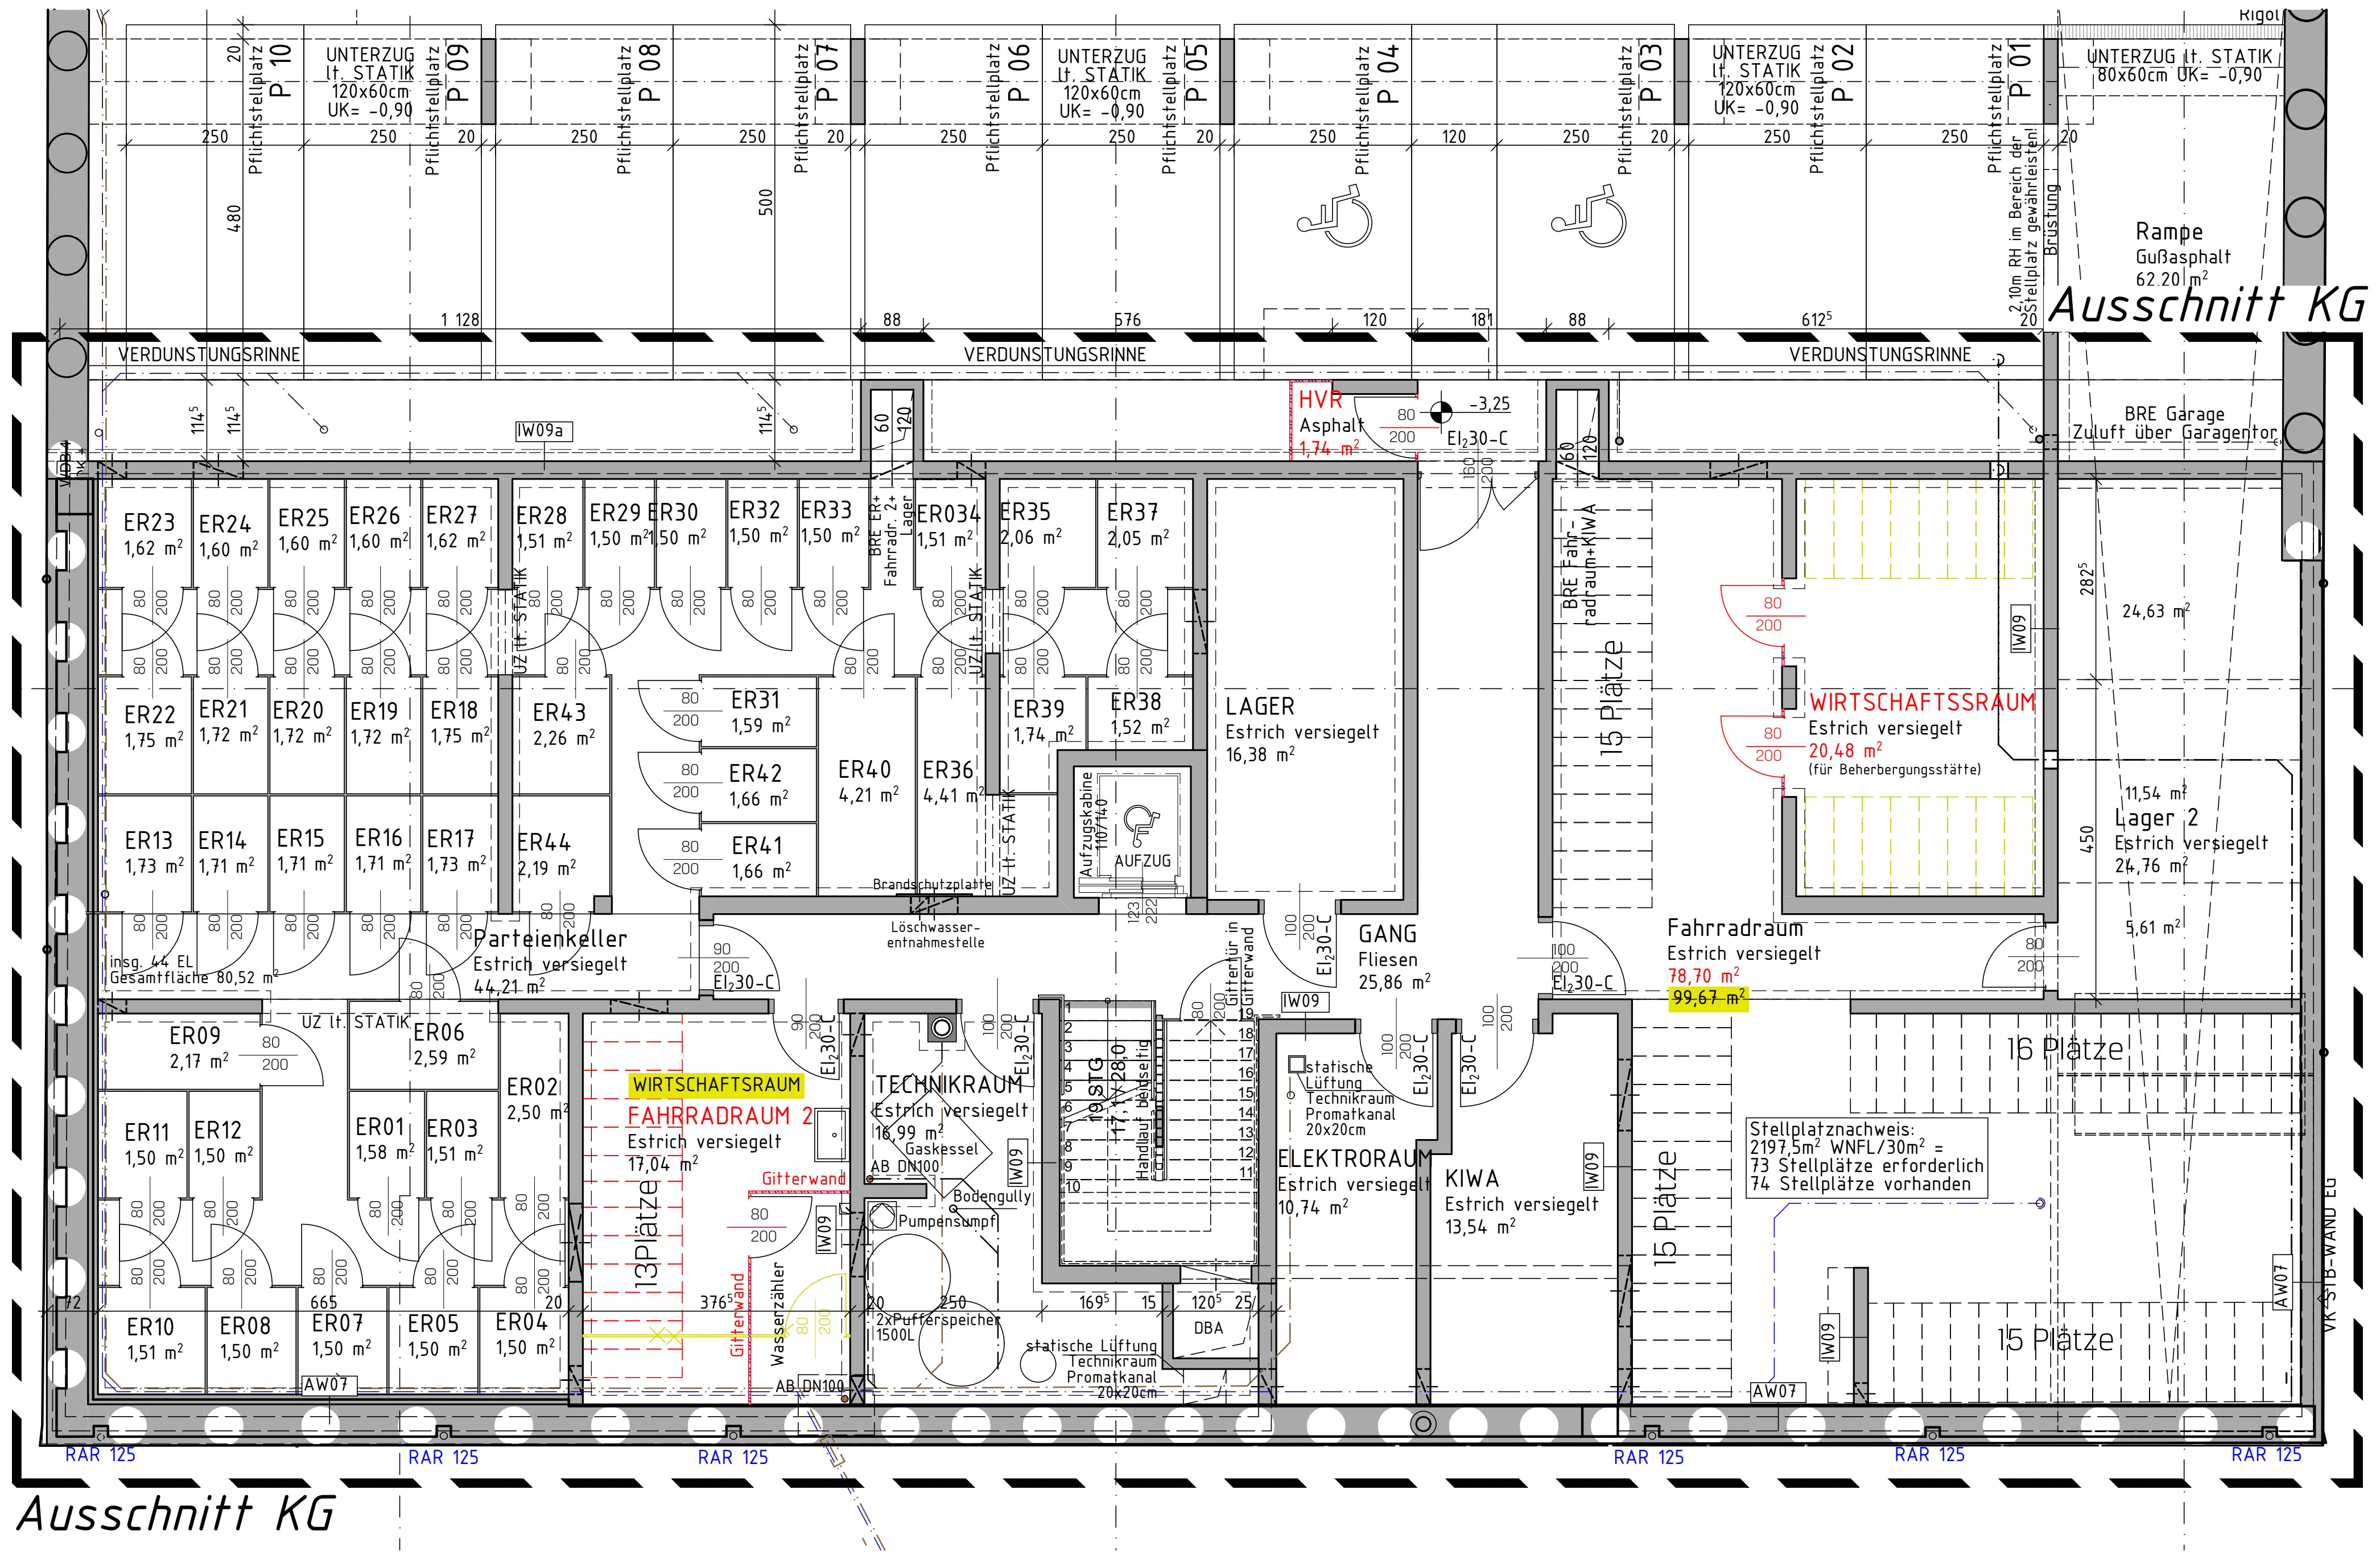

KELLERGESCHOSS M1:100