VISUALISIERUNGEN DIENEN LEDIGLICH ZUR BESSEREN DARSTELLUNG DES ENTWURFS UND SIND FÜR DIE EINREICHUNG NICHT RELEVANT:

STELLPLATZNACHWEIS: 2264m² WOHNNUTZFLÄCHE = 22 STELLPLÄTZE
5 REIHENHÄUSER = 1 STELLPLATZ
INSGESAMT 23 STELLPLÄTZE
22 STELLPLÄTZE VORHANDEN

FAHRRAD-STELLPLATZNACHWEIS: 2264m² WOHNNUTZFLÄCHE / 30m²
min. 75 FAHRRADABSTELLPLÄTZE

BETTENANZAHL: INSGESAMT 5 REIHENHÄUSER (BEHERBERGUNGSBETRIEB)
2 BETTEN PRO BETRIEBSEINHEIT
INSGESAMT 10 BETTEN

LEGENDE:

⬜	BESTAND	—	SCHMUTZWASSER	UZ	UNTERZUG
🟨	ABBRUCH	—	REGENWASSER	ÜZ	ÜBERZUG
🟥	NEUBAU	—	WASSER	AR	ABFALLROHR
		—	HEIZUNG	RR	REGENROHR
🟩	STAHLBETON	—	STROM	RSK	REGENSINKKASTEN
🟩	UNBEWEHRTER BETON	—	GAS	PH	PARAPETHÖHE
🟥	MAUERWERK	—	FERNWÄRME	STUK	STURZUNTERKANTE
🟫	HOLZ			DL	DURCHGANGSLICHTE
🟪	DÄMMUNG (HART)	DFF	DACHFLÄCHENFENSTER	OK	OBERKANTE
🟧	DÄMMUNG (WEICH)	LK	LICHTKUPPEL	UK	UNTERKANTE
▨	STAHL	VSG	VERBUND-SICHERKEITSGLAS	FOK	FUSSBODENOBERKANTE
🟦	GLAS	ESG	EINSCHEIBEN-SICHERHEITSGLAS	WD	WANDDURCHBRUCH
🟧	GIPSKARTON	BRE	BRANDRAUCHENTLÜFTUNG	DD	DECKENDURCHBRUCH

- LÜFTUNGEN DURCH FREMDE BRANDABSCHNITTE EI90 UND A2 UMMANTELT
- RESTRÄUME IM DACHGESCHOSS EI60 VON INNEN 2x GKF
- WOHNUNGSEINGANGSTÜREN EI_2-30
- AUSWECHSLUNGEN REI90 UMMANTELT
- HEIZUNGSSYSTEM: GASHEIZUNG
- PHOTOVOLTAIKANLAGE IST AM FLACHDACH VORDERTRAKT AUFGESTÄNDERT
- ALLE AUSKRAGENDEN TEILE THERMISCH GETRENNT
- ALLE INNENLIEGENDEN BÄDER UND WC's LÜFTUNG ÜBER DACH
- FÜR JEDE WOHNUNG IST EIN EINLAGERUNGSRAUM VORHANDEN
- IN JEDER WOHNUNG IST EINE GEEIGNETE AUFSTELLMÖGLICHKEIT UND EIN ANSCHLUSS FÜR EINE WASCHMASCHINE UND EINE MASCHINELLE TROCKENEINRICHTUNG VORGESEHEN.
- NIEDERSCHLAGSWÄSSER UND FÄKALWÄSSER WERDEN IN DEN ÖFFENTLICHEN KANAL GELEITET
- STIEGEN UND GÄNGE KUNSTSTEINBELAG, BELAG MÜLLRAUM UND GARAGE MIND. Bfl
- GEMÄSS OIB RICHTLINIE 2, ABSATZ 3, PUNKT 11 – UNVERNETZTE RAUCHWARNMELDER IN ALLEN AUFENTHALTSRÄUMEN (AUSGEN. KÜCHEN, BEI WOHNKÜ. NICHT IM KOCHBEREICH) SOWIE BEI GÄNGEN ÜBER DIE FLUCHTWEGE VON AUFENTHALTSR. FÜHREN
- SCHADENSFOLGEKLASSE CC2 nach ÖNORM EN 1090-2 Tab. B3
- NÄCHSTE HYDRANT BIS GRUNDGRENZE: ca.115m<150m
- ALLE INNENLIEGENDE RÄUME SIND MECHANISCH ENTLÜFTET
- SCHÄCHTE WERDEN GEMÄSS WIENER INSTALLATIONSRICHTLINIE SCHACHTTYP B AUSGEFÜHRT
- AUFZUGSSCHÄCHTE SIND MIT MIND 2,5% DES SCHACHTQUERSCHNITTS ENTLÜFTET.
- FLUCHTWEGS UND ORIENTIERUNGSBELEUCHTUNG GEMÄß DEN BESTIMMUNGEN DER TRVB 102E
- DRUCKBELÜFTUNGSANLAGE GEMÄSS DEN BESTIMMUNGEN DER TRVB 112S (AUFENTHALTSKONZEPT)

± 0.00 ENTSPRICHT 70,12M ÜBER WIENER NULL

DOLL FUSS ARCHITEKT

AUSFÜHRUNGSPLAN

PLANINHALT:
SCHNITTE, ANSICHTEN

Parie	A	B	C	D	E	F	G	H	I	J	K
Nr.	1	2	3	4	5	6	7				

BAUVORHABEN:

1160 Wien, Heigerleinstrasse 20

NEUBAU EINES MEHRFAMILIENWOHNHAUSES MIT 44 WOHNUNGEN UND 5 REIHENHAUSERN (BEHERBERUNGSBETRIEB MIT 5 BETRIEBSEINHAITEN UND 10 BETTEN)
Heigerleinstraße 20
1160 Wien-Ottakring

GRUNDSTÜCKSNUMMER	801/39, 801/40
EINLAGEZAHL	2240
KATASTRALGEMEINDE	01405 Ottakring

GRUNDEIGENTÜMER/BAUWERBER

HEIGE20 Projekt GmbH & Co KG
Sterngasse 11/4B
1010 Wien

BEHÖRDE

BAUFÜHRER

Auböck Bau GmbH
Drosselstraße 36
A-4470 Enns

PLANVERFASSER

ARCHITEKT
DIPL.ING. GERHARD DOLLFUSS
STAATLICH BEFUGTER U. BEEIDETER ZIVILTECHNIKER
3240 MANK, BAHNHOFSTRASSE 4/4
0676/9490946 · office@dollfuss.eu

PLANINHALT	GRUNDRISSE, LAGEPLAN, SCHNITT, ANSICHT
MAßSTAB	1:100,1:200
PLANDATUM	12.08.2021 DRUCKDATUM 27.10.2021
PLANNUMMER	A2017-04-202
PROJEKT	1160 Wien, Heigerleinstrasse 20
CAD-FILE	A2017-04_Heigerlein_FPL_20210812.pln

DIESER PLAN IST GEISTIGES EIGENTUM DES PLANVERFASSERS UND DARF NUR MIT DESSEN ZUSTIMMUNG WEITERGEGEBEN UND VERVIELFÄLTIGT WERDEN !
DAS VORLIEGENDE PLANDOKUMENT DIENT ALS GRUNDLAGE FÜR DIE BEHÖRDLICHE GENEHMIGUNG lt. WRBO UND STELLT KEINEN AUSFÜHRUNGSPLAN DAR!

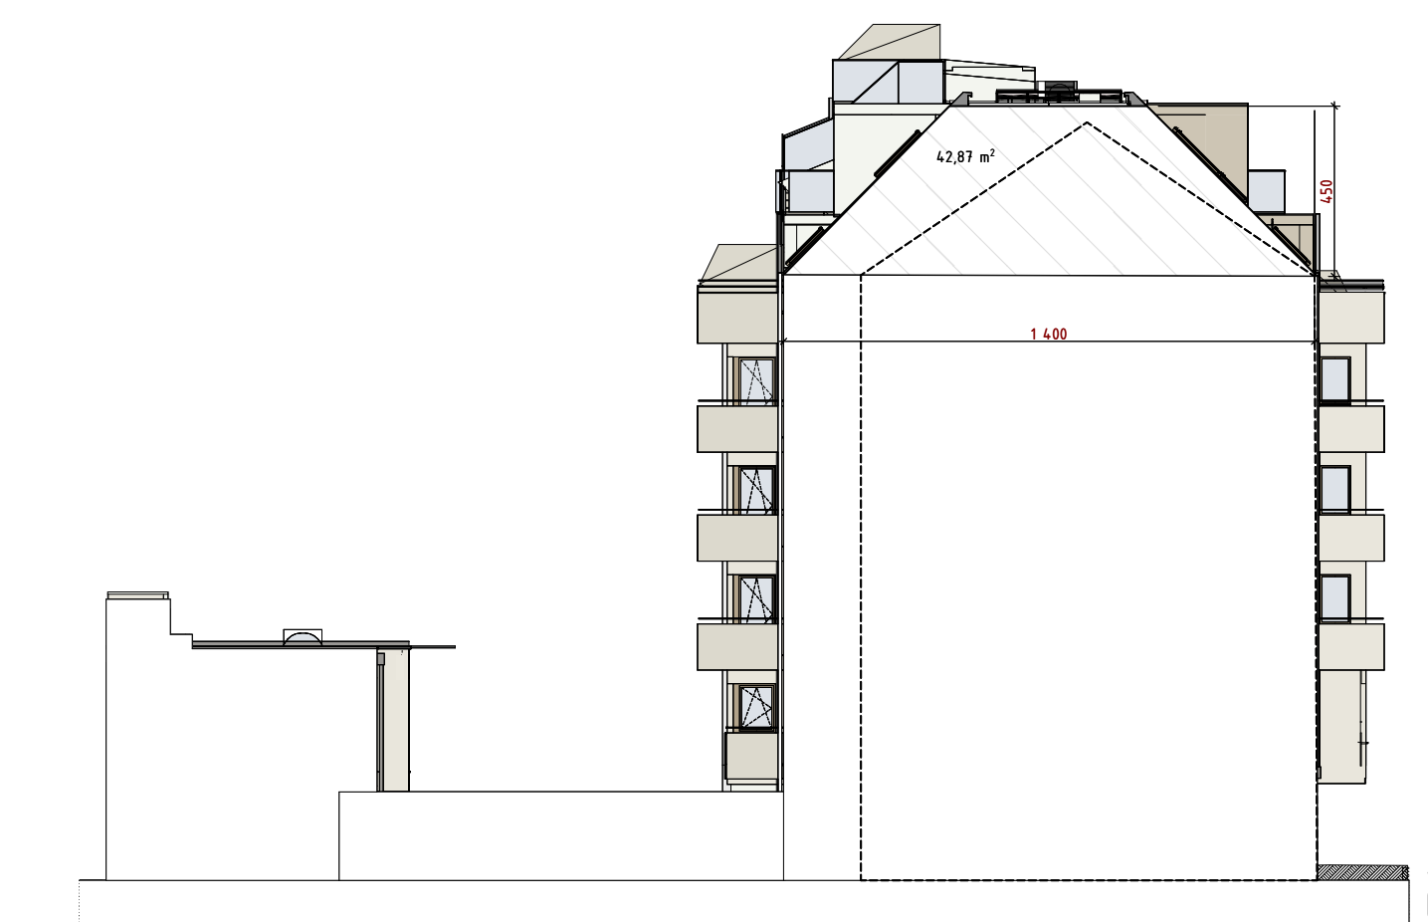

ANSICHT 1:200
GIEBELFLÄCHE

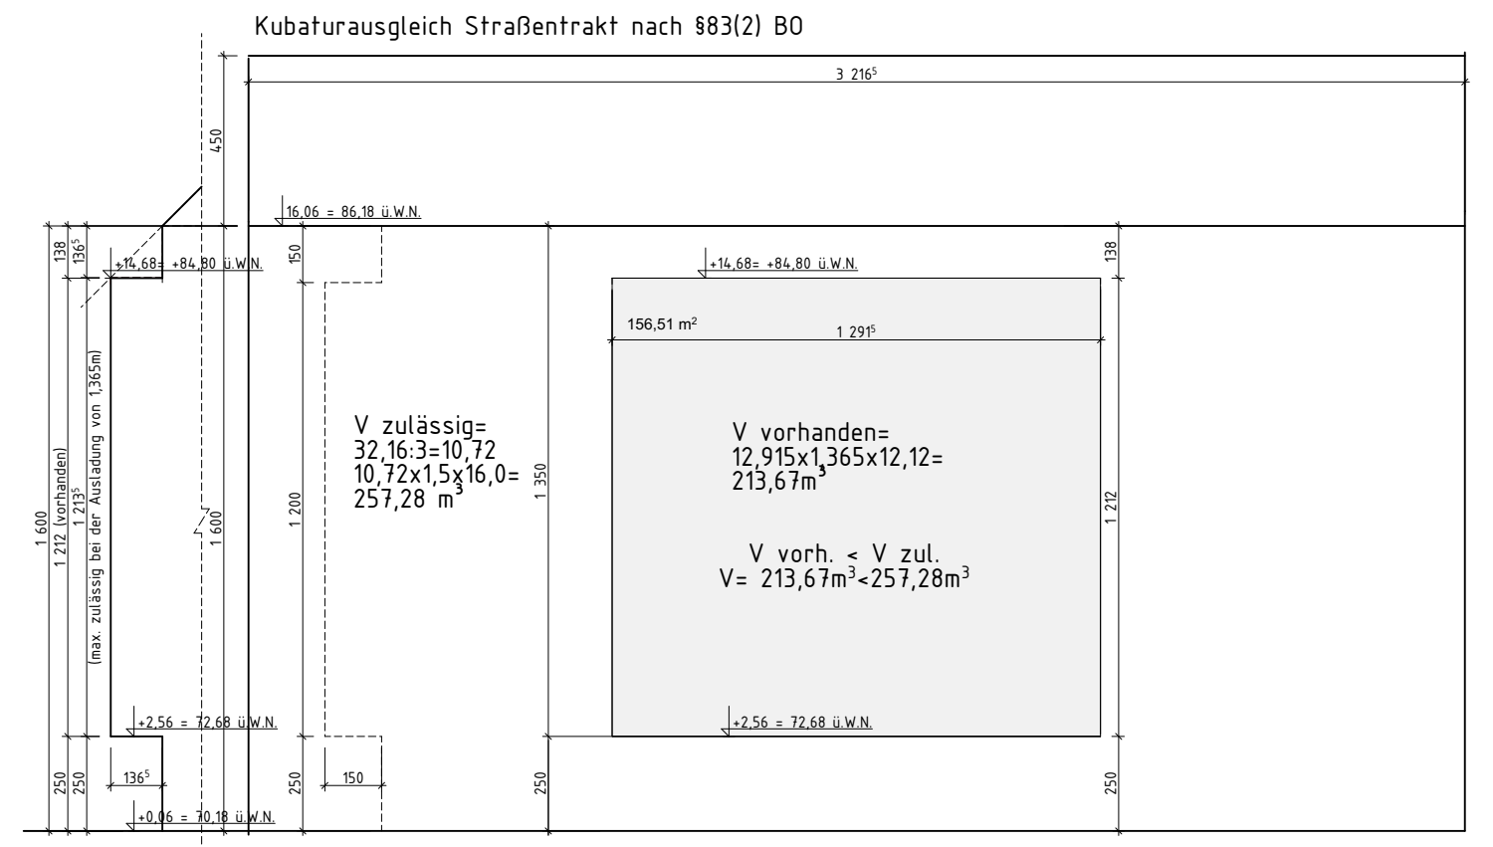

Kubaturausgleich Straßentrakt nach §83(2) BO

V zulässig=
32,16:3=10,72
10,72x1,5x16,0=
257,28 m³

V vorhanden=
12,915x1,365x12,12=
213,67m³

V vorh. < V zul.
V= 213,67m³<257,28m³

KUBATURAUSGLEICH

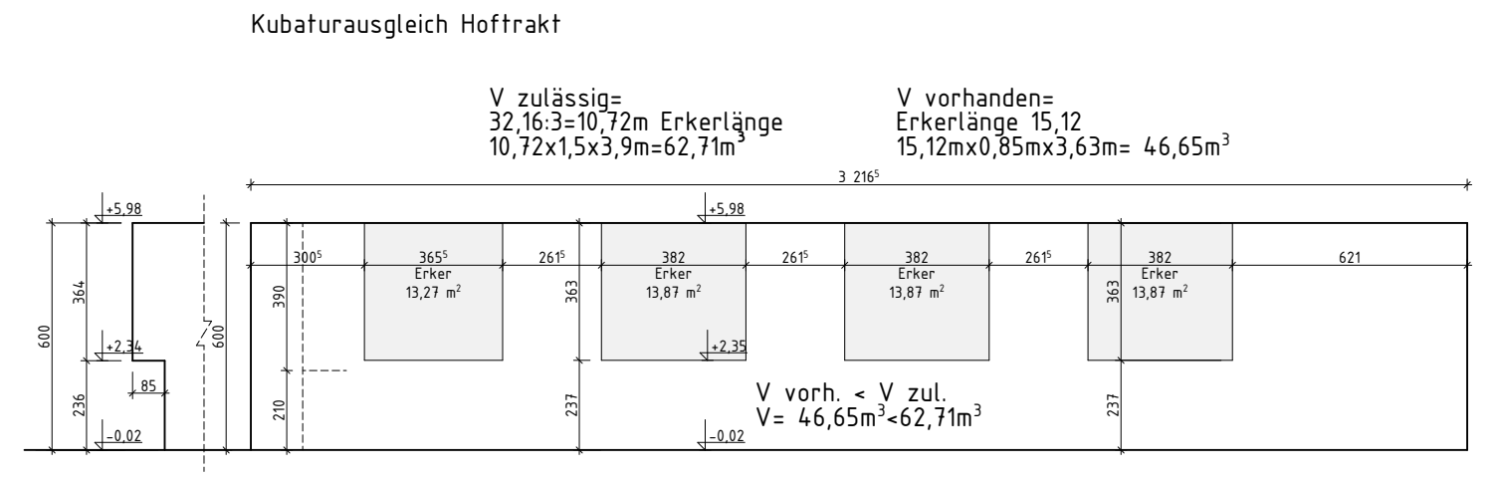

Kubaturausgleich Hoftrakt

V zulässig=
32,16:3=10,72m Erkerlänge
10,72x1,5x3,9m=62,71m³

V vorhanden=
Erkerlänge 15,12
15,12mx0,85mx3,63m= 46,65m³

V vorh. < V zul.
V= 46,65m³<62,71m³

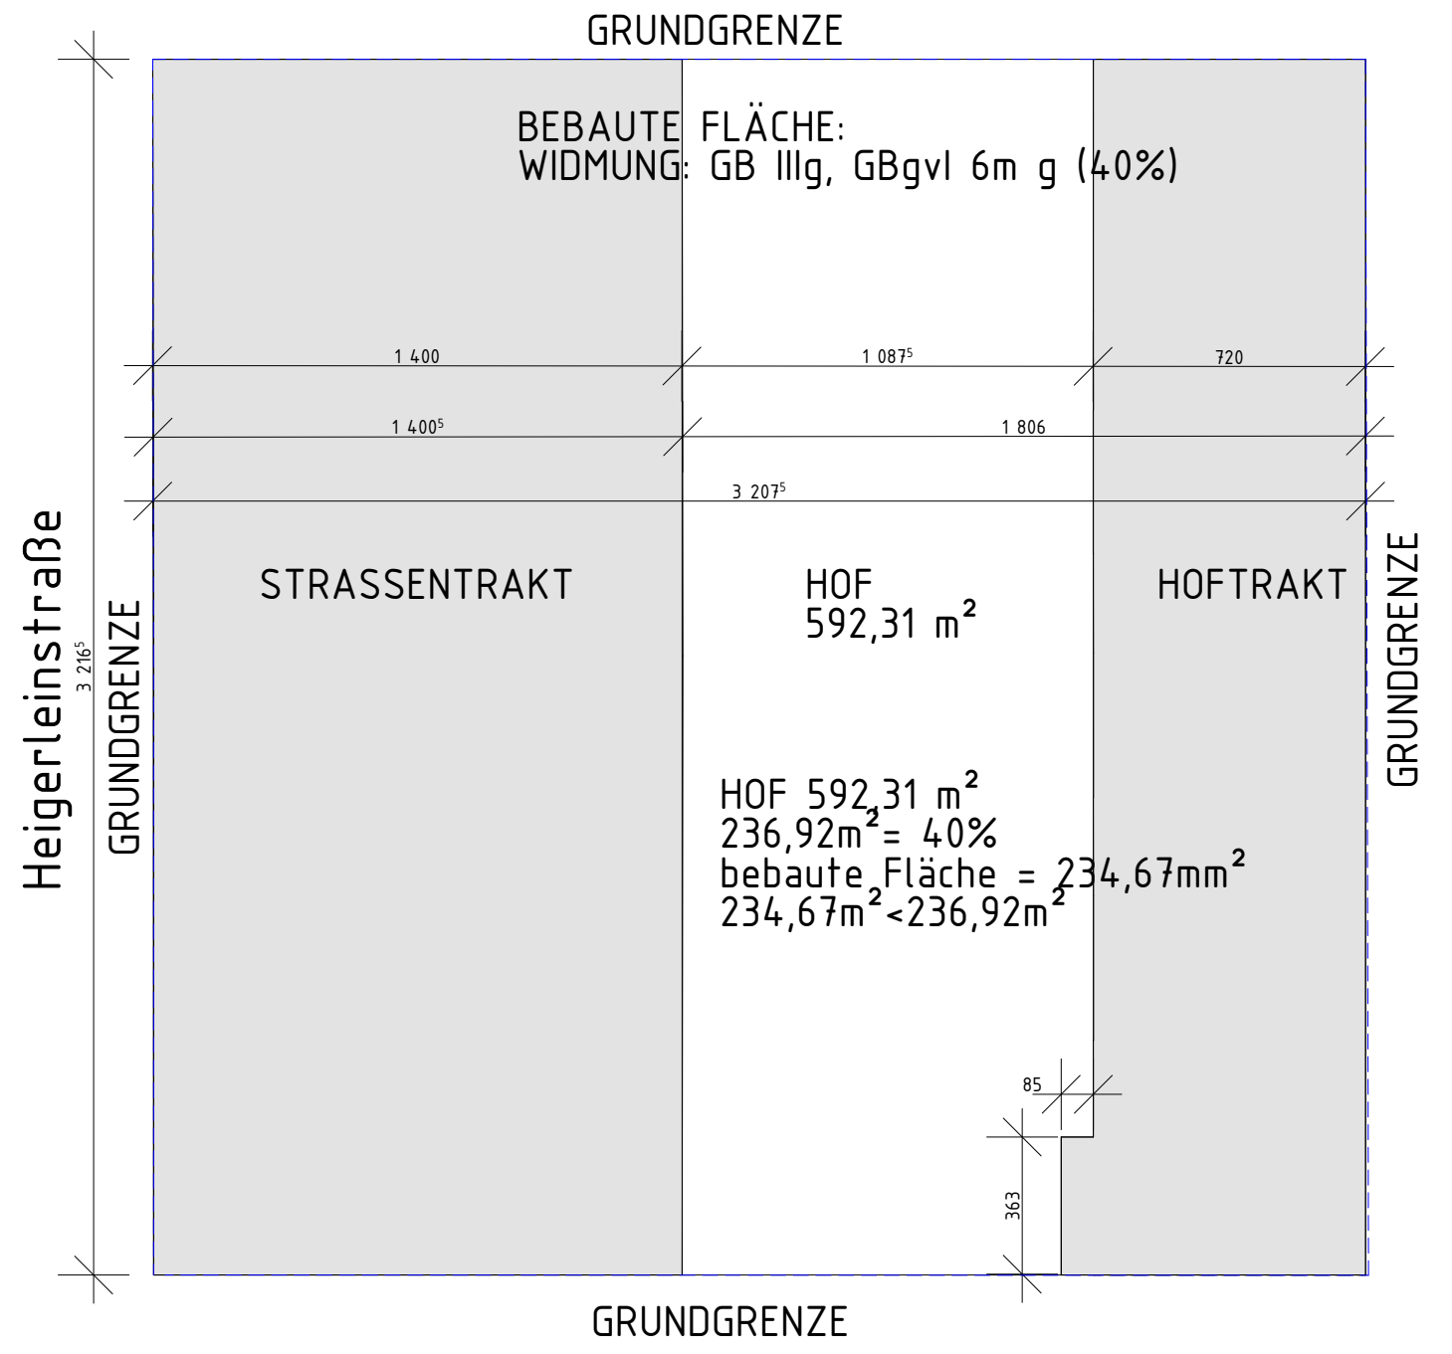

HOF 592,31 m²
236,92m² = 40%
bebaute Fläche = 234,67mm²
234,67m² < 236,92m²

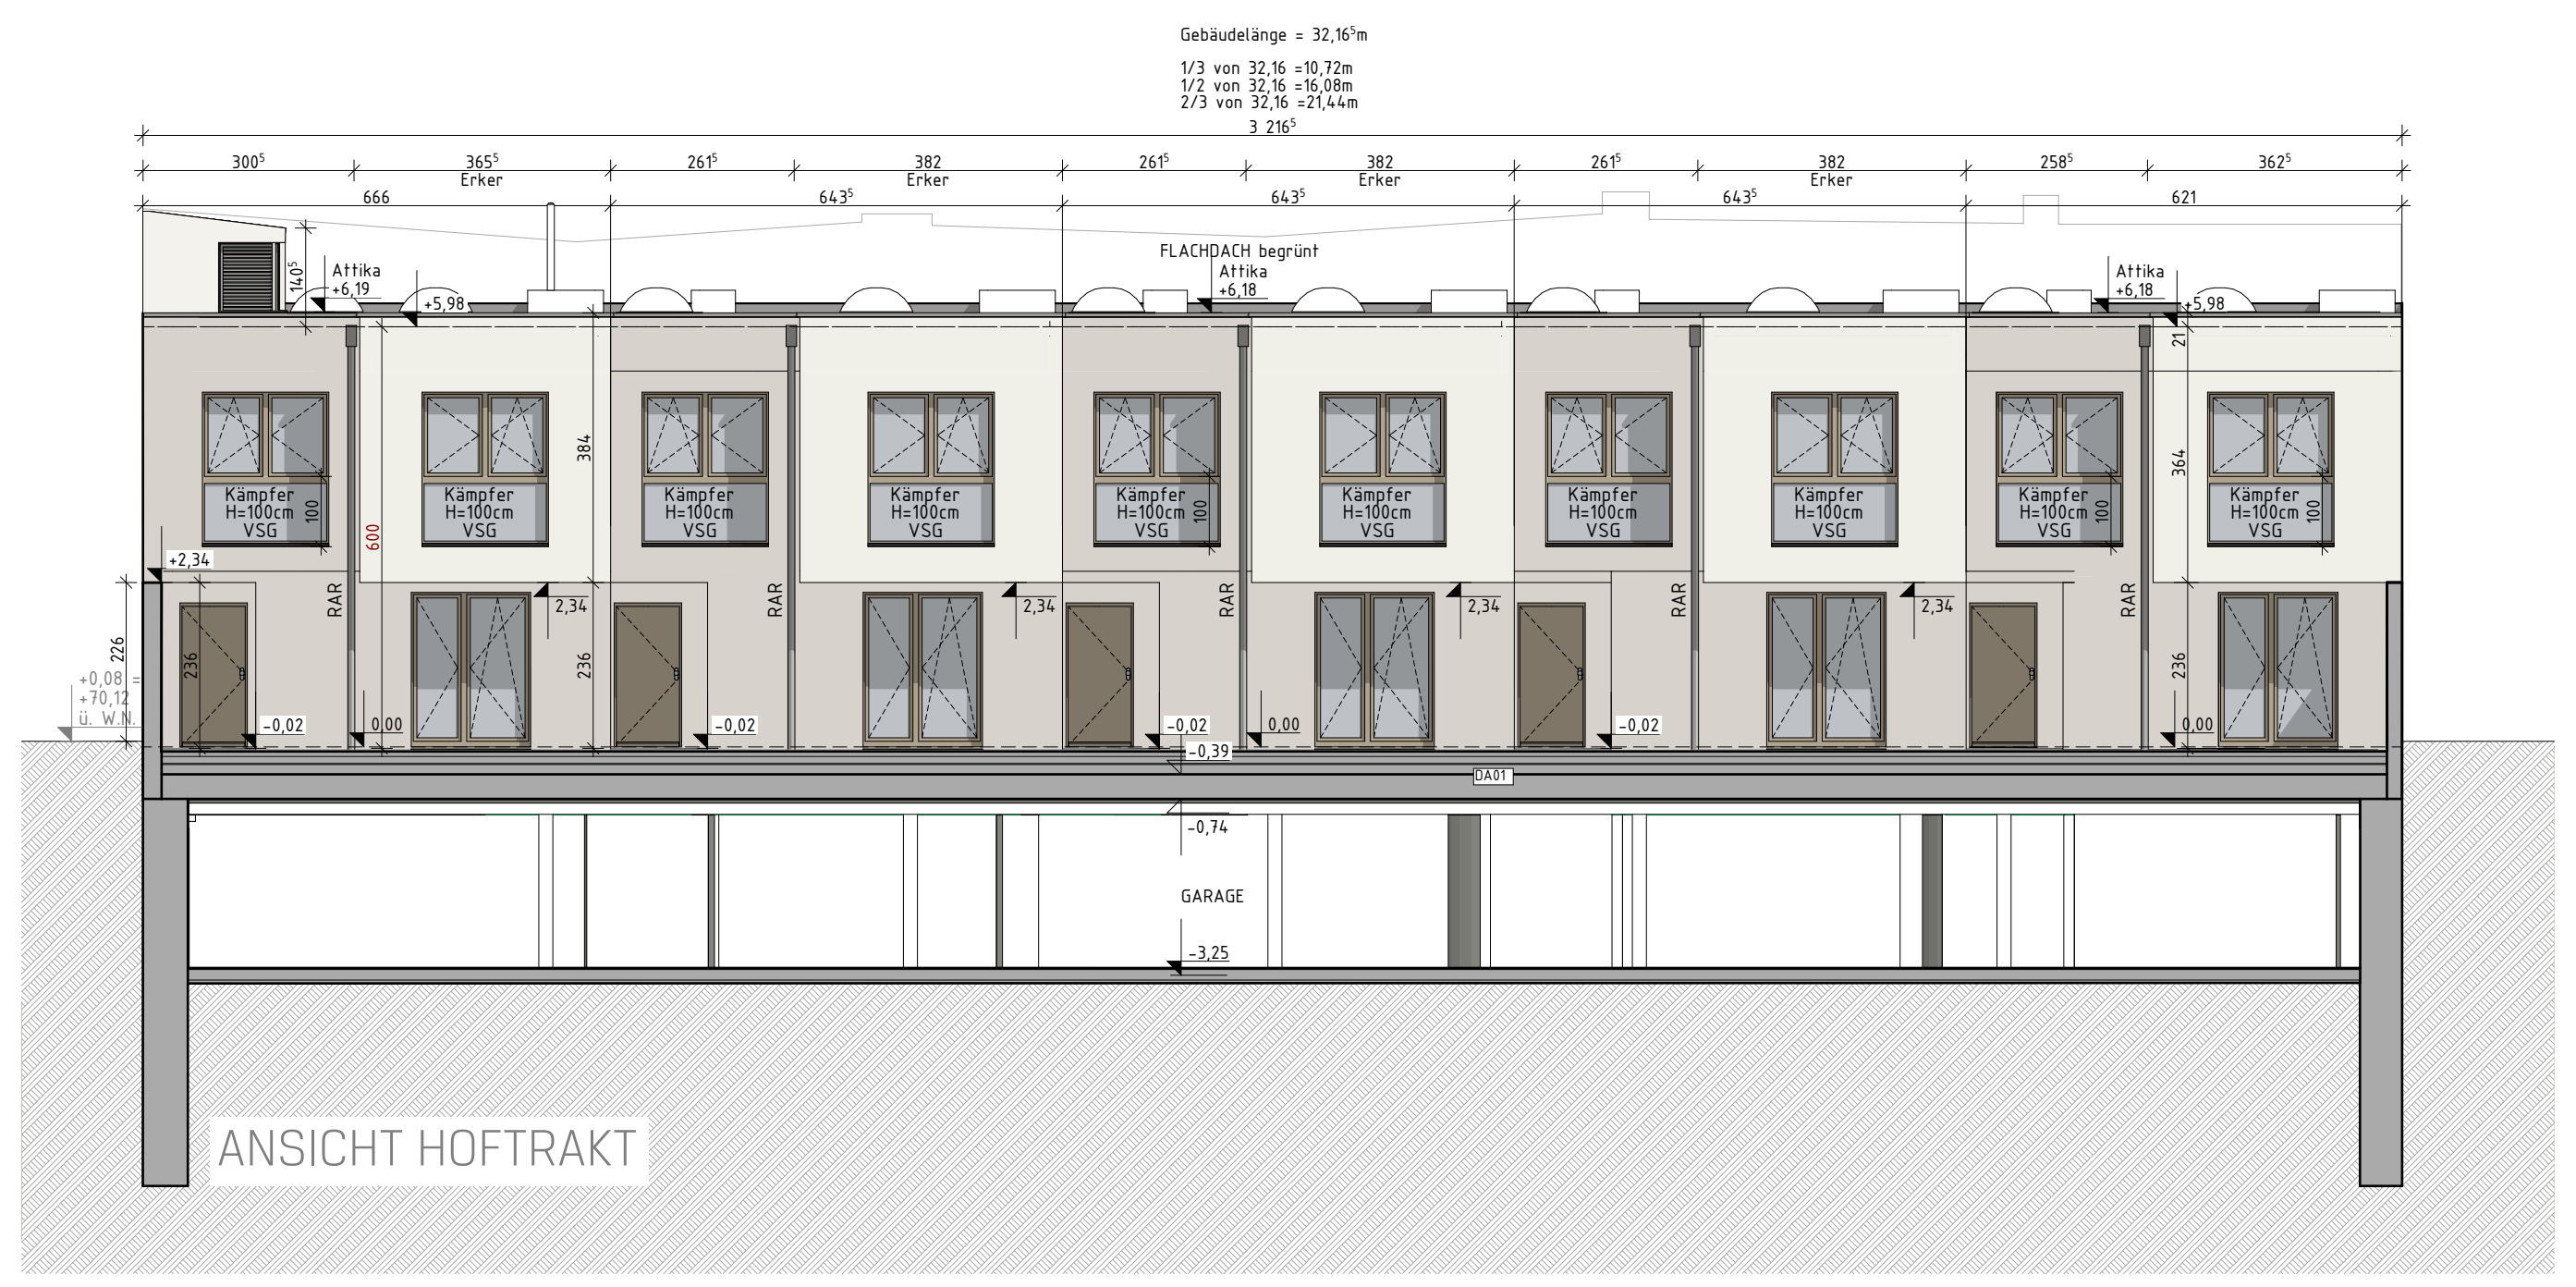

HOFTRAKT. WESTANSICHT

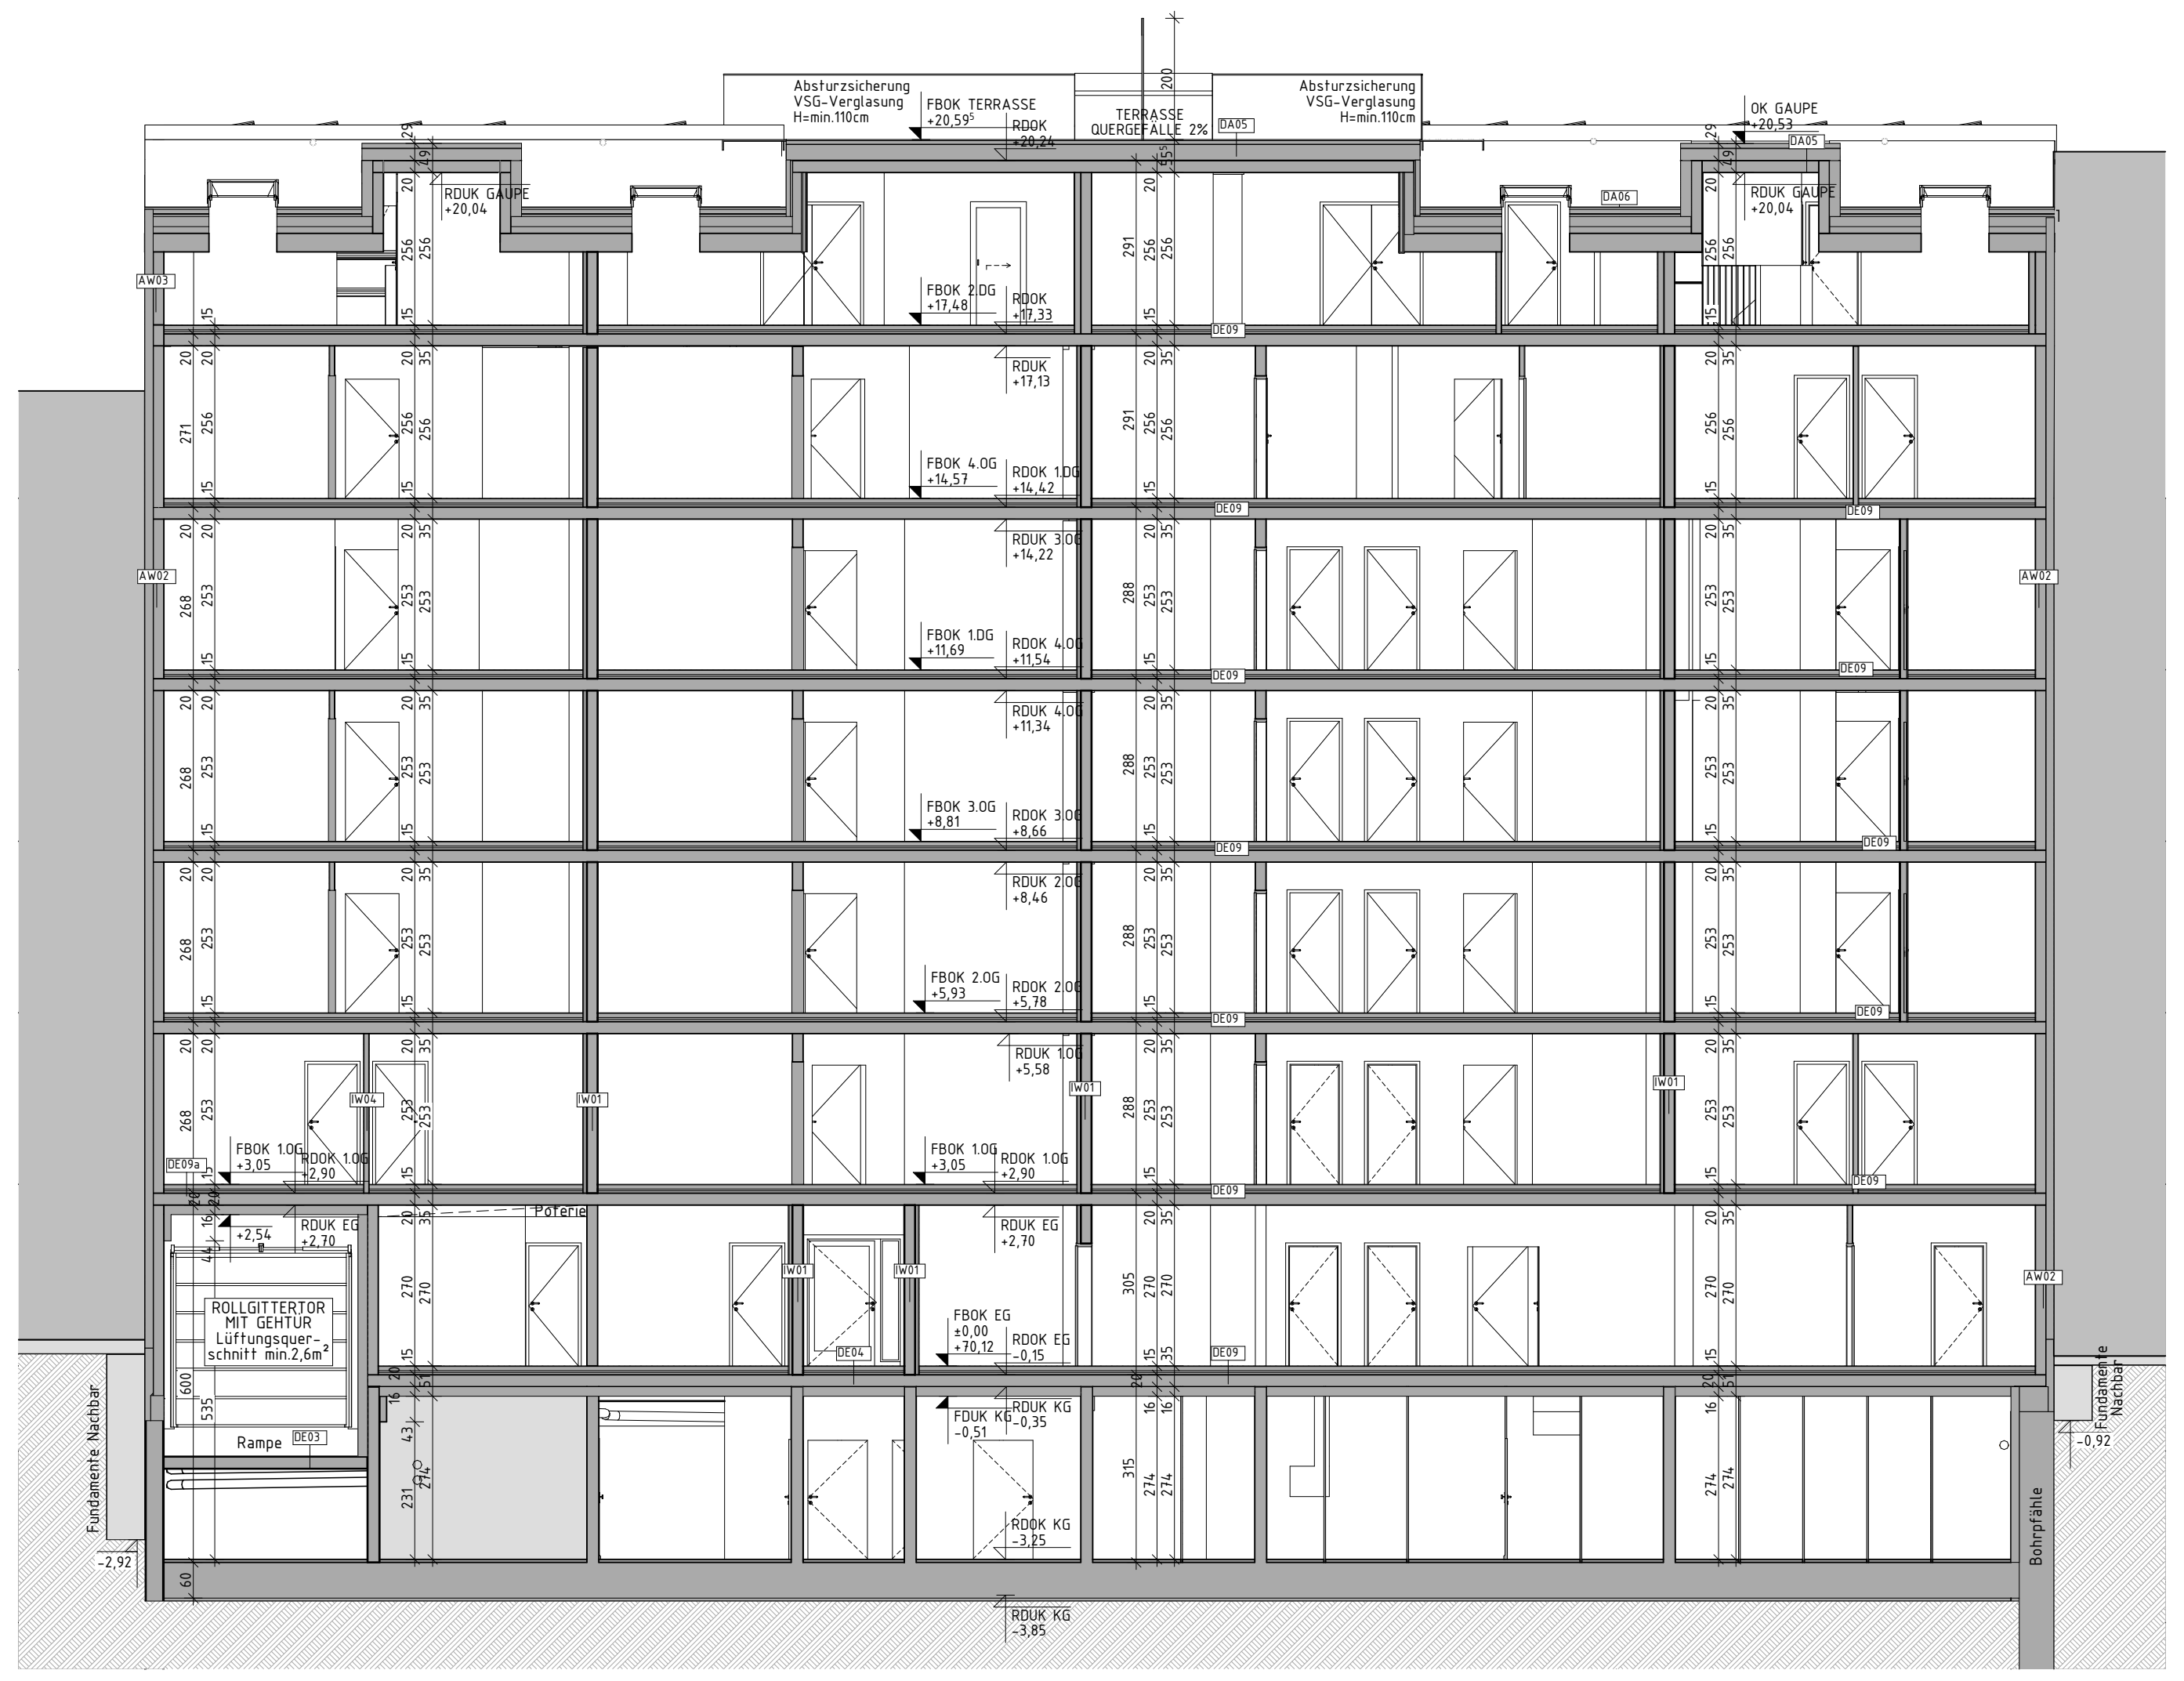

SCHNITT 1-1

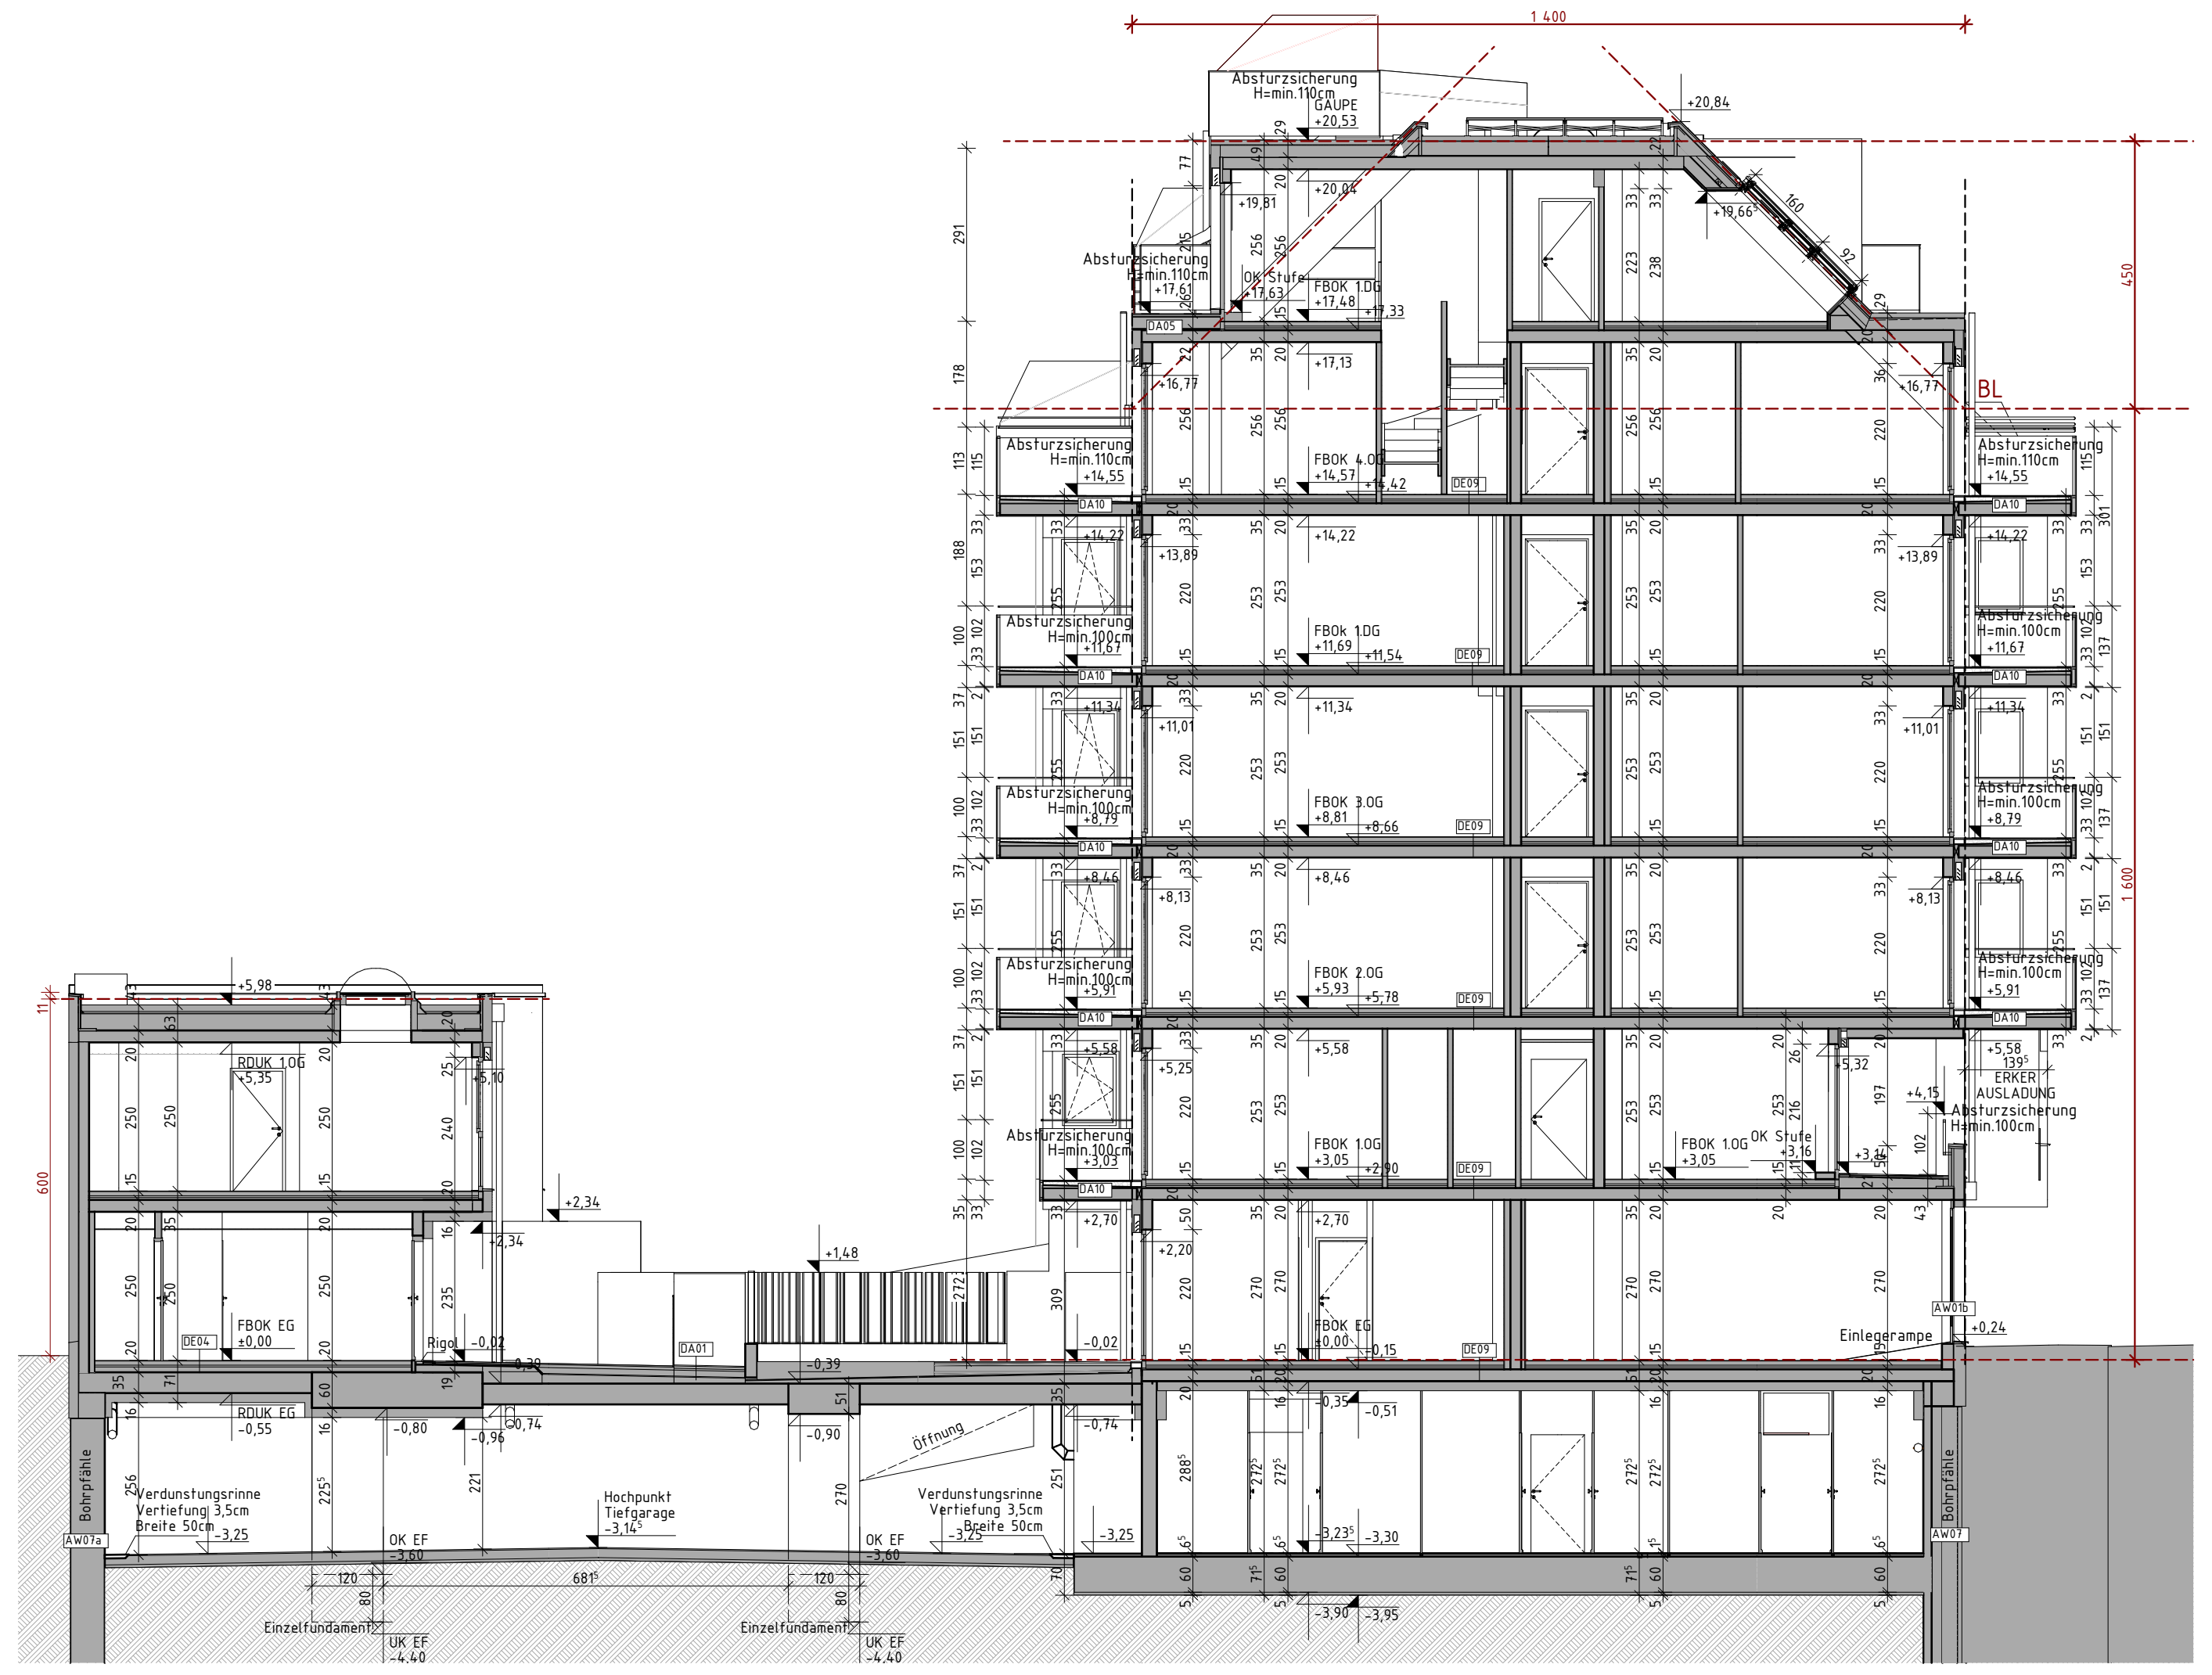

SCHNITT C-C

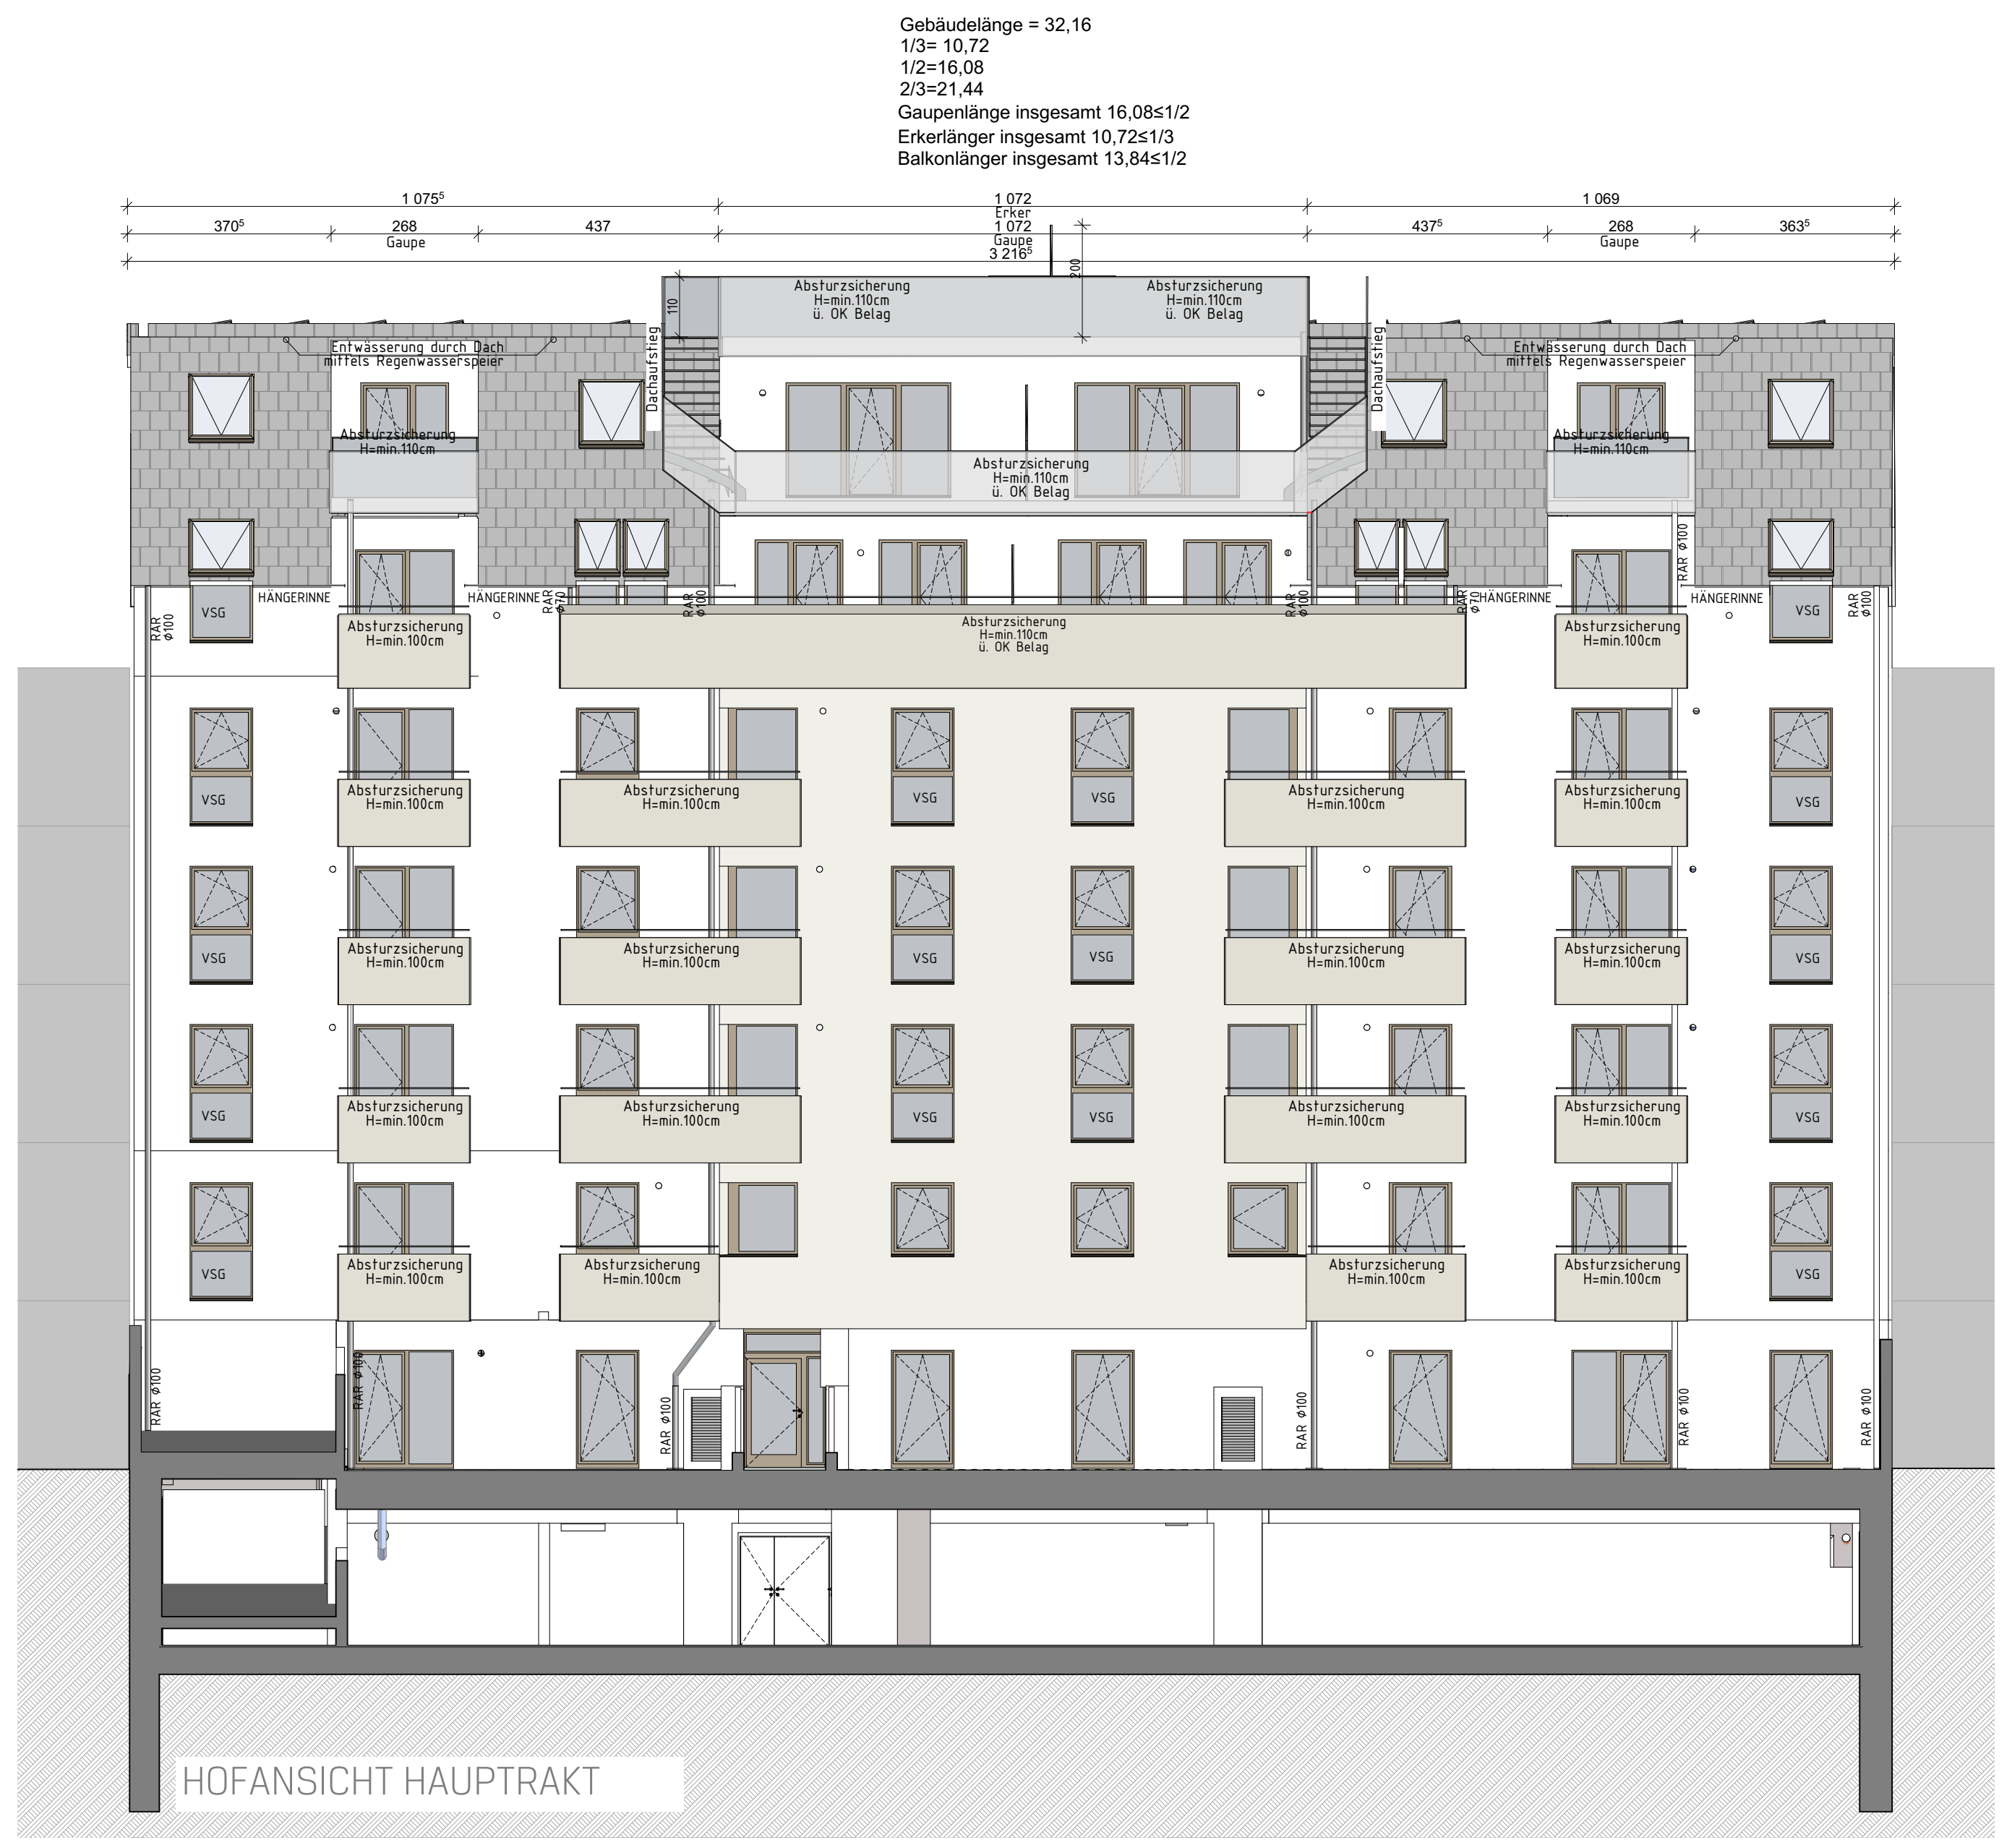

Gebäudelänge = 32,16
1/3= 10,72
1/2=16,08
2/3=21,44
Gaupenlänge insgesamt 16,08≤1/2
Erkerlänger insgesamt 10,72≤1/3
Balkonlänger insgesamt 13,84≤1/2

STRASSENTRAKT. OSTANSICHT

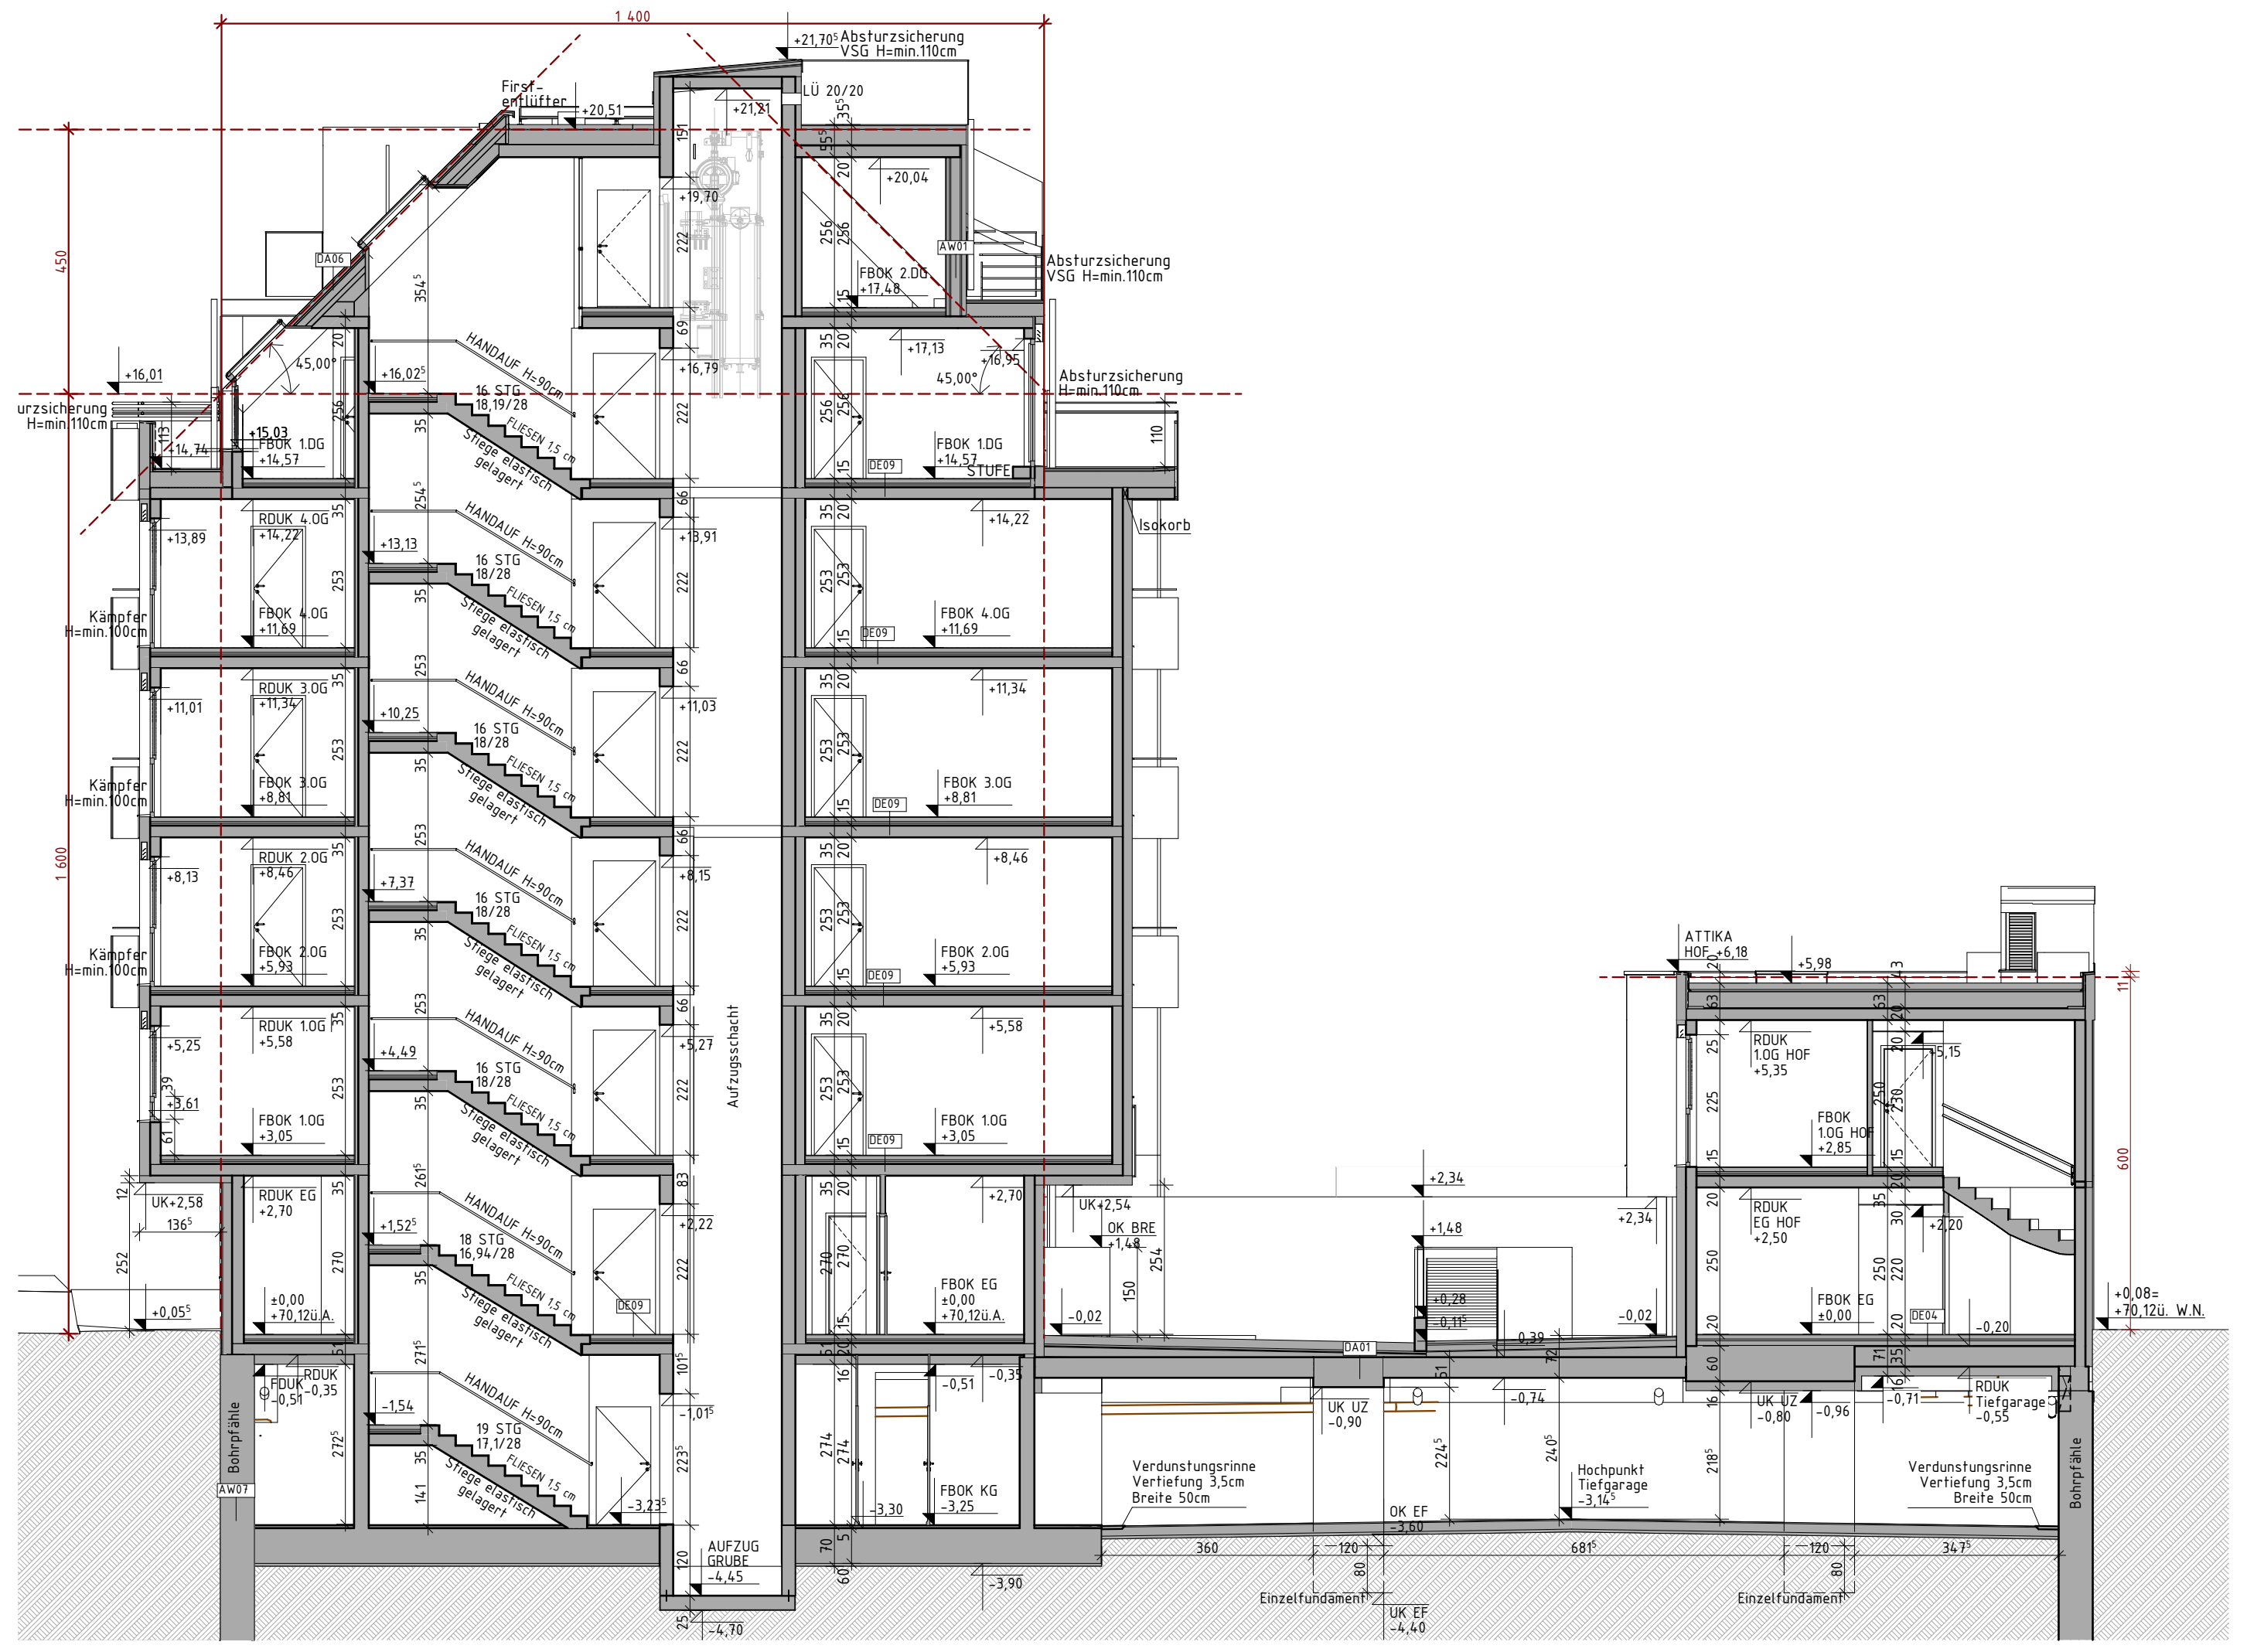

SCHNITT A-A

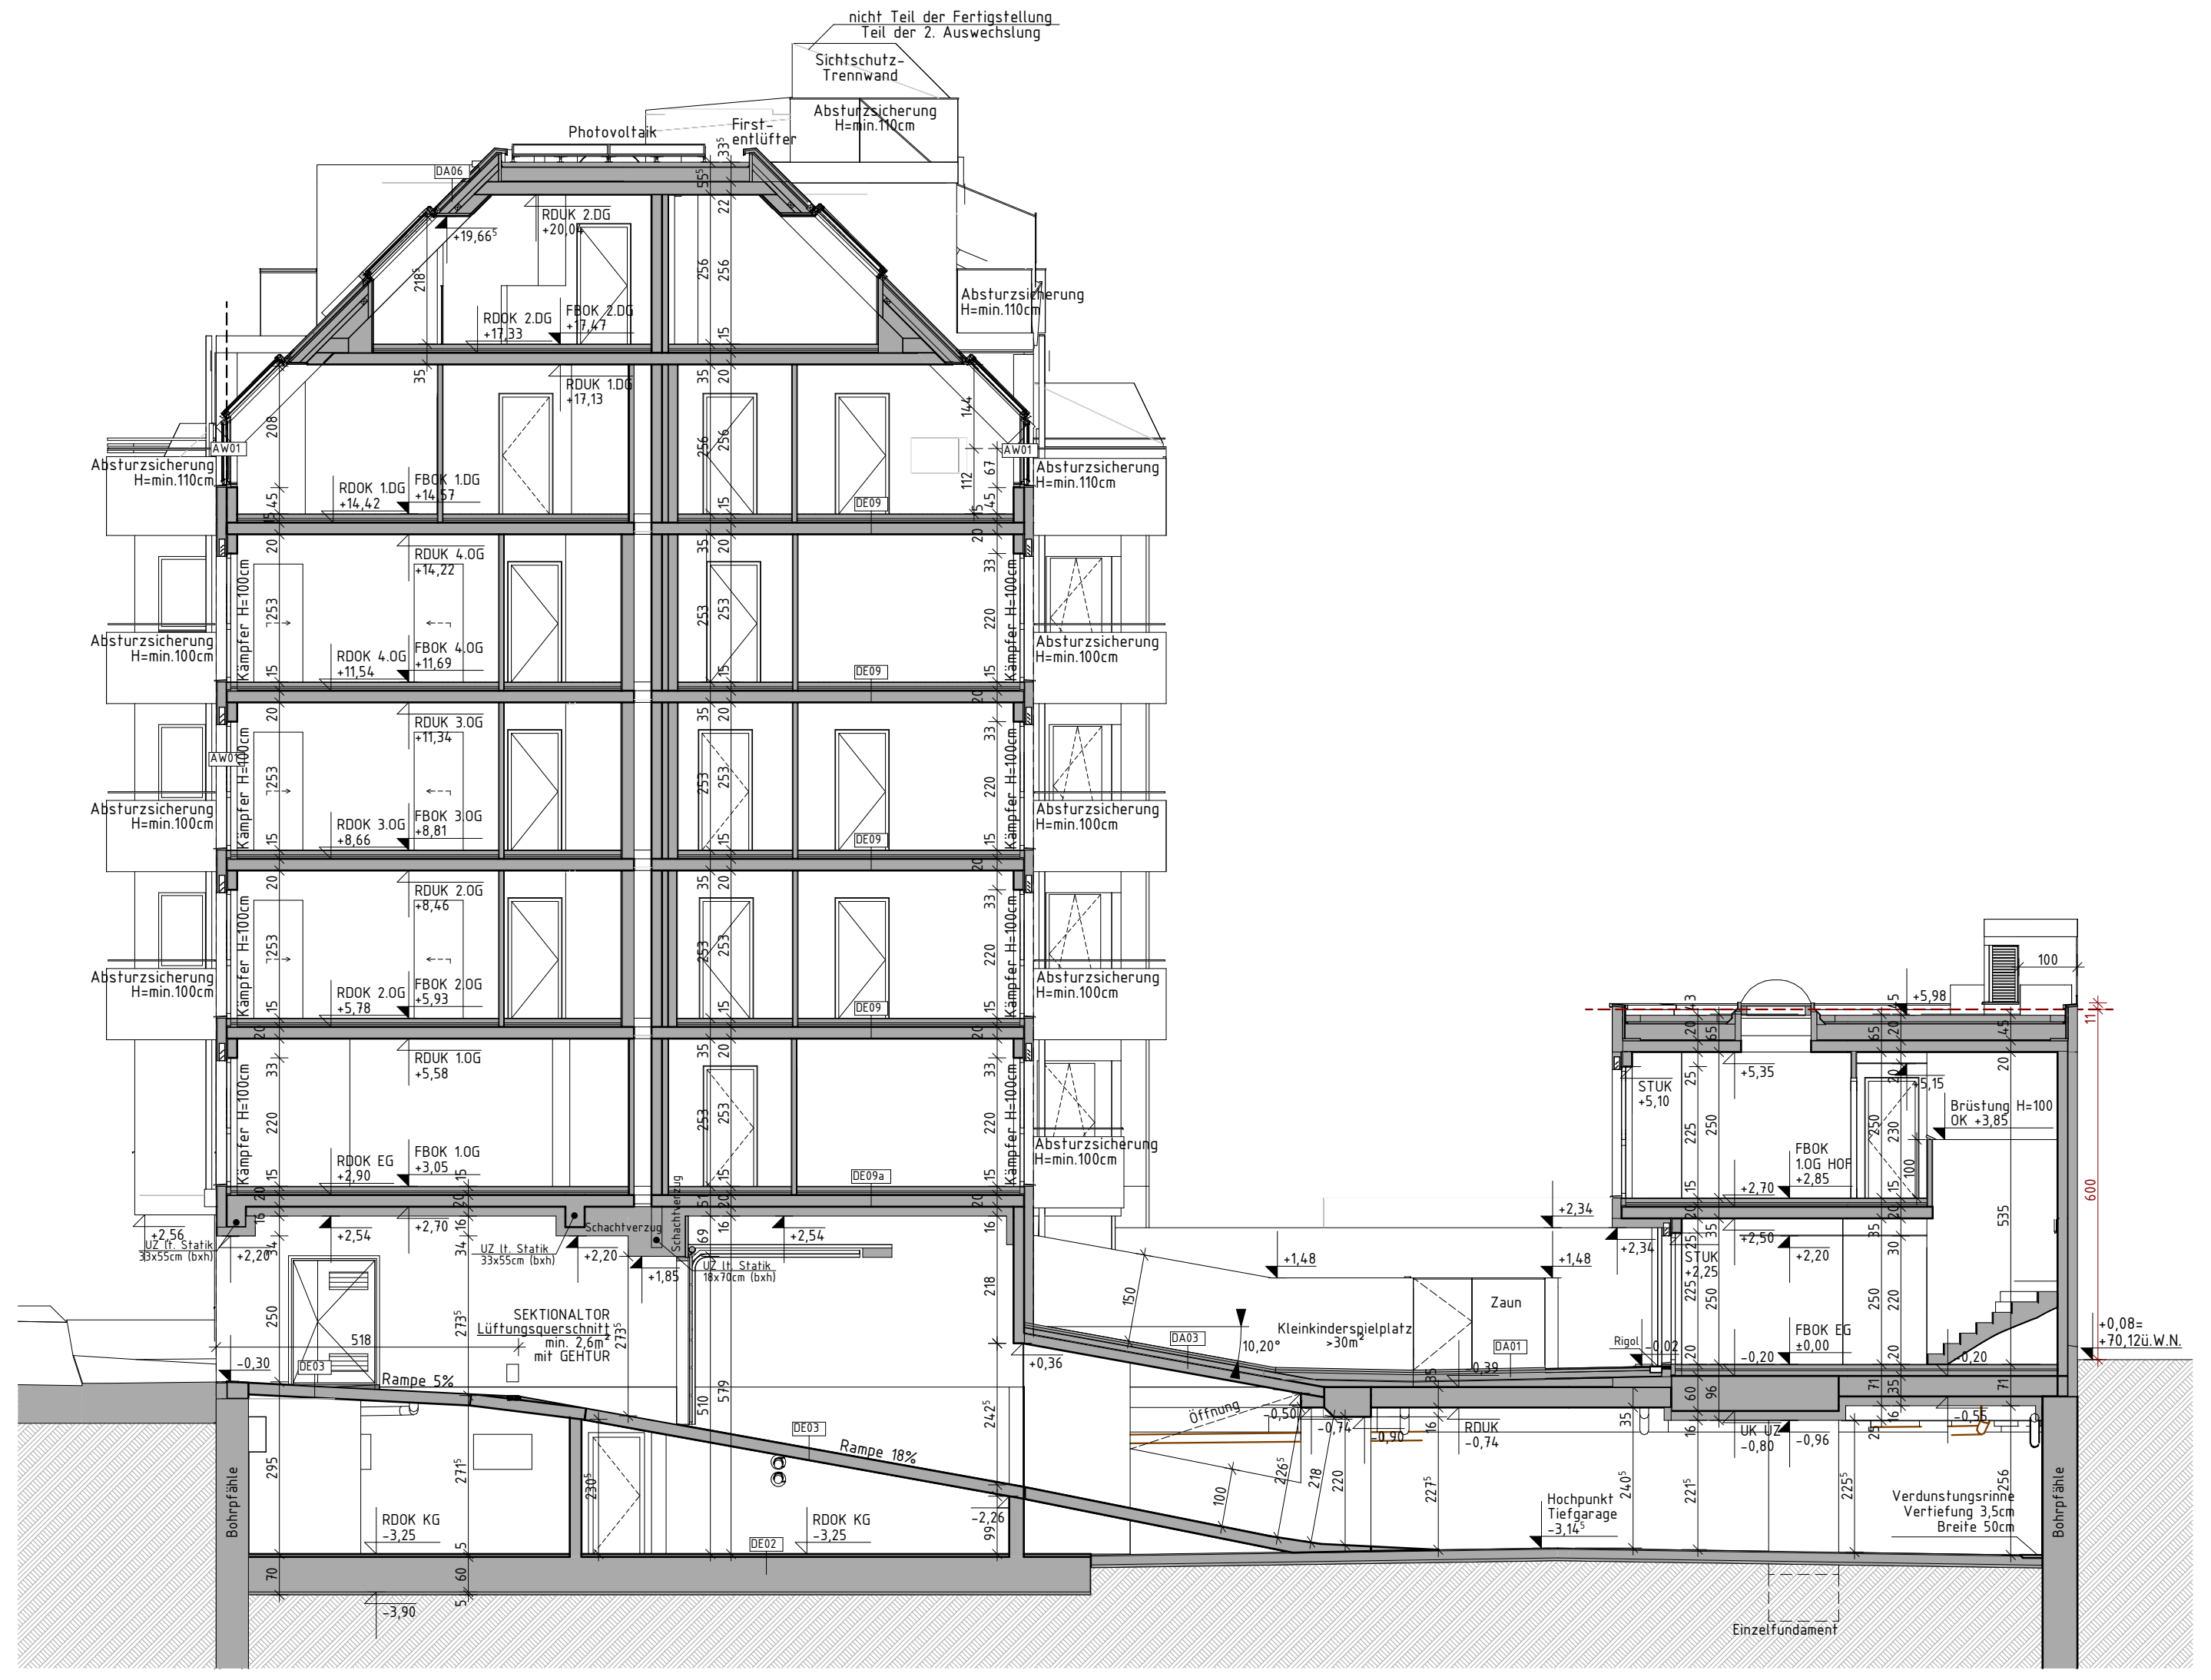

SCHNITT B-B

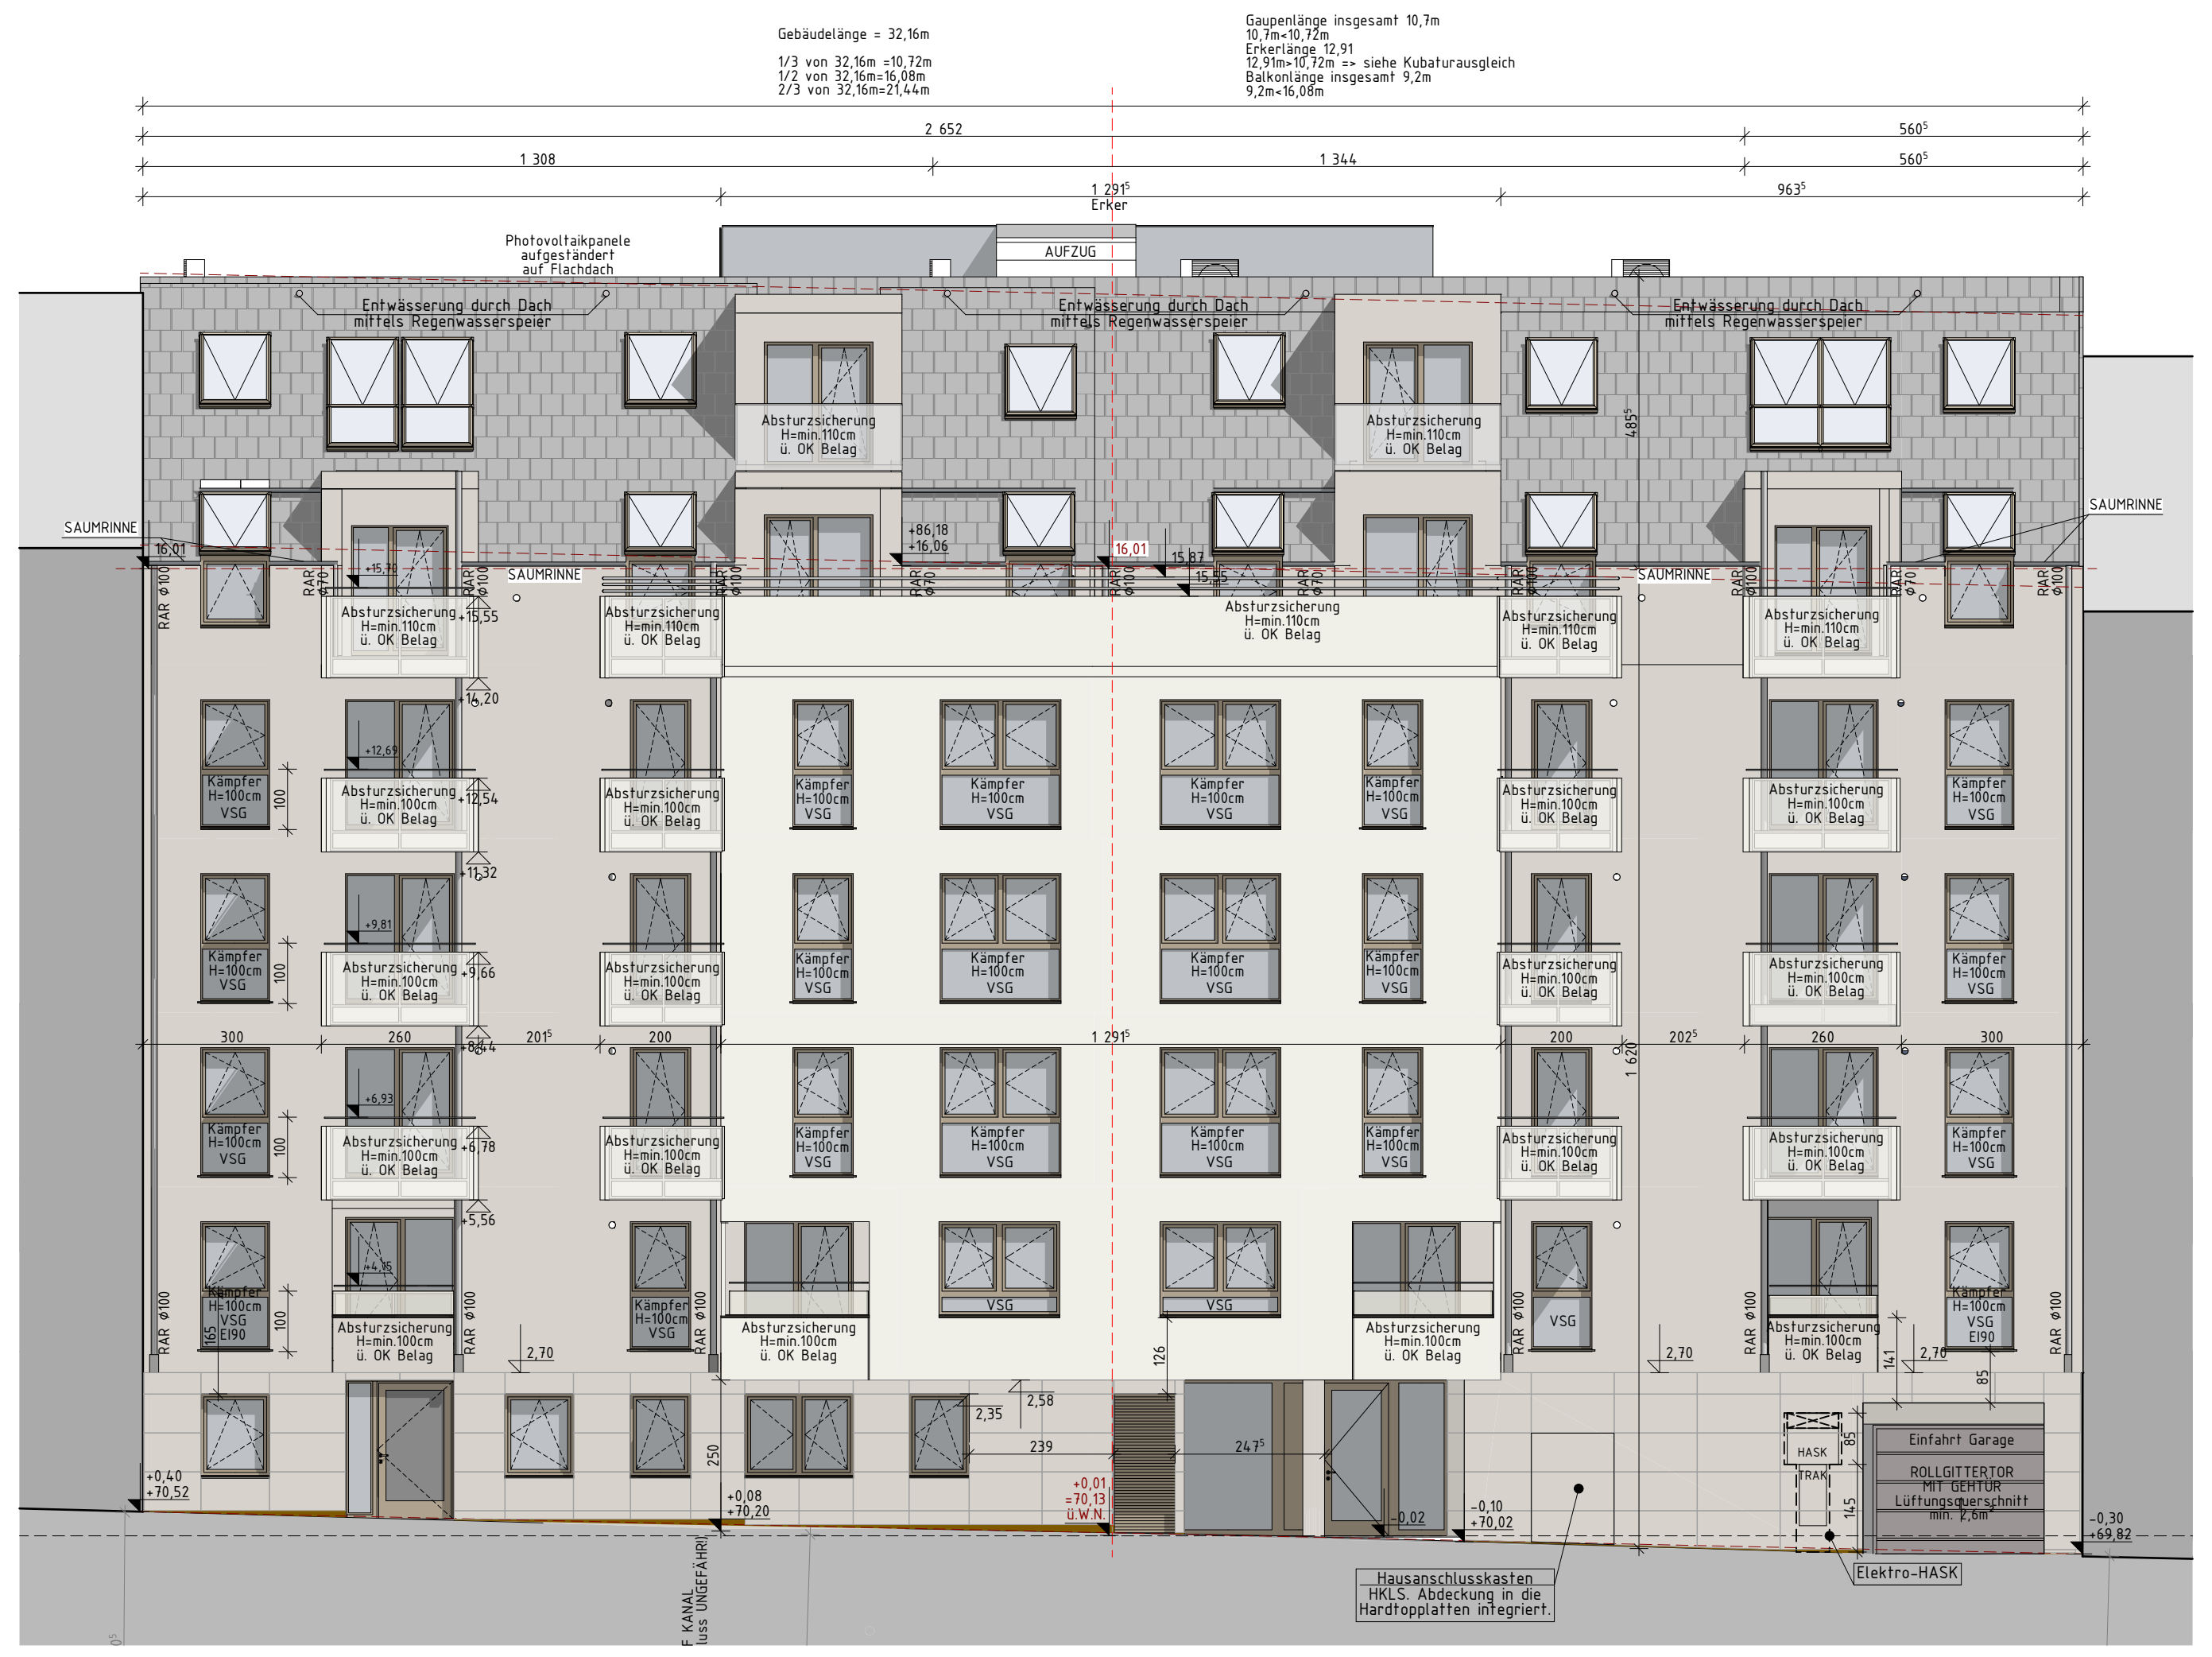

Gebäudelänge = 32,16m

1/3 von 32,16m =10,72m
1/2 von 32,16m=16,08m
2/3 von 32,16m=21,44m

Gaupenlänge insgesamt 10,7m
10,7m<10,72m
Erkerlänge 12,91
12,91m>10,72m => siehe Kubaturausgleich
Balkonlänge insgesamt 9,2m
9,2m<16,08m

STRASSENTRAKT. WESTANSICHT HEIGERLEINSTRASSE