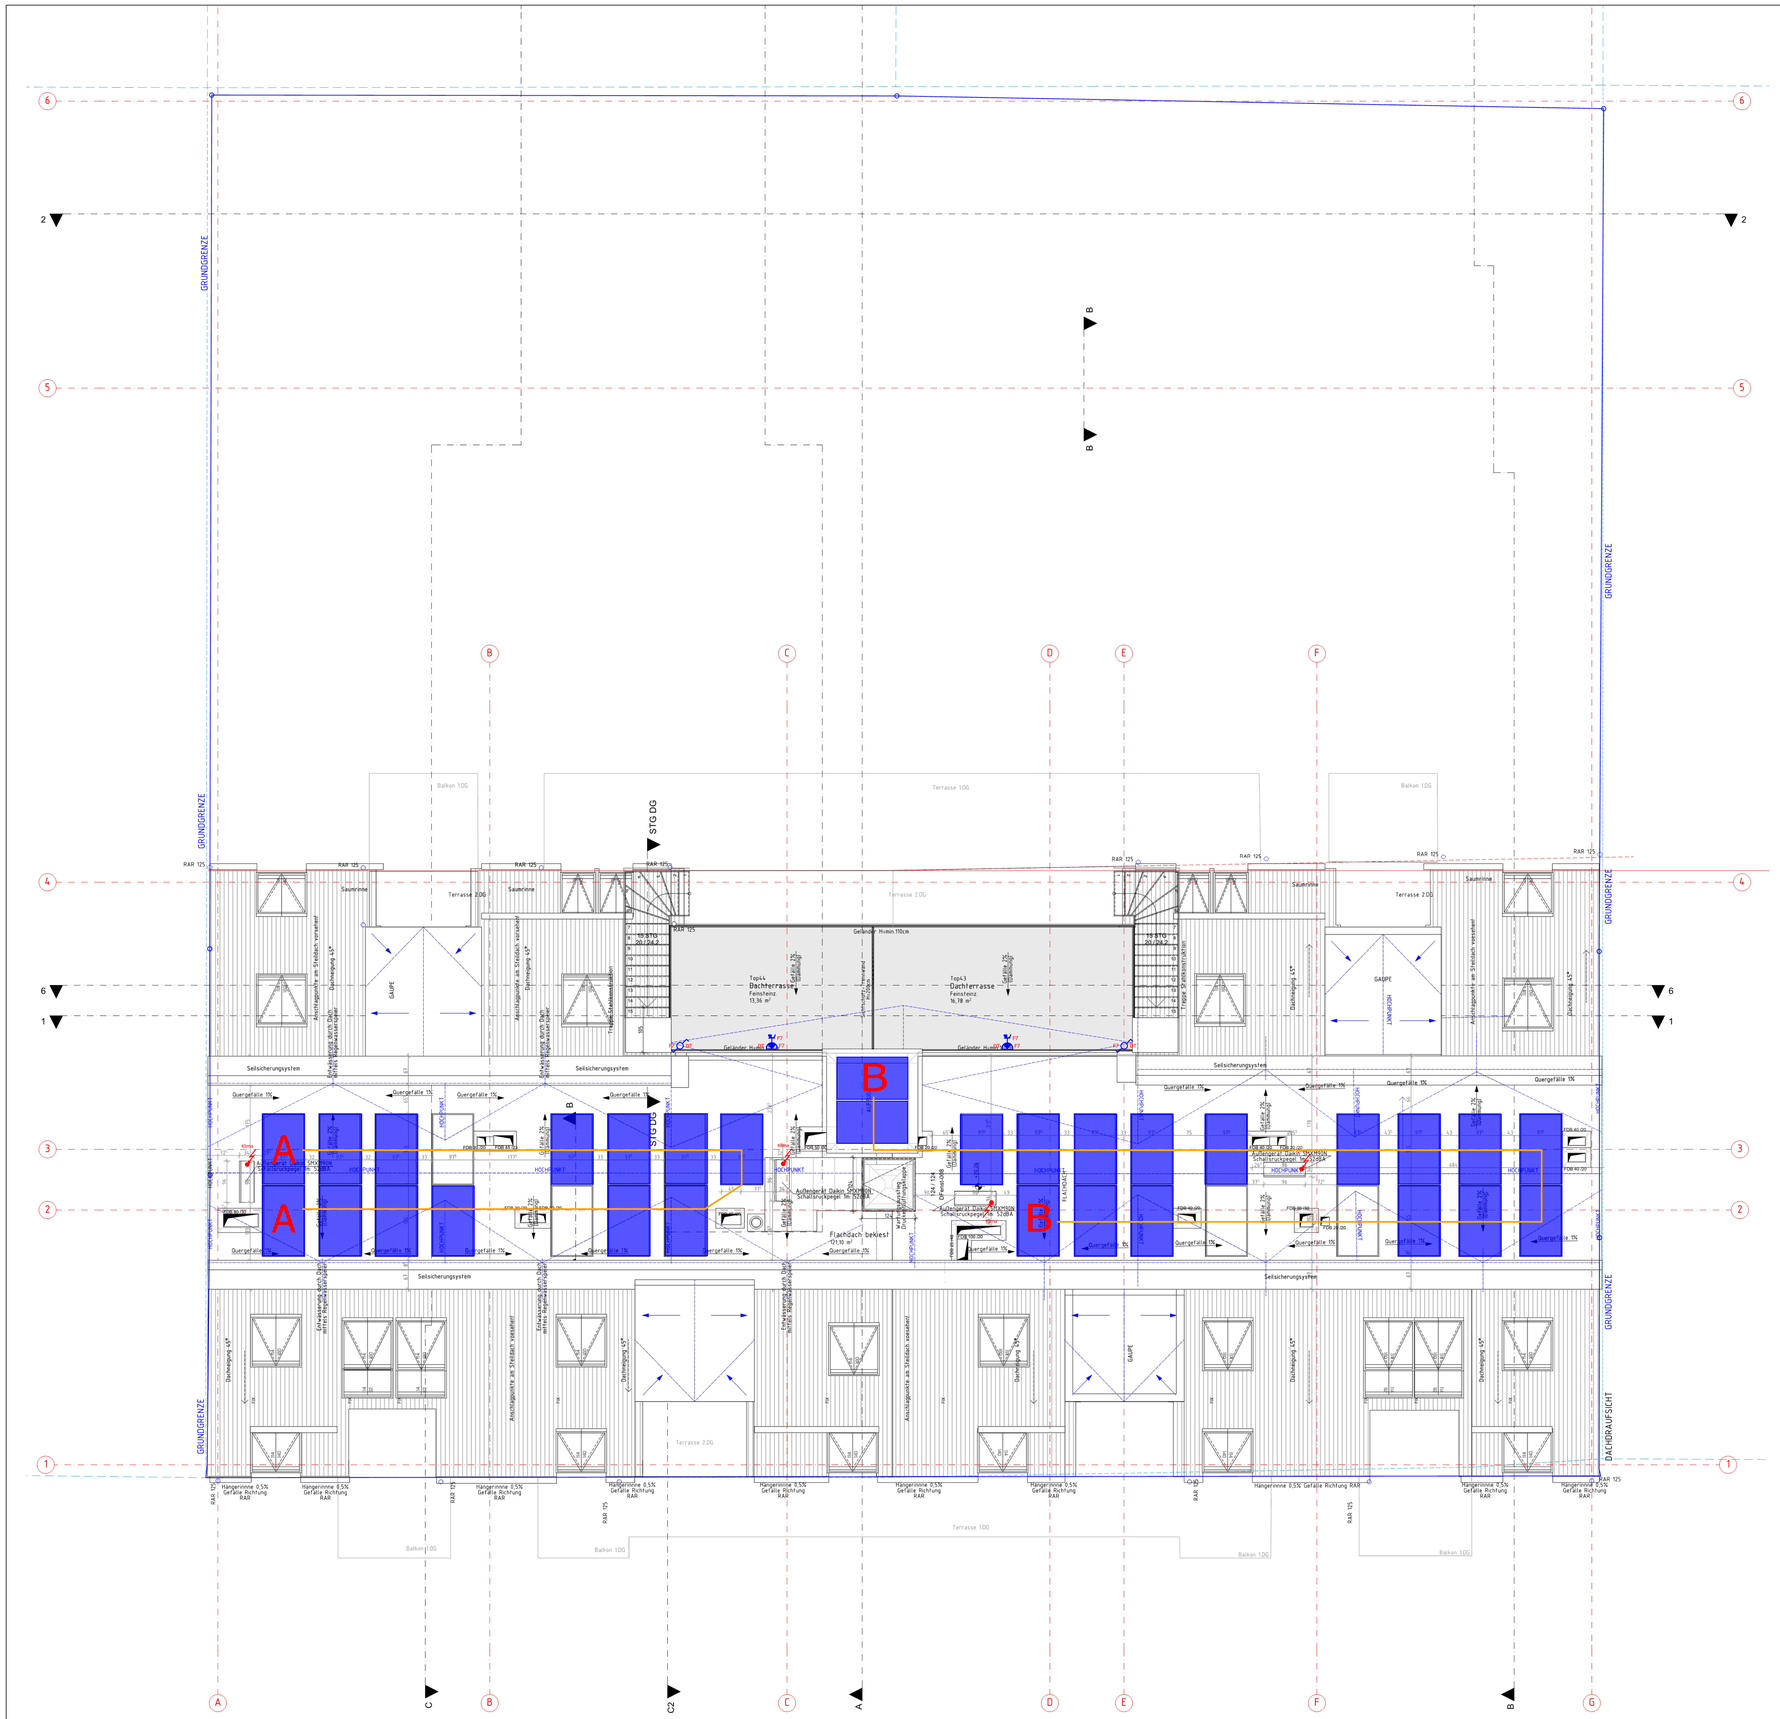


ELEKTROINSTALLATION	Objekt Nr.: DDS	Änderungen	
		Datum	Vis.
Planhintergrund A2017-04_Heigerlein_PPL_DD_Index 3_20210702	**Auftraggeber** Auböck Bau GmbH Drosselstraße 36 4470 Enns	12.10.20 20.04.21 31.05.21 07.07.21 26.08.21	Vis...
Firma: **deg.elektro.gmbh** **Hasnerstraße 97** **1160 Wien**	**Objekt:** Heigerleinstraße 20-22 1160Wien		
	Plan Nr.: VA **Plan Gr.:** A0 **Mst:** 1:50 **Gezeichnet:** Seker **Datum:** 24.08.2020		