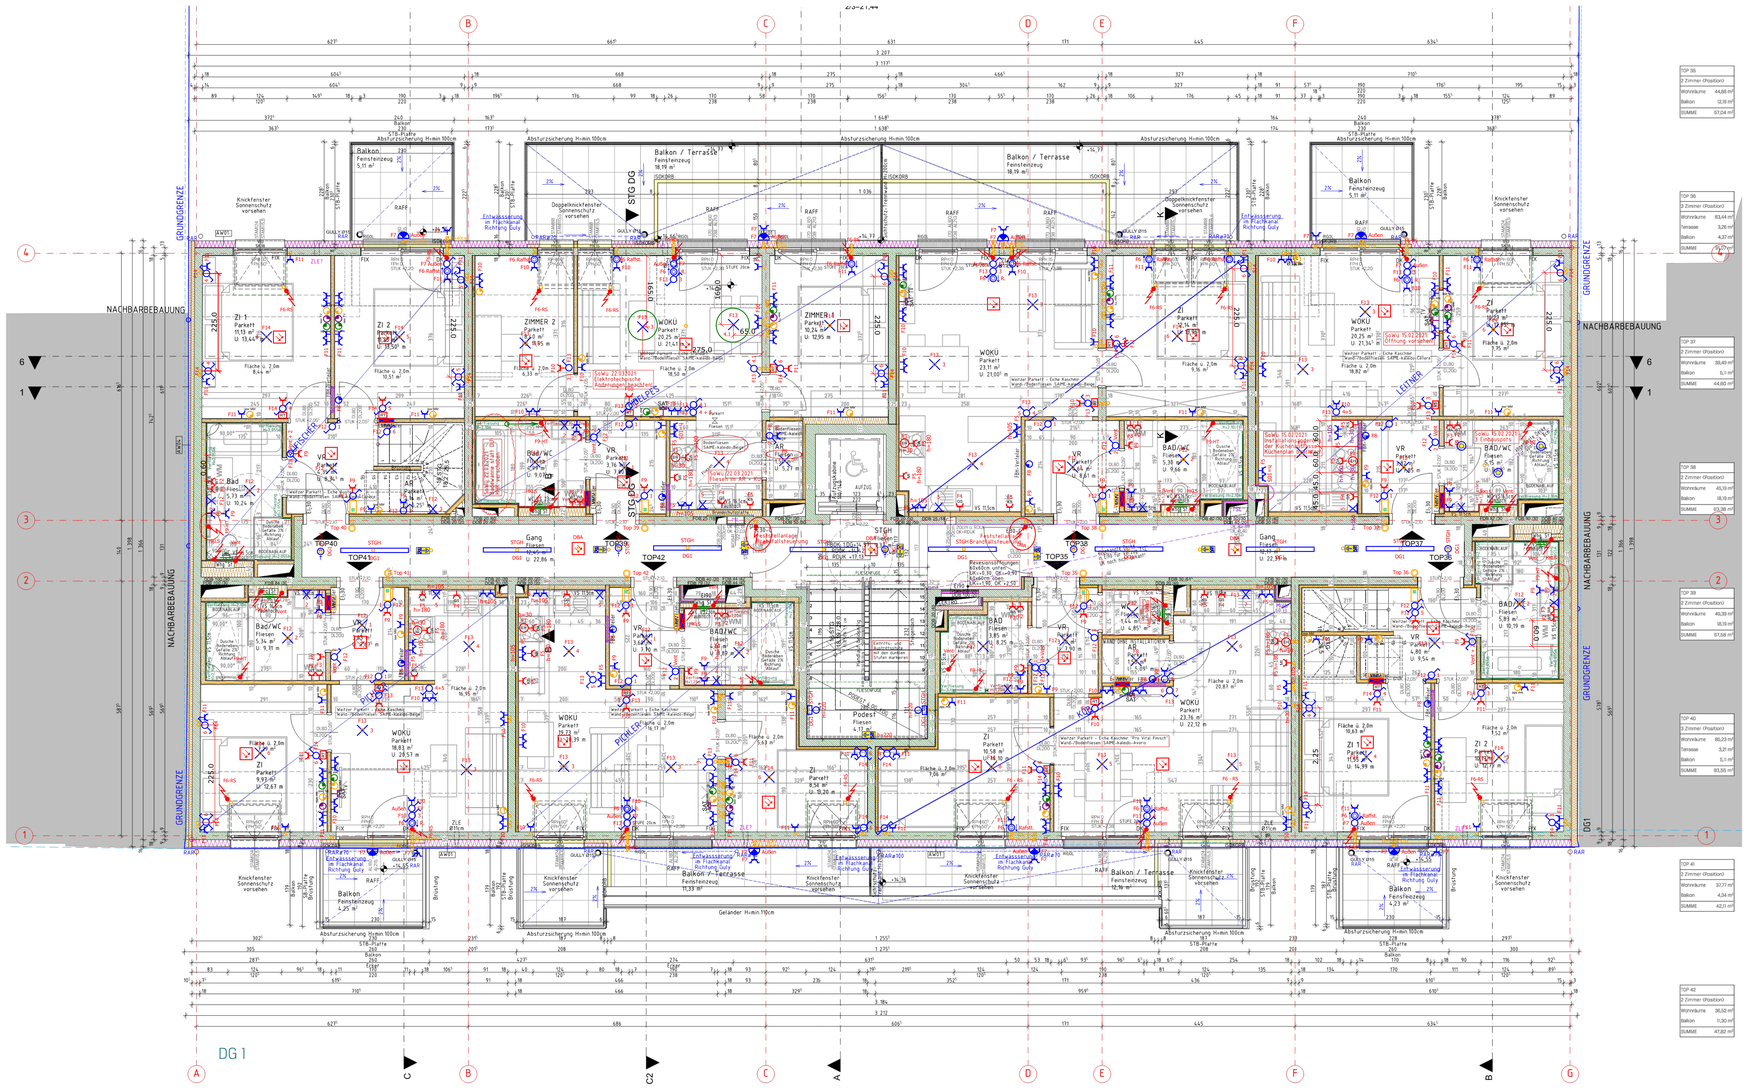


12.10.2020: Einarbeitung der Anmerkungen Fa. ELCONS.

15.10.20: Detailänderung Top 40 Bad.

29.10.20: Auslässe für Brandfallsteuerung nachgetragen.

25.11.20: Grundrissänderung Top 39.

26.11.2020: Beleuchtung im Geländer entfallen.

10.03.2021: Änderungen in Top 39

- Aufbauleuchte Wand
- Ausschalter
- Deckenauslass
- E-Herd
- Elektroanschluss
- Erdung
- Etagenruftaster
- EXIT links
- EXIT rechts
- FL 1x58W geschlossen
- FL Vertikal
- Gegensprechanlage - Video
- Jalousieschalter
- Kreuzschalter
- Leerdose
- Leerdose MM
- Multimedia - Verteiler
- PIR Melder
- Rauchmelder, optischer RMMO
- Raumthermostat
- Serieschalter
- Steckdose
- Steckdose 1-fach
- Steckdose 2-fach
- Steckdose allgmein
- Steckdose Dampfabzug
- Steckdose Geschirrspüler
- Steckdose Kühlschrank
- Steckdose Mikrowelle
- Steckdose mit Abdeckung
- Steckdosen 2-fach horizontal
- Telefonleerdose
- TV Leerdose
- TV Steckdose
- Unterverteilung
- Wandauslass
- Wechselschalter
- Auslass 180cm
- Auslass 40cm
- Betondose 2f.
- Betondose 3f.
- Betondose 7cm
- Betondose-Kombi V2
- Kombi Waschmaschine/Trockner

ELEKTROINSTALLATION	Objekt Nr.: DG1	Änderungen
		Datum / Vis.
Planhintergrund A2017-04_Heigerlein_PPL_DD_20210527	**Auftraggeber** Aubock Bau GmbH Drosselstraße 36 4470 Enns	24.08.20 26.08.20 10.09.20 12.10.20 15.10.20 20.10.20 29.10.20 27.11.20 25.11.20 03.12.20 28.01.21 02.03.21 10.03.21 15.03.21 17.03.21 22.03.21 20.04.21 20.05.21 31.05.21 06.10.23
Firma: **deg.elektro.gmbh** **Hanneristraße 97** **1160 Wien**	**Objekt:** Heigerleinstraße 20-22 1160Wien	
	Plan Nr.: A **Plan Gr.:** A0 **Mst:** 1:50 **Gezeichnet:** Seker **Datum:** 24.08.2020	