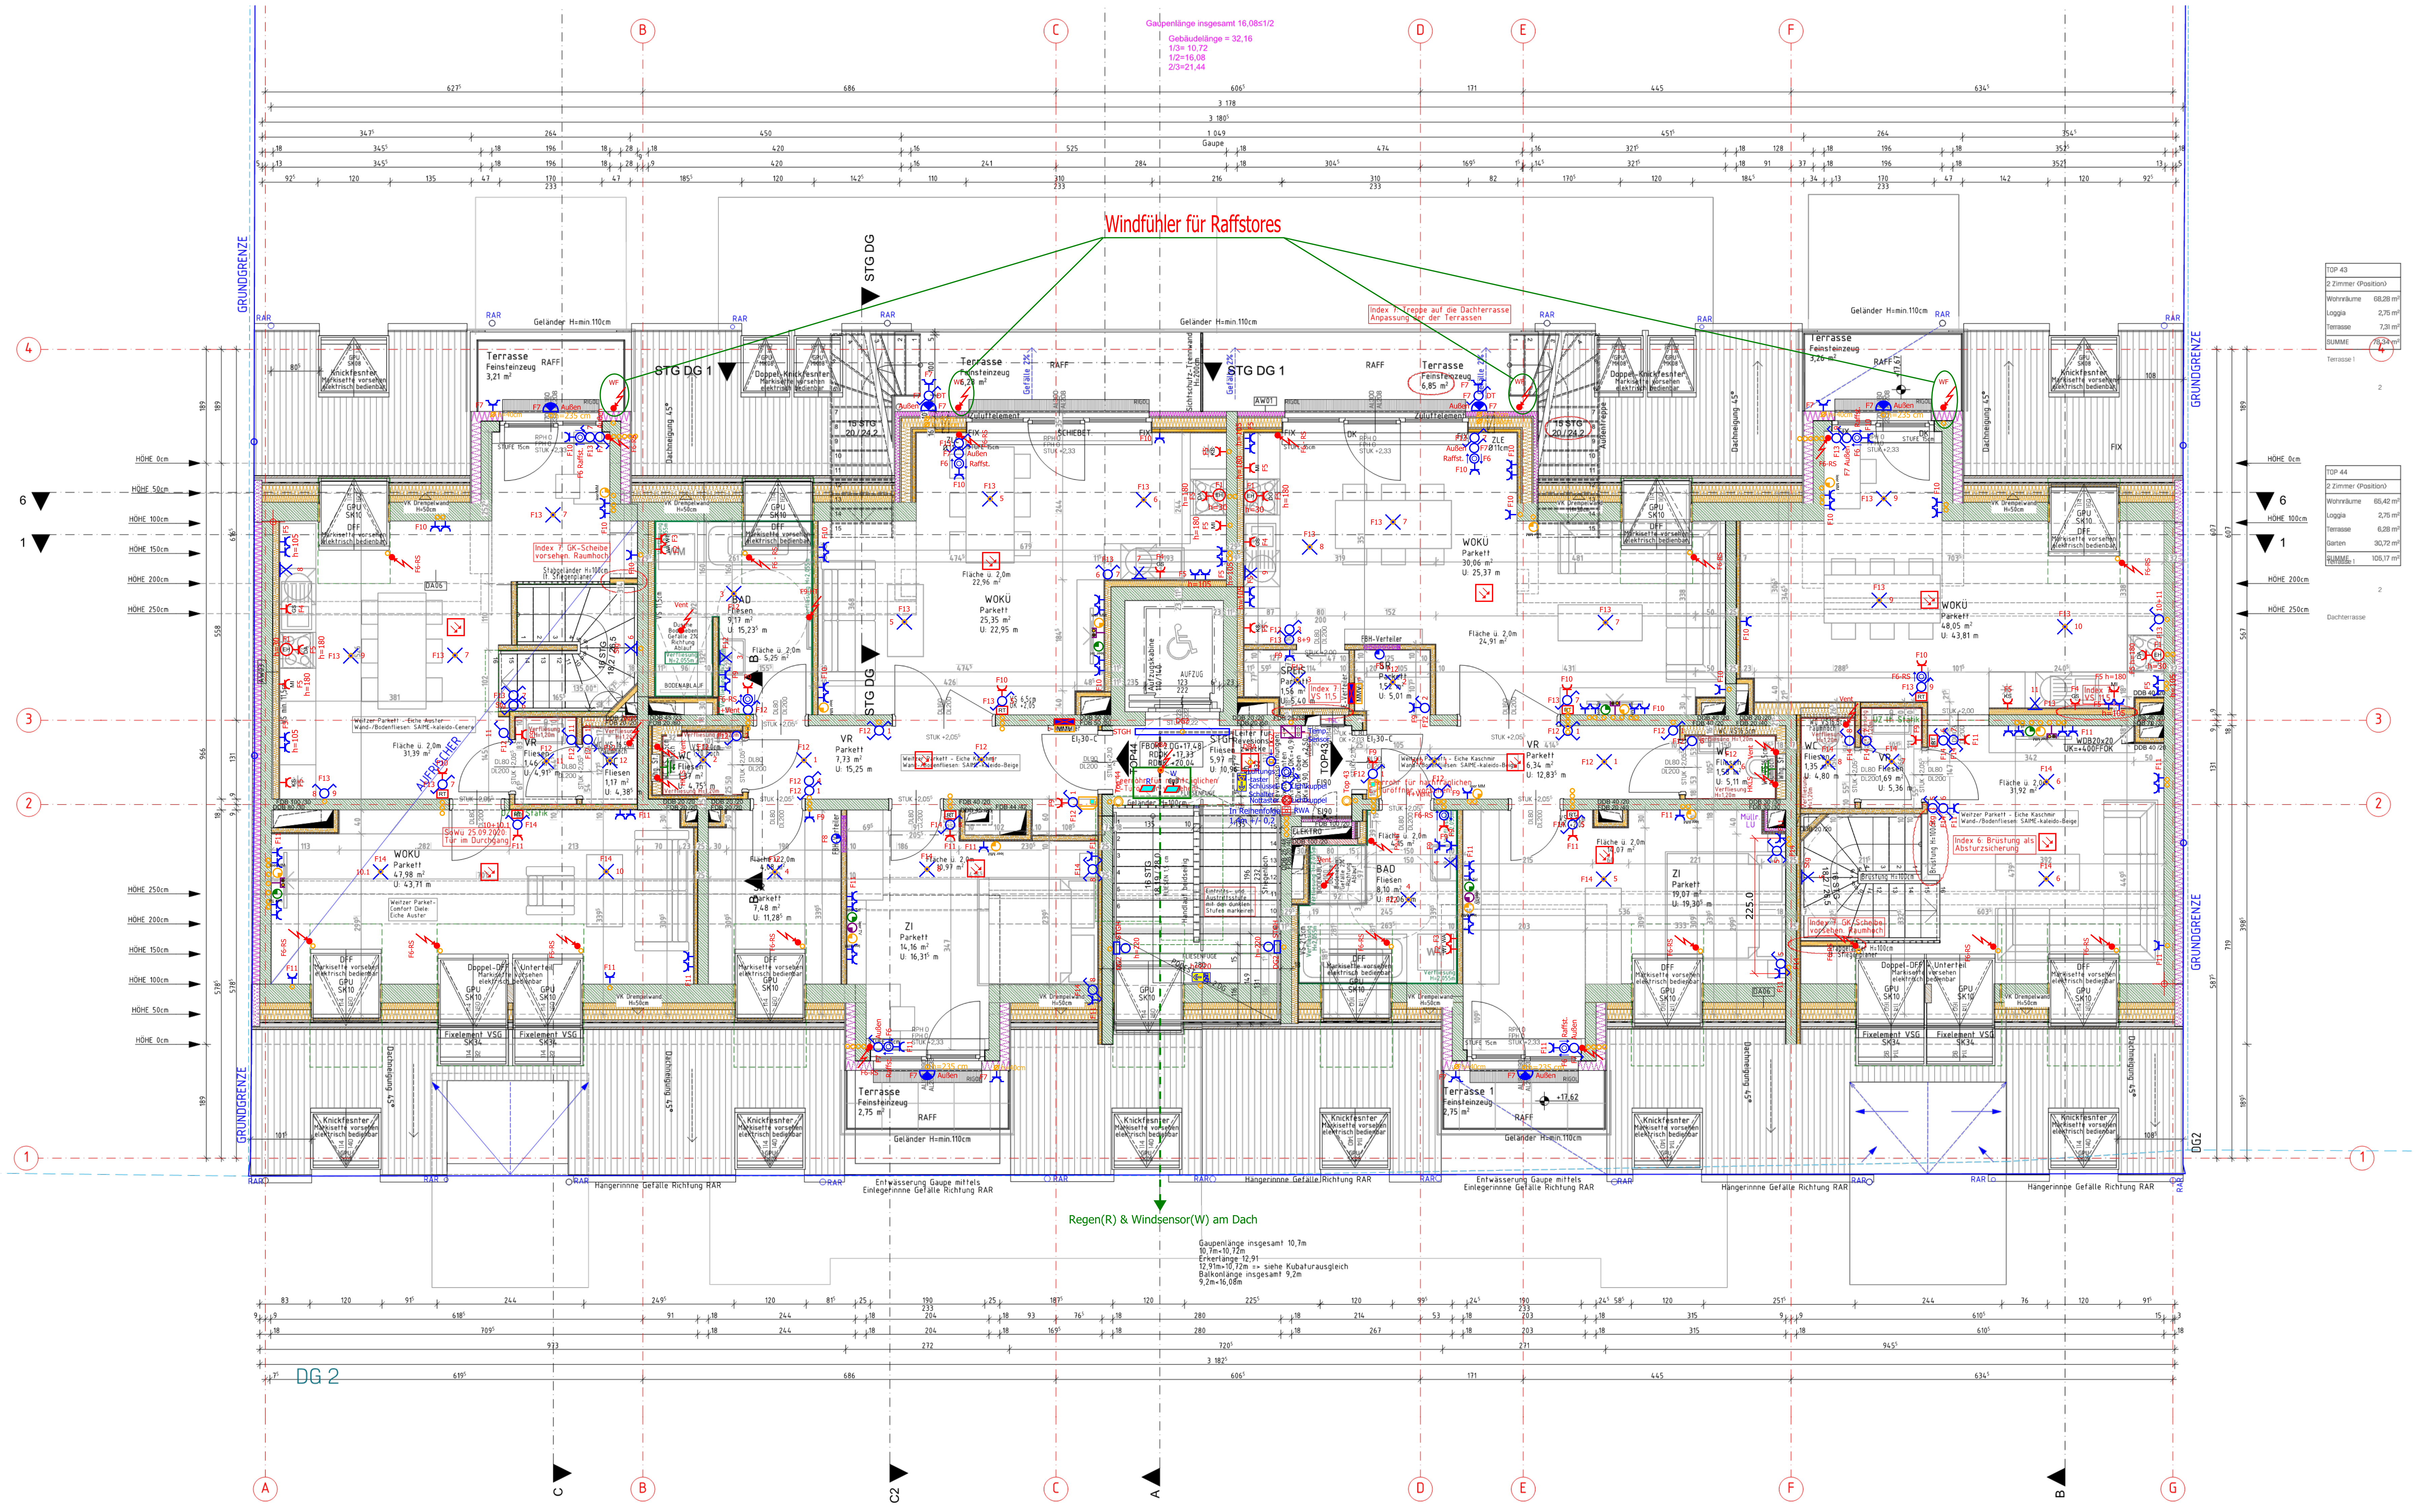

12.10.2020: Einarbeitung der Anmerkungen Fa. ELCONS.

26.11.2020: Beleuchtung im Geländer entfallen.

◐	Aufbauleuchte Wand	○⁄	Ausschalter
✕	Deckenauslass	⊡	Druckknopfmelder DK
EH	E-Herd	ϟ	Elektroanschluss
⏚	Erdung	◎	Etagenruftaster
⇐	EXIT links	⇒	EXIT rechts
▭	FL 1x58W geschlossen	○	FL Vertikal
▯	Gegensprechanlage - Video	↑◎↓	Jalousieschalter
✕	Kreuzschalter	◔	Leerdose
leer MM	Leerdose MM	⊗	Leuchttaster
MMV	Multimedia - Verteiler	◎←	PIR Melder
▨	Rauchmelder, optischer RMMO	RT	Raumthermostat
▱	Regen- u. Windsensor	▱	Regensensor
○⁄	Schlüsselschalter	○	Serieschalter
Ƴ	Steckdose	Ƴ	Steckdose 1-fach
ƳƳ	Steckdose 2-fach	Ƴ	Steckdose allgmein
DA	Steckdose Dampfabzug	DG	Steckdose Dampfgarer
GS	Steckdose Geschirrspüler	KS	Steckdose Kühlschrank
MI	Steckdose Mikrowelle	Ƴ	Steckdose mit Abdeckung
ƳƳ	Steckdosen 2-fach horizontal	leer Tel	Telefonleerdose
T	Temperataur-Sensor	leer TV	TV Leerdose
●	TV Steckdose	☒	Unterverteilung
✕	Wandauslass	○⁄	Wechselschalter
Ø h=180cm	Auslass 180cm	Ø h=40cm	Auslass 40cm
8	Betondose 2f.	○○○	Betondose 3f.
○	Betondose 7cm	○ ○ ○○	Betondose-Kombi V2
ƳƳ	Kombi Waschmaschine/Trockner		

ELEKTROINSTALLATION	**Objekt Nr.: DG2**	**Änderungen**	
		Datum	Vis.
Planhintergrund A2017-04_Heigerlein_PPL_DG_20210527	**Auftraggeber** Auböck Bau GmbH Drosselstraße 36 4470 Enns	24.08.20 26.08.20 10.09.20 12.10.20 20.10.20 03.12.20 02.03.21 20.04.21 31.05.21 06.10.21	Vis...
Firma: **deg.elektro.gmbh** **Hasnerstraße 97** **1160 Wien**	**Objekt:** Heigerleinstraße 20-22 1160Wien		
	Plan Nr.: A **Plan Gr.:** A0 **Mst:** 1:50 **Gezeichnet:** Seker **Datum:** 24.08.2020		