FREIGABE BAUPHYSIK
ERFORDERLICH!
BETONROST IM BEREICH
BRE ANPASSEN!

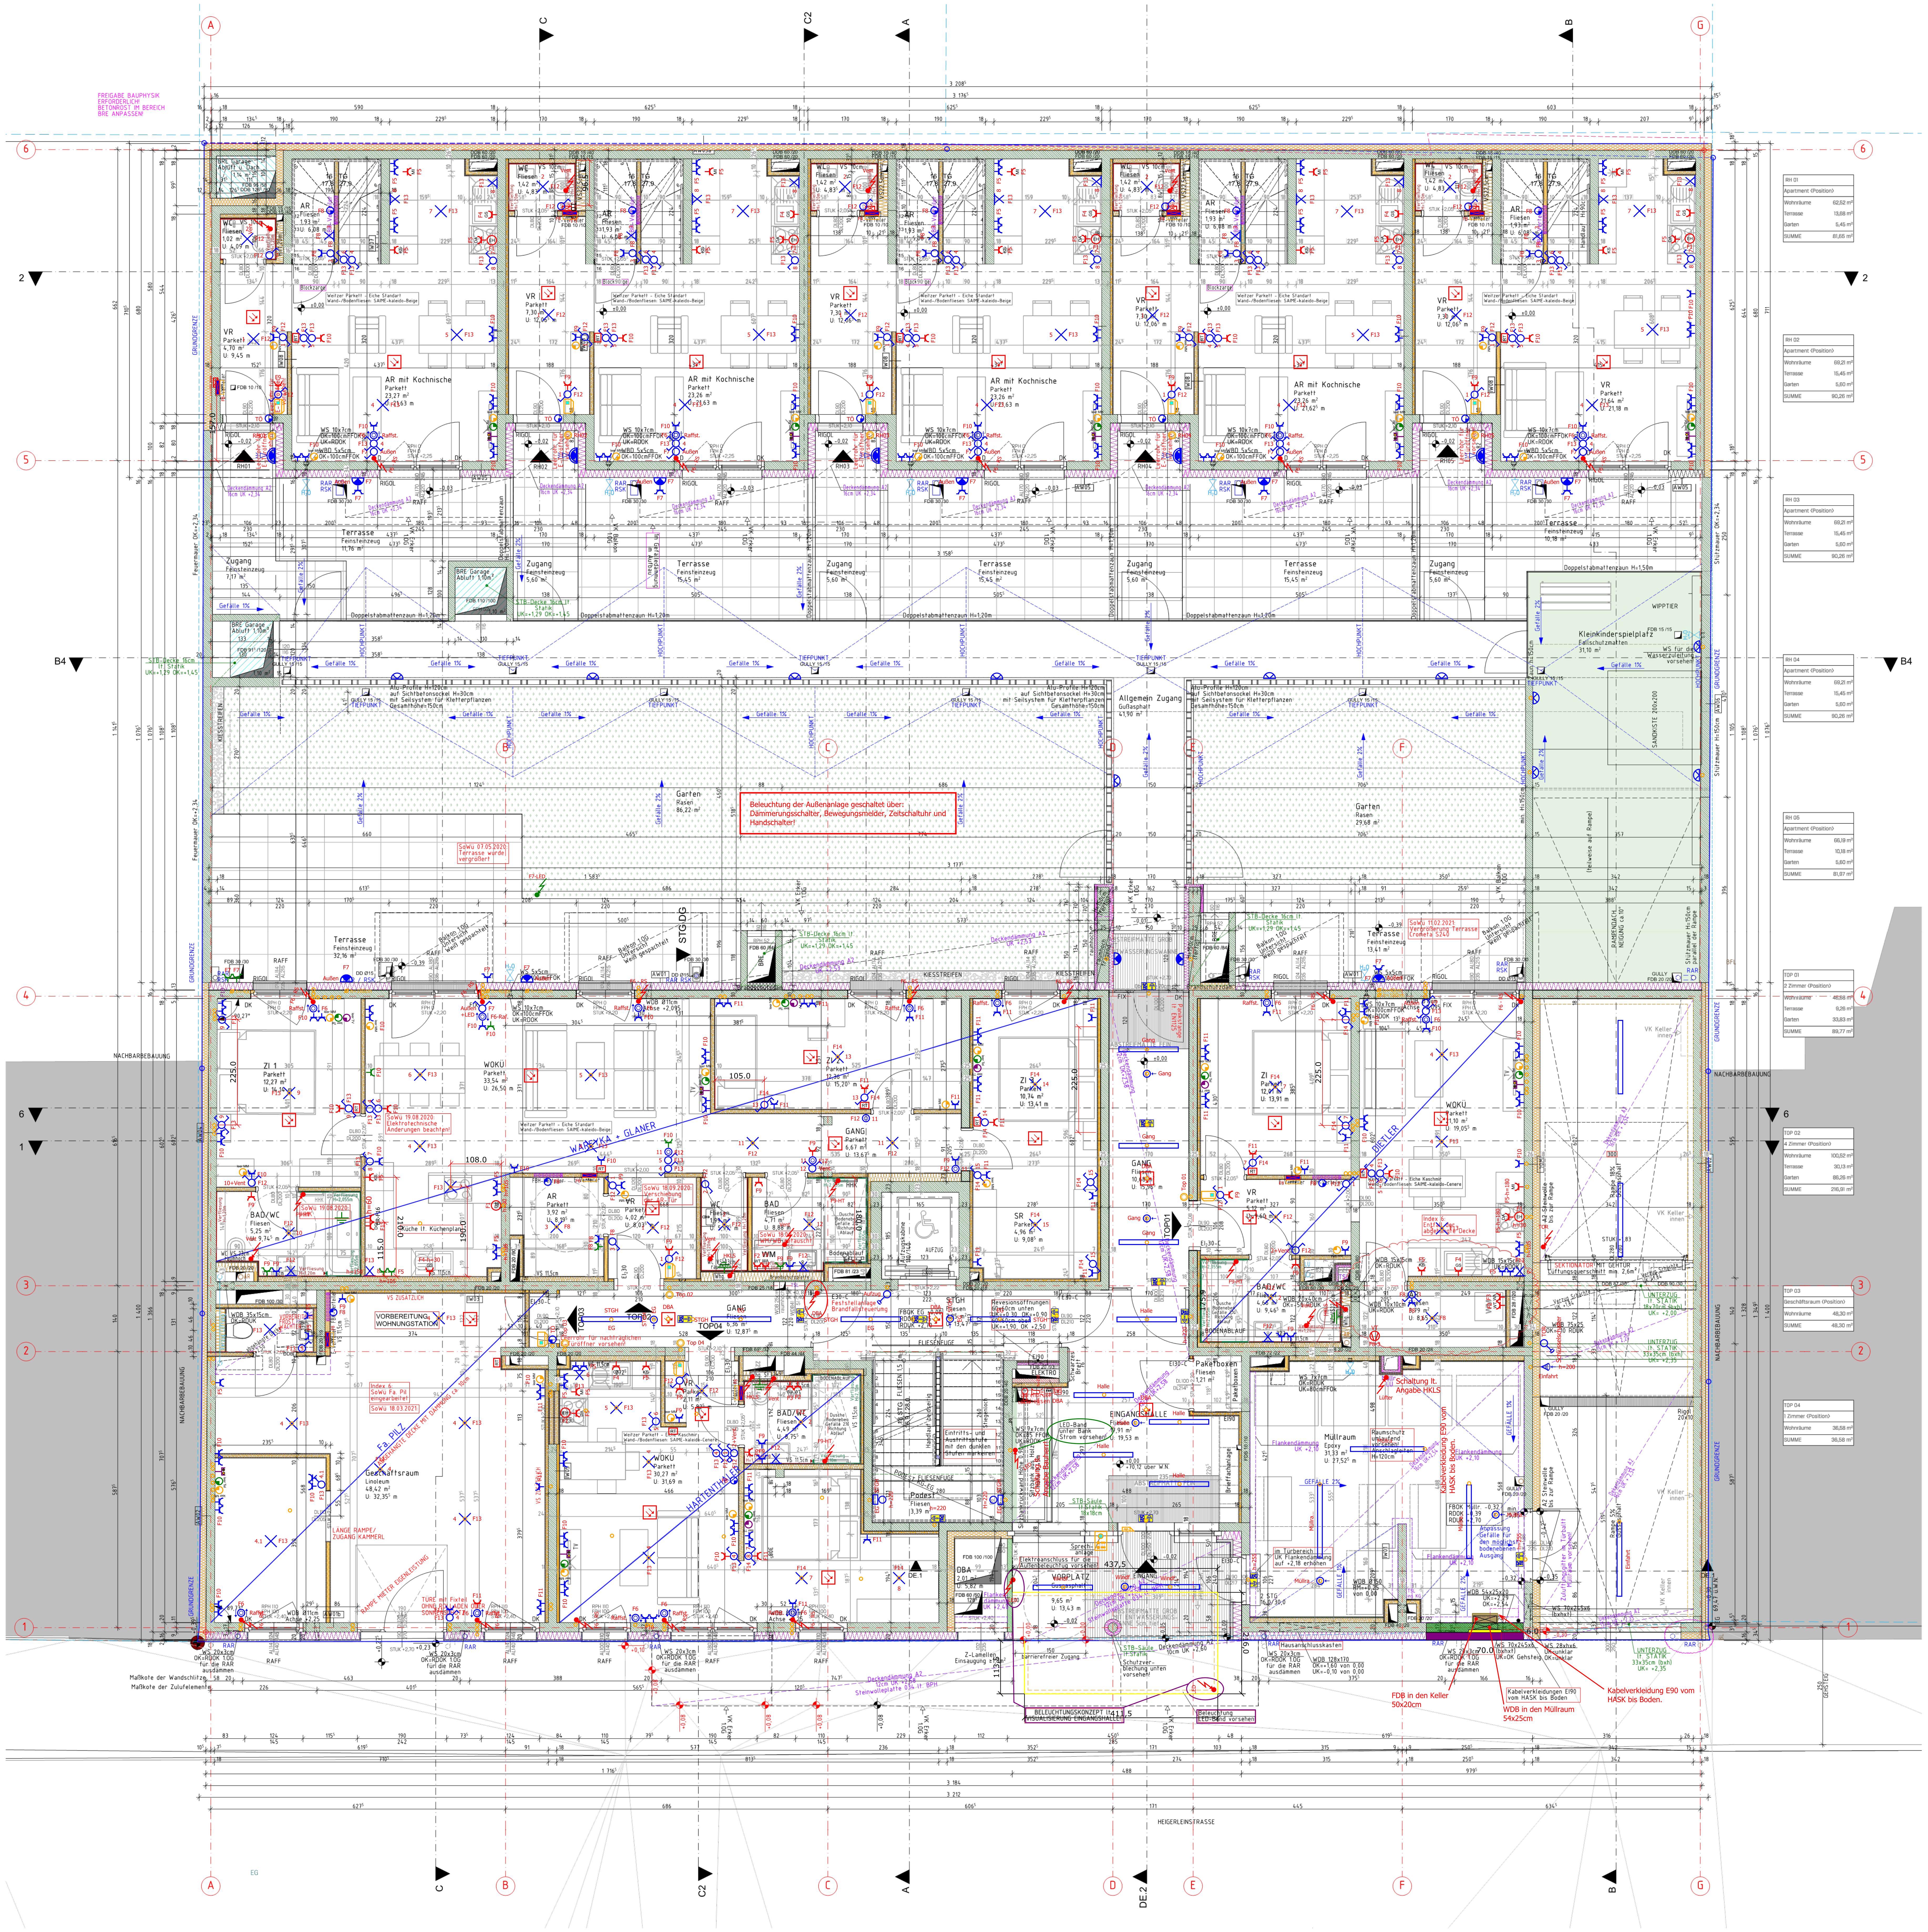

Beleuchtung der Außenanlage geschaltet über:
Dämmerungsschalter, Bewegungsmelder, Zeitschaltuhr und
Handschalter!

RH 01	
Apartment (Position)	
Wohnräume	62,52 m²
Terrasse	13,68 m²
Garten	5,45 m²
SUMME	81,65 m²

RH 02	
Apartment (Position)	
Wohnräume	69,21 m²
Terrasse	15,45 m²
Garten	5,60 m²
SUMME	90,26 m²

RH 03	
Apartment (Position)	
Wohnräume	69,21 m²
Terrasse	15,45 m²
Garten	5,60 m²
SUMME	90,26 m²

RH 04	
Apartment (Position)	
Wohnräume	69,21 m²
Terrasse	15,45 m²
Garten	5,60 m²
SUMME	90,26 m²

RH 05	
Apartment (Position)	
Wohnräume	66,19 m²
Terrasse	10,18 m²
Garten	5,60 m²
SUMME	81,97 m²

TOP 01	
2 Zimmer (Position)	
Wohnräume	46,68 m²
Terrasse	9,26 m²
Garten	33,83 m²
SUMME	89,77 m²

TOP 02	
4 Zimmer (Position)	
Wohnräume	100,52 m²
Terrasse	30,13 m²
Garten	86,26 m²
SUMME	216,91 m²

TOP 03	
Geschäftsraum (Position)	
Wohnräume	48,30 m²
SUMME	48,30 m²

TOP 04	
1 Zimmer (Position)	
Wohnräume	36,58 m²
SUMME	36,58 m²

11.08.2020
Angaben über die DBA Bedienteile und Anschlusspositionen der Betriebsmittel laut AN-HKLS

07.10.2020: Einarbeitung der Anmerkungen Fa. ELCONS.

20.10.2020: Rückbau der Top 4 zur Wohnung.

29.10.2020: Auslässe für Brandfallsteuerung nachgetragen.

26.11.2020: Beleuchtung im Geländer entfallen.

- Aufbauleuchte Wand
- Aussenfühler
- Deckenauslass
- Drucktaster
- Durchbruch
- Einfügepunkt
- Elektroanschluss
- Etagenruftaster
- EXIT rechts
- FL 1x36W geschlossen
- FL Vertikal
- Jalousieschalter
- Leerdose
- MMV Multimedia - Verteiler
- Rauchmelder, optischer RMMO
- Schlüsselschalter
- Signalgeber, optischer (Rundumkennleuchte, Blitzleuchte) SO
- Steckdose
- Steckdose 2-fach
- DA Steckdose Dampfabzug
- GS Steckdose Geschirrspüler
- MI Steckdose Mikrowelle
- Steckdose mit Abdeckung
- WA Steckdose Waschmaschine
- Türöffner
- leer TV TV Leerdose
- Unterverteilung
- Wandeinbauleuchte
- RM-DBA-Betondose
- ⌀ h=40cm Auslass 40cm
- Betondose 3f.
- Betondose-Kombi V2
- Ausschalter
- Aussenwandleuchte mit PIR
- Druckknopfmelder DK
- Durchbruch
- EH E-Herd
- Elektroanschluss
- Erdung
- EXIT
- FBF Feuerwehrbedienfeld FBF
- FL 1x58W geschlossen
- Gegensprechanlage - Video
- Kreuzschalter
- leer MM Leerdose MM
- PIR Melder
- RT Raumthermostat
- Serieschalter
- Steckdose
- Steckdose 2-fach
- Steckdose allgmein
- DG Steckdose Dampfgarer
- KS Steckdose Kühlschrank
- Steckdose mit Abdeckung
- WT Steckdose Wäschetrockner
- leer Tel Telefonleerdose
- Türspechstelle Video
- TV Steckdose
- Wandauslass
- Wechselschalter
- ⌀ h=180cm Auslass 180cm
- Betondose 2f.
- Betondose 7cm
- Kombi Waschmaschine/Trockner

Elektroinstallation

Objekt Nr.: EG

Planhintergrund
A2017-04_HEIGE20_PPL_EG_Index 6_20210419

Auftraggeber:
Auböck Bau GmbH
Drosselstraße 36
4470 Enns

Firma:
deg.elektro.gmbh
Hasnerstraße 97
1160 Wien

Objekt:
Heigerleinstraße 20-22
1160Wien

Neubau Wohnhausanlage

Plan Nr.: A
Plan Gr.: A0
Mst: 1:50
Gezeichnet: AM
Datum: 16.06.2020

Änderungen	
Datum	Vis.
07.07.20 09.07.20 10.08.20 11.08.20 12.08.20 13.08.20 19.08.20 10.09.20 15.09.20 07.10.20 20.10.20 29.10.20 25.11.20 03.12.20 15.03.21 20.04.21 20.05.21 07.10.21	Vis...