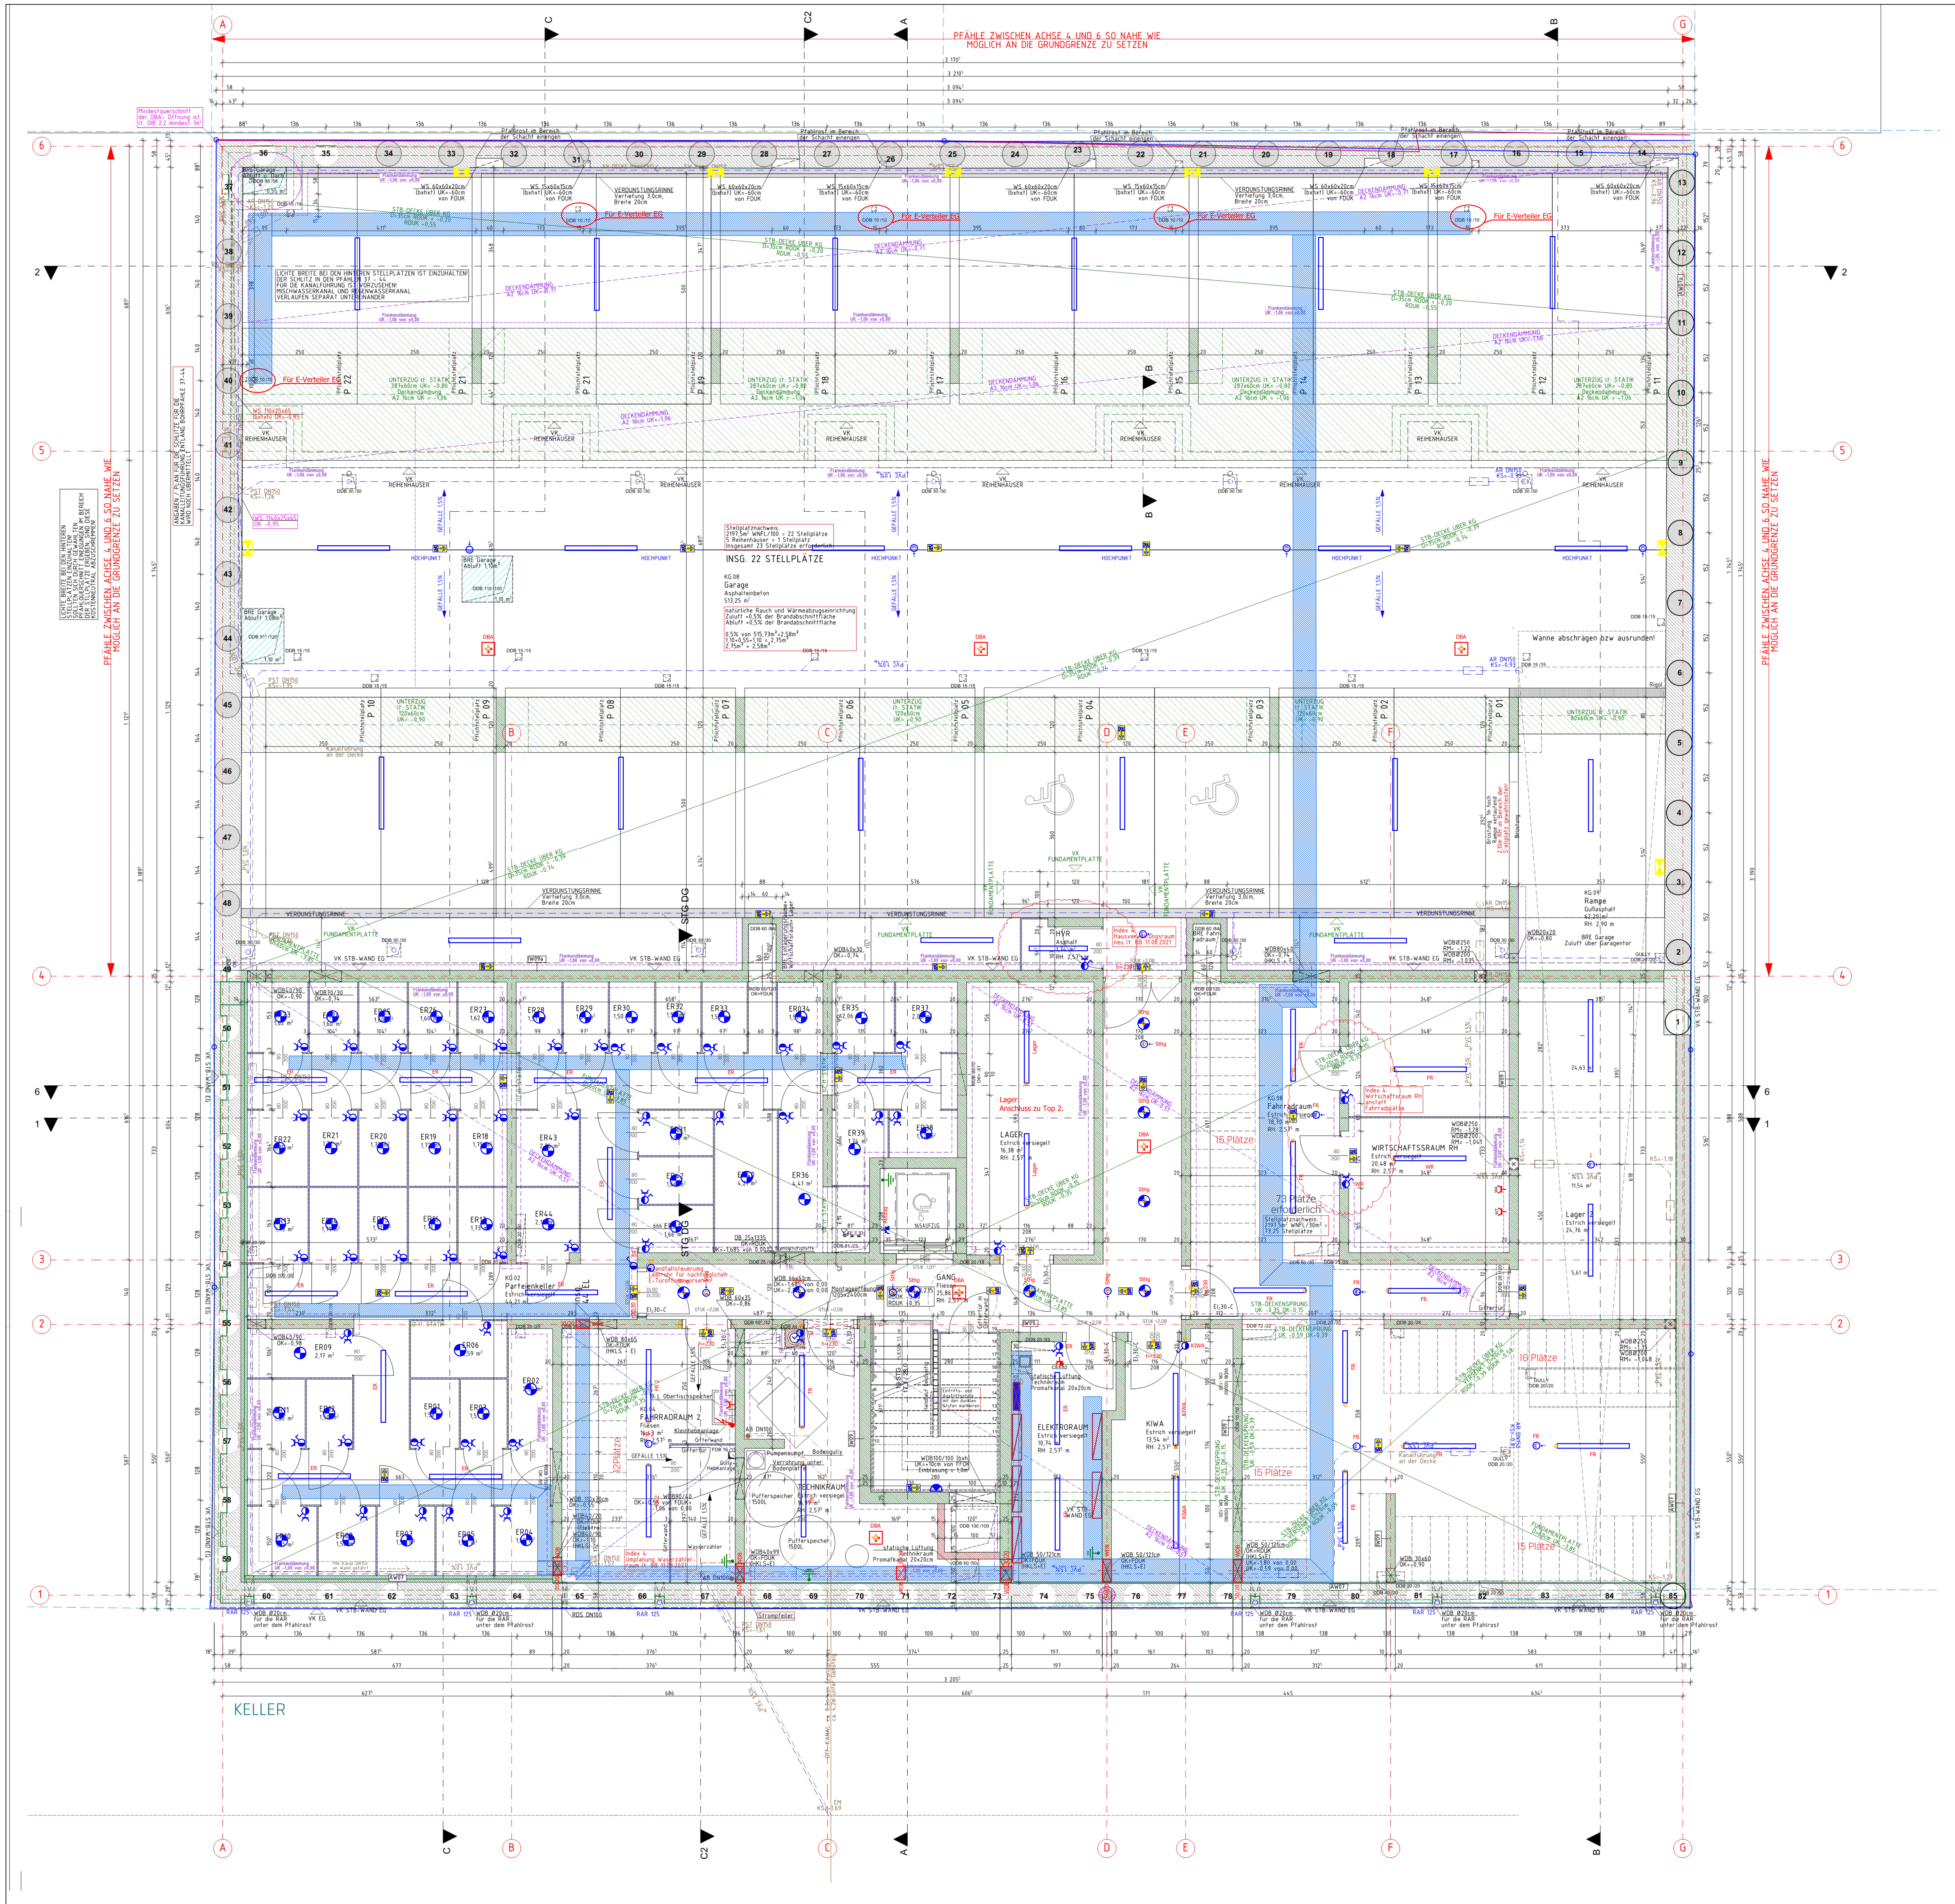
PFÄHLE ZWISCHEN ACHSE 4 UND 6 SO NAHE WIE MÖGLICH AN DIE GRUNDGRENZE ZU SETZEN
INSG 22 STELLPLÄTZE
Garage
Für E-Verteiler EG
Wanne abschrägen bzw ausrunden!
Rampe
Parteienkeller
FAHRRADRAUM
TECHNIKRAUM
ELEKTRORAUM
KIWA
LAGER
WIRTSCHAFTSRAUM
Fahrradraum
GANG
STG DG
KELLER
A
B
C
C2
D
E
F
G
1
2
3
4
5
6

Rauchmelder für DBA eingetragen.
Kabeltassenführung lt. Baubesprechung vom 09.07.2020 angepasst.
13.08.20: zusätzl. Rauchmelder für DBA im Gangbereich lt. HKLS.

07.10.2020: Einarbeitung der Anmerkungen Fa. ELCONS.

◐	Aufbauleuchte	◖	Aufbauleuchte Wand
◐	Ausschalter AP	⏚	Erdungs-Anschluss
⇩	EXIT	⇦	EXIT links
⇨	EXIT rechts	▭	FL 1x36W geschlossen
▭	FL 1x58W geschlossen	▭	Hauptverteilung
	Kombi Ausschalter - Steckdose AP	◔	Leerdose
	PIR Melder		Steckdose AP
CEE32	Steckdose CEE32 AP	WA	Steckdose Waschmaschine
☒	Unterverteilung	⧗	Bereitschaftsleuchte
8	Betondose 2f.	○	Betondose 7cm

Elektroinstallation

Objekt Nr.: KG

Planhintergrund:
A2017-04_Heigerlein_PPL_KG_Index 4_20210811

Auftraggeber:
Auböck Bau GmbH
Drosselstraße 36
4470 Enns

Firma:
deg-elektro.gmbh
Hasnerstraße 97
1160 Wien

deg elektro

Objekt:
Heigerleinstraße 20-22
1160Wien

Neubau Wohnhausanlage

Plan Nr.: VA
Plan Gr.: A0
Mst: 1:50

Gezeichnet: AM
Datum: 16.06.2020

Änderungen	
Datum	Vis.
22.06.20	Vis...
29.06.20	
07.07.20	
09.07.20	
13.08.20	
07.10.20	
20.10.20	
20.04.21	
16.08.21	