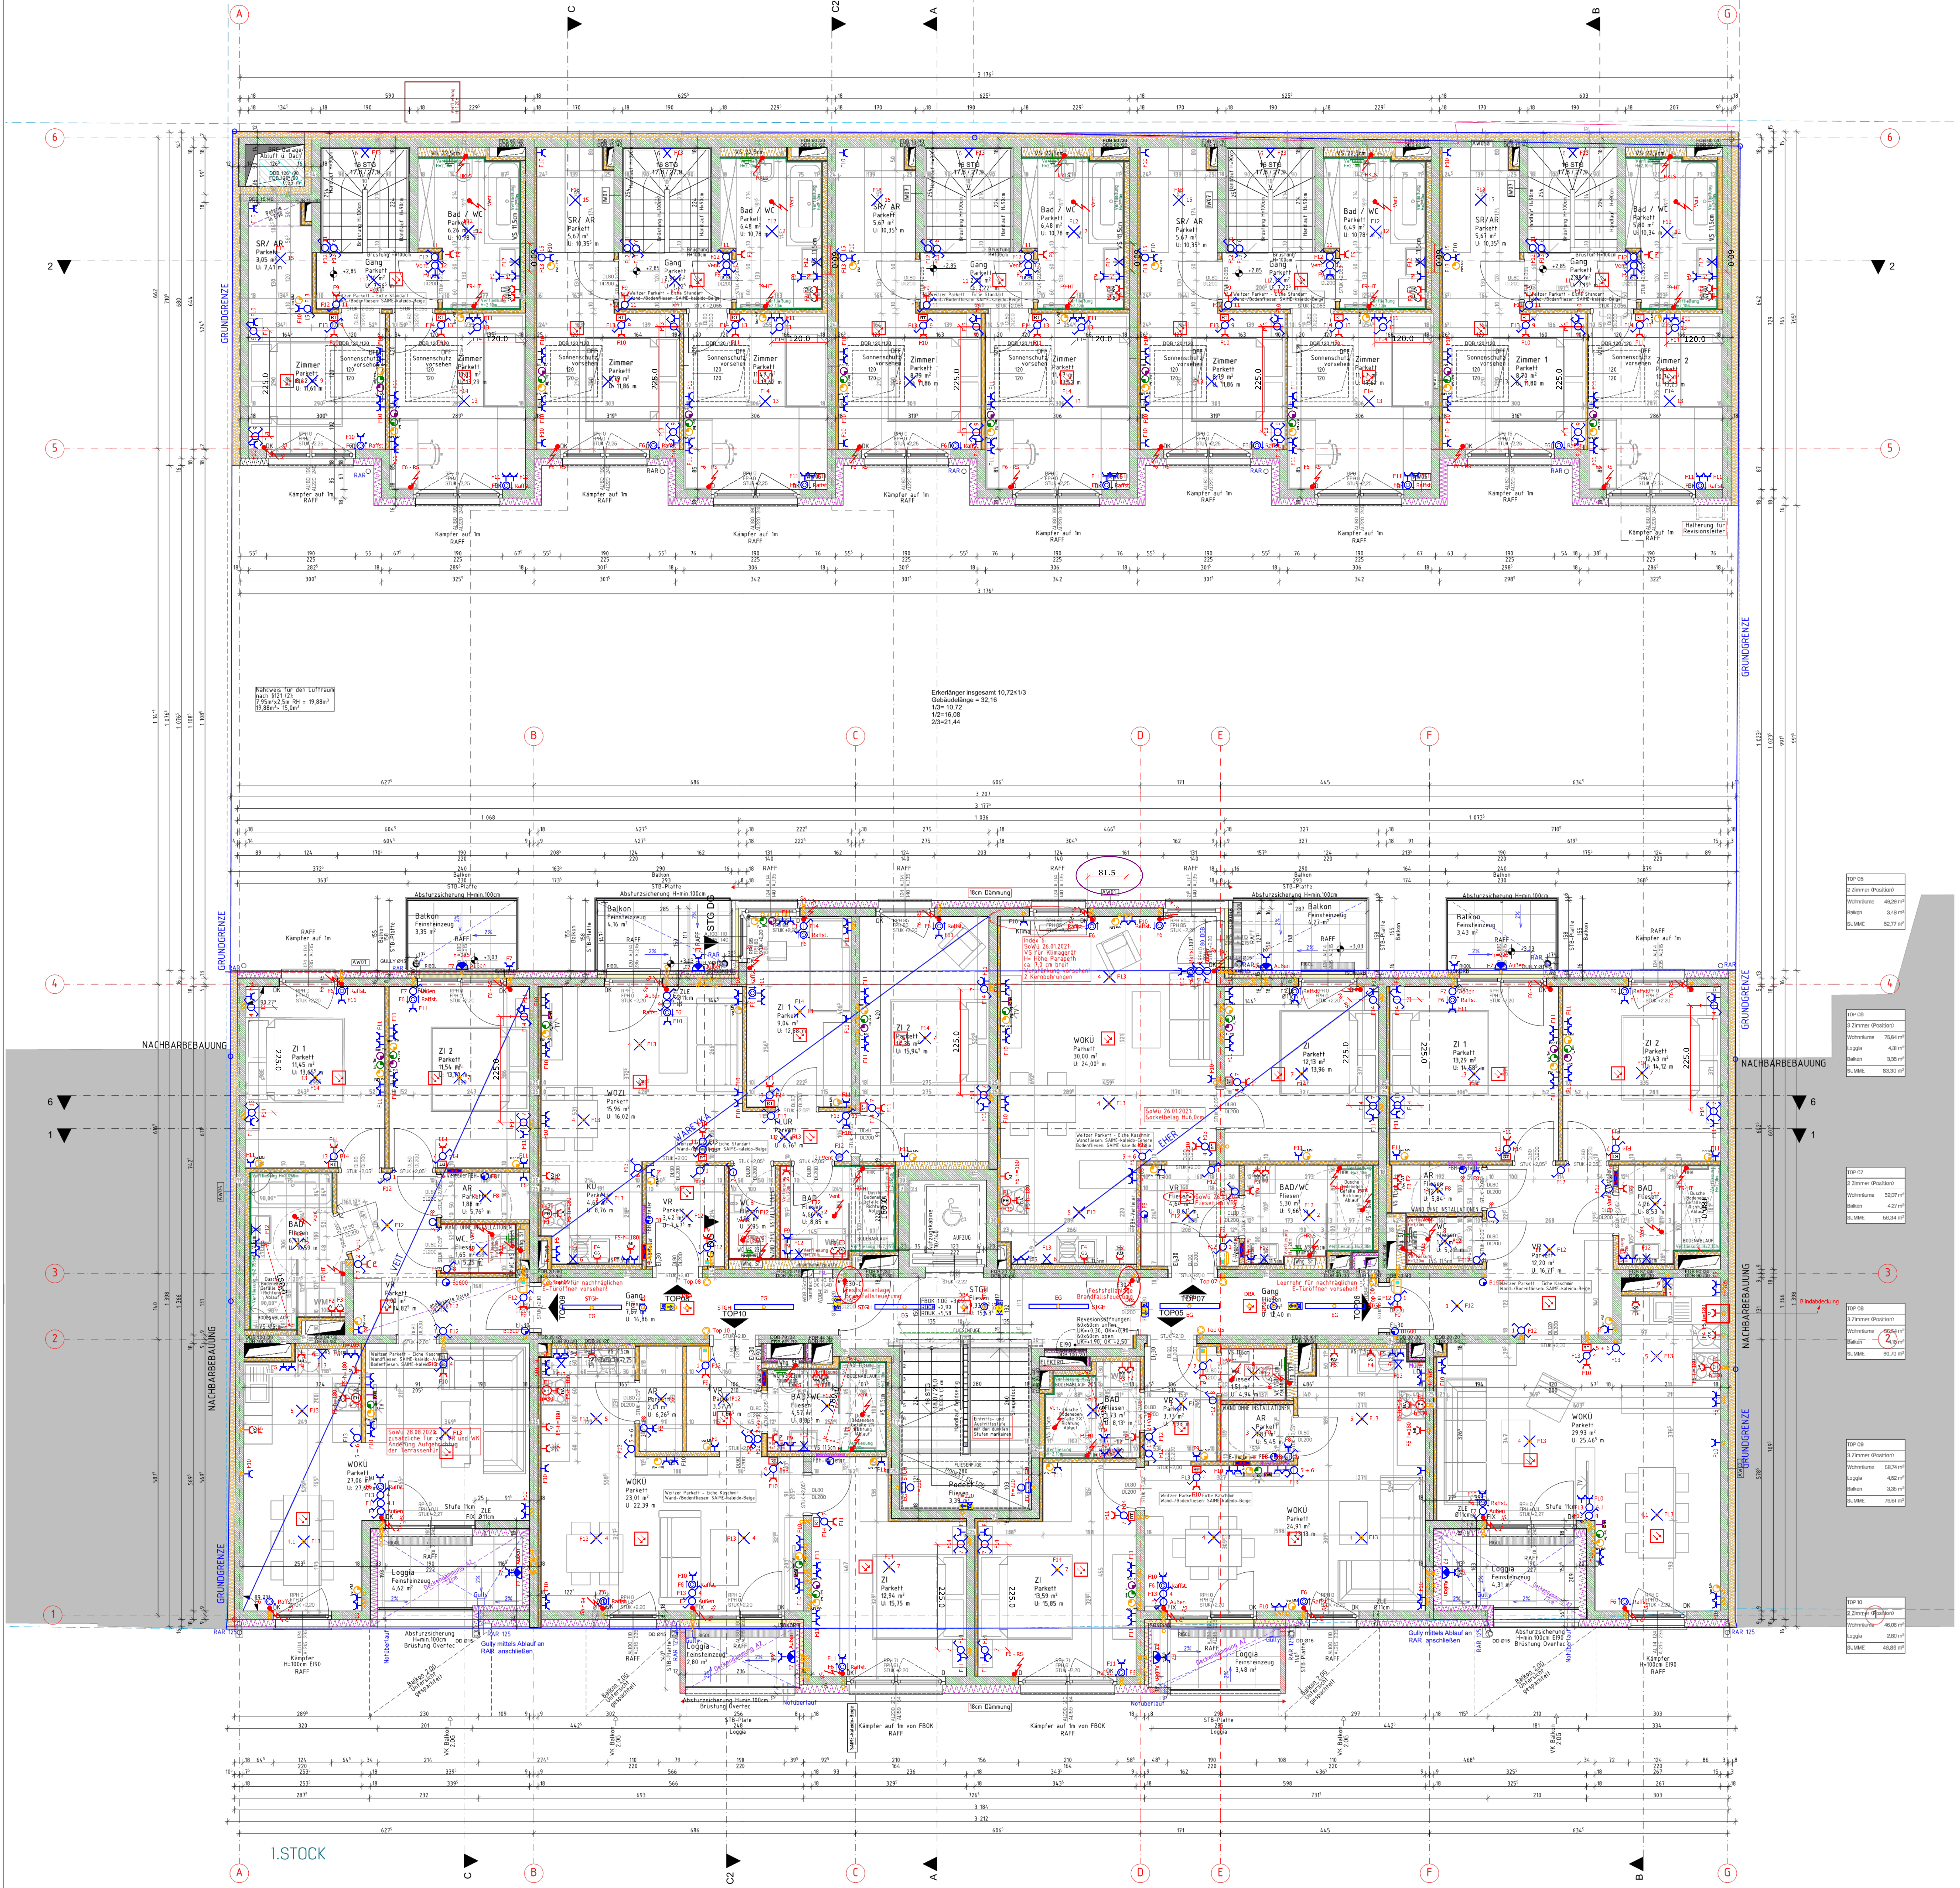

TOP 05	
2 Zimmer (Position)	
Wohnräume	49,29 m²
Balkon	3,48 m²
SUMME	52,77 m²

TOP 06	
3 Zimmer (Position)	
Wohnräume	75,64 m²
Loggia	4,31 m²
Balkon	3,35 m²
SUMME	83,30 m²

TOP 07	
2 Zimmer (Position)	
Wohnräume	52,07 m²
Balkon	4,27 m²
SUMME	56,34 m²

TOP 08	
3 Zimmer (Position)	
Wohnräume	56,54 m²
Balkon	4,16 m²
SUMME	60,70 m²

TOP 09	
3 Zimmer (Position)	
Wohnräume	68,74 m²
Loggia	4,52 m²
Balkon	3,35 m²
SUMME	76,61 m²

TOP 10	
2 Zimmer (Position)	
Wohnräume	46,06 m²
Loggia	2,80 m²
SUMME	48,86 m²

11.08.2020
Angaben über die DBA Bedienteile und Anschlusspositionen der Betriebsmittel laut AN-HKLS

07.10.2020: Einarbeitung der Anmerkungen Fa. ELCONS.

15.10.20: Detailänderung Top 09 Bad.

29.10.20: Auslässe für Brandfallsteuerung nachgetragen.

26.11.2020: Beleuchtung im Geländer entfallen.

- Aufbauleuchte Wand
- Deckenauslass
- Einfügepunkt
- Erdung
- EXIT
- FL 1x36W geschlossen
- Gegensprechanlage - Video
- Kreuzschalter
- Leerdose MM
- PIR Melder
- Raumthermostat
- Steckdose
- Steckdose allgmein
- Steckdose Geschirrspüler
- Steckdose Mikrowelle
- Telefonleerdose
- TV Steckdose
- Wandauslass
- RM-DBA-Betondose
- Auslass 40cm
- Betondose 3f.
- Betondose-Kombi V2
- Ausschalter
- E-Herd
- Elektroanschluss
- Etagenruftaster
- EXIT rechts
- FL Vertikal
- Jalousieschalter
- Leerdose
- Multimedia - Verteiler
- Rauchmelder, optischer RMMO
- Serieschalter
- Steckdose 2-fach
- Steckdose Dampfabzug
- Steckdose Kühlschrank
- Steckdose mit Abdeckung
- TV Leerdose
- Unterverteilung
- Wechselschalter
- Auslass 180cm
- Betondose 2f.
- Betondose 7cm
- Kombi Waschmaschine/Trockner

Elektroinstallation

Objekt Nr.: 1.OG

Planhintergrund
A2017-04_HEIGE20_PPL_1.OG_Index 4_20210419

Auftraggeber:
Auböck Bau GmbH
Drosselstraße 36
4470 Enns

Firma:
deg-elektro.gmbh
Hasnerstraße 97
1160 Wien

deg elektro

Objekt:
Heigerleinstraße 20-22
1160Wien

Neubau Wohnhausanlage

Plan Nr.: A
Plan Gr.: A0
Mst: 1:50

Gezeichnet: AM
Datum: 16.06.2020

Änderungen	
Datum	Vis.
12.08.20 17.08.20 10.09.20 07.10.20 15.10.20 20.10.20 29.10.20 03.12.20 02.03.21 19.04.21 07.10.21	Vis...