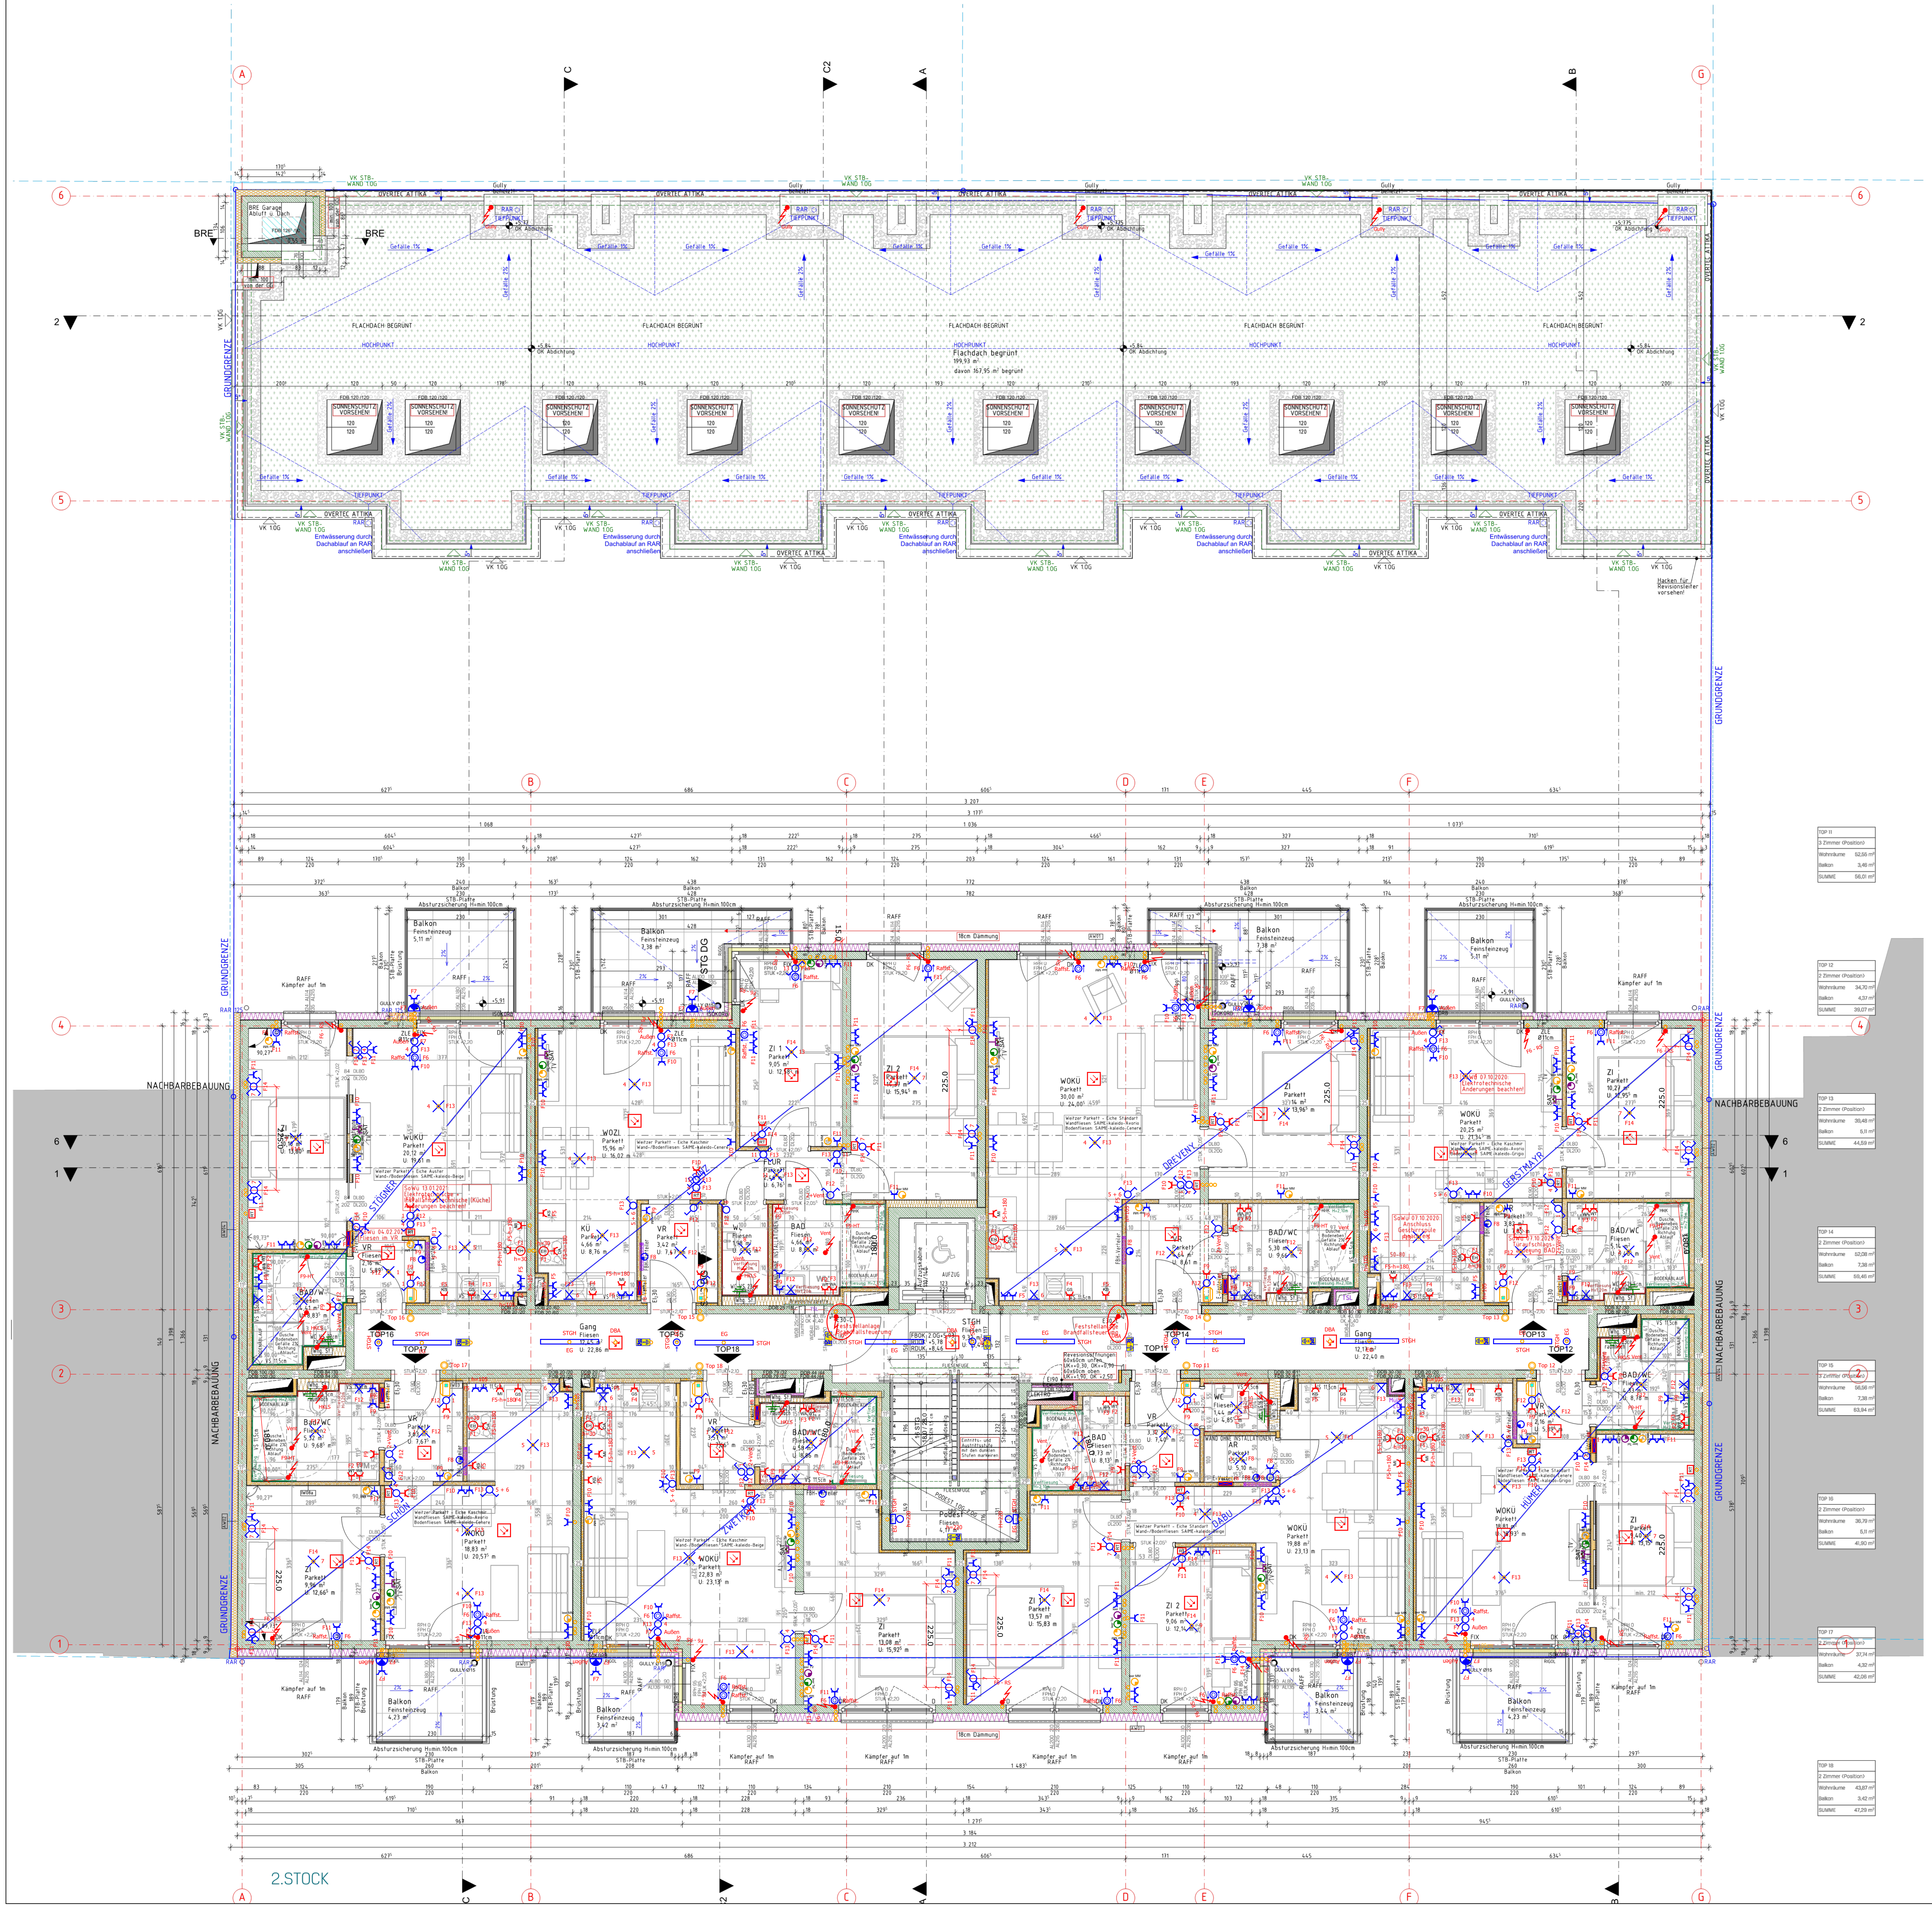

TOP	Zimmer	Wohnräume	Balkon	SUMME
TOP 11	3 Zimmer (Position)	52,55 m²	3,46 m²	56,01 m²
TOP 12	2 Zimmer (Position)	34,70 m²	4,37 m²	39,07 m²
TOP 13	2 Zimmer (Position)	39,48 m²	5,11 m²	44,59 m²
TOP 14	2 Zimmer (Position)	52,08 m²	7,38 m²	59,46 m²
TOP 15	3 Zimmer (Position)	56,56 m²	7,38 m²	63,94 m²
TOP 16	2 Zimmer (Position)	36,79 m²	5,11 m²	41,90 m²
TOP 17	2 Zimmer (Position)	37,74 m²	4,32 m²	42,06 m²
TOP 18	2 Zimmer (Position)	43,87 m²	3,42 m²	47,29 m²

11.08.2020
Angaben über die DBA Bedienteile und Anschlusspositionen der Betriebsmittel laut AN-HKLS

07.10.2020: Einarbeitung der Anmerkungen Fa. ELCONS.

13.10.2020: Top 15 ZI1 Dose verschoben.

29.10.20: Auslässe für Brandfallsteuerung nachgetragen.

26.11.2020: Beleuchtung im Geländer entfallen. Gullyheizung Hofgebäude nachgeführt.

- Aufbauleuchte Wand
- Deckenauslass
- Einfügepunkt
- Erdung
- EXIT
- FL 1x36W geschlossen
- Gegensprechanlage - Video
- Kreuzschalter
- Leerdose MM
- PIR Melder
- RT Raumthermostat
- Steckdose
- Steckdose allgmein
- GS Steckdose Geschirrspüler
- MI Steckdose Mikrowelle
- Telefonleerdose
- TV Steckdose
- Wandauslass
- RM-DBA-Betondose
- Auslass 40cm
- Betondose 3f.
- Betondose-Kombi V2
- Ausschalter
- EH E-Herd
- Elektroanschluss
- Etagenruftaster
- EXIT rechts
- FL Vertikal
- Jalousieschalter
- Leerdose
- MMV Multimedia - Verteiler
- Rauchmelder, optischer RMMO
- Serieschalter
- Steckdose 2-fach
- DA Steckdose Dampfabzug
- KS Steckdose Kühlschrank
- Steckdose mit Abdeckung
- TV Leerdose
- Unterverteilung
- Wechselschalter
- Auslass 180cm
- Betondose 2f.
- Betondose 7cm
- Kombi Waschmaschine/Trockner

Elektroinstallation

Objekt Nr.: 2.OG

Planhintergrund
A2017-04_HEIGE20_PPL_2,OG_Index 4_20210419

Auftraggeber:
Auböck Bau GmbH
Drosselstraße 36
4470 Enns

Firma:
deg.elektro.gmbh
Hasnerstraße 97
1160 Wien

Objekt:
Heigerleinstraße 20-22
1160Wien

Neubau Wohnhausanlage

Plan Nr.: A
Plan Gr.: A0
Mst: 1:50

Gezeichnet: AM
Datum: 16.06.2020

Änderungen	
Datum	Vis.
17.08.20 18.08.20 10.09.20 07.10.20 13.10.20 20.10.20 29.10.20 03.12.20 28.01.21 02.03.21 20.04.21 04.10.21	Vis...