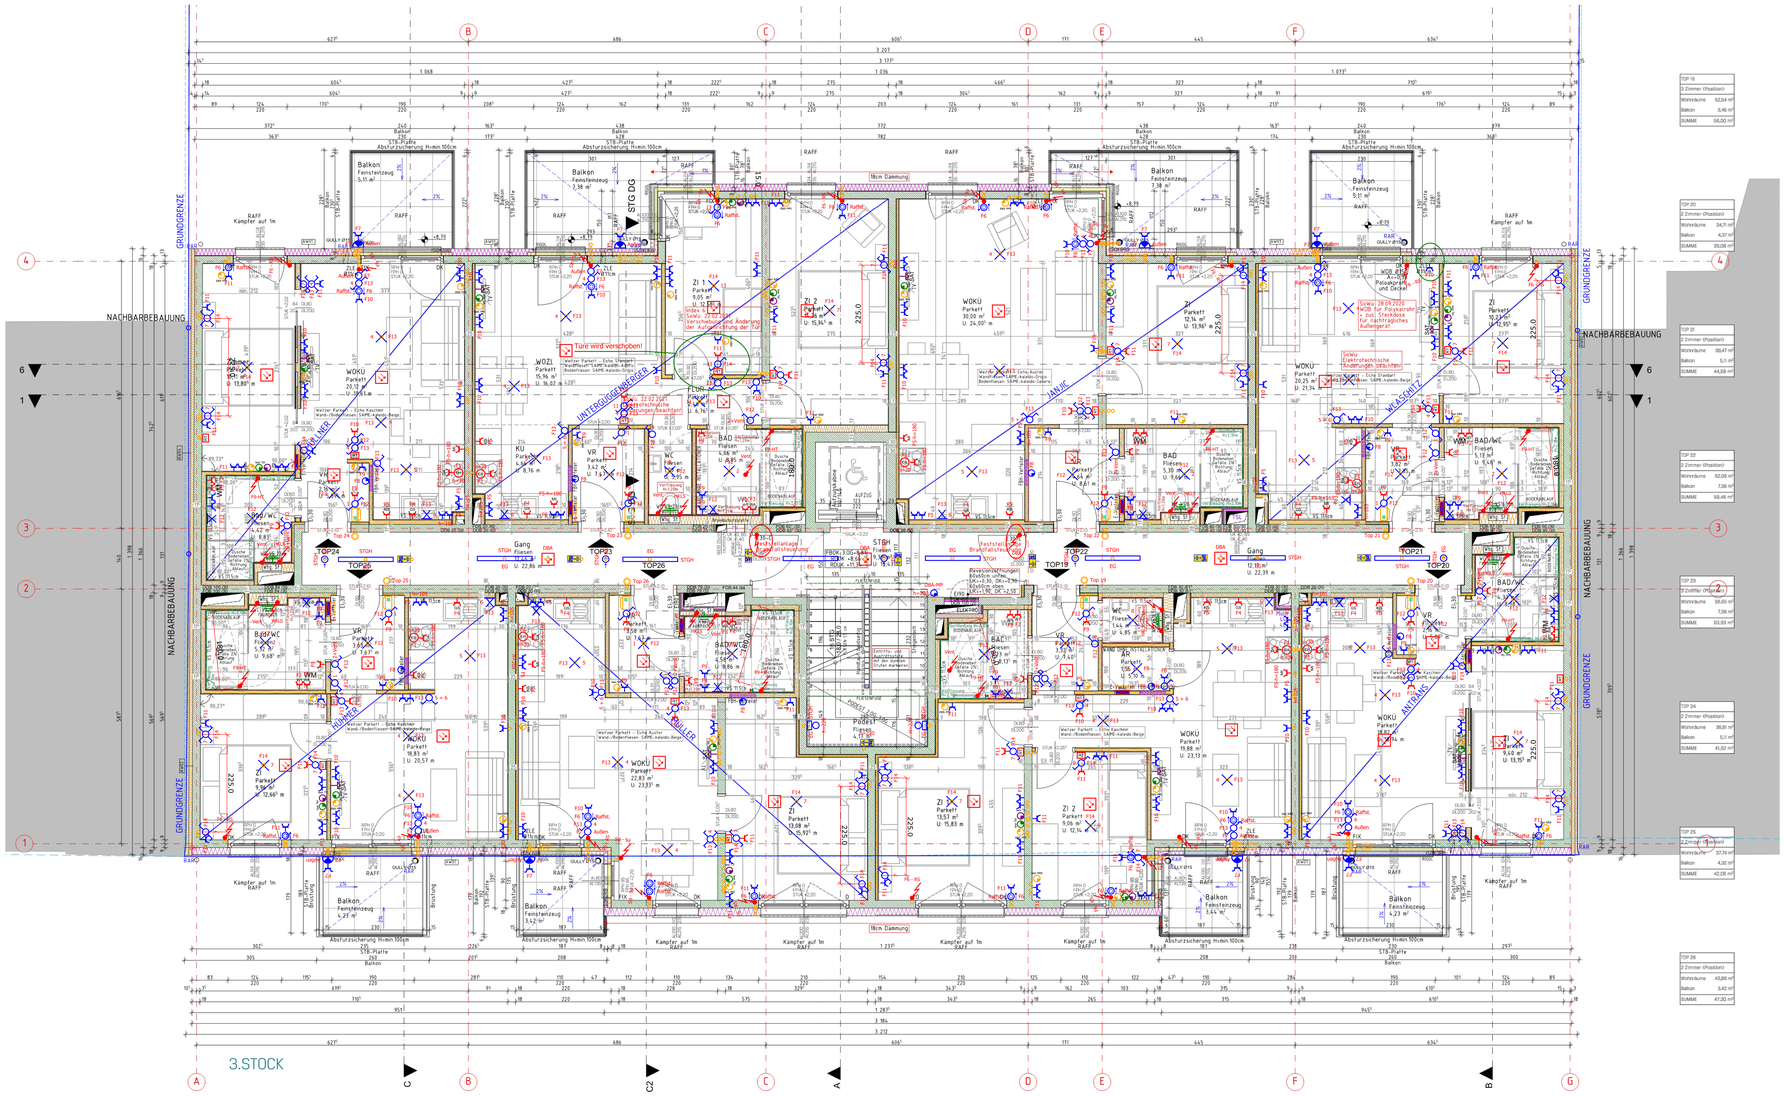


TOP 19	
3 Zimmer (Position)	
Wohnräume	52,54 m²
Balkon	3,46 m²
SUMME	56,00 m²
TOP 20	
2 Zimmer (Position)	
Wohnräume	34,71 m²
Balkon	4,37 m²
SUMME	39,08 m²
TOP 21	
2 Zimmer (Position)	
Wohnräume	39,47 m²
Balkon	5,31 m²
SUMME	44,58 m²
TOP 22	
2 Zimmer (Position)	
Wohnräume	52,08 m²
Balkon	7,38 m²
SUMME	59,46 m²
TOP 23	
2 Zimmer (Position)	
Wohnräume	56,55 m²
Balkon	7,38 m²
SUMME	63,93 m²
TOP 24	
2 Zimmer (Position)	
Wohnräume	36,81 m²
Balkon	6,1 m²
SUMME	43,02 m²
TOP 25	
2 Zimmer (Position)	
Wohnräume	37,74 m²
Balkon	4,32 m²
SUMME	42,06 m²
TOP 26	
2 Zimmer (Position)	
Wohnräume	43,88 m²
Balkon	3,42 m²
SUMME	47,30 m²

11.08.2020
Angaben über die DBA Bedientelle und Anschlusspositionen der Betriebsmittel laut AN-HKLS

07.10.2020: Einarbeitung der Anmerkungen Fa. ELCONS.

13.10.2020: Top 23 Z11 Dose verschoben.

29.10.20: Auslässe für Brandfallsteuerung nachgetragen.

19.11.20: Sonderwunsch Top 21 eingetragen.

26.11.2020: Beleuchtung im Geländer entfallen.

Elektroinstallation	Objekt Nr.: 3.OG	Änderungen	
		Datum	Vis.
Planhintergrund A2017-04_HEIGE20_PPL_3.-4.OG_Index 4_20210419	**Auftraggeber:** Aubück Bau GmbH Drosselstraße 36 4470 Enns	18.08.20. 10.09.20 07.10.20 13.10.20 20.10.20 29.10.20 19.11.20 03.12.20 28.01.21 02.03.21 17.03.21 20.04.21 04.10.21	Vis...
Firma: deg-elektro.gmbh Hasnerstraße 97 1160 Wien	**Objekt:** Heigerleinstraße 20-22 1160Wien Neubau Wohnhausanlage		
	Plan Nr.: A **Plan Gr.:** A0 **Mst.:** 1:50 **Gezeichnet:** AM **Datum:** 16.06.2020		