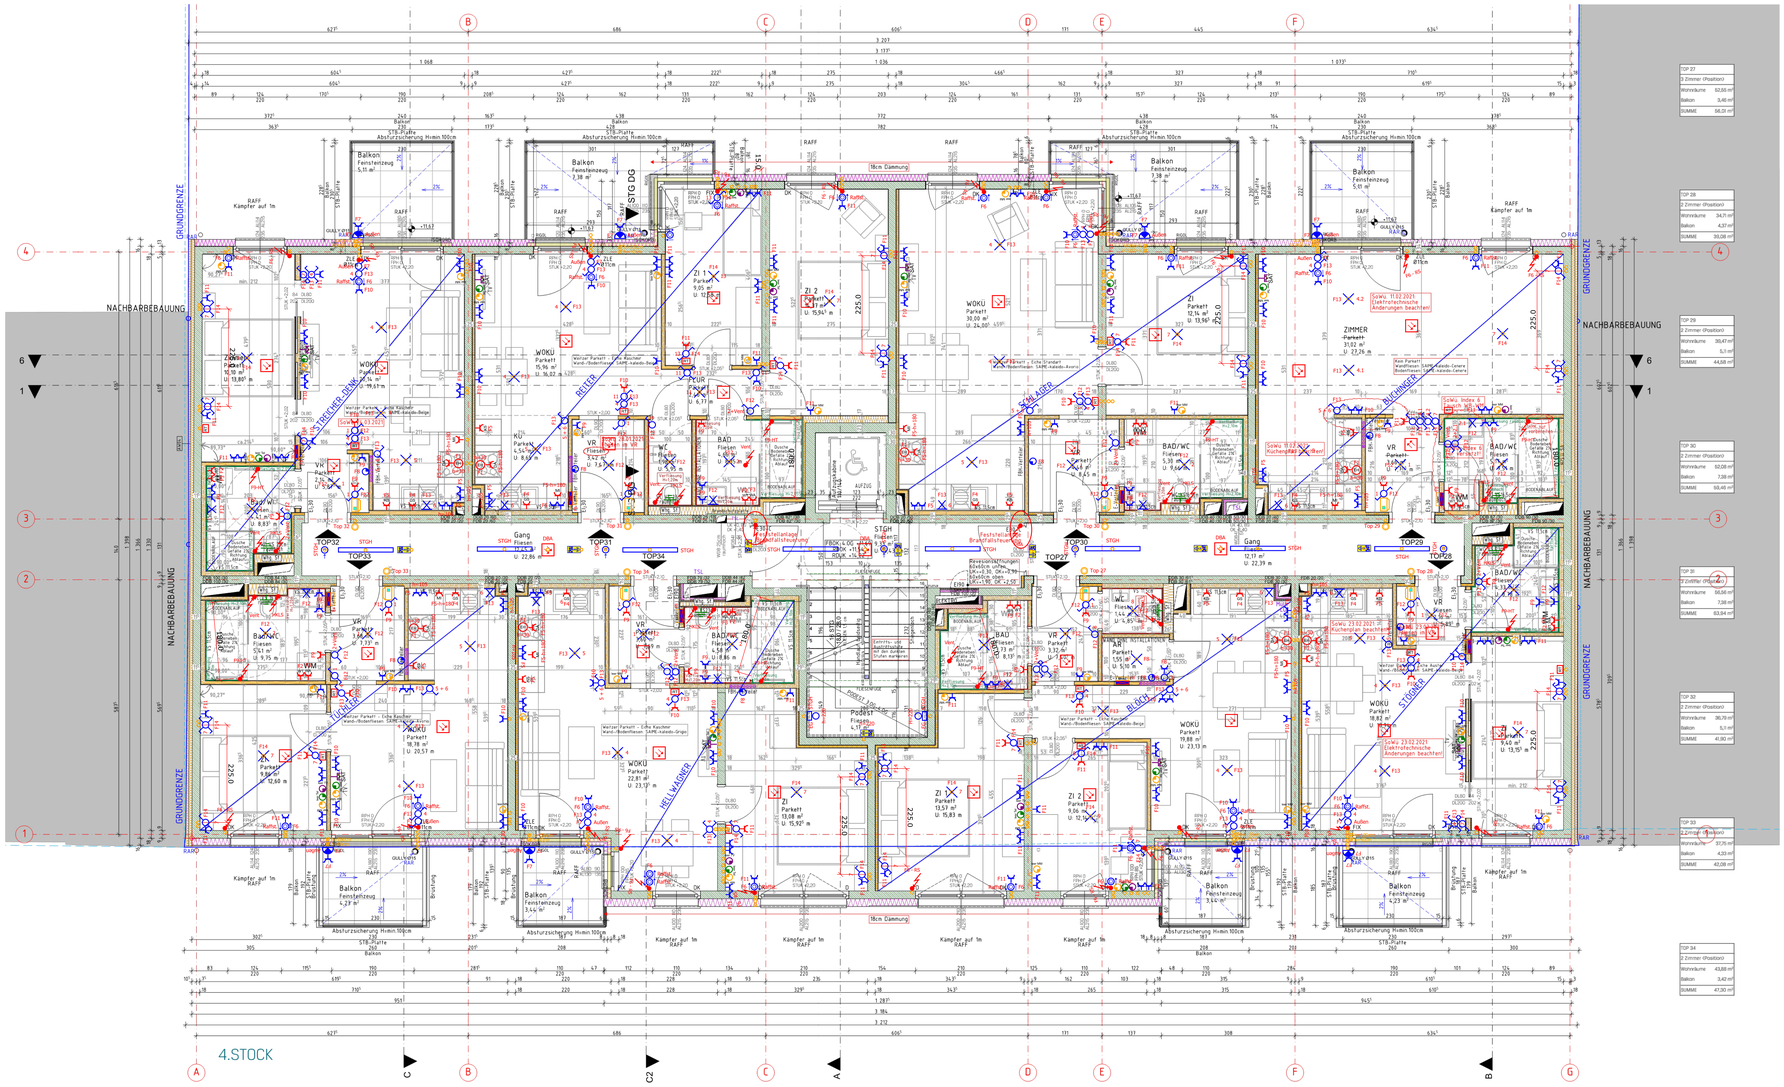


11.08.2020
Angaben über die DBA Bedienteile und Anschlusspositionen der Betriebsmittel laut AN-HKLS

07.10.2020: Einarbeitung der Anmerkungen Fa. ELCONS.

13.10.2020: Top 31 ZI1 Dose verschoben.

29.10.20: Auslässe für Brandfallsteuerung nachgetragen.

26.11.2020: Beleuchtung im Geländer entfallen.

Elektroinstallation	**Objekt Nr.: 4.OG**	**Änderungen**
		Datum / Vis.
Planhintergrund A2017-04_HEIGE20_PPL_3.-4.OG_Index 4_20210419	**Auftraggeber:** Auböck Bau GmbH Drosselstraße 36 4470 Enns	18.08.20 10.09.20 07.10.20 13.10.20 20.10.20 29.10.20 03.12.20 28.01.21 15.03.21 20.04.21 04.10.21
Firma: deg-elektro.gmbh Hasnerstraße 97 1160 Wien	**Objekt:** Heigerleinstraße 20-22 1160Wien Neubau Wohnhausanlage	
	Plan Nr.: A **Plan Gr.:** A0 **Mst:** 1:50	**Gezeichnet:** AM **Datum:** 16.06.2020