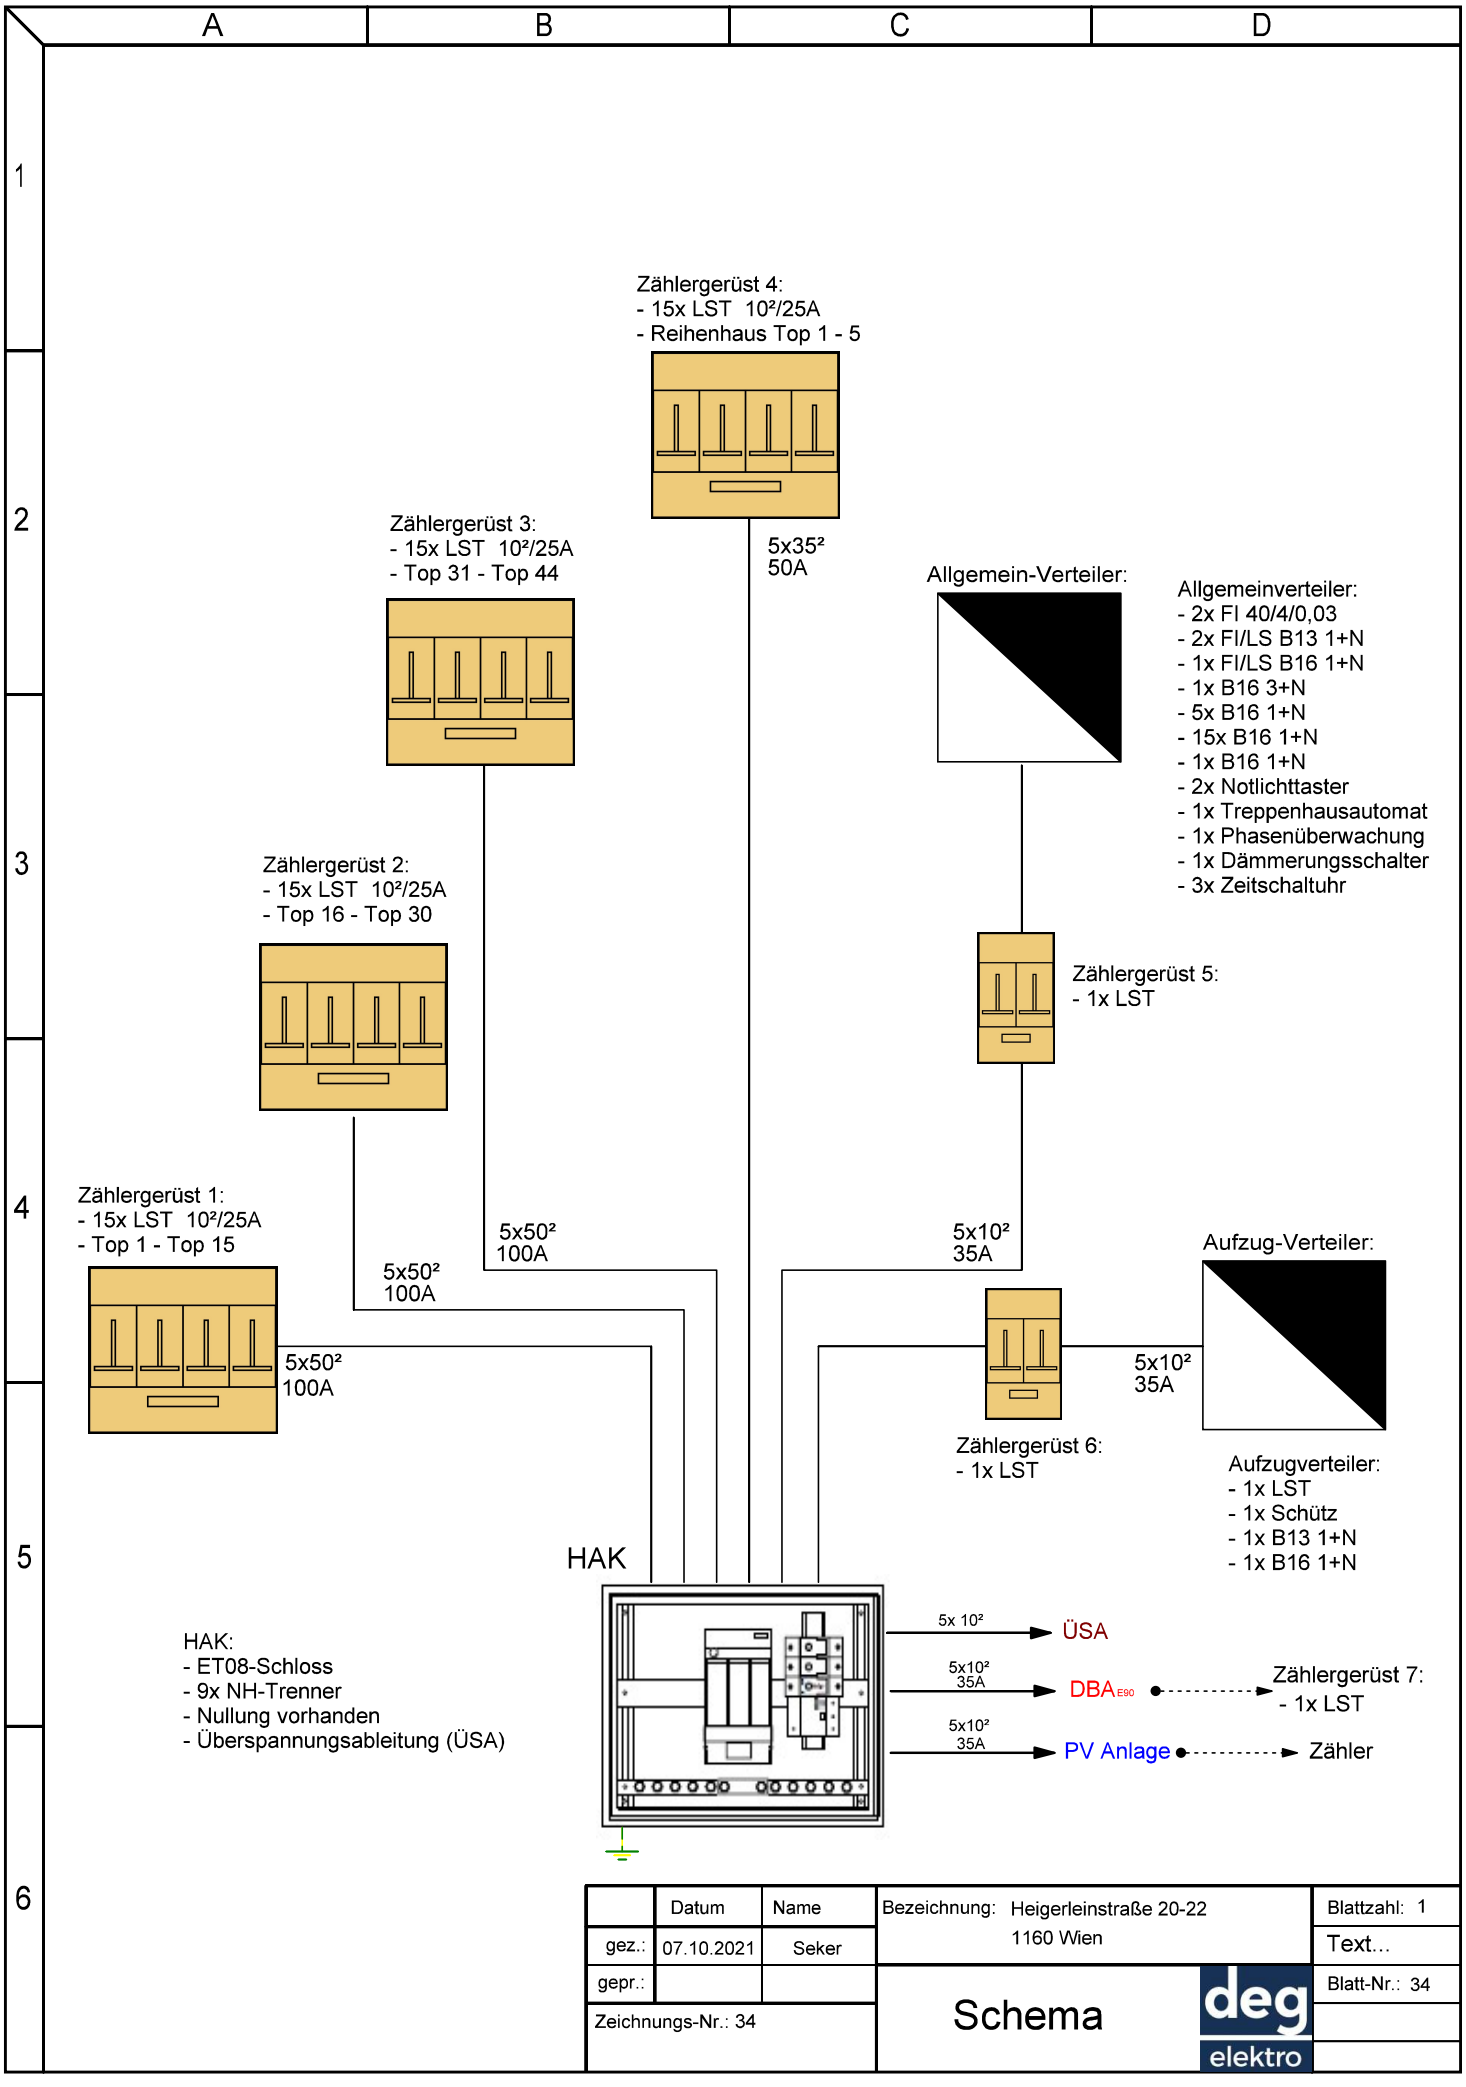

A
B
C
D
1
2
3
4
5
6
Zählergerüst 4:
- 15x LST 10²/25A
- Reihenhaus Top 1 - 5
5x35²
50A
Zählergerüst 3:
- 15x LST 10²/25A
- Top 31 - Top 44
Allgemein-Verteiler:
Allgemeinverteiler:
- 2x FI 40/4/0,03
- 2x FI/LS B13 1+N
- 1x FI/LS B16 1+N
- 1x B16 3+N
- 5x B16 1+N
- 15x B16 1+N
- 1x B16 1+N
- 2x Notlichttaster
- 1x Treppenhausautomat
- 1x Phasenüberwachung
- 1x Dämmerungsschalter
- 3x Zeitschaltuhr
Zählergerüst 2:
- 15x LST 10²/25A
- Top 16 - Top 30
Zählergerüst 5:
- 1x LST
Zählergerüst 1:
- 15x LST 10²/25A
- Top 1 - Top 15
5x50²
100A
5x50²
100A
5x50²
100A
5x10²
35A
Aufzug-Verteiler:
5x10²
35A
Zählergerüst 6:
- 1x LST
Aufzugverteiler:
- 1x LST
- 1x Schütz
- 1x B13 1+N
- 1x B16 1+N
HAK
HAK:
- ET08-Schloss
- 9x NH-Trenner
- Nullung vorhanden
- Überspannungsableitung (ÜSA)
5x 10²
ÜSA
5x10²
35A
DBA E90
Zählergerüst 7:
- 1x LST
5x10²
35A
PV Anlage
Zähler
Datum
Name
gez.:
07.10.2021
Seker
gepr.:
Zeichnungs-Nr.: 34
Bezeichnung: Heigerleinstraße 20-22
1160 Wien
Schema
deg
elektro
Blattzahl: 1
Text...
Blatt-Nr.: 34