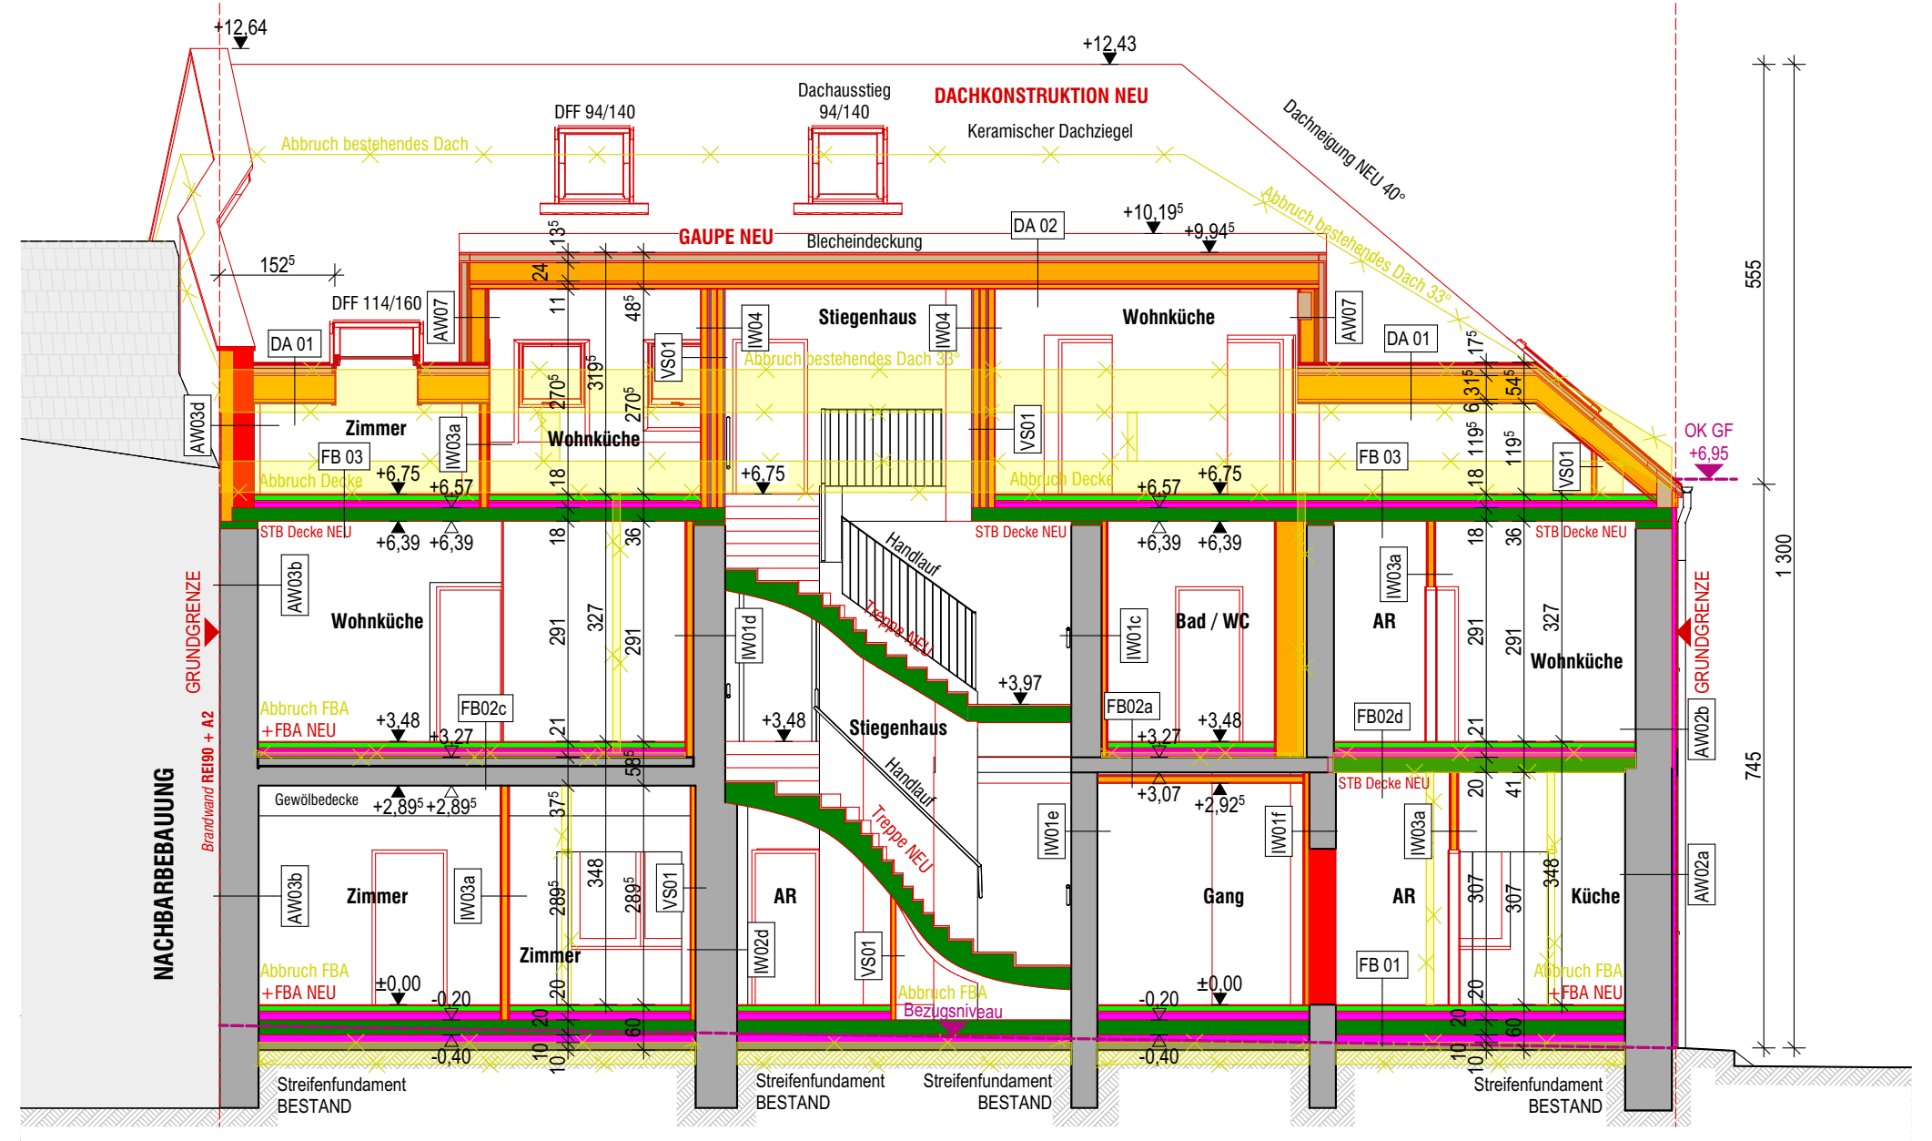

SCHNITT 2-2 M 1:100

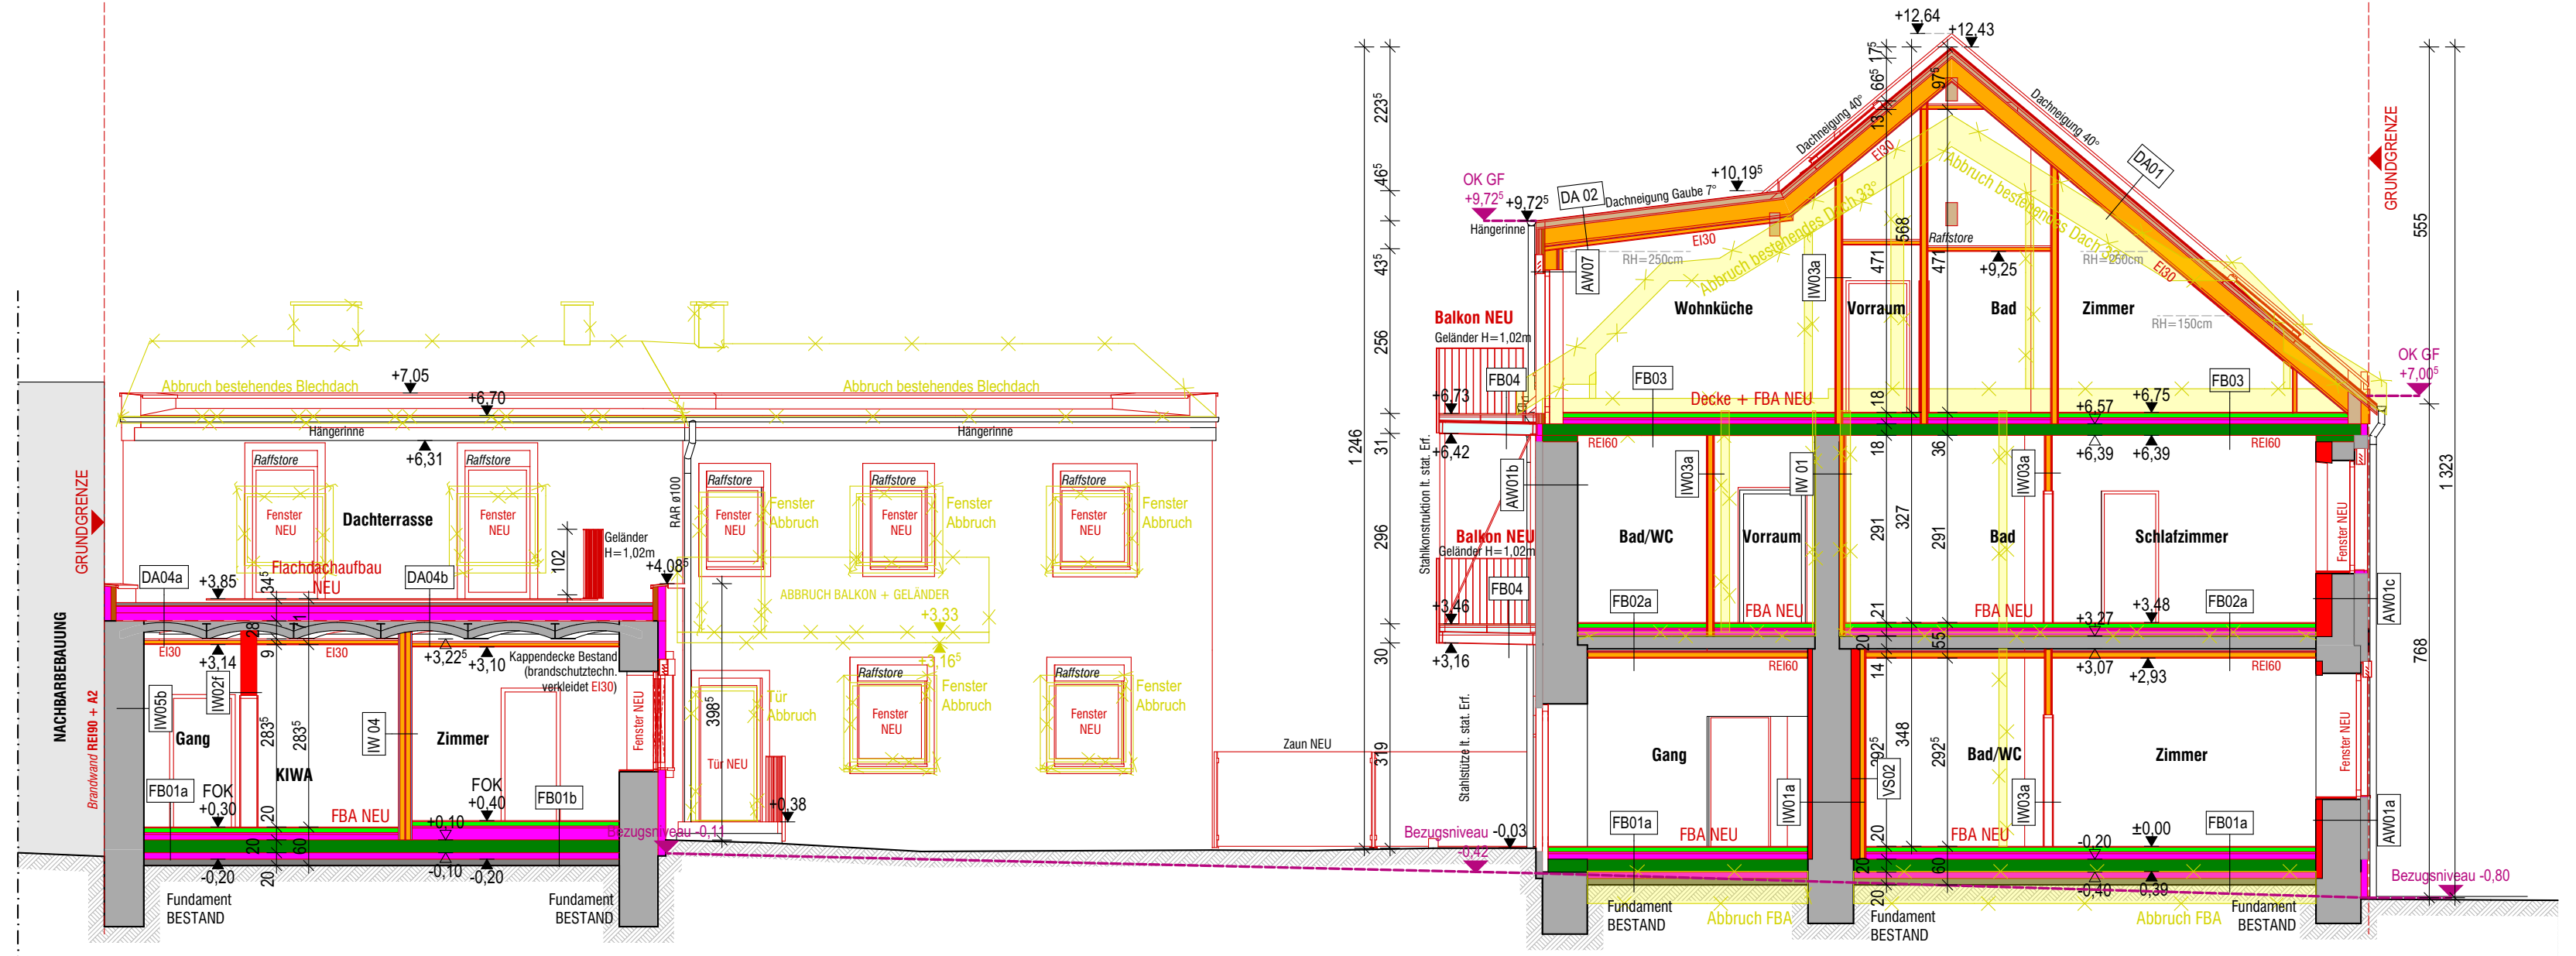

SCHNITT 1-1 M 1:100

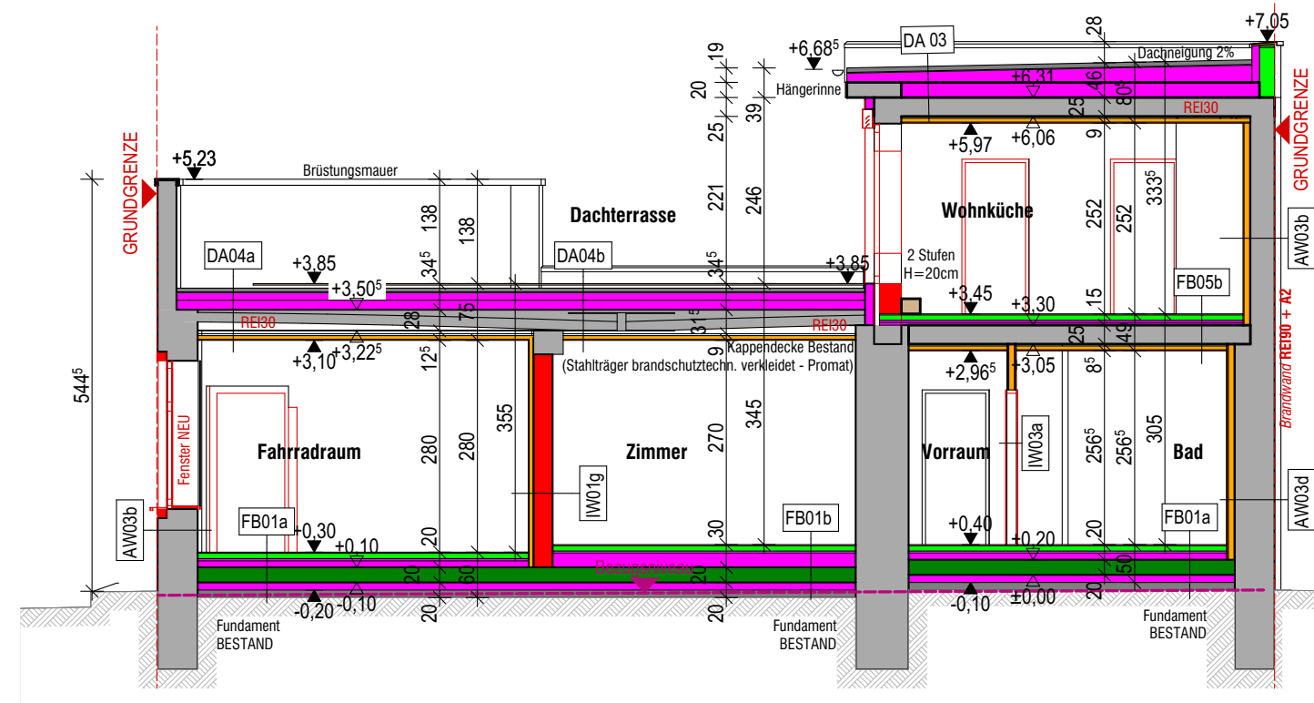

SCHNITT 3-3 M 1:100

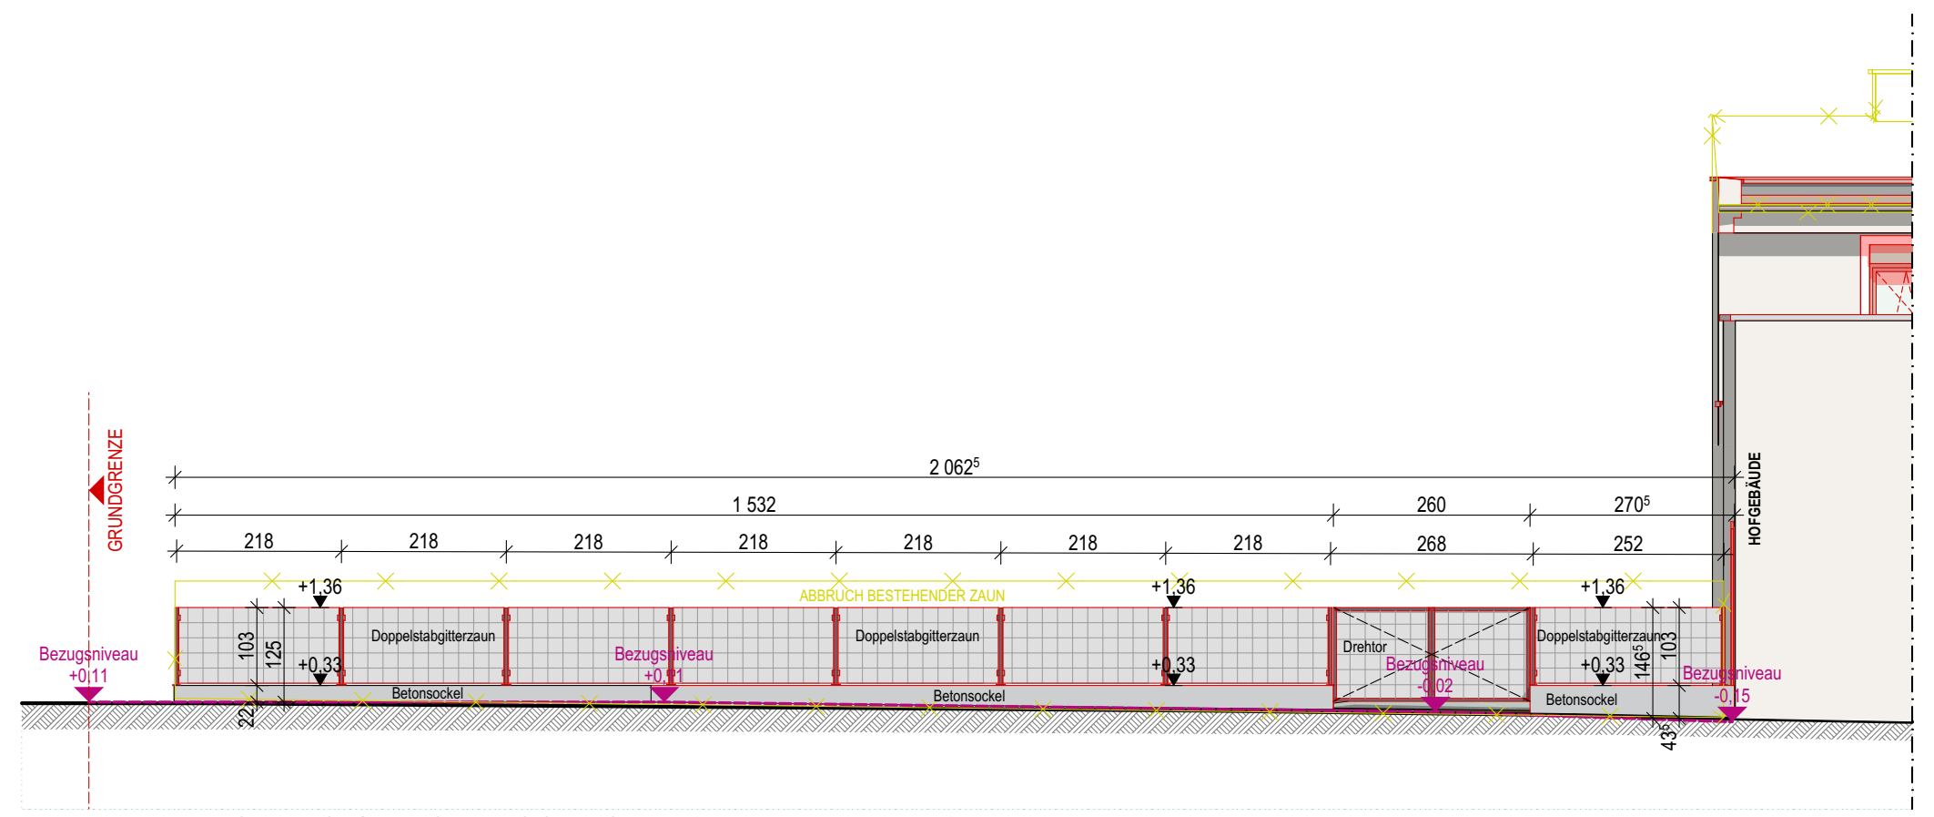

WESTANSICHT STRASSENSEITIGE EINFRIEDUNG M 1:100

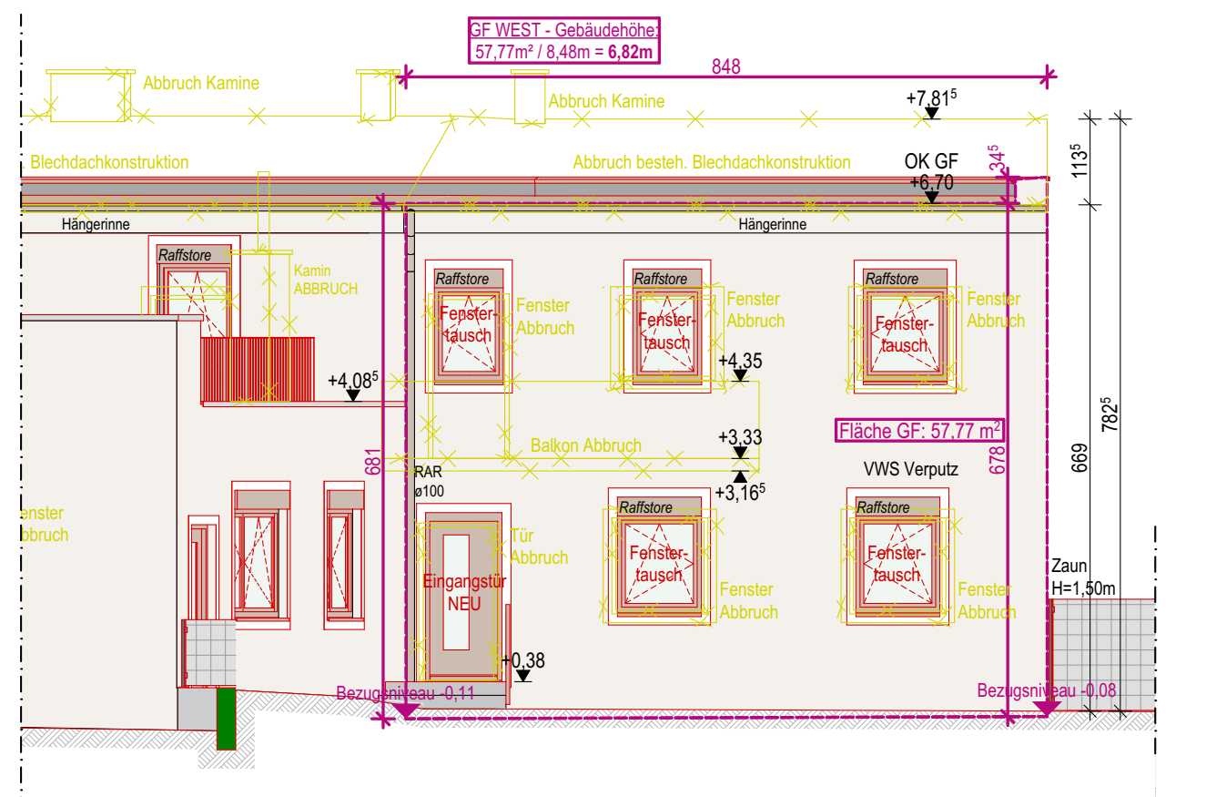

WESTANSICHT HOFGEBÄUDE M 1:100

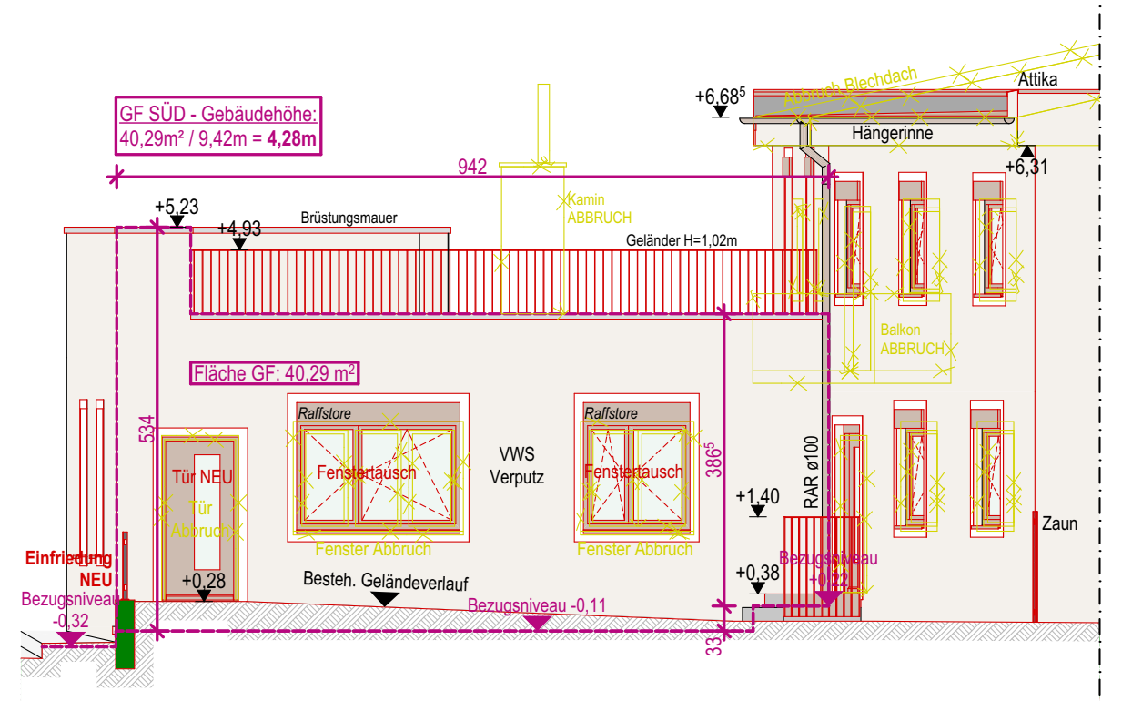

SÜDANSICHT HOFGEBÄUDE M 1:100

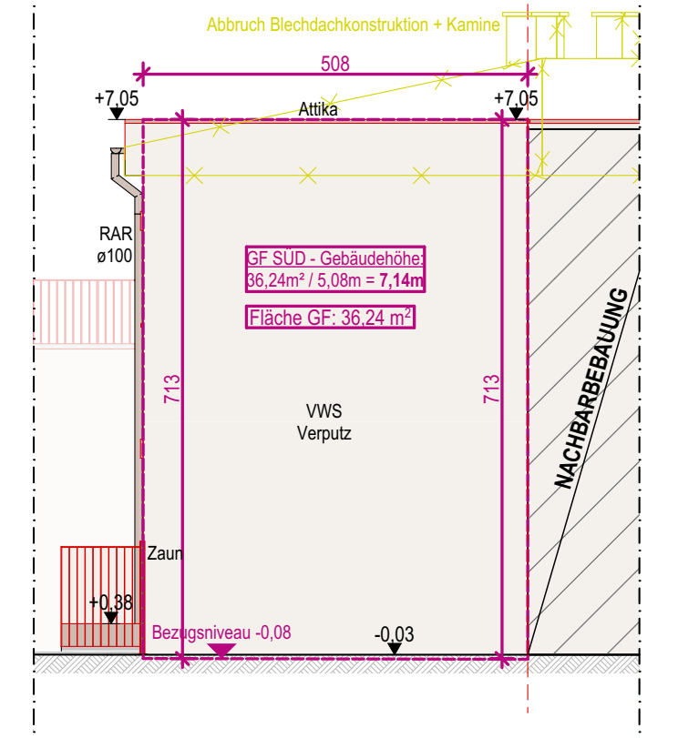

SÜDANSICHT 2 HOFGEBÄUDE M 1:100

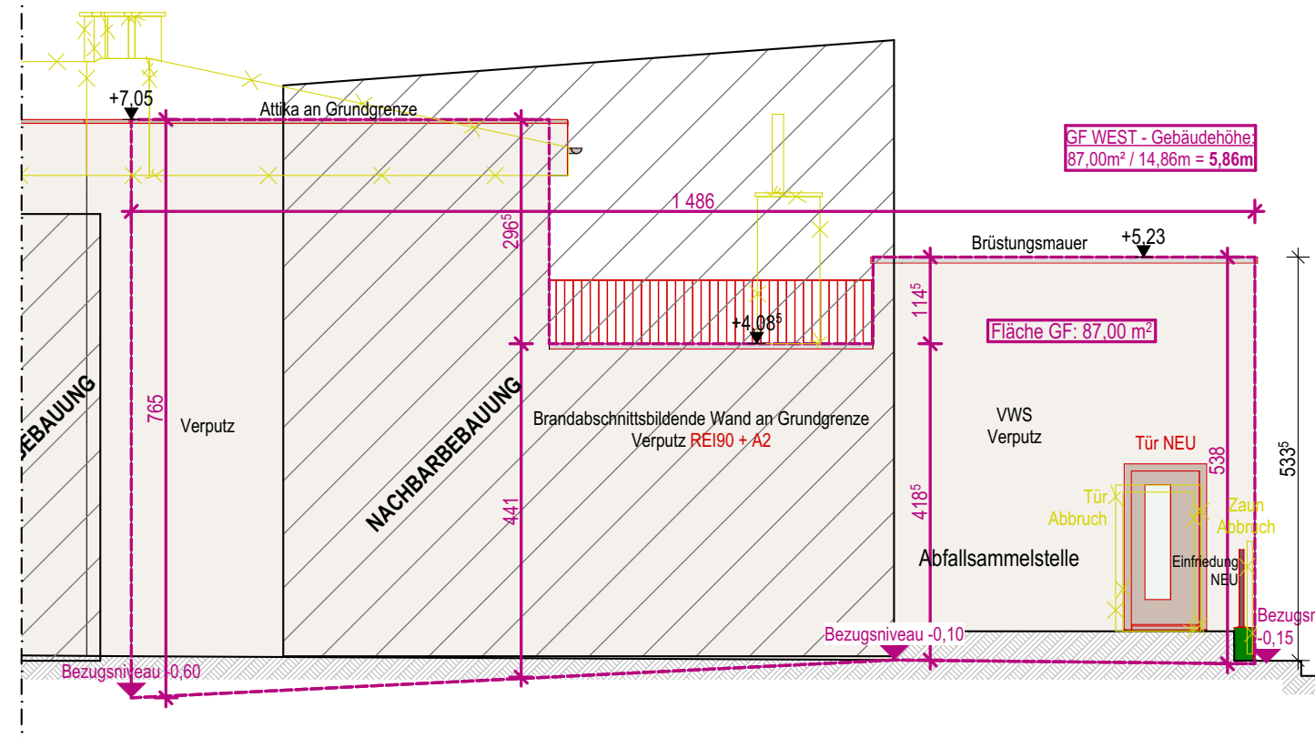

NORDANSICHT HOFGEBÄUDE M 1:100

BRUTTO - GESCHOSSFLÄCHE:		GRUNDSTÜCKSGRÖSSE	657,00 m²
STRASSENTRAKT EG	255,98 m²		
STRASSENTRAKT 1.OG	255,98 m²	ÜBERBAUTE FLÄCHE:	
STRASSENTRAKT DG	255,98 m²	STRASSENTRAKT	276,89 m²
STRASSENTRAKT GESAMT	767,94 m²	HOFTRAKT	169,54 m²
		ÜBERBAUTE FLÄCHE GESAMT	446,43 m²
HOFTRAKT EG	167,40 m²		
HOFTRAKT 1.OG	85,89 m²	BRUTTO - RAUMINHALT:	
HOFGEBÄUDE GESAMT	253,29 m²	STRASSENTRAKT	2.621,69 m²
		HOFTRAKT	941,18 m²
BRUTTO - GESCHOSSFLÄCHE GESAMT	1.021,23 m²	BRUTTO - RAUMINHALT GESAMT	3.562,87 m²

GstNr .18 EZ 1056 1/1 DI Wolfgang Bartmann Chemin Chez Buffet null, FRA 01170 Crozet, Frankreich	**GstNr 131 EZ 1157** Ing. Doris Bartmann Kirchenplatz 12, 2512 Tribuswinkel Ing. Konstantin Bartmann Kirchenplatz 12, 2512 Tribuswinkel	**GstNr .19 EZ 51** 1/1	**GstNr 1411/2 EZ 1526** Land Niederösterreich (Landesstraßenverwaltung) öffentliches Gut Amt der NÖ Landesregierung, Gruppe Straßenbau Landhausplatz 1, 3100 St. Pölten
GstNr .22 EZ 2083 1/1 Acar Zafer Baslergasse 50-66/41/22, 1230 Wien	**GstNr .1410/9 EZ 1525** 1/1 Stadtgemeinde Traiskirchen Öffentliches Gut Hauptplatz 13, 2514 Traiskirchen	**GstNr 1410/7 EZ 1526** Land Niederösterreich (Landesstraßenverwaltung) öffentliches Gut Amt der NÖ Landesregierung, Gruppe Straßenbau Landhausplatz 1, 3100 St. Pölten	**GstNr .23/2 EZ 2020** 1/2 Josef Willich Pfarrgasse 3, 2512 Tribuswinkel 1/2 Ingrid Willich Pfarrgasse 3, 2512 Tribuswinkel
GstNr .23/1 EZ 80 1/2 Felix Kohlert Pfarrgasse 5, 2512 Tribuswinkel 1/2 Elisabeth Kohlert Pfarrgasse 5, 2512 Tribuswinkel	**GstNr .1410/11 EZ 1525** 1/1 Stadtgemeinde Traiskirchen Öffentliches Gut Hauptplatz 13, 2514 Traiskirchen	**GstNr 1410/1 EZ 1526** Land Niederösterreich (Landesstraßenverwaltung) öffentliches Gut Amt der NÖ Landesregierung, Gruppe Straßenbau Landhausplatz 1, 3100 St. Pölten	**GstNr .22 EZ 2083** 1/1 Acar Zafer Baslergasse 50-66/41/22, 1230 Wien

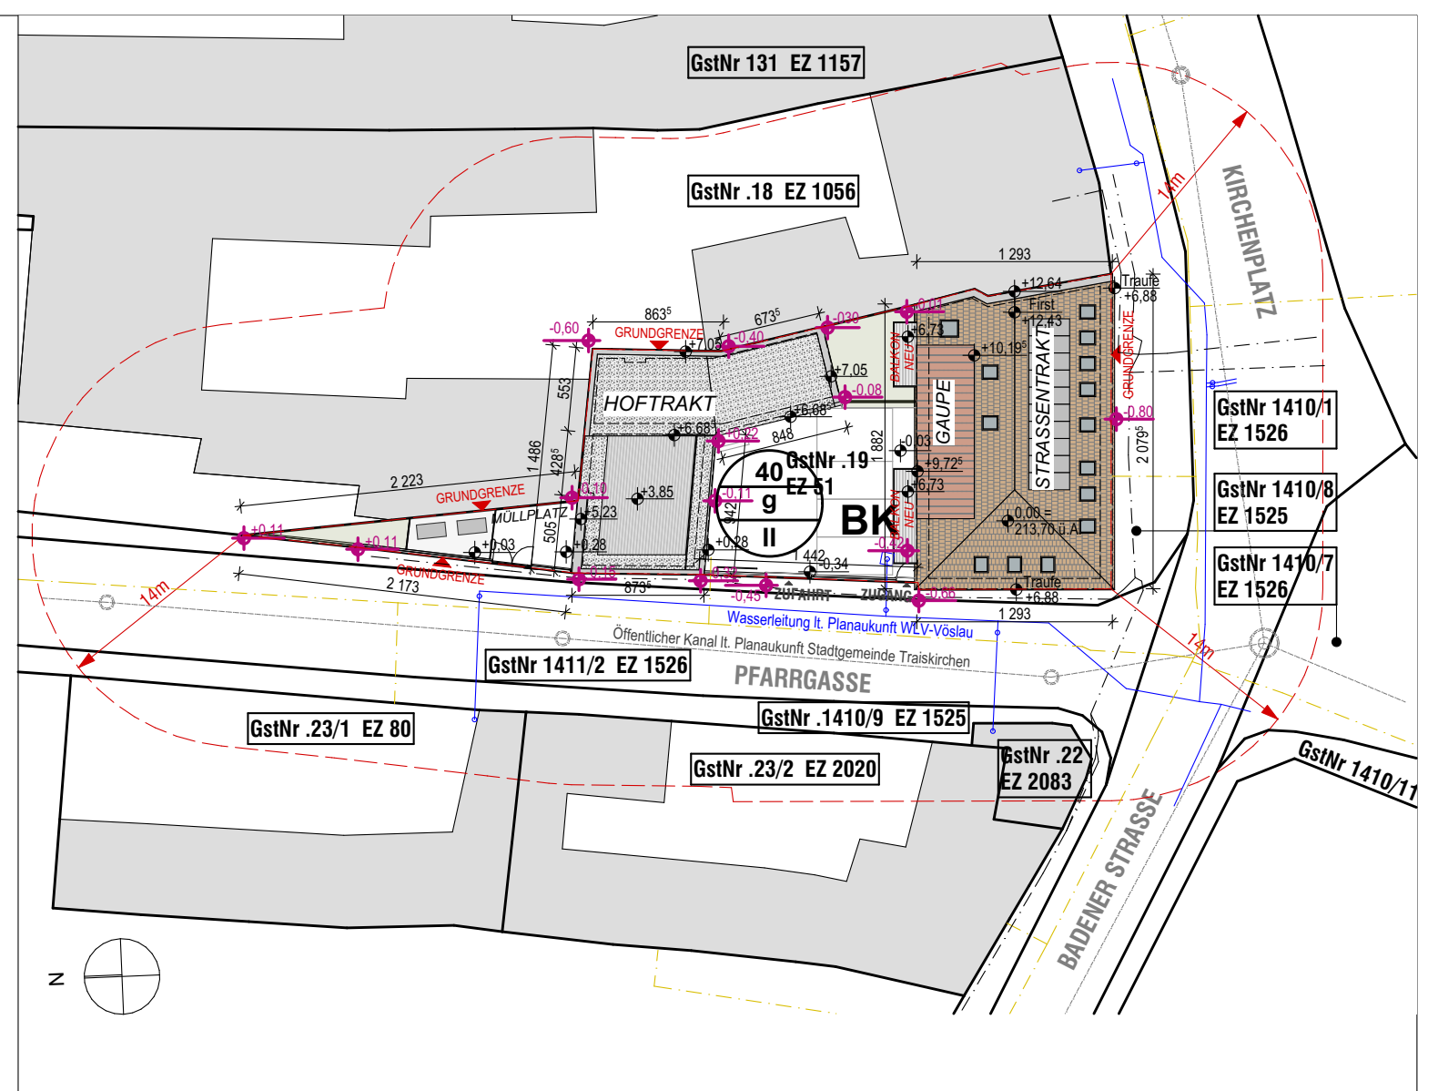

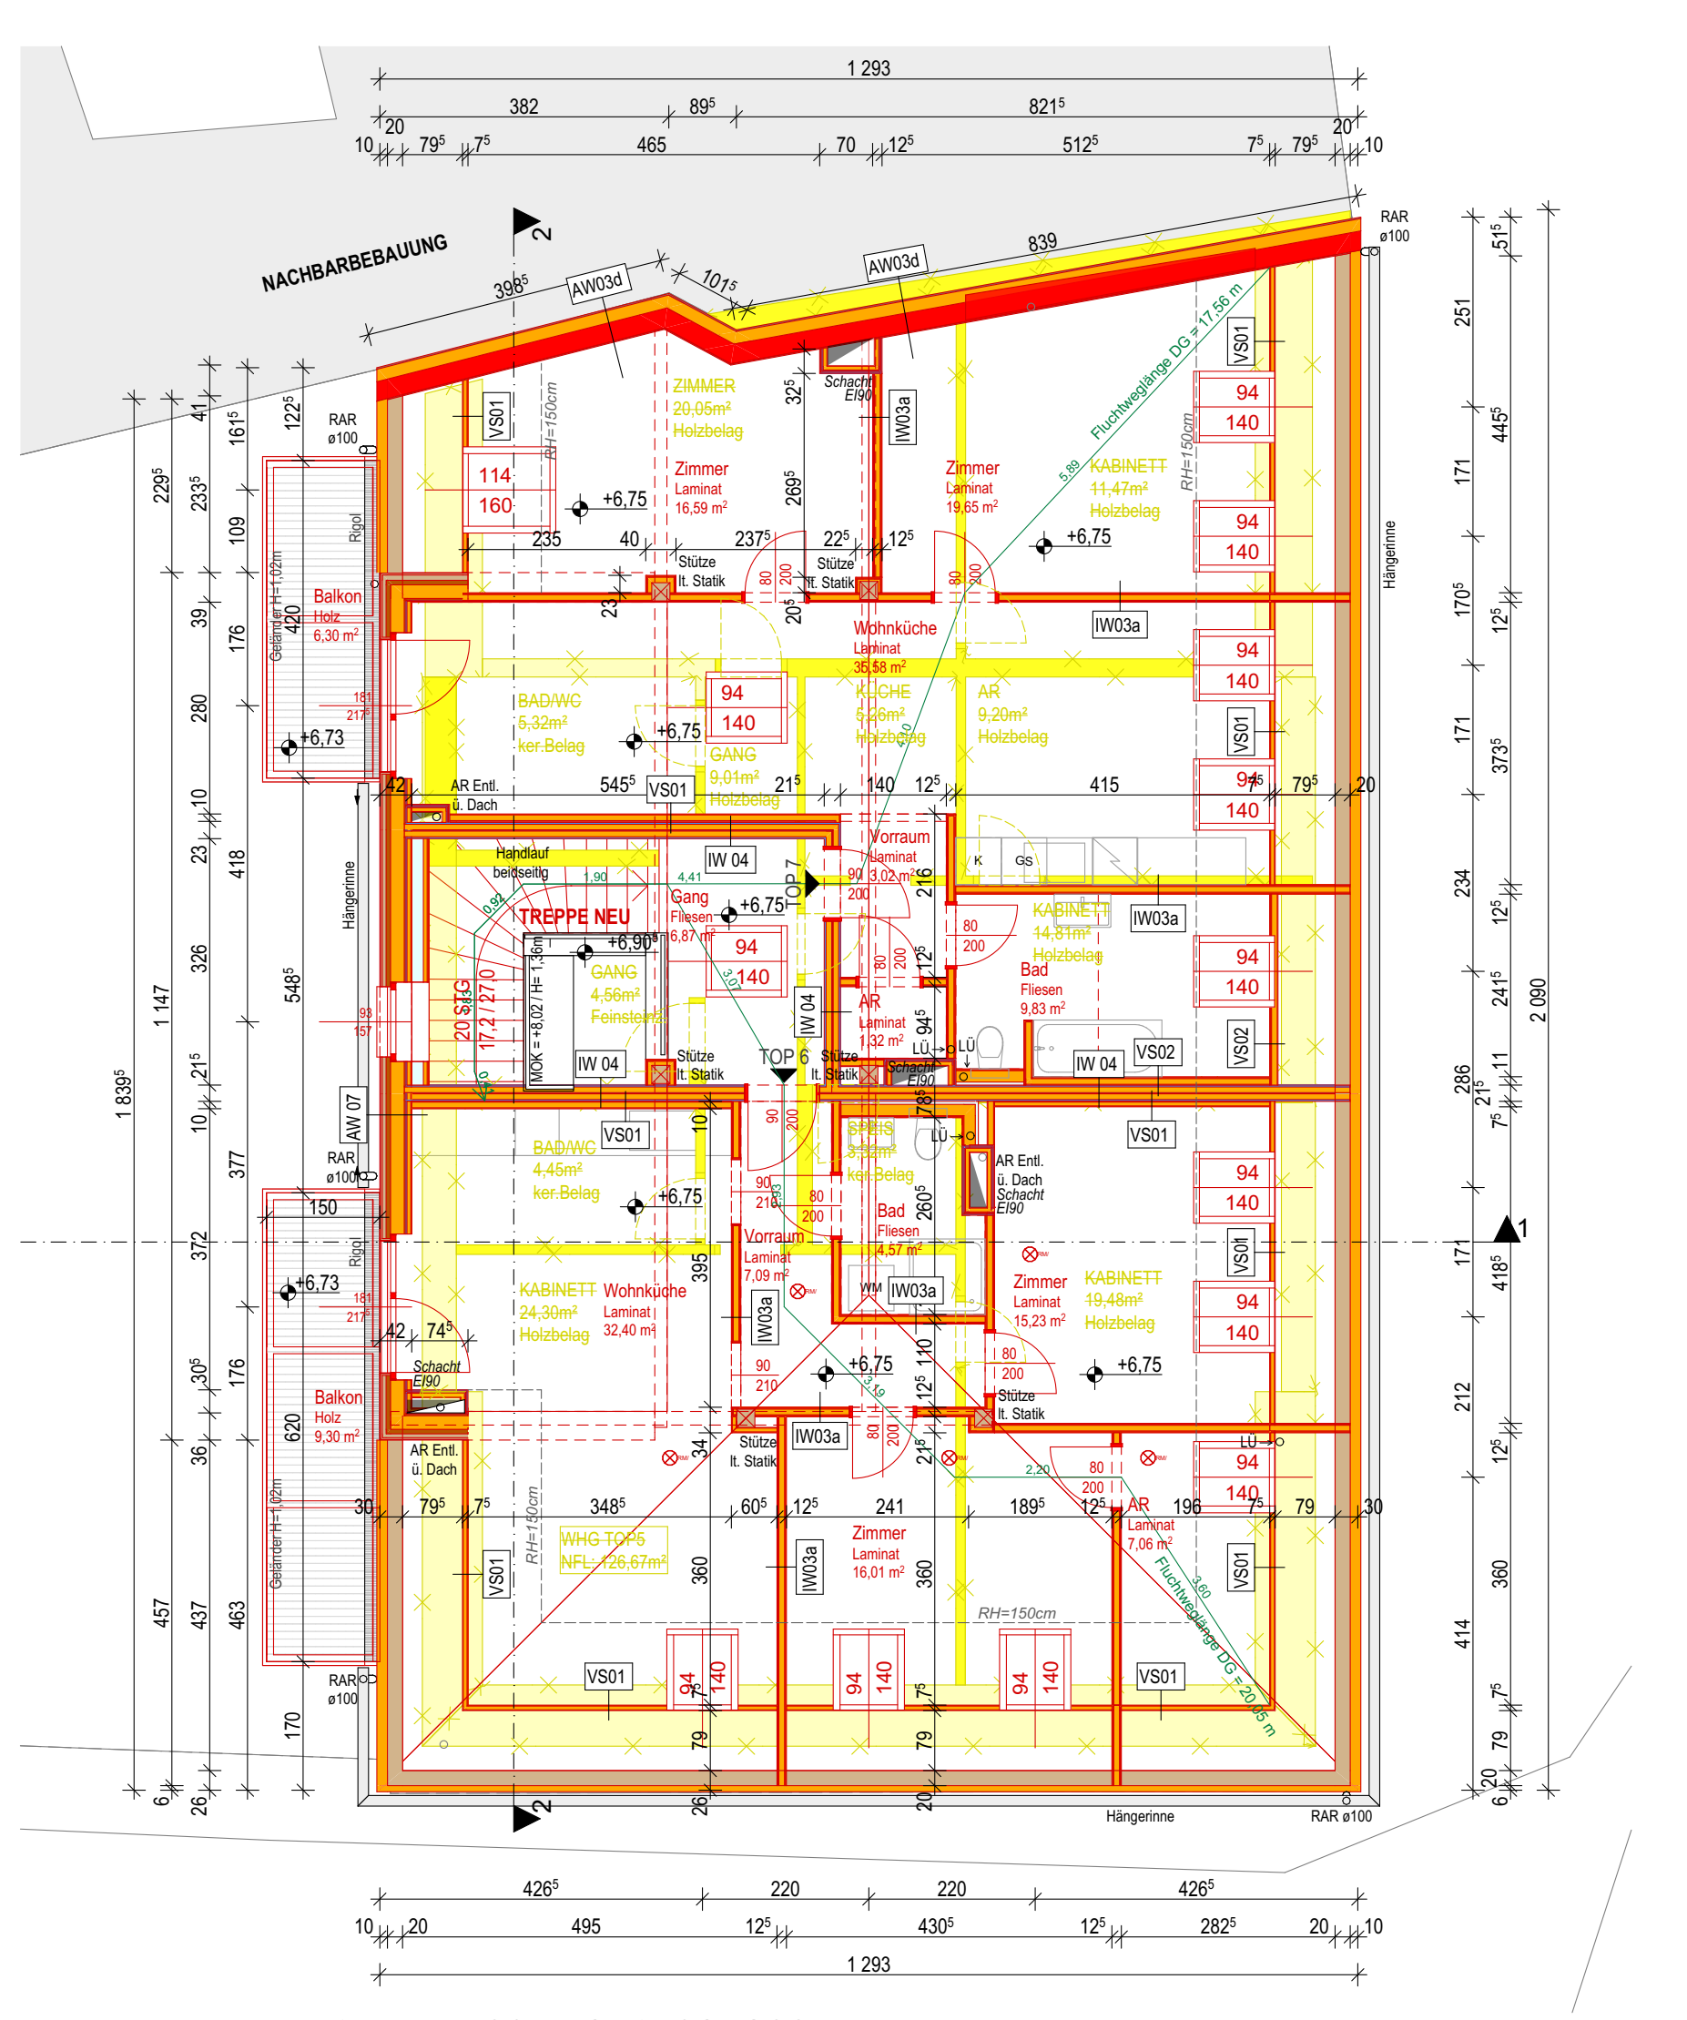

GRUNDRISS DACHGESCHOSS M 1:100

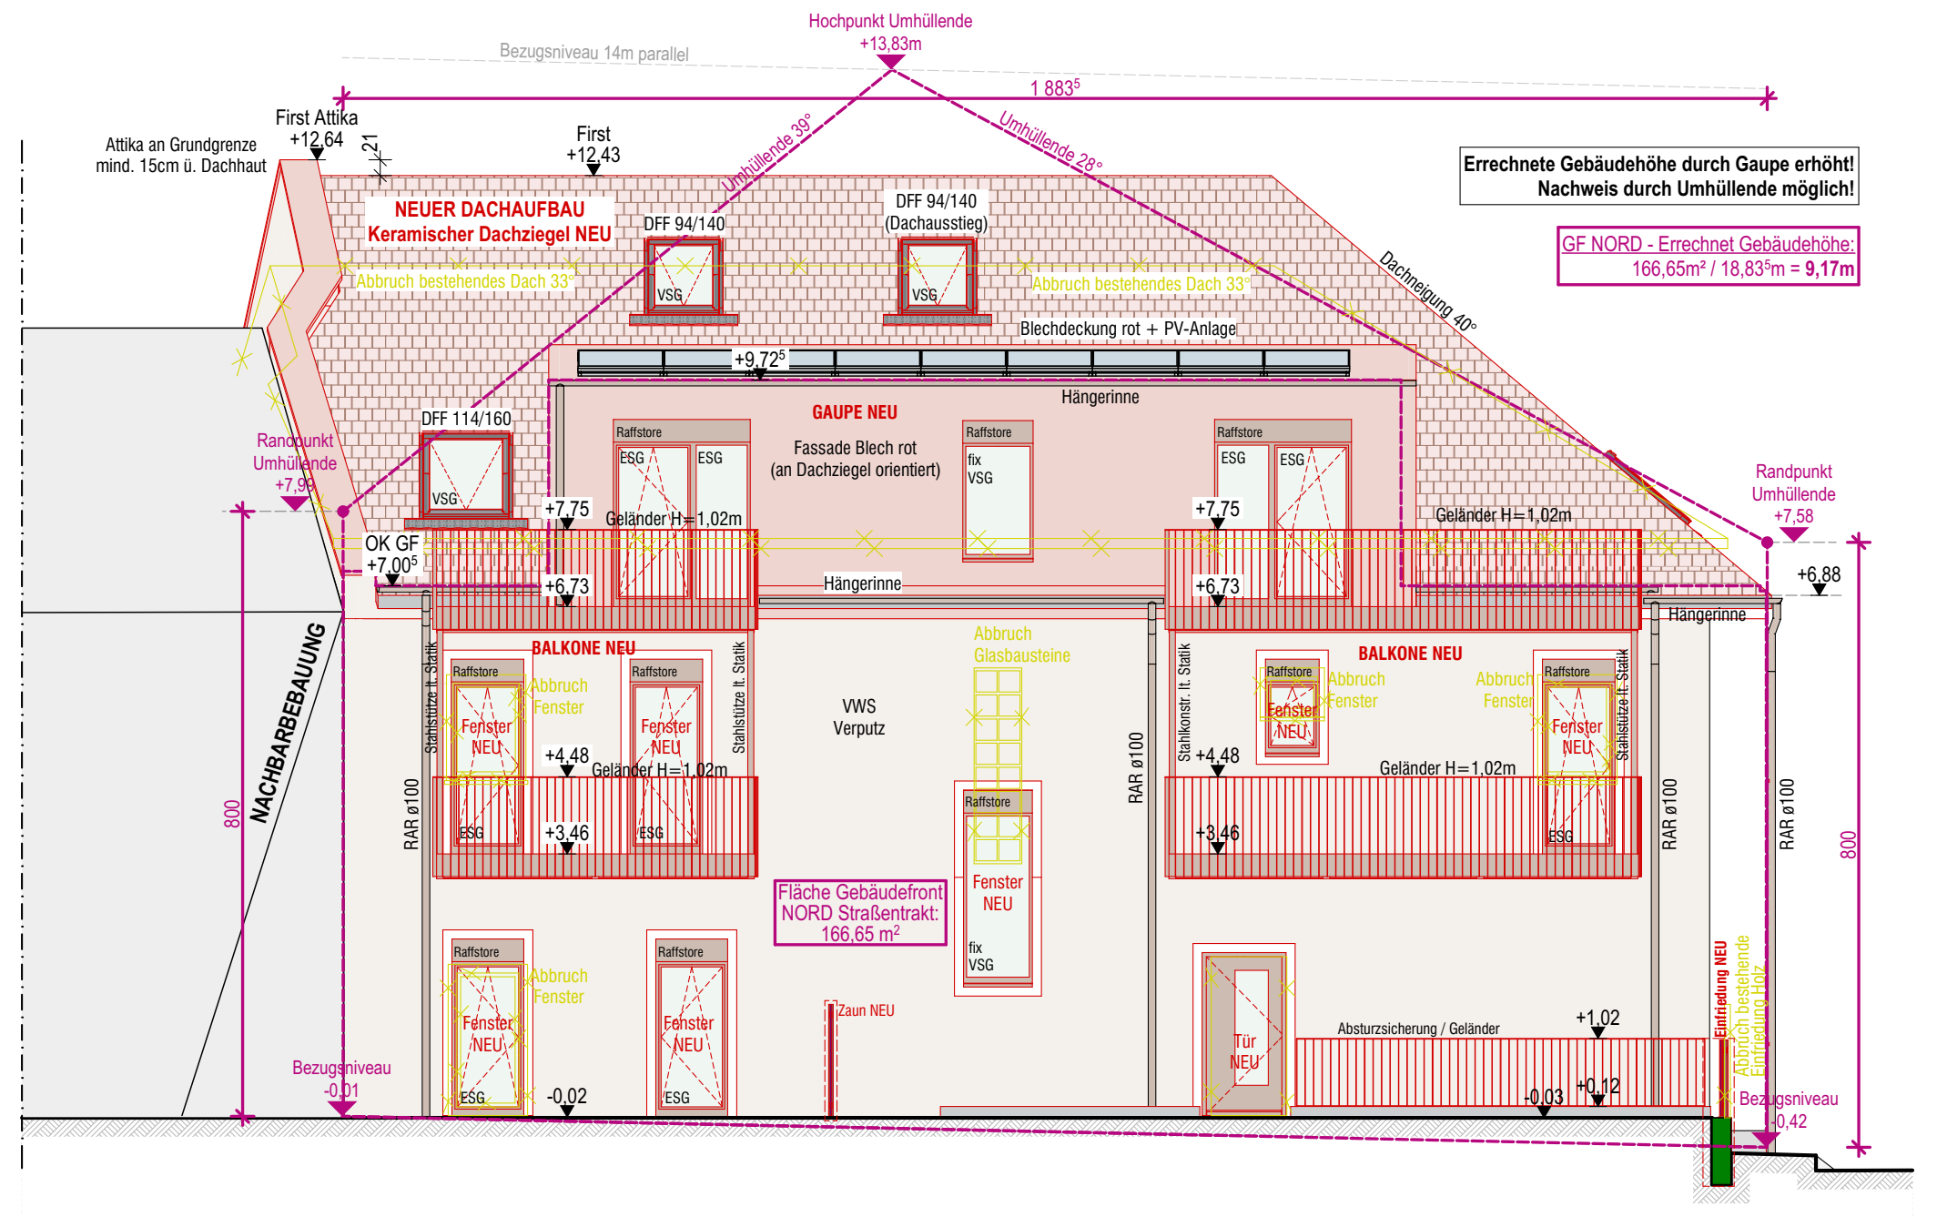
NEUER DACHAUFBAU
Keramischer Dachziegel NEU
GAUPE NEU
BALKONE NEU
Errechnete Gebäudehöhe durch Gaupe erhöht! Nachweis durch Umhüllende möglich!
NACHBARBEBAUUNG

NORDANSICHT STRASSENTRAKT M 1:100

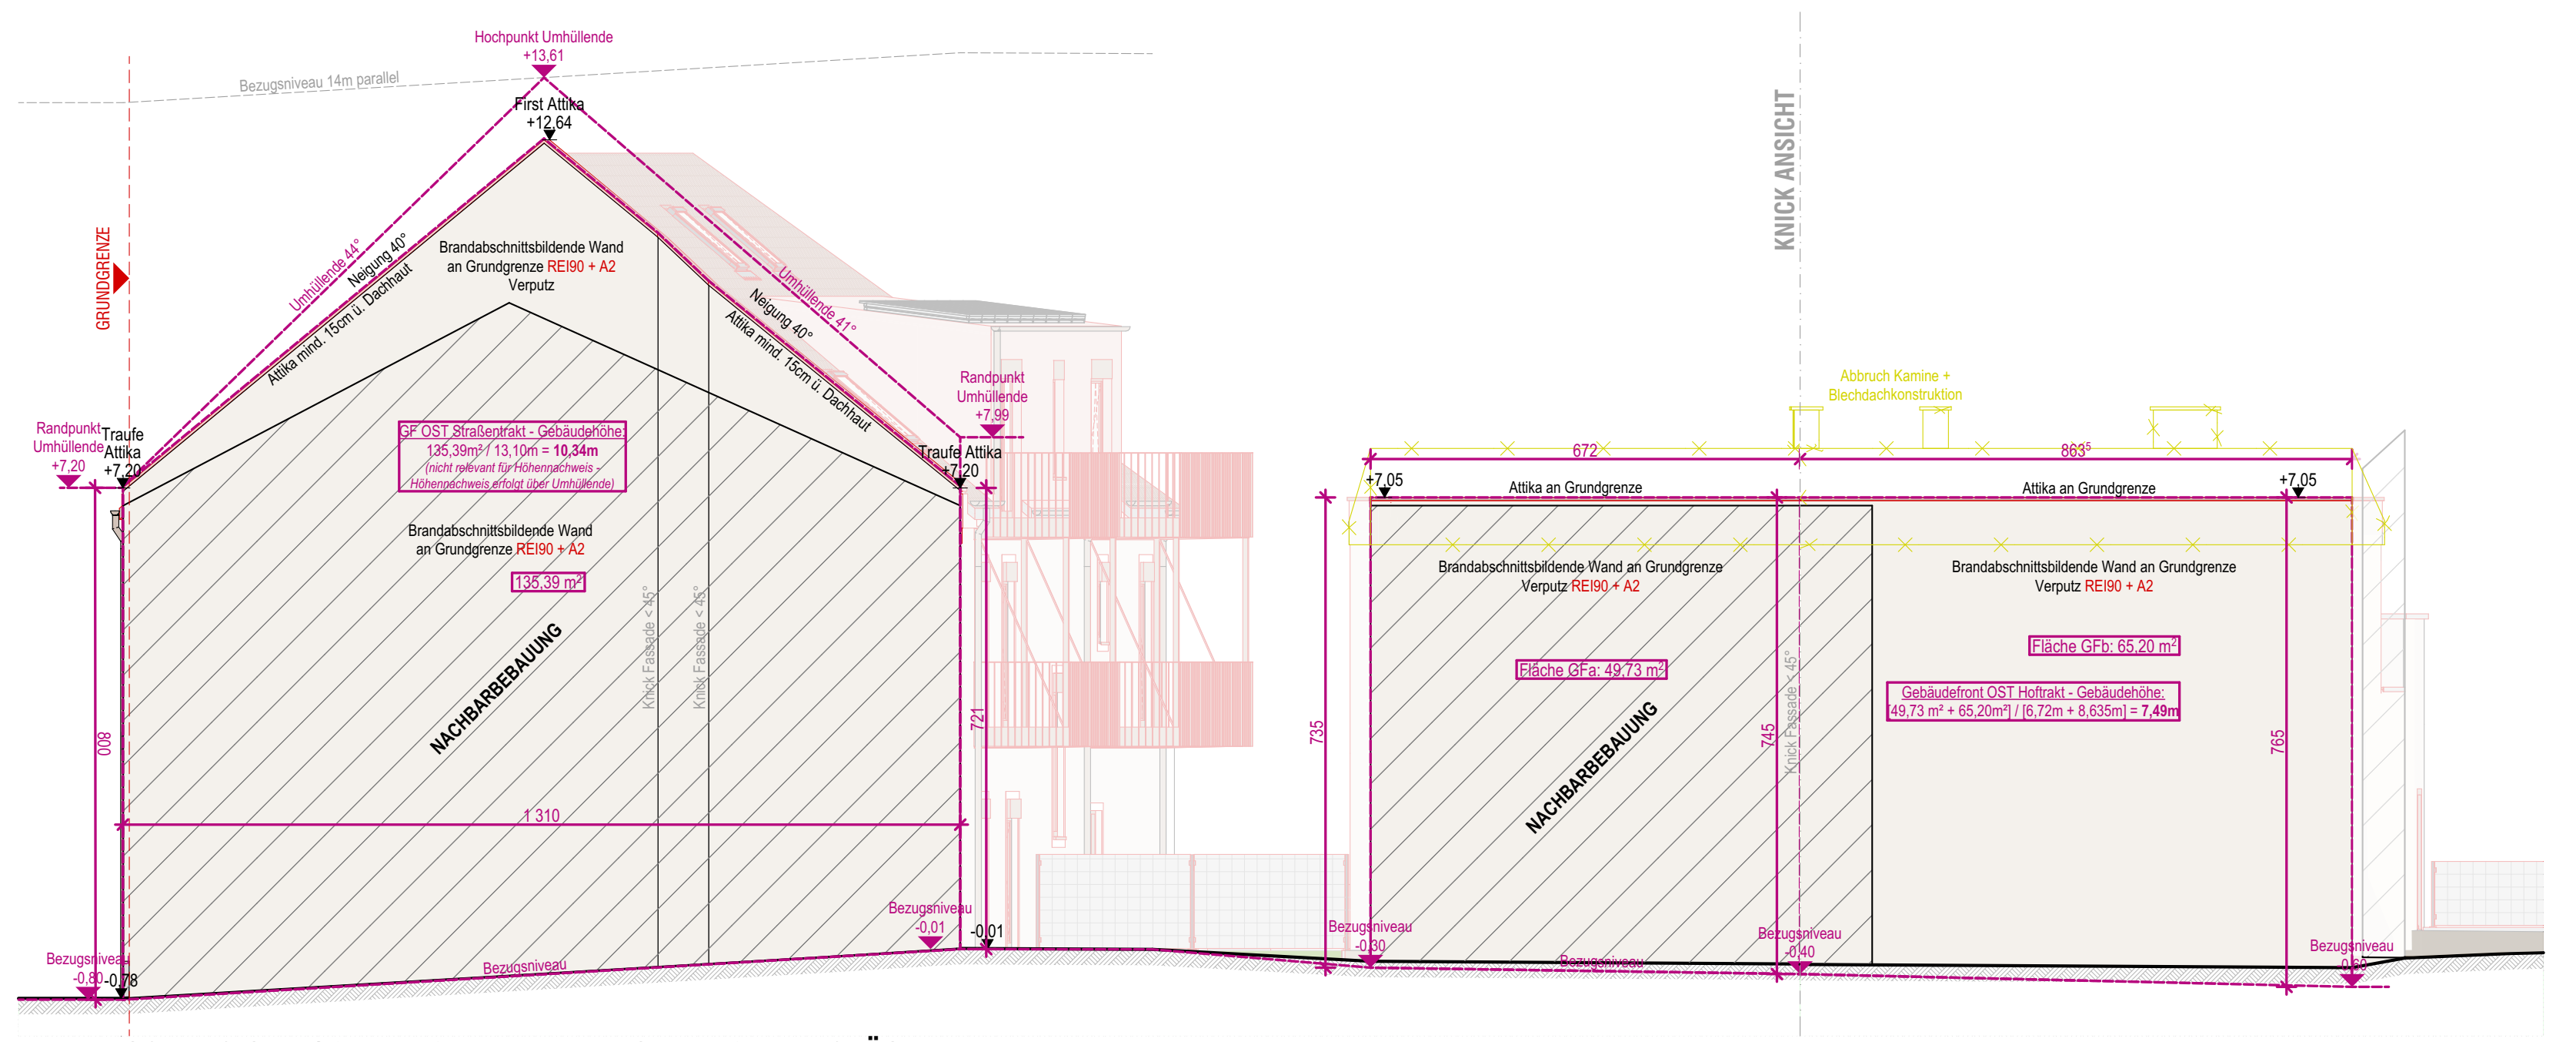

OSTANSICHT / GRUNDGRENZE ZU NACHBARGRUNDSTÜCK M 1:100

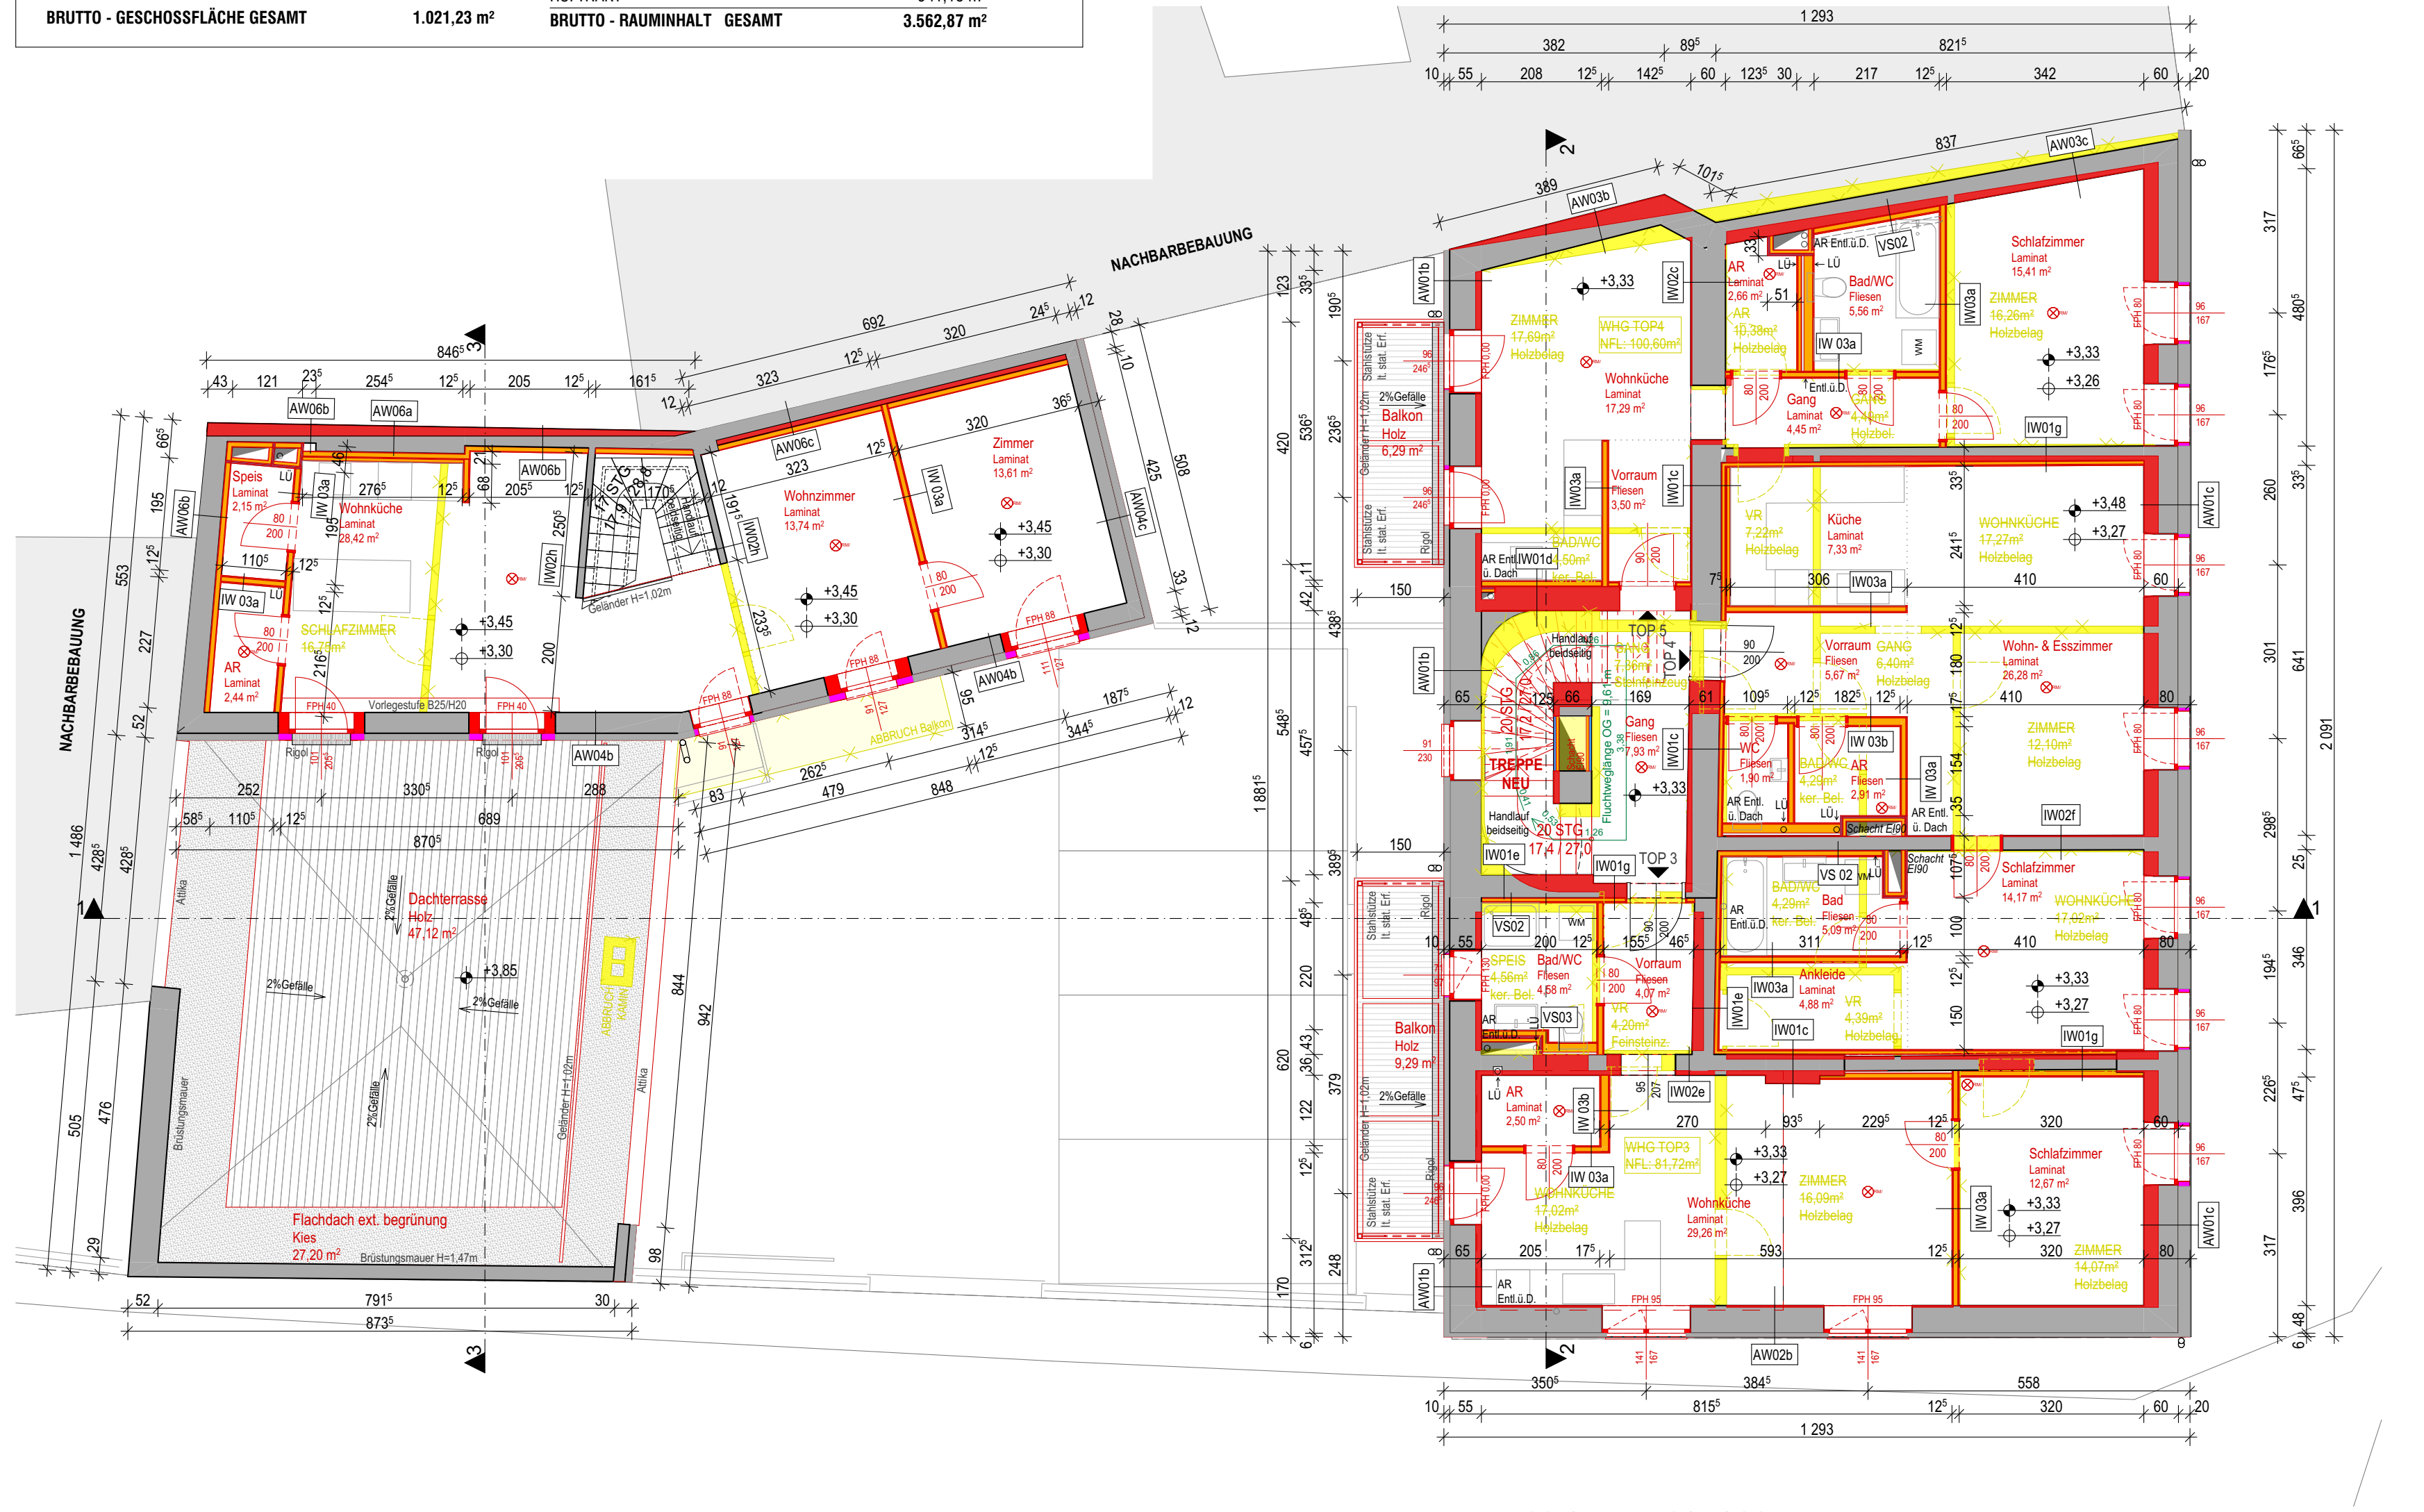

GRUNDRISS OBERGESCHOSS M 1:100

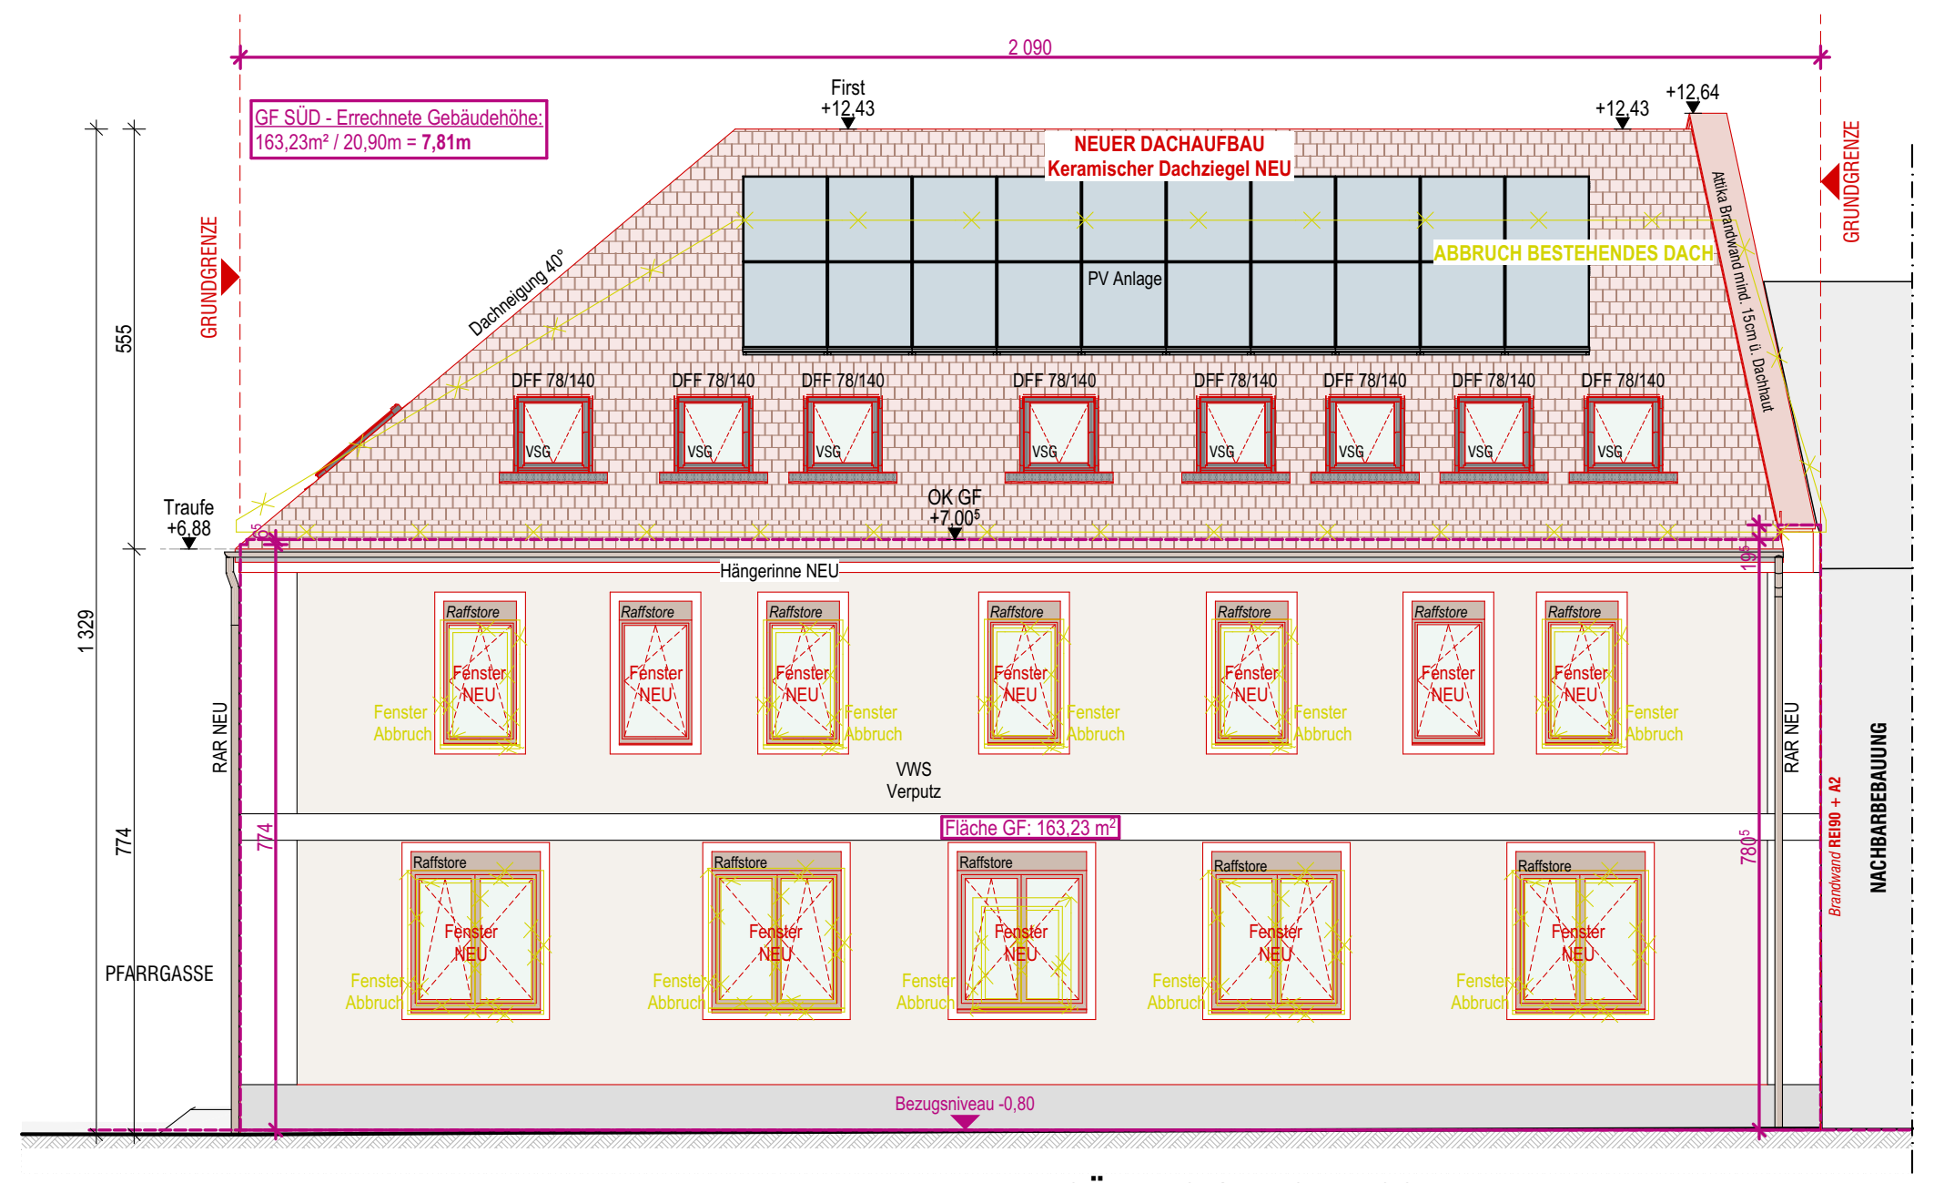

SÜDANSICHT STRASSENTRAKT M 1:100

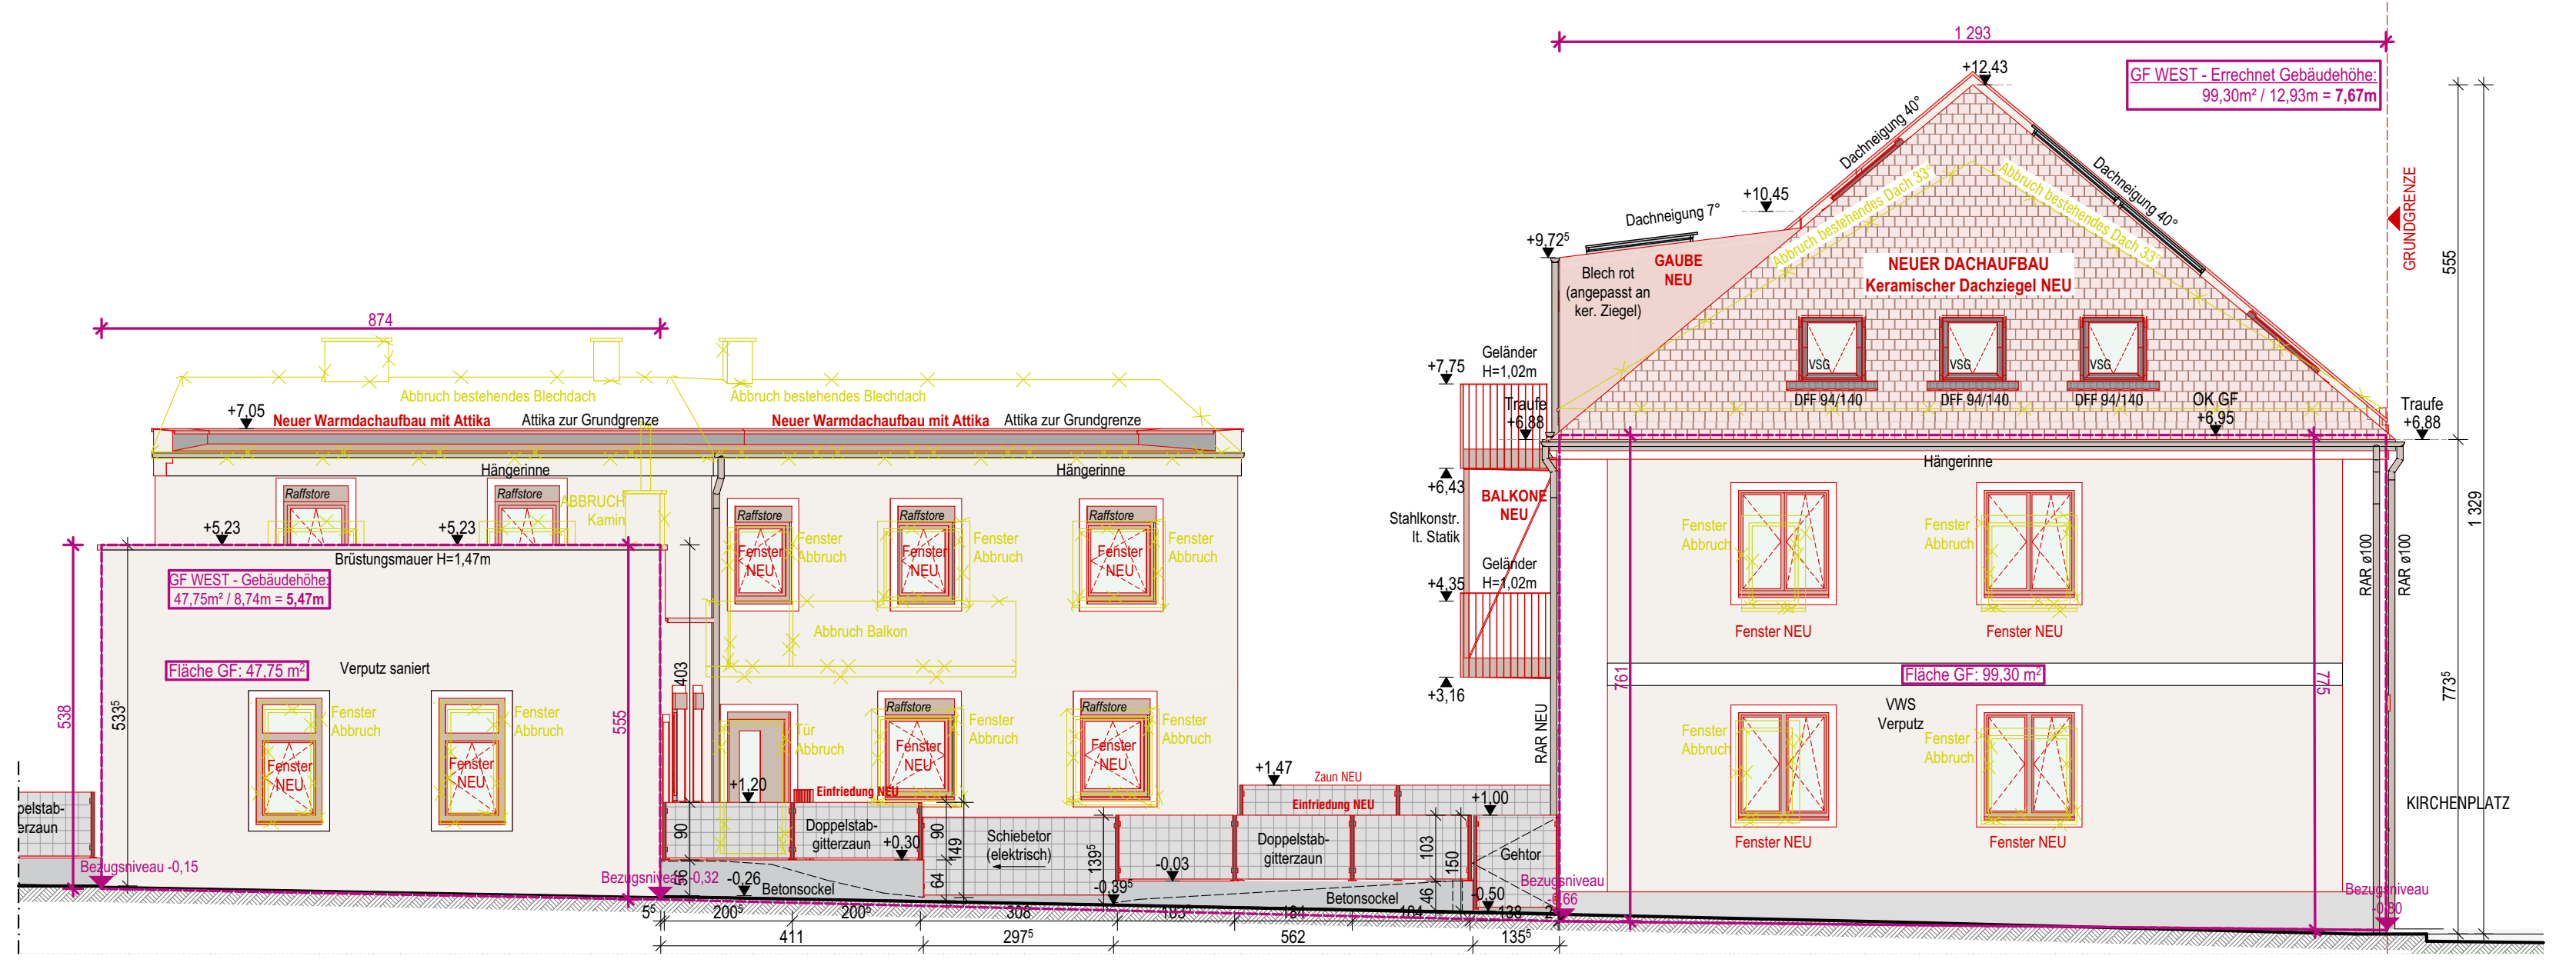

WESTANSICHT // ANSICHT STRASSENSEITIGE EINFRIEDUNG M 1:100

AW01a/b	MAUERWERK VWS 10cm	R60
1,00 cm	Silikatputz genetzt und gespachtelt, In Anschlussbereichen mit Feuchtigkeitsabdichtung / Hochzug	
10,00 cm	EPS Wärmedämmung (XPS im Sockelbereich)	
0,80 cm	Klebespachtel	
70 / 55 cm	Mischmauerwerk a=70, b=55 cm	
1,50 cm	Innenputz	
83,3 / 68,30 cm	**BAUTEIL GESAMT**	

AW01c	MAUERWERK VWS 20cm	R60
1,00 cm	Silikatputz genetzt und gespachtelt, In Anschlussbereichen mit Feuchtigkeitsabdichtung / Hochzug	
20,00 cm	EPS Wärmedämmung	
0,80 cm	Klebespachtel	
60,00 cm	Mischmauerwerk	
1,50 cm	Innenputz	
83,30 cm	**BAUTEIL GESAMT**	

AW02 a/b	MAUERWERK VWS 6cm	R60
1,00 cm	Silikatputz genetzt und gespachtelt, In Anschlussbereichen mit Feuchtigkeitsabdichtung / Hochzug	
6,00 cm	EPS Wärmedämmung (XPS im Sockelbereich)	
0,80 cm	Klebespachtel	
60 / 45 cm	Mischmauerwerk a=60, b=45	
1,50 cm	Innenputz	
69,3 / 54,3cm	**BAUTEIL GESAMT**	

AW03 a/b/c	ZIEGELMAUERWERK FEUERMAUER	R90 + A2
1,50 cm	Außenputz	
60 / 50 / 40 cm	Ziegelmauerwerk a=60, b=50, c=40 cm	
1,50 cm	Innenputz	
63 / 53 / 43 cm	**BAUTEIL GESAMT**	

AW 03 d	MWK DG NEU FEUERMAUER + VS	R90 + A2
1,00 cm	Silikatputz genetzt und gespachtelt	
16,00 cm	Mineralwolle	
0,80 cm	Klebespachtel	
25,00 cm	Porotherm - Ziegelmauerwerk 25,00 cm	
1,50 cm	Innenputz	
44,30 cm	**BAUTEIL GESAMT**	

AW 04 a/b/c	MAUERWERK VWS 12cm HOFTRAKT	R60
1,00 cm	Silikatputz genetzt und gespachtelt, In Anschlussbereichen mit Feuchtigkeitsabdichtung / Hochzug	
12,00 cm	EPS Wärmedämmung (XPS im Sockelbereich)	
0,80 cm	Klebespachtel	
60 / 30 / 25 cm	Ziegelmauerwerk a=60, b=30, c=25 cm	
1,50 cm	Innenputz	
75,3 - 40,3cm	**BAUTEIL GESAMT**	

AW 05 a/b	MAUERWERK OHNE VWS HOFTRAKT	R60
1,50 cm	Außenputz	
50 / 65 cm	Ziegelmauerwerk a=50, b=65 cm	
1,50 cm	Innenputz	
53 / 68 cm	**BAUTEIL GESAMT**	

AW 06 a/b/c	MWK HOFTRAKT FEUERMAUER + VS	R90 + A2
1,50 cm	Außenputz	
45/30/25 cm	Ziegelmauerwerk a=45, b=30, c=25 cm	
1,75 cm	Innenputz	
1,00 cm	Luftschicht (Abstand)	
7,50 cm	C-Profil dazw. Mineralwolle lt. Bauphysik	
	Dampfbremse, sd Wert lt. Bauphysik, allseits angebunden	
1,25 cm	1 x 1,25 cm GKB-Platte (GKBi in Nassräumen)	
58 / 43 / 38cm	**BAUTEIL GESAMT**	

AW 07	HOLZ-LEICHTBAU BLECH (GAUBE)	EI60
0,80 cm	Blech Aluminium, gefalzt auf Strukturgewebe	
2,40 cm	Vollholzschalung	
5,00 cm	Konterlattung / Hinterlüftung mit Nageldichtband	
0,10 cm	Diffusionsoffene UV-beständige Winddichtbahn lt. Bauphysik allseitig und alle Durchdringungen eingebunden	
6,00 cm	Holzfaserdämmplatte	
18,00 cm	Konstruktionsholz lt. Statik, fungizid behandelt dazw. Dämmung lt. Bauphysik	
2,20 cm	OSB Platte, allseits luftdicht verklebt	
1,50 cm	GKF-Platte (EI30)	
5,00 cm	UK / Lattung dazw. Mineralwolle - Installationsebene	
1,25 cm	GKB-Platte (GKBi in Nassräumen)	
42,25 cm	**BAUTEIL GESAMT**	

IW 01 a/b/c/d/e	WOHNUNGSTRENNWAND MISCH-MWK	REI 60
2,50 cm	Innenputz	
65 - 35 cm	Mischmauerwerk a=65, b=60, c=50, d=40, e=35 cm (REI60)	
2,50 cm	Innenputz	
0,25 cm	Luftraum (Abstand)	
5,00 cm	C-Profil dazw. Mineralwolle	
1,25 cm	GKB-Platte	
76,50 - 46,50cm	**BAUTEIL GESAMT**	DnT,w ≥ 55 dB

IW 01 f/g	WOHNUNGSTRENNWAND ZIEGEL-MWK	REI 60
2,50 cm	Innenputz	
30 / 20 cm	Ziegelmauerwerk f=30, g=20 cm (mind.REI60)	
2,50 cm	Innenputz	
0,25 cm	Luftraum (Abstand)	
5,00 cm	C-Profil dazw. Mineralwolle	
1,25 cm	GKB-Platte	
41,5 / 31,5 cm	**BAUTEIL GESAMT**	DnT,w ≥ 55 dB

IW 02 a/b/c/d	INNENWAND MISCHMAUERWERK	R60
2,50 cm	Innenputz	
65 - 50 cm	Mischmauerwerk a=65 b=60, c=55, d=50 cm	
2,50 cm	Innenputz	
70 - 55 cm	**BAUTEIL GESAMT**	

IW 02 e/f/g/h	INNENWAND HLZ-MWK	R60
2,50 cm	Innenputz	
30 - 10 cm	Hochlochziegelmauerk e=30, f=20 cm, g=15cm, h=10cm	
2,50 cm	Innenputz	
35 - 15 cm	**BAUTEIL GESAMT**	

IW 03 a/b	INNENWAND TROCKENBAU DOPPELT BEPLANKT	
2,50 cm	2 x 1,25 cm GKB-Platte (GKBi in Nassräumen)	
7,5 / 12,5 cm	C-Profil / UK dazw. Mineralwolle a=7,50, b=12,5	
2,50 cm	2 x 1,25 cm GKB-Platte (GKBi in Nassräumen)	
12,50 cm	**BAUTEIL GESAMT**	

IW 04	WOHNUNGSTRENNWAND TROCKENBAU	EI 90
2,50 cm	2 x 1,25 cm GKF-Platte	
7,50 cm	C-Profil dazw. Mineralwolle	
1,25 cm	1 x 1,25 cm GKF- Platte	
	PE- Folie allseits luftdicht verklebt	
0,25cm	Luftraum (Abstand)	
7,50 cm	C-Profil dazw. Mineralwolle	
2,50 cm	2 x 1,25 cm GKB-Platte (GKBi in Nassräumen)	
21,50 cm	**BAUTEIL GESAMT**	DnT,w ≥ 55 dB

VS 01	VORSATZSCHALE TROCKENBAU	
1,00 cm	Luftraum (Abstand)	
5,00 cm	C-Profil dazw. Mineralwolle	
1,25 cm	1 x 1,25 cm GKB-Platte (GKBi in Nassräumen)	
7,25 cm	**BAUTEIL GESAMT**	

VS 02	VORSATZSCHALE TROCKENBAU NASSRAUM	
1,00 cm	Luftraum (Abstand)	
7,50 cm	C-Profil dazw. Mineralwolle	
2,50 cm	2 x 1,25 cm GKB-Platte (GKBi in Nassräumen)	
11,00 cm	**BAUTEIL GESAMT**	

VS 03	VORSATZSCHALE TROCKENBAU WC	
4,00 cm	Luftraum (Abstand)	
15,00 cm	C-Profil dazw. Mineralwolle	
2,50 cm	2 x 1,25 cm GKB-Platte (GKBi in Nassräumen)	
21,50 cm	**BAUTEIL GESAMT**	

FB 01 a/b	FUSSBODEN GEGEN ERDREICH	REI 60
1,50 cm	Bodenbelag (Parkett / Fliese)	
7,00 cm	Zementestrich mit FBH, inkl. Randdämmstreifen 1cm PE-Folie seitlich hochgezogen bis Estrich OK	
3,00 cm	Trittschalldämmplatten lt. Bauphysik	
	Dampfbremse	
7,5 / 17,5 cm	EPS - Schüttung zementgebunden	
1,00 cm	Bituminöse Bauwerksabdichtung	
20,00 cm	Stahlbetonplatte	
	PE-Folie	
10,00 cm	XPS - Perimeterdämmung	
10,00 cm	Unterbau / Rollierung	
60 / 70 cm	**BAUTEIL GESAMT**	

FB 02 a	DIPPELBAUMDECKE ÜBER EG	REI 60
1,50 cm	Bodenbelag (Parkett / Fliese)	
7,00 cm	Zementestrich mit FBH, inkl. Randdämmstreifen 1cm PE-Folie seitlich hochgezogen bis Estrich OK	
3,00 cm	Trittschalldämmplatten lt. Bauphysik	
9,50 cm	Schüttung zementgebunden	
	PE-Folie	
20,00 cm	Bestehende Dippelbaumdecke	
3,00 cm	Holzlattung	
2,50 cm	2 x 1,25 cm GKF-Platte (EI60)	
7,50 cm	Metall-UK dazw. MW (Installationsebene)	
1,25 cm	1 x 1,25 cm GKB-Platte (GKBi in Nassräumen)	
55,25 cm	**BAUTEIL GESAMT**	

FB 02 b	TRAMDECKE ÜBER EG	REI 60
1,50 cm	Bodenbelag (Parkett / Fliese)	
7,00 cm	Zementestrich mit FBH, inkl. Randdämmstreifen 1cm PE-Folie seitlich hochgezogen bis Estrich OK	
3,00 cm	Trittschalldämmplatten lt. Bauphysik	
8,00 cm	Schüttung zementgebunden	
	PE-Folie	
2,40 cm	Vollholzschalung	
18,00 cm	Besteh. Holztramdecke (dazw. 10cm MW)	
3,00 cm	Holzlattung	
2,50 cm	2 x 1,25 cm GKF-Platte (EI60)	
7,50 cm	Metall-UK dazw. MW (Installationsebene)	
1,25 cm	1 x 1,25 cm GKB-Platte (GKBi in Nassräumen)	
54,15 cm	**BAUTEIL GESAMT**	

FB 02 c	DECKE / GEWÖLBE ÜBER EG	REI 60
1,50 cm	Bodenbelag (Parkett / Fliese)	
7,00 cm	Zementestrich mit FBH, inkl. Randdämmstreifen 1cm PE-Folie seitlich hochgezogen bis Estrich OK	
3,00 cm	Trittschalldämmplatten lt. Bauphysik	
9,50 cm	Schüttung zementgebunden	
	PE-Folie	
27,5 - 78,0 cm	Bestehendes Ziegelgewölbe (mind. REI60)	
1,50 cm	Innenputz	
50 - 100,5 cm	**BAUTEIL GESAMT**	

FB 02 d	DECKE ÜBER EG STB NEU	
1,50 cm	Bodenbelag (Parkett / Fliese)	
7,00 cm	Zementestrich mit FBH, inkl. Randdämmstreifen 1cm PE-Folie seitlich hochgezogen bis Estrich OK	
3,00 cm	Trittschalldämmplatten lt. Bauphysik	
9,50 cm	Schüttung zementgebunden	
20,00 cm	Stahlbetondecke (mind. REI60)	
0,50 cm	Spachtelung	
41,50 cm	**BAUTEIL GESAMT**	

FB 03	STB-DECKE ÜBER 1.OG	REI 60
1,50 cm	Bodenbelag (Parkett / Fliese)	
7,00 cm	Zementestrich mit FBH, inkl. Randdämmstreifen 1cm PE-Folie seitlich hochgezogen bis Estrich OK	
3,00 cm	Trittschalldämmplatten lt. Bauphysik	
6,50 cm	EPS - Schüttung zementgebunden	
18,00 cm	Stalbetondecke (mind. REI60)	
0,50 cm	Spachtelung	
36,50 cm	**BAUTEIL GESAMT**	

FB 04	BALKON STAHLKONSTR. THERMISCH ENTKOPPELT	
2,50 cm	Holzbelag, rutsch- und witterungsfest	
9,00 cm	Stellfüße Höhenausgleich 60-90 mm	
0,80 cm	Gummigranulatplatte mit Trittschallfunktion	
0,50 cm	Bituminöse Abdichtung 2-lagig, erste Lage selbstklebend	
0,50 cm	Stahlblech lt. Statik, im Gefälle 2%	
18,00 cm	Konstruktion aus Stahlträgern lt. Statik, Untersicht verkleidet mit MAX Exterior	
31,30 cm	**BAUTEIL GESAMT**	

FB 05 a	ZIEGELDECKE ÜBER EG (HOFTRAKT)	REI 60
1,50 cm	Bodenbelag (Parkett / Fliese)	
7,00 cm	Zementestrich mit FBH, inkl. Randdämmstreifen 1cm PE-Folie seitlich hochgezogen bis Estrich OK	
3,00 cm	Trittschalldämmplatten lt. Bauphysik	
3,50 cm	EPS - Schüttung zementgebunden	
23,00 cm	Bestehende Ziegeleinhängdecke (REI60)	
2,00 cm	Bestehender Innenputz	
2,50 cm	Luftraum (Abstand)	
5,00 cm	UK lt. Erfordernis dazw. Mineralwolle	
1,25 cm	1 x 1,25 cm GKB-Platte (GKBi in Nassräumen)	
48,75 cm	**BAUTEIL GESAMT**	

FB 05 b	KAPPENDECKE ÜBER EG (HOFTRAKT)	REI 60
1,50 cm	Bodenbelag (Parkett / Fliese)	
7,00 cm	Zementestrich mit FBH, inkl. Randdämmstreifen 1cm PE-Folie seitlich hochgezogen bis Estrich OK	
3,00 cm	Trittschalldämmplatten lt. Bauphysik	
	Dampfbremse	
3,50 cm	EPS - Schüttung zementgebunden	
28,00 cm	Kappendecke BESTAND mit Aufbeton / Schüttung Stahlträger brandschutztechn. verkleidet (Promat) (REI60)	
4,50 cm	UK lt. Erfordernis dazw. Mineralwolle	
1,25 cm	1 x 1,25 cm GKB-Platte (GKBi in Nassräumen)	
48,75 cm	**BAUTEIL GESAMT**	

DA 01	HAUPTDACH ZIEGELDECKUNG	REI 30
3,00 cm	Keramischer Dachziegel	
3,00 cm	Lattung 30/50 mm	
5,00 cm	Konterlattung 50/50 mit Nageldichtband - Hinterlüftung	
0,20 cm	Diffussionsoffene Dachauflegebahn - erhöhte Regensicherheit, sd- Wert lt. Bauphysik	
2,40 cm	Vollholzschalung	
24,00 cm	Holzsparren lt. Statik dazw. Mineralwolle lt. Bauphysik	
3,00 cm	UK / Lattung dazw. Mineralwolle lt. Bauphysik	
0,10 cm	Dampfbremse allseits verklebt lt. Bauphysik	
1,50 cm	GKF-Platte (EI30)	
42,20 cm	**BAUTEIL GESAMT**	

DA 02	DACH GAUBE BLECHDECKUNG	REI 30
0,80 cm	Blech Aluminium, gefalzt auf Strukturgewebe	
2,40 cm	Vollholzschalung	
8,00 cm	Konterlattung 50/80 mit Nageldichtband - Hinterlüftung	
0,20 cm	Diffussionsoffene Dachauflegebahn - erhöhte Regensicherheit, sd- Wert lt. Bauphysik	
2,40 cm	Vollholzschalung	
24,00 cm	Holzsparren lt. Statik dazw. Mineralwolle lt. Bauphysik	
3,00 cm	UK / Lattung dazw. Mineralwolle lt. Bauphysik	
0,10 cm	Dampfbremse allseits verklebt lt. Bauphysik	
1,50 cm	GKF-Platte (EI30)	
5,00 cm	UK / Lattung dazw. Mineralwolle - Installationsebene	
1,25 cm	GKB-Platte	
48,65 cm	**BAUTEIL GESAMT**	

DA 03	WARMDACH 1.OG HOFTRAKT	R 30
6,00 cm	Kies	
1,00 cm	2 lagige bit. Abdichtung, erste Lage selbstklebend	
17,00 cm	Gefälledämmung 12 - 22cm (17cm im Mittel)	
20,00 cm	Grunddämmung EPS	
0,50 cm	Dampfsperre	
23,00 cm	Bestehende Ziegeleinhängdecke	
2,00 cm	Bestehender Innenputz	
2,50 cm	Luftraum (Abstand)	
5,00 cm	UK lt. Erfordernis dazw. Mineralwolle	
1,25 cm	GKB-Platte	
78,25 cm	**BAUTEIL GESAMT**	

DA 04 a	FLACHDACH / KIES (HOFTRAKT)	R 30
5,00 cm	Bekiesung, im Traufenbereich verfestigt	
0,10 cm	diffusionsoffene, wasserableitende Trennlage	
0,80 cm	Granulatmatte als Schutzschicht	
1,00 cm	2 lagige bit. Abdichtung, erste Lage selbstklebend	
6,50 cm	Gefälledämmung im Mittel 6,5cm (2-11cm)	
10,00 cm	Grunddämmung EPS F Plus lt. Bauphysik	
0,50 cm	Dampfsperre bituminös, alukaschiert, sd Wert lt. Bauphysik, Überlappend und verklebt	
28,00 cm	Kappendecke BESTAND mit Aufbeton / Schüttung Stahlträger brandschutztechn. verkleidet (Promat) (REI30)	
2,50 cm	Luftraum (Abstand)	
5,00 cm	UK lt. Erfordernis dazw. Mineralwolle	
1,25 cm	GKB-Platte	
60,65 cm	**BAUTEIL GESAMT**	

DA 04 b	FLACHDACH / DACHTERRASSE (HOFTRAKT)	R 30
2,00 cm	Holzbelag, rutsch- und witterungsfest	
11,50 cm	Alukonstruktion auf Stelzlager (7-16cm) höhenausgleich	
0,80 cm	Granulatmatte als Schutzschicht	
1,00 cm	2 lagige bit. Abdichtung, erste Lage selbstklebend	
6,50 cm	Gefälledämmung im Mittel 6,5cm (2-11cm)	
10,00 cm	Grunddämmung EPS F Plus lt. Bauphysik	
0,50 cm	Dampfsperre bituminös, alukaschiert, sd Wert lt. Bauphysik, Überlappend und verklebt	
28,00 cm	Kappendecke BESTAND mit Aufbeton / Sauberkeitsschicht Stahlträger brandschutztechn. verkleidet (Promat) (REI30)	
2,50 cm	Luftraum (Abstand)	
5,00 cm	UK lt. Erfordernis dazw. Mineralwolle	
1,25 cm	GKB-Platte	
69,05 cm	**BAUTEIL GESAMT**	

PFAR02
Pfarrgasse 2-4, 2512 Tribuswinkel

FLÄCHENAUFSTELLUNG

Nutzflächen	VR1	Gang	AR	Ankleide	WC1	Bad	Bad/WC	Woh./Ess.	Kü	Speis	Zimmer 1	Zimmer 2	Zimmer 3	NF GESAMT	Garten	Balkon/Terr.	Außenflächen Gesamt
EG - Straßentrakt																	
TOP 1	4,83 m²		2,51 m²				7,39 m²	22,91 m²	10,61 m²		13,02 m²			61,27 m²			0,00 m²
TOP 2	5,63 m²	9,76 m²	2,66 m²				7,85 m²	21,10 m²	8,33 m²		12,72 m²	16,90 m²	11,65 m²	96,60 m²	26,18 m²	6,30 m²	32,48 m²
1. OG - Straßentrakt																	
TOP 3	4,07 m²		2,50 m²				4,58 m²	29,26 m²			12,67 m²			53,08 m²		9,29 m²	9,29 m²
TOP 4	5,67 m²		2,91 m²	4,88 m²	1,90 m²	5,09 m²		26,28 m²	7,33 m²		14,17 m²			68,23 m²			0,00 m²
TOP 5	3,50 m²	4,45 m²	2,66 m²				5,56 m²	17,29 m²			15,41 m²			48,87 m²		6,29 m²	6,29 m²
1. DG Straßentrakt																	
TOP 6	7,09 m²		7,06 m²				4,57 m²	32,40 m²			16,01 m²	15,23 m²		82,36 m²		9,30 m²	9,30 m²
TOP 7	3,02 m²		1,32 m²				9,83 m²	35,58 m²			19,65 m²	16,59 m²		85,99 m²		6,30 m²	6,30 m²
Hoftrakt (Townhouse)																	
TOP 8	11,60 m²		2,44 m²	6,04 m²	1,60 m²	6,99 m²		13,74 m²	28,42 m²	2,15 m²	20,70 m²	12,96 m²	13,61 m²	120,25 m²		47,12 m²	47,12 m²
SUMME GESAMTE NUTZFLÄCHE														616,65 m²			110,78 m²

Allgemeinflächen	Gang	KIWA	Fahrradraum	Technik	Gesamt
EG Straßentrakt	11,88 m²				11,88 m²
1. OG Straßentrakt	7,93 m²				7,93 m²
DG Straßentrakt	6,87 m²				6,87 m²
EG Hoftrakt		8,58 m²	38,22 m²	10,44 m²	57,24 m²
SUMME ALLGEMEIN FLÄCHEN					83,92 m²
SUMME NUTZFLÄCHE + ALLGEMEINFLÄCHEN					700,57 m²

SUMME NUTZFLÄCHE + ALLGEMEINFLÄCHEN, Außenflächen Gesamt: 110,78 m²

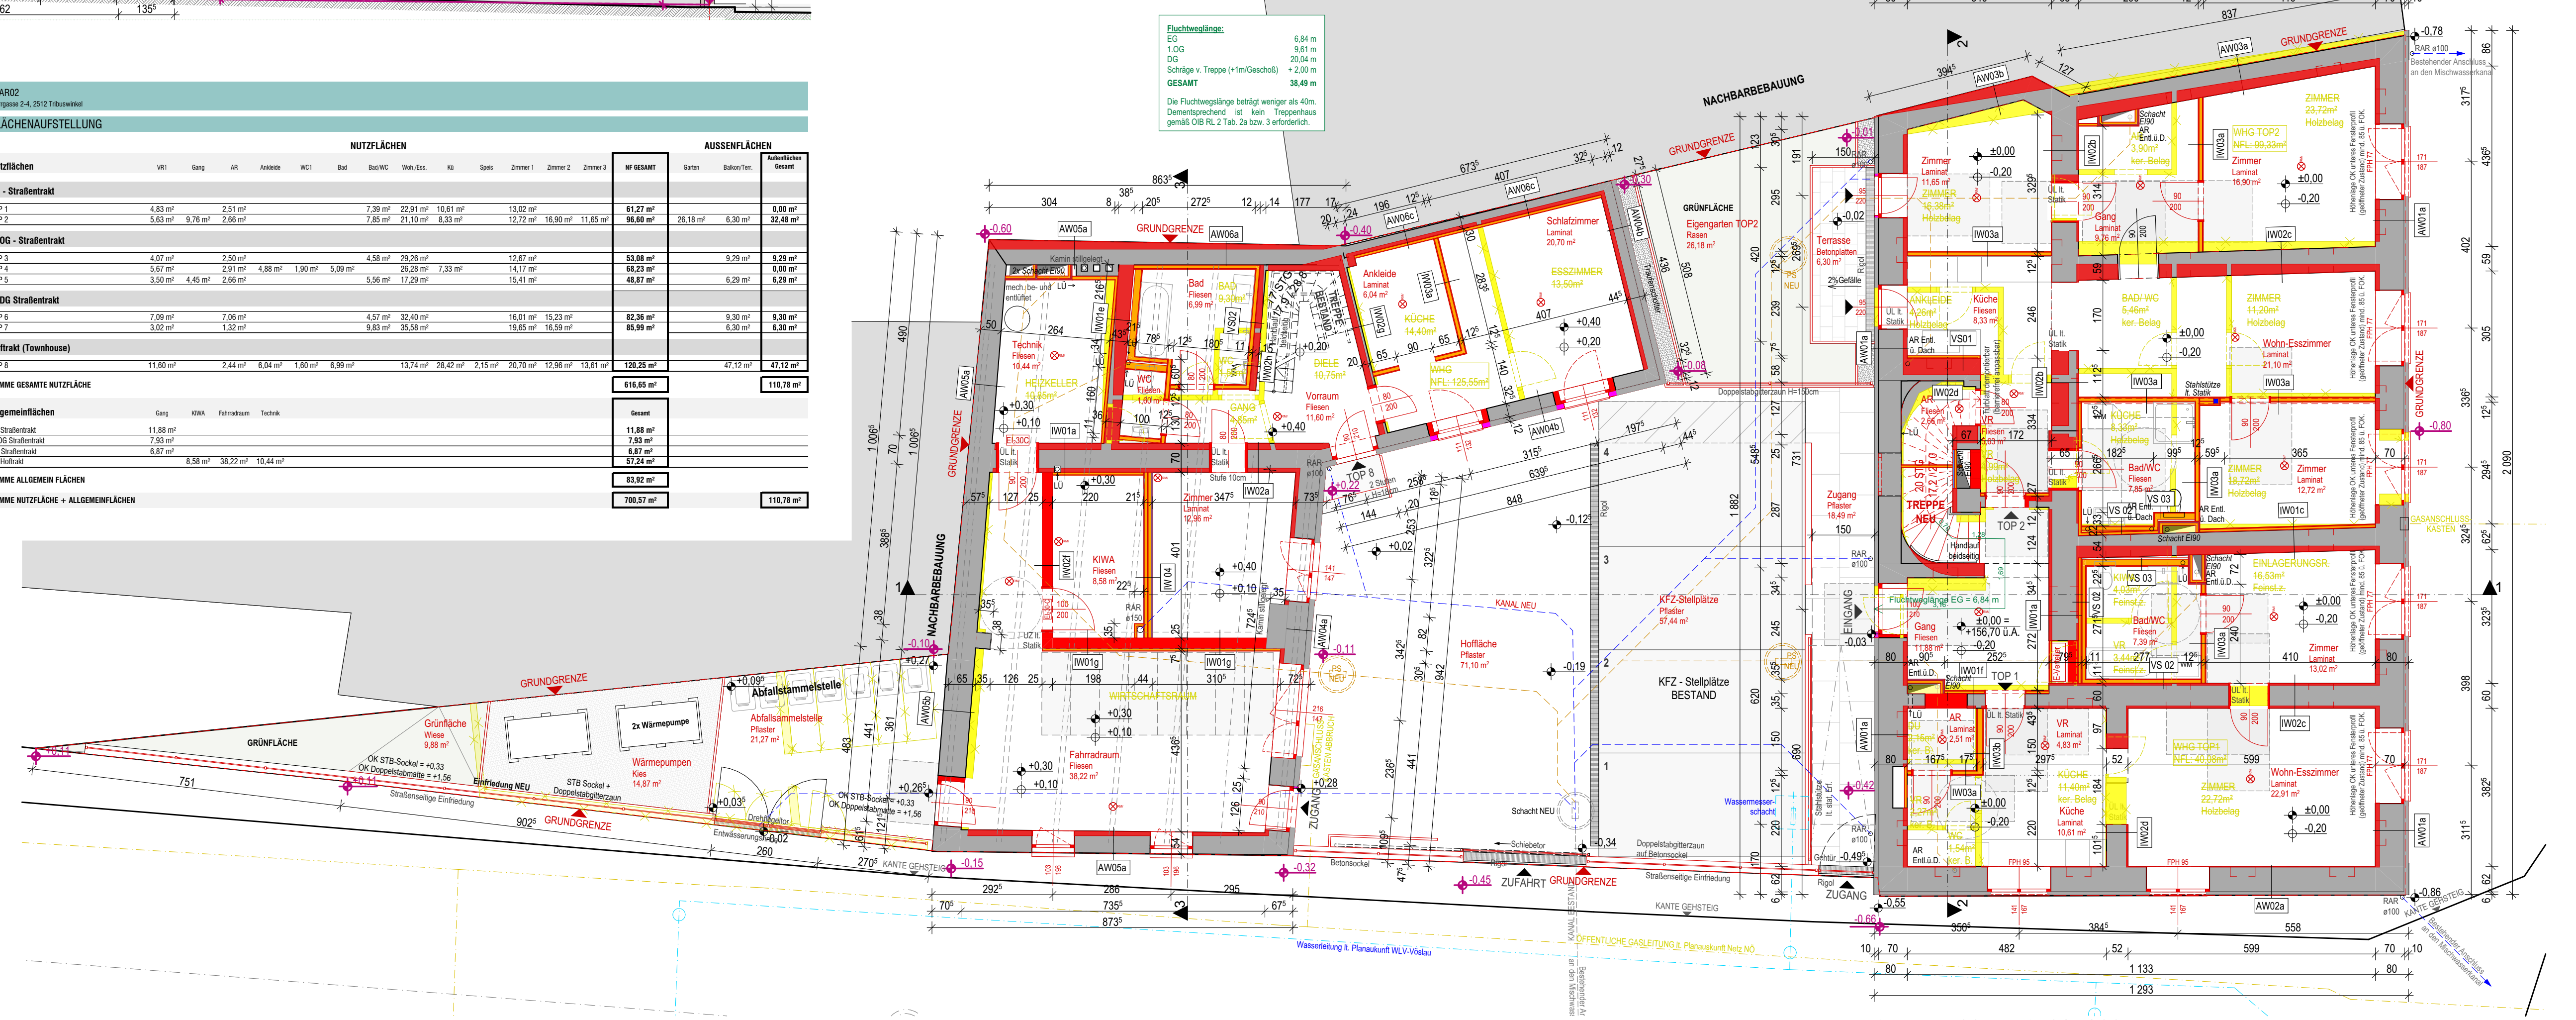

GRUNDRISS ERDGESCHOSS M 1:100

Durch die Sanierung werden 8 Wohneinheiten geschaffen.
Das entspricht einer Erweiterung um 2 Wohneinheiten, da sich bisher 6 Wohneinheiten auf der Liegenschaft befunden haben.

Höhenbezugspunkte:
±0.00 = + 213,70 über Adria

Heizung:	2 Wärmepumpen
Bauweise:	Massives Bauweise; Bestehende Holzdecken, Neue STB-Decken, Neuerrichtung des Dachstuhls inkl. Dachausbau und Gaube aus Hoz; Innenwände Leichtbau; Neuerrichtung Bodenplatte; Neuer Innenausbau
Abfallsammelstelle:	im nördlichen Bereich des Grundstücks

KFZ - Stellplätze:
→ Gemäß §63 Abs. 1b wird auf die Schaffung zusätzlicher KFZ - Stellplätze verzichtet.

FAHRRADABSTELLPLÄTZE:
1 Fahrradabstellplatz / Wohneinheit 8 Stellplätze
→ Auf dem Grundstück sollen gemäß NÖ BTV §14 8 Fahrradabstellplätze errichtet werden.
→ Der Abstellraum für Fahrräder befindet sich im Erdgeschoß des Hofgebäudes.

BRANDSCHUTZ

STRASSENTRAKT, GEBÄUDEKLASSE: GK3 lt. OIB RL2 2023
0 unterirdisches Geschoss
3 oberirdirsche Geschosse
Fluchtniveau < 7m

HOFTRAKT, GEBÄUDEKLASSE: GK2 lt OIB RL2 2023
0 unterirdisches Geschoss
2 oberirdirsche Geschosse

→ Gemäß NÖ BTV 2014 Anlage 2 (OIB2) Pkt. 3.1.1 ist keine Unterteilung in mehrere Brandabschnitte erforderlich.
→ Die allgemeinen Anforderungen an das Brandverhalten gemäß Tabelle 1a werden eingehalten.
→ Die allgemeinen Anforderungen an den Feuerwiderstand von Bauteilen gemäß Tabelle 1b werden eingehalten.
→ Brandschutztechnische Ausführung neuer Schächte und Führung der Leitungen lt. TRVB 110 B 2019
→ Bodenbeläge lt. Ö-NORM B 3806, Aussenwände lt. Ö-NORM B 3806,
→ Außenbauteile wie Geländer werden feuerverzinkt und korrosionsbeständig ausgeführt.
→ Sofern Schächte, Kanäle, Leitungen und sonstige Einbauten in Wänden bzw. Decken liegen oder diese durchdringen, ist entweder durch Abschottung oder Ummantelung sicher gestellt , dass die Feuerwiderstandsklasse dieser Bauteile nicht beeinträchtigt wird. Brandschutzschotts gemäß OIB 2 Punkt 3.5.3
→ Sämtliche Kamine werden abgebrochen und stillgelegt.
→ Öffenbare Dachflächenfenster sind mind. 1m von der Grundstückgrenze entfernt.
→ Alle Aufenthaltsräume sowie alle Gänge über die eine Fluchtweg führt, sind mit Rauchwarnmeldern - batteriebetrieben ausgestattet (in den Wohnküchen nicht unmittelbar im Kochbereich).
→ Brandabschnittsbildende Wände an der Nachbargrundstücksgrenze werden in REI90 und A2 ausgeführt.

VER- / ENTSORGUNG:
→ Das Stiegenhaus wird natürlich belüftet.
→ Trinkwasser: Bestehender Anschluss an das öffentliche Versorgungsnetz.
→ Wasserzählerschacht im Hofbereich
→ Anfallende Niederschlagswässer und Abwässer werden über den bestehenden Anschluss in das öffentliche Kanalsystem eingeleitet.
→ Kanalleitungen PVC bzw. Guss in kg, mind. 2% Gefälle
→ Die Müllsammlung erfolgt bei der Abfallsammelstelle im nördlichen Grundstücksbereich. Die Zugänglichkeit vom öffenlichen Gut ist durch ein Drehtor gegeben.
→ Heizung: Wärmepumpe
→ Heizung / Warmwasser: Wärmepumpe + E-Speicher in den Bädern.
→ Wärmeabgabe durch Fußbodenheizung, elektrische Handtuchheizkörper in den Bädern.
→ Elektroversorgung: Bestehender Anschluss an das Ortsnetz.

NUTZUNGSSICHERHEIT und BARRIEREFREIHEIT

→ Es wird bestätigt, dass gemäß § 46 NÖ Bauordnung zwei Wohneinheit barrierefrei anpassbar ausgeführt werden.
→ TOP 1 und TOP2 im EG werden barrierefrei anpassbar ausgeführt.
→ Geländerhöhen mind. 1,02 m. Abstände von vertikalen Stäben max. 12cm.
→ Alle Treppen werden beidseitig mit Handläufen ausgestattet.
→ Dachflächenfenster werden in VSG ausgeführt.

HYGIENE, GESUNDHEIT und UMWELTSCHUTZ

→In sämtlichen Nassräumen wird eine Kunststoffabdichtung unter Fliesenbelägen mit 15cm Wandhochzug ausgeführt.
→ Alle Aufenthaltsräume sind durch Fenster belüftbar und verfügen über ausreichende Lichteintrittsflächen gemäß OIB RL3 9.1.1
→ Alle zur Belichtung von Aufenthaltsräumen notwendigen Lichteintrittsflächen verfügen über eine freie Sicht von mind. 2m und zumindest in einem Aufenthaltsraum über eine freie waagrechte Sicht von mind. 6m in 1,20m Höhe.
→Sanitärräume, die über kein öffenbares Fenster verfügen, werden mechanisch entlüftet.
→sonstige innen liegende Räume werden entsprechend ihrem Verwendungszweck be- und entlüftet.
→alle Glasgeländer und bodentiefen Verglasungen mit Absturzgefahr werden in VSG ausgeführt, vertikale Verglasungen mit Durchsturzgefahr in ESG

BAUPHYSIK
→Die im Einreichplan angegebenen Aufbauten und Angaben sind mit jenen im bauphysikalischen Nachweis ident; insbesondere hinsichtlich der Dicke sowie des Materials bzw. der Type der Baustoffe.
→ Balkone werden thermisch vom Bestand getrennt ausgeführt (ISO-Korb).

AUSSTATTUNG

→ In allen Wohnungen wird ein Anschluß für eine Waschmaschine (Badezimmer oder Küche) vorgesehen.
→ Sämtliche Absturzsicherungen / Geländer in Stahl werden verzinkt.
→ Gemäß NÖ Bauordnung 2014 §66a Abs. (1) besteht keine Verpflichtung zur Errichtung einer Photovoltaikanlage.

SONSTIGES

→ Der Einstellraum für Kinderwägen und Mobilitätshilfen befindet sich im Ergeschoss des Hofgebäudes.
→ Brieffachanlage befindet sich beim Hauseingangsbereich des Straßentraktes.

FASSADENGESTALTUNG

→Die Entwässerung von den Dachflächen erfolgt über Regenabfallrohre, Hänge- und Saumrinnen. Die Entwässerung der Terrassen erfolgt über Gullys oder Regenrinnen.
→Für sämtliche Terrassen und Balkonflächen werden Notüberläufe vorgesehen.
→Blitzschutz wird an der Fassade gem. Ö-NORM ausgeführt.

EINREICHUNG GEM. OIB RICHTLINIEN IN DER FASSUNG 2023

Der Bestand wurde basiernd auf Geometerangaben des Büros "Manfred Haselbauer Ingenieurbüro für Vermessungswesen" (Plandatum: 29.11.2024) sowie dem Einreichplan vom 27.03.2017 des Büros "Arch. DI Marc Wohlschak" dargestellt.
Das Niveau ±0,00 des vorliegenden Plans ist um 39cm höher als im derzeit bewilligten und im Bauakt aufliegenden Einreichplan vom 27.03.2017 - dementsprechend sind die Koten des Bezugsniveaus nicht ident.

LEGENDE

☒	Wanddurchbruch	▨	Bestand	—	Medien
☒	Deckendurchbruch	🟨	Abbruch	—	Fernwärme
◺	Bodenschlitz	🟩	unbewehrter Beton	—	Gas
◢	Bodendurchbruch	🟩	bewehrter Beton	—	Strom
▼	OK Fertigbau	🟥	Mauerwerk	—	Heizung
▲	UK Fertigbau	🟦	Stahl (allgemein)	—	Regenwasser
▽	OK Rohbau	🟫	Holz (allgemein)	—	Schmutzwasser
△	UK Rohbau	🟪	Dämmstoff (hart)	—	Wasser
± 0,00	Höhenangabe einer waagrechten Fläche	🟧	Dämmstoff (weich)	- - -	Grundgrenze
⊕ ±0,00	Höhenangabe eines Punktes in einem Bauwerk - Fertigmaß	▞	Dichtstoff (allgemein)	- - -	Baufluchtlinie
⌖ ±0,00	Höhenangabe eines Punktes in einem Bauwerk - Rohbaumaß	🟦	Glas	- - -	Baulinie
		🟦	Gipskarton GKF (Brandschutz)	—	Widmungsgrenze
		🟧	Gipskarton GKB - im Nassraum GKBi		
		▭	Grünfläche		
		▨	Erdmaterial (allgemein)		

BGF	Bruttogesamtfläche
HNF / NNF	Haupt- Nebennutzfläche
KG	Kochgelegenheit

Höhenbezugs- und Maßangaben

DOK	Deckenoberkante
DUK	Deckenunterkante
FBOK	Fußbodenoberkante
FDOK	Fundamentoberkante
FDUK	Fundamentunterkante
RDOK	Deckenoberkante
RDUK	Deckenunterkante
RH	lichte Raumhöhe
GH	Geschoßhöhe
OK	Oberkante
OS	Oberseite
UK	Unterkante
US	Unterseite
VK	Vorderkante
STUK	Sturzunterkante (Rohbaumaß)
STH	Sturzhöhe gemessen von STUK bis DUK (Rohbaumaß)
RPH	Rohbauparapethöhe
FPH	fertige Parapethöhe (FBOK bis OK Fensterbank Innen)

Rauch-, Abgas- und Luftfänge, Schächte

PT	Putztürchen
L	Lüftungsschacht
ABL	Abluft
ZUL	Zuluft
DBA	Druckbelüftungsanlage
DRE	Druckregeleinheit
BSK	Brandsschutzklappe
RAE	Rauchabzugseinrichtung lt. OIB 2
SEL	Schachtentlüftung

Öffnungen und deren Abschlüsse

WD	Wanddurchbruch
DD	Deckendurchbruch
FBD	Fußbodendurchbruch
FDD	Fundamentdurchbruch
WS	Wandschlitz
WA	Wandaussparung
DA	Deckenaussparung
FBA	Fußbodenaussparung
RBL	Rohbaulichte
AL	Architekturlichte
STL	Stocklichte
GL	Glaslichte
STAM	Stockaußenmaß
DF	Drehflügel
DKF	Drehkippflügel
KF	Kippflügel
SF	Schiebeflügel
SWF	Schwingflügel
WF	Wendeflügel
HT	Hebetüre
HST	Hebeschiebetüre
DL	Durchgangslichte
OL	Oberlichte
FIX	Fixverglasung
GGT	Ganzglastüre
VSG	Verbund-Sicherheitsglas
ESG	Einscheiben-Sicherheitsglas

EI2 30-C-, EI2 60-C-und EI2 90-C
Feuerschutztüren mit Angabe der Feuerwiderstandsklasse (gemäß ÖNORM B 3850 und ÖNORM B 3807)

GT	gasdichte Türe
DT	Drucktüre
S 200	Rauchabschluss
C	Selbstschließend
FLS	Freilaufschließer

EINREICHPLAN

PARIE A B C

Bauvorhaben
PFAR02
2512 Traiskirchen, Tribuswinkel Pfarrgasse 2-4

Katastralgemeinde 04034 Tribuswinkel
EZ: 51
GstNr.: .19

Übersicht

Flächenwidmungsplan

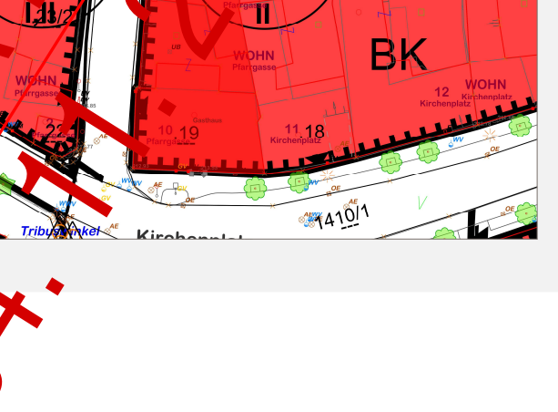

VORABZUG 04.11.2026

Behörde
Stadtgemeinde Traiskirchen
Hauptplatz 13
A - 2514 Traiskirchen

Die Plän sind derzeit unter Bearbeitung, aufgrund diverser Erkenntisse durch Bauteilöffnungen. Es handelt sich dementsprechend um einen Arbeitsstand und dient lediglich der Vorab- Information! Kein offizieller Planstand!

Grundeigentümer

Bauwerber

c/o BS Real 360 GmbH
Marokkanergasse 22, A - 1030 Wien

ARTMÜLLER ARCHITEKTEN
ZIVILTECHNIKER GMBH
Stolberggasse 34|26 A-1050 Wien
t [+43] 01 . 581 40 83 f [+43] 01. 581 40 83 99 office@artmueller.eu

Planinhalt
EINREICHPLAN

Maßstab	Gez	Datum	Plannr.	Index
1:100, 1:500	ML	26.05.2026	PFAR02_40_01	

Erstellt, am 11.11.2026