LEGENDE

☒	Wanddurchbruch
⬚	Deckendurchbruch
◺	Bodenschlitz
◢	Bodendurchbruch
▼	OK Fertigbau
▲	UK Fertigbau
▽	OK Rohbau
△	UK Rohbau
± 0,00	Höhenangabe einer waagrechten Fläche
±0,00	Höhenangabe eines Punktes in einem Bauwerk - Fertigmaß
±0,00	Höhenangabe eines Punktes in einem Bauwerk - Rohbaumaß
BGF	Bruttogesamtfläche
HNF / NNF	Haupt- Nebennutzfläche

▨	Mauerwerk (wärmedämmend)
▨	Mauerwerk (nicht wärmedämmend)
▨	unbewehrter Beton
▨	bewehrter Beton
▦	Betonfertigteil
▤	Stein
▨	Stahl (allgemein)
▨	Holz (allgemein)
▨	Holzwerkstoffe
▩	Dämmstoff (hart)
▩	Dämmstoff (weich)
▩	Kunststoff (allgemein)
▚	Dichtstoff (allgemein)
▥	Gips (Gipskartonplatte)
▥	Gipskartonplatte Brandschutz
☐	Erdmaterial (allgemein)
⬜	Bestand
🟨	Abbruch
🟥	Neubau

—	Medien
—	Fernwärme
—	Gas
—	Strom
—	Heizung
—	Regenwasser
—	Schmutzwasser
—	Wasser
—	Blech
- - -	Abdichtung
- - -	Folie
- - -	Dampfsperre, -bremse

Höhenbezugs- und Maßangaben

DOK	Deckenoberkante
DOS	Deckenoberseite
DUK	Deckenunterkante
DUS	Deckenunterseite
DUF	Deckenunterkante (fertige Untersicht)
FBOK	Fußbodenoberkante
OFF	Oberfläche des fertigen Fußbodens
FDOK	Fundamentoberkante
FDOS	Fundamentoberseite
FDUK	Fundamentunterkante
FDUS	Fundamentunterseite
RH	lichte Raumhöhe
GH	Geschoßhöhe
OK	Oberkante
OS	Oberseite
UK	Unterkante
US	Unterseite
STUK	Sturzunterkante (Rohbaumaß)
STH	Sturzhöhe gemessen von STUK bis DUK (Rohbaumaß)
RPH	Rohbauparapethöhe
FPH	fertige Parapethöhe (FBOK bis OK Fensterbank Innen)

Rauch-, Abgas- und Luftfänge, Schächte

L	Lüftungsschacht
PT	Putztürchen
PS	Putzstück
KT	Kehrtürchen
ABL	Abluft
ZUL	Zuluft
DBA	Druckbelüftungsanlage
DES	Druckentlastungsschacht
BÖ	Belüftungsöffnung
ÜÖ	Überströmöffnung
AÖ	Abströmöffnung mit Überdruckentlastungsorgan
BSK	Brandsschutzklappe
FBHV	Fussbodenheizungsverteiler
E-Verteiler	Elektroverteiler

Öffnungen und deren Abschlüsse

WD	Wanddurchbruch
DD	Deckendurchbruch
FBD	Fußbodendurchbruch
FDD	Fundamentdurchbruch
WS	Wandschlitz
WA	Wandaussparung
DA	Deckenaussparung
FBA	Fußbodenaussparung
RBL	Rohbaulichte
AL	Architekturlichte
STL	Stocklichte
GL	Glaslichte
STAM	Stockaußenmaß
DL	Durchgangslichte
GGT	Ganzglastüre
MGT	Metallgittertür
HT	Hebetüre
HST	Hebeschiebetüre
T	Türe
AT	Allgemeintüre
ET	Eingangstüre
WET	Wohnungseingangstür
IT	Innentür
DF	Drehflügel
DKF	Drehkippflügel
SF	Schiebe-Fenster
SWF	Schwingflügel
WF	Wendeflügel
K	Kippfenster
OL	Oberlichte
DF	Dachflächenfenster
PFR	Pfostenriegelkonstruktion
FE	Fenster
FT	Fenstertüre
R	Rechtsöffnend
L	Linksöffnend
FIX	Fixverglasung
VSG	Verbund-Sicherheitsglas
ESG	Einscheiben-Sicherheitsglas

Drehflügel
Drehkippflügel
Kippflügel
Fenstertüre

EI2 30-C-, EI2 60-C-und EI2 90-C
Feuerschutztüren mit Angabe der Feuerwiderstandsklasse
(gemäß ÖNORM B 3850 und ÖNORM B 3807)

GT	gasdichte Türe
DT	Drucktüre
S 200	Rauchabschluss
S 200	Rauchabschluss
C	Selbstschließend
FLS	Freilaufschließer
LVfTÖ	Lehrverrohrung für Türöffner
elTÖ	elektrischer Türöffner

AUSFÜHRUNG POLIERPLAN GESAMT

Bauvorhaben
PFAR02
2512 Traiskirchen, Tribuswinkel Pfarrgasse 2-4

XXX

Katastralgemeinde 04034 Tribuswinkel
EZ: 51
GstNr.: .19

Diese Zeichnung bzw. Ausarbeitung sowie deren Daten auf Datenträgern sind geistiges Eigentum des Erstellers Arch. Artmüller Georg. Jede Benützung, Veröffentlichung,Vervielfältigung jeglicher Art oder Weitergabe an Dritte bedarf der schriftlichen Zustimmung durch Architekt Artmüller.

Durch die Übernahme dieses Planes akzeptiert die ausführende Firma bzw. Person die darauf dargestellten Anordnungen. Geschriebene Planmaße auf dieser Zeichnunghaben Vorrang gegenüber gezeichneten Dimensionen. Der Auftragnehmer verpflichtet sich **vor** Arbeitsbeginn alle Maße und Bedingungen im Zusammenhang mit seinerArbeit auf der Baustelle verantwortlich zu überprüfen.

Abweichungen gegenüber dargestellten oder schriftlich vereinbarten Anordnungen müssen Architekt Artmüller und der Bauleitung unverzüglich schriftlich mitgeteiltwerden. Vor Arbeitsbeginn sind dem Architekten gültige Werkzeichnungen zur Genehmigung vorzulegen.

NATURMASSE SIND ZU NEHMEN, KOTEN ZU PRÜFEN

VORABZUG
28. 09. 2026

Index	Datum	Bearbeiter	Änderung

Die Plän sind derzeit unter Bearbeitung, aufgrund diverser Erkenntisse durch Bauteilöffnungen. Es handelt sich dementsprechend um einen Arbeitsstand und dient lediglich der Vorab- Information! Kein offizieller Planstand!

Index	Änderung	Datum

Grundeigentümer

Bauwerber / Auftraggeber

ARTMÜLLER ARCHITEKTEN
ZIVILTECHNIKER GMBH
Stolberggasse 34|26 A-1050 Wien
t [+43] 01 . 581 40 83 f [+43] 01. 581 40 83 99 office@artmueller.eu

Planinhalt
ERDGESCHOSS

Maßstab	Gez	Datum	Plannr.	Index
1:50			PFAR02_50_01	

Erstellt, am 11.11.2026

Speis Laminat 2,15 m²
Wohnküche Laminat 28,42 m²
AR Laminat 2,44 m²
Wohnzimmer Laminat 13,74 m²
Zimmer Laminat 13,61 m²
Dachterrasse Holz 47,12 m²
Flachdach ext. begrünung Kies 27,20 m²
Balkon Holz 6,29 m²
Balkon Holz 9,29 m²
Wohnküche Laminat 17,29 m²
Vorraum Fliesen 3,50 m²
Schlafzimmer Laminat 15,41 m²
Bad/WC Fliesen 5,56 m²
Gang Laminat 4,45 m²
Küche Laminat 7,33 m²
Wohn- & Esszimmer Laminat 26,28 m²
Vorraum Fliesen 5,67 m²
Gang Fliesen 7,93 m²
Bad Fliesen 5,09 m²
Schlafzimmer Laminat 14,12 m²
Ankleide Laminat 4,88 m²
Wohnküche Laminat 29,26 m²
Schlafzimmer Laminat 12,67 m²
TOP3
TOP4
TOP5
Bauphysikalische Abklärung ob Innendämmung (Flankendämmung) notwendig.
Bauphysikalische Abklärung erforderlich ob Innendämmung notwendig.
OG | 1:50

LEGENDE

☒	Wanddurchbruch
⬚	Deckendurchbruch
◺	Bodenschlitz
◢	Bodendurchbruch
▼	OK Fertigbau
▲	UK Fertigbau
▽	OK Rohbau
△	UK Rohbau
± 0,00	Höhenangabe einer waagrechten Fläche
⊕ ±0,00	Höhenangabe eines Punktes in einem Bauwerk - Fertigmaß
⌖ ±0,00	Höhenangabe eines Punktes in einem Bauwerk - Rohbaumaß
BGF	Bruttogesamtfläche
HNF / NNF	Haupt- Nebennutzfläche

▨	Mauerwerk (wärmedämmend)
▨	Mauerwerk (nicht wärmedämmend)
▨	unbewehrter Beton
▨	bewehrter Beton
▦	Betonfertigteil
▤	Stein
▨	Stahl (allgemein)
▨	Holz (allgemein)
▨	Holzwerkstoffe
▩	Dämmstoff (hart)
▩	Dämmstoff (weich)
▩	Kunststoff (allgemein)
▚	Dichtstoff (allgemein)
▥	Gips (Gipskartonplatte)
▥	Gipskartonplatte Brandschutz
□	Erdmaterial (allgemein)
■	Bestand
🟨	Abbruch
🟥	Neubau

—	Medien
—	Fernwärme
—	Gas
—	Strom
—	Heizung
—	Regenwasser
—	Schmutzwasser
—	Wasser
—	Blech
- - -	Abdichtung
- - -	Folie
– – –	Dampfsperre, -bremse

Höhenbezugs- und Maßangaben

DOK	Deckenoberkante
DOS	Deckenoberseite
DUK	Deckenunterkante
DUS	Deckenunterseite
DUF	Deckenunterkante (fertige Untersicht)
FBOK	Fußbodenoberkante
OFF	Oberfläche des fertigen Fußbodens
FDOK	Fundamentoberkante
FDOS	Fundamentoberseite
FDUK	Fundamentunterkante
FDUS	Fundamentunterseite
RH	lichte Raumhöhe
GH	Geschoßhöhe
OK	Oberkante
OS	Oberseite
UK	Unterkante
US	Unterseite
STUK	Sturzunterkante (Rohbaumaß)
STH	Sturzhöhe gemessen von STUK bis DUK (Rohbaumaß)
RPH	Rohbauparapethöhe
FPH	fertige Parapethöhe (FBOK bis OK Fensterbank Innen)

Rauch-, Abgas- und Luftfänge, Schächte

L	Lüftungsschacht
PT	Putztürchen
PS	Putzstück
KT	Kehrtürchen
ABL	Abluft
ZUL	Zuluft
DBA	Druckbelüftungsanlage
DES	Druckentlastungsschacht
BÖ	Belüftungsöffnung
ÜÖ	Überströmöffnung
AÖ	Abströmöffnung mit Überdruckentlastungsorgan
BSK	Brandsschutzklappe
FBHV	Fussbodenheizungsverteiler
E-Verteiler	Elektroverteiler

Öffnungen und deren Abschlüsse

WD	Wanddurchbruch
DD	Deckendurchbruch
FBD	Fußbodendurchbruch
FDD	Fundamentdurchbruch
WS	Wandschlitz
WA	Wandaussparung
DA	Deckenaussparung
FBA	Fußbodenaussparung
RBL	Rohbaulichte
AL	Architekturlichte
STL	Stocklichte
GL	Glaslichte
STAM	Stockaußenmaß
DL	Durchgangslichte
GGT	Ganzglastüre
MGT	Metallgittertür
HT	Hebetüre
HST	Hebeschiebetüre
T	Türe
AT	Allgemeintüre
ET	Eingangstüre
WET	Wohnungseingangstür
IT	Innentür
DF	Drehflügel
DKF	Drehkippflügel
SF	Schiebe-Fenster
SWF	Schwingflügel
WF	Wendeflügel
K	Kippfenster
OL	Oberlichte
DF	Dachflächenfenster
PFR	Pfostenriegelkonstruktion
FE	Fenster
FT	Fenstertüre
R	Rechtsöffnend
L	Linksöffnend
FIX	Fixverglasung
VSG	Verbund-Sicherheitsglas
ESG	Einscheiben-Sicherheitsglas

Drehflügel
Drehkippflügel
Kippflügel
Fenstertüre

EI2 30-C-, EI2 60-C-und EI2 90-C
Feuerschutztüren mit Angabe der Feuerwiderstandsklasse
(gemäß ÖNORM B 3850 und ÖNORM B 3807)

GT	gasdichte Türe
DT	Drucktüre
S 200	Rauchabschluss
S 200	Rauchabschluss
C	Selbstschließend
FLS	Freilaufschließer
LVfTÖ	Lehrverrohrung für Türöffner
elTÖ	elektrischer Türöffner

AUSFÜHRUNG POLIERPLAN GESAMT

Bauvorhaben
PFAR02
2512 Traiskirchen, Tribuswinkel Pfarrgasse 2-4

XXX

Katastralgemeinde 04034 Tribuswinkel
EZ: 51
GstNr.: .19

Diese Zeichnung bzw. Ausarbeitung sowie deren Daten auf Datenträgern sind geistiges Eigentum des Erstellers Arch. Artmüller Georg. Jede Benützung, Veröffentlichung,Vervielfältigung jeglicher Art oder Weitergabe an Dritte bedarf der schriftlichen Zustimmung durch Architekt Artmüller.

Durch die Übernahme dieses Planes akzeptiert die ausführende Firma bzw. Person die darauf dargestellten Anordnungen. Geschriebene Planmaße auf dieser Zeichnunghaben Vorrang gegenüber gezeichneten Dimensionen. Der Auftragnehmer verpflichtet sich **vor** Arbeitsbeginn alle Maße und Bedingungen im Zusammenhang mit seinerArbeit auf der Baustelle verantwortlich zu überprüfen.

Abweichungen gegenüber dargestellten oder schriftlich vereinbarten Anordnungen müssen Architekt Artmüller und der Bauleitung unverzüglich schriftlich mitgeteiltwerden. Vor Arbeitsbeginn sind dem Architekten gültige Werkzeichnungen zur Genehmigung vorzulegen.

NATURMASSE SIND ZU NEHMEN, KOTEN ZU PRÜFEN

Index	Datum	Bearbeiter	Änderung

VORABZUG
28. 09. 2026

Die Plän sind derzeit unter Bearbeitung, aufgrund diverser Erkenntisse durch Bauteilöffnungen. Es handelt sich dementsprechend um einen Arbeitsstand und dient lediglich der Vorab- Information! Kein offizieller Planstand!

Index	Änderung	Datum

Grundeigentümer

Bauwerber / Auftraggeber

ARTMÜLLER ARCHITEKTEN
ZIVILTECHNIKER GMBH
Stolberggasse 34|26 A-1050 Wien
t [+43] 01 . 581 40 83 f [+43] 01. 581 40 83 99 office@artmueller.eu

Planinhalt
OBERGESCHOSS

Maßstab	Gez	Datum	Plannr.	Index
1:50			PFAR02_50_02	

Erstellt, am 11.11.2026

DG | 1:50

LEGENDE

- Wanddurchbruch
- Deckendurchbruch
- Bodenschlitz
- Bodendurchbruch
- ▼ OK Fertigbau
- ▲ UK Fertigbau
- ▽ OK Rohbau
- △ UK Rohbau
- ± 0,00 Höhenangabe einer waagrechten Fläche
- ±0,00 Höhenangabe eines Punktes in einem Bauwerk - Fertigmaß
- ±0,00 Höhenangabe eines Punktes in einem Bauwerk - Rohbaumaß

BGF	Bruttogesamtfläche
HNF / NNF	Haupt- Nebennutzfläche

- Mauerwerk (wärmedämmend)
- Mauerwerk (nicht wärmedämmend)
- unbewehrter Beton
- bewehrter Beton
- Betonfertigteil
- Stein
- Stahl (allgemein)
- Holz (allgemein)
- Holzwerkstoffe
- Dämmstoff (hart)
- Dämmstoff (weich)
- Kunststoff (allgemein)
- Dichtstoff (allgemein)
- Gips (Gipskartonplatte)
- Gipskartonplatte Brandschutz
- Erdmaterial (allgemein)
- Bestand
- 🟨 Abbruch
- 🟥 Neubau

- Medien
- Fernwärme
- Gas
- Strom
- Heizung
- Regenwasser
- Schmutzwasser
- Wasser

- Blech
- Abdichtung
- Folie
- Dampfsperre, -bremse

Höhenbezugs- und Maßangaben

DOK	Deckenoberkante
DOS	Deckenoberseite
DUK	Deckenunterkante
DUS	Deckenunterseite
DUF	Deckenunterkante (fertige Untersicht)
FBOK	Fußbodenoberkante
OFF	Oberfläche des fertigen Fußbodens
FDOK	Fundamentoberkante
FDOS	Fundamentoberseite
FDUK	Fundamentunterkante
FDUS	Fundamentunterseite
RH	lichte Raumhöhe
GH	Geschoßhöhe
OK	Oberkante
OS	Oberseite
UK	Unterkante
US	Unterseite
STUK	Sturzunterkante (Rohbaumaß)
STH	Sturzhöhe gemessen von STUK bis DUK (Rohbaumaß)
RPH	Rohbauparapethöhe
FPH	fertige Parapethöhe (FBOK bis OK Fensterbank Innen)

Rauch-, Abgas- und Luftfänge, Schächte

L	Lüftungsschacht
PT	Putztürchen
PS	Putzstück
KT	Kehrtürchen
ABL	Abluft
ZUL	Zuluft
DBA	Druckbelüftungsanlage
DES	Druckentlastungsschacht
BÖ	Belüftungsöffnung
ÜÖ	Überströmöffnung
AÖ	Abströmöffnung mit Überdruckentlastungsorgan
BSK	Brandsschutzklappe
FBHV	Fussbodenheizungsverteiler
E-Verteiler	Elektroverteiler

Öffnungen und deren Abschlüsse

WD	Wanddurchbruch
DD	Deckendurchbruch
FBD	Fußbodendurchbruch
FDD	Fundamentdurchbruch
WS	Wandschlitz
WA	Wandaussparung
DA	Deckenaussparung
FBA	Fußbodenaussparung
RBL	Rohbaulichte
AL	Architekturlichte
STL	Stocklichte
GL	Glaslichte
STAM	Stockaußenmaß
DL	Durchgangslichte
GGT	Ganzglastüre
MGT	Metallgittertür
HT	Hebetüre
HST	Hebeschiebetüre
T	Türe
AT	Allgemeintüre
ET	Eingangstüre
WET	Wohnungseingangstür
IT	Innentür
DF	Drehflügel
DKF	Drehkippflügel
SF	Schiebe-Fenster
SWF	Schwingflügel
WF	Wendeflügel
K	Kippfenster
OL	Oberlichte
DF	Dachfächenfenster
PFR	Pfostenriegelkonstruktion
FE	Fenster
FT	Fenstertüre
R	Rechtsöffnend
L	Linksöffnend
FIX	Fixverglasung
VSG	Verbund-Sicherheitsglas
ESG	Einscheiben-Sicherheitsglas

- Drehflügel
- Drehkippflügel
- Kippflügel
- Fenstertüre

EI2 30-C-, EI2 60-C-und EI2 90-C
Feuerschutztüren mit Angabe der Feuerwiderstandsklasse
(gemäß ÖNORM B 3850 und ÖNORM B 3807)

GT	gasdichte Türe
DT	Drucktüre
S 200	Rauchabschluss
S 200	Rauchabschluss
C	Selbstschließend
FLS	Freilaufschließer
LVfTÖ	Lehrverrohrung für Türöffner
elTÖ	elektrischer Türöffner

AUSFÜHRUNG POLIERPLAN GESAMT

Bauvorhaben
PFAR02
2512 Traiskirchen, Tribuswinkel Pfarrgasse 2-4

XXX

Katastralgemeinde 04034 Tribuswinkel
EZ: 51
GstNr.: .19

Diese Zeichnung bzw. Ausarbeitung sowie deren Daten auf Datenträgern sind geistiges Eigentum des Erstellers Arch. Artmüller Georg. Jede Benützung, Veröffentlichung,Vervielfältigung jeglicher Art oder Weitergabe an Dritte bedarf der schriftlichen Zustimmung durch Architekt Artmüller.

Durch die Übernahme dieses Planes akzeptiert die ausführende Firma bzw. Person die darauf dargestellten Anordnungen. Geschriebene Planmaße auf dieser Zeichnunghaben Vorrang gegenüber gezeichneten Dimensionen. Der Auftragnehmer verpflichtet sich **vor** Arbeitsbeginn alle Maße und Bedingungen im Zusammenhang mit seinerArbeit auf der Baustelle verantwortlich zu überprüfen.

Abweichungen gegenüber dargestellten oder schriftlich vereinbarten Anordnungen müssen Architekt Artmüller und der Bauleitung unverzüglich schriftlich mitgeteiltwerden. Vor Arbeitsbeginn sind dem Architekten gültige Werkzeichnungen zur Genehmigung vorzulegen.

NATURMASSE SIND ZU NEHMEN, KOTEN ZU PRÜFEN

VORABZUG
28. 09. 2026

Index	Datum	Bearbeiter	Änderung

Die Plän sind derzeit unter Bearbeitung, aufgrund diverser Erkenntisse durch Bauteilöffnungen. Es handelt sich dementsprechend um einen Arbeitsstand und dient lediglich der Vorab- Information! Kein offizieller Planstand!

Index	Änderung	Datum

Grundeigentümer

Bauwerber / Auftraggeber

ARTMÜLLER ARCHITEKTEN
ZIVILTECHNIKER GMBH
Stolberggasse 34|26 A-1050 Wien
t [+43] 01 . 581 40 83 f [+43] 01. 581 40 83 99 office@artmueller.eu

Planinhalt
DACHGESCHOSS

Maßstab	Gez	Datum	Plannr.	Index
1:50			PFAR02_50_03	

Erstellt, am 11.11.2026

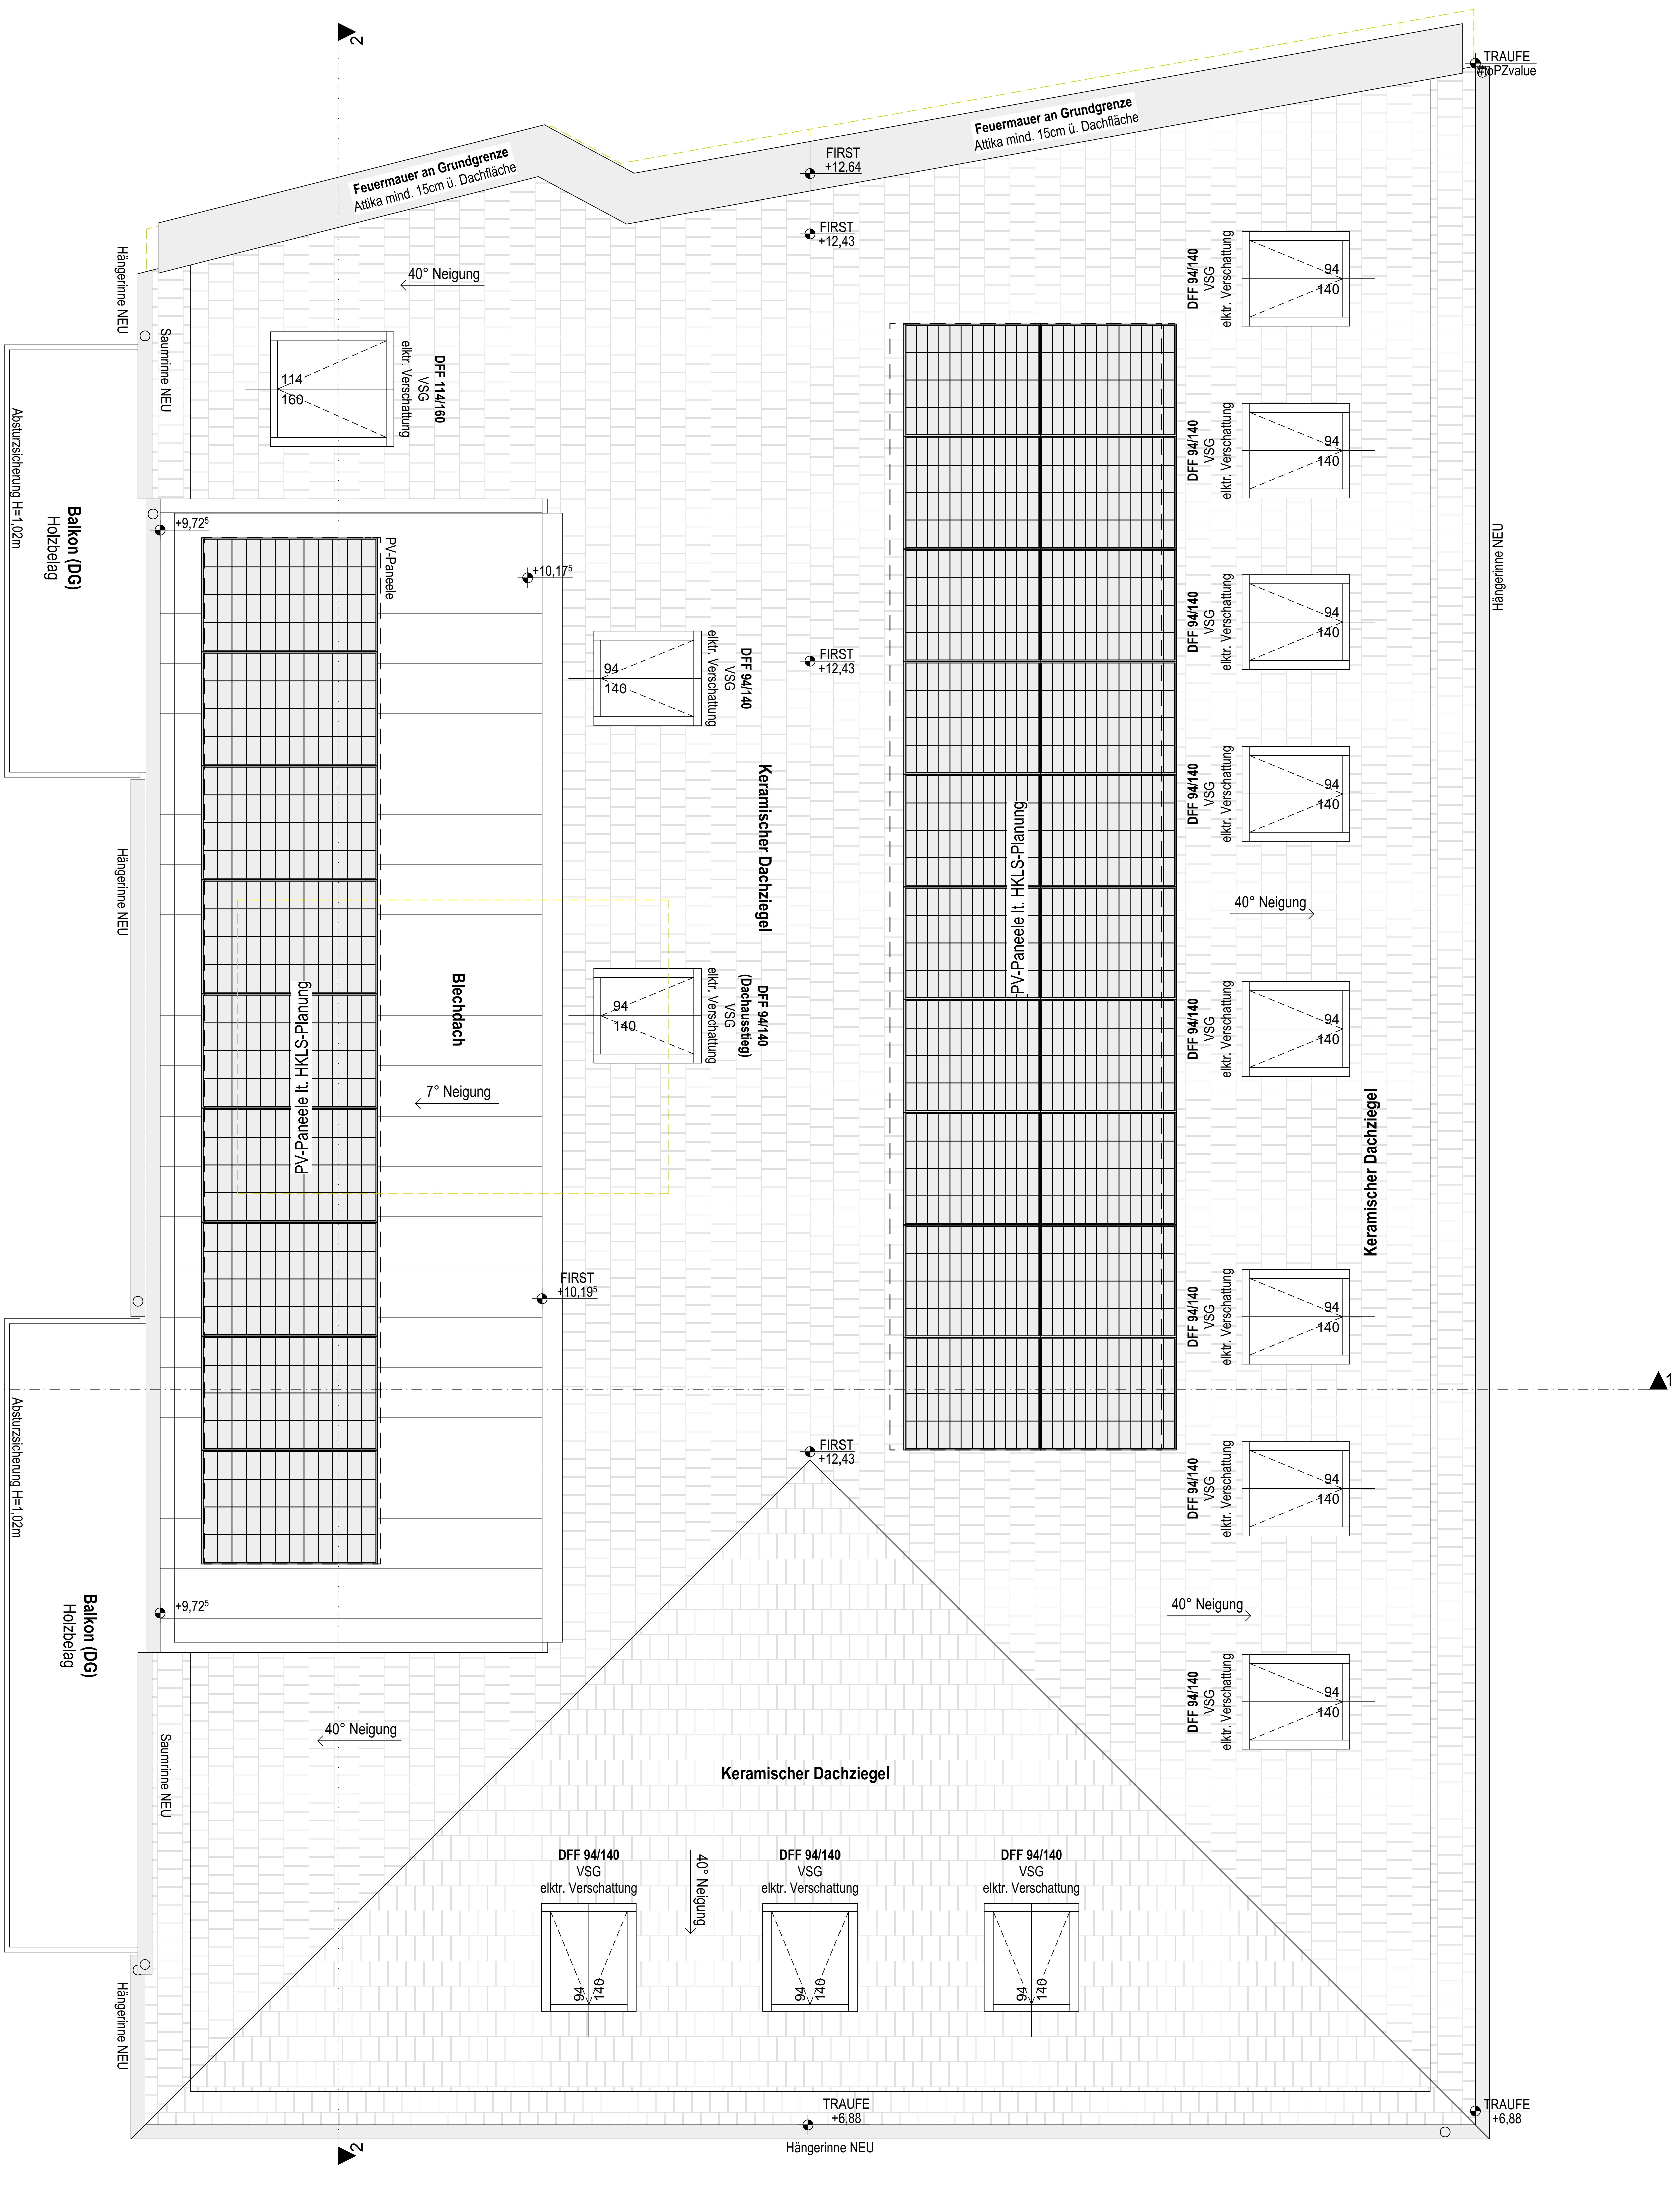

Dachdraufsicht | 1:50

LEGENDE

☒	Wanddurchbruch
▭	Deckendurchbruch
▭	Bodenschlitz
◢	Bodendurchbruch
▼	OK Fertigbau
▲	UK Fertigbau
▽	OK Rohbau
△	UK Rohbau
± 0,00	Höhenangabe einer waagrechten Fläche
±0,00	Höhenangabe eines Punktes in einem Bauwerk - Fertigmaß
±0,00	Höhenangabe eines Punktes in einem Bauwerk - Rohbaumaß
BGF	Bruttogesamtfläche
HNF / NNF	Haupt- Nebennutzfläche

▨	Mauerwerk (wärmedämmend)
▨	Mauerwerk (nicht wärmedämmend)
▨	unbewehrter Beton
▨	bewehrter Beton
▦	Betonfertigteil
▤	Stein
▨	Stahl (allgemein)
▨	Holz (allgemein)
▨	Holzwerkstoffe
▩	Dämmstoff (hart)
▩	Dämmstoff (weich)
▩	Kunststoff (allgemein)
▚	Dichtstoff (allgemein)
▥	Gips (Gipskartonplatte)
▥	Gipskartonplatte Brandschutz
☐	Erdmaterial (allgemein)
■	Bestand
🟨	Abbruch
🟥	Neubau

—	Medien
—	Fernwärme
—	Gas
—	Strom
—	Heizung
—	Regenwasser
—	Schmutzwasser
—	Wasser
—	Blech
- - -	Abdichtung
- - -	Folie
- - -	Dampfsperre, -bremse

Höhenbezugs- und Maßangaben

DOK	Deckenoberkante
DOS	Deckenoberseite
DUK	Deckenunterkante
DUS	Deckenunterseite
DUF	Deckenunterkante (fertige Untersicht)
FBOK	Fußbodenoberkante
OFF	Oberfläche des fertigen Fußbodens
FDOK	Fundamentoberkante
FDOS	Fundamentoberseite
FDUK	Fundamentunterkante
FDUS	Fundamentunterseite
RH	lichte Raumhöhe
GH	Geschoßhöhe
OK	Oberkante
OS	Oberseite
UK	Unterkante
US	Unterseite
STUK	Sturzunterkante (Rohbaumaß)
STH	Sturzhöhe gemessen von STUK bis DUK (Rohbaumaß)
RPH	Rohbauparapethöhe
FPH	fertige Parapethöhe (FBOK bis OK Fensterbank Innen)

Rauch-, Abgas- und Luftfänge, Schächte

L	Lüftungsschacht
PT	Putztürchen
PS	Putzstück
KT	Kehrtürchen
ABL	Abluft
ZUL	Zuluft
DBA	Druckbelüftungsanlage
DES	Druckentlastungsschacht
BÖ	Belüftungsöffnung
ÜÖ	Überströmöffnung
AÖ	Abströmöffnung mit Überdruckentlastungsorgan
BSK	Brandsschutzklappe
FBHV	Fussbodenheizungsverteiler
E-Verteiler	Elektroverteiler

Öffnungen und deren Abschlüsse

WD	Wanddurchbruch
DD	Deckendurchbruch
FBD	Fußbodendurchbruch
FDD	Fundamentdurchbruch
WS	Wandschlitz
WA	Wandaussparung
DA	Deckenaussparung
FBA	Fußbodenaussparung
RBL	Rohbaulichte
AL	Architekturlichte
STL	Stocklichte
GL	Glaslichte
STAM	Stockaußenmaß
DL	Durchgangslichte
GGT	Ganzglastüre
MGT	Metallgittertür
HT	Hebetüre
HST	Hebeschiebetüre
T	Türe
AT	Allgemeintüre
ET	Eingangstüre
WET	Wohnungseingangstür
IT	Innentür
DF	Drehflügel
DKF	Drehkippflügel
SF	Schiebe-Fenster
SWF	Schwingflügel
WF	Wendeflügel
K	Kippfenster
OL	Oberlichte
DF	Dachfächenfenster
PFR	Pfostenriegelkonstruktion
FE	Fenster
FT	Fenstertüre
R	Rechtsöffnend
L	Linksöffnend
FIX	Fixverglasung
VSG	Verbund-Sicherheitsglas
ESG	Einscheiben-Sicherheitsglas

Drehflügel
Drehkippflügel
Kippflügel
Fenstertüre

EI2 30-C-, EI2 60-C-und EI2 90-C
Feuerschutztüren mit Angabe der Feuerwiderstandsklasse
(gemäß ÖNORM B 3850 und ÖNORM B 3807)

GT	gasdichte Türe
DT	Drucktüre
S 200	Rauchabschluss
S 200	Rauchabschluss
C	Selbstschließend
FLS	Freilaufschließer
LVfTÖ	Lehrverrohrung für Türöffner
elTÖ	elektrischer Türöffner

AUSFÜHRUNG POLIERPLAN GESAMT

Bauvorhaben
PFAR02
2512 Traiskirchen, Tribuswinkel Pfarrgasse 2-4

XXX

Katastralgemeinde 04034 Tribuswinkel
EZ: 51
GstNr.: .19

Diese Zeichnung bzw. Ausarbeitung sowie deren Daten auf Datenträgern sind geistiges Eigentum des Erstellers Arch. Artmüller Georg. Jede Benützung, Veröffentlichung,Vervielfältigung jeglicher Art oder Weitergabe an Dritte bedarf der schriftlichen Zustimmung durch Architekt Artmüller.

Durch die Übernahme dieses Planes akzeptiert die ausführende Firma bzw. Person die darauf dargestellten Anordnungen. Geschriebene Planmaße auf dieser Zeichnunghaben Vorrang gegenüber gezeichneten Dimensionen. Der Auftragnehmer verpflichtet sich **vor** Arbeitsbeginn alle Maße und Bedingungen im Zusammenhang mit seinerArbeit auf der Baustelle verantwortlich zu überprüfen.

Abweichungen gegenüber dargestellten oder schriftlich vereinbarten Anordnungen müssen Architekt Artmüller und der Bauleitung unverzüglich schriftlich mitgeteiltwerden. Vor Arbeitsbeginn sind dem Architekten gültige Werkzeichnungen zur Genehmigung vorzulegen.

NATURMASSE SIND ZU NEHMEN, KOTEN ZU PRÜFEN

VORABZUG
28. 09. 2026

Index	Datum	Bearbeiter	Änderung

Die Plän sind derzeit unter Bearbeitung, aufgrund diverser Erkenntisse durch Bauteilöffnungen. Es handelt sich dementsprechend um einen Arbeitsstand und dient lediglich der Vorab- Information! Kein offizieller Planstand!

Index	Änderung	Datum

Grundeigentümer

Bauwerber / Auftraggeber

ARTMÜLLER ARCHITEKTEN
ZIVILTECHNIKER GMBH
Stolberggasse 34|26 A-1050 Wien
t [+43] 01 . 581 40 83 f [+43] 01. 581 40 83 99 office@artmueller.eu

Planinhalt
DACHDRAUFSICHT

Maßstab	Gez	Datum	Plannr.	Index
1:50			PFAR02_50_04	

Erstellt, am 11.11.2026

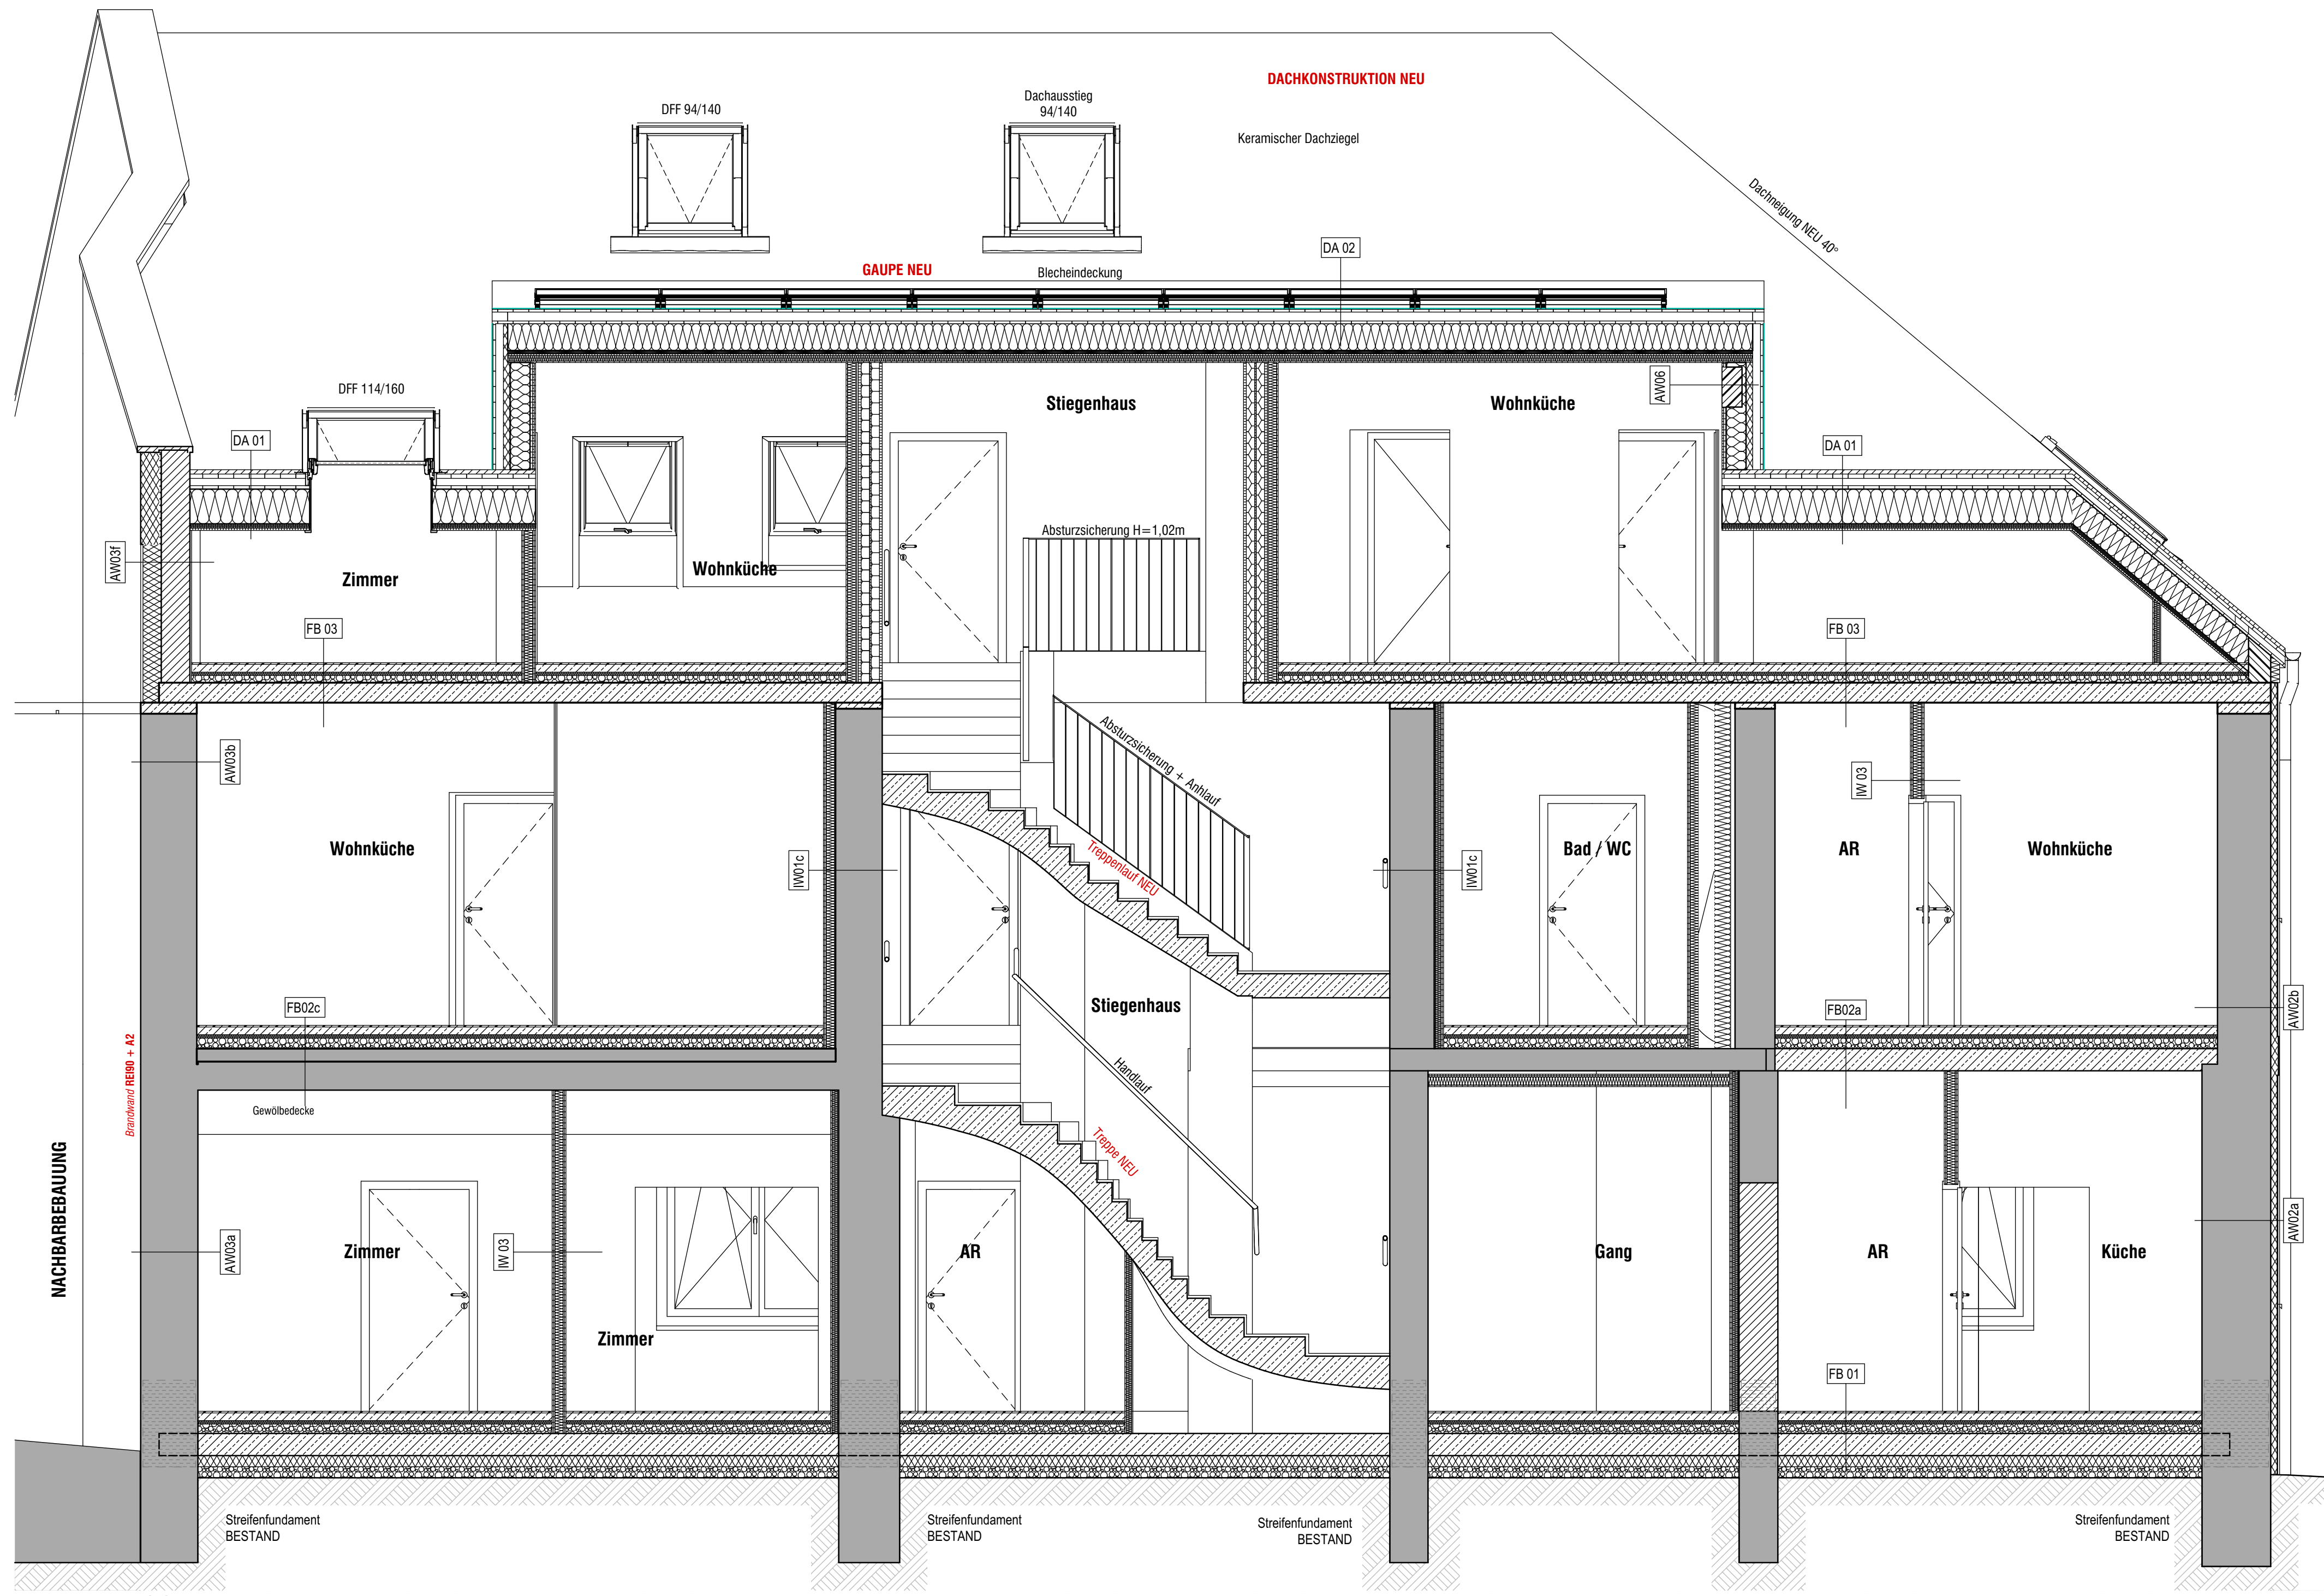

SCHNITT 2-2 M 1:50

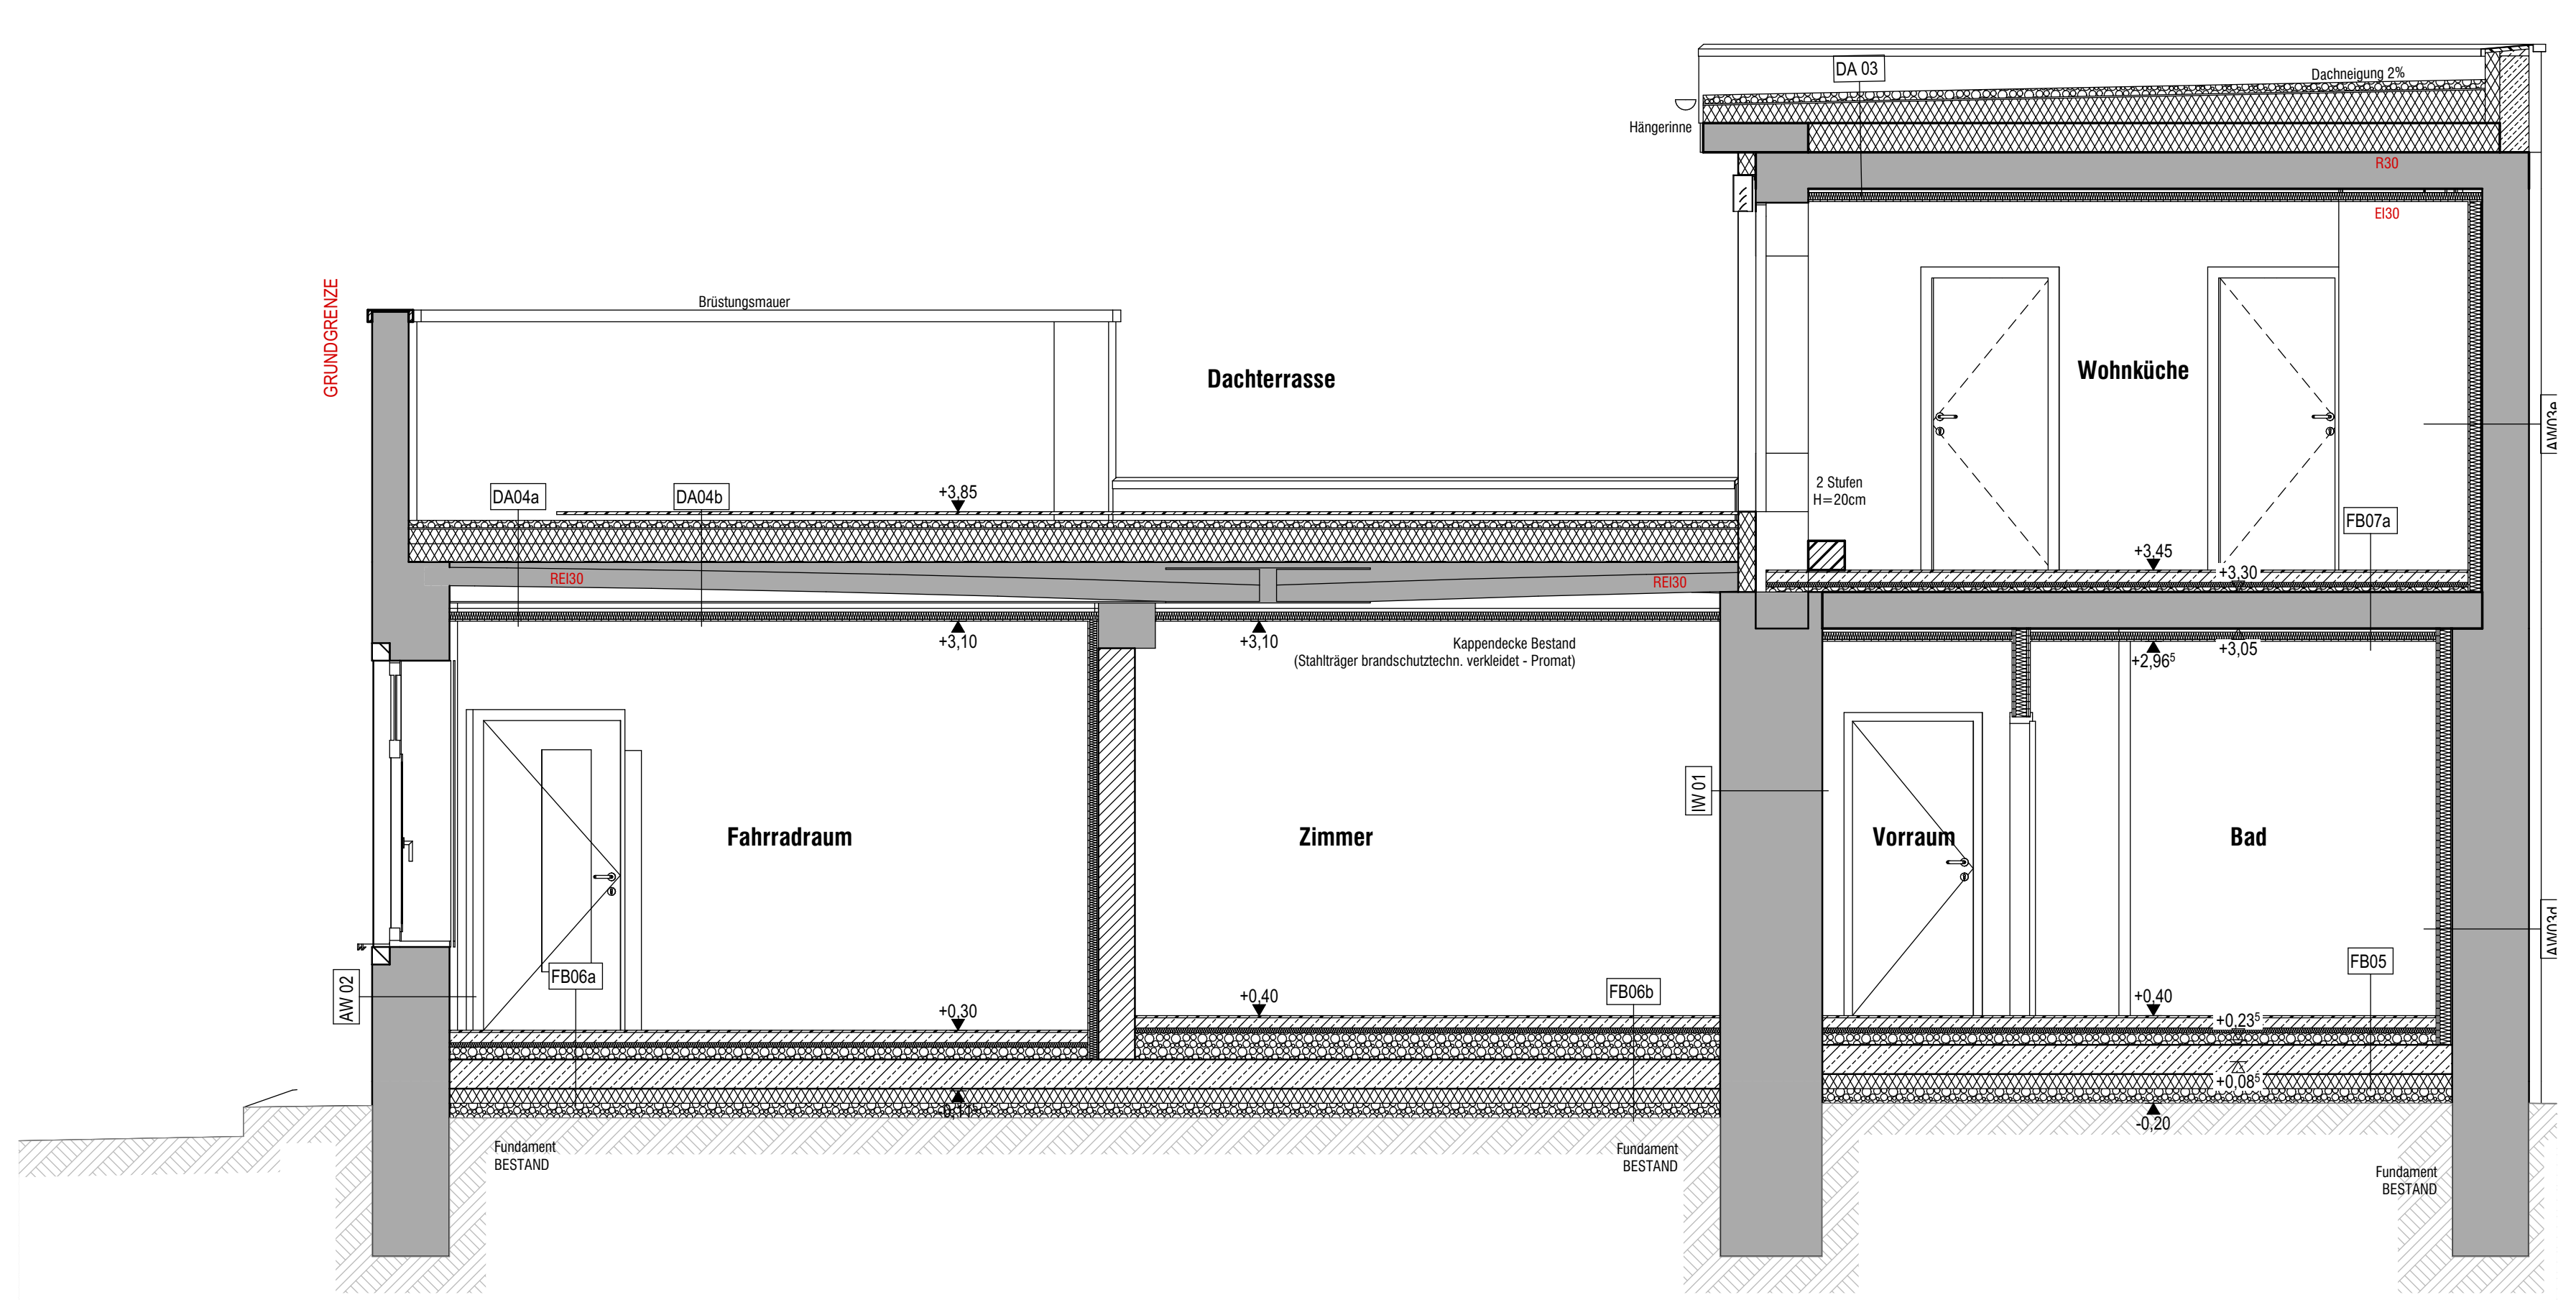

SCHNITT 3-3 M 1:50

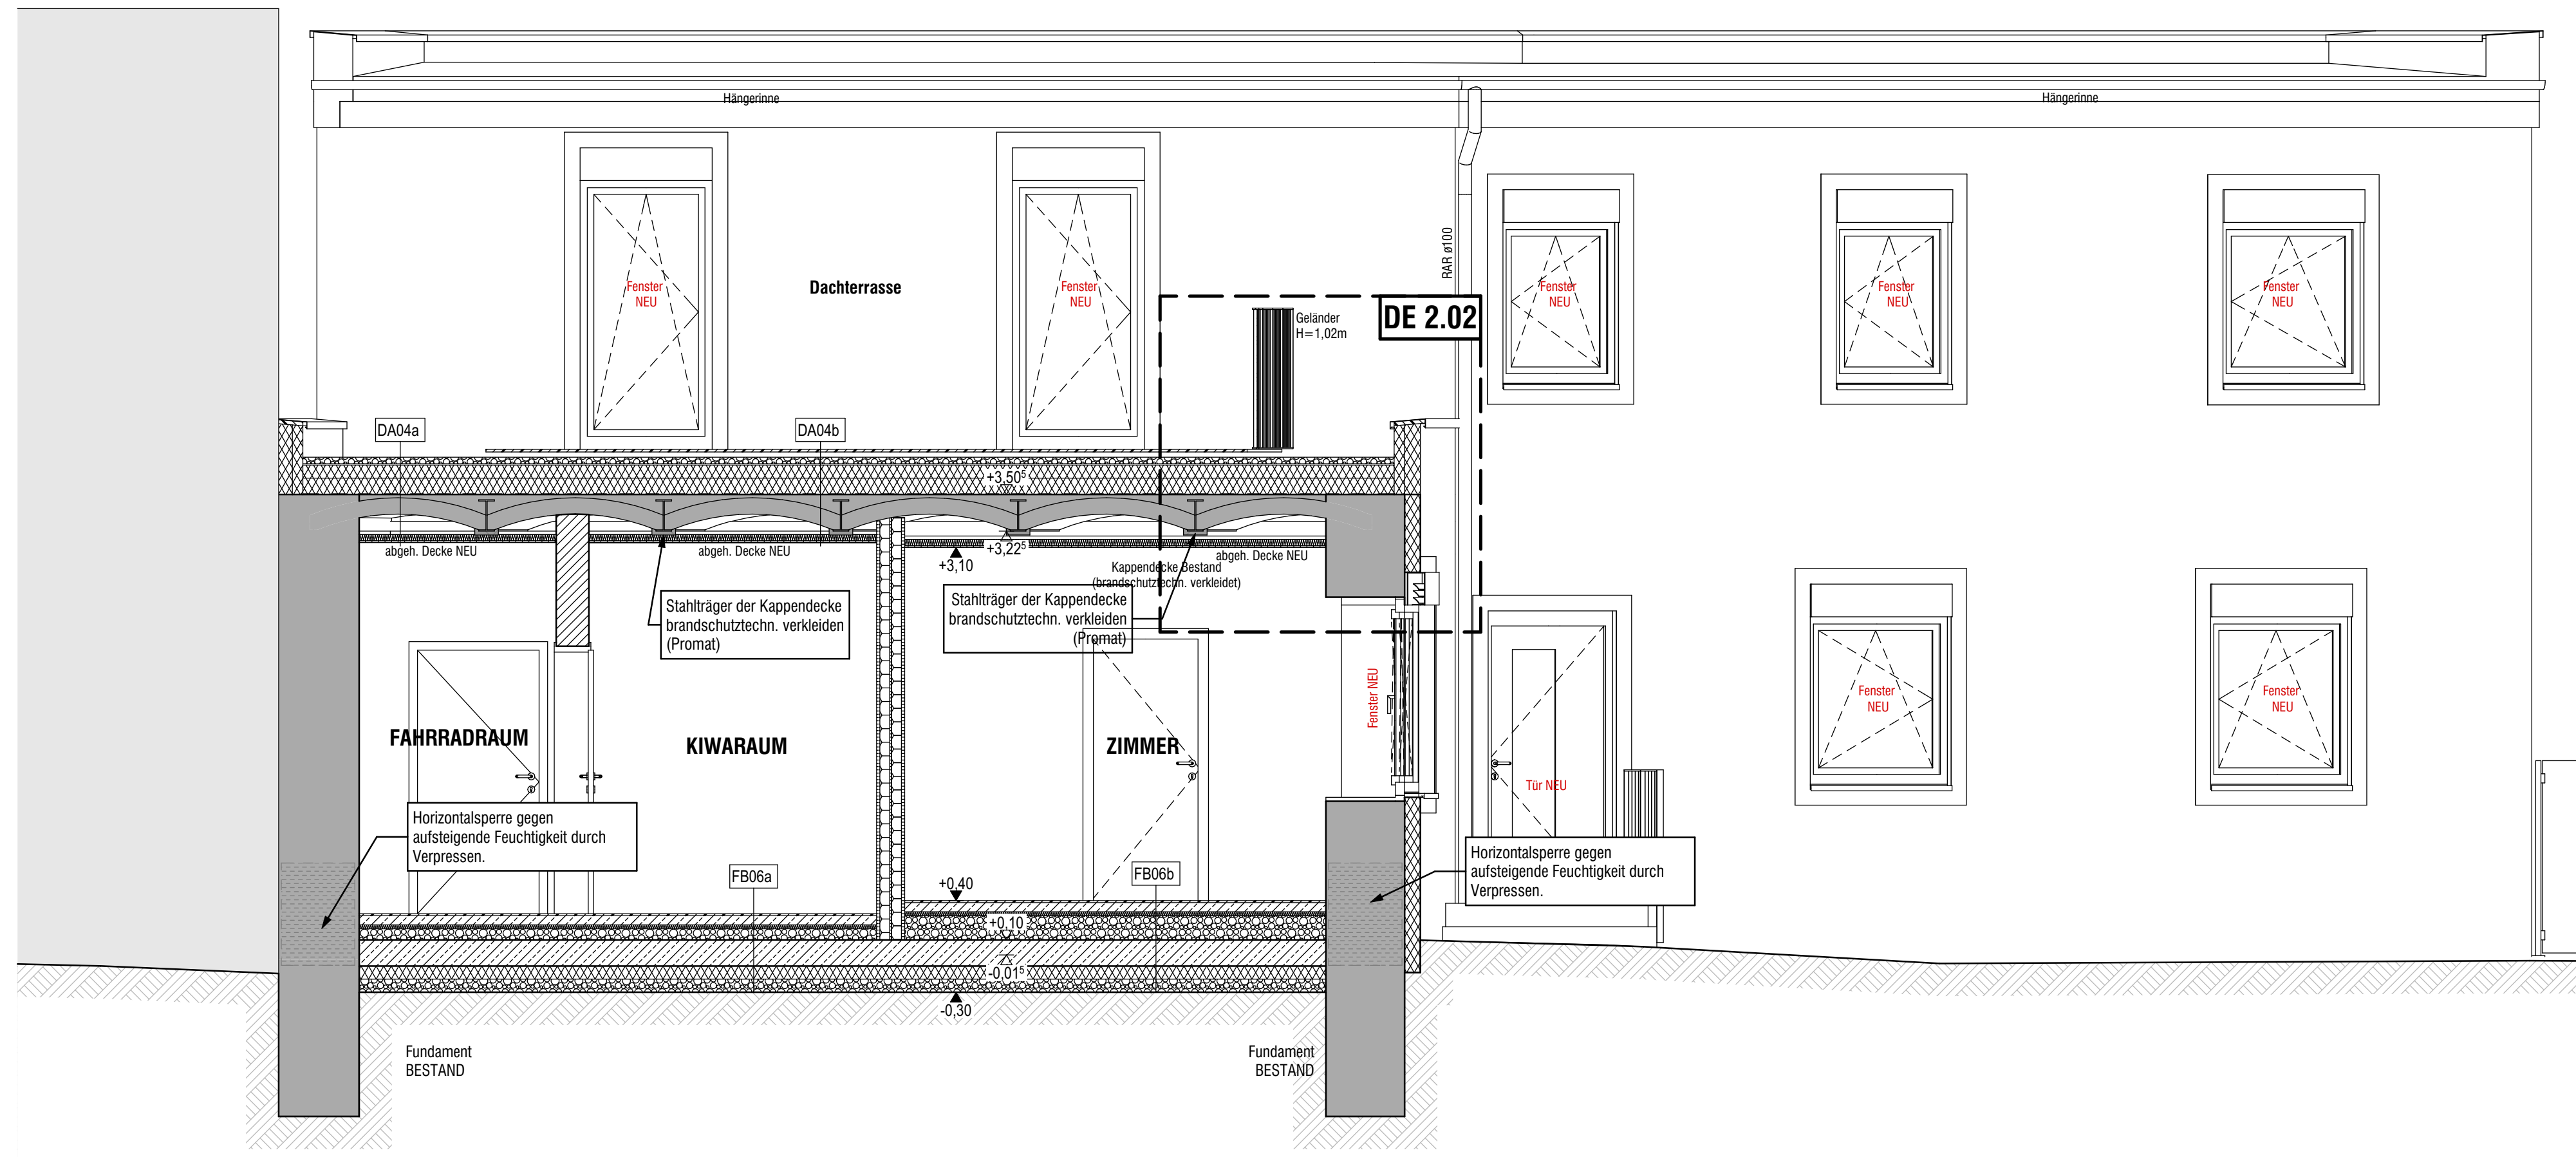
Dachterrasse
DA04a
DA04b
DE 2.02
FAHRRADRAUM
KIWARAUM
ZIMMER
Stahlträger der Kappendecke brandschutztechn. verkleidet (Promat)
Horizontalsperre gegen aufsteigende Feuchtigkeit durch Verpressen.
Fundament BESTAND

SCHNITT 1-1 M 1:50

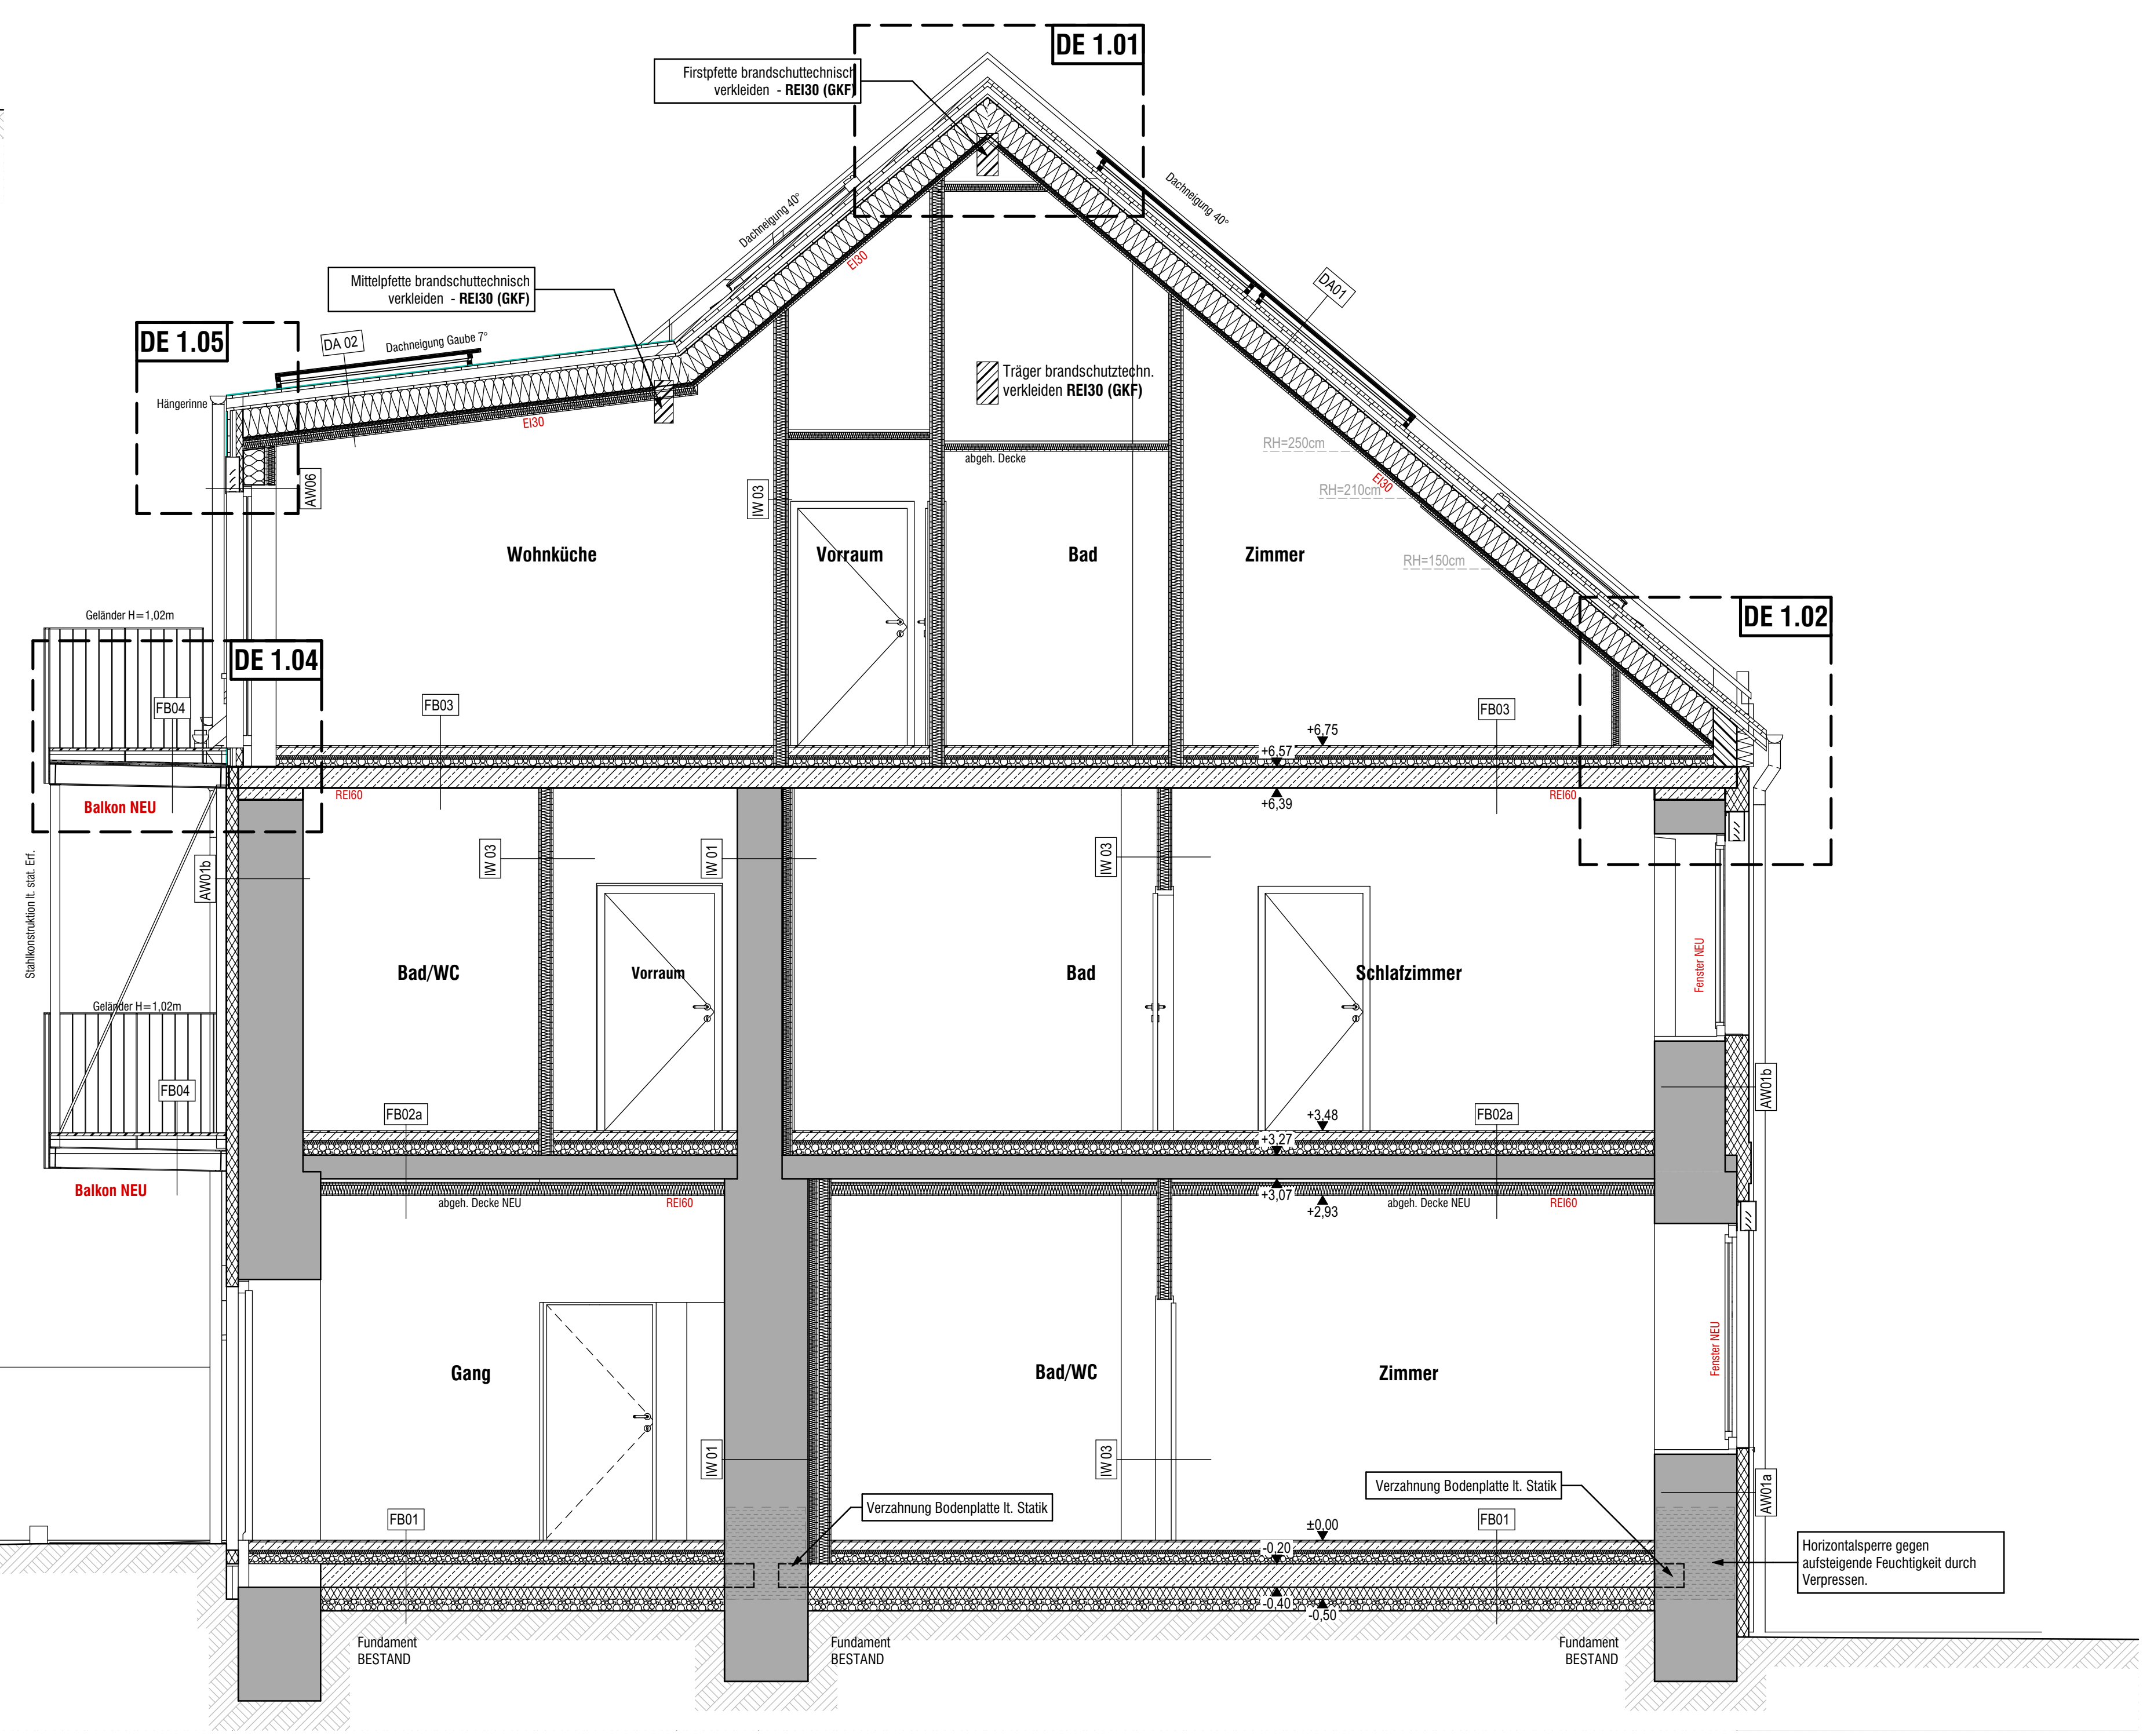
Firstpfette brandschutztechnisch verkleidet - REI30 (GKF)
DE 1.01
Mittelpfette brandschutztechnisch verkleidet - REI30 (GKF)
DE 1.05
Träger brandschutztechn. verkleidet REI30 (GKF)
DE 1.02
DE 1.04
Balkon NEU
Wohnküche
Vorraum
Bad
Zimmer
Bad/WC
Vorraum
Bad
Schlafzimmer
Gang
Bad/WC
Zimmer
Verzahnung Bodenplatte lt. Statik
Horizontalsperre gegen aufsteigende Feuchtigkeit durch Verpressen.
Fundament BESTAND

SCHNITT 1-1 M 1:50

AW01a/b	ZIEGELMAUERWERK VWS 10cm	R60
1,00 cm	Silikatputz genetzt und gespachtelt, In Anschlussbereichen mit Feuchtigkeitsabdichtung / Hochzug	
10,00 cm	EPS Wärmedämmung (XPS im Sockelbereich)	
0,80 cm	Klebespachtel	
70 / 50 cm	Ziegelmauerwerk 70,00 / 50,00 cm	
1,50 cm	Innenputz	
73,3 / 58,30 cm	BAUTEIL GESAMT	

AW02 a/b	ZIEGELMAUERWERK VWS 6cm	R60
1,00 cm	Silikatputz genetzt und gespachtelt, In Anschlussbereichen mit Feuchtigkeitsabdichtung / Hochzug	
6,00 cm	EPS Wärmedämmung (XPS im Sockelbereich)	
0,80 cm	Klebespachtel	
60 / 45 cm	Ziegelmauerwerk 45,00 / 60,00 cm	
1,50 cm	Innenputz	
69,3 / 54,3cm	BAUTEIL GESAMT	

AW03 a/b/c	ZIEGELMAUERWERK FEUERMAUER	R90 + A2
1,50 cm	Außenputz	
60 / 40 / 30 cm	Ziegelmauerwerk 30,00 / 40,00 / 60,00 cm	
1,50 cm	Innenputz	
63 / 43 / 33 cm	BAUTEIL GESAMT	

AW 03 d/e	MWK HOFTRAKT FEUERMAUER + VS	R90 + A2
1,50 cm	Außenputz	
38 / 30 cm	Ziegelmauerwerk 38 / 30 cm	
1,50 cm	Innenputz	
1,00 cm	Luftschicht (Abstand)	
7,50 cm	C-Profil dazw. Mineralwolle lt. Bauphysik Dampfbremse, sd Wert lt. Bauphysik, allseits angebunden	
1,25 cm	1 x 1,25 cm GKB-Platte (GKBi in Nassräumen)	
50,75 / 42,75 cm	BAUTEIL GESAMT	

AW 03 f	MWK DG NEU FEUERMAUER + VS	R90 + A2
1,00 cm	Silikatputz genetzt und gespachtelt	
16,00 cm	Mineralwolle	
0,80 cm	Klebespachtel	
25,00 cm	Porotherm - Ziegelmauerwerk 25,00 cm	
1,50 cm	Innenputz	
44,30 cm	BAUTEIL GESAMT	

AW 04 a/b/c	ZIEGELMAUERWERK VWS 12cm HOFTRAKT	R60
1,00 cm	Silikatputz genetzt und gespachtelt, In Anschlussbereichen mit Feuchtigkeitsabdichtung / Hochzug	
12,00 cm	EPS Wärmedämmung (XPS im Sockelbereich)	
0,80 cm	Klebespachtel	
65 / 30 / 25 cm	Ziegelmauerwerk 65 / 30 / 25 cm	
1,50 cm	Innenputz	
3 / 45,3 / 40,3cm	BAUTEIL GESAMT	

AW 05	ZIEGELMAUERWERK OHNE VWS HOFTRAKT	R60
1,50 cm	Außenputz	
50,00 cm	Ziegelmauerwerk 50,00 cm	
1,50 cm	Innenputz	
52,50cm	BAUTEIL GESAMT	

AW 06	HOLZ-LEICHTBAU BLECH (GAUBE)	EI60
0,80 cm	Blech Zink, gefalzt auf Strukturgewebe	
2,40 cm	Vollholzschalung	
5,00 cm	Konterlattung / Hinterlüftung mit Nageldichtband	
0,10 cm	Diffusionsoffene UV-beständige Winddichtbahn lt. Bauphysik allseitig und alle Durchdringungen eingebunden	
6,00 cm	Holzfaserdämmplatte	
20,00 cm	Konstruktionsholz lt. Statik, fungizid behandelt dazw. Dämmung lt. Bauphysik	
2,20 cm	OSB Platte, allseits luftdicht verklebt	
1,50 cm	1 x 1,5 GKF-Platte (EI30)	
5,00 cm	UK / Lattung dazw. Mineralwolle - Installationsebene	
1,25 cm	1 x 1,25 cm GKB-Platte (GKBi in Nassräumen)	
44,25 cm	BAUTEIL GESAMT	

IW 01 a/b/c/d	WOHNUNGSTRENNWAND ZIEGEL	REI 60
2,50 cm	Innenputz	
/ 50 / 40 / 20 cm	Ziegelmauerwerk 20 / 40 / 50 / 60 cm (mind.REI60)	
2,50 cm	Innenputz	
0,25 cm	Luftraum (Abstand)	
5,00 cm	C-Profil dazw. Mineralwolle	
1,25 cm	1,25 cm GKB-Platte	
82,75 -32,75 cm	BAUTEIL GESAMT	DnT,w ≥ 55 dB

IW 02 a/b/c/d	INNENWAND TRAGEND BESTAND	R60
2,50 cm	Innenputz	
/ 70 / 60 / 40 cm	Vollziegelmauerwerk 40 / 60 / 70 / 80 cm	
2,50 cm	Innenputz	
85,0 - 45,0 cm	BAUTEIL GESAMT	

IW 02 e/f/g	INNENWAND NICHTTRAGEND BESTAND
1,50 cm	Innenputz
25 / 15 / 10 cm	Hochlochziegelmauerwerk 10 / 15 / 25 cm
1,50 cm	Innenputz
28 -13 cm	BAUTEIL GESAMT

IW 03	INNENWAND TROCKENBAU DOPPELT BEPLANKT
2,50 cm	2 x 1,25 cm GKB-Platte (GKBi in Nassräumen)
7,50 cm	C-Profil dazw. Mineralwolle
2,50 cm	2 x 1,25 cm GKB-Platte (GKBi in Nassräumen)
12,50 cm	BAUTEIL GESAMT

IW 04	WOHNUNGSTRENNWAND TROCKENBAU	EI 90
2,50 cm	2 x 1,25 cm GKF-Platte	
7,50 cm	C-Profil dazw. Mineralwolle	
1,25 cm	1 x 1,25 cm GKF- Platte PE- Folie allseits luftdicht verklebt	
0,25cm	Luftraum (Abstand)	
7,50 cm	C-Profil dazw. Mineralwolle	
2,50 cm	2 x 1,25 cm GKB-Platte (GKBi in Nassräumen)	
21,50 cm	BAUTEIL GESAMT	DnT,w ≥ 55 dB

VS 01	VORSATZSCHALE TROCKENBAU
1,00 cm	Luftraum (Abstand)
5,00 cm	C-Profil dazw. Mineralwolle
1,25 cm	1 x 1,25 cm GKB-Platte (GKBi in Nassräumen)
7,25 cm	BAUTEIL GESAMT

VS 02	VORSATZSCHALE TROCKENBAU NASSRAUM
1,00 cm	Luftraum (Abstand)
7,50 cm	C-Profil dazw. Mineralwolle
2,50 cm	2 x 1,25 cm GKB-Platte (GKBi in Nassräumen)
11,00 cm	BAUTEIL GESAMT

VS 03	VORSATZSCHALE TROCKENBAU WC
4,00 cm	Luftraum (Abstand)
15,00 cm	C-Profil dazw. Mineralwolle
2,50 cm	2 x 1,25 cm GKB-Platte (GKBi in Nassräumen)
21,50 cm	BAUTEIL GESAMT

FB 01	FUSSBODEN GEGEN ERDREICH (STRASSENTRAKT)
1,50 cm	Bodenbelag (Parkett / Fliese)
7,00 cm	Zementestrich mit FBH, inkl. Randdämmstreifen 1cm PE-Folie seitlich hochgezogen bis Estrich OK
3,00 cm	Trittschalldämmplatten lt. Bauphysik Dampfbremse
7,50 cm	EPS - Schüttung zementgebunden
1,00 cm	Bituminöse Bauwerksabdichtung
20,00 cm	Stahlbetonplatte PE-Folie
10,00 cm	XPS - Perimeterdämmung
15,00 cm	Unterbau / Rollierung
65,00 cm	BAUTEIL GESAMT

FB 02 a	DIPPELBAUMDECKE ÜBER EG	REI 60
1,50 cm	Bodenbelag (Parkett / Fliese)	
7,00 cm	Zementestrich mit FBH, inkl. Randdämmstreifen 1cm PE-Folie seitlich hochgezogen bis Estrich OK	
3,00 cm	Trittschalldämmplatten lt. Bauphysik	
9,50 cm	Schüttung zementgebunden PE-Folie	
20,00 cm	Bestehende Dippelbaumdecke	
3,00 cm	Holzlattung	
2,50 cm	2 x 1,25 cm GKF-Platte (EI60)	
7,50 cm	Metall-UK dazw. MW (Installationsebene)	
1,25 cm	1 x 1,25 cm GKB-Platte (GKBi in Nassräumen)	
45,35 cm	BAUTEIL GESAMT	

FB 02 b	TRAMDECKE ÜBER EG	REI 60
1,50 cm	Bodenbelag (Parkett / Fliese)	
7,00 cm	Zementestrich mit FBH, inkl. Randdämmstreifen 1cm PE-Folie seitlich hochgezogen bis Estrich OK	
3,00 cm	Trittschalldämmplatten lt. Bauphysik	
8,00 cm	Schüttung zementgebunden PE-Folie	
2,40 cm	Vollholzschalung	
18,00 cm	Besteh. Holztramdecke (dazw. 10cm MW)	
3,00 cm	Holzlattung	
2,50 cm	2 x 1,25 cm GKF-Platte (EI60)	
7,50 cm	Metall-UK dazw. MW (Installationsebene)	
1,25 cm	1 x 1,25 cm GKB-Platte (GKBi in Nassräumen)	
54,15 cm	BAUTEIL GESAMT	

FB 02 c	DECKE ÜBER EG	REI 60
1,50 cm	Bodenbelag (Parkett / Fliese)	
7,00 cm	Zementestrich mit FBH, inkl. Randdämmstreifen 1cm PE-Folie seitlich hochgezogen bis Estrich OK	
3,00 cm	Trittschalldämmplatten lt. Bauphysik	
9,50 cm	Schüttung zementgebunden PE-Folie	
27,5 - 78,0 cm	Bestehendes Ziegelgewölbe (mind. REI60)	
1,50 cm	Innenputz	
45,50 - 96,0cm	BAUTEIL GESAMT	

FB 02 d	DECKE ÜBER EG STB NEU	REI 60
1,50 cm	Bodenbelag (Parkett / Fliese)	
7,00 cm	Zementestrich mit FBH, inkl. Randdämmstreifen 1cm PE-Folie seitlich hochgezogen bis Estrich OK	
3,00 cm	Trittschalldämmplatten lt. Bauphysik	
9,50 cm	Schüttung zementgebunden	
20,00 cm	Stahlbetondecke (mind. REI60)	
0,50 cm	Spachtelung	
41,50 cm	BAUTEIL GESAMT	

FB 03	STB-DECKE ÜBER 1.OG	REI 60
1,50 cm	Bodenbelag (Parkett / Fliese)	
7,00 cm	Zementestrich mit FBH, inkl. Randdämmstreifen 1cm PE-Folie seitlich hochgezogen bis Estrich OK	
3,00 cm	Trittschalldämmplatten lt. Bauphysik	
6,50 cm	EPS - Schüttung zementgebunden	
18,00 cm	Stalbetondecke (mind. REI60)	
0,50 cm	Spachtelung	
36,50 cm	BAUTEIL GESAMT	

FB 04	BALKON STAHLKONSTR. THERMISCH ENTKOPPELT
2,50 cm	Holzbelag, rutsch- und witterungsfest
9,00 cm	Stellfüße Höhenausgleich 40-90 mm
0,80 cm	Gummigranulatplatte mit Trittschallfunktion
0,50 cm	Bituminöse Abdichtung 2-lagig, erste Lage selbstklebend
0,50 cm	Stahlblech lt. Statik, OK im Gefälle 2%
18,00 cm	Konstruktion aus Stahlträgern lt. Statik, Untersicht verkleidet mit MAX Exterior
31,30 cm	BAUTEIL GESAMT

FB 05	FUSSBODEN GEGEN ERDREICH (HOFTRAKT)
1,50 cm	Bodenbelag (Parkett / Fliese)
7,00 cm	Zementestrich mit FBH, inkl. Randdämmstreifen 1cm PE-Folie seitlich hochgezogen bis Estrich OK
3,00 cm	Trittschalldämmplatten lt. Bauphysik Dampfbremse
6,00 cm	EPS - Schüttung zementgebunden PE-Folie
8,00 cm	EPS - Platten
1,00 cm	Bituminöse Bauwerksabdichtung
20,00 cm	Stahlbetondecke
10,00 cm	Unterbau / Rollierung
56,50 cm	BAUTEIL GESAMT

FB 06 a/b	FUSSBODEN GEGEN ERDREICH (HOFTRAKT)
1,50 cm	Bodenbelag (Parkett / Fliese)
7,00 cm	Zementestrich mit FBH, inkl. Randdämmstreifen 1cm PE-Folie seitlich hochgezogen bis Estrich OK
3,00 cm	Trittschalldämmplatten lt. Bauphysik Dampfbremse
4,0 / 14,0 cm	EPS - Schüttung zementgebunden
1,00 cm	Bituminöse Bauwerksabdichtung
15,00 cm	Stahlbetondecke
10,00 cm	Perimeterdämmung XPS
10,00 cm	Unterbau / Rollierung
51,5 / 61,5 cm	BAUTEIL GESAMT

FB 07 a	ZIEGELDECKE ÜBER EG (HOFTRAKT)	REI 60
1,50 cm	Bodenbelag (Parkett / Fliese)	
7,00 cm	Zementestrich mit FBH, inkl. Randdämmstreifen 1cm PE-Folie seitlich hochgezogen bis Estrich OK	
3,00 cm	Trittschalldämmplatten lt. Bauphysik	
3,50 cm	EPS - Schüttung zementgebunden	
25,00 cm	Bestehende Ziegeleinhängdecke (REI60)	
2,50 cm	Luftraum (Abstand)	
5,00 cm	UK lt. Erfordernis dazw. Mineralwolle	
1,25 cm	1 x 1,25 cm GKB-Platte (GKBi in Nassräumen)	
48,75 cm	BAUTEIL GESAMT	

FB 07 b	KAPPENDECKE ÜBER EG (HOFTRAKT)	REI 60
1,50 cm	Bodenbelag (Parkett / Fliese)	
7,00 cm	Zementestrich mit FBH, inkl. Randdämmstreifen 1cm PE-Folie seitlich hochgezogen bis Estrich OK	
3,00 cm	Trittschalldämmplatten lt. Bauphysik Dampfbremse	
3,50 cm	EPS - Schüttung zementgebunden	
28,00 cm	Kappendecke BESTAND mit Aufbeton / Schüttung Stahlträger brandschutztechn. verkleidet (Promat) (REI60)	
2,50 cm	Luftraum (Abstand)	
5,00 cm	UK lt. Erfordernis dazw. Mineralwolle	
1,25 cm	1 x 1,25 cm GKB-Platte (GKBi in Nassräumen)	
51,75 cm	BAUTEIL GESAMT	

DA 01	HAUPTDACH ZIEGELDECKUNG	REI
3,00 cm	Keramischer Dachziegel	
3,00 cm	Lattung 30/50 mm	
5,00 cm	Konterlattung 50/50 mit Nageldichtband - Hinterlüftung	
0,20 cm	Diffussionsoffene Dachauflegebahn - erhöhte Regensicherheit, sd- Wert lt. Bauphysik	
2,40 cm	Vollholzschalung	
24,00 cm	Holzsparren lt. Statik dazw. Mineralwolle lt. Bauphysik	
3,00 cm	UK / Lattung dazw. Mineralwolle lt. Bauphysik	
0,10 cm	Feuchteadaptive Dampfbremse allseits verklebt lt. Bauphy	
1,50 cm	1x 1,50 cm GKF-Platte (EI30)	
48,45 cm	BAUTEIL GESAMT	

DA 02	DACH GAUBE BLECHDECKUNG	REI
0,80 cm	Zinkblech auf Strukturmatte	
2,40 cm	Vollholzschalung	
8,00 cm	Konterlattung 50/80 mit Nageldichtband - Hinterlüftung	
0,20 cm	Diffussionsoffene Dachauflegebahn - erhöhte Regensicherheit, sd- Wert lt. Bauphysik	
2,40 cm	Vollholzschalung	
24,00 cm	Holzsparren lt. Statik dazw. Mineralwolle lt. Bauphysik	
3,00 cm	UK / Lattung dazw. Mineralwolle lt. Bauphysik	
0,10 cm	Feuchteadaptive Dampfbremse allseits verklebt lt. Bauphy	
1,50 cm	1 x 1,50 cm GKF-Platte (EI30)	
5,00 cm	UK / Lattung dazw. Mineralwolle - Installationsebene	
1,25 cm	1 x 1,25 cm GKB-Platte (GKBi in Nassräumen)	
48,65 cm	BAUTEIL GESAMT	

DA 03	WARMDACH 1.OG HOFTRAKT	R
6,00 cm	Kies	
1,00 cm	2 lagige bituminöse Abdichtung erste Lage selbstklebend	
17,00 cm	Gefälledämmung 12 - 22cm (17cm im Mittel)	
20,00 cm	Grunddämmung EPS	
0,50 cm	Dampfsperre	
23,00 cm	Bestehende Ziegeleinhängdecke	
2,00 cm	Bestehender Innenputz	
2,50 cm	Luftraum (Abstand)	
5,00 cm	UK lt. Erfordernis dazw. Mineralwolle	
1,25 cm	1 x 1,25 GKB-Platte (GKBi in Nassräumen)	
78,25 cm	BAUTEIL GESAMT	

DA 04 a	FLACHDACH / KIES (HOFTRAKT)	R
5,00 cm	Bekiesung, im Traufenbereich verfestigt	
0,10 cm	diffusionsoffene, wasserableitende Trennlage	
0,80 cm	Granulatmatte als Schutzschicht	
1,00 cm	Bituminöse Flachdachabdichtung 2-lagig samt Höchzüge, Erste Lage selbstklebend	
12,00 cm	Gefälledämmung im Mittel 12cm lt. Bauphysik	
14,00 cm	Grunddämmung EPS lt. Bauphysik	
0,50 cm	Dampfsperre bituminös, alukaschiert, sd Wert lt. Bauphysi Überlappend und verklebt	
28,00 cm	Kappendecke BESTAND mit Aufbeton / Schüttung Stahlträger brandschutztechn. verkleidet (Promat) (REI30)	
2,50 cm	Luftraum (Abstand)	
5,00 cm	UK lt. Erfordernis dazw. Mineralwolle	
1,25 cm	1 x 1,25 GKB-Platte (GKBi in Nassräumen)	
70,15 cm	BAUTEIL GESAMT	

DA 04 b	FLACHDACH / DACHTERRASSE (HOFTRAKT)	R
2,00 cm	Holzbelag, rutsch- und witterungsfest	
8,00 cm	Alukonstruktion auf Stelzlager	
0,80 cm	Granulatmatte als Schutzschicht	
1,00 cm	Bituminöse Flachdachabdichtung 2-lagig samt Höchzüge, Erste Lage selbstklebend	
12,00 cm	Gefälledämmung im Mittel 12cm lt. Bauphysik	
14,00 cm	Grunddämmung EPS lt. Bauphysik	
0,50 cm	Dampfsperre bituminös, alukaschiert, sd Wert lt. Bauphysi Überlappend und verklebt	
28,00 cm	Kappendecke BESTAND mit Aufbeton / Schüttung Stahlträger brandschutztechn. verkleidet (Promat) (REI30)	
2,50 cm	Luftraum (Abstand)	
5,00 cm	UK lt. Erfordernis dazw. Mineralwolle	
1,25 cm	1 x 1,25 GKB-Platte (GKBi in Nassräumen)	
75,05 cm	BAUTEIL GESAMT	

LEGENDE

☒	Wanddurchbruch
⬚	Deckendurchbruch
◺	Bodenschlitz
◢	Bodendurchbruch
▼	OK Fertigbau
▲	UK Fertigbau
▽	OK Rohbau
△	UK Rohbau
± 0,00	Höhenangabe einer waagrechten Fläche
±0,00	Höhenangabe eines Punktes in einem Bauwerk - Fertigmaß
±0,00	Höhenangabe eines Punktes in einem Bauwerk - Rohbaumaß
BGF	Bruttogesamtfläche
HNF / NNF	Haupt- Nebennutzfläche

▨	Mauerwerk (wärmedämmend)
▨	Mauerwerk (nicht wärmedämmend)
▨	unbewehrter Beton
▨	bewehrter Beton
▦	Betonfertigteil
▤	Stein
▨	Stahl (allgemein)
▨	Holz (allgemein)
▨	Holzwerkstoffe
▩	Dämmstoff (hart)
▩	Dämmstoff (weich)
▩	Kunststoff (allgemein)
▚	Dichtstoff (allgemein)
▥	Gips (Gipskartonplatte)
▥	Gipskartonplatte Brandschutz
☐	Erdmaterial (allgemein)
■	Bestand
🟨	Abbruch
🟥	Neubau

—	Medien
—	Fernwärme
—	Gas
—	Strom
—	Heizung
—	Regenwasser
—	Schmutzwasser
—	Wasser
—	Blech
- - -	Abdichtung
- - -	Folie
– – –	Dampfsperre, -bremse

Höhenbezugs- und Maßangaben

DOK	Deckenoberkante
DOS	Deckenoberseite
DUK	Deckenunterkante
DUS	Deckenunterseite
DUF	Deckenunterkante (fertige Untersicht)
FBOK	Fußbodenoberkante
OFF	Oberfläche des fertigen Fußbodens
FDOK	Fundamentoberkante
FDOS	Fundamentoberseite
FDUK	Fundamentunterkante
FDUS	Fundamentunterseite
RH	lichte Raumhöhe
GH	Geschoßhöhe
OK	Oberkante
OS	Oberseite
UK	Unterkante
US	Unterseite
STUK	Sturzunterkante (Rohbaumaß)
STH	Sturzhöhe gemessen von STUK bis DUK (Rohbaumaß)
RPH	Rohbauparapethöhe
FPH	fertige Parapethöhe (FBOK bis OK Fensterbank Innen)

Rauch-, Abgas- und Luftfänge, Schächte

L	Lüftungsschacht
PT	Putztürchen
PS	Putzstück
KT	Kehrtürchen
ABL	Abluft
ZUL	Zuluft
DBA	Druckbelüftungsanlage
DES	Druckentlastungsschacht
BÖ	Belüftungsöffnung
ÜÖ	Überströmöffnung
AÖ	Abströmöffnung mit Überdruckentlastungsorgan
BSK	Brandsschutzklappe
FBHV	Fussbodenheizungsverteiler
E-Verteiler	Elektroverteiler

Öffnungen und deren Abschlüsse

WD	Wanddurchbruch
DD	Deckendurchbruch
FBD	Fußbodendurchbruch
FDD	Fundamentdurchbruch
WS	Wandschlitz
WA	Wandaussparung
DA	Deckenaussparung
FBA	Fußbodenaussparung
RBL	Rohbaulichte
AL	Architekturlichte
STL	Stocklichte
GL	Glaslichte
STAM	Stockaußenmaß
DL	Durchgangslichte
GGT	Ganzglastüre
MGT	Metallgittertür
HT	Hebetüre
HST	Hebeschiebetüre
T	Türe
AT	Allgemeintüre
ET	Eingangstüre
WET	Wohnungseingangstür
IT	Innentür
DF	Drehflügel
DKF	Drehkippflügel
SF	Schiebe-Fenster
SWF	Schwingflügel
WF	Wendeflügel
K	Kippfenster
OL	Oberlichte
DF	Dachfächenfenster
PFR	Pfostenriegelkonstruktion
FE	Fenster
FT	Fenstertüre
R	Rechtsöffnend
L	Linksöffnend
FIX	Fixverglasung
VSG	Verbund-Sicherheitsglas
ESG	Einscheiben-Sicherheitsglas

Drehflügel
Drehkippflügel
Kippflügel
Fenstertüre

EI2 30-C-, EI2 60-C-und EI2 90-C
Feuerschutztüren mit Angabe der Feuerwiderstandsklasse
(gemäß ÖNORM B 3850 und ÖNORM B 3807)

GT	gasdichte Türe
DT	Drucktüre
S 200	Rauchabschluss
S 200	Rauchabschluss
C	Selbstschließend
FLS	Freilaufschließer
LVfTÖ	Lehrverrohrung für Türöffner
elTÖ	elektrischer Türöffner

AUSFÜHRUNG POLIERPLAN GESAMT

Bauvorhaben
PFAR02
2512 Traiskirchen, Tribuswinkel Pfarrgasse 2-4

XXX

Katastralgemeinde 04034 Tribuswinkel
EZ: 51
GstNr.: .19

Diese Zeichnung bzw. Ausarbeitung sowie deren Daten auf Datenträgern sind geistiges Eigentum des Erstellers Arch. Artmüller Georg. Jede Benützung, Veröffentlichung,Vervielfältigung jeglicher Art oder Weitergabe an Dritte bedarf der schriftlichen Zustimmung durch Architekt Artmüller.

Durch die Übernahme dieses Planes akzeptiert die ausführende Firma bzw. Person die darauf dargestellten Anordnungen. Geschriebene Planmaße auf dieser Zeichnunghaben Vorrang gegenüber gezeichneten Dimensionen. Der Auftragnehmer verpflichtet sich **vor** Arbeitsbeginn alle Maße und Bedingungen im Zusammenhang mit seinerArbeit auf der Baustelle verantwortlich zu überprüfen.

Abweichungen gegenüber dargestellten oder schriftlich vereinbarten Anordnungen müssen Architekt Artmüller und der Bauleitung unverzüglich schriftlich mitgeteiltwerden. Vor Arbeitsbeginn sind dem Architekten gültige Werkzeichnungen zur Genehmigung vorzulegen.

NATURMASSE SIND ZU NEHMEN, KOTEN ZU PRÜFEN

VORABZUG
28. 09. 2026

Index	Datum	Bearbeiter	Änderung

Die Plän sind derzeit unter Bearbeitung, aufgrund diverser Erkenntisse durch Bauteilöffnungen. Es handelt sich dementsprechend um einen Arbeitsstand und dient lediglich der Vorab- Information! Kein offizieller Planstand!

Index	Änderung	Datum

Grundeigentümer

Bauwerber / Auftraggeber

ARTMÜLLER ARCHITEKTEN
ZIVILTECHNIKER GMBH
Stolberggasse 34|26 A-1050 Wien
t [+43] 01 . 581 40 83 f [+43] 01. 581 40 83 99 office@artmueller.eu

Planinhalt
SCHNITTE

Maßstab	Gez	Datum	Plannr.	Index
1:50			PFAR02_50_05	

Erstellt, am 11.11.2026

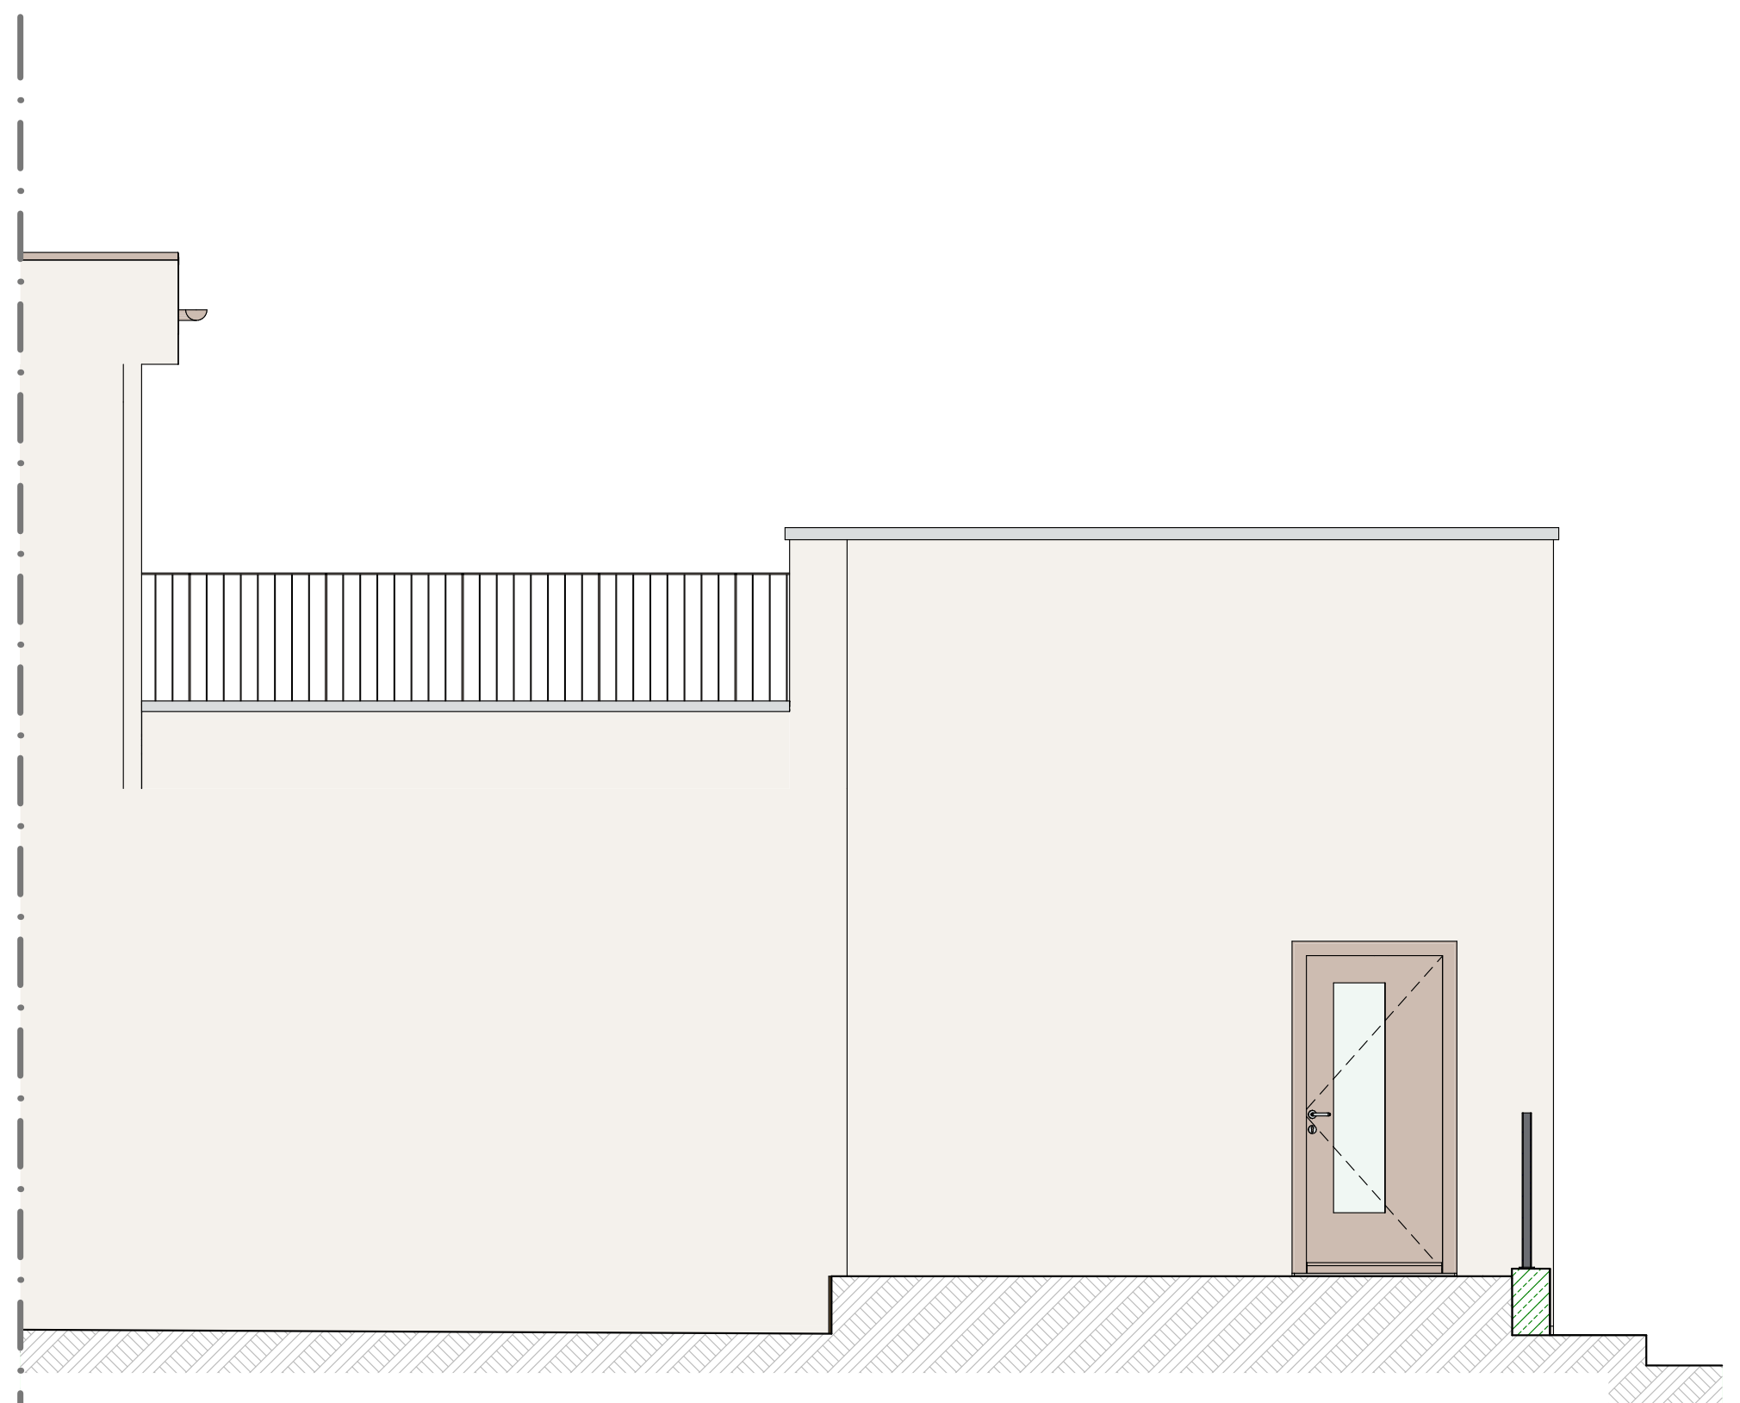

ANSICHT HOFTRAKT NORD M 1:50

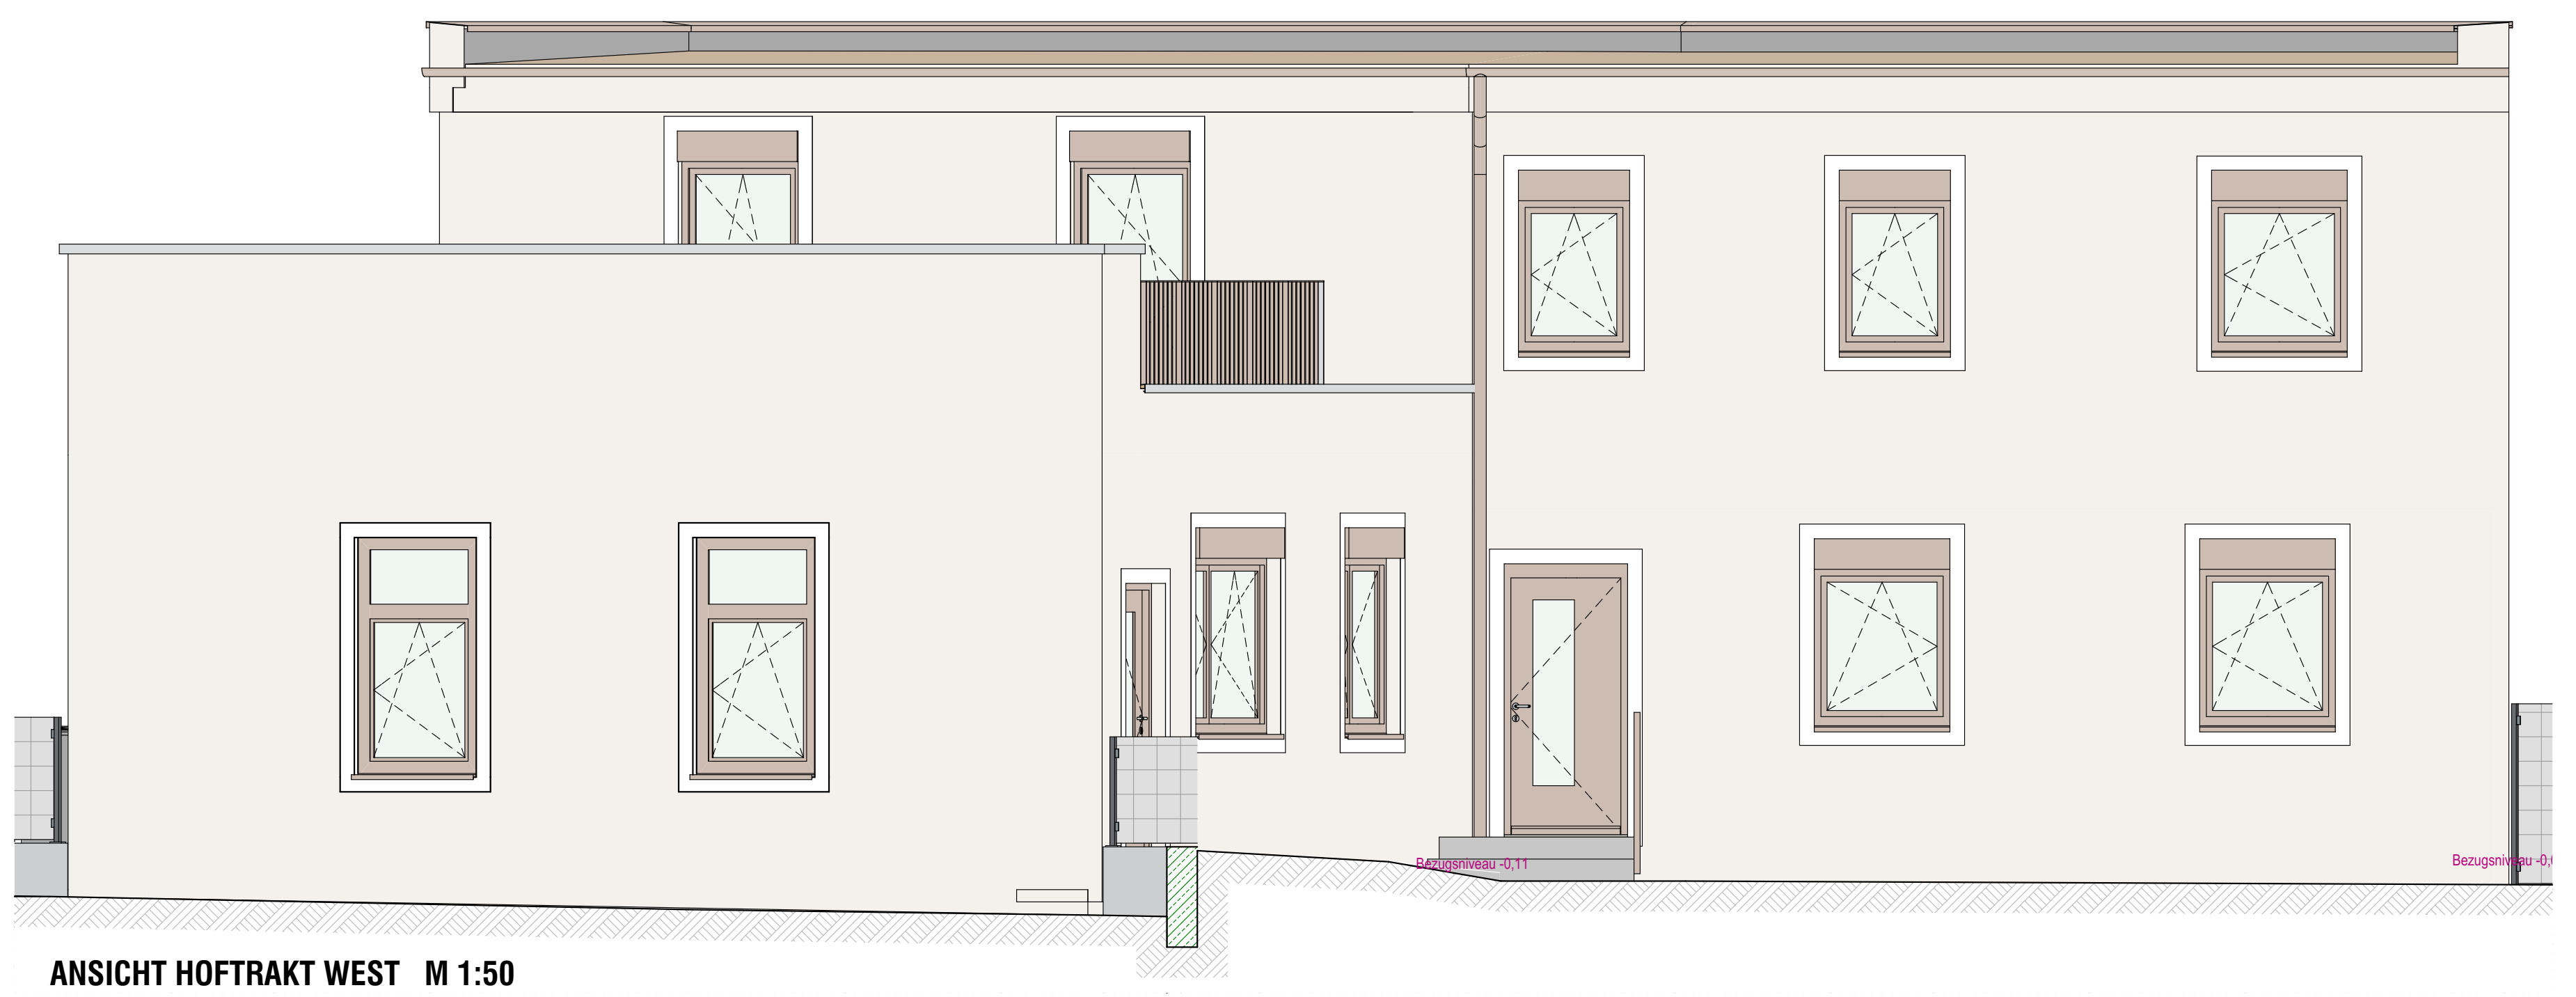

ANSICHT HOFTRAKT WEST M 1:50

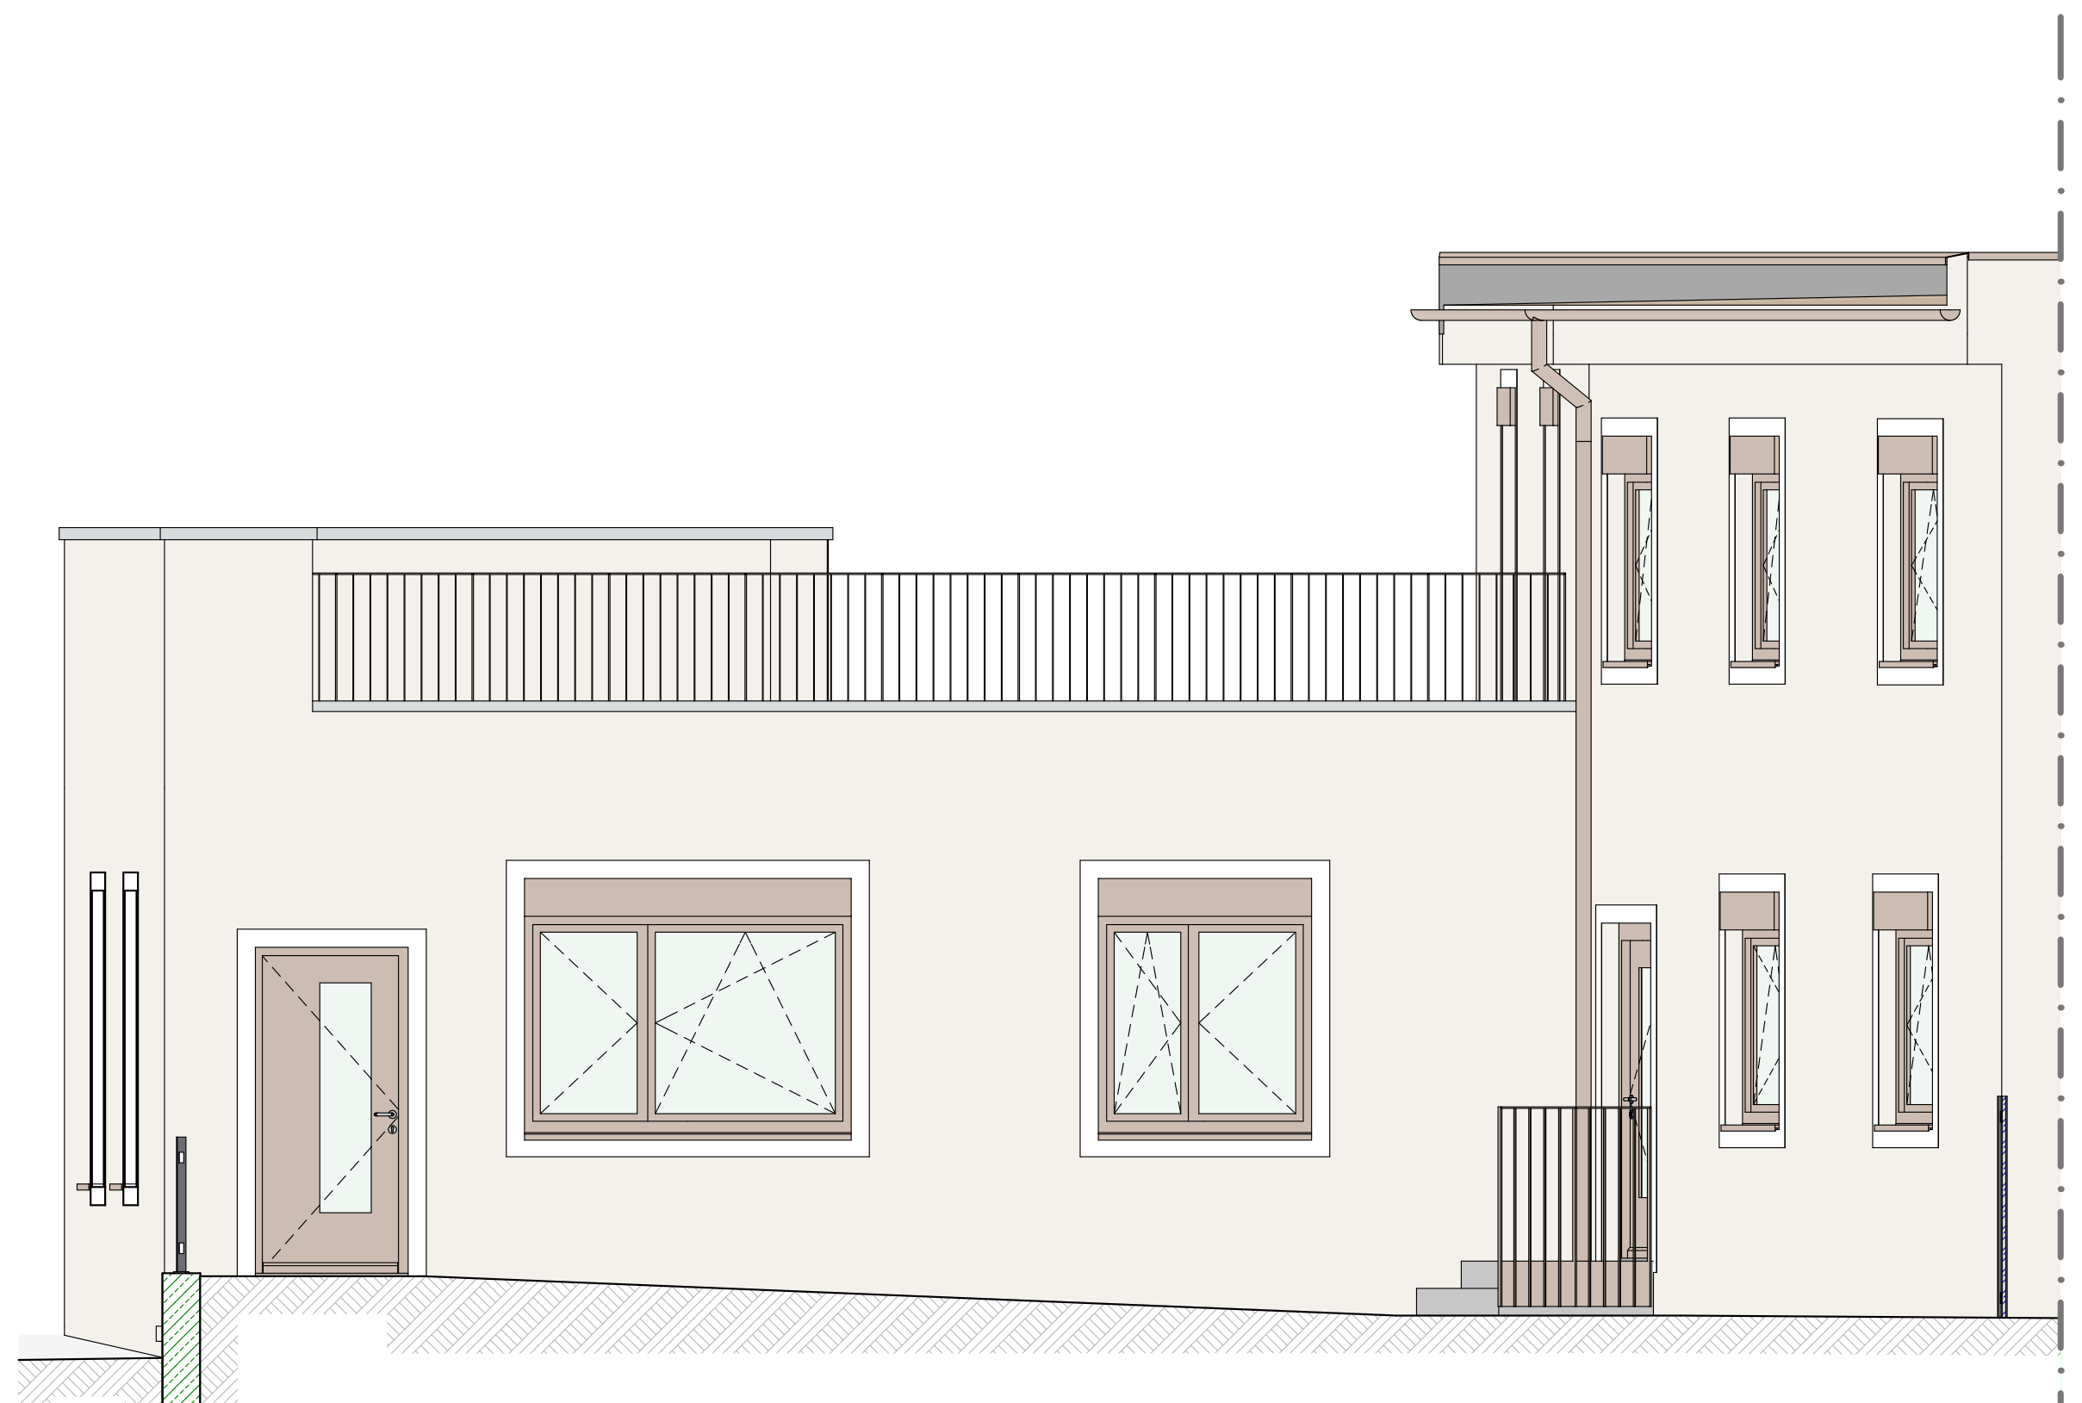

ANSICHT HOFTRAKT SÜD M 1:50

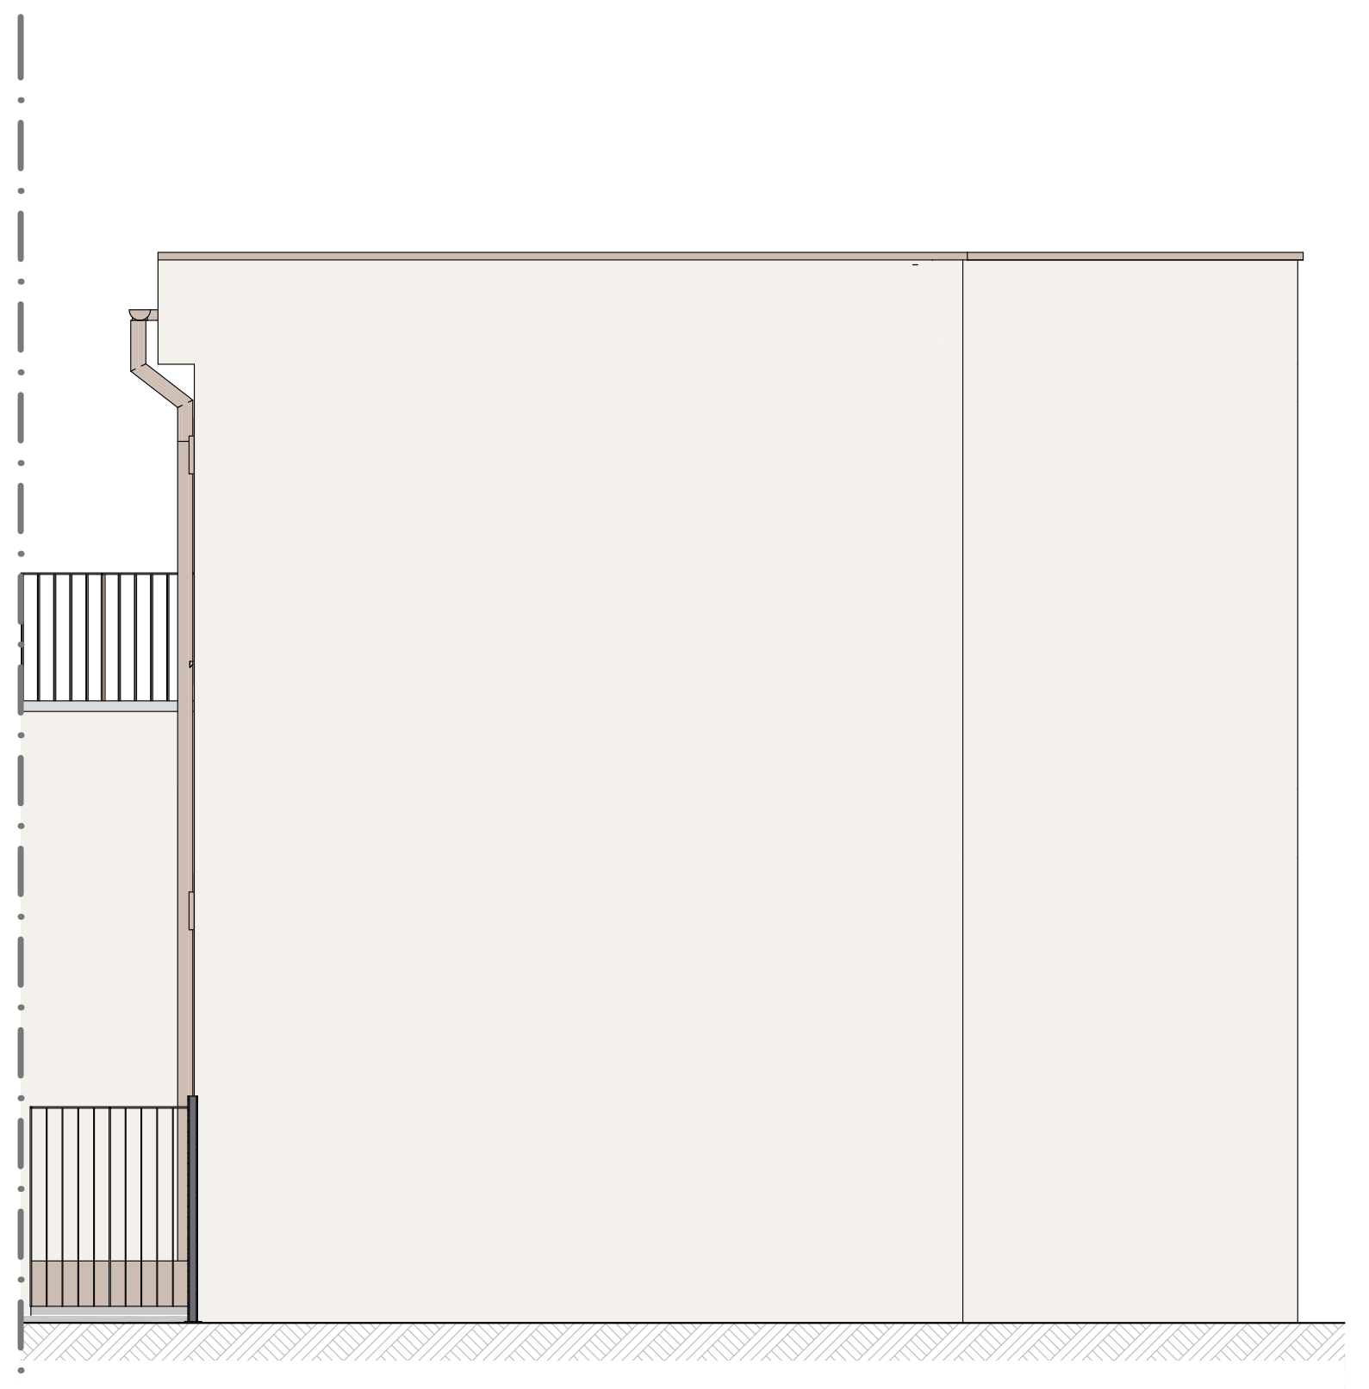

ANSICHT HOFTRAKT SÜD M 1:50

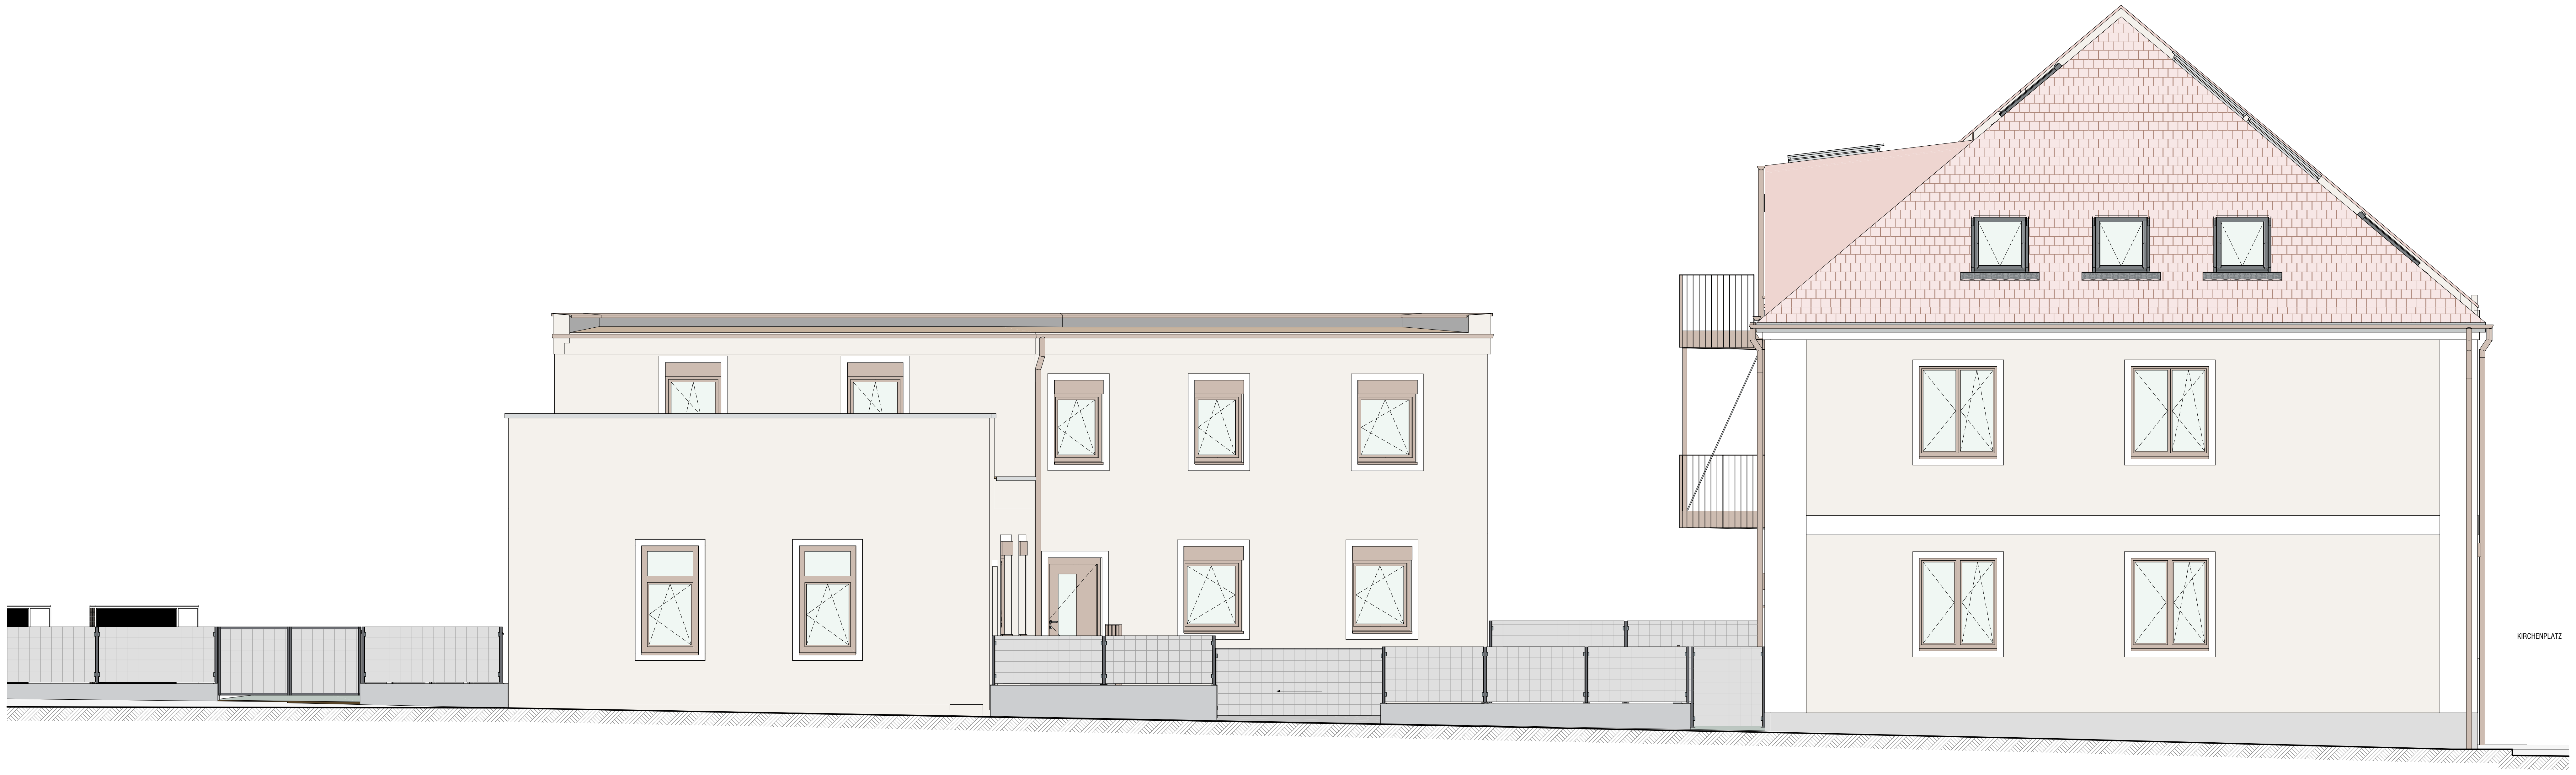

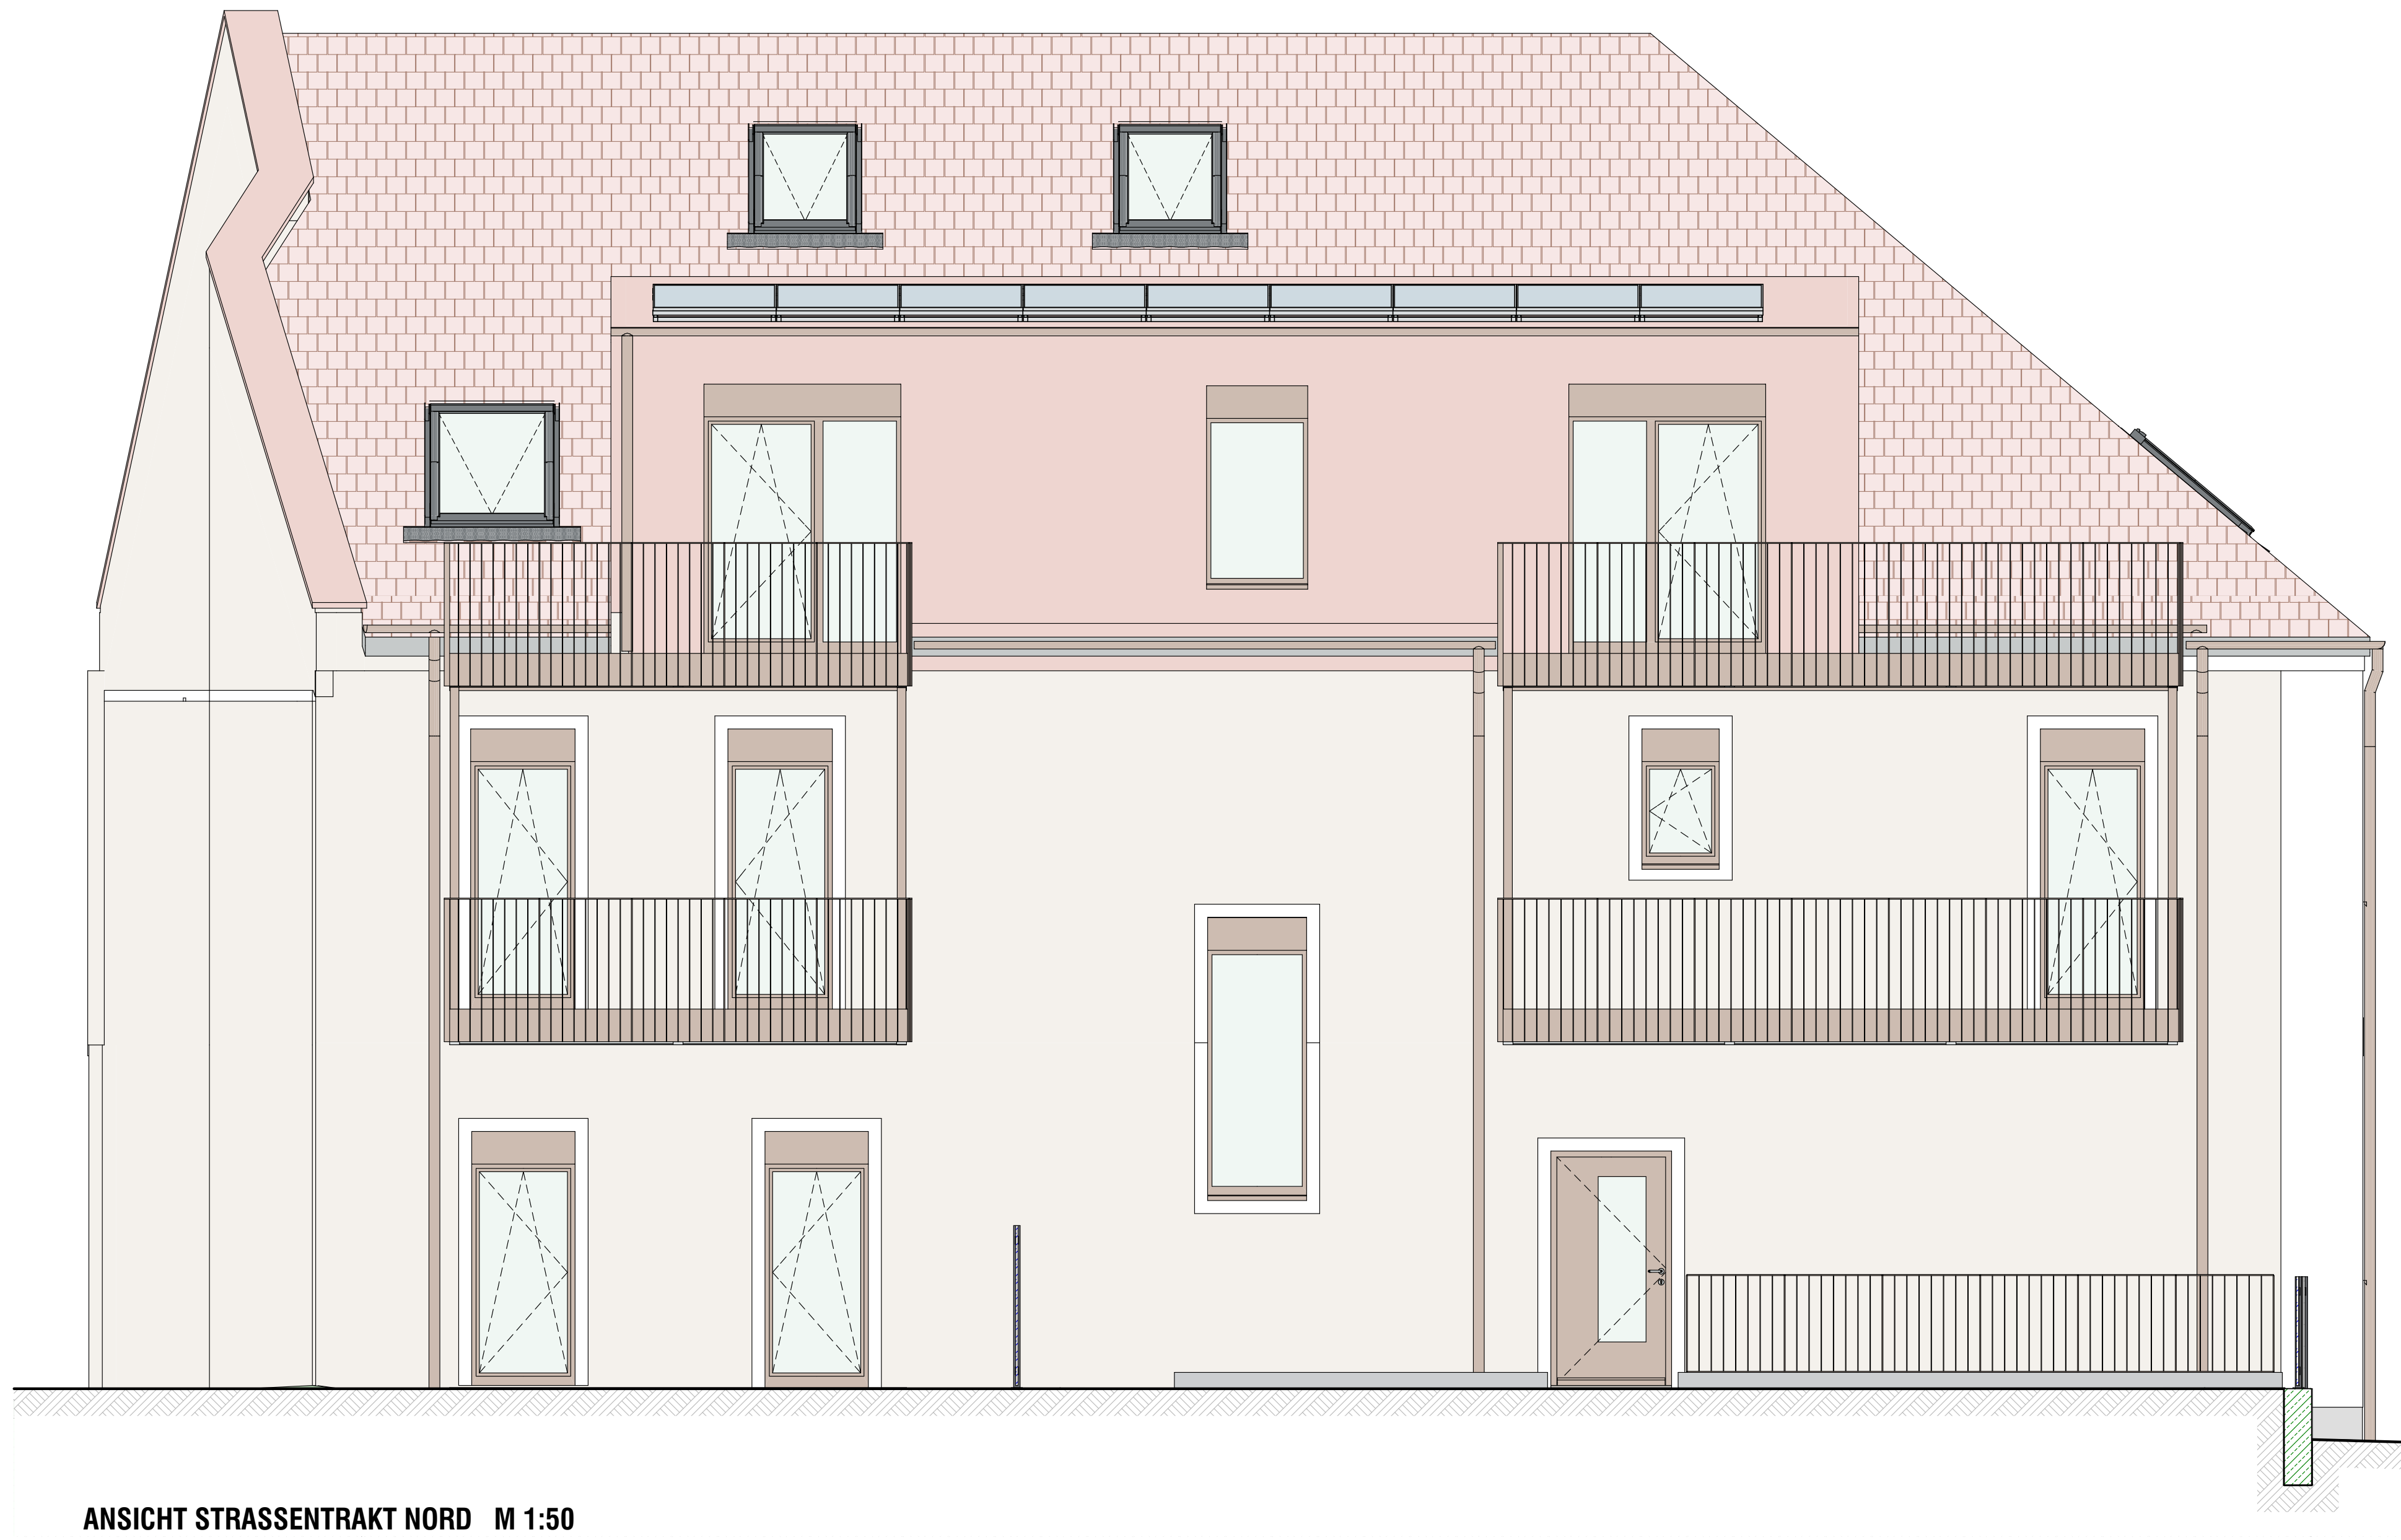

ANSICHT STRASSENTRAKT NORD M 1:50

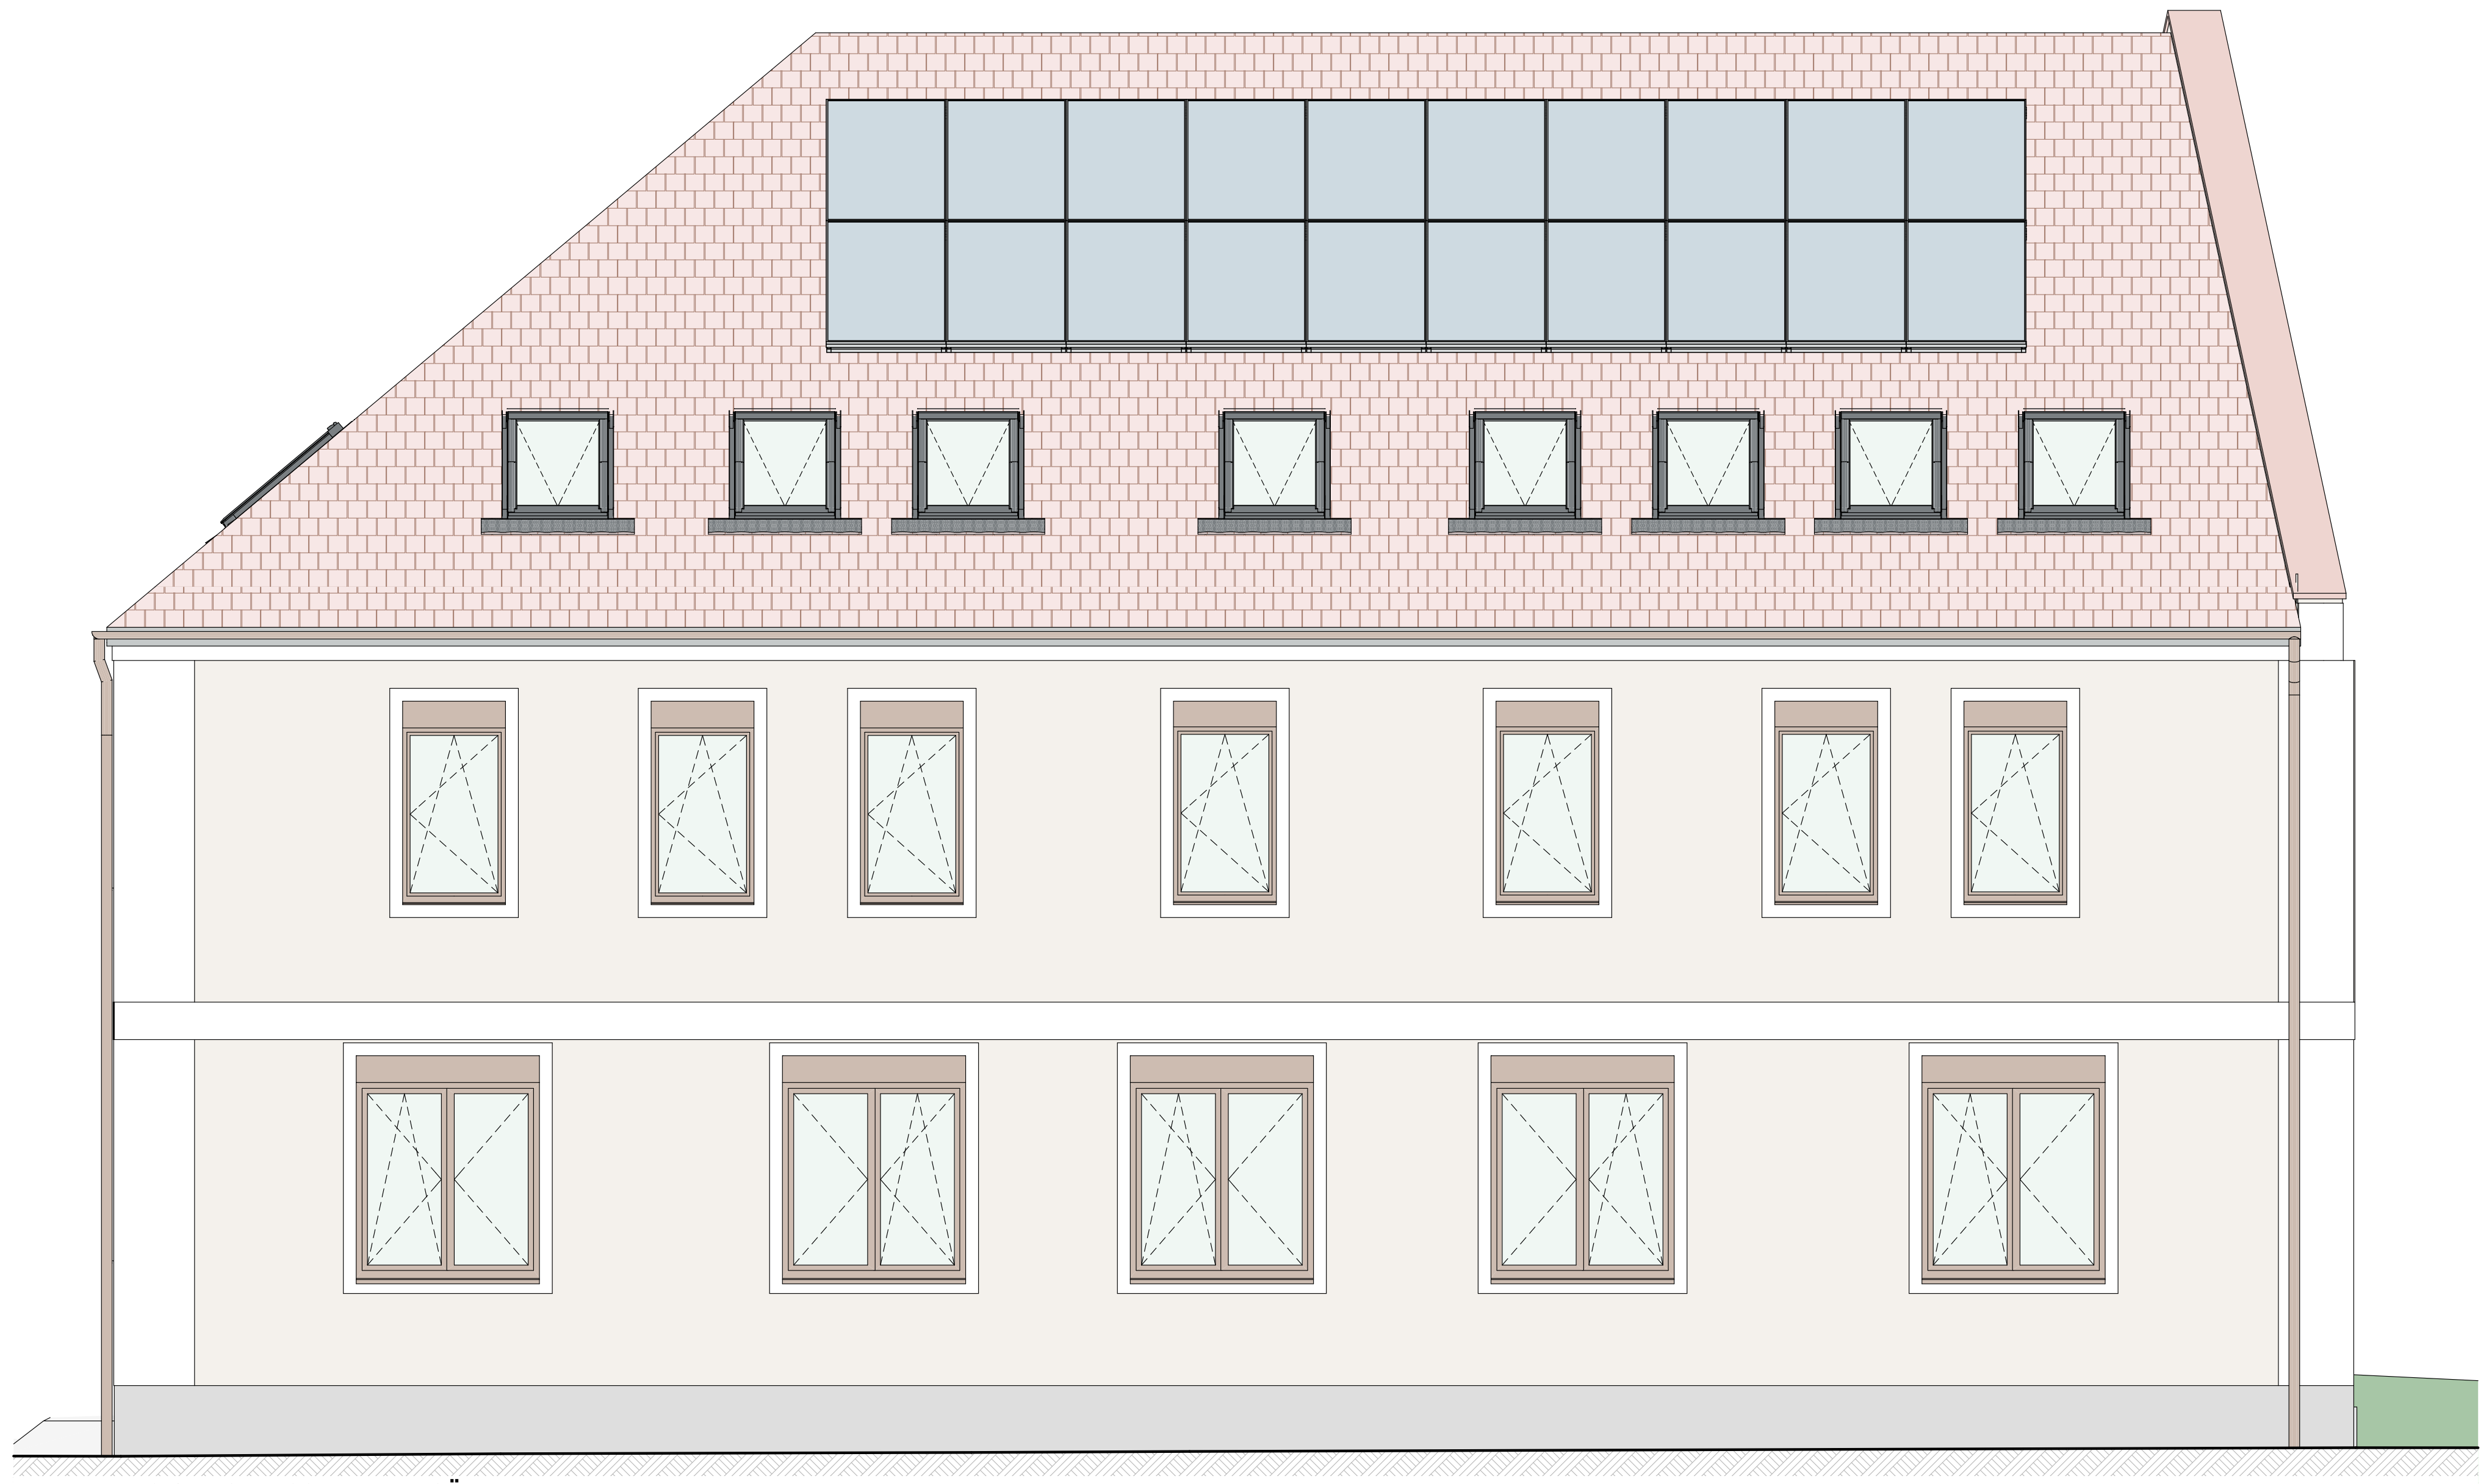

ANSICHT STRASSENTRAKT SÜD M 1:50

LEGENDE

- ☒ Wanddurchbruch
- ☐ Deckendurchbruch
- ☐ Bodenschlitz
- ◣ Bodendurchbruch
- ▼ OK Fertigbau
- ▲ UK Fertigbau
- ▽ OK Rohbau
- △ UK Rohbau
- ± 0,00 Höhenangabe einer waagrechten Fläche
- ±0,00 Höhenangabe eines Punktes in einem Bauwerk - Fertigmaß
- ±0,00 Höhenangabe eines Punktes in einem Bauwerk - Rohbaumaß

BGF	Bruttogesamtfläche
HNF / NNF	Haupt- Nebennutzfläche

- ▨ Mauerwerk (wärmedämmend)
- ▨ Mauerwerk (nicht wärmedämmend)
- ▨ unbewehrter Beton
- ▨ bewehrter Beton
- ▦ Betonfertigteil
- ▨ Stein
- ▨ Stahl (allgemein)
- ▨ Holz (allgemein)
- ▨ Holzwerkstoffe
- ▨ Dämmstoff (hart)
- ▨ Dämmstoff (weich)
- ▨ Kunststoff (allgemein)
- ▨ Dichtstoff (allgemein)
- ▨ Gips (Gipskartonplatte)
- ▨ Gipskartonplatte Brandschutz
- ☐ Erdmaterial (allgemein)
- ⬛ Bestand
- 🟨 Abbruch
- 🟥 Neubau

- — Medien
- — Fernwärme
- — Gas
- — Strom
- — Heizung
- — Regenwasser
- — Schmutzwasser
- — Wasser
- — Blech
- - - Abdichtung
- - - Folie
- - - Dampfsperre, -bremse

Höhenbezugs- und Maßangaben

DOK	Deckenoberkante
DOS	Deckenoberseite
DUK	Deckenunterkante
DUS	Deckenunterseite
DUF	Deckenunterkante (fertige Untersicht)
FBOK	Fußbodenoberkante
OFF	Oberfläche des fertigen Fußbodens
FDOK	Fundamentoberkante
FDOS	Fundamentoberseite
FDUK	Fundamentunterkante
FDUS	Fundamentunterseite
RH	lichte Raumhöhe
GH	Geschoßhöhe
OK	Oberkante
OS	Oberseite
UK	Unterkante
US	Unterseite
STUK	Sturzunterkante (Rohbaumaß)
STH	Sturzhöhe gemessen von STUK bis DUK (Rohbaumaß)
RPH	Rohbauparapethöhe
FPH	fertige Parapethöhe (FBOK bis OK Fensterbank Innen)

Rauch-, Abgas- und Luftfänge, Schächte

L	Lüftungsschacht
PT	Putztürchen
PS	Putzstück
KT	Kehrtürchen
ABL	Abluft
ZUL	Zuluft
DBA	Druckbelüftungsanlage
DES	Druckentlastungsschacht
BÖ	Belüftungsöffnung
ÜÖ	Überströmöffnung
AÖ	Abströmöffnung mit Überdruckentlastungsorgan
BSK	Brandsschutzklappe
FBHV	Fussbodenheizungsverteiler
E-Verteiler	Elektroverteiler

Öffnungen und deren Abschlüsse

WD	Wanddurchbruch
DD	Deckendurchbruch
FBD	Fußbodendurchbruch
FDD	Fundamentdurchbruch
WS	Wandschlitz
WA	Wandaussparung
DA	Deckenaussparung
FBA	Fußbodenaussparung
RBL	Rohbaulichte
AL	Architekturlichte
STL	Stocklichte
GL	Glaslichte
STAM	Stockaußenmaß
DL	Durchgangslichte
GGT	Ganzglastüre
MGT	Metallgittertür
HT	Hebetüre
HST	Hebeschiebetüre
T	Türe
AT	Allgemeintüre
ET	Eingangstüre
WET	Wohnungseingangstür
IT	Innentür
DF	Drehflügel
DKF	Drehkippflügel
SF	Schiebe-Fenster
SWF	Schwingflügel
WF	Wendeflügel
K	Kippfenster
OL	Oberlichte
DF	Dachfächenfenster
PFR	Pfostenriegelkonstruktion
FE	Fenster
FT	Fenstertüre
R	Rechtsöffnend
L	Linksöffnend
FIX	Fixverglasung
VSG	Verbund-Sicherheitsglas
ESG	Einscheiben-Sicherheitsglas

- Drehflügel
- Drehkippflügel
- Kippflügel
- Fenstertüre

EI2 30-C-, EI2 60-C-und EI2 90-C
Feuerschutztüren mit Angabe der Feuerwiderstandsklasse
(gemäß ÖNORM B 3850 und ÖNORM B 3807)

GT	gasdichte Türe
DT	Drucktüre
S 200	Rauchabschluss
S 200	Rauchabschluss
C	Selbstschließend
FLS	Freilaufschließer
LVfTÖ	Lehrverrohrung für Türöffner
elTÖ	elektrischer Türöffner

AUSFÜHRUNG POLIERPLAN GESAMT

Bauvorhaben
PFAR02
2512 Traiskirchen, Tribuswinkel Pfarrgasse 2-4

XXX

Katastralgemeinde 04034 Tribuswinkel
EZ: 51
GstNr.: .19

Diese Zeichnung bzw. Ausarbeitung sowie deren Daten auf Datenträgern sind geistiges Eigentum des Erstellers Arch. Artmüller Georg. Jede Benützung, Veröffentlichung,Vervielfältigung jeglicher Art oder Weitergabe an Dritte bedarf der schriftlichen Zustimmung durch Architekt Artmüller.

Durch die Übernahme dieses Planes akzeptiert die ausführende Firma bzw. Person die darauf dargestellten Anordnungen. Geschriebene Planmaße auf dieser Zeichnunghaben Vorrang gegenüber gezeichneten Dimensionen. Der Auftragnehmer verpflichtet sich **vor** Arbeitsbeginn alle Maße und Bedingungen im Zusammenhang mit seinerArbeit auf der Baustelle verantwortlich zu überprüfen.

Abweichungen gegenüber dargestellten oder schriftlich vereinbarten Anordnungen müssen Architekt Artmüller und der Bauleitung unverzüglich schriftlich mitgeteiltwerden. Vor Arbeitsbeginn sind dem Architekten gültige Werkzeichnungen zur Genehmigung vorzulegen.

NATURMASSE SIND ZU NEHMEN, KOTEN ZU PRÜFEN

VORABZUG
28. 09. 2026

Index	Datum	Bearbeiter	Änderung

Die Plän sind derzeit unter Bearbeitung, aufgrund diverser Erkenntisse durch Bauteilöffnungen. Es handelt sich dementsprechend um einen Arbeitsstand und dient lediglich der Vorab- Information! Kein offizieller Planstand!

Index	Änderung	Datum

Grundeigentümer

Bauwerber / Auftraggeber

ARTMÜLLER ARCHITEKTEN
ZIVILTECHNIKER GMBH
Stolberggasse 34|26 A-1050 Wien
t [+43] 01 . 581 40 83 f [+43] 01. 581 40 83 99 office@artmueller.eu

Planinhalt
ANSICHTEN

Maßstab	Gez	Datum	Plannr.	Index
1:50			PFAR02_50_06	

Erstellt, am 11.11.2026