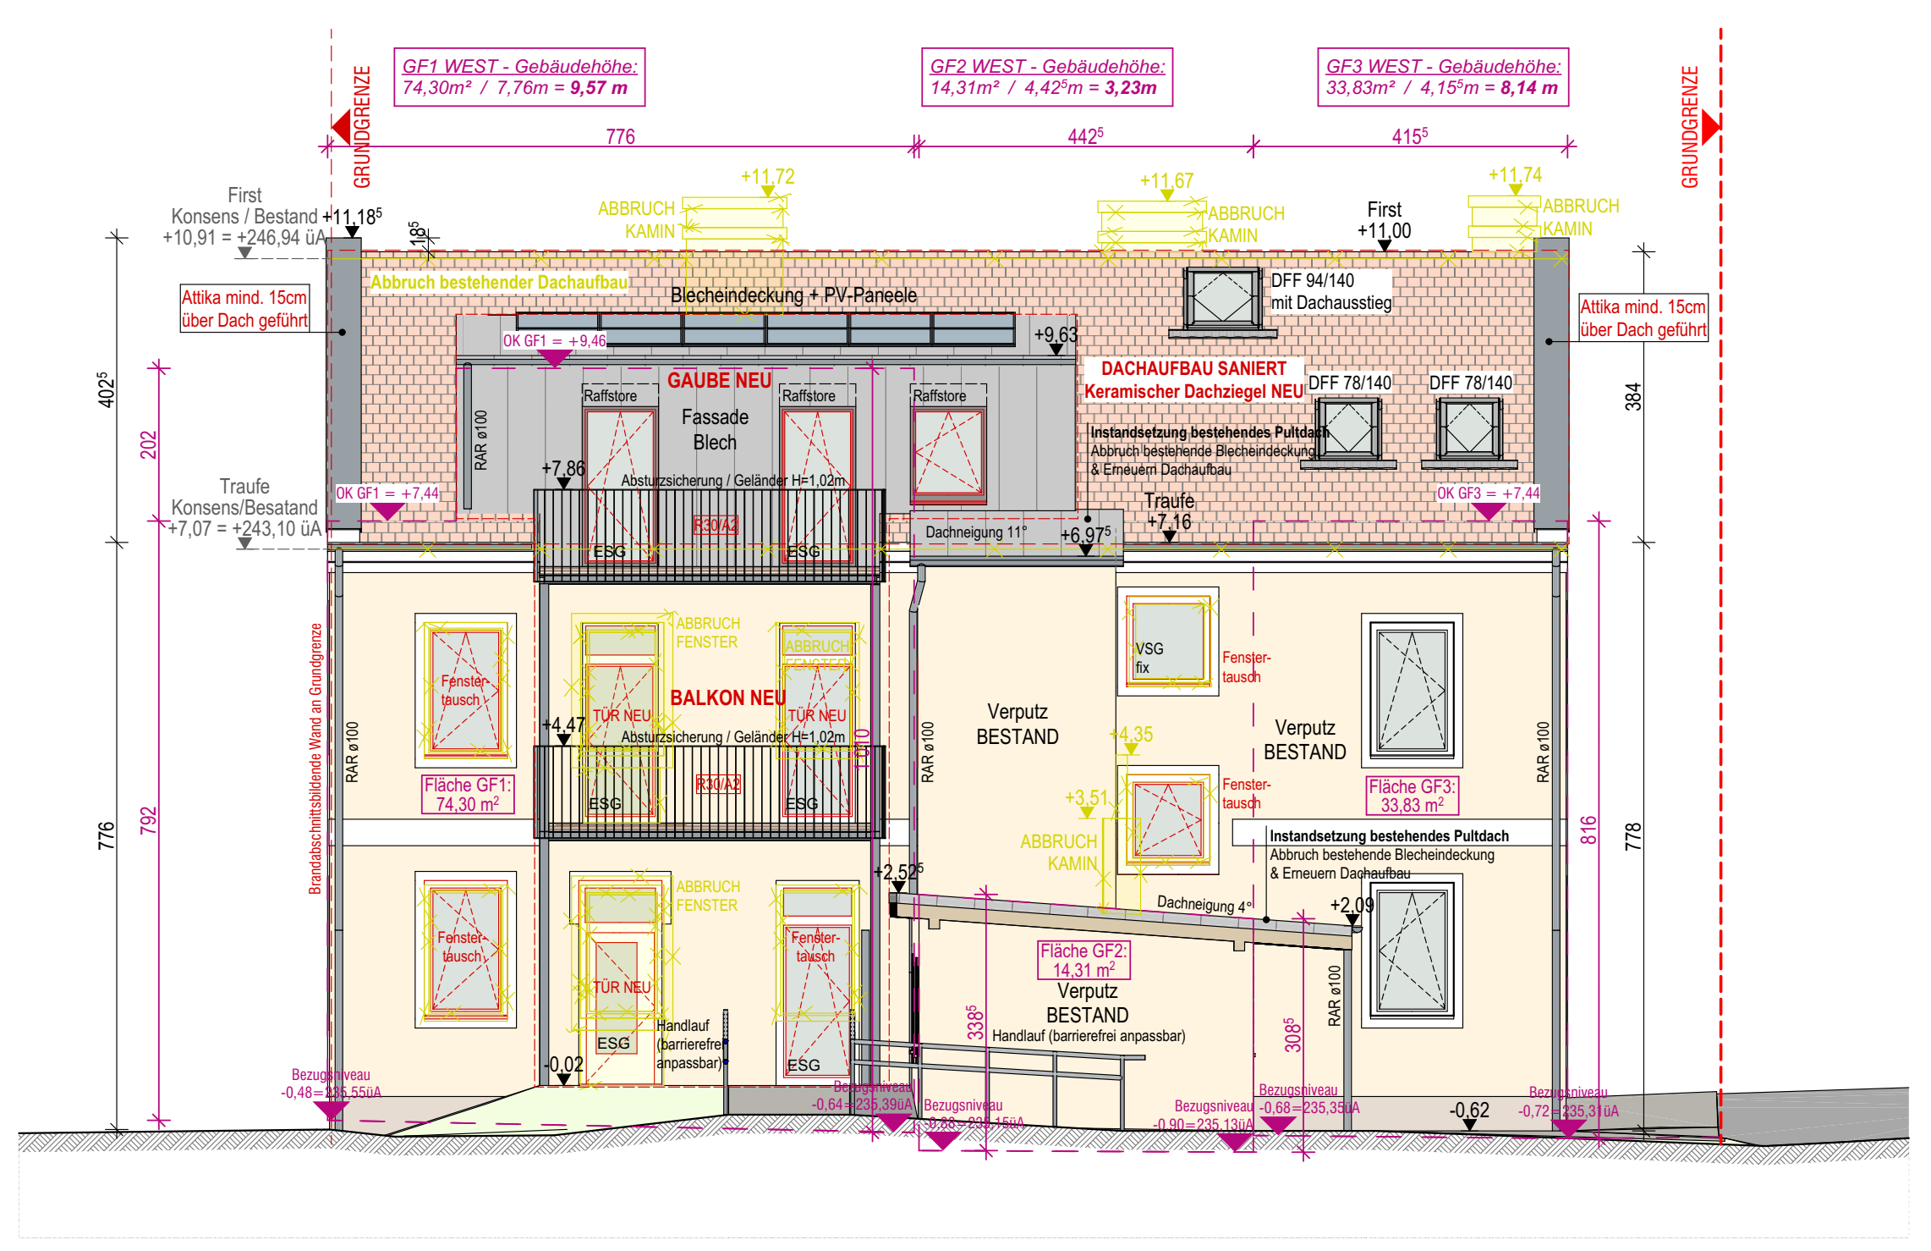

WESTANSICHT M1:100

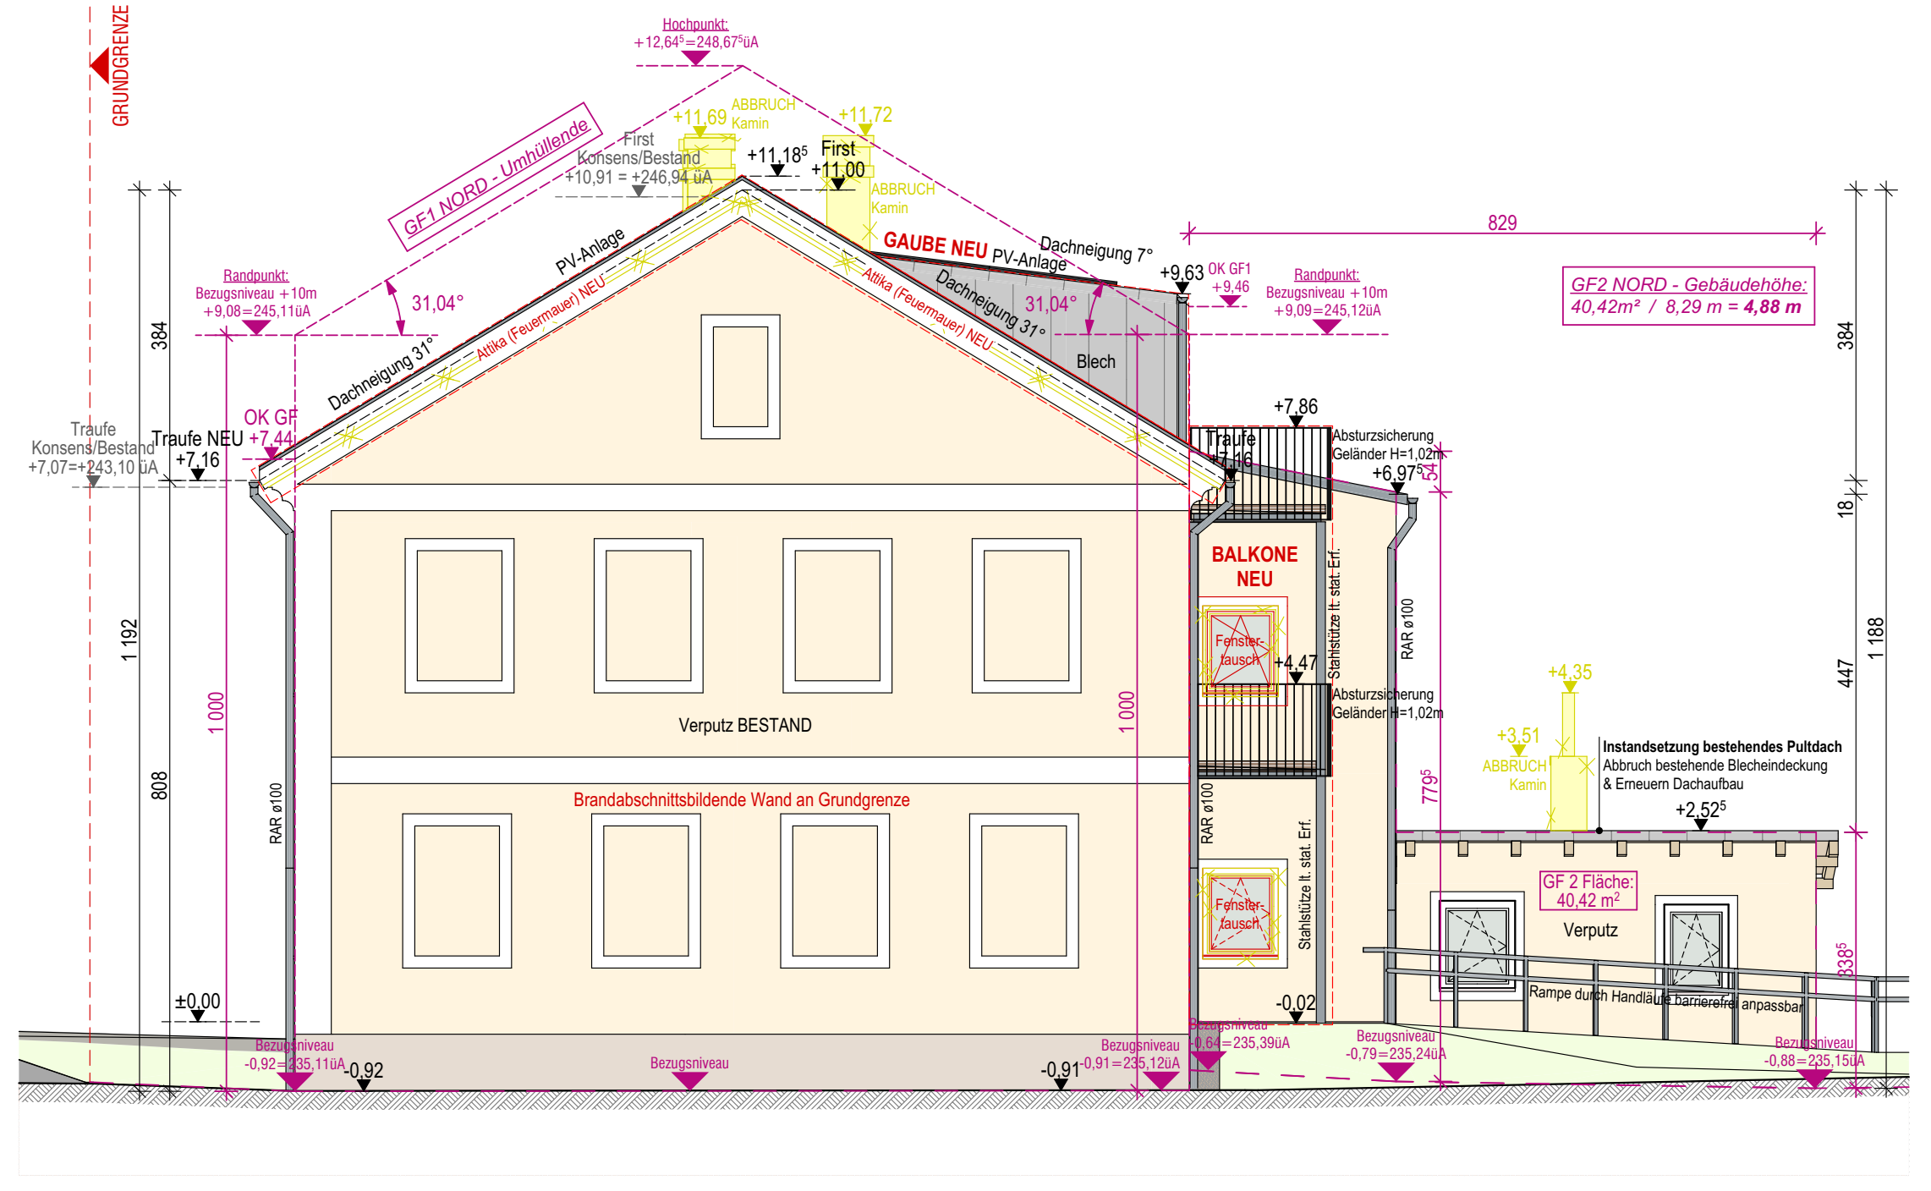

NORDANSICHT M1:100

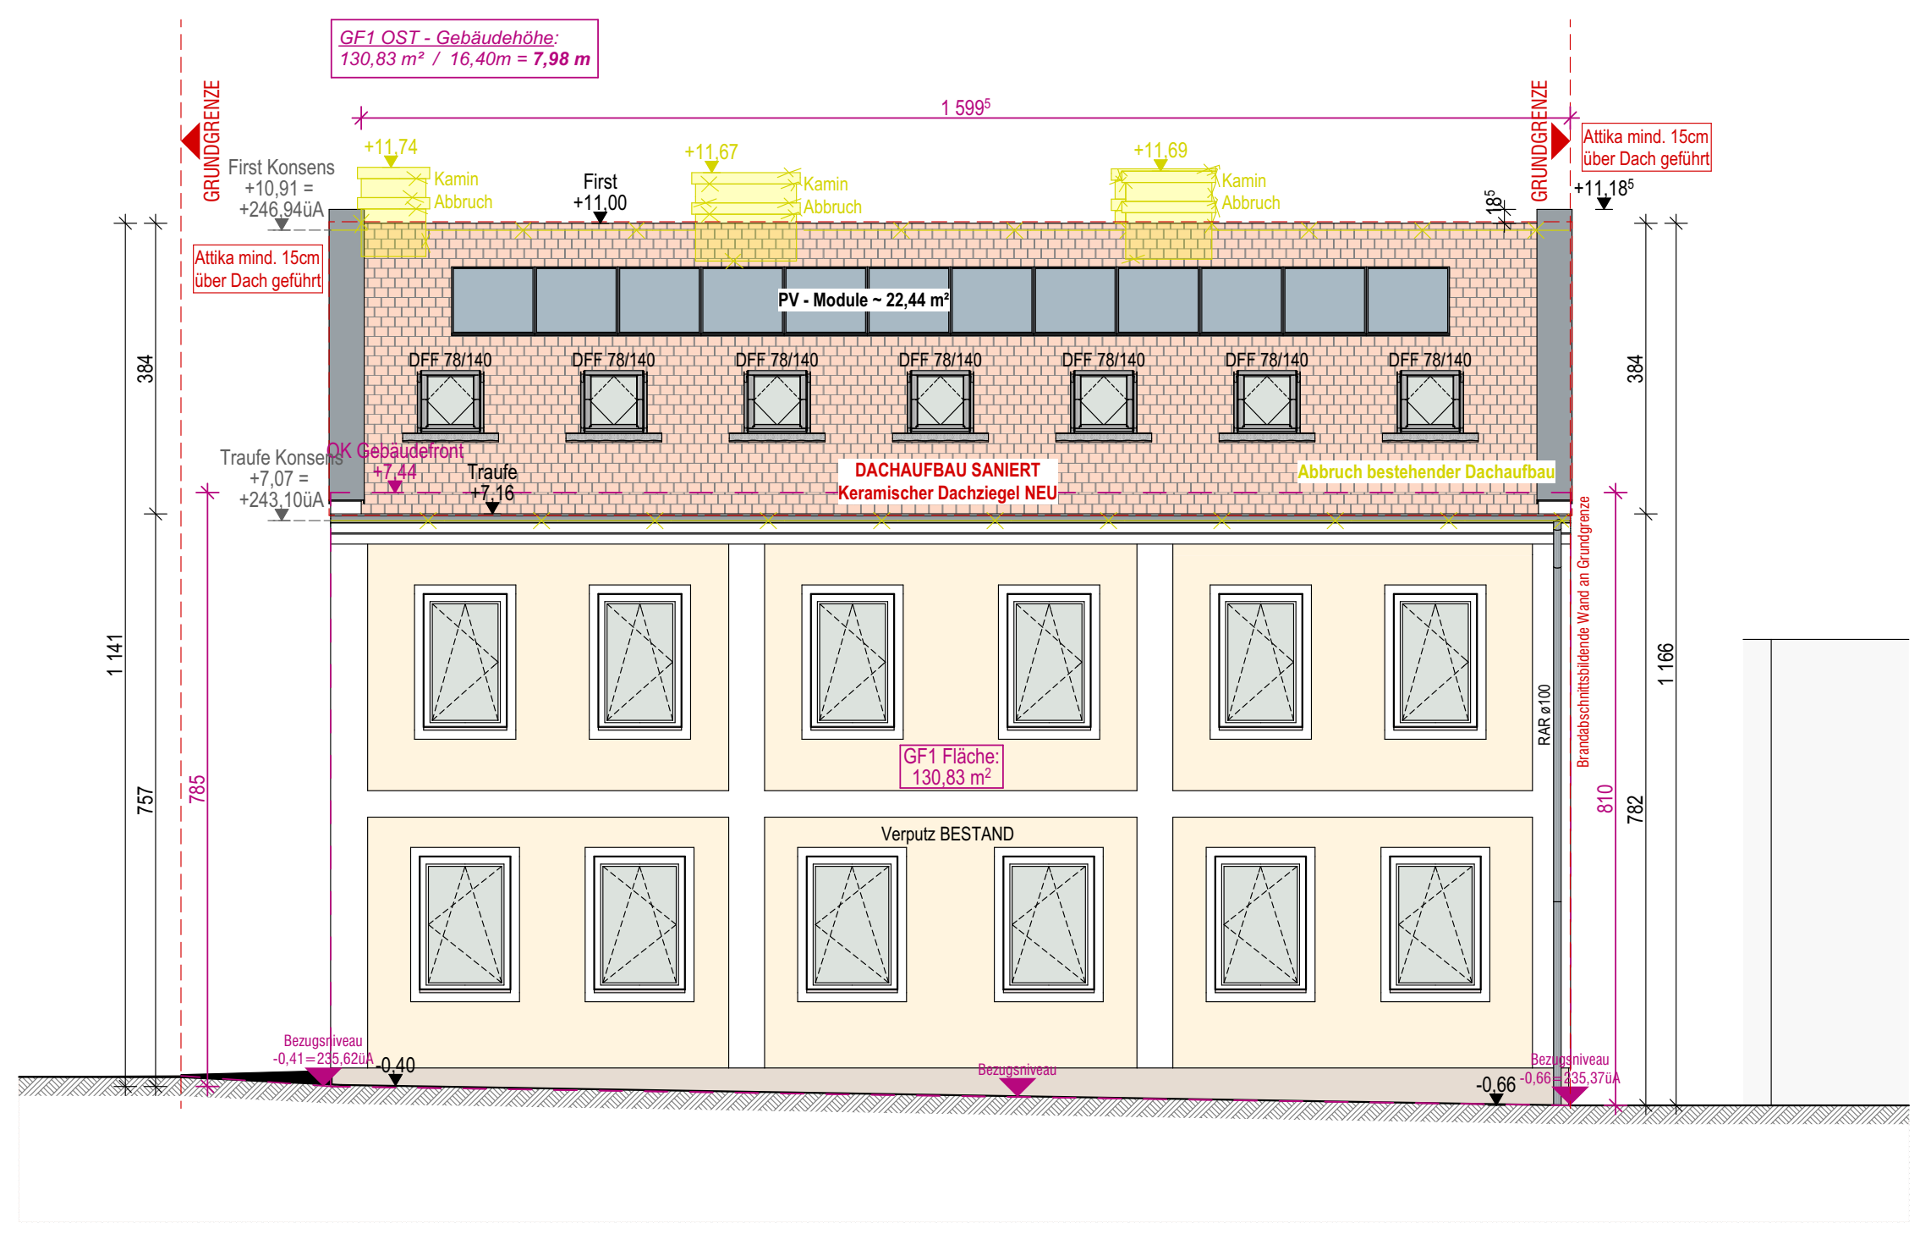

OSTANSICHT M1:100

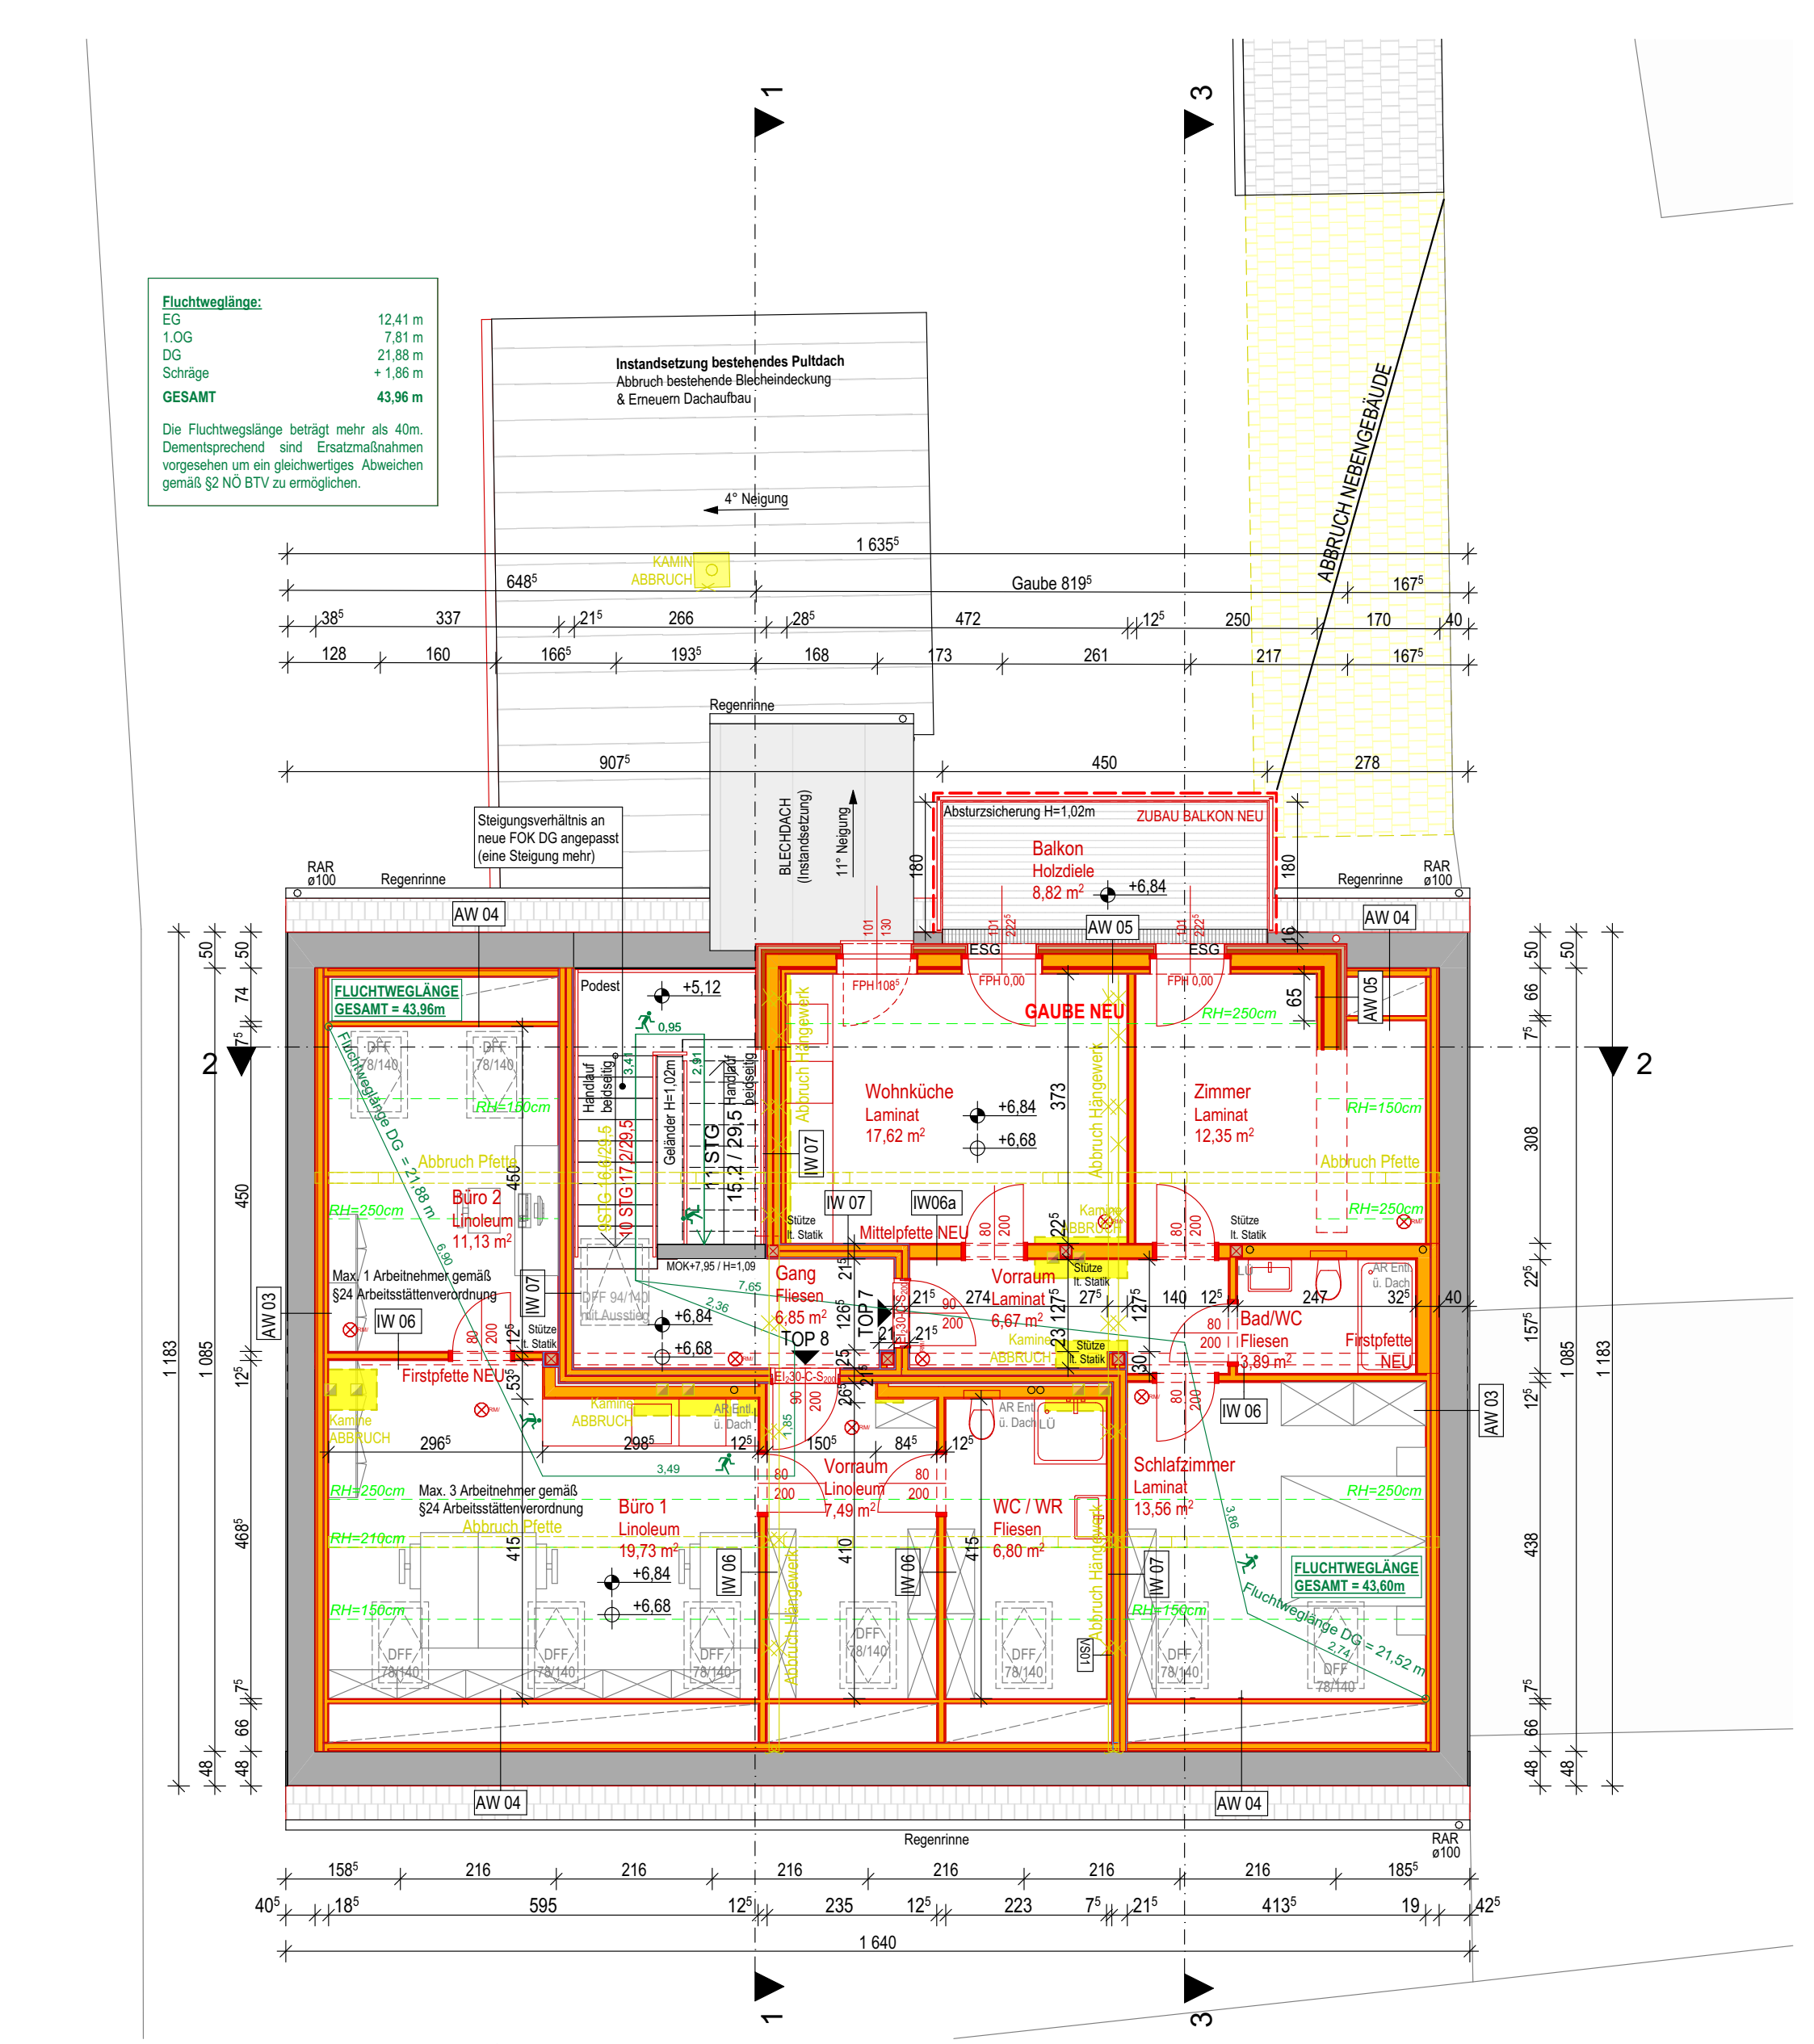

DACHGESCHOSS M1:100

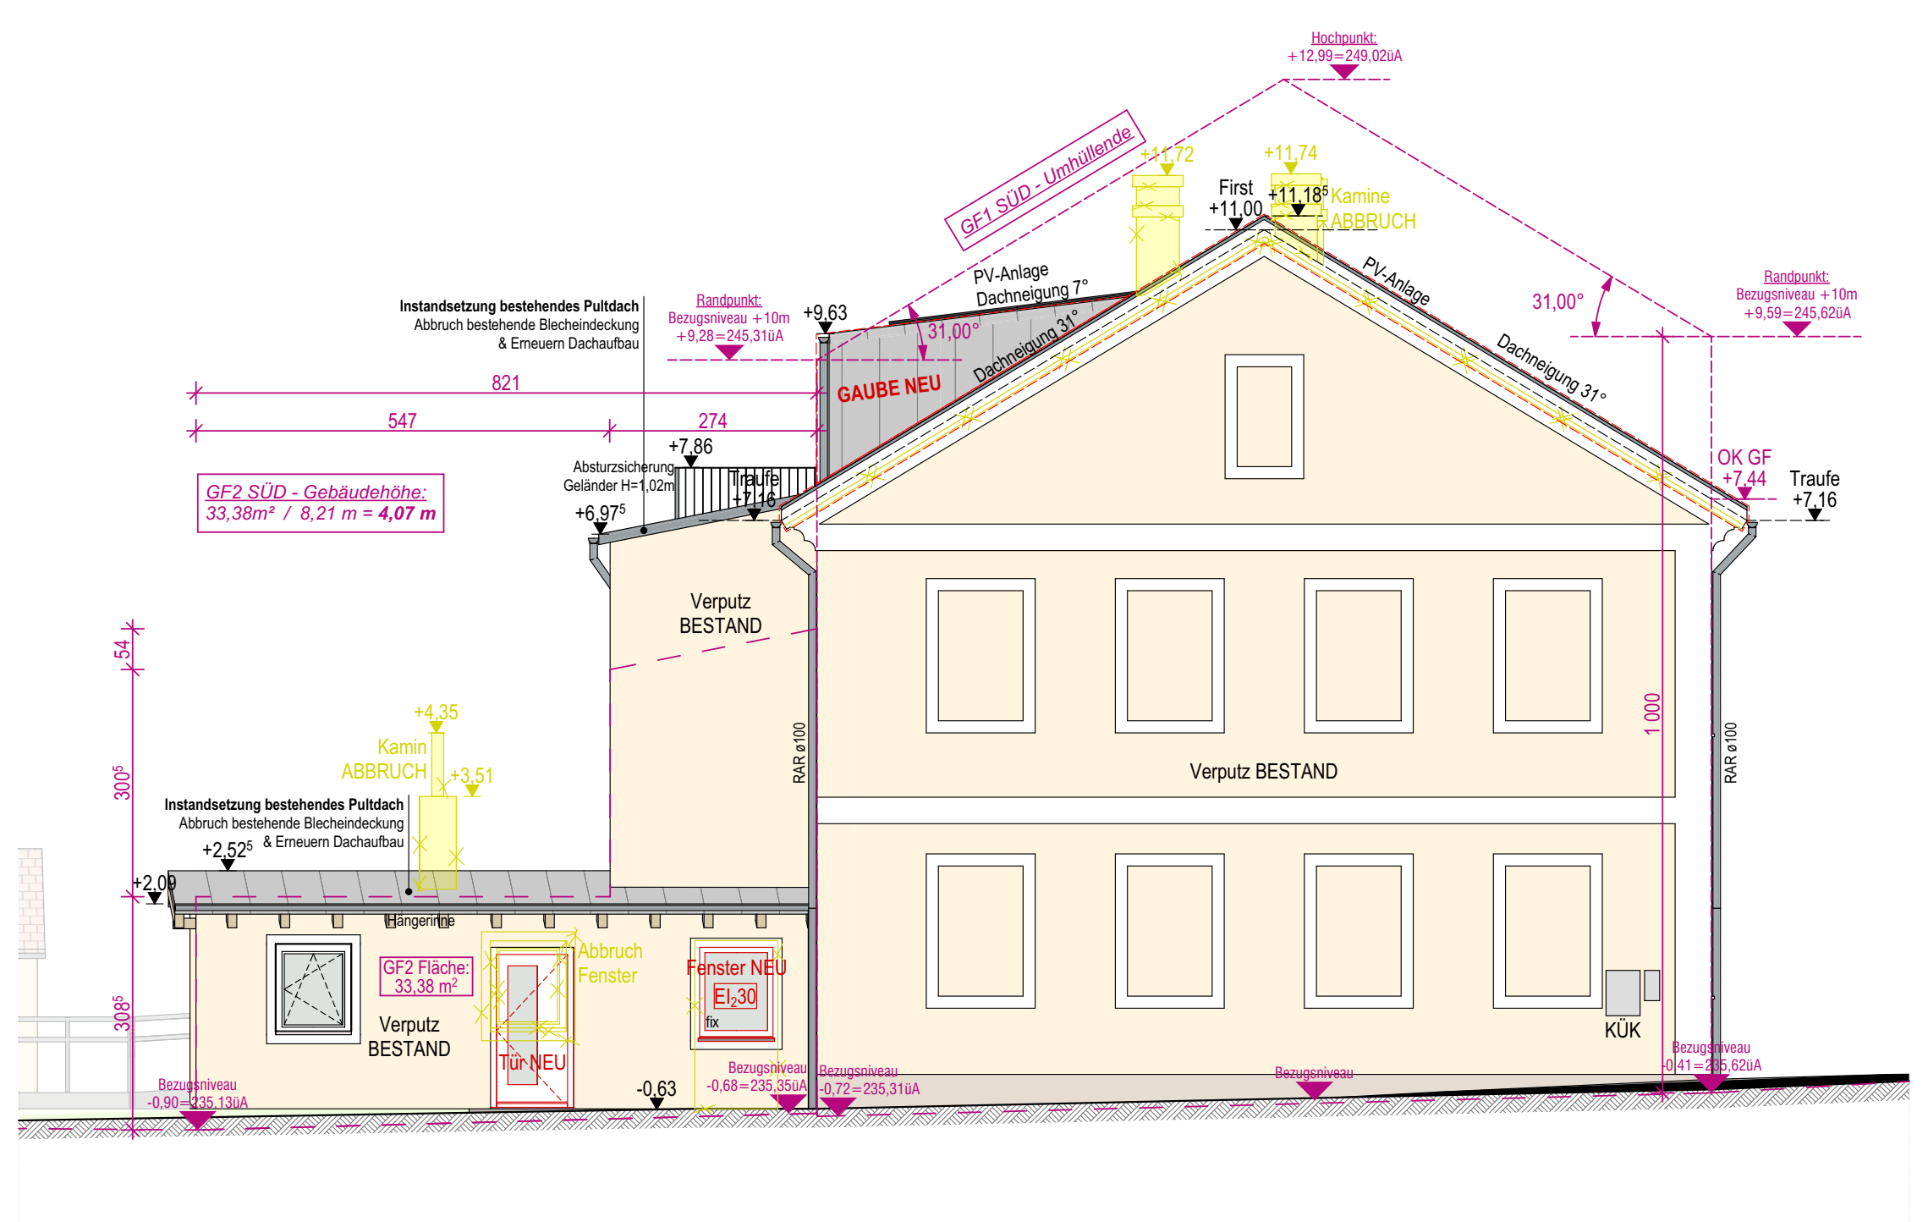

SÜDANSICHT M1:100

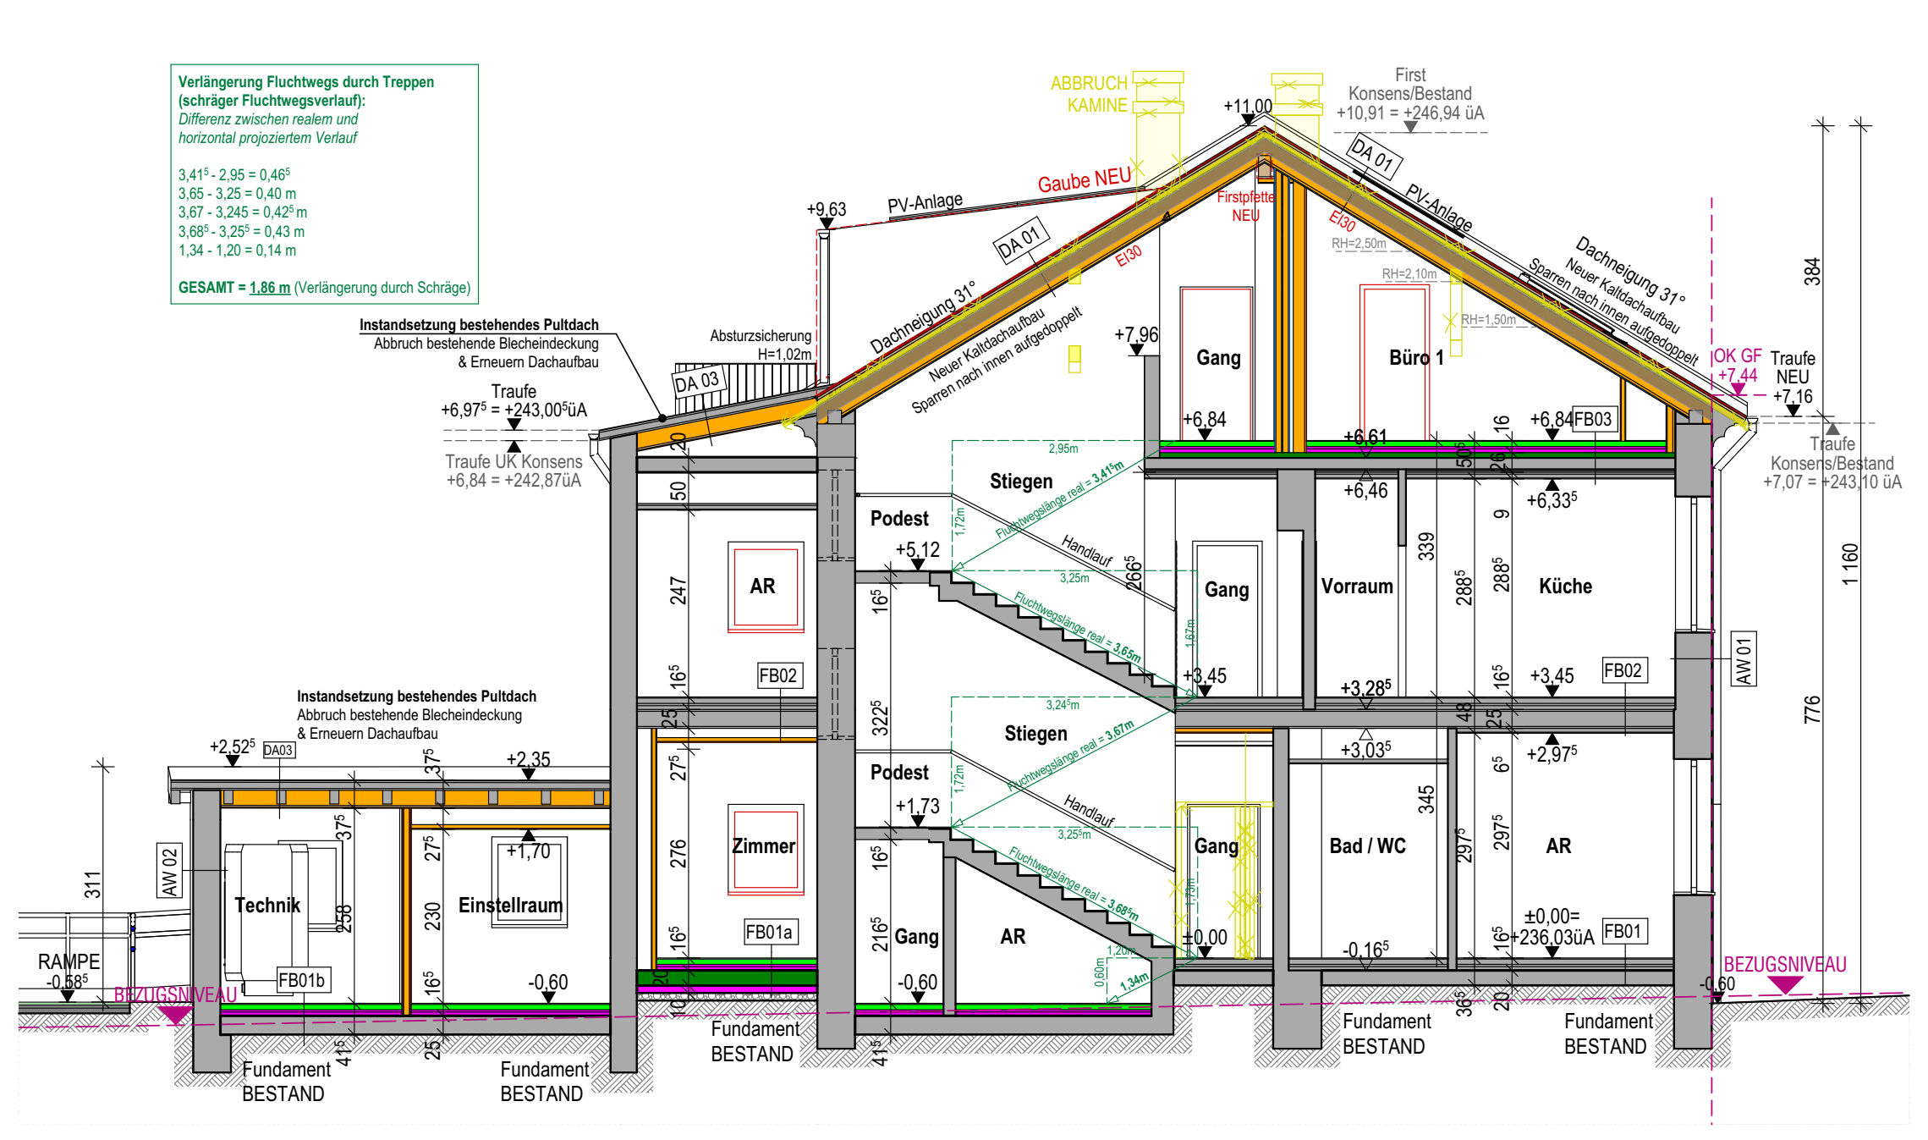

SCHNITT 1-1 M1:100

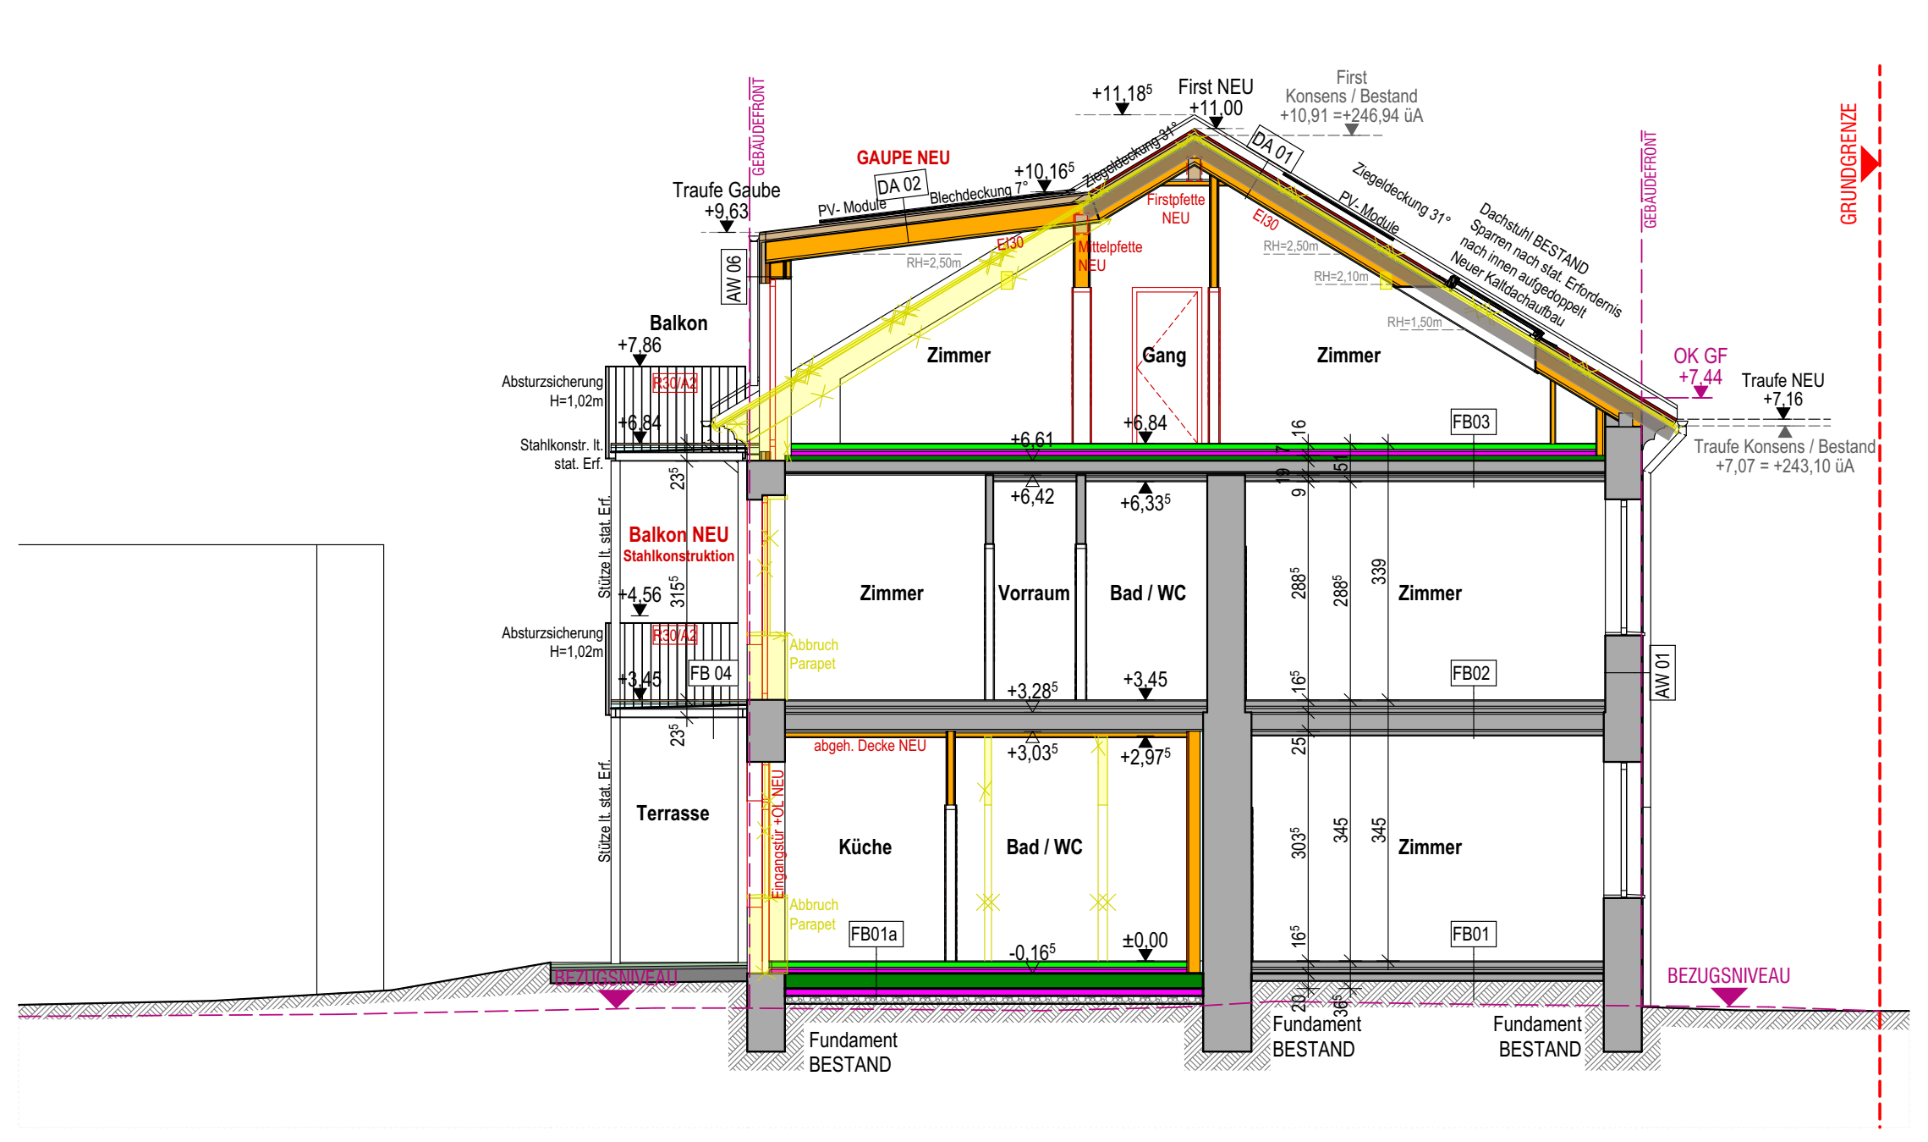

SCHNITT 3-3 M1:100

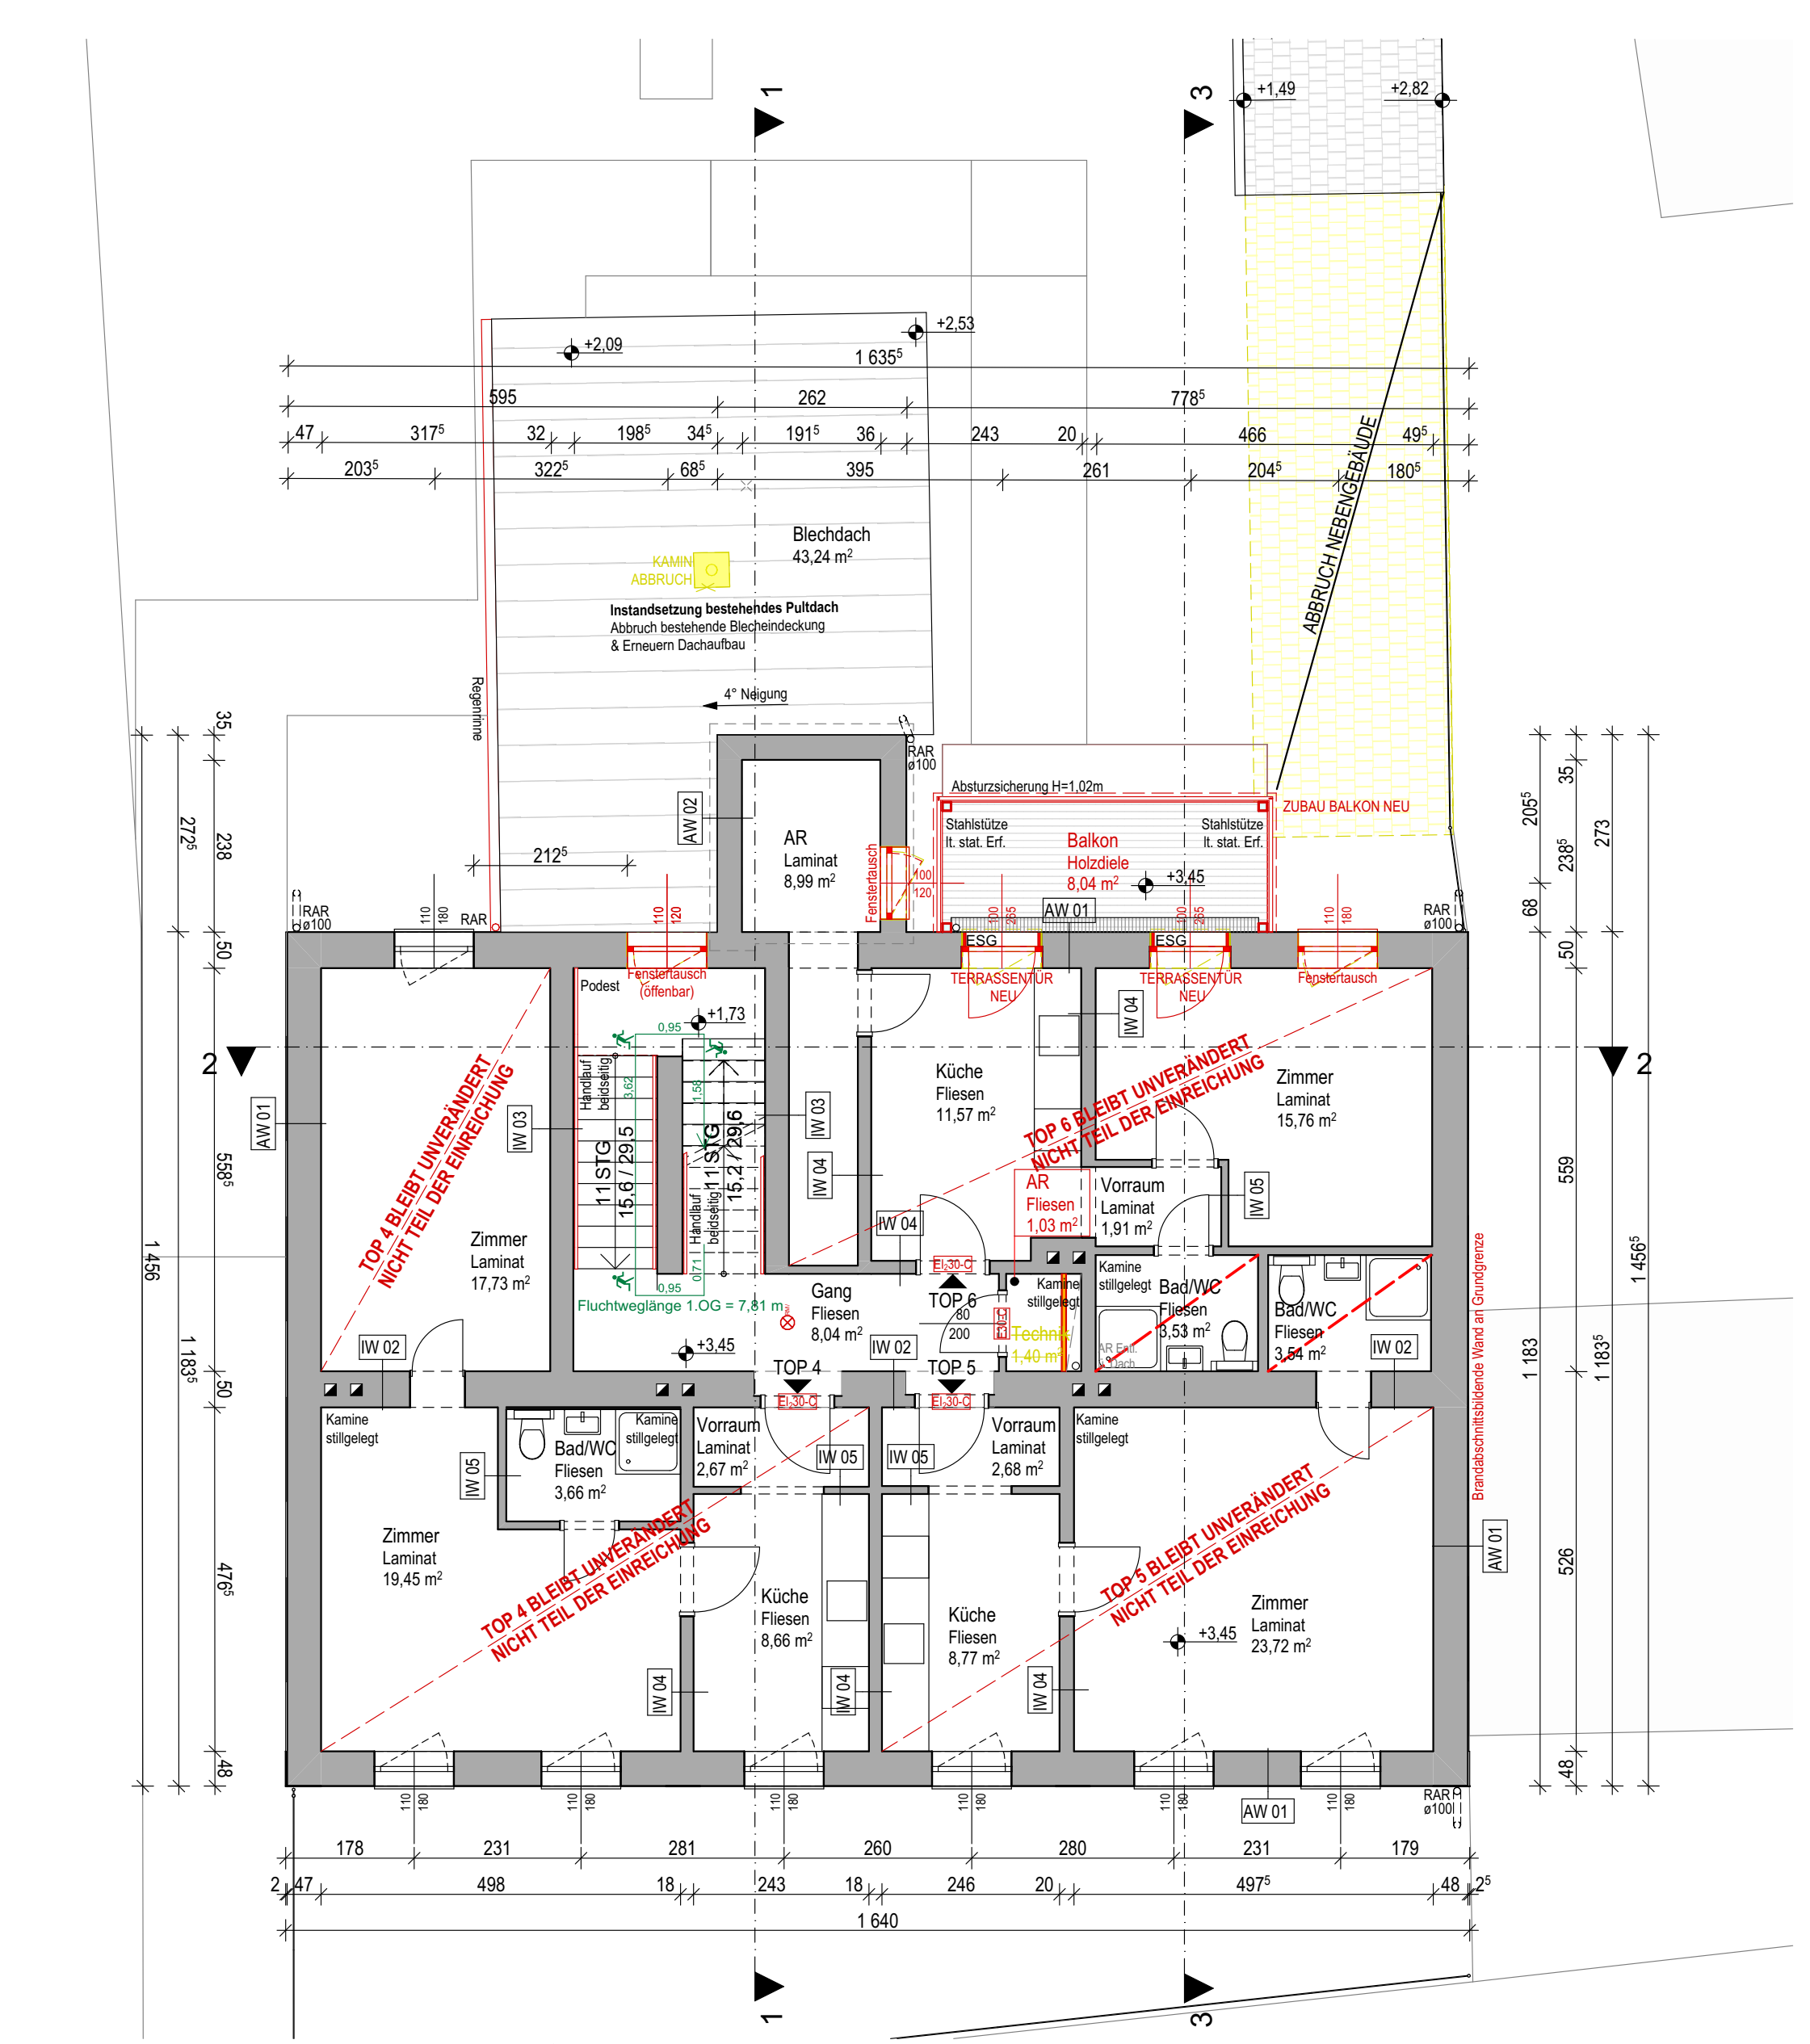

1. OBERGESCHOSS M1:100

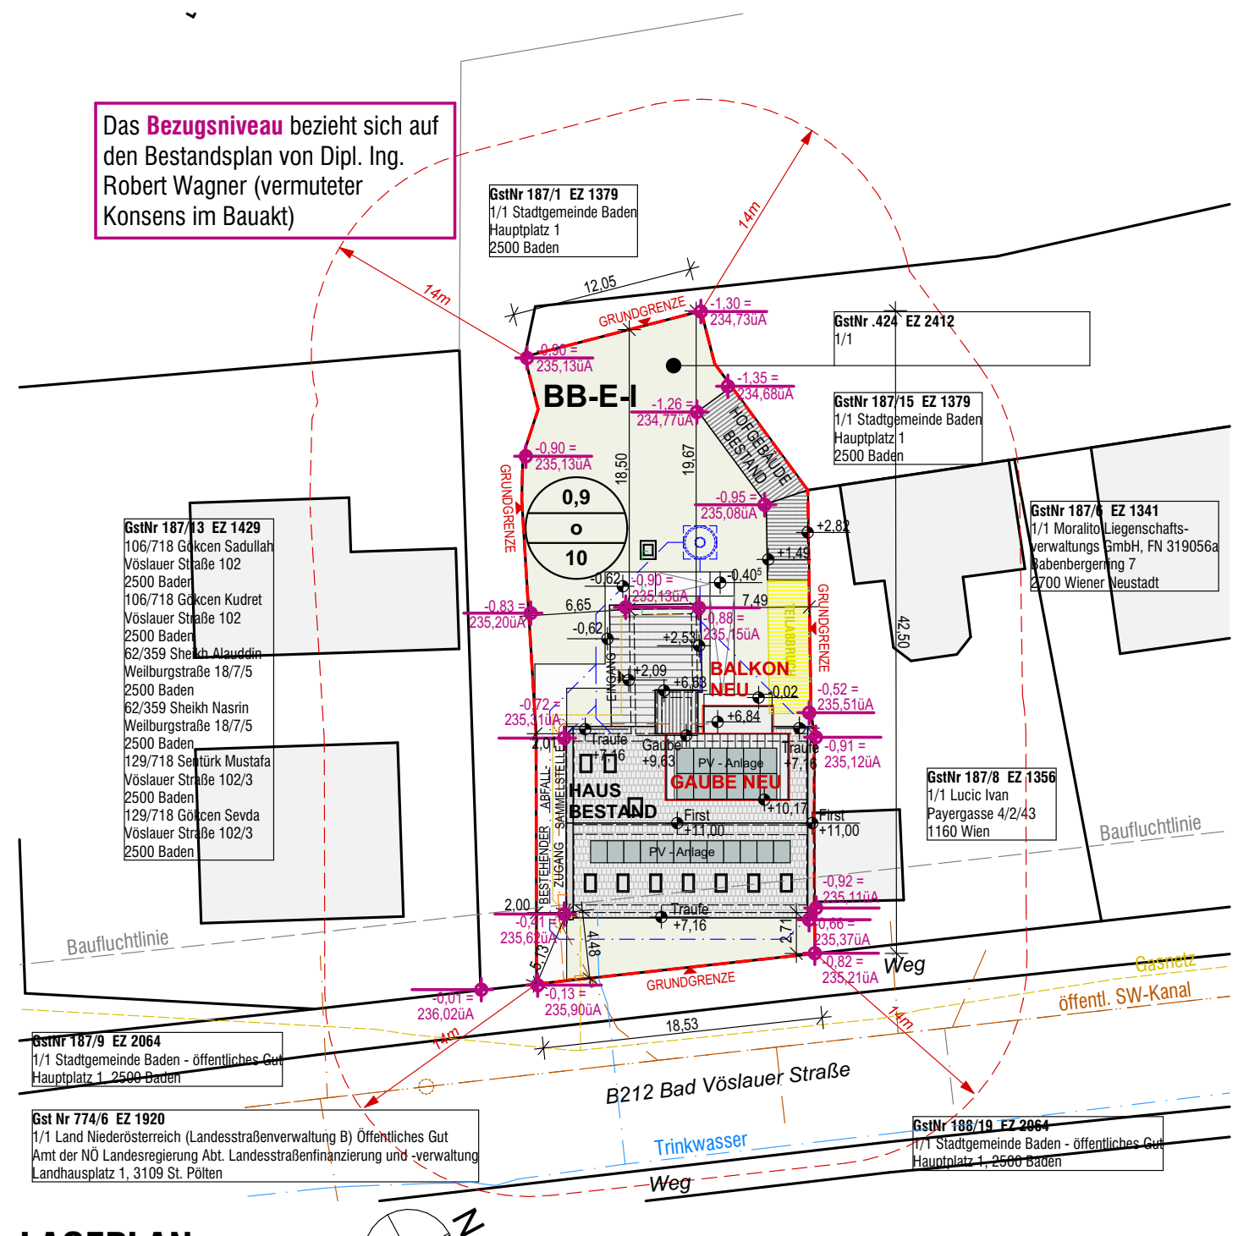

LAGEPLAN M1:500

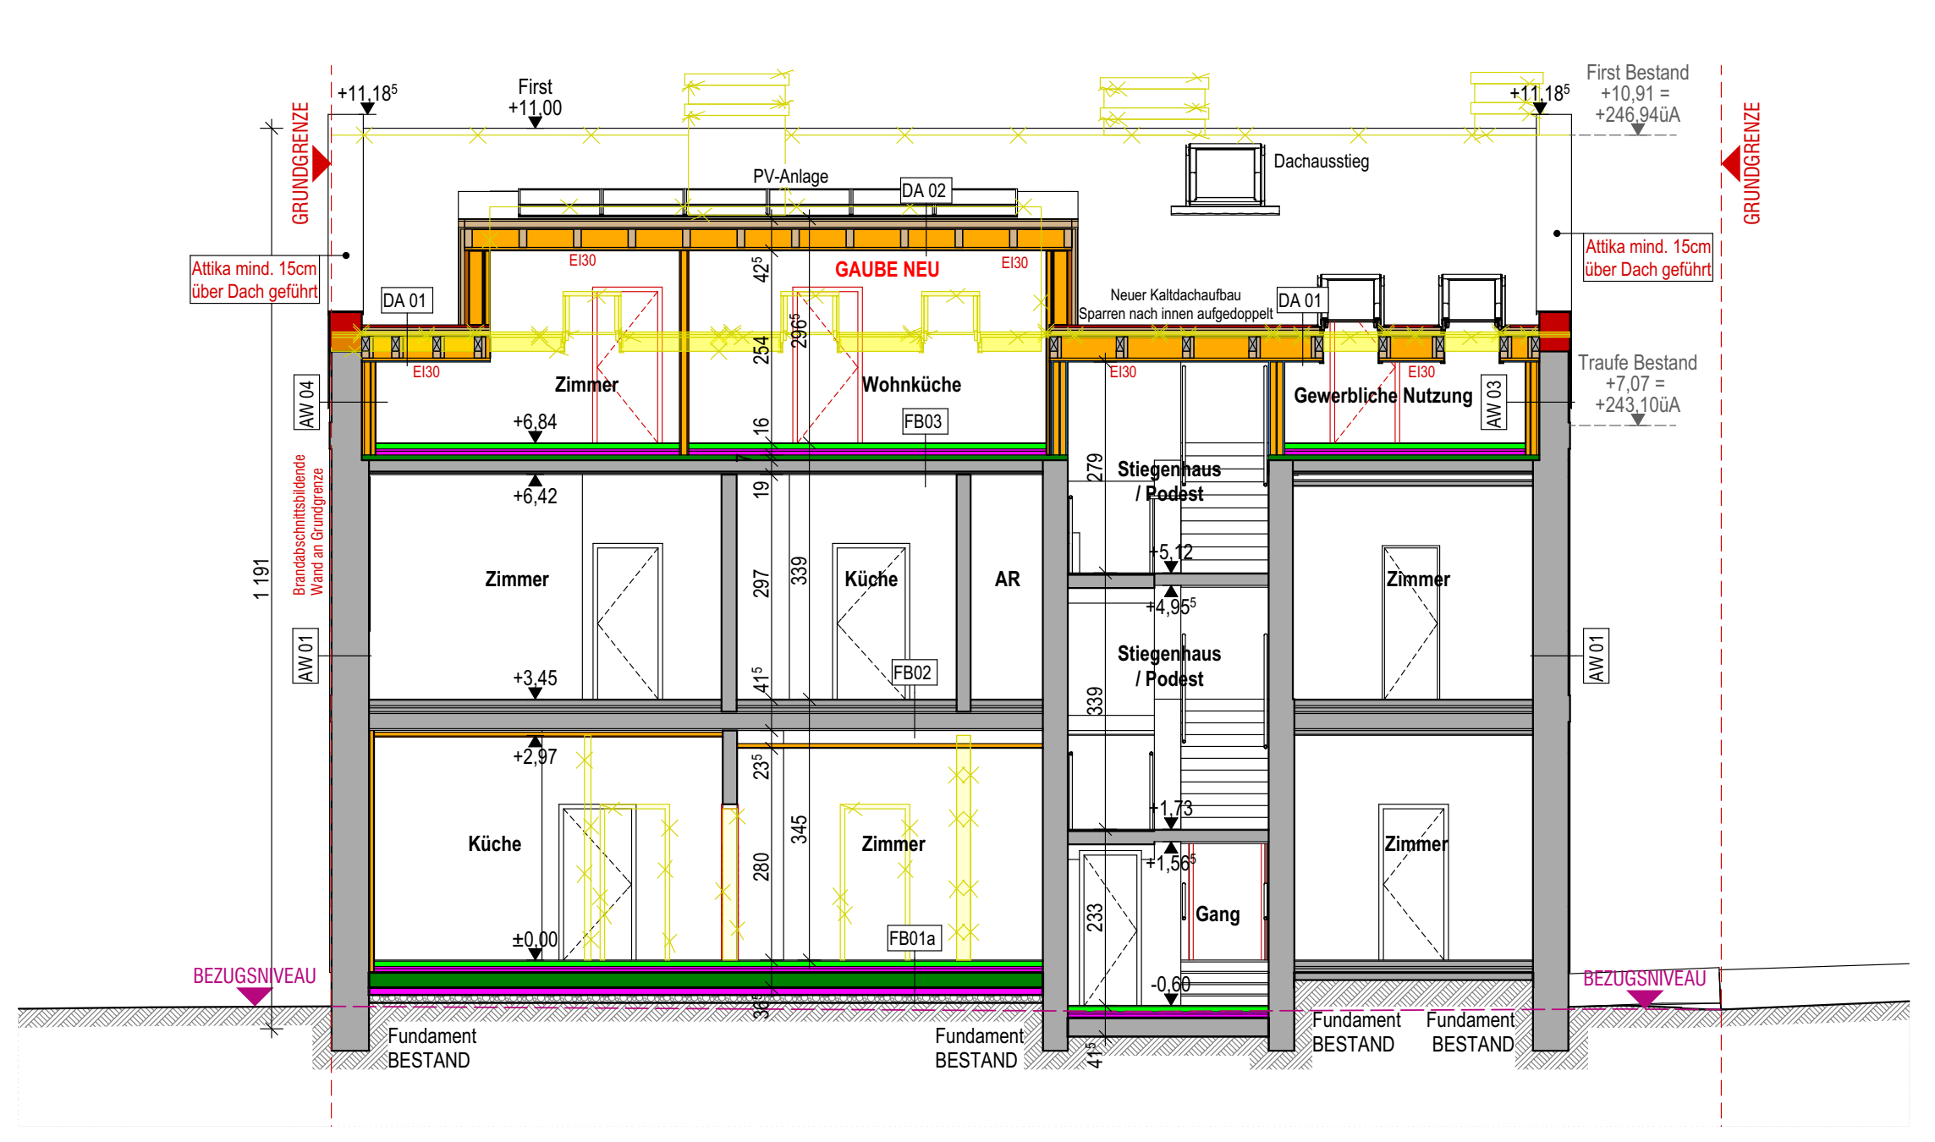

SCHNITT 2-2 M1:100

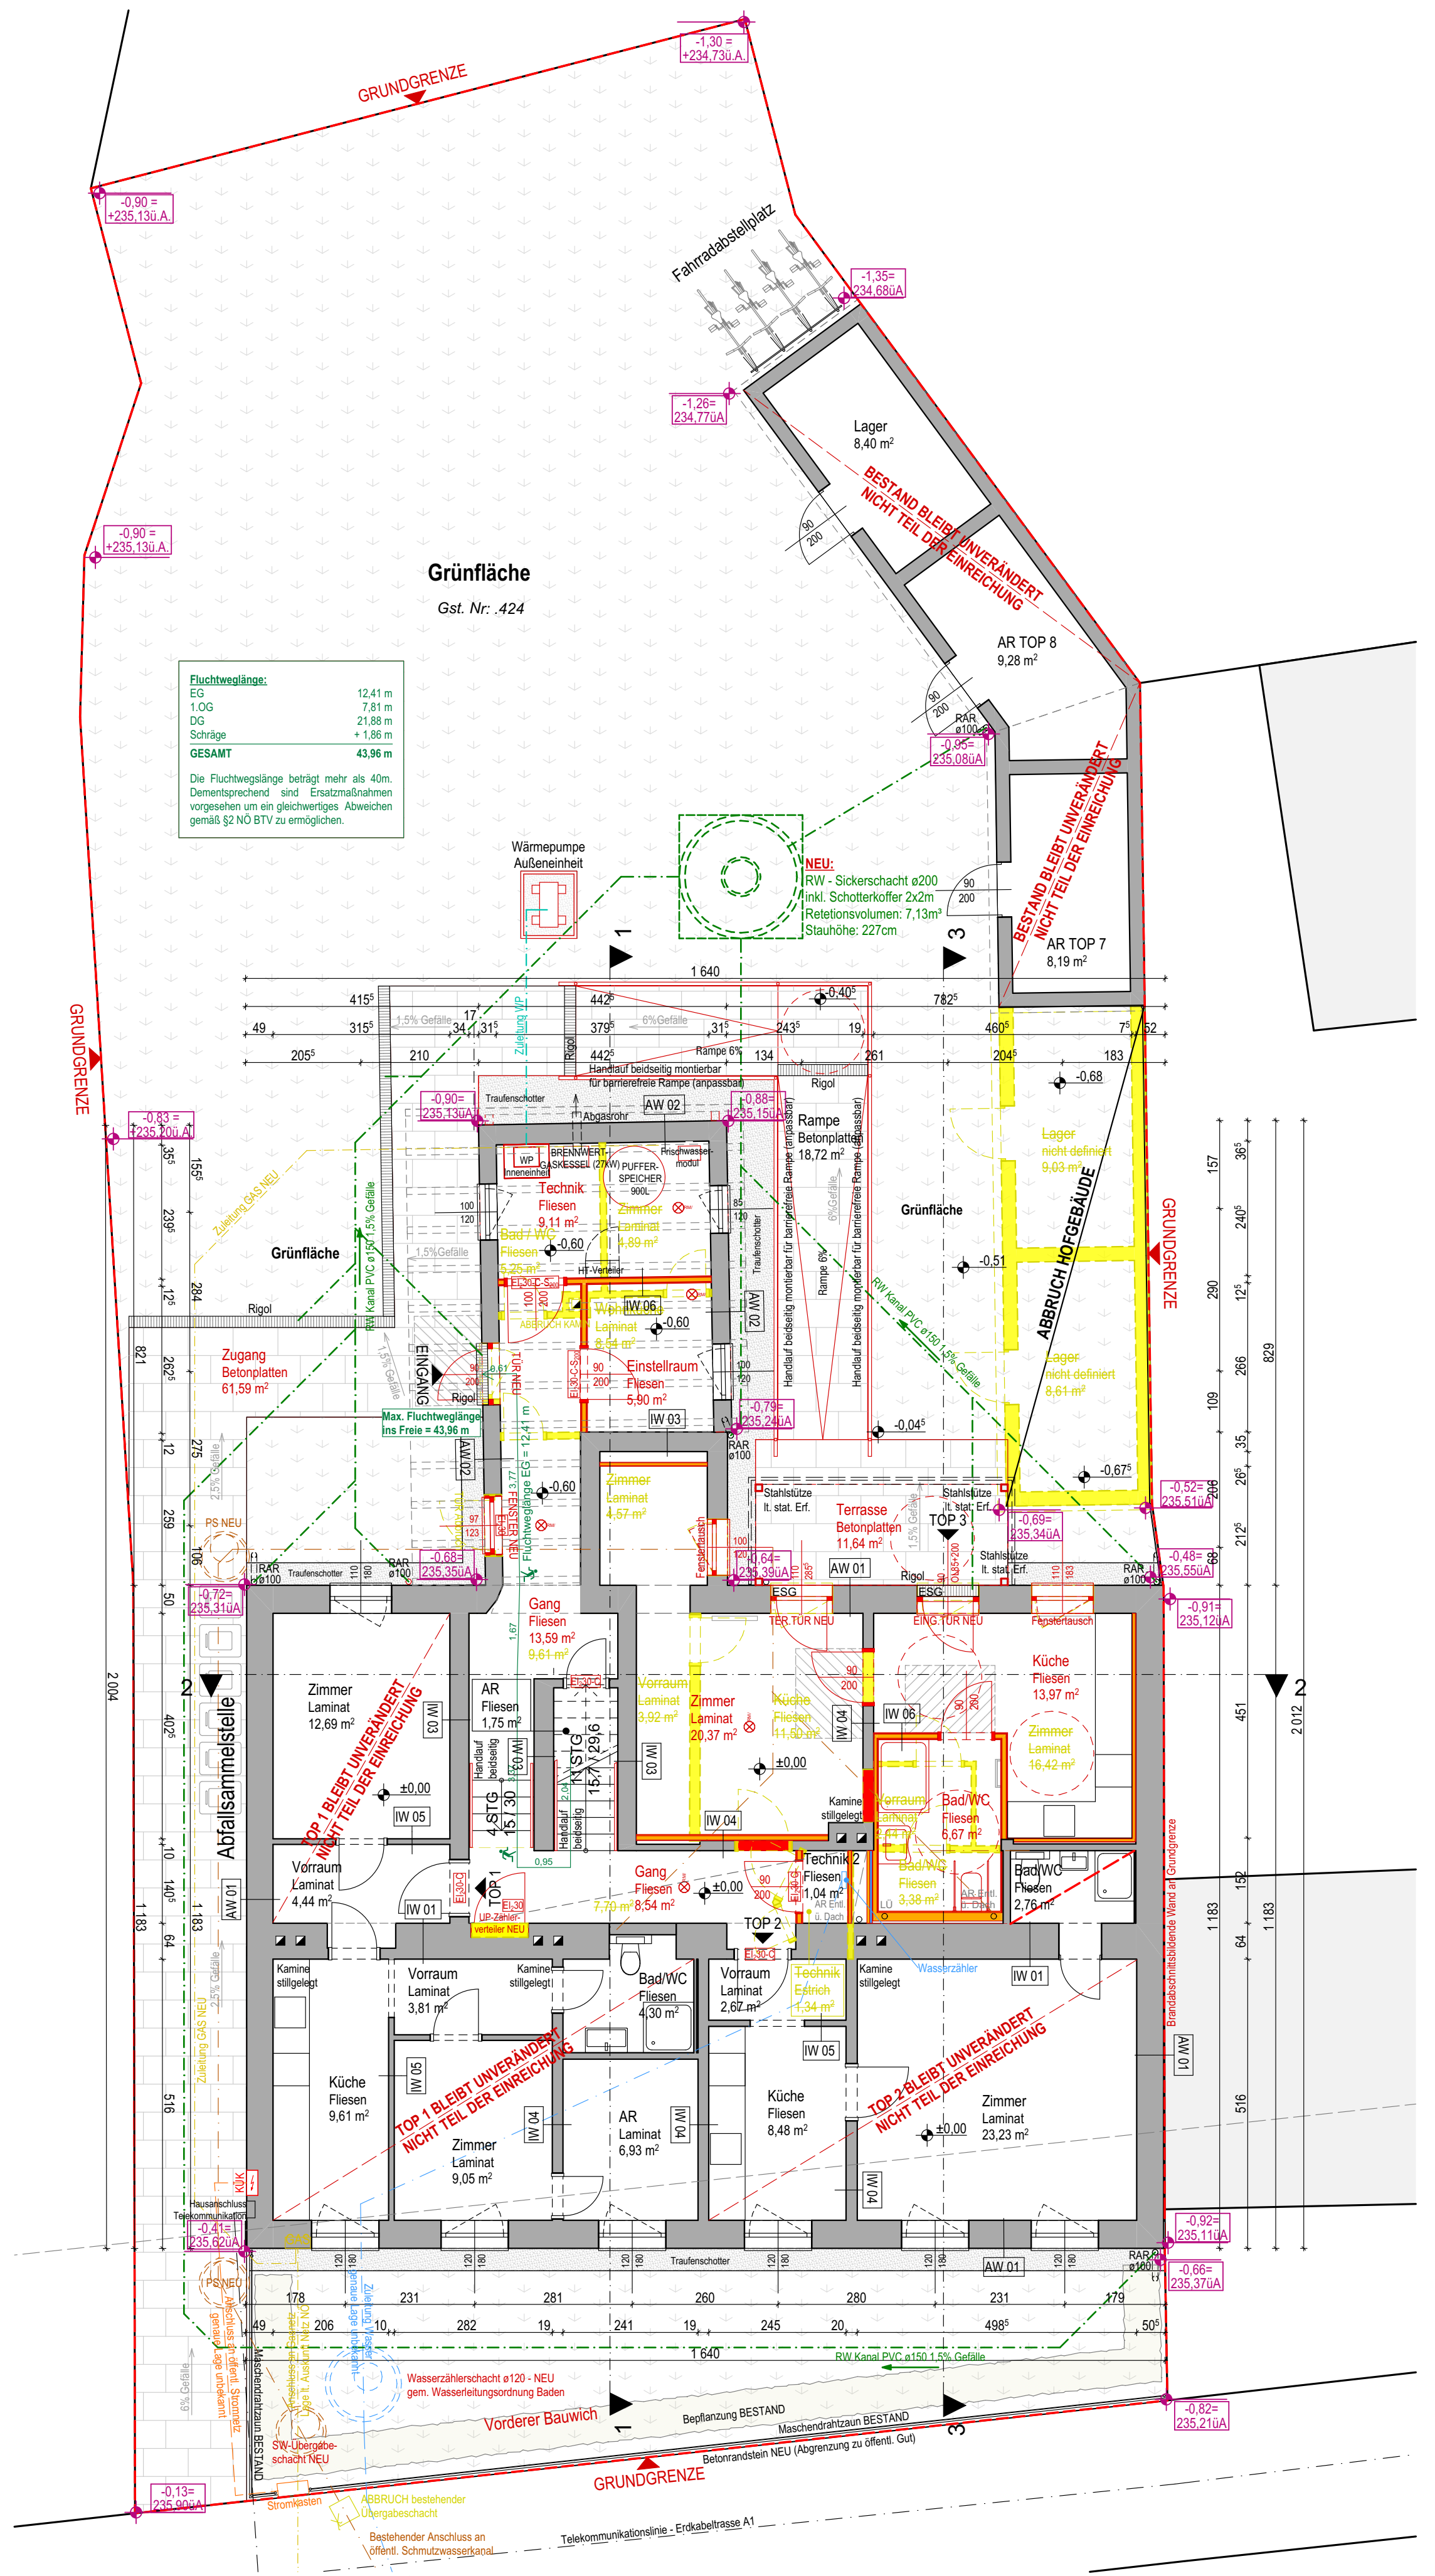

ERDGESCHOSS M1:100

Max. zulässige Zubauten - Wohnnutzung im BBI-E

Gemäß §16 (2) ROG dürfen dürfen in Bauland-Betriebsgebieten und Bauland-Verkehrsbeschränkten Betriebsgebieten an bestehenden Wohngebäuden Zubauten bis 20 % der Grundrissfläche der bisherigen Wohnnutzung, insgesamt höchstens jedoch 60 m², vorgenommen werden.

GRUNDRISSFLÄCHE - Wohnnutzung	
Erdgeschoß	179,68 m²
Obergeschoß	178,94 m²
GESAMT	**358,62 m²**

358,62 x 20% = **71,724 m² > 60m²**

Dementsprechend dürfen max. 60m² Wohnnutzfläche errichtet werden.

TOP7 - 54,09 m² < 60m²

Gleichwertiges Abweichen nach §2 NÖ BTV

Gemäß §2 der Niederösterreichischen Bautechnikverordnung darf von den bautechnischen Bestimmungen abgewichen werden, wenn die **Grundanforderungen** an Bauwerke nach §43 Abs.1 der NÖ Bauordnung 2014, die in der NÖ BTV 2014 als Mindestanforderungen definiert sind, **gleichwertig erfüllt** werden.

Gemäß NÖ BTV Anlage 2 (OIB 2 - Brandschutz) Pkt. 5.1.1 a) muss von jeder Stelle jedes Raumes in höchstens 40m Gehweglänge ein direkter Ausgang zu einem sicheren Ort des angrenzenden Geländes im Freien erreichbar sein.

In dem vorliegenden Projekt beträgt die maximale Fluchtwegslänge (reale Fluchtweglänge durch Treppen /schräger Verlauf ist berücksichtigt) 43,96m.
Um dasselbe bzw. ein höheres Sicherheitsniveau zu erreichen wie bei einem Fluchtweg von 40m werden folgende zusätzliche Maßnahmen getroffen:

- Die Wohnungseingangstüren von TOP 1, 2, 4, 5 und 6 sollen zu $EI_2 30$-C Türen getauscht werden.
- Die Türen zu Technikraum, Einlagerungsraum, TOP 7 und 8 werden als $EI_2 30$-C-S200 Türen ausgeführt.
- Die Türen zu Elektroverteiler, kleinem Technikraum 2 und Abstellraum werden als $EI_2 30$-C Türen ausgeführt.
- Es ist ein öffenbares Fenster beim Podest zwischen Erdgeschoß und 1. Obergeschoß vorhanden.

GRUNDRISSFLÄCHEN:

EG:
A: 11,83m x 16,40m = 194,01m²
B: 2,695m x 4,33 = 11,67m²
C: 5,555m x 4,425m = 24,58m²
D: 5,335 x 2,60m = 13,87m²
E: 7,985 x 2,60m = 20,76m²
1.OG:
F: 11,83m x 16,40m = 194,01m²
G: 2,62m x 2,735 = 7,17m²
DG:
H: 11,83m x 16,40m = 194,01m²

GESAMT = 660,08 m²

NACHWEIS:
Fläche Bauplatz = **738 m²**
max. zulässige GFZ = **0,9**

max. zulässige Grundrissfläche:
738 x 0,9 = **664,2 m²**

660,08 m² < 664,2 m²
Nachweis erfüllt - GFZ zulässig

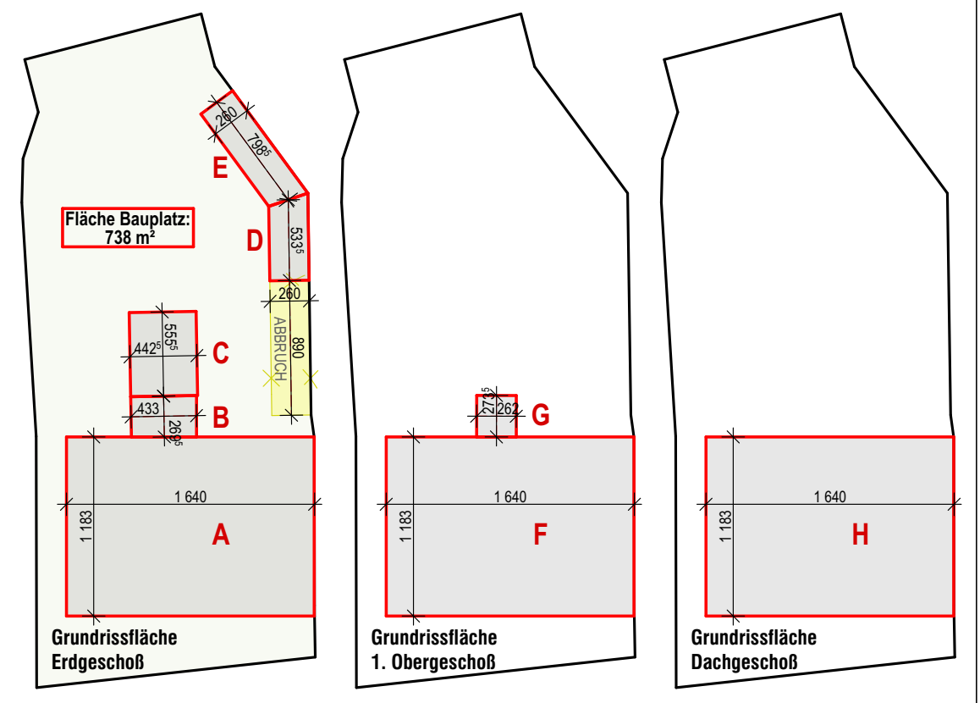
Fläche Bauplatz: 738 m²
A
B
C
D
E
F
G
H
ABBRUCH
1 640
1 183
Grundrissfläche Erdgeschoß
Grundrissfläche 1. Obergeschoß
Grundrissfläche Dachgeschoß

Durch den Dachgeschoßausbau und die Errichtung einer Gaube wird eine neue Wohnung sowie eine neue Gewerbefläche (Büronutzung) geschaffen.

HÖHENBEZUG
±0.00 = + 236,03 m über Adria

Heizung:	Zentrale Gastherme + Luft/Wasser Wärmepumpe
Bauweise:	Massivbauweise Ziegel (Bestand), Dachgeschoßausbau und Errichtung einer Gaube in Holzleichtbau, Balkonzubau aus Stahl
Müllgefäßstandplatz:	im Außenbereich

KFZ - STELLPLÄTZE:
→ Gemäß §63 Abs. 1b wird auf die Schaffung zusätzlicher KFZ - Stellplätze verzichtet.

FAHRRADABSTELLPLÄTZE:

1 Fahrradabstellplatz / Wohneinheit	1 neue WHG	1 Stellplatz
1 Fahrradabstellplatz / 20 Arbeitsplätze	< 20 Arbeitspl.	1 Stellplatz
GESAMT		**2 Stellplätze**

→ Auf dem Grundstück sollen gemäß NÖ BTV §14 zwei Fahrradabstellplätze errichtet werden.
→ Der Fahrradabstellplatz soll im hinteren Bereich des Grundstücks errichtet werden.

BRANDSCHUTZ
GEBÄUDEKLASSE: GK4 lt. OIB RL2 2023
0 unterirdisches Geschoss
3 oberirdirsche Geschosse
Fluchtniveau > 7m

→ Gemäß NÖ BTV 2014 Anlage 2 (OIB2) Pkt. 3.1.1 ist keine Unterteilung in mehrere Brandabschnitte erforderlich.
→ Die allgemeinen Anforderungen an das Brandverhalten gemäß Tabelle 1a werden eingehalten.
→ Die allgemeinen Anforderungen an den Feuerwiderstand von Bauteilen gemäß Tabelle 1b werden eingehalten.
→ Alle neu hergestellten Eingangstüren zu neuen Nutzungseinheiten sowie Türen zu Technik und Einlagerungsraum werden EI_2 30-C-S_{200} ausgeführt.
→ Alle Eingangstüren zu bestehenden Nutzungseinheiten sowie Türen zu Technik 2, Abstellraum etc. werden EI_2 30-C ausgeführt.
→ Brandschutztechnische Ausführung neuer Schächte und Führung der Leitungen lt. TRVB 110 B 2015
→ Außenbauteile wie Geländer werden feuerverzinkt und korrosionsbeständig ausgeführt.
→ Sofern Schächte, Kanäle, Leitungen und sonstige Einbauten in Wänden bzw. Decken liegen oder diese durchdringen, ist entweder durch Abschottung oder Ummantelung sicher gestellt , dass die Feuerwiderstandsklasse dieser Bauteile nicht beeinträchtigt wird. Brandschutzschotts gemäß OIB 2 Punkt 3.5.3
→ Sämtliche Kamine werden stillgelegt und teilweise abgebrochen. Nicht abgebrochene Teile werden ausbetoniert.
→ Die Balkone sind R 30 oder A2 ausgeführt. Balkone werden thermisch vom Bestand getrennt ausgeführt.
→ Öffenbare Dachflächenfenster sind mind. 1m von der Grundstückgrenze entfernt. Dachflächenfenster werden in VSG ausgeführt.
→ Alle Aufenthaltsräume sowie alle Gänge über die eine Fluchtweg führt, sind mit Rauchwarnmeldern - batteriebetrieben ausgestattet (in den Wohnküchen nicht unmittelbar im Kochbereich).
→ Eine Sicherheitsbeleuchtung wird im Stiegenhaus und dem Gangbereich außerhalb der Wohnungen installiert.
→ Nennwärmeleistung zentrales Gasbrennwertgerät 27 kW

VER- / ENTSORGUNG:
→ Das Stiegenhaus wird natürlich belüftet.
→ Trinkwasser: Bestehender Anschluss an das öffentliche Versorgungsnetz.
→ Abwässer werden über den bestehenden Anschluss in das öffentliche Kanalsystem eingeleitet.
→ Niederschlagswässer werden in einem Schacht auf Eigengrund zur Versickerung gebracht.
→ Kanalleitungen PVC bzw. Guss in kg, mind. 2% Gefälle
→ Die Müllsammlung erfolgt über den geplanten Müllplatz im Hofbereich.
→ Heizung / Warmwasser für bestehende Wohneinheiten: Zentrales Gasbrennwertgerät (Nennwärmeleistung 27kW).
→ Heizung / Warmwasser für neue Nutzungseinheiten: Neue Wärmepumpe.
→ Dachgeschoß: Beheizung durch Fußbodenheizung, elektrische Handtuchheizkörper in den Bädern.
→ Elektroversorgung: Bestehender Anschluss an das Ortsnetz.

NUTZUNGSSICHERHEIT und BARRIEREFREIHEIT
→ Es wird bestätigt, dass gemäß § 46 NÖ Bauordnung eine Wohneinheit barrierefrei anpassbar ausgeführt wird.
→ TOP 3 (Erdgeschoß) wird barrierefrei anpassbar ausgeführt. Erschließung erfolgt über eine Rampe im Außenbereich.
→ Geländerhöhen mind. 1,02 m. Abstände von vertikalen Stäben max. 12cm.

HYGIENE, GESUNDHEIT und UMWELTSCHUTZ
→In sämtlichen Nassräumen wird eine Kunststoffabdichtung unter Fliesenbelägen mit 15cm Wandhochzug ausgeführt.
→ Alle Aufenthaltsräume sind durch Fenster belüftbar und verfügen über ausreichende Lichteintrittsflächen gemäß OIB RL3 9.1.1
→ Alle zur Belichtung von Aufenthaltsräumen notwendigen Lichteintrittsflächen verfügen über eine freie Sicht von mind. 2m und zumindest in einem Aufenthaltsraum über eine freie waagrechte Sicht von mind. 6m in 1,20m Höhe.
→Sanitärräume, die über kein Fenster verfügen, werden mechanisch entlüftet.
→sonstige innen liegende Räume werden entsprechend ihrem Verwendungszweck be- und entlüftet.
→Das notwendige Luftvolumen ist in sämtlichen neu errichteten Räumen vorhanden.
→alle Glasgeländer und bodentiefen Verglasungen mit Absturzgefahr werden in VSG ausgeführt, vertikale Verglasungen mit Durchsturzgefahr in ESG

BAUPHYSIK
→Die im Einreichplan angegebenen Aufbauten und Angaben sind mit jenen im bauphysikalischen Nachweis ident; insbesondere hinsichtlich der Dicke sowie des Materials bzw. der Type der Baustoffe.

AUSSTATTUNG
→ In allen von der Einreichung umfassten Wohnungen wird ein Anschluß für eine Waschmaschine (Badezimmer oder Küche) vorgesehen.
→ Sämtliche Absturzsicherungen / Geländer in Stahl werden verzinkt.
→ Gemäß NÖ Bauordnung 2014 §66a Abs. (1) besteht keine Verpflichtung zur Errichtung einer Photovoltaikanlage, da die bebaute Fläche des Objekts < 300m² beträgt. Es wird trotzdem zur Steigerung der Energieeffizienz eine PV-Anlage mit 5kWp Leistung auf der südöstichen Dachfläche installiert.

SONSTIGES
→ Der Einstellraum für Kinderwägen und Mobilitätshilfen befindet sich im Ergeschoss.
→ Brieffachanlage befindet sich beim Hauseingangsbereich.

FASSADENGESTALTUNG
→ Die Entwässerung der Dachflächen erfolgt über Regenabfallrohre und Hängerinnen.
→ Blitzschutz wird an der Fassade gem. Ö-NORM ausgeführt.

EINREICHUNG gemäß NÖ Bauordnung 2014 und NÖ Bautechnikverordnung (inkl. OIB Richtlinien in der Fassung 2023)

Der Bestand wurde basiernd auf Geometerangaben von Bestandsplänen des Büros "Manfred Haslbauer - Ingenieurbüro für Vermessungswesen" (Plandatum: 14.11.2024) sowie den Bestandsplänen des Büros "Dipl.-Ing. Robert Wagner - Ingenieurkonsulent für Vermessungswesen" (Plandatum 09.07.2019), welche im Bauakt als Vermuteter Konsens aufliegen dargestellt.

AW 01	**ZIEGELWAND BESTAND**
1,00 cm	Bestehender Außenputz
44,0-47,0 cm	Ziegelmauerwerk 44,00 - 47,00 cm
1,50 cm	Bestehender Innenputz
40,3 - 70,3cm	**BAUTEIL GESAMT**

AW 02	**ZIEGELWAND BESTAND**
1,00 cm	Bestehender Außenputz
28,0-32,0 cm	Ziegelmauerwerk 44,00 - 47,00 cm
1,50 cm	Bestehender Innenputz
31,0-35,0cm	**BAUTEIL GESAMT**

AW 03	**GIBELWAND INNEN GEDÄMMT**
1,50 cm	Bestehender Außenputz
36,00 cm	Bestehendes Ziegelmauerwerk
1,50 cm	Bestehender Innenputz
1,00 cm	Luftschicht (Abstand)
10,00 cm	C-Profil 75 dazw. 10cm Mineralwolle Dampfbremse, sd Wert lt. Bauphysik, allseits angebunden
1,50 cm	1 x 1,50 GKF-Platte **EI30**
5,00 cm	UK / Lattung dazw. Mineralwolle - Installationsebene
1,25 cm	1 x 1,25 cm GKB-Platte
57,75cm	**BAUTEIL GESAMT**

AW 04	**KNIESTOCK INNEN GEDÄMMT**
1,50 cm	Bestehender Außenputz
45,00 cm	Bestehendes Ziegelmauerwerk
1,50 cm	Bestehender Innenputz
1,00 cm	Luftschicht (Abstand)
10,00 cm	C-Profil 75 dazw. 10cm Mineralwolle
0,10 cm	Dampfbremse, sd Wert lt. Bauphysik, allseits angebunden
1,50 cm	1 x 1,50 GKF-Platte **EI30**
62,25 cm	Luftschicht (Abstand)
5,00 cm	UK / Lattung dazw. Mineralwolle - Installationsebene
1,25 cm	1 x 1,25 cm GKB-Platte (GKBi in Nassräumen)
121,10 cm	**BAUTEIL GESAMT**

AW 05	**AUSSENWAND HOLZ-LEICHTBAU BLECH (GAUBE)**
0,80 cm	Blech Zink, gefalzt auf Strukturgewebe
2,40 cm	Vollholzschalung
5,00 cm	Konterlattung / Hinterlüftung mit Nageldichtband
0,10 cm	Diffusionsoffene UV-beständige Winddichtbahn lt. Bauphysik allseitig und alle Durchdringungen eingebunden
6,00 cm	Holzfaserdämmplatte
18,00 cm	Konstruktionsholz lt. Statik, fungizid behandelt dazw. Dämmung lt. Bauphysik
2,20 cm	OSB Platte, allseits luftdicht verklebt
1,50 cm	1 x 1,5 GKF-Platte **EI30**
5,00 cm	UK / Lattung dazw. Mineralwolle - Installationsebene
1,25 cm	1 x 1,25 cm GKB-Platte (GKBi in Nassräumen)
42,25 cm	**BAUTEIL GESAMT**

IW 01	**INNENWAND ZIEGEL TRAGEND BESTAND**
2,00 cm	Bestehender Innenputz
64,00 cm	Bestehendes Ziegelmauerwerk
2,00 cm	Bestehender Innenputz
64,00 cm	**BAUTEIL GESAMT** NICHT TEIL DER EINREICHUNG

IW 02	**INNENWAND ZIEGEL NICHTTRAGEND BESTAND**
1,50 cm	Bestehender Innenputz
45 - 49 cm	Bestehendes Ziegelmauerwerk
1,50 cm	Bestehender Innenputz
48 - 52 cm	**BAUTEIL GESAMT** NICHT TEIL DER EINREICHUNG

IW 03	**INNENWAND ZIEGEL NICHTTRAGEND BESTAND**
1,50 cm	Bestehender Innenputz
28 - 32 cm	Bestehendes Ziegelmauerwerk
1,50 cm	Bestehender Innenputz
31 - 35 cm	**BAUTEIL GESAMT** NICHT TEIL DER EINREICHUNG

IW 04	**INNENWAND BESTAND**
18 -20 cm	**BAUTEIL GESAMT** NICHT TEIL DER EINREICHUNG

IW 05	**INNENWAND BESTAND**
10,00 cm	**BAUTEIL GESAMT** NICHT TEIL DER EINREICHUNG

IW 06	**INNENWAND TROCKENBAU DOPPELT BEPLANKT**
2,50 cm	2 x 1,25 cm GKB-Platte (GKBi in Nassräumen)
7,50 cm	C-Profil dazw. Mineralwolle
2,50 cm	2 x 1,25 cm GKB-Platte (GKBi in Nassräumen)
12,50 cm	**BAUTEIL GESAMT**

IW 06 a	**INNENWAND TROCKENBAU DOPPELT BEPLANKT**
2,50 cm	2 x 1,25 cm GKB-Platte (GKBi in Nassräumen)
7,50 cm	C-Profil dazw. Mineralwolle
2,50 cm	Mineralwolle
7,50 cm	C-Profil dazw. Mineralwolle
2,50 cm	2 x 1,25 cm GKB-Platte (GKBi in Nassräumen)
22,50 cm	**BAUTEIL GESAMT**

IW 07	**WOHNUNGSTRENNWAND TROCKENBAU**
2,50 cm	2 x 1,25 cm GKF-Platte
7,50 cm	C-Profil dazw. Mineralwolle
1,25 cm	1 x 1,25 cm GKF- Platte PE- Folie allseits luftdicht verklebt
0,25cm	Luftraum (Abstand)
7,50 cm	C-Profil dazw. Mineralwolle
2,50 cm	2 x 1,25 cm GKB-Platte (GKBi in Nassräumen)
21,50 cm	**BAUTEIL GESAMT**

VS 01	**VORSATZSCHALE TROCKENBAU**
1,00 cm	Luftraum (Abstand)
5,00 cm	C-Profil dazw. Mineralwolle
1,25 cm	1 x 1,25 cm GKB-Platte (GKBi in Nassräumen)
7,25 cm	**BAUTEIL GESAMT**

VS 02	**VORSATZSCHALE TROCKENBAU NASSRAUM**
1,00 cm	Luftraum (Abstand)
7,50 cm	C-Profil dazw. Mineralwolle
2,50 cm	2 x 1,25 cm GKB-Platte (GKBi in Nassräumen)
11,00 cm	**BAUTEIL GESAMT**

VS 03	**VORSATZSCHALE TROCKENBAU WC**
4,00 cm	Luftraum (Abstand)
15,00 cm	C-Profil dazw. Mineralwolle
2,50 cm	2 x 1,25 cm GKB-Platte (GKBi in Nassräumen)
21,50 cm	**BAUTEIL GESAMT**

FB 01	**FUSSBODEN GEGEN ERDREICH EG**
	Bestehender Fußbodenbelag
	Bestehender Fußbodenaufbau
	Bestehende Betondecke
	Bestehender Unterbau
	NICHT TEIL DER EINREICHUNG

FB 01 a	**FUSSBODEN GEGEN ERDREICH EG NEU**
1,00 cm	Bodenbelag (Parkett / Fliese)
7,00 cm	Zementestrich, inkl. Randdämmstreifen 1cm PE-Folie seitlich hochgezogen bis Estrich OK
3,00 cm	Trittschalldämmplatten lt. Bauphysik Dampfbremse
5,00 cm	EPS - Schüttung zementgebunden
0,50 cm	Bituminöse Abdichtung
20,00 cm	Stahlbetonbodenplatte PE-Folie
10,00 cm	XPS
10,00 cm	Rollierung
56,50 cm	**BAUTEIL GESAMT**

FB 01 b	**FUSSBODEN GEGEN ERDREICH EG NEU**
1,00 cm	Bodenbelag (Parkett / Fliese)
7,00 cm	Zementestrich, inkl. Randdämmstreifen 1cm PE-Folie seitlich hochgezogen bis Estrich OK
3,00 cm	Trittschalldämmplatten lt. Bauphysik Dampfbremse
5,00 cm	EPS - Schüttung zementgebunden
0,50 cm	Bituminöse Abdichtung
25,00 cm	Bestehende Betonplatte
56,50 cm	**BAUTEIL GESAMT**

FB 02	**DECKE ÜBER EG**
	Bestehender Fußbodenbelag
	Bestehender Fußbodenaufbau
	Bestehende Holztramdecke
	Bestehender abgehängte Decke
	NICHT TEIL DER EINREICHUNG

FB 03	**DECKE Ü. 1.OG - DIPPELBAUMD. BESTAND / FBA NEU**
1,00 cm	Bodenbelag (Parkett / Fliese)
7,00 cm	Zementestrich mit FBH, inkl. Randdämmstreifen 1cm PE-Folie seitlich hochgezogen bis Estrich OK
3,00 cm	Trittschalldämmplatten lt. Bauphysik Dampfbremse
5,00 cm	EPS - Schüttung zementgebunden
7,00 cm	Verbundbeton
15,00 cm	Bestehende Dippelbaumdecke
4,00 cm	Bestehende Schilfmatte + Innenputz
8,50 cm	Bestehende abgehängte Decke
50,50 cm	**BAUTEIL GESAMT**

FB 04	**BALKON STAHLKONSTR. THERMISCH ENTKOPPELT**
2,50 cm	Holzbelag, rutsch- und witterungsfest
9,00 cm	Stellfüße Höhenausgleich 40-90 mm
0,80 cm	Gummigranulatplatte mit Trittschallfunktion
0,50 cm	Bituminöse Abdichtung 2-lagig, erste Lage selbstklebend
0,50 cm	Stahlblech lt. Statik, OK im Gefälle 2%
18,00 cm	Konstruktion aus Stahlträgern lt. Statik, Untersicht verkleidet mit MAX Exterior
31,30 cm	**BAUTEIL GESAMT**

DA 01	**DACHAUFBAU, ZIEGELDECKUNG (HAUPTDACH)**
3,00 cm	Keramischer Dachziegel
3,00 cm	Lattung 30/50 mm
5,00 cm	Konterlattung 50/50 mit Nageldichtband - Hinterlüftung
0,20 cm	Diffussionsoffene Dachauflegebahn - erhöhte Regensicherheit, sd- Wert lt. Bauphysik
2,40 cm	Vollholzschalung
24,00 cm	Holzsparren BESTAND nach innen aufgedoppelt lt. Statik dazw. Mineralwolle lt. Bauphysik
3,00 cm	UK / Lattung dazw. Mineralwolle lt. Bauphysik
0,10 cm	Feuchteadaptive Dampfbremse allseits verklebt lt. Bauphysik
1,50 cm	1x 1,50 cm GKF-Platte **(EI30)**
1,25 cm	1 x 1,25 cm GKB-Platte (GKBi in Nassräumen)
42,20 cm	**BAUTEIL GESAMT**

DA 02	**DACHAUFBAU, BLECHDECKUNG (GAUBE)**
0,80 cm	Zinkblech auf Strukturmatte
2,40 cm	Vollholzschalung
8,00 cm	Konterlattung 80/50 mit Nageldichtband - Hinterlüftung
0,20 cm	Diffussionsoffene Dachauflegebahn - erhöhte Regensicherheit, sd- Wert lt. Bauphysik
2,40 cm	Vollholzschalung
24,00 cm	Holzsparren lt. Statik dazw. Mineralwolle lt. Bauphysik
3,00 cm	UK / Lattung dazw. Mineralwolle lt. Bauphysik
0,10 cm	Feuchteadaptive Dampfbremse allseits verklebt lt. Bauphysik
1,50 cm	1 x 1,50 cm GKF-Platte **(EI30)**
42,40 cm	**BAUTEIL GESAMT**

DA 03	**BESTEHENDES PULTDACH SANIERT**
0,80 cm	Zinkblech auf Strukturmatte
2,40 cm	Vollholzschalung
8,00 cm	Konterlattung 80/50 mit Nageldichtband - Hinterlüftung
0,20 cm	Diffussionsoffene Dachauflegebahn - erhöhte Regensicherheit, sd- Wert lt. Bauphysik
2,40 cm	Vollholzschalung
18,00 cm	Bestehender Holzsparren dazw. Mineralwolle
0,10 cm	Feuchteadaptive Dampfbremse allseits verklebt lt. Bauphysik
2,40 cm	UK / Sparschalung
1,50 cm	1 x 1,50 cm GKF-Platte **(EI30)**
35,80 cm	**BAUTEIL GESAMT**

BAUTEILE

Nutzflächen	NUTZFLACHEN VR1	VR2	Bad/WC	WoKü/Zi	Kü	Zimmer 1	Zimmer 2	Zimmer 3	NF GESAMT	AUSSENFLACHEN Terrasse	Balkon	Außenflächen Gesamt
EG												
TOP 1 - Bestand	4,44 m²	3,81 m²	4,30 m²		9,61 m²	12,69 m²	9,05 m²	6,93 m²	**50,83 m²**			**0,00 m²**
TOP 2 - Bestand	2,67 m²		2,76 m²		8,48 m²	23,23 m²			**37,14 m²**			**0,00 m²**
TOP 3 - barrierefrei anpassbar			6,67 m²		13,97 m²	20,37 m²			**41,01 m²**	11,64 m²		**11,64 m²**
1. OG												
TOP 4 - Bestand	2,67 m²		3,66 m²		8,66 m²	19,45 m²	17,73 m²		**52,17 m²**			**0,00 m²**
TOP 5 - Bestand	2,68 m²		3,54 m²		8,77 m²	23,72 m²			**38,71 m²**			**0,00 m²**
TOP 6 - Bestand	1,91 m²		3,53 m²		11,57 m²	15,76 m²	8,99 m²		**41,76 m²**		8,04 m²	**8,04 m²**
1. DG												
TOP 7 - NEU	6,67 m²		3,89 m²	17,62 m²		13,56 m²	12,35 m²		**54,09 m²**		8,82 m²	**8,82 m²**
TOP 8 - gewerbliche Nutzung	7,49 m²		6,80 m²			19,73 m²	11,13 m²		**45,15 m²**			**0,00 m²**
SUMME WOHNFLÄCHE									**315,71 m²**			
SUMME GEWERBLICHE NUTZUNG									**45,15 m²**			
SUMME GESAMTE NUTZFLÄCHE									**360,86 m²**			**28,50 m²**

Allgemeinflächen	Gang	Gang	Einstellraum	Technik	Technik 2	AR / Lager	AR / Lager	AR / Lager	Gesamt	
Erdgeschoss	13,59 m²	8,54 m²	5,90 m²	9,11 m²	1,04 m²	1,75 m²			**39,93 m²**	
Hofgebäude						8,19 m²	9,28 m²	8,40 m²	**25,87 m²**	
1. Obergeschoss	8,04 m²					1,03 m²			**9,07 m²**	
Dachgeschoss	6,85 m²								**6,85 m²**	
SUMME ALLGEMEIN FLÄCHEN									*81,72 m²*	
SUMME NUTZFLÄCHE + ALLGEMEINFLÄCHEN									**442,58 m²**	**28,50 m²**

STATISTISCHE ANGABEN

GRUNDSTÜCKSGRÖSSE	**738,00 m²**
BEBAUTE FLÄCHE:	
WOHNHAUS	230,26 m²
HOFGEBÄUDE	34,63 m²
BEBAUTE FLÄCHE GESAMT	**264,89 m²**
ÜBERBAUTE FLÄCHE:	
WOHNHAUS	263,43 m²
HOFGEBÄUDE	37,04 m²
GESAMT	**300,47 m²**

BRUTTO-GESCHOSSFLÄCHE:	
WOHNHAUS EG	230,26 m²
WOHNHAUS 1. OG	201,18 m²
WOHNHAUS DG	194,01 m²
WOHNHAUS GESAMT	**625,45 m²**
HOFGEBÄUDE	34,63m²
BGF GESAMT	**660,08 m²**
BRUTTO-RAUMINHALT:	
WOHNHAUS	2.052,98 m³
HOFGEBÄUDE	110,06 m³
GESAMT	**2.163,04 m³**

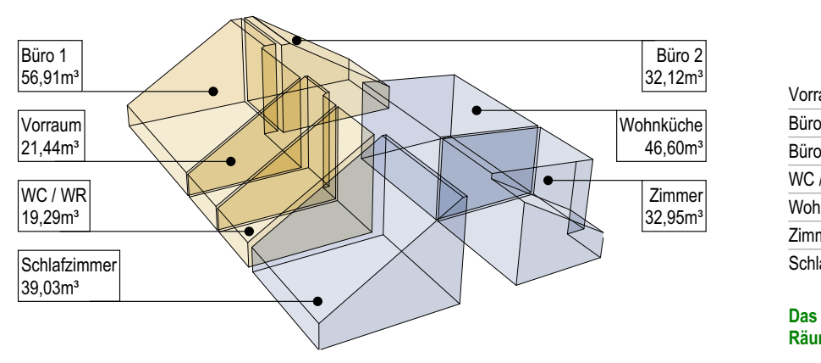

	Errechnetes Luftvolumen	Erforderliches Luftvolumen *(gem. OIB 3 Pkt. 11.2)*
Vorraum	21,44 m³	*7,49m² x 2,50m* = 18,725m³
Büro 1	56,91 m³	*19,73m² x 2,50m* = 49,325m³
Büro 2	32,12 m³	*11,13m² x 2,50m* = 27,825m³
WC / WR	19,29 m³	*6,80m² x 2,50m* = 17,00m³
Wohnküche	46,60 m³	*17,62m² x 2,50m* = 44,05m³
Zimmer	32,95 m³	*12,35m² x 2,50m* = 30,875m³
Schlafzimmer	39,03 m³	*13,56m² x 2,50m* = 33,90m³

Das erforderliche Luftvolumen gemäß OIB 3 wird in allen Räumen des Dachgeschoßes erreicht.

LEGENDE

- ☒ Wanddurchbruch
- ☒ Deckendurchbruch
- ◺ Bodenschlitz
- ◢ Bodendurchbruch
- ▼ OK Fertigbau
- ▲ UK Fertigbau
- ▽ OK Rohbau
- △ UK Rohbau
- ± 0,00 Höhenangabe einer waagrechten Fläche
- ±0,00 Höhenangabe eines Punktes in einem Bauwerk - Fertigmaß
- ±0,00 Höhenangabe eines Punktes in einem Bauwerk - Rohbaumaß

- ■ Bestand
- 🟨 Abbruch
- 🟩 unbewehrter Beton
- 🟩 bewehrter Beton
- 🟥 Mauerwerk
- 🟦 Stahl (allgemein)
- 🟫 Holz (allgemein)
- 🟪 Dämmstoff (hart)
- 🟧 Dämmstoff (weich)
- ▨ Dichtstoff (allgemein)
- 🟦 Glas
- 🟦 Gipskarton GKF (Brandschutz)
- 🟧 Gipskarton GKB - im Nassraum GKBi
- ▨ Grünfläche
- ▨ Erdmaterial (allgemein)

- — Medien
- — Fernwärme
- — Gas
- — Strom
- — Heizung
- — Regenwasser
- — Schmutzwasser
- — Wasser
- - - Grundgrenze
- — — Baufluchtlinie
- — — Baulinie
- ━ Widmungsgrenze

BGF	Bruttogesamtfläche
HNF / NNF	Haupt- Nebennutzfläche
KG	Kochgelegenheit

Höhenbezugs- und Maßangaben

DOK	Deckenoberkante
DUK	Deckenunterkante
FBOK	Fußbodenoberkante
FDOK	Fundamentoberkante
FDUK	Fundamentunterkante
RDOK	Deckenoberkante
RDUK	Deckenunterkante
RH	lichte Raumhöhe
GH	Geschoßhöhe
OK	Oberkante
OS	Oberseite
UK	Unterkante
US	Unterseite
VK	Vorderkante
STUK	Sturzunterkante (Rohbaumaß)
STH	Sturzhöhe gemessen von STUK bis DUK (Rohbaumaß)
RPH	Rohbauparapethöhe
FPH	fertige Parapethöhe (FBOK bis OK Fensterbank Innen)

Rauch-, Abgas- und Luftfänge, Schächte

PT	Putztürchen
L	Lüftungsschacht
ABL	Abluft
ZUL	Zuluft
DBA	Druckbelüftungsanlage
DRE	Druckregeleinheit
BSK	Brandsschutzklappe
RAE	Rauchabzugseinrichtung lt. OIB 2
SEL	Schachtentlüftung

Öffnungen und deren Abschlüsse

WD	Wanddurchbruch
DD	Deckendurchbruch
FBD	Fußbodendurchbruch
FDD	Fundamentdurchbruch
WS	Wandschlitz
WA	Wandaussparung
DA	Deckenaussparung
FBA	Fußbodenaussparung
RBL	Rohbaulichte
AL	Architekturlichte
STL	Stocklichte
GL	Glaslichte
STAM	Stockaußenmaß
DF	Drehflügel
DKF	Drehkippflügel
KF	Kippflügel
SF	Schiebeflügel
SWF	Schwingflügel
WF	Wendeflügel
HT	Hebetüre
HST	Hebeschiebetüre
DL	Durchgangslichte
OL	Oberlichte
FIX	Fixverglasung
GGT	Ganzglastüre
VSG	Verbund-Sicherheitsglas
ESG	Einscheiben-Sicherheitsglas

EI2 30-C-, EI2 60-C-und EI2 90-C
Feuerschutztüren mit Angabe der Feuerwiderstandsklasse
(gemäß ÖNORM B 3850 und ÖNORM B 3807)

GT	gasdichte Türe
DT	Drucktüre
S 200	Rauchabschluss
C	Selbstschließend
FLS	Freilaufschließer

EINREICHPLAN

PARIE **A B C**

Bauvorhaben
VÖSL100
Dachgeschoßausbau samt Errichtung einer Gaupe, Balkonzubau,
Wohnungsadaptierung sowie Teilabbruch des Hofgebäudes

2500 Baden, Vöslauerstraße 100

Katastralgemeinde 4025 Rauhenstein
EZ: 2412
GstNr.: .424

Übersicht

Bebauungsplan

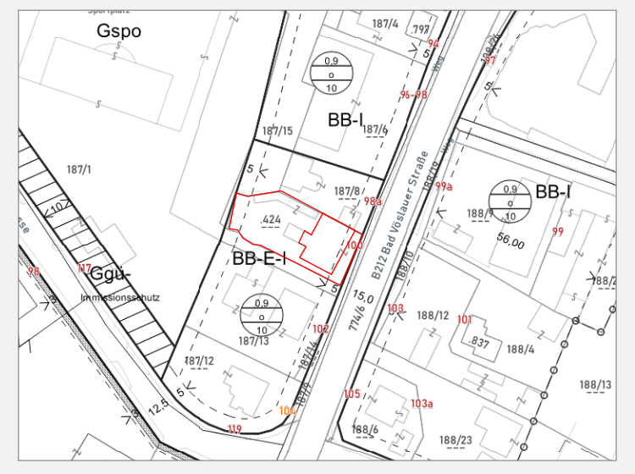

Behörde
Stadtgemeinde Baden
Hauptplatz 1
A - 2500 Baden bei Wien

Grundeigentümer

Bauwerber / Auftraggeber

c/o BS Real 360 GmbH
Marokkanergasse 22, A - 1030 Wien

ARTMÜLLER ARCHITEKTEN
ZIVILTECHNIKER GMBH
Stolberggasse 34|26 A-1050 Wien
t [+43] 01 . 581 40 83 f [+43] 01. 581 40 83 99 office@artmueller.eu

Planinhalt
EINREICHPLAN

Maßstab	Gez	Datum	Plannr.	Index
1:100, 1:500	ML	25-08-2026	VÖSL100_40_01	

Erstellt, am 16.10.2026