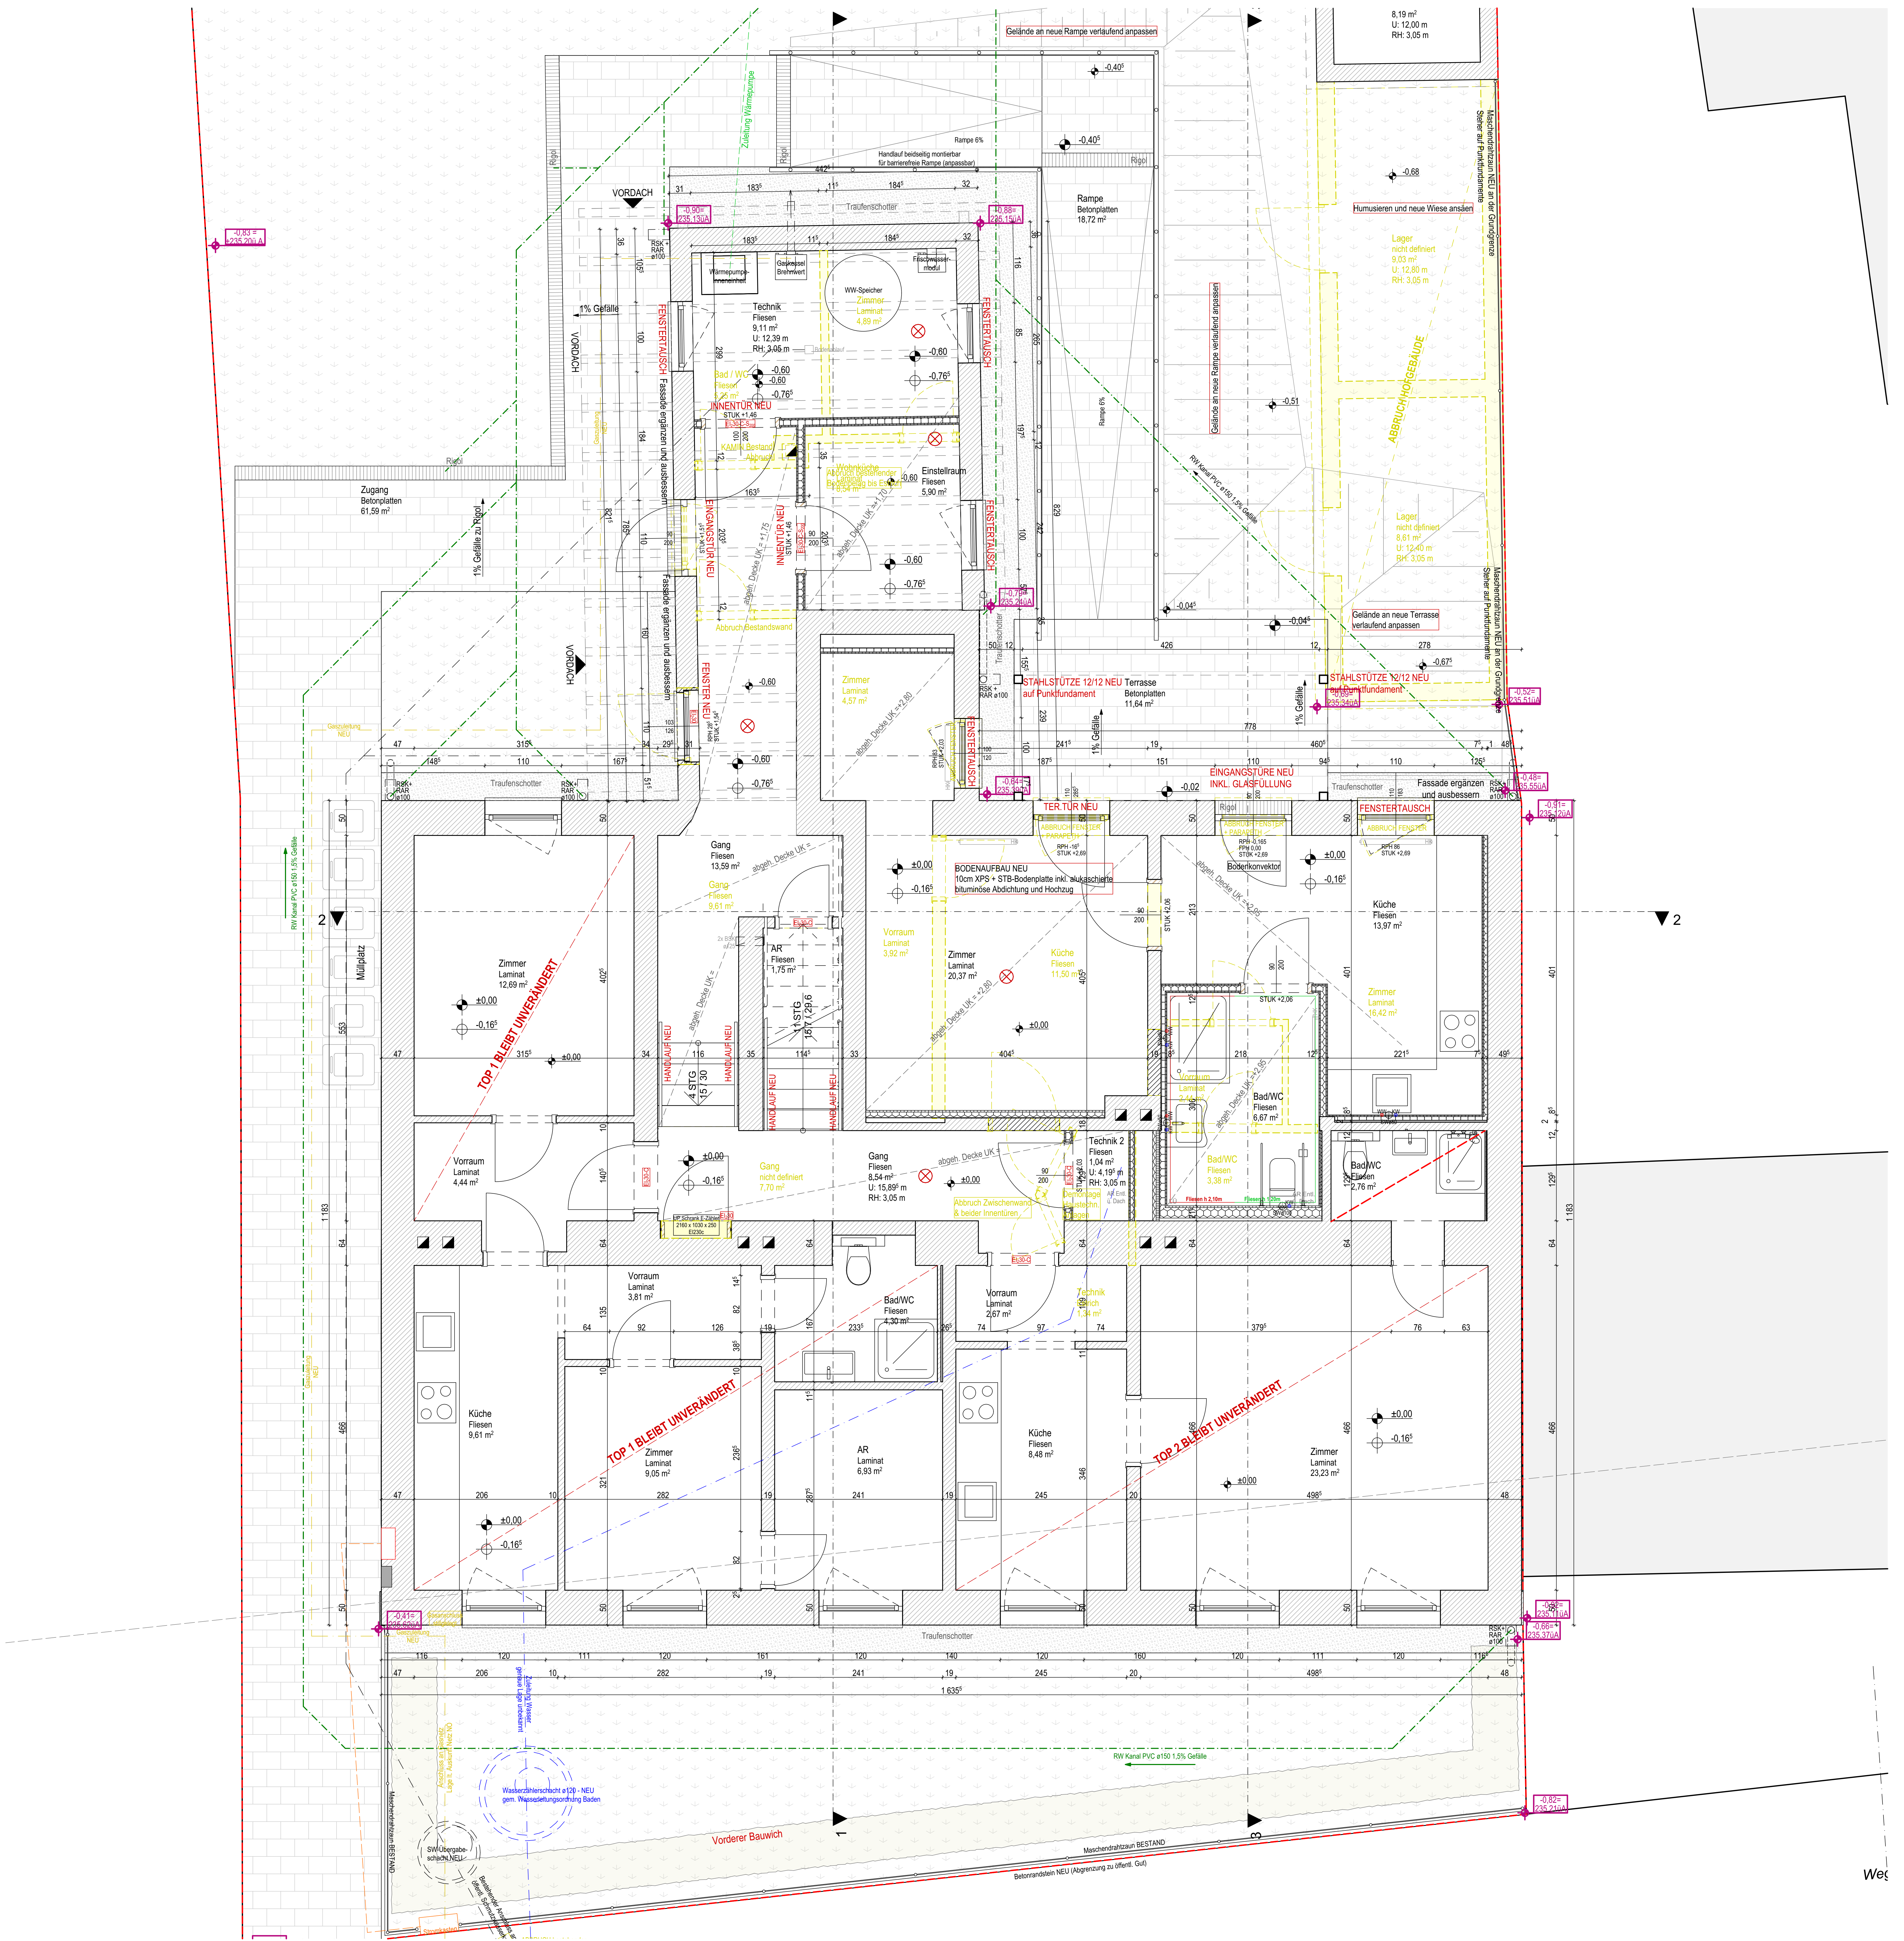

ERDGESCHOSS | 1:50

LEGENDE

☒	Wanddurchbruch
⬚	Deckendurchbruch
◸	Bodenschlitz
◢	Bodendurchbruch
▼	OK Fertigbau
▲	UK Fertigbau
▽	OK Rohbau
△	UK Rohbau
± 0,00	Höhenangabe einer waagrechten Fläche
±0,00	Höhenangabe eines Punktes in einem Bauwerk - Fertigmaß
±0,00	Höhenangabe eines Punktes in einem Bauwerk - Rohbaumaß
BGF	Bruttogesamtfläche
HNF / NNF	Haupt- Nebennutzfläche

▨	Mauerwerk (wärmedämmend)
▨	Mauerwerk (nicht wärmedämmend)
▨	unbewehrter Beton
▨	bewehrter Beton
▦	Betonfertigteil
▤	Stein
▨	Stahl (allgemein)
▨	Holz (allgemein)
▨	Holzwerkstoffe
▩	Dämmstoff (hart)
▩	Dämmstoff (weich)
▩	Kunststoff (allgemein)
▚	Dichtstoff (allgemein)
▥	Gips (Gipskartonplatte)
▥	Gipskartonplatte Brandschutz
☐	Erdmaterial (allgemein)
⬜	Bestand
🟨	Abbruch
🟥	Neubau

—	Medien
—	Fernwärme
—	Gas
—	Strom
—	Heizung
—	Regenwasser
—	Schmutzwasser
—	Wasser
—	Blech
- - -	Abdichtung
- - -	Folie
– – –	Dampfsperre, -bremse

Höhenbezugs- und Maßangaben

DOK	Deckenoberkante
DOS	Deckenoberseite
DUK	Deckenunterkante
DUS	Deckenunterseite
DUF	Deckenunterkante (fertige Untersicht)
FBOK	Fußbodenoberkante
OFF	Oberfläche des fertigen Fußbodens
FDOK	Fundamentoberkante
FDOS	Fundamentoberseite
FDUK	Fundamentunterkante
FDUS	Fundamentunterseite
RH	lichte Raumhöhe
GH	Geschoßhöhe
OK	Oberkante
OS	Oberseite
UK	Unterkante
US	Unterseite
STUK	Sturzunterkante (Rohbaumaß)
STH	Sturzhöhe gemessen von STUK bis DUK (Rohbaumaß)
RPH	Rohbauparapethöhe
FPH	fertige Parapethöhe (FBOK bis OK Fensterbank Innen)

Rauch-, Abgas- und Luftfänge, Schächte

L	Lüftungsschacht
PT	Putztürchen
PS	Putzstück
KT	Kehrtürchen
ABL	Abluft
ZUL	Zuluft
DBA	Druckbelüftungsanlage
DES	Druckentlastungsschacht
BÖ	Belüftungsöffnung
ÜÖ	Überströmöffnung
AÖ	Abströmöffnung mit Überdruckentlastungsorgan
BSK	Brandsschutzklappe
FBHV	Fussbodenheizungsverteiler
E-Verteiler	Elektroverteiler

Öffnungen und deren Abschlüsse

WD	Wanddurchbruch
DD	Deckendurchbruch
FBD	Fußbodendurchbruch
FDD	Fundamentdurchbruch
WS	Wandschlitz
WA	Wandaussparung
DA	Deckenaussparung
FBA	Fußbodenaussparung
RBL	Rohbaulichte
AL	Architekturlichte
STL	Stocklichte
GL	Glaslichte
STAM	Stockaußenmaß
DL	Durchgangslichte
GGT	Ganzglastüre
MGT	Metallgittertür
HT	Hebetüre
HST	Hebeschiebetüre
T	Türe
AT	Allgemeintüre
ET	Eingangstüre
WET	Wohnungseingangstür
IT	Innentür
DF	Drehflügel
DKF	Drehkippflügel
SF	Schiebe-Fenster
SWF	Schwingflügel
WF	Wendeflügel
K	Kippfenster
OL	Oberlichte
DF	Dachfächenfenster
PFR	Pfostenriegelkonstruktion
FE	Fenster
FT	Fenstertüre
R	Rechtsöffnend
L	Linksöffnend
FIX	Fixverglasung
VSG	Verbund-Sicherheitsglas
ESG	Einscheiben-Sicherheitsglas

Drehflügel
Drehkippflügel
Kippflügel
Fenstertüre

EI2 30-C-, EI2 60-C-und EI2 90-C
Feuerschutztüren mit Angabe der Feuerwiderstandsklasse
(gemäß ÖNORM B 3850 und ÖNORM B 3807)

GT	gasdichte Türe
DT	Drucktüre
S 200	Rauchabschluss
S 200	Rauchabschluss
C	Selbstschließend
FLS	Freilaufschließer
LVfTÖ	Lehrverrohrung für Türöffner
elTÖ	elektrischer Türöffner

AUSFÜHRUNG POLIERPLAN GESAMT

Bauvorhaben
VÖSL100

2500 Baden, Vöslauerstraße 100

XXX

Katastralgemeinde 4025 Rauhenstein
EZ: 2412
GstNr.: .424

Diese Zeichnung bzw. Ausarbeitung sowie deren Daten auf Datenträgern sind geistiges Eigentum des Erstellers Arch. Artmüller Georg. Jede Benützung, Veröffentlichung,Vervielfältigung jeglicher Art oder Weitergabe an Dritte bedarf der schriftlichen Zustimmung durch Architekt Artmüller.

Durch die Übernahme dieses Planes akzeptiert die ausführende Firma bzw. Person die darauf dargestellten Anordnungen. Geschriebene Planmaße auf dieser Zeichnunghaben Vorrang gegenüber gezeichneten Dimensionen. Der Auftragnehmer verpflichtet sich **vor** Arbeitsbeginn alle Maße und Bedingungen im Zusammenhang mit seinerArbeit auf der Baustelle verantwortlich zu überprüfen.

Abweichungen gegenüber dargestellten oder schriftlich vereinbarten Anordnungen müssen Architekt Artmüller und der Bauleitung unverzüglich schriftlich mitgeteiltwerden. Vor Arbeitsbeginn sind dem Architekten gültige Werkzeichnungen zur Genehmigung vorzulegen.

NATURMASSE SIND ZU NEHMEN, KOTEN ZU PRÜFEN

Index	Datum	Bearbeiter	Änderung

VORABZUG
16. 10. 2026

Index	Änderung	Datum

Grundeigentümer

Bauwerber / Auftraggeber

ARTMÜLLER ARCHITEKTEN
ZIVILTECHNIKER GMBH
Stolberggasse 34|26 A-1050 Wien
t [+43] 01 . 581 40 83 f [+43] 01. 581 40 83 99 office@artmueller.eu

Planinhalt
Erdgeschoss

Maßstab	Gez	Datum	Plannr.	Index
1:50	LM	16-10-2026	VÖSL100_50_01	01

Erstellt, am 11.11.2026

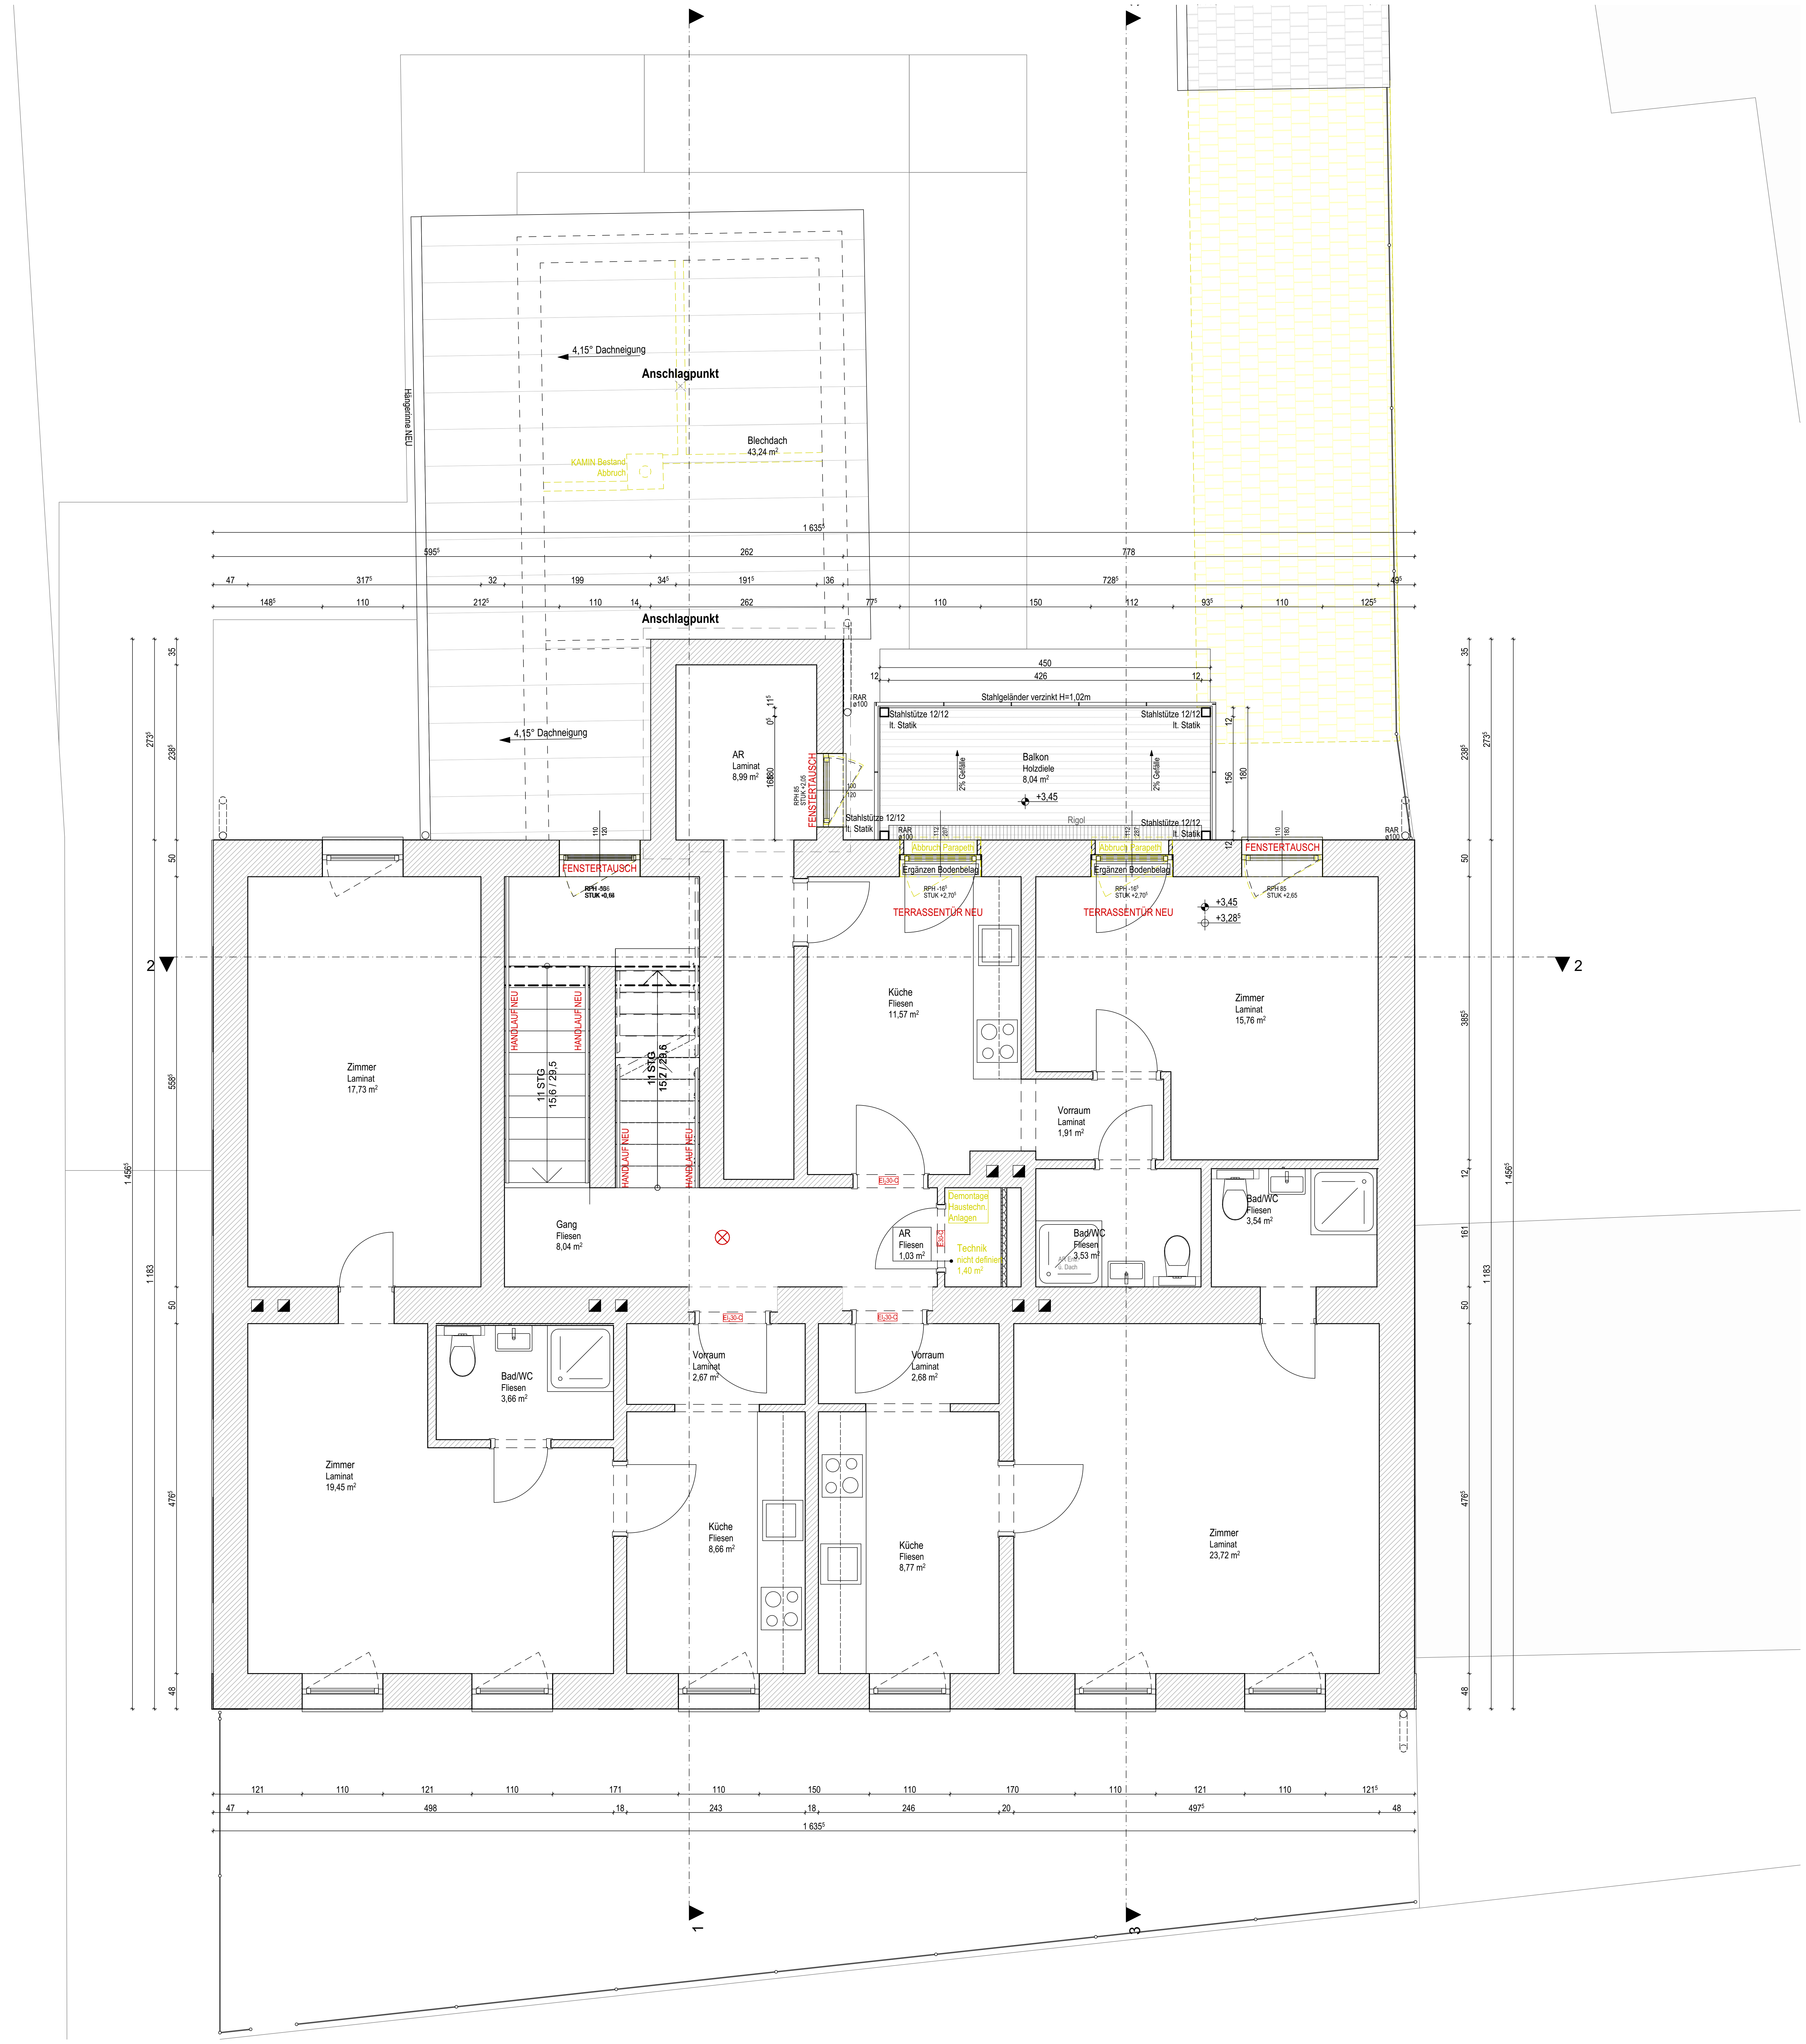

OBERGESCHOSS | 1:50

LEGENDE

☒	Wanddurchbruch
	Deckendurchbruch
	Bodenschlitz
	Bodendurchbruch
▼	OK Fertigbau
▲	UK Fertigbau
▽	OK Rohbau
△	UK Rohbau
± 0,00	Höhenangabe einer waagrechten Fläche
±0,00	Höhenangabe eines Punktes in einem Bauwerk - Fertigmaß
±0,00	Höhenangabe eines Punktes in einem Bauwerk - Rohbaumaß
BGF	Bruttogesamtfläche
HNF / NNF	Haupt- Nebennutzfläche

▨	Mauerwerk (wärmedämmend)
▨	Mauerwerk (nicht wärmedämmend)
▨	unbewehrter Beton
▨	bewehrter Beton
▦	Betonfertigteil
▤	Stein
▨	Stahl (allgemein)
▨	Holz (allgemein)
▨	Holzwerkstoffe
▩	Dämmstoff (hart)
▩	Dämmstoff (weich)
▩	Kunststoff (allgemein)
■	Dichtstoff (allgemein)
▥	Gips (Gipskartonplatte)
▥	Gipskartonplatte Brandschutz
☐	Erdmaterial (allgemein)
⬜	Bestand
🟨	Abbruch
🟥	Neubau

—	Medien
—	Fernwärme
—	Gas
—	Strom
—	Heizung
—	Regenwasser
—	Schmutzwasser
—	Wasser
—	Blech
- - -	Abdichtung
- - -	Folie
- - -	Dampfsperre, -bremse

Höhenbezugs- und Maßangaben

DOK	Deckenoberkante
DOS	Deckenoberseite
DUK	Deckenunterkante
DUS	Deckenunterseite
DUF	Deckenunterkante (fertige Untersicht)
FBOK	Fußbodenoberkante
OFF	Oberfläche des fertigen Fußbodens
FDOK	Fundamentoberkante
FDOS	Fundamentoberseite
FDUK	Fundamentunterkante
FDUS	Fundamentunterseite
RH	lichte Raumhöhe
GH	Geschoßhöhe
OK	Oberkante
OS	Oberseite
UK	Unterkante
US	Unterseite
STUK	Sturzunterkante (Rohbaumaß)
STH	Sturzhöhe gemessen von STUK bis DUK (Rohbaumaß)
RPH	Rohbauparapethöhe
FPH	fertige Parapethöhe (FBOK bis OK Fensterbank Innen)

Rauch-, Abgas- und Luftfänge, Schächte

L	Lüftungsschacht
PT	Putztürchen
PS	Putzstück
KT	Kehrtürchen
ABL	Abluft
ZUL	Zuluft
DBA	Druckbelüftungsanlage
DES	Druckentlastungsschacht
BÖ	Belüftungsöffnung
ÜÖ	Überströmöffnung
AÖ	Abströmöffnung mit Überdruckentlastungsorgan
BSK	Brandsschutzklappe
FBHV	Fussbodenheizungsverteiler
E-Verteiler	Elektroverteiler

Öffnungen und deren Abschlüsse

WD	Wanddurchbruch
DD	Deckendurchbruch
FBD	Fußbodendurchbruch
FDD	Fundamentdurchbruch
WS	Wandschlitz
WA	Wandaussparung
DA	Deckenaussparung
FBA	Fußbodenaussparung
RBL	Rohbaulichte
AL	Architekturlichte
STL	Stocklichte
GL	Glaslichte
STAM	Stockaußenmaß
DL	Durchgangslichte
GGT	Ganzglastüre
MGT	Metallgittertür
HT	Hebetüre
HST	Hebeschiebetüre
T	Türe
AT	Allgemeintüre
ET	Eingangstüre
WET	Wohnungseingangstür
IT	Innentür
DF	Drehflügel
DKF	Drehkippflügel
SF	Schiebe-Fenster
SWF	Schwingflügel
WF	Wendeflügel
K	Kippfenster
OL	Oberlichte
DF	Dachfächenfenster
PFR	Pfostenriegelkonstruktion
FE	Fenster
FT	Fenstertüre
R	Rechtsöffnend
L	Linksöffnend
FIX	Fixverglasung
VSG	Verbund-Sicherheitsglas
ESG	Einscheiben-Sicherheitsglas

Drehflügel
Drehkippflügel
Kippflügel
Fenstertüre

EI2 30-C-, EI2 60-C-und EI2 90-C
Feuerschutztüren mit Angabe der Feuerwiderstandsklasse
(gemäß ÖNORM B 3850 und ÖNORM B 3807)

GT	gasdichte Türe
DT	Drucktüre
S 200	Rauchabschluss
S 200	Rauchabschluss
C	Selbstschließend
FLS	Freilaufschließer
LVfTÖ	Lehrverrohrung für Türöffner
elTÖ	elektrischer Türöffner

AUSFÜHRUNG POLIERPLAN GESAMT

Bauvorhaben
VÖSL100
2500 Baden, Vöslauerstraße 100

XXX

Katastralgemeinde 4025 Rauhenstein
EZ: 2412
GstNr.: .424

Diese Zeichnung bzw. Ausarbeitung sowie deren Daten auf Datenträgern sind geistiges Eigentum des Erstellers Arch. Artmüller Georg. Jede Benützung, Veröffentlichung,Vervielfältigung jeglicher Art oder Weitergabe an Dritte bedarf der schriftlichen Zustimmung durch Architekt Artmüller.

Durch die Übernahme dieses Planes akzeptiert die ausführende Firma bzw. Person die darauf dargestellten Anordnungen. Geschriebene Planmaße auf dieser Zeichnunghaben Vorrang gegenüber gezeichneten Dimensionen. Der Auftragnehmer verpflichtet sich **vor** Arbeitsbeginn alle Maße und Bedingungen im Zusammenhang mit seinerArbeit auf der Baustelle verantwortlich zu überprüfen.

Abweichungen gegenüber dargestellten oder schriftlich vereinbarten Anordnungen müssen Architekt Artmüller und der Bauleitung unverzüglich schriftlich mitgeteiltwerden. Vor Arbeitsbeginn sind dem Architekten gültige Werkzeichnungen zur Genehmigung vorzulegen.

NATURMASSE SIND ZU NEHMEN, KOTEN ZU PRÜFEN

VORABZUG
15.09.2026

Index	Datum	Bearbeiter	Änderung

Index	Änderung	Datum

Grundeigentümer

Bauwerber / Auftraggeber

ARTMÜLLER ARCHITEKTEN
ZIVILTECHNIKER GMBH
Stolberggasse 34|26 A-1050 Wien
t [+43] 01 . 581 40 83 f [+43] 01. 581 40 83 99 office@artmueller.eu

Planinhalt
Obergeschoß

Maßstab	Gez	Datum	Plannr.	Index
1:50	LM	16-10-2026	VÖSL100_50_02	01

Erstellt, am 11.11.2026

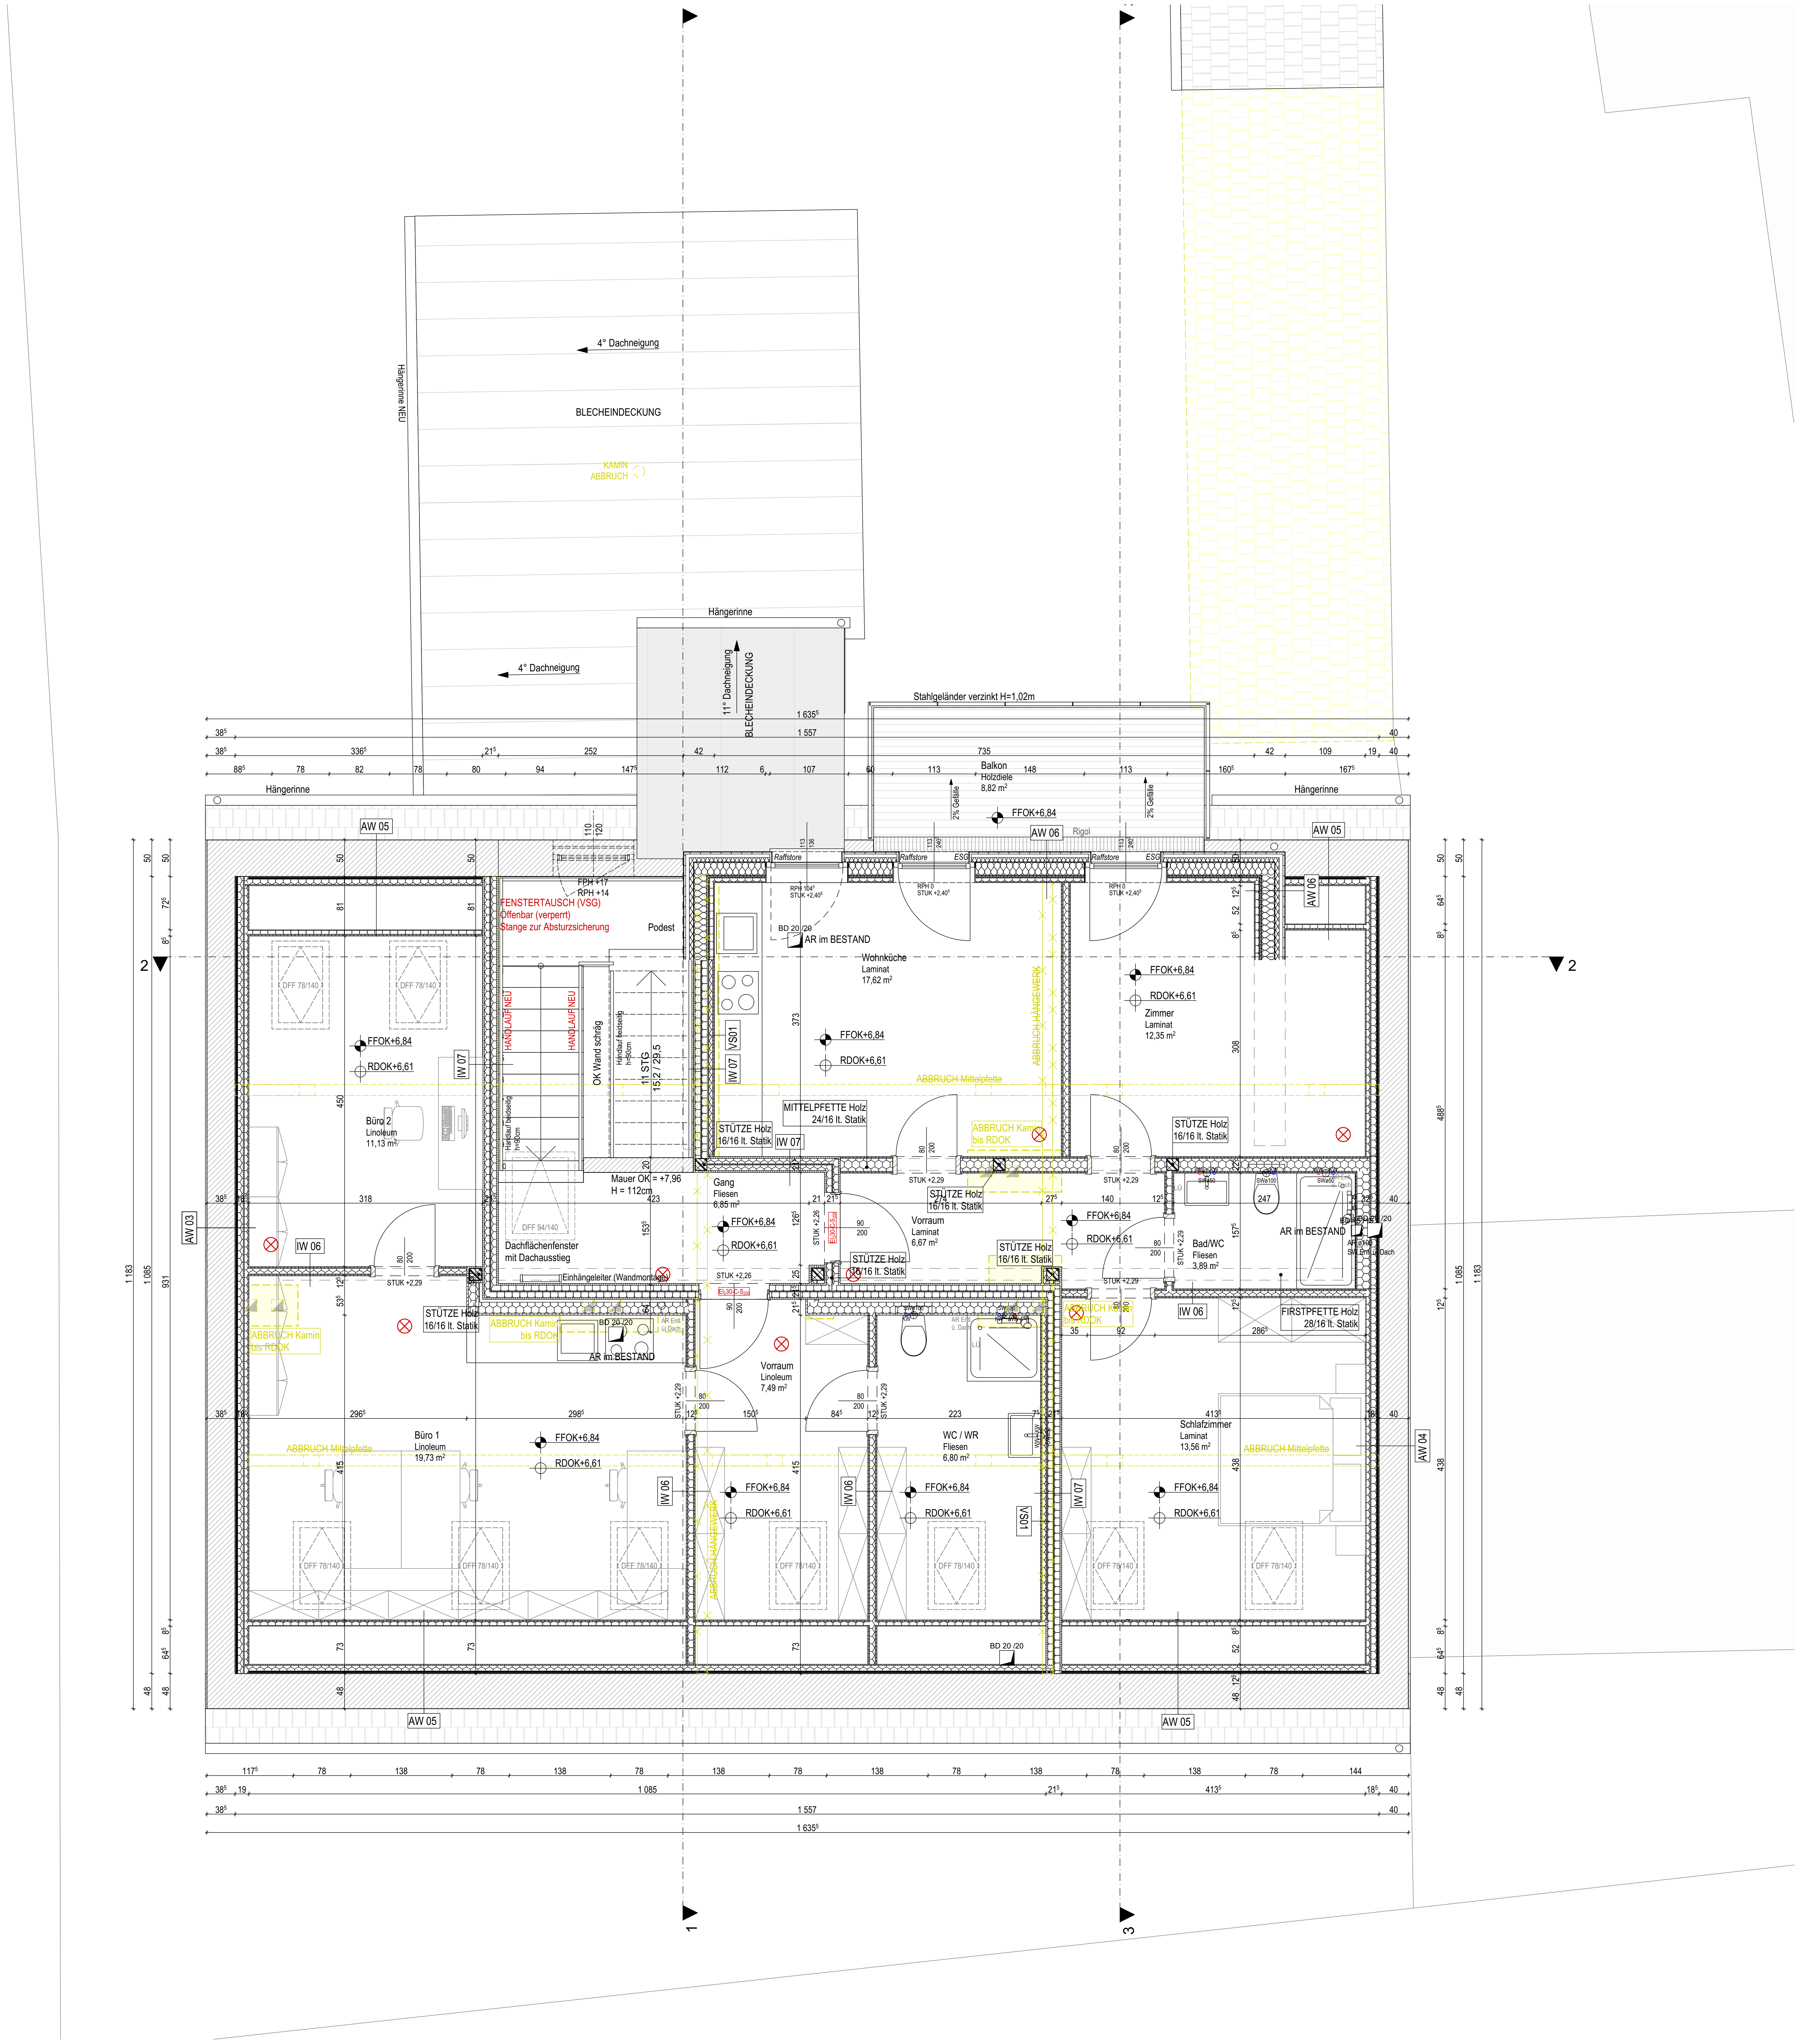

DACHGESCHOSS | 1:50

LEGENDE

☒	Wanddurchbruch
⬚	Deckendurchbruch
◺	Bodenschlitz
◢	Bodendurchbruch
▼	OK Fertigbau
▲	UK Fertigbau
▽	OK Rohbau
△	UK Rohbau
± 0,00	Höhenangabe einer waagrechten Fläche
±0,00	Höhenangabe eines Punktes in einem Bauwerk - Fertigmaß
±0,00	Höhenangabe eines Punktes in einem Bauwerk - Rohbaumaß
BGF	Bruttogesamtfläche
HNF / NNF	Haupt- Nebennutzfläche

▨	Mauerwerk (wärmedämmend)
▨	Mauerwerk (nicht wärmedämmend)
▨	unbewehrter Beton
▨	bewehrter Beton
▦	Betonfertigteil
▤	Stein
▨	Stahl (allgemein)
▨	Holz (allgemein)
▨	Holzwerkstoffe
▩	Dämmstoff (hart)
▩	Dämmstoff (weich)
▩	Kunststoff (allgemein)
▚	Dichtstoff (allgemein)
▥	Gips (Gipskartonplatte)
▥	Gipskartonplatte Brandschutz
☐	Erdmaterial (allgemein)
⬜	Bestand
🟨	Abbruch
🟥	Neubau

—	Medien
—	Fernwärme
—	Gas
—	Strom
—	Heizung
—	Regenwasser
—	Schmutzwasser
—	Wasser
—	Blech
- - -	Abdichtung
- - -	Folie
– – –	Dampfsperre, -bremse

Höhenbezugs- und Maßangaben

DOK	Deckenoberkante
DOS	Deckenoberseite
DUK	Deckenunterkante
DUS	Deckenunterseite
DUF	Deckenunterkante (fertige Untersicht)
FBOK	Fußbodenoberkante
OFF	Oberfläche des fertigen Fußbodens
FDOK	Fundamentoberkante
FDOS	Fundamentoberseite
FDUK	Fundamentunterkante
FDUS	Fundamentunterseite
RH	lichte Raumhöhe
GH	Geschoßhöhe
OK	Oberkante
OS	Oberseite
UK	Unterkante
US	Unterseite
STUK	Sturzunterkante (Rohbaumaß)
STH	Sturzhöhe gemessen von STUK bis DUK (Rohbaumaß)
RPH	Rohbauparapethöhe
FPH	fertige Parapethöhe (FBOK bis OK Fensterbank Innen)

Rauch-, Abgas- und Luftfänge, Schächte

L	Lüftungsschacht
PT	Putztürchen
PS	Putzstück
KT	Kehrtürchen
ABL	Abluft
ZUL	Zuluft
DBA	Druckbelüftungsanlage
DES	Druckentlastungsschacht
BÖ	Belüftungsöffnung
ÜÖ	Überströmöffnung
AÖ	Abströmöffnung mit Überdruckentlastungsorgan
BSK	Brandsschutzklappe
FBHV	Fussbodenheizungsverteiler
E-Verteiler	Elektroverteiler

Öffnungen und deren Abschlüsse

WD	Wanddurchbruch
DD	Deckendurchbruch
FBD	Fußbodendurchbruch
FDD	Fundamentdurchbruch
WS	Wandschlitz
WA	Wandaussparung
DA	Deckenaussparung
FBA	Fußbodenaussparung
RBL	Rohbaulichte
AL	Architekturlichte
STL	Stocklichte
GL	Glaslichte
STAM	Stockaußenmaß
DL	Durchgangslichte
GGT	Ganzglastüre
MGT	Metallgittertür
HT	Hebetüre
HST	Hebeschiebetüre
T	Türe
AT	Allgemeintüre
ET	Eingangstüre
WET	Wohnungseingangstür
IT	Innentür
DF	Drehflügel
DKF	Drehkippflügel
SF	Schiebe-Fenster
SWF	Schwingflügel
WF	Wendeflügel
K	Kippfenster
OL	Oberlichte
DF	Dachfächenfenster
PFR	Pfostenriegelkonstruktion
FE	Fenster
FT	Fenstertüre
R	Rechtsöffnend
L	Linksöffnend
FIX	Fixverglasung
VSG	Verbund-Sicherheitsglas
ESG	Einscheiben-Sicherheitsglas

Drehflügel
Drehkippflügel
Kippflügel
Fenstertüre

EI2 30-C-, EI2 60-C-und EI2 90-C
Feuerschutztüren mit Angabe der Feuerwiderstandsklasse
(gemäß ÖNORM B 3850 und ÖNORM B 3807)

GT	gasdichte Türe
DT	Drucktüre
S 200	Rauchabschluss
S 200	Rauchabschluss
C	Selbstschließend
FLS	Freilaufschließer
LVfTÖ	Lehrverrohrung für Türöffner
elTÖ	elektrischer Türöffner

AUSFÜHRUNG POLIERPLAN GESAMT

Bauvorhaben
VÖSL100

2500 Baden, Vöslauerstraße 100

XXX

Katastralgemeinde 4025 Rauhenstein
EZ: 2412
GstNr.: .424

Diese Zeichnung bzw. Ausarbeitung sowie deren Daten auf Datenträgern sind geistiges Eigentum des Erstellers Arch. Artmüller Georg. Jede Benützung, Veröffentlichung,Vervielfältigung jeglicher Art oder Weitergabe an Dritte bedarf der schriftlichen Zustimmung durch Architekt Artmüller.

Durch die Übernahme dieses Planes akzeptiert die ausführende Firma bzw. Person die darauf dargestellten Anordnungen. Geschriebene Planmaße auf dieser Zeichnunghaben Vorrang gegenüber gezeichneten Dimensionen. Der Auftragnehmer verpflichtet sich **vor** Arbeitsbeginn alle Maße und Bedingungen im Zusammenhang mit seinerArbeit auf der Baustelle verantwortlich zu überprüfen.

Abweichungen gegenüber dargestellten oder schriftlich vereinbarten Anordnungen müssen Architekt Artmüller und der Bauleitung unverzüglich schriftlich mitgeteiltwerden. Vor Arbeitsbeginn sind dem Architekten gültige Werkzeichnungen zur Genehmigung vorzulegen.

NATURMASSE SIND ZU NEHMEN, KOTEN ZU PRÜFEN

VORABZUG
15. 09. 2026

Index	Datum	Bearbeiter	Änderung

Index	Änderung	Datum

Grundeigentümer

Bauwerber / Auftraggeber

ARTMÜLLER ARCHITEKTEN
ZIVILTECHNIKER GMBH
Stolberggasse 34|26 A-1050 Wien
t [+43] 01 . 581 40 83 f [+43] 01. 581 40 83 99 office@artmueller.eu

Planinhalt
Dachgeschoß

Maßstab	Gez	Datum	Plannr.	Index
1:50	LM	16-10-2026	VÖSL100_50_03	01

Erstellt, am 11.11.2026

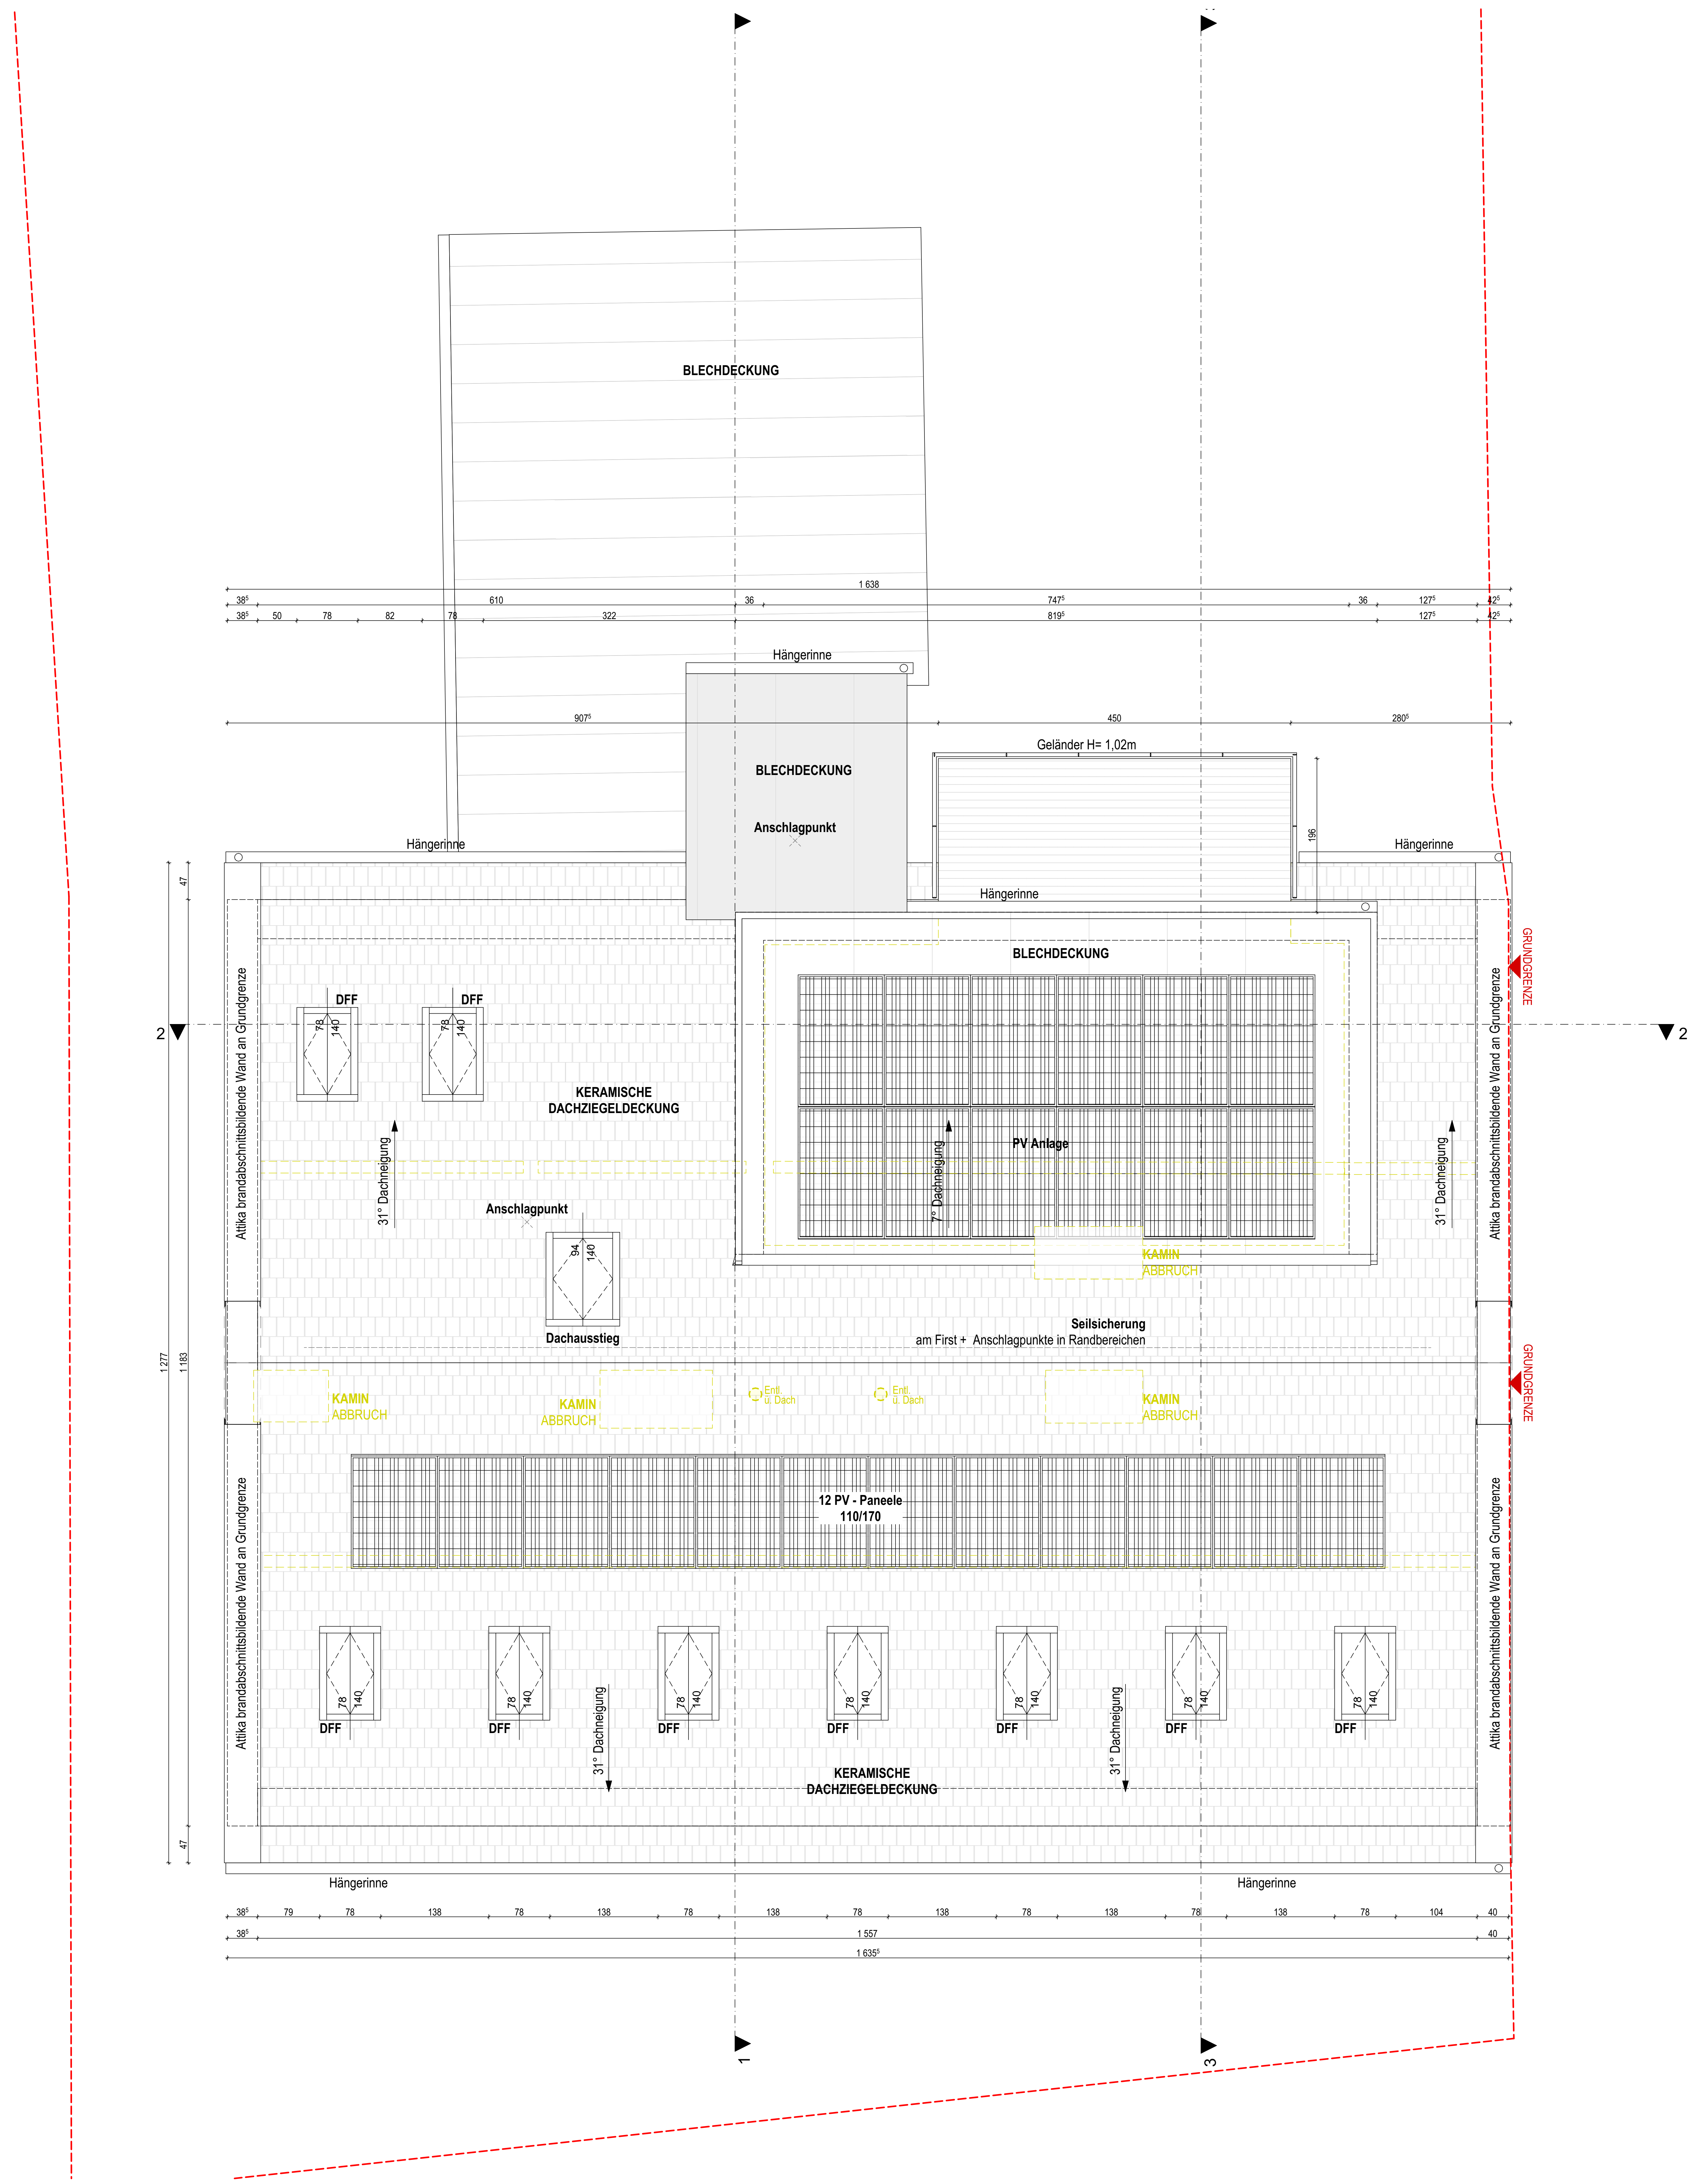

DACHDRAUFSICHT | 1:50

LEGENDE

☒	Wanddurchbruch
	Deckendurchbruch
	Bodenschlitz
	Bodendurchbruch
▼	OK Fertigbau
▲	UK Fertigbau
▽	OK Rohbau
△	UK Rohbau
± 0,00	Höhenangabe einer waagrechten Fläche
±0,00	Höhenangabe eines Punktes in einem Bauwerk - Fertigmaß
±0,00	Höhenangabe eines Punktes in einem Bauwerk - Rohbaumaß
BGF	Bruttogesamtfläche
HNF / NNF	Haupt- Nebennutzfläche

▨	Mauerwerk (wärmedämmend)
▨	Mauerwerk (nicht wärmedämmend)
▨	unbewehrter Beton
▨	bewehrter Beton
▦	Betonfertigteil
▤	Stein
▨	Stahl (allgemein)
▨	Holz (allgemein)
▨	Holzwerkstoffe
▩	Dämmstoff (hart)
▩	Dämmstoff (weich)
▩	Kunststoff (allgemein)
▚	Dichtstoff (allgemein)
▥	Gips (Gipskartonplatte)
▥	Gipskartonplatte Brandschutz
☐	Erdmaterial (allgemein)
■	Bestand
🟨	Abbruch
🟥	Neubau

—	Medien
—	Fernwärme
—	Gas
—	Strom
—	Heizung
—	Regenwasser
—	Schmutzwasser
—	Wasser
—	Blech
- - -	Abdichtung
- - -	Folie
- - -	Dampfsperre, -bremse

Höhenbezugs- und Maßangaben

DOK	Deckenoberkante
DOS	Deckenoberseite
DUK	Deckenunterkante
DUS	Deckenunterseite
DUF	Deckenunterkante (fertige Untersicht)
FBOK	Fußbodenoberkante
OFF	Oberfläche des fertigen Fußbodens
FDOK	Fundamentoberkante
FDOS	Fundamentoberseite
FDUK	Fundamentunterkante
FDUS	Fundamentunterseite
RH	lichte Raumhöhe
GH	Geschoßhöhe
OK	Oberkante
OS	Oberseite
UK	Unterkante
US	Unterseite
STUK	Sturzunterkante (Rohbaumaß)
STH	Sturzhöhe gemessen von STUK bis DUK (Rohbaumaß)
RPH	Rohbauparapethöhe
FPH	fertige Parapethöhe (FBOK bis OK Fensterbank Innen)

Rauch-, Abgas- und Luftfänge, Schächte

L	Lüftungsschacht
PT	Putztürchen
PS	Putzstück
KT	Kehrtürchen
ABL	Abluft
ZUL	Zuluft
DBA	Druckbelüftungsanlage
DES	Druckentlastungsschacht
BÖ	Belüftungsöffnung
ÜÖ	Überströmöffnung
AÖ	Abströmöffnung mit Überdruckentlastungsorgan
BSK	Brandsschutzklappe
FBHV	Fussbodenheizungsverteiler
E-Verteiler	Elektroverteiler

Öffnungen und deren Abschlüsse

WD	Wanddurchbruch
DD	Deckendurchbruch
FBD	Fußbodendurchbruch
FDD	Fundamentdurchbruch
WS	Wandschlitz
WA	Wandaussparung
DA	Deckenaussparung
FBA	Fußbodenaussparung
RBL	Rohbaulichte
AL	Architekturlichte
STL	Stocklichte
GL	Glaslichte
STAM	Stockaußenmaß
DL	Durchgangslichte
GGT	Ganzglastüre
MGT	Metallgittertür
HT	Hebetüre
HST	Hebeschiebetüre
T	Türe
AT	Allgemeintüre
ET	Eingangstüre
WET	Wohnungseingangstür
IT	Innentür
DF	Drehflügel
DKF	Drehkippflügel
SF	Schiebe-Fenster
SWF	Schwingflügel
WF	Wendeflügel
K	Kippfenster
OL	Oberlichte
DF	Dachfächenfenster
PFR	Pfostenriegelkonstruktion
FE	Fenster
FT	Fenstertüre
R	Rechtsöffnend
L	Linksöffnend
FIX	Fixverglasung
VSG	Verbund-Sicherheitsglas
ESG	Einscheiben-Sicherheitsglas

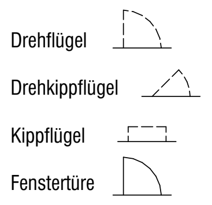

EI2 30-C-, EI2 60-C-und EI2 90-C
Feuerschutztüren mit Angabe der Feuerwiderstandsklasse
(gemäß ÖNORM B 3850 und ÖNORM B 3807)

GT	gasdichte Türe
DT	Drucktüre
S 200	Rauchabschluss
S 200	Rauchabschluss
C	Selbstschließend
FLS	Freilaufschließer
LVfTÖ	Lehrverrohrung für Türöffner
elTÖ	elektrischer Türöffner

AUSFÜHRUNG POLIERPLAN GESAMT

Bauvorhaben
VÖSL100

2500 Baden, Vöslauerstraße 100

XXX

Katastralgemeinde 4025 Rauhenstein
EZ: 2412
GstNr.: .424

Diese Zeichnung bzw. Ausarbeitung sowie deren Daten auf Datenträgern sind geistiges Eigentum des Erstellers Arch. Artmüller Georg. Jede Benützung, Veröffentlichung,Vervielfältigung jeglicher Art oder Weitergabe an Dritte bedarf der schriftlichen Zustimmung durch Architekt Artmüller.

Durch die Übernahme dieses Planes akzeptiert die ausführende Firma bzw. Person die darauf dargestellten Anordnungen. Geschriebene Planmaße auf dieser Zeichnunghaben Vorrang gegenüber gezeichneten Dimensionen. Der Auftragnehmer verpflichtet sich **vor** Arbeitsbeginn alle Maße und Bedingungen im Zusammenhang mit seinerArbeit auf der Baustelle verantwortlich zu überprüfen.

Abweichungen gegenüber dargestellten oder schriftlich vereinbarten Anordnungen müssen Architekt Artmüller und der Bauleitung unverzüglich schriftlich mitgeteiltwerden. Vor Arbeitsbeginn sind dem Architekten gültige Werkzeichnungen zur Genehmigung vorzulegen.

NATURMASSE SIND ZU NEHMEN, KOTEN ZU PRÜFEN

Index	Datum	Bearbeiter	Änderung

VORABZUG
15.09. 2026

Index	Änderung	Datum

Grundeigentümer

Bauwerber / Auftraggeber

ARTMÜLLER ARCHITEKTEN
ZIVILTECHNIKER GMBH
Stolberggasse 34|26 A-1050 Wien
t [+43] 01 . 581 40 83 f [+43] 01. 581 40 83 99 office@artmueller.eu

Planinhalt
Dachdraufsicht

Maßstab	Gez	Datum	Plannr.	Index
1:50	LM	16-10-2026	VÖSL100_50_04	01

Erstellt, am 11.11.2026

AW 01	ZIEGELWAND BESTAND
1,00 cm	Bestehender Außenputz
44,0-47,0 cm	Ziegelmauerwerk 44,00 - 47,00 cm
1,50 cm	Bestehender Innenputz
40,3 - 70,3cm	**BAUTEIL GESAMT**

AW 02	ZIEGELWAND BESTAND
1,00 cm	Bestehender Außenputz
28,0-32,0 cm	Ziegelmauerwerk 44,00 - 47,00 cm
1,50 cm	Bestehender Innenputz
31,0-35,0cm	**BAUTEIL GESAMT**

AW 03	GIBELWAND INNEN GEDÄMMT
1,50 cm	Bestehender Außenputz
36,00 cm	Bestehendes Ziegelmauerwerk
1,50 cm	Bestehender Innenputz
1,00 cm	Luftschicht (Abstand)
10,00 cm	C-Profil 75 dazw. 10cm Mineralwolle
	Dampfbremse, sd Wert lt. Bauphysik, allseits angebunden
1,50 cm	1 x 1,50 GKF-Platte **EI30**
5,00 cm	UK / Lattung dazw. Mineralwolle - Installationsebene
1,25 cm	1 x 1,25 cm GKB-Platte
57,75cm	**BAUTEIL GESAMT**

AW 04	KNIESTOCK INNEN GEDÄMMT
1,50 cm	Bestehender Außenputz
45,00 cm	Bestehendes Ziegelmauerwerk
1,50 cm	Bestehender Innenputz
1,00 cm	Luftschicht (Abstand)
10,00 cm	C-Profil 75 dazw. 10cm Mineralwolle
0,10 cm	Dampfbremse, sd Wert lt. Bauphysik, allseits angebunden
1,50 cm	1 x 1,50 GKF-Platte **EI30**
62,25 cm	Luftschicht (Abstand)
5,00 cm	UK / Lattung dazw. Mineralwolle - Installationsebene
1,25 cm	1 x 1,25 cm GKB-Platte (GKBi in Nassräumen)
121,10 cm	**BAUTEIL GESAMT**

AW 05	AUSSENWAND HOLZ-LEICHTBAU BLECH (GAUBE)
0,80 cm	Blech Zink, gefalzt auf Strukturgewebe
2,40 cm	Vollholzschalung
5,00 cm	Konterlattung / Hinterlüftung mit Nageldichtband
0,10 cm	Diffusionsoffene UV-beständige Winddichtbahn lt. Bauphysik allseitig und alle Durchdringungen eingebunden
6,00 cm	Holzfaserdämmplatte
18,00 cm	Konstruktionsholz lt. Statik, fungizid behandelt dazw. Dämmung lt. Bauphysik
2,20 cm	OSB Platte, allseits luftdicht verklebt
1,50 cm	1 x 1,5 GKF-Platte **EI30**
5,00 cm	UK / Lattung dazw. Mineralwolle - Installationsebene
1,25 cm	1 x 1,25 cm GKB-Platte (GKBi in Nassräumen)
42,25 cm	**BAUTEIL GESAMT**

IW 01	INNENWAND ZIEGEL TRAGEND BESTAND	
2,00 cm	Bestehender Innenputz	
64,00 cm	Bestehendes Ziegelmauerwerk	
2,00 cm	Bestehender Innenputz	
64,00 cm	**BAUTEIL GESAMT**	NICHT TEIL DER EINREICHUNG

IW 02	INNENWAND ZIEGEL NICHTTRAGEND BESTAND	
1,50 cm	Bestehender Innenputz	
45 - 49 cm	Bestehendes Ziegelmauerwerk	
1,50 cm	Bestehender Innenputz	
48 - 52 cm	**BAUTEIL GESAMT**	NICHT TEIL DER EINREICHUNG

IW 03	INNENWAND ZIEGEL NICHTTRAGEND BESTAND	
1,50 cm	Bestehender Innenputz	
28 - 32 cm	Bestehendes Ziegelmauerwerk	
1,50 cm	Bestehender Innenputz	
31 - 35 cm	**BAUTEIL GESAMT**	NICHT TEIL DER EINREICHUNG

IW 04	INNENWAND BESTAND	
18 -20 cm	**BAUTEIL GESAMT**	NICHT TEIL DER EINREICHUNG

IW 05	INNENWAND BESTAND	
10,00 cm	**BAUTEIL GESAMT**	NICHT TEIL DER EINREICHUNG

IW 06	INNENWAND TROCKENBAU DOPPELT BEPLANKT
2,50 cm	2 x 1,25 cm GKB-Platte (GKBi in Nassräumen)
7,50 cm	C-Profil dazw. Mineralwolle
2,50 cm	2 x 1,25 cm GKB-Platte (GKBi in Nassräumen)
12,50 cm	**BAUTEIL GESAMT**

IW 06 a	INNENWAND TROCKENBAU DOPPELT BEPLANKT
2,50 cm	2 x 1,25 cm GKB-Platte (GKBi in Nassräumen)
7,50 cm	C-Profil dazw. Mineralwolle
2,50 cm	Mineralwolle
7,50 cm	C-Profil dazw. Mineralwolle
2,50 cm	2 x 1,25 cm GKB-Platte (GKBi in Nassräumen)
22,50 cm	**BAUTEIL GESAMT**

IW 07	WOHNUNGSTRENNWAND TROCKENBAU
2,50 cm	2 x 1,25 cm GKF-Platte
7,50 cm	C-Profil dazw. Mineralwolle
1,25 cm	1 x 1,25 cm GKF- Platte
	PE- Folie allseits luftdicht verklebt
0,25cm	Luftraum (Abstand)
7,50 cm	C-Profil dazw. Mineralwolle
2,50 cm	2 x 1,25 cm GKB-Platte (GKBi in Nassräumen)
21,50 cm	**BAUTEIL GESAMT**

VS 01	VORSATZSCHALE TROCKENBAU
1,00 cm	Luftraum (Abstand)
5,00 cm	C-Profil dazw. Mineralwolle
1,25 cm	1 x 1,25 cm GKB-Platte (GKBi in Nassräumen)
7,25 cm	**BAUTEIL GESAMT**

VS 02	VORSATZSCHALE TROCKENBAU NASSRAUM
1,00 cm	Luftraum (Abstand)
7,50 cm	C-Profil dazw. Mineralwolle
2,50 cm	2 x 1,25 cm GKB-Platte (GKBi in Nassräumen)
11,00 cm	**BAUTEIL GESAMT**

VS 03	VORSATZSCHALE TROCKENBAU WC
4,00 cm	Luftraum (Abstand)
15,00 cm	C-Profil dazw. Mineralwolle
2,50 cm	2 x 1,25 cm GKB-Platte (GKBi in Nassräumen)
21,50 cm	**BAUTEIL GESAMT**

FB 01	FUSSBODEN GEGEN ERDREICH EG
	Bestehender Fußbodenbelag
	Bestehender Fußbodenaufbau
	Bestehende Betondecke
	Bestehender Unterbau
	NICHT TEIL DER EINREICHUNG

FB 01 a	FUSSBODEN GEGEN ERDREICH EG NEU
1,00 cm	Bodenbelag (Parkett / Fliese)
7,00 cm	Zementestrich, inkl. Randdämmstreifen 1cm PE-Folie seitlich hochgezogen bis Estrich OK
3,00 cm	Trittschalldämmplatten lt. Bauphysik Dampfbremse
5,00 cm	EPS - Schüttung zementgebunden
0,50 cm	Bituminöse Abdichtung
20,00 cm	Stahlbetonbodenplatte PE-Folie
10,00 cm	XPS
10,00 cm	Rollierung
56,50 cm	**BAUTEIL GESAMT**

FB 01 b	FUSSBODEN GEGEN ERDREICH EG NEU
1,00 cm	Bodenbelag (Parkett / Fliese)
7,00 cm	Zementestrich, inkl. Randdämmstreifen 1cm PE-Folie seitlich hochgezogen bis Estrich OK
3,00 cm	Trittschalldämmplatten lt. Bauphysik Dampfbremse
5,00 cm	EPS - Schüttung zementgebunden
0,50 cm	Bituminöse Abdichtung
25,00 cm	Bestehende Betonplatte
56,50 cm	**BAUTEIL GESAMT**

FB 02	DECKE ÜBER EG
	Bestehender Fußbodenbelag
	Bestehender Fußbodenaufbau
	Bestehende Holztramdecke
	Bestehender abgehängte Decke
	NICHT TEIL DER EINREICHUNG

FB 03	DECKE Ü. 1.OG - DIPPELBAUMD. BESTAND / FBA NEU
1,00 cm	Bodenbelag (Parkett / Fliese)
7,00 cm	Zementestrich mit FBH, inkl. Randdämmstreifen 1cm PE-Folie seitlich hochgezogen bis Estrich OK
3,00 cm	Trittschalldämmplatten lt. Bauphysik Dampfbremse
5,00 cm	EPS - Schüttung zementgebunden
7,00 cm	Verbundbeton
15,00 cm	Bestehende Dippelbaumdecke
4,00 cm	Bestehende Schilfmatte + Innenputz
8,50 cm	Bestehende abgehängte Decke
50,50 cm	**BAUTEIL GESAMT**

FB 04	BALKON STAHLKONSTR. THERMISCH ENTKOPPELT
2,50 cm	Holzbelag, rutsch- und witterungsfest
9,00 cm	Stellfüße Höhenausgleich 40-90 mm
0,80 cm	Gummigranulatplatte mit Trittschallfunktion
0,50 cm	Bituminöse Abdichtung 2-lagig, erste Lage selbstklebend
0,50 cm	Stahlblech lt. Statik, OK im Gefälle 2%
18,00 cm	Konstruktion aus Stahlträgern lt. Statik, Untersicht verkleidet mit MAX Exterior
31,30 cm	**BAUTEIL GESAMT**

DA 01	DACHAUFBAU, ZIEGELDECKUNG (HAUPTDACH)
3,00 cm	Keramischer Dachziegel
3,00 cm	Lattung 30/50 mm
5,00 cm	Konterlattung 50/50 mit Nageldichtband - Hinterlüftung
0,20 cm	Diffussionsoffene Dachauflegebahn - erhöhte Regensicherheit, sd- Wert lt. Bauphysik
2,40 cm	Vollholzschalung
24,00 cm	Holzsparren BESTAND nach innen aufgedoppelt lt. Statik dazw. Mineralwolle lt. Bauphysik
3,00 cm	UK / Lattung dazw. Mineralwolle lt. Bauphysik
0,10 cm	Feuchteadaptive Dampfbremse allseits verklebt lt. Bauphysik
1,50 cm	1x 1,50 cm GKF-Platte **(EI30)**
1,25 cm	1 x 1,25 cm GKB-Platte (GKBi in Nassräumen)
42,20 cm	**BAUTEIL GESAMT**

DA 02	DACHAUFBAU, BLECHDECKUNG (GAUBE)
0,80 cm	Zinkblech auf Strukturmatte
2,40 cm	Vollholzschalung
8,00 cm	Konterlattung 80/50 mit Nageldichtband - Hinterlüftung
0,20 cm	Diffussionsoffene Dachauflegebahn - erhöhte Regensicherheit, sd- Wert lt. Bauphysik
2,40 cm	Vollholzschalung
24,00 cm	Holzsparren lt. Statik dazw. Mineralwolle lt. Bauphysik
3,00 cm	UK / Lattung dazw. Mineralwolle lt. Bauphysik
0,10 cm	Feuchteadaptive Dampfbremse allseits verklebt lt. Bauphysik
1,50 cm	1 x 1,50 cm GKF-Platte **(EI30)**
42,40 cm	**BAUTEIL GESAMT**

DA 03	PULTDACH
0,80 cm	Zinkblech auf Strukturmatte
2,40 cm	Vollholzschalung
8,00 cm	Konterlattung 80/50 mit Nageldichtband - Hinterlüftung
0,20 cm	Diffussionsoffene Dachauflegebahn - erhöhte Regensicherheit, sd- Wert lt. Bauphysik
2,40 cm	Vollholzschalung
18,00 cm	Holzsparren dazw. Mineralwolle
0,10 cm	Feuchteadaptive Dampfbremse allseits verklebt lt. Bauphysik
2,40 cm	UK / Sparschalung
1,50 cm	1 x 1,50 cm GKF-Platte **(EI30)**
7 - 40,0 cm	*UK / Installationsebene nach Erfordernis*
1,25 cm	*1,25 GKB-Platte*
35,80 cm	**BAUTEIL GESAMT**

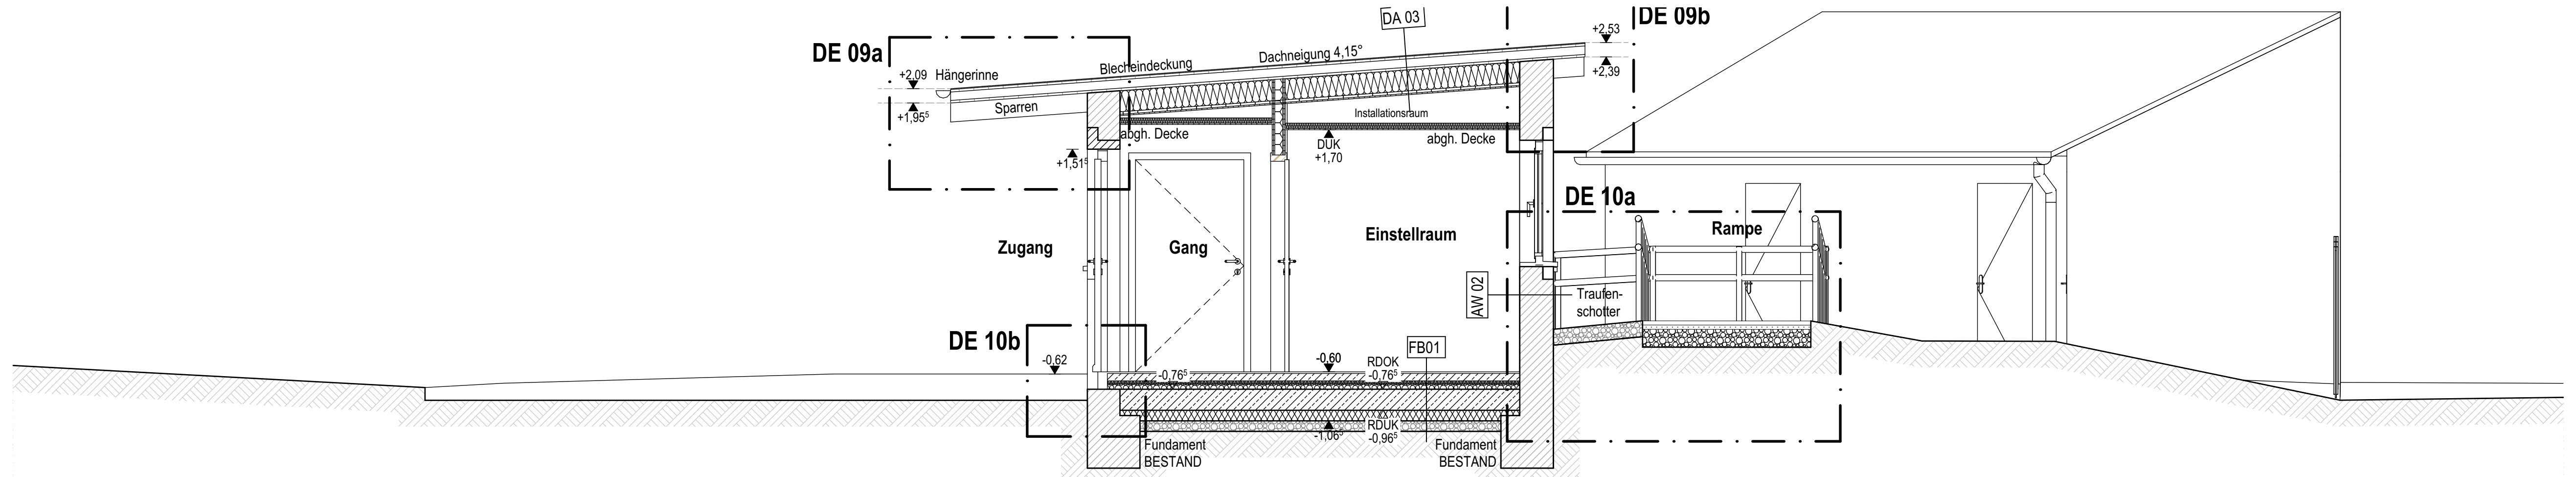

SCHNITT 4-4 M1:50

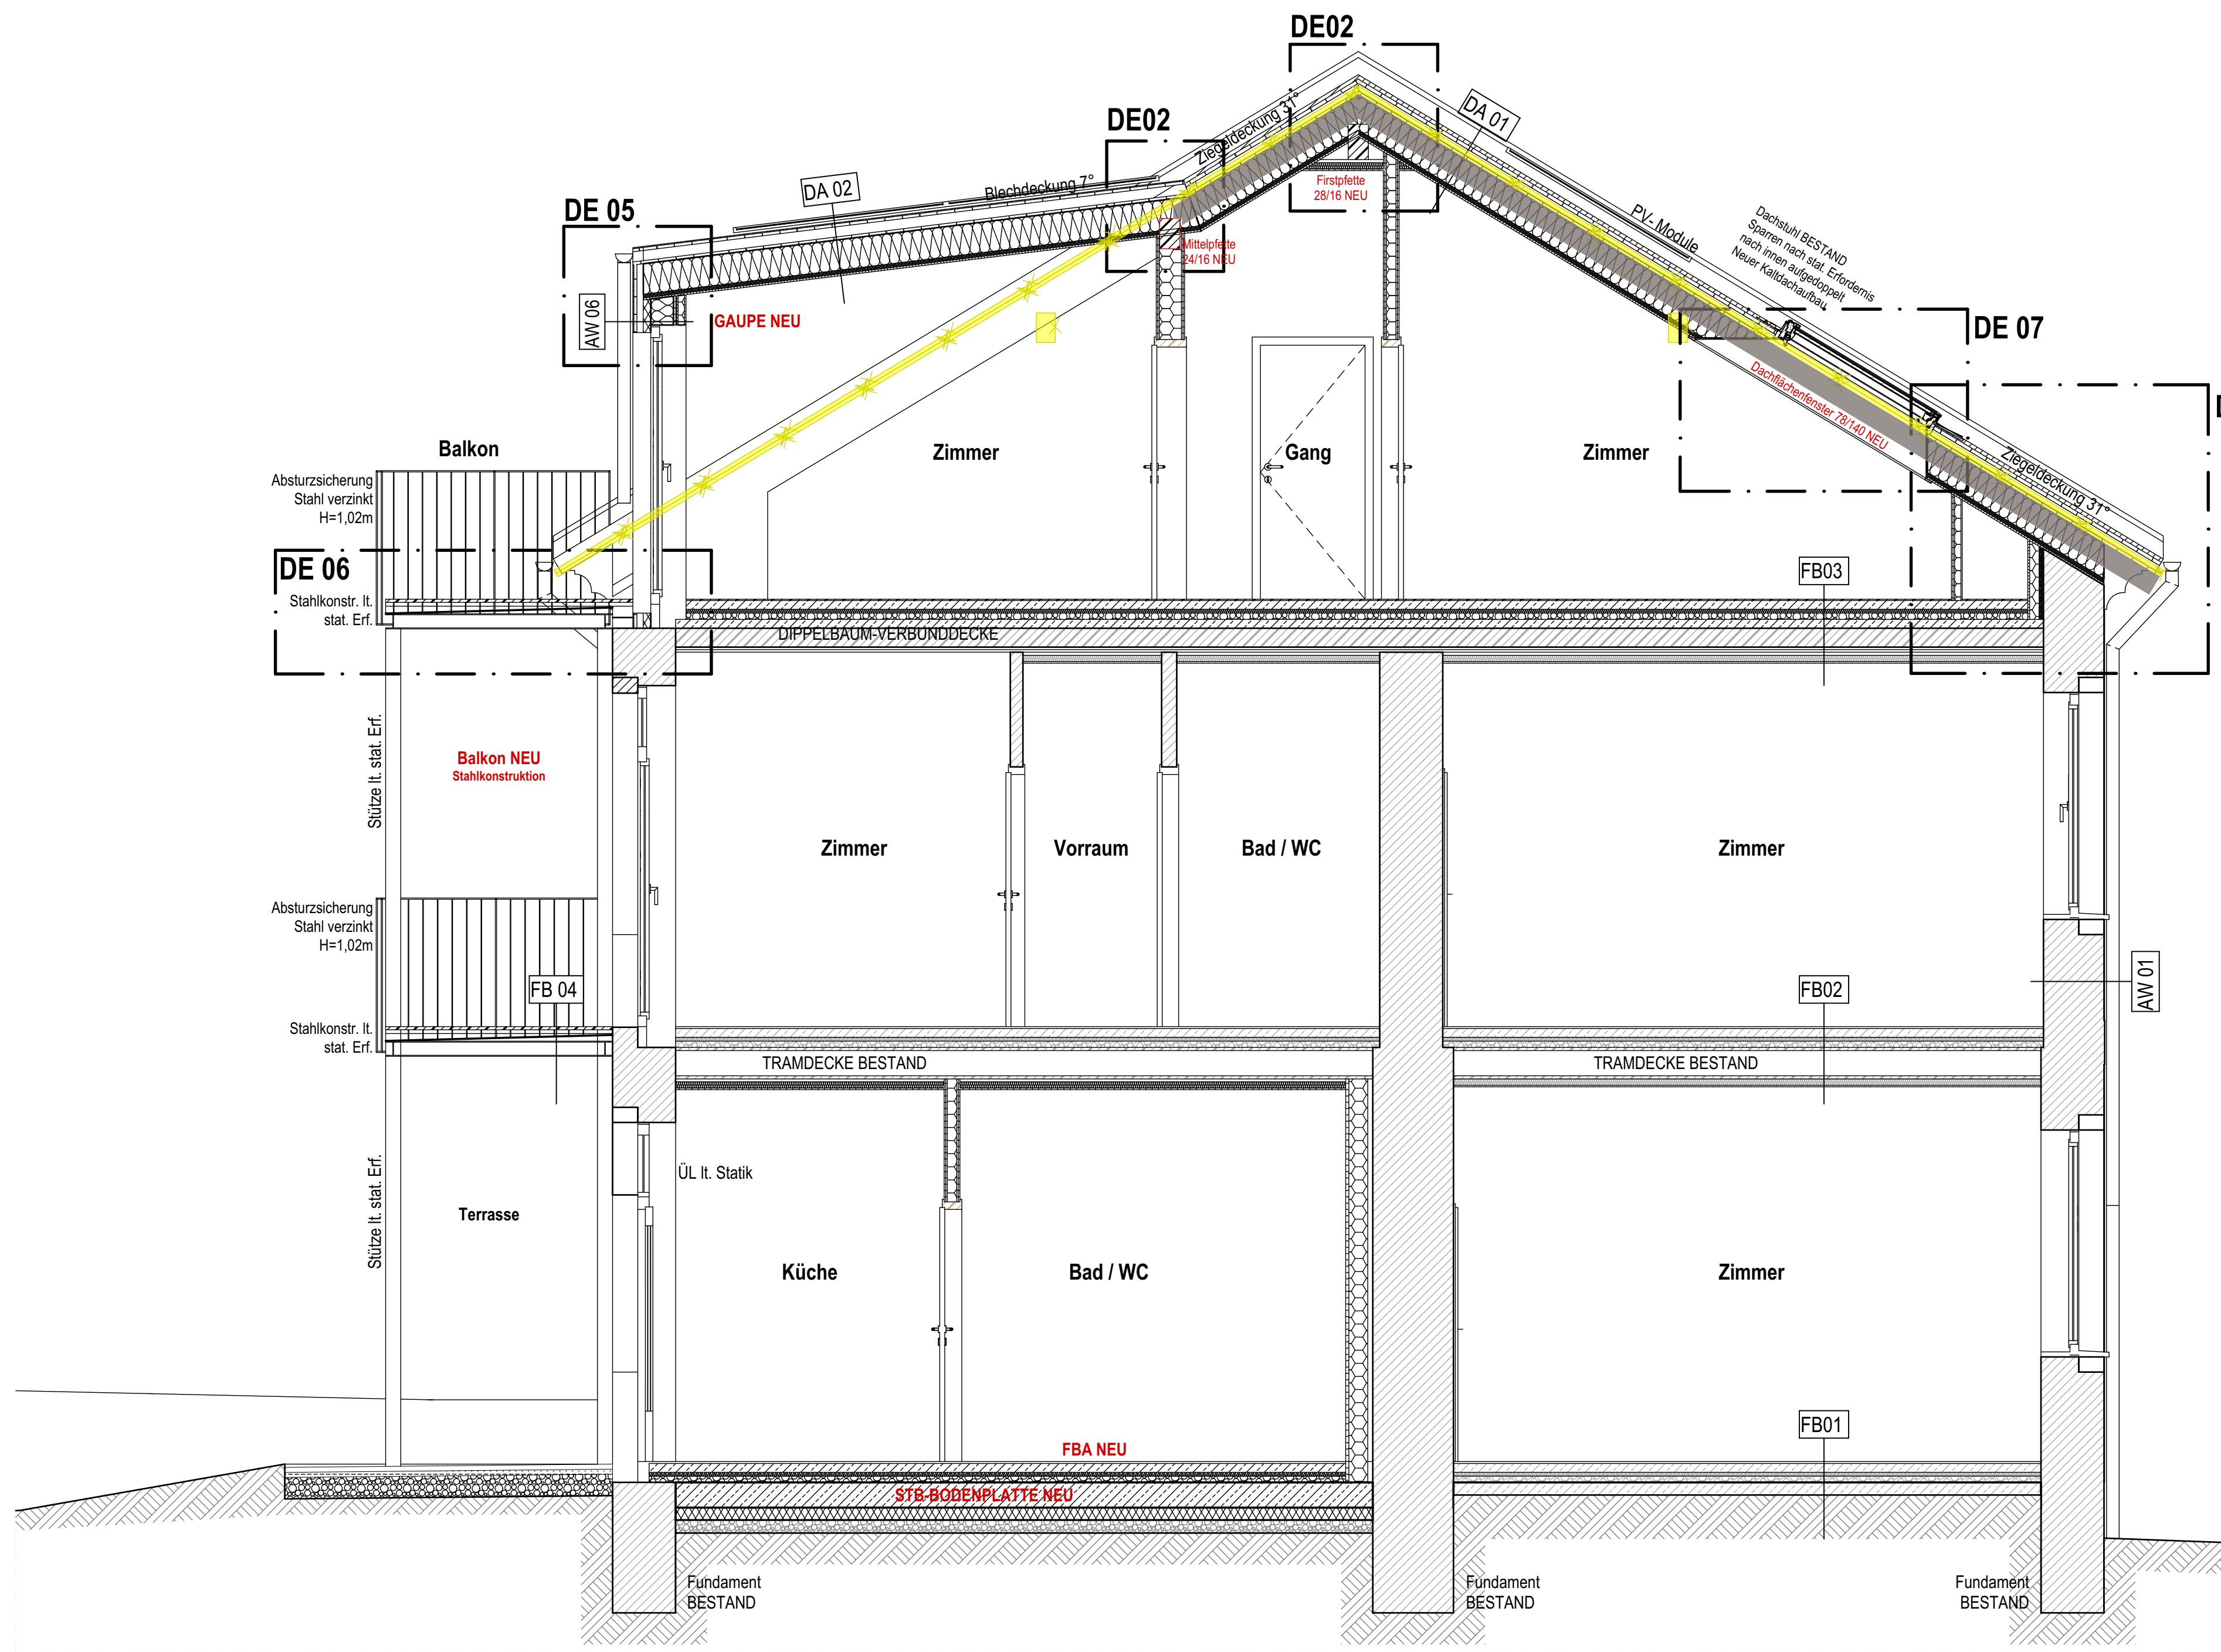

SCHNITT 3-3 M1:50

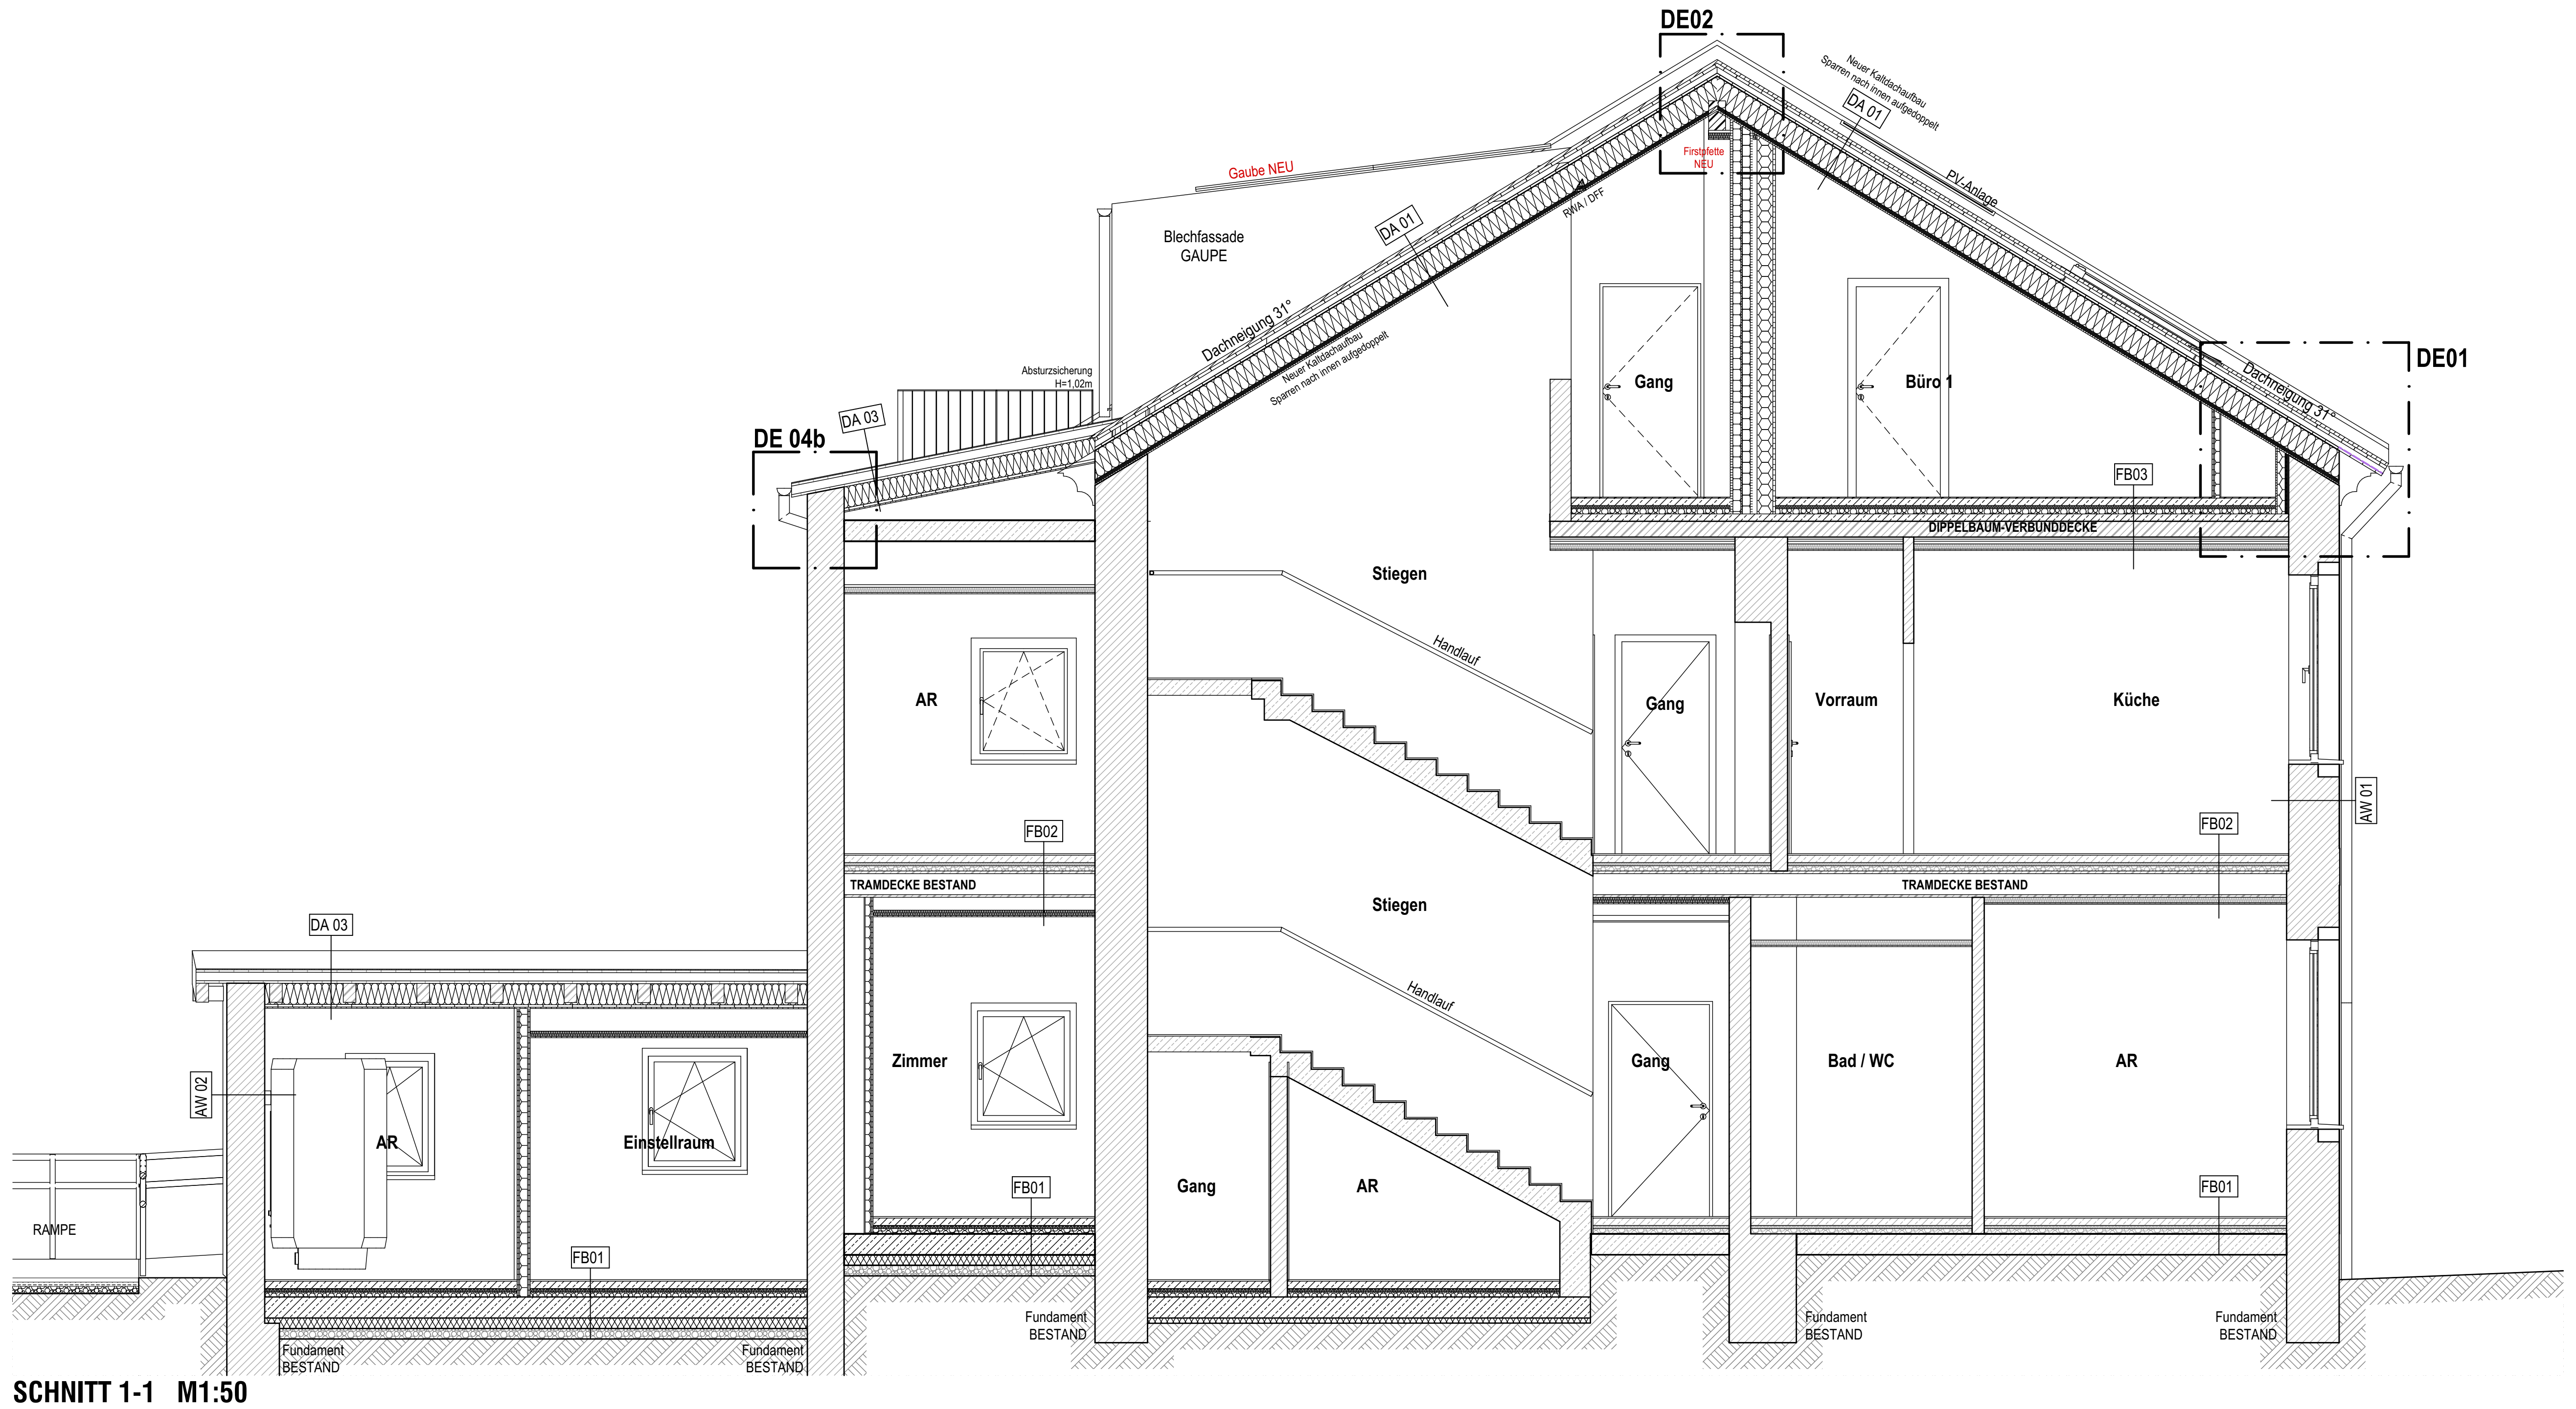

SCHNITT 1-1 M1:50

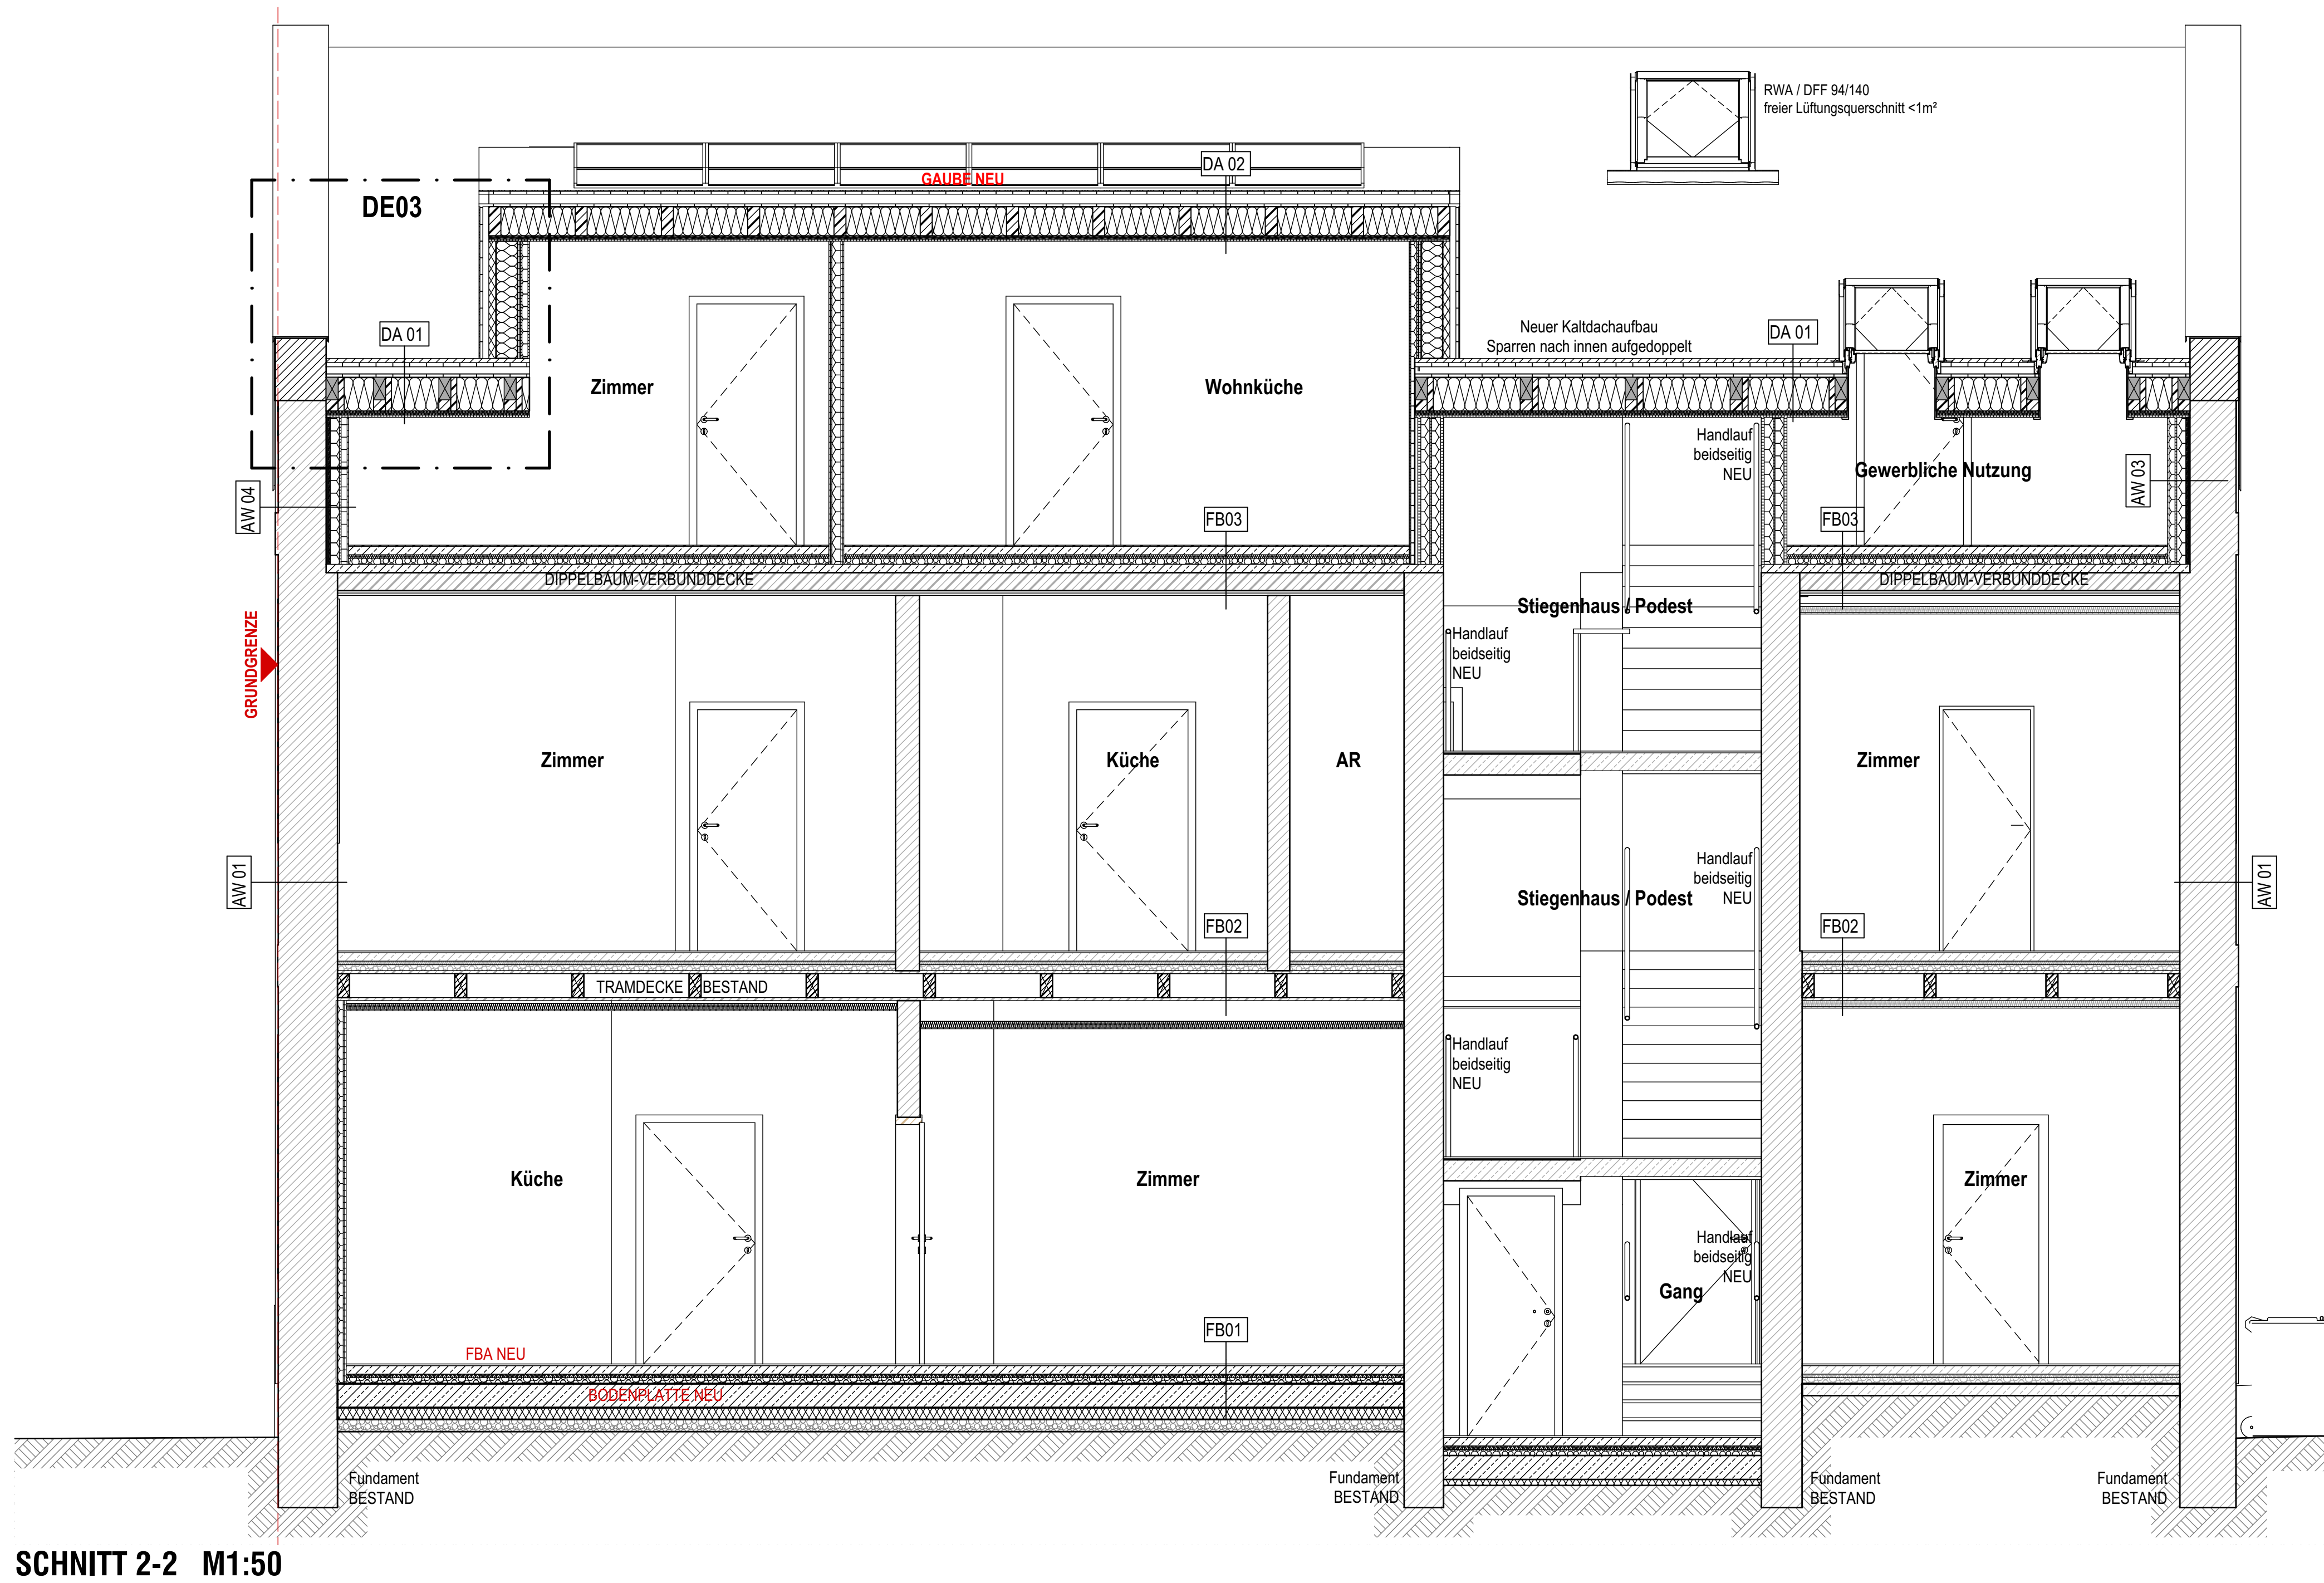

SCHNITT 2-2 M1:50

LEGENDE

☒	Wanddurchbruch
⬚	Deckendurchbruch
◺	Bodenschlitz
◢	Bodendurchbruch
▼	OK Fertigbau
▲	UK Fertigbau
▽	OK Rohbau
△	UK Rohbau
± 0,00	Höhenangabe einer waagrechten Fläche
⊕ ±0,00	Höhenangabe eines Punktes in einem Bauwerk - Fertigmaß
⌖ ±0,00	Höhenangabe eines Punktes in einem Bauwerk - Rohbaumaß
BGF	Bruttogesamtfläche
HNF / NNF	Haupt- Nebennutzfläche

▨	Mauerwerk (wärmedämmend)
▨	Mauerwerk (nicht wärmedämmend)
▨	unbewehrter Beton
▨	bewehrter Beton
▦	Betonfertigteil
▤	Stein
▨	Stahl (allgemein)
▨	Holz (allgemein)
▨	Holzwerkstoffe
▩	Dämmstoff (hart)
▩	Dämmstoff (weich)
▩	Kunststoff (allgemein)
▚	Dichtstoff (allgemein)
▥	Gips (Gipskartonplatte)
▥	Gipskartonplatte Brandschutz
☐	Erdmaterial (allgemein)
■	Bestand
🟨	Abbruch
🟥	Neubau

—	Medien
—	Fernwärme
—	Gas
—	Strom
—	Heizung
—	Regenwasser
—	Schmutzwasser
—	Wasser
—	Blech
- - -	Abdichtung
- - -	Folie
– – –	Dampfsperre, -bremse

Höhenbezugs- und Maßangaben

DOK	Deckenoberkante
DOS	Deckenoberseite
DUK	Deckenunterkante
DUS	Deckenunterseite
DUF	Deckenunterkante (fertige Untersicht)
FBOK	Fußbodenoberkante
OFF	Oberfläche des fertigen Fußbodens
FDOK	Fundamentoberkante
FDOS	Fundamentoberseite
FDUK	Fundamentunterkante
FDUS	Fundamentunterseite
RH	lichte Raumhöhe
GH	Geschoßhöhe
OK	Oberkante
OS	Oberseite
UK	Unterkante
US	Unterseite
STUK	Sturzunterkante (Rohbaumaß)
STH	Sturzhöhe gemessen von STUK bis DUK (Rohbaumaß)
RPH	Rohbauparapethöhe
FPH	fertige Parapethöhe (FBOK bis OK Fensterbank Innen)

Rauch-, Abgas- und Luftfänge, Schächte

L	Lüftungsschacht
PT	Putztürchen
PS	Putzstück
KT	Kehrtürchen
ABL	Abluft
ZUL	Zuluft
DBA	Druckbelüftungsanlage
DES	Druckentlastungsschacht
BÖ	Belüftungsöffnung
ÜÖ	Überströmöffnung
AÖ	Abströmöffnung mit Überdruckentlastungsorgan
BSK	Brandsschutzklappe
FBHV	Fussbodenheizungsverteiler
E-Verteiler	Elektroverteiler

Öffnungen und deren Abschlüsse

WD	Wanddurchbruch
DD	Deckendurchbruch
FBD	Fußbodendurchbruch
FDD	Fundamentdurchbruch
WS	Wandschlitz
WA	Wandaussparung
DA	Deckenaussparung
FBA	Fußbodenaussparung
RBL	Rohbaulichte
AL	Architekturlichte
STL	Stocklichte
GL	Glaslichte
STAM	Stockaußenmaß
DL	Durchgangslichte
GGT	Ganzglastüre
MGT	Metallgittertür
HT	Hebetüre
HST	Hebeschiebetüre
T	Türe
AT	Allgemeintüre
ET	Eingangstüre
WET	Wohnungseingangstür
IT	Innentür
DF	Drehflügel
DKF	Drehkippflügel
SF	Schiebe-Fenster
SWF	Schwingflügel
WF	Wendeflügel
K	Kippfenster
OL	Oberlichte
DF	Dachfächenfenster
PFR	Pfostenriegelkonstruktion
FE	Fenster
FT	Fenstertüre
R	Rechtsöffnend
L	Linksöffnend
FIX	Fixverglasung
VSG	Verbund-Sicherheitsglas
ESG	Einscheiben-Sicherheitsglas

Drehflügel
Drehkippflügel
Kippflügel
Fenstertüre

EI2 30-C-, EI2 60-C-und EI2 90-C
Feuerschutztüren mit Angabe der Feuerwiderstandsklasse
(gemäß ÖNORM B 3850 und ÖNORM B 3807)

GT	gasdichte Türe
DT	Drucktüre
S 200	Rauchabschluss
S 200	Rauchabschluss
C	Selbstschließend
FLS	Freilaufschließer
LVfTÖ	Lehrverrohrung für Türöffner
elTÖ	elektrischer Türöffner

AUSFÜHRUNG POLIERPLAN GESAMT

Bauvorhaben
VÖSL100
2500 Baden, Vöslauerstraße 100

XXX

Katastralgemeinde 4025 Rauhenstein
EZ: 2412
GstNr.: .424

Diese Zeichnung bzw. Ausarbeitung sowie deren Daten auf Datenträgern sind geistiges Eigentum des Erstellers Arch. Artmüller Georg. Jede Benützung, Veröffentlichung,Vervielfältigung jeglicher Art oder Weitergabe an Dritte bedarf der schriftlichen Zustimmung durch Architekt Artmüller.

Durch die Übernahme dieses Planes akzeptiert die ausführende Firma bzw. Person die darauf dargestellten Anordnungen. Geschriebene Planmaße auf dieser Zeichnunghaben Vorrang gegenüber gezeichneten Dimensionen. Der Auftragnehmer verpflichtet sich **vor** Arbeitsbeginn alle Maße und Bedingungen im Zusammenhang mit seinerArbeit auf der Baustelle verantwortlich zu überprüfen.

Abweichungen gegenüber dargestellten oder schriftlich vereinbarten Anordnungen müssen Architekt Artmüller und der Bauleitung unverzüglich schriftlich mitgeteiltwerden. Vor Arbeitsbeginn sind dem Architekten gültige Werkzeichnungen zur Genehmigung vorzulegen.

NATURMASSE SIND ZU NEHMEN, KOTEN ZU PRÜFEN

Index	Datum	Bearbeiter	Änderung

Index	Änderung	Datum

VORABZUG
16. 10. 2026

Grundeigentümer

Bauwerber / Auftraggeber

ARTMÜLLER ARCHITEKTEN
ZIVILTECHNIKER GMBH
Stolberggasse 34|26 A-1050 Wien
t [+43] 01 . 581 40 83 f [+43] 01. 581 40 83 99 office@artmueller.eu

Planinhalt
Schnitte

Maßstab	Gez	Datum	Plannr.	Index
1:50	LM	16-10-2026	VÖSL100_50_05	01

Erstellt, am 11.11.2026

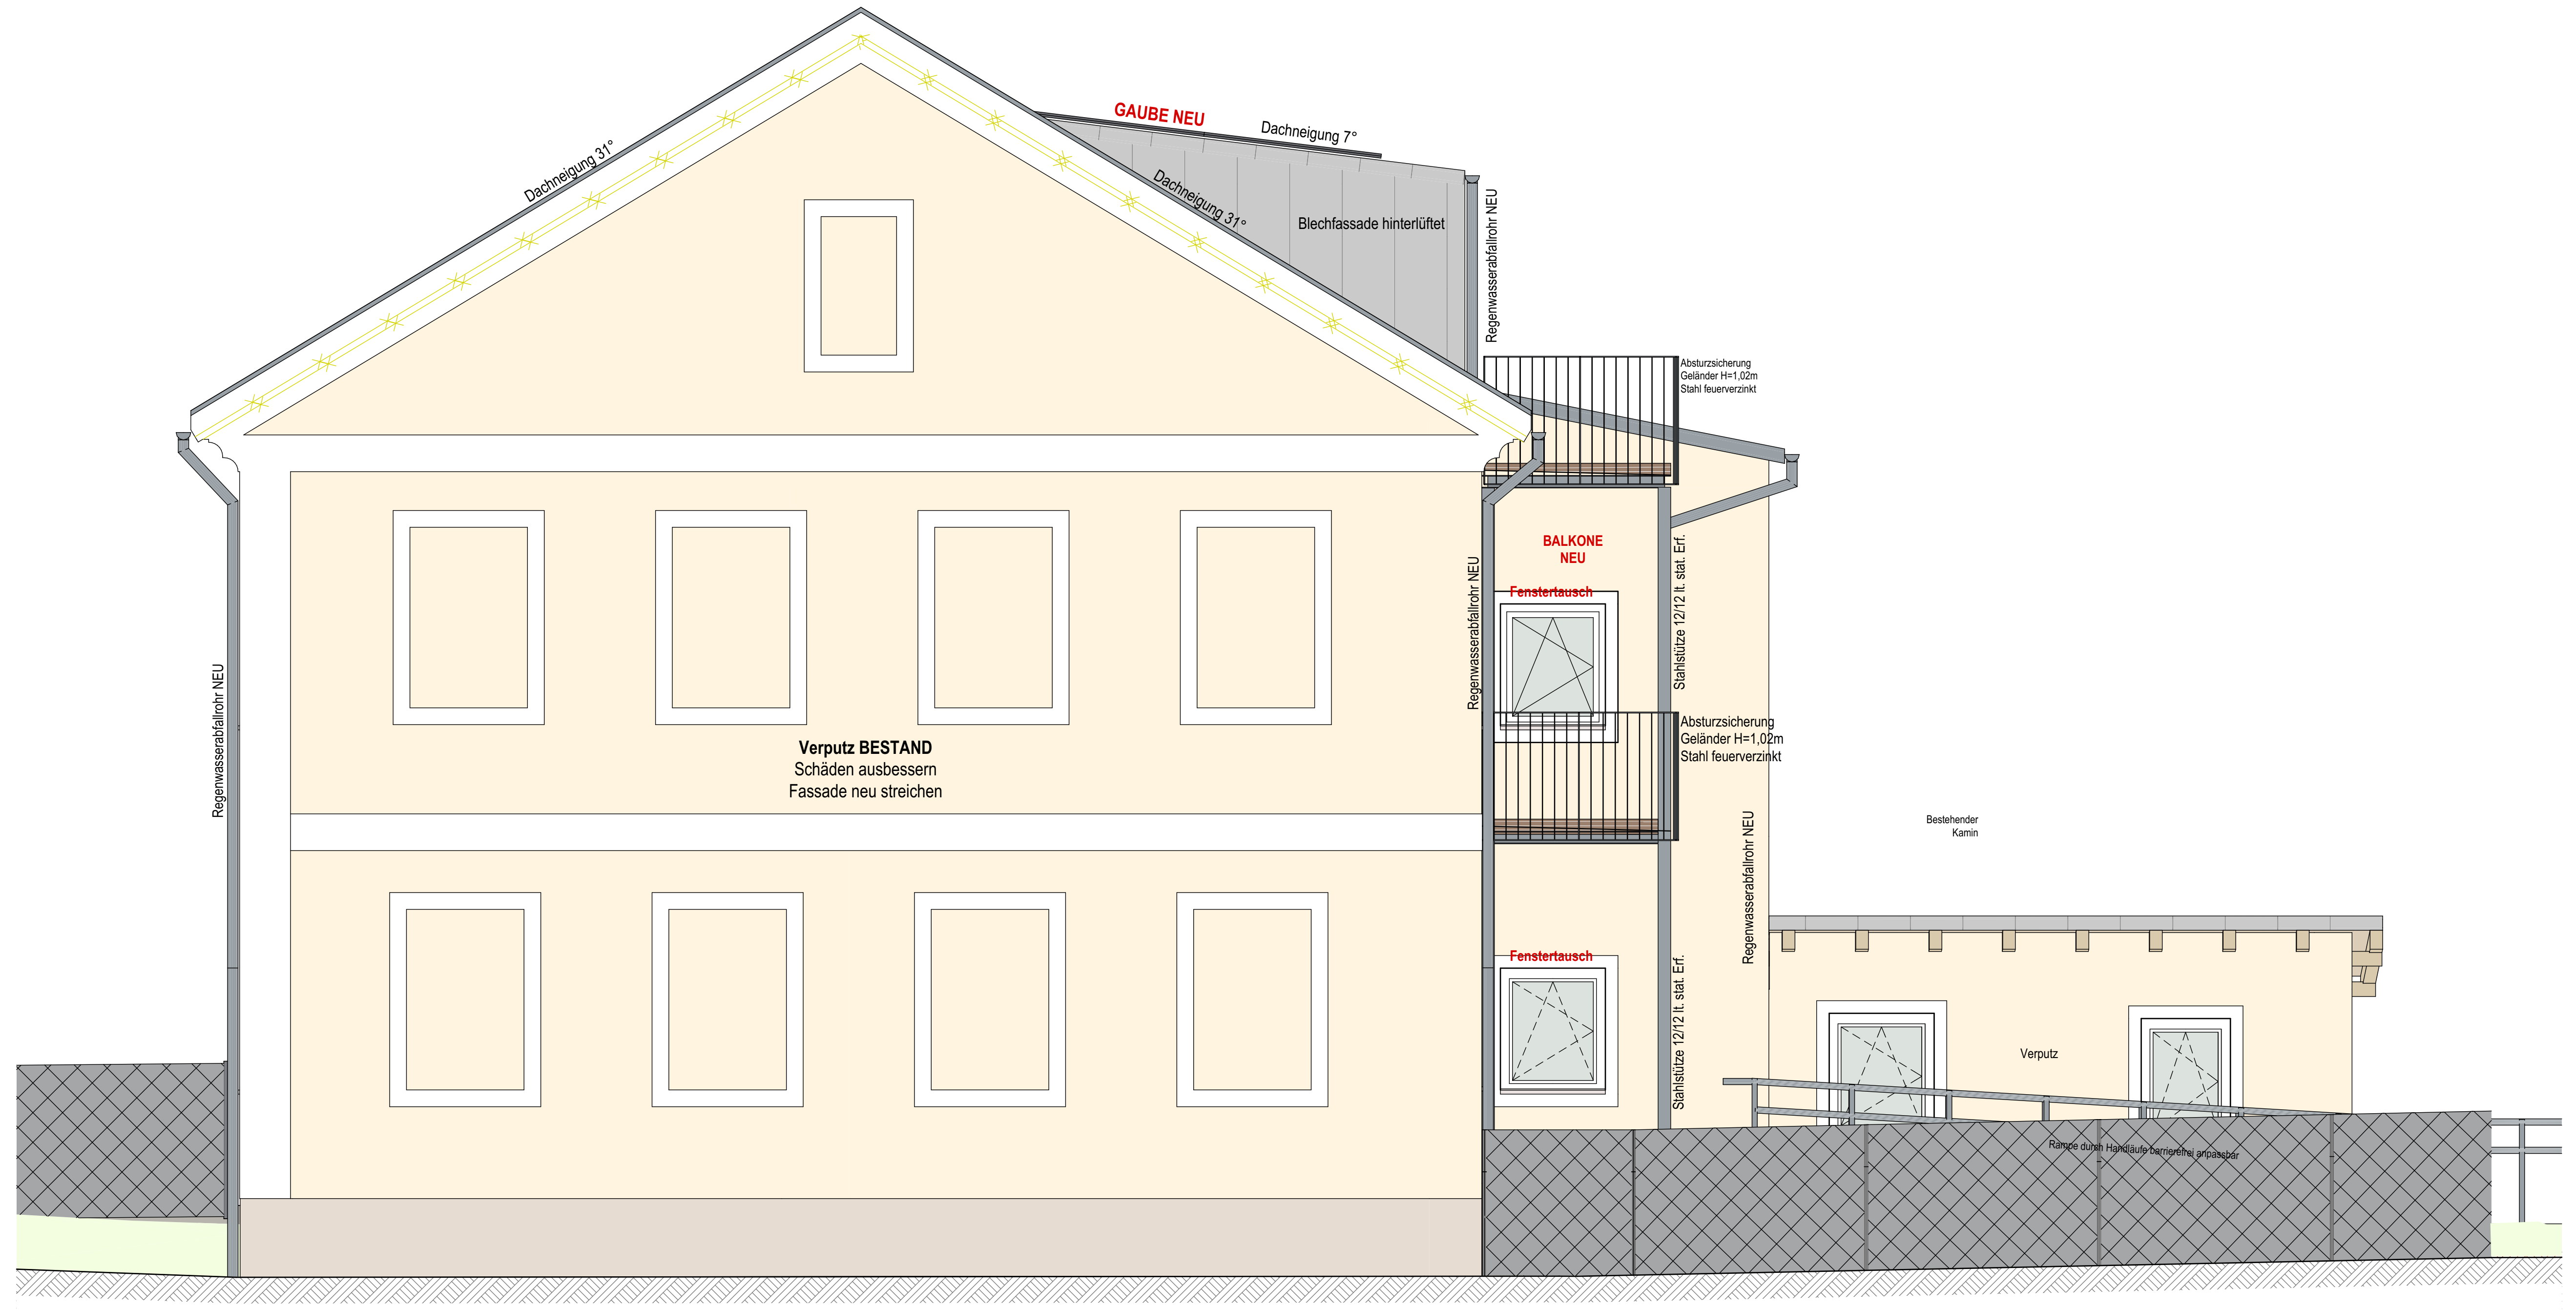

NORDANSICHT M1:50

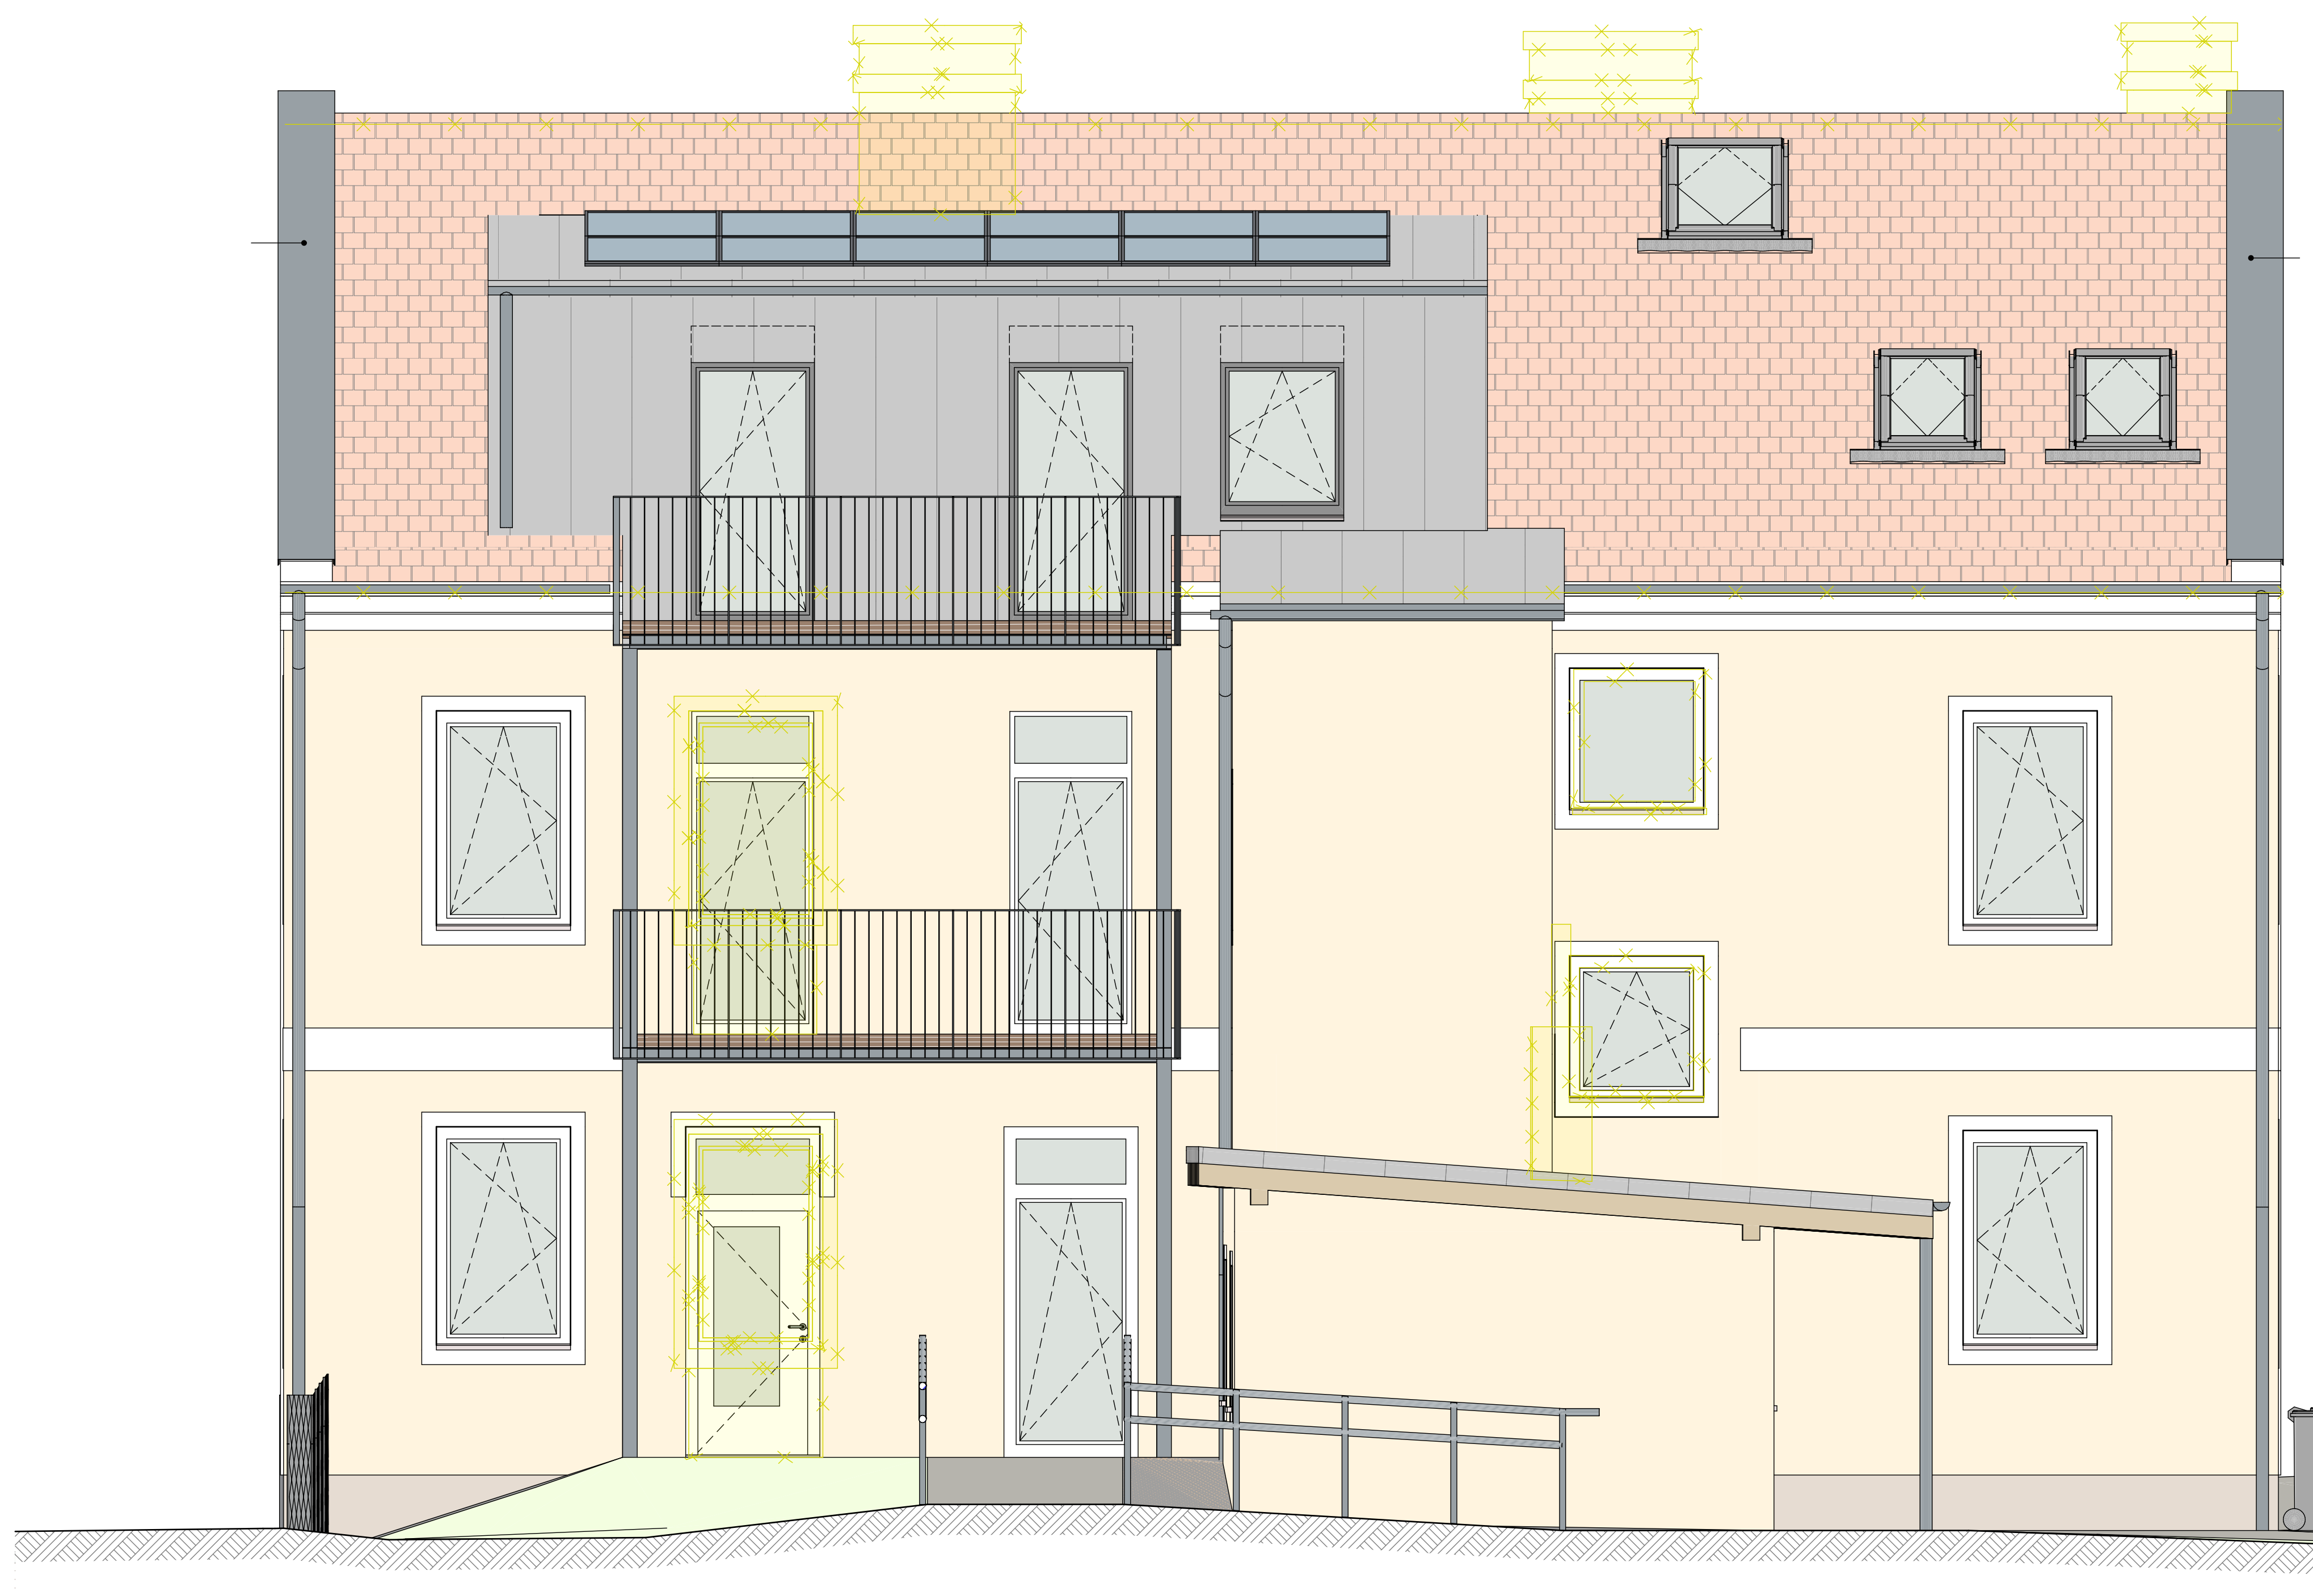

WESTANSICHT M1:50

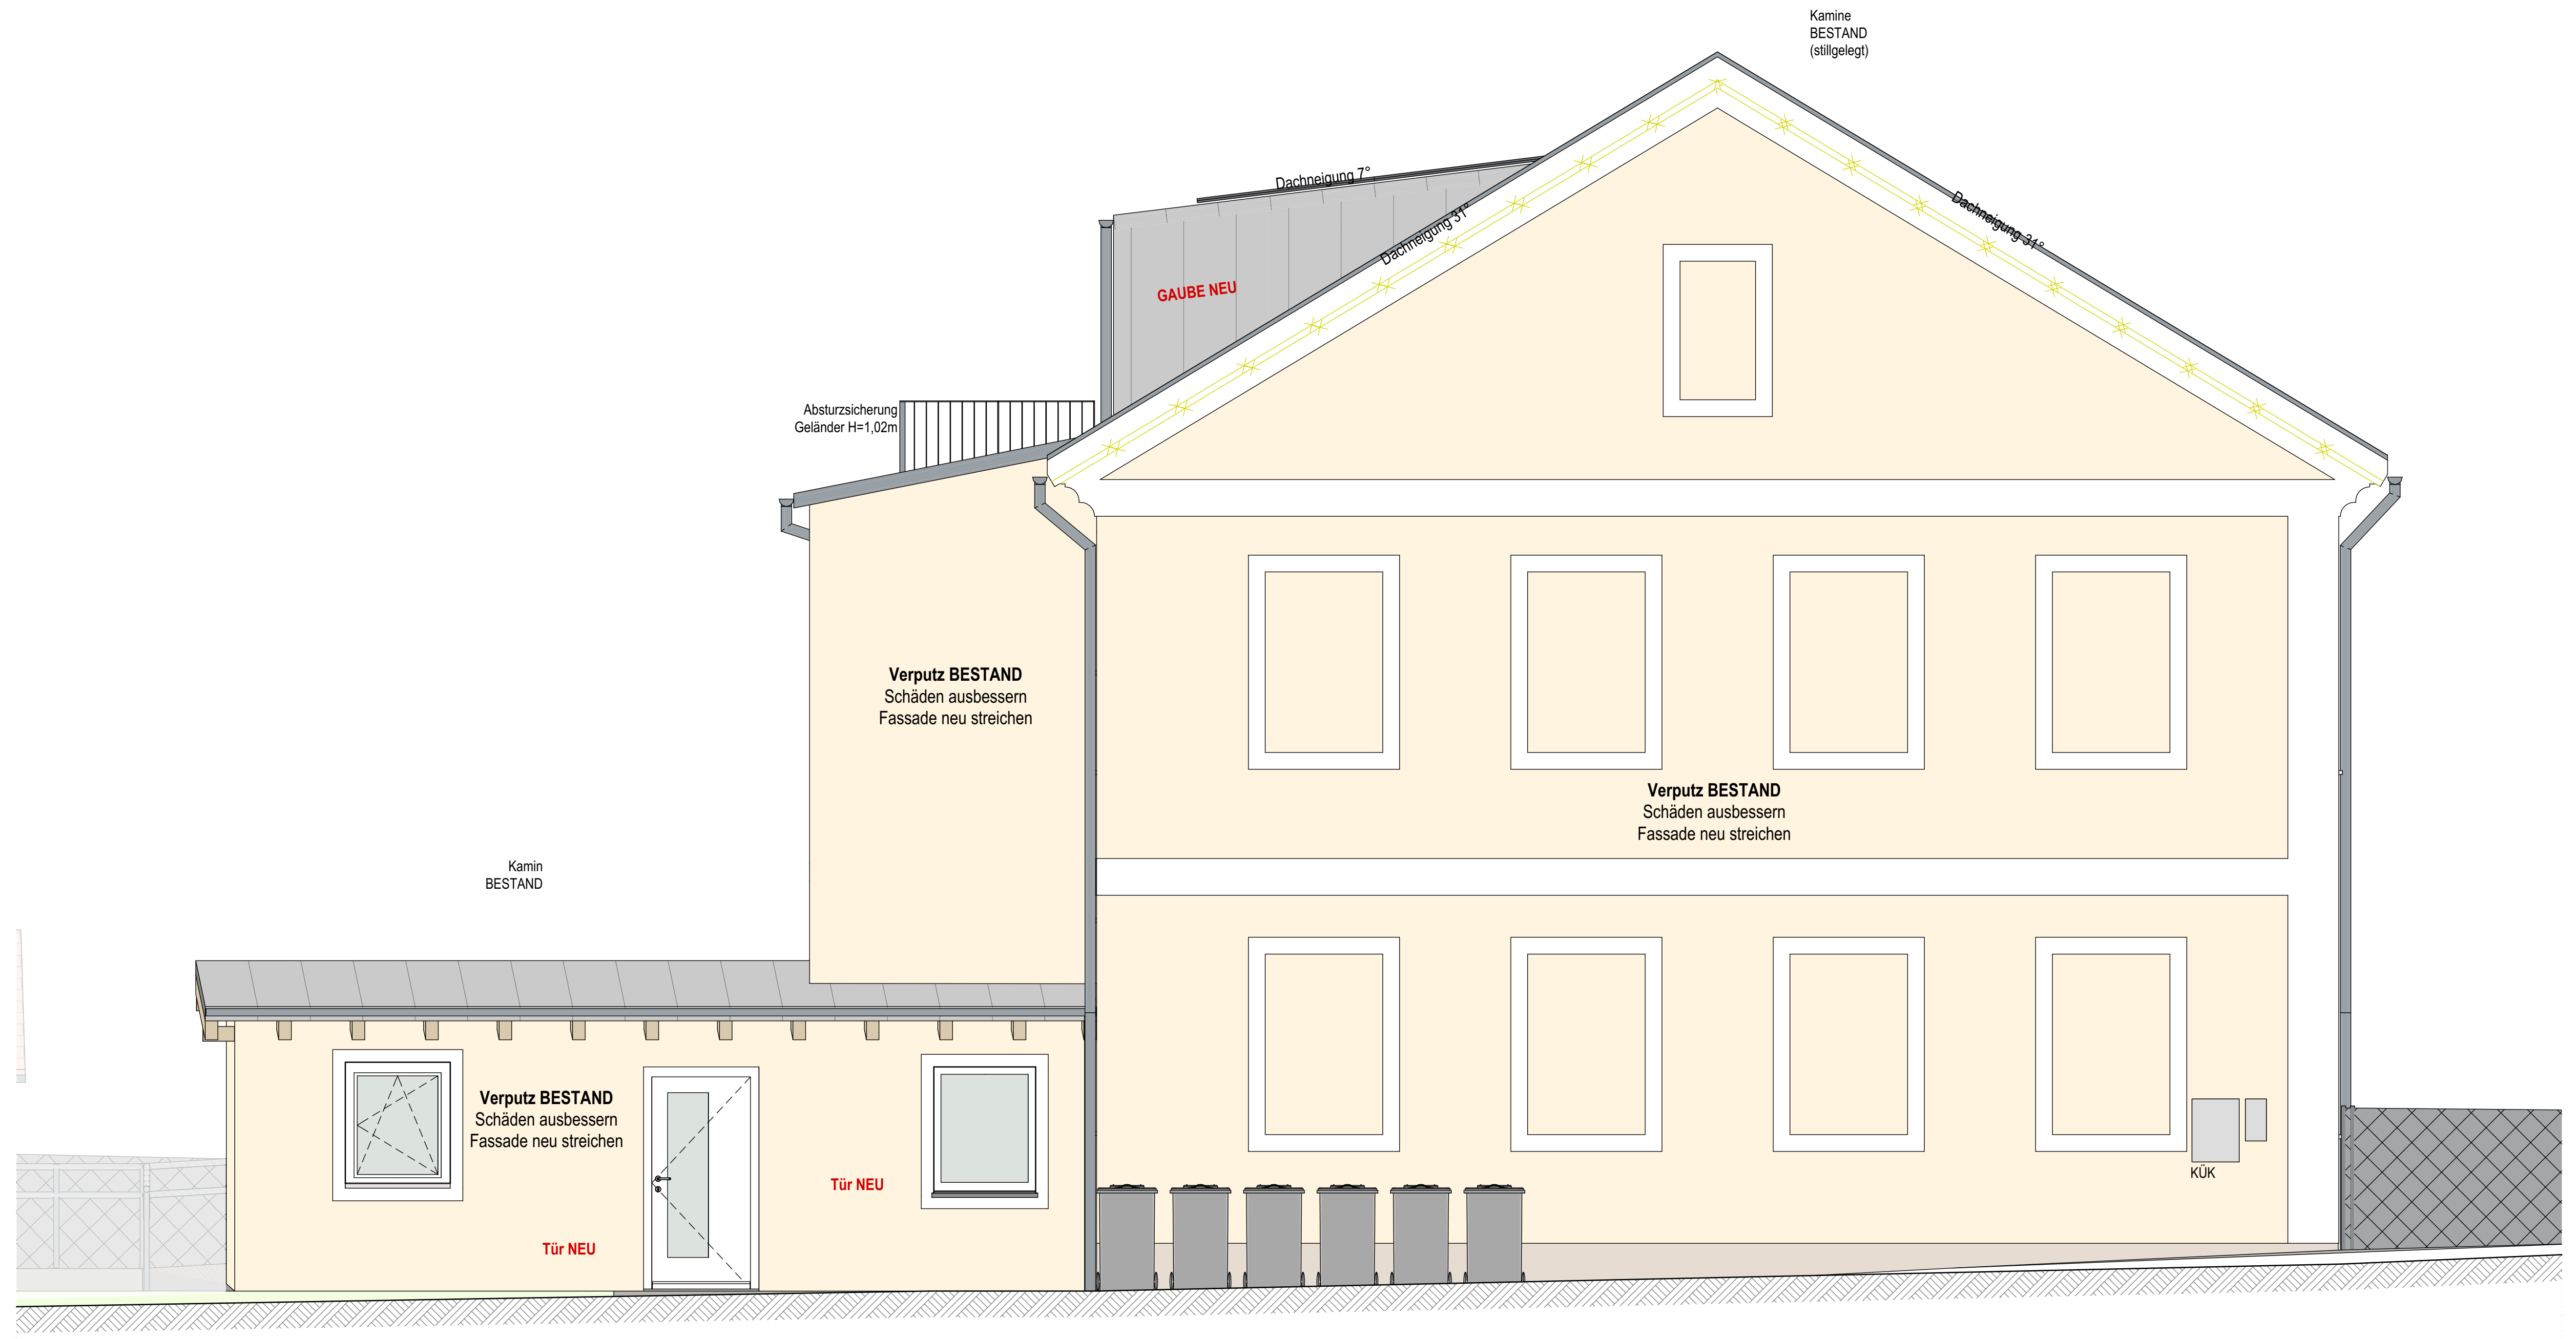

SÜDANSICHT M1:50

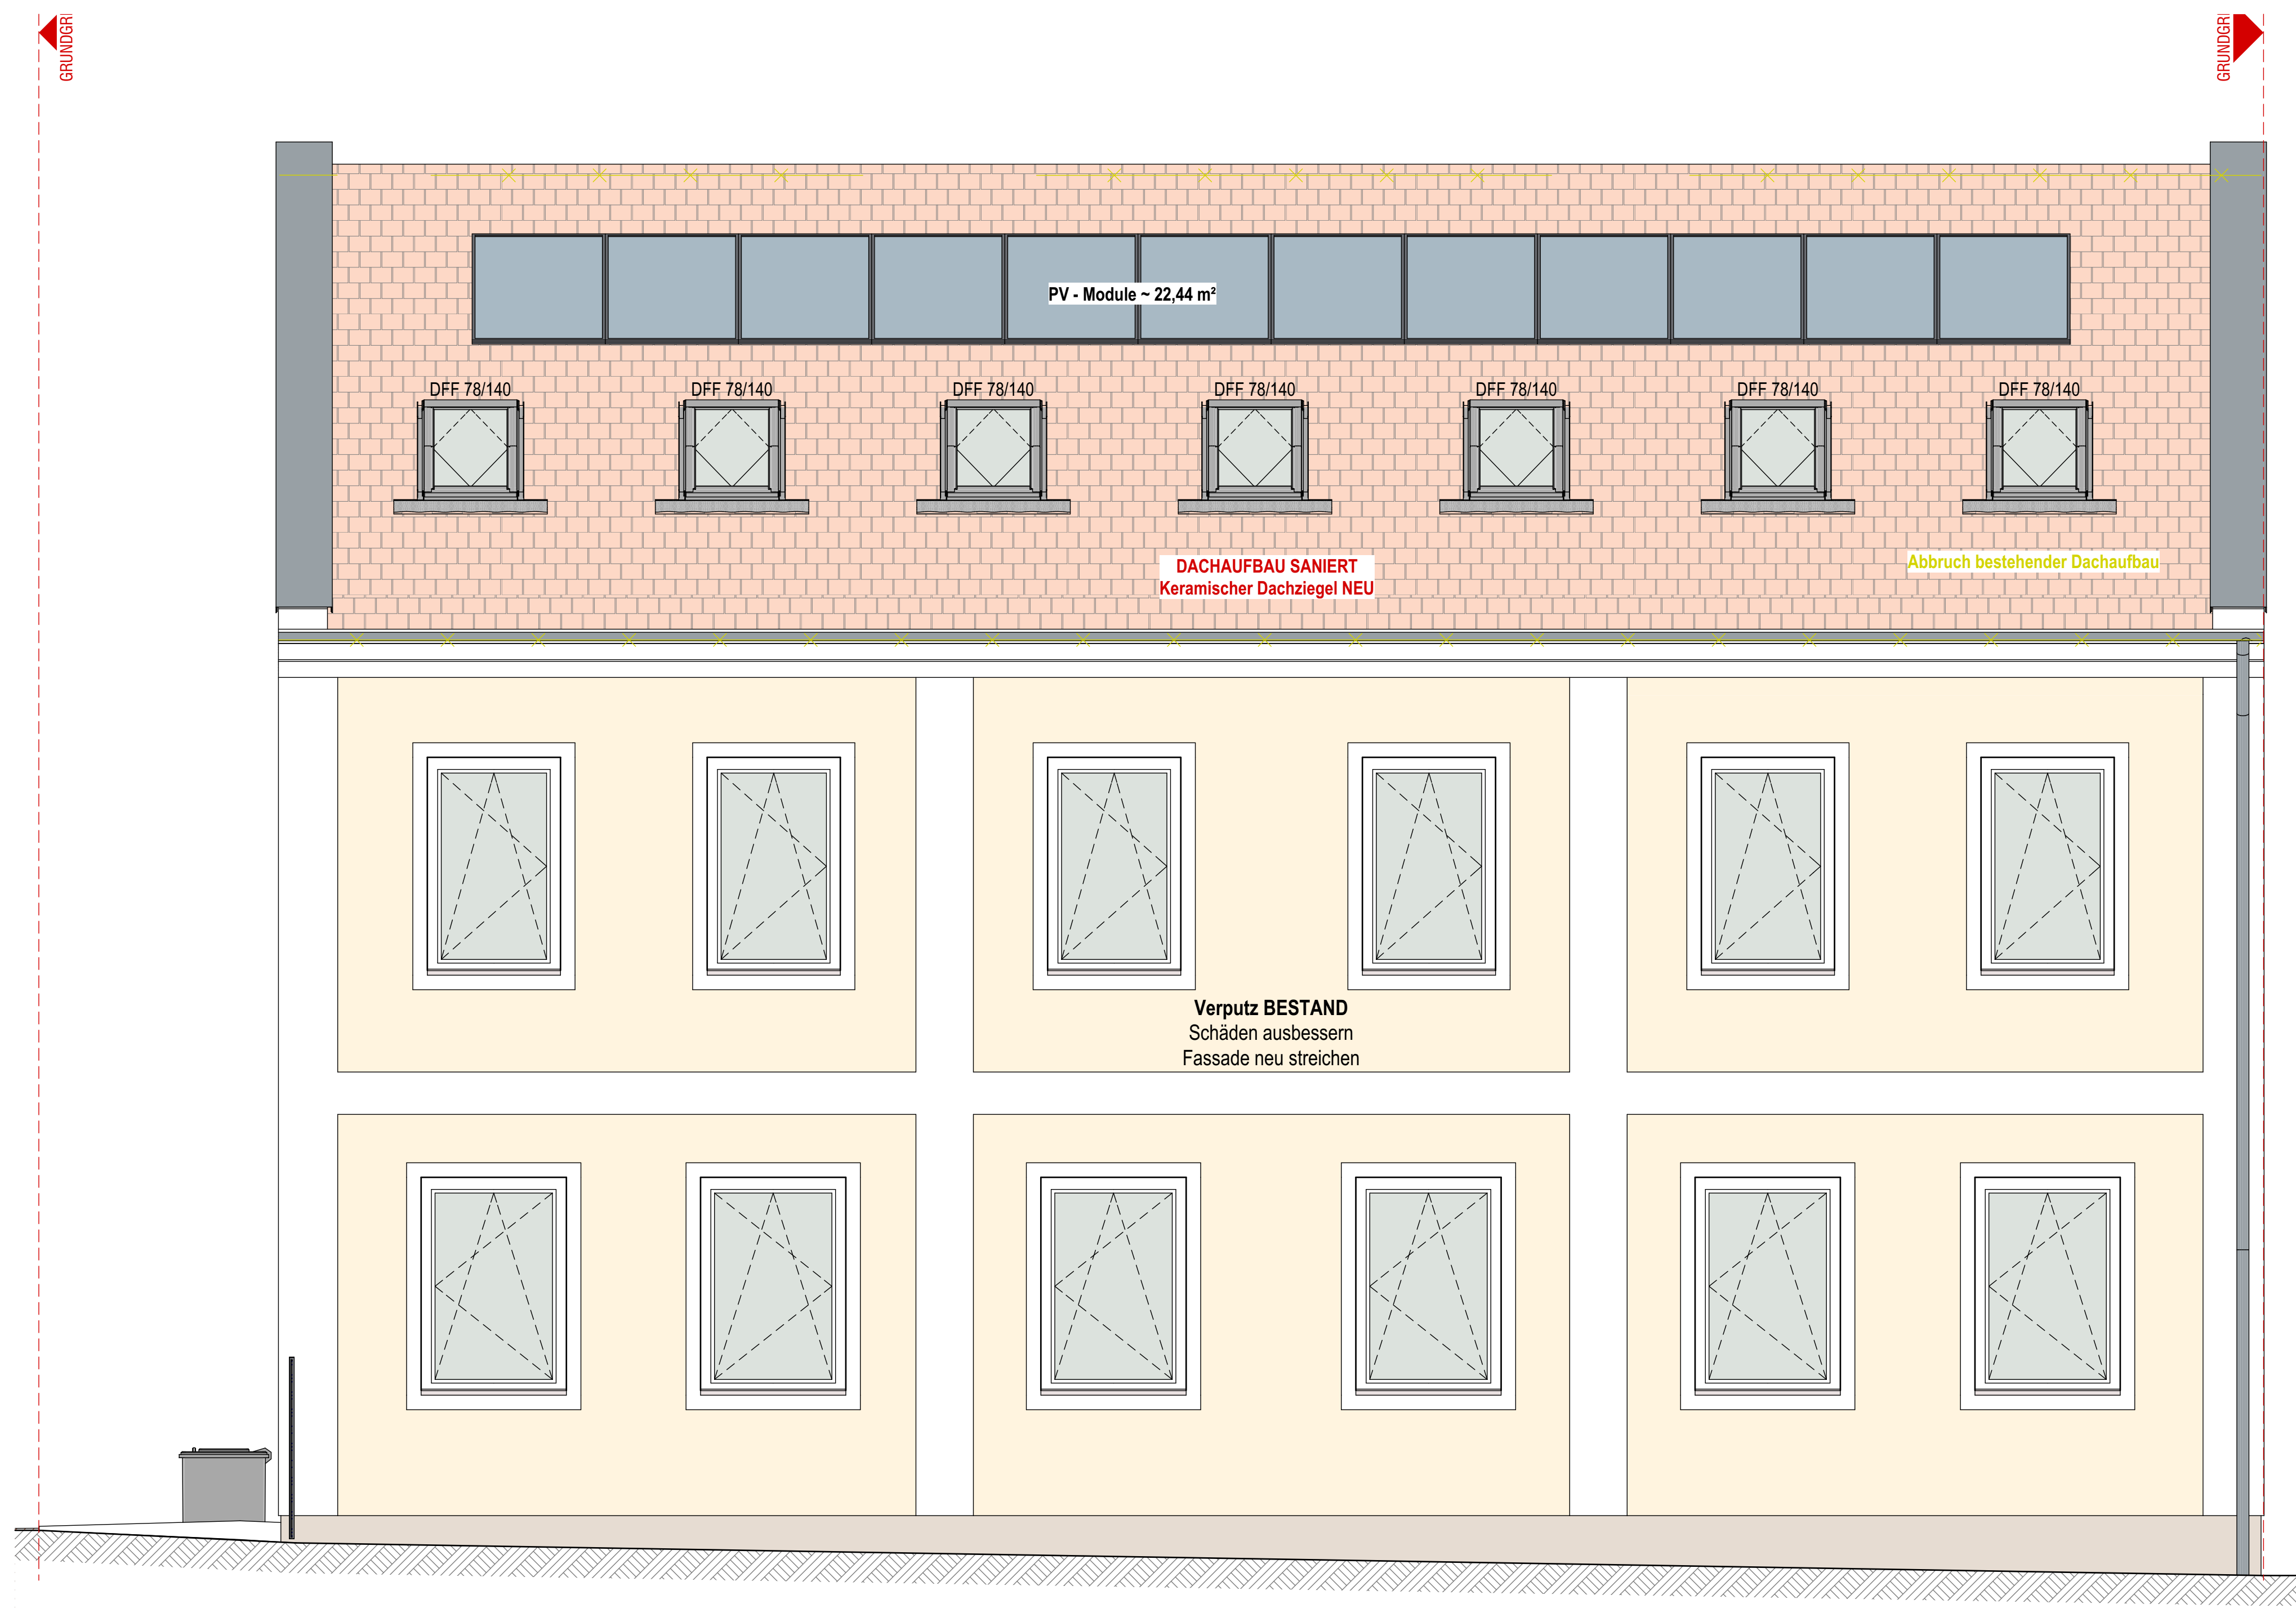

OSTANSICHT M1:50

LEGENDE

- ☒ Wanddurchbruch
- ⬚ Deckendurchbruch
- ☐ Bodenschlitz
- ◩ Bodendurchbruch
- ▼ OK Fertigbau
- ▲ UK Fertigbau
- ▽ OK Rohbau
- △ UK Rohbau
- ± 0,00 Höhenangabe einer waagrechten Fläche
- ⊕ ±0,00 Höhenangabe eines Punktes in einem Bauwerk - Fertigmaß
- ⊕ ±0,00 Höhenangabe eines Punktes in einem Bauwerk - Rohbaumaß

BGF	Bruttogesamtfläche
HNF / NNF	Haupt- Nebennutzfläche

- ▨ Mauerwerk (wärmedämmend)
- ▨ Mauerwerk (nicht wärmedämmend)
- ▨ unbewehrter Beton
- ▨ bewehrter Beton
- ▦ Betonfertigteil
- ▤ Stein
- ▨ Stahl (allgemein)
- ▨ Holz (allgemein)
- ▨ Holzwerkstoffe
- ▩ Dämmstoff (hart)
- ▩ Dämmstoff (weich)
- ▩ Kunststoff (allgemein)
- ▚ Dichtstoff (allgemein)
- ▥ Gips (Gipskartonplatte)
- ▥ Gipskartonplatte Brandschutz
- ☐ Erdmaterial (allgemein)
- ■ Bestand
- 🟨 Abbruch
- 🟥 Neubau

- — Medien
- — Fernwärme
- — Gas
- — Strom
- — Heizung
- — Regenwasser
- — Schmutzwasser
- — Wasser
- — Blech
- - - Abdichtung
- - - Folie
- - - Dampfsperre, -bremse

Höhenbezugs- und Maßangaben

DOK	Deckenoberkante
DOS	Deckenoberseite
DUK	Deckenunterkante
DUS	Deckenunterseite
DUF	Deckenunterkante (fertige Untersicht)
FBOK	Fußbodenoberkante
OFF	Oberfläche des fertigen Fußbodens
FDOK	Fundamentoberkante
FDOS	Fundamentoberseite
FDUK	Fundamentunterkante
FDUS	Fundamentunterseite
RH	lichte Raumhöhe
GH	Geschoßhöhe
OK	Oberkante
OS	Oberseite
UK	Unterkante
US	Unterseite
STUK	Sturzunterkante (Rohbaumaß)
STH	Sturzhöhe gemessen von STUK bis DUK (Rohbaumaß)
RPH	Rohbauparapethöhe
FPH	fertige Parapethöhe (FBOK bis OK Fensterbank Innen)

Rauch-, Abgas- und Luftfänge, Schächte

L	Lüftungsschacht
PT	Putztürchen
PS	Putzstück
KT	Kehrtürchen
ABL	Abluft
ZUL	Zuluft
DBA	Druckbelüftungsanlage
DES	Druckentlastungsschacht
BÖ	Belüftungsöffnung
ÜÖ	Überströmöffnung
AÖ	Abströmöffnung mit Überdruckentlastungsorgan
BSK	Brandsschutzklappe
FBHV	Fussbodenheizungsverteiler
E-Verteiler	Elektroverteiler

Öffnungen und deren Abschlüsse

WD	Wanddurchbruch
DD	Deckendurchbruch
FBD	Fußbodendurchbruch
FDD	Fundamentdurchbruch
WS	Wandschlitz
WA	Wandaussparung
DA	Deckenaussparung
FBA	Fußbodenaussparung
RBL	Rohbaulichte
AL	Architekturlichte
STL	Stocklichte
GL	Glaslichte
STAM	Stockaußenmaß
DL	Durchgangslichte
GGT	Ganzglastüre
MGT	Metallgittertür
HT	Hebetüre
HST	Hebeschiebetüre
T	Türe
AT	Allgemeintüre
ET	Eingangstüre
WET	Wohnungseingangstür
IT	Innentür
DF	Drehflügel
DKF	Drehkippflügel
SF	Schiebe-Fenster
SWF	Schwingflügel
WF	Wendeflügel
K	Kippfenster
OL	Oberlichte
DF	Dachfächenfenster
PFR	Pfostenriegelkonstruktion
FE	Fenster
FT	Fenstertüre
R	Rechtsöffnend
L	Linksöffnend
FIX	Fixverglasung
VSG	Verbund-Sicherheitsglas
ESG	Einscheiben-Sicherheitsglas

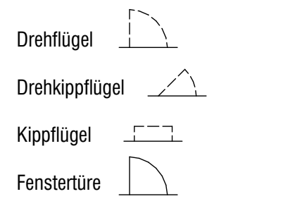

EI2 30-C-, EI2 60-C-und EI2 90-C
Feuerschutztüren mit Angabe der Feuerwiderstandsklasse
(gemäß ÖNORM B 3850 und ÖNORM B 3807)

GT	gasdichte Türe
DT	Drucktüre
S 200	Rauchabschluss
S 200	Rauchabschluss
C	Selbstschließend
FLS	Freilaufschließer
LVfTÖ	Lehrverrohrung für Türöffner
elTÖ	elektrischer Türöffner

AUSFÜHRUNG POLIERPLAN GESAMT

Bauvorhaben
VÖSL100

2500 Baden, Vöslauerstraße 100

XXX

Katastralgemeinde 4025 Rauhenstein
EZ: 2412
GstNr.: .424

Diese Zeichnung bzw. Ausarbeitung sowie deren Daten auf Datenträgern sind geistiges Eigentum des Erstellers Arch. Artmüller Georg. Jede Benützung, Veröffentlichung,Vervielfältigung jeglicher Art oder Weitergabe an Dritte bedarf der schriftlichen Zustimmung durch Architekt Artmüller.

Durch die Übernahme dieses Planes akzeptiert die ausführende Firma bzw. Person die darauf dargestellten Anordnungen. Geschriebene Planmaße auf dieser Zeichnunghaben Vorrang gegenüber gezeichneten Dimensionen. Der Auftragnehmer verpflichtet sich **vor** Arbeitsbeginn alle Maße und Bedingungen im Zusammenhang mit seinerArbeit auf der Baustelle verantwortlich zu überprüfen.

Abweichungen gegenüber dargestellten oder schriftlich vereinbarten Anordnungen müssen Architekt Artmüller und der Bauleitung unverzüglich schriftlich mitgeteiltwerden. Vor Arbeitsbeginn sind dem Architekten gültige Werkzeichnungen zur Genehmigung vorzulegen.

NATURMASSE SIND ZU NEHMEN, KOTEN ZU PRÜFEN

VORABZUG
15. 09. 2026

Index	Datum	Bearbeiter	Änderung	

Index Änderung Datum

Grundeigentümer

Bauwerber / Auftraggeber

ARTMÜLLER ARCHITEKTEN
ZIVILTECHNIKER GMBH
Stolberggasse 34|26 A-1050 Wien
t [+43] 01 . 581 40 83 f [+43] 01. 581 40 83 99 office@artmueller.eu

Planinhalt
Ansichten

Maßstab	Gez	Datum	Plannr.	Index
	LM	16-10-2026	VÖSL100_50_06	01

Erstellt, am 11.11.2026

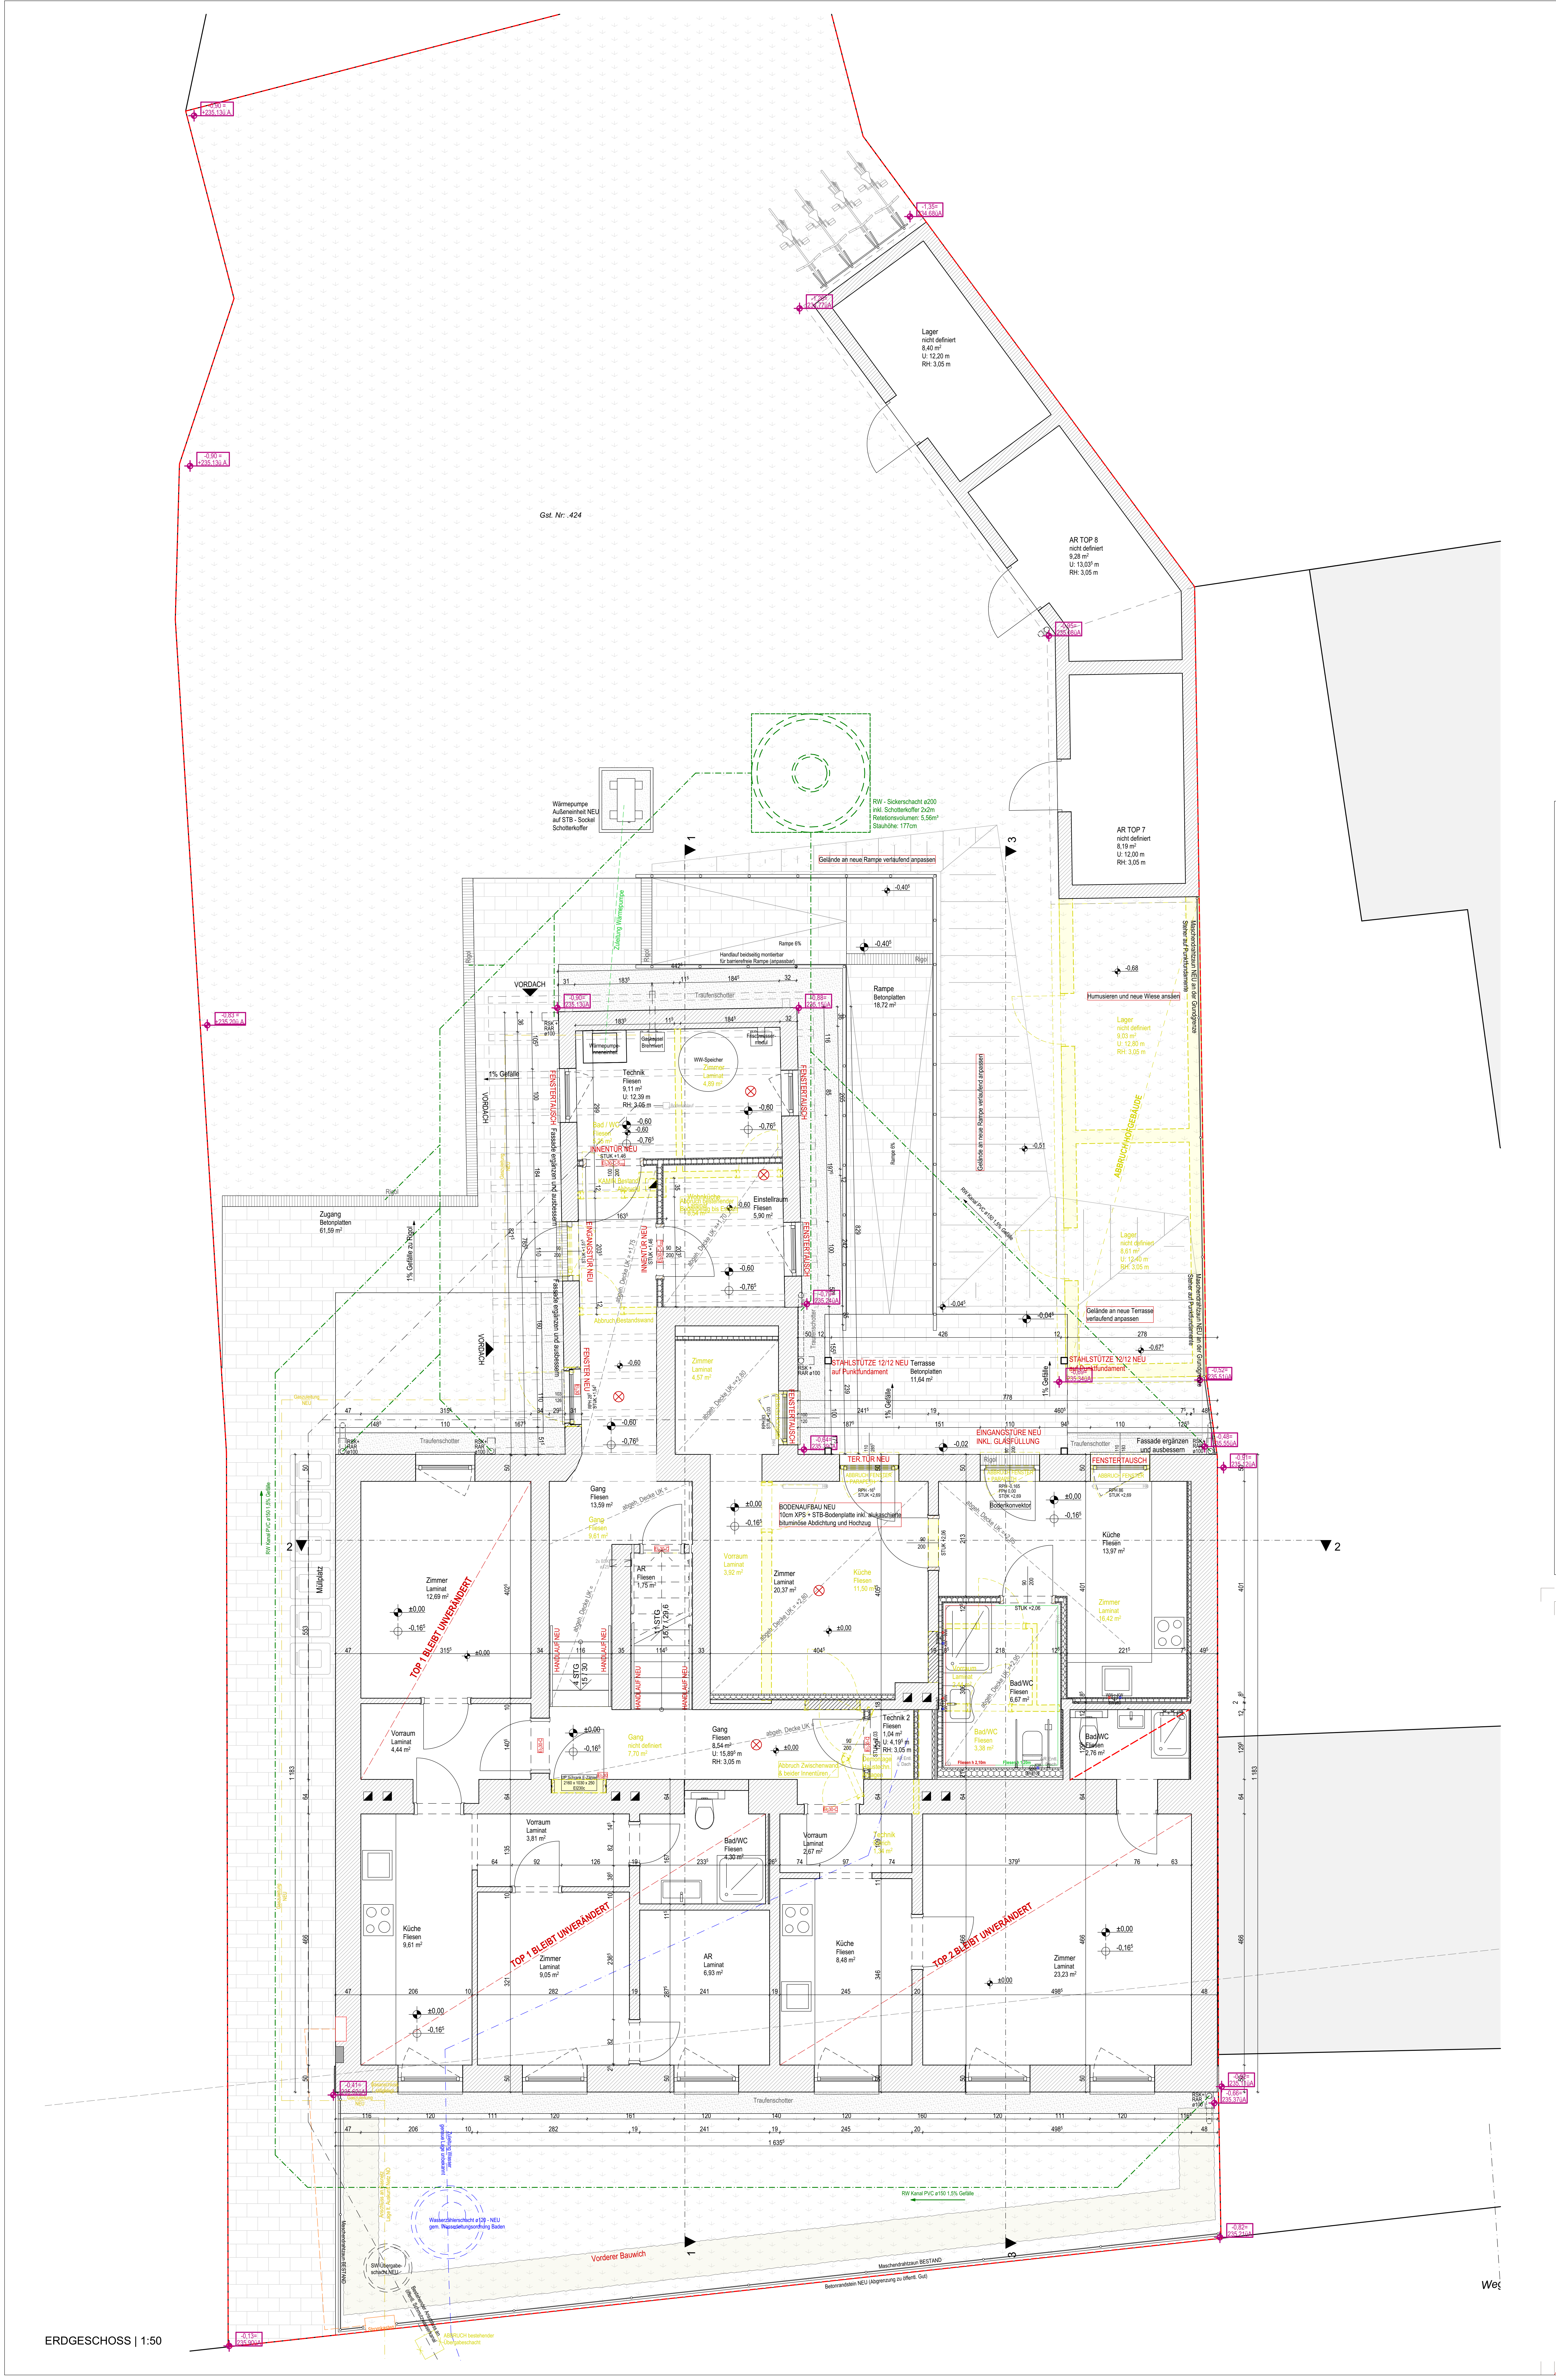

ERDGESCHOSS | 1:50

LEGENDE

☒	Wanddurchbruch
	Deckendurchbruch
	Bodenschlitz
	Bodendurchbruch
▼	OK Fertigbau
▲	UK Fertigbau
▽	OK Rohbau
△	UK Rohbau
± 0,00	Höhenangabe einer waagrechten Fläche
±0,00	Höhenangabe eines Punktes in einem Bauwerk - Fertigmaß
±0,00	Höhenangabe eines Punktes in einem Bauwerk - Rohbaumaß
BGF	Bruttogesamtfläche
HNF / NNF	Haupt- Nebennutzfläche

▨	Mauerwerk (wärmedämmend)
▨	Mauerwerk (nicht wärmedämmend)
▨	unbewehrter Beton
▨	bewehrter Beton
▦	Betonfertigteil
▤	Stein
▨	Stahl (allgemein)
▨	Holz (allgemein)
▨	Holzwerkstoffe
▩	Dämmstoff (hart)
▩	Dämmstoff (weich)
▩	Kunststoff (allgemein)
▚	Dichtstoff (allgemein)
▥	Gips (Gipskartonplatte)
▥	Gipskartonplatte Brandschutz
☐	Erdmaterial (allgemein)
⬜	Bestand
🟨	Abbruch
🟥	Neubau

—	Medien
—	Fernwärme
—	Gas
—	Strom
—	Heizung
—	Regenwasser
—	Schmutzwasser
—	Wasser
—	Blech
- - -	Abdichtung
- - -	Folie
- - -	Dampfsperre, -bremse

Höhenbezugs- und Maßangaben

DOK	Deckenoberkante
DOS	Deckenoberseite
DUK	Deckenunterkante
DUS	Deckenunterseite
DUF	Deckenunterkante (fertige Untersicht)
FBOK	Fußbodenoberkante
OFF	Oberfläche des fertigen Fußbodens
FDOK	Fundamentoberkante
FDOS	Fundamentoberseite
FDUK	Fundamentunterkante
FDUS	Fundamentunterseite
RH	lichte Raumhöhe
GH	Geschoßhöhe
OK	Oberkante
OS	Oberseite
UK	Unterkante
US	Unterseite
STUK	Sturzunterkante (Rohbaumaß)
STH	Sturzhöhe gemessen von STUK bis DUK (Rohbaumaß)
RPH	Rohbauparapethöhe
FPH	fertige Parapethöhe (FBOK bis OK Fensterbank Innen)

Rauch-, Abgas- und Luftfänge, Schächte

L	Lüftungsschacht
PT	Putztürchen
PS	Putzstück
KT	Kehrtürchen
ABL	Abluft
ZUL	Zuluft
DBA	Druckbelüftungsanlage
DES	Druckentlastungsschacht
BÖ	Belüftungsöffnung
ÜÖ	Überströmöffnung
AÖ	Abströmöffnung mit Überdruckentlastungsorgan
BSK	Brandsschutzklappe
FBHV	Fussbodenheizungsverteiler
E-Verteiler	Elektroverteiler

Öffnungen und deren Abschlüsse

WD	Wanddurchbruch
DD	Deckendurchbruch
FBD	Fußbodendurchbruch
FDD	Fundamentdurchbruch
WS	Wandschlitz
WA	Wandaussparung
DA	Deckenaussparung
FBA	Fußbodenaussparung
RBL	Rohbaulichte
AL	Architekturlichte
STL	Stocklichte
GL	Glaslichte
STAM	Stockaußenmaß
DL	Durchgangslichte
GGT	Ganzglastüre
MGT	Metallgittertür
HT	Hebetüre
HST	Hebeschiebetüre
T	Türe
AT	Allgemeintüre
ET	Eingangstüre
WET	Wohnungseingangstür
IT	Innentür
DF	Drehflügel
DKF	Drehkippflügel
SF	Schiebe-Fenster
SWF	Schwingflügel
WF	Wendeflügel
K	Kippfenster
OL	Oberlichte
DF	Dachfächenfenster
PFR	Pfostenriegelkonstruktion
FE	Fenster
FT	Fenstertüre
R	Rechtsöffnend
L	Linksöffnend
FIX	Fixverglasung
VSG	Verbund-Sicherheitsglas
ESG	Einscheiben-Sicherheitsglas

Drehflügel
Drehkippflügel
Kippflügel
Fenstertüre

EI2 30-C-, EI2 60-C-und EI2 90-C
Feuerschutztüren mit Angabe der Feuerwiderstandsklasse
(gemäß ÖNORM B 3850 und ÖNORM B 3807)

GT	gasdichte Türe
DT	Drucktüre
S 200	Rauchabschluss
S 200	Rauchabschluss
C	Selbstschließend
FLS	Freilaufschließer
LVfTÖ	Lehrverrohrung für Türöffner
elTÖ	elektrischer Türöffner

AUSFÜHRUNG POLIERPLAN GESAMT

Bauvorhaben
VÖSL100

2500 Baden, Vöslauerstraße 100

XXX

Katastralgemeinde 4025 Rauhenstein
EZ: 2412
GstNr.: .424

Diese Zeichnung bzw. Ausarbeitung sowie deren Daten auf Datenträgern sind geistiges Eigentum des Erstellers Arch. Artmüller Georg. Jede Benützung, Veröffentlichung,Vervielfältigung jeglicher Art oder Weitergabe an Dritte bedarf der schriftlichen Zustimmung durch Architekt Artmüller.

Durch die Übernahme dieses Planes akzeptiert die ausführende Firma bzw. Person die darauf dargestellten Anordnungen. Geschriebene Planmaße auf dieser Zeichnunghaben Vorrang gegenüber gezeichneten Dimensionen. Der Auftragnehmer verpflichtet sich **vor** Arbeitsbeginn alle Maße und Bedingungen im Zusammenhang mit seinerArbeit auf der Baustelle verantwortlich zu überprüfen.

Abweichungen gegenüber dargestellten oder schriftlich vereinbarten Anordnungen müssen Architekt Artmüller und der Bauleitung unverzüglich schriftlich mitgeteiltwerden. Vor Arbeitsbeginn sind dem Architekten gültige Werkzeichnungen zur Genehmigung vorzulegen.

NATURMASSE SIND ZU NEHMEN, KOTEN ZU PRÜFEN

VORABZUG
15. 09. 2026

Index	Datum	Bearbeiter	Änderung

Index	Änderung	Datum

Grundeigentümer

Bauwerber / Auftraggeber

ARTMÜLLER ARCHITEKTEN
ZIVILTECHNIKER GMBH
Stolberggasse 34|26 A-1050 Wien
t [+43] 01 . 581 40 83 f [+43] 01. 581 40 83 99 office@artmueller.eu

Planinhalt
Aussenanalagen

Maßstab	Gez	Datum	Plannr.	Index
	LM	16-10-2026	VÖSL100_50_07	01

Erstellt, am 11.11.2026