BAUTEILLISTE

DA01 Schrägdach - Leichtdach

5,0 cm	Trapezblech Alu / Hinterlüftung diffusionsoffene Unterdachbahn
2,4 cm	Vollholzschalung
20,0 cm	, Holzkonstruktion, dazwischen 20cm Mineralwolle Wärmedämmung
6,0 cm	Unterkonstruktion Profile, dazwischen 6cm Mineralwolle Wärmedämmung Dampfbremse
2,5 cm	Gipskartonfeuerschutzplatten 2x12,5mm
3,0 cm	Installationsebene
1,25 cm	Gipskartonfeuerschutzplatten
40,0 cm	gesamt

FB01 Fußboden Wohnungen, Fundamentplatte

2,0 cm	Belag (alt.Abdichtung in Nassräumen)
7,0 cm	Heizestrich Folie
3,0 cm	Trittschalldämmung EPS T 650
4,5 cm	Schüttung
0,5 cm	Abdichtung
30,0 cm	Stahlbetonplatte Gleitschicht
16,0 cm	Wärmedämmung XPS
8,0 cm	Sauberkeitsschicht Folie
25,0 cm	Rollierung
96,0 cm	gesamt

FB02 Decke - Wohnraum über Wohnraum

2,0 cm	Belag (alt.Abdichtung in Nassräumen)
7,0 cm	Heizestrich
3,0 cm	Trittschalldämmung EPS T 650
5,0 cm	Schüttung
18,0 cm	Stahlbetondecke Spachtelung
35,0 cm	gesamt

FB02A Decke über EG - Wohnraum über Nebenräume

2,0 cm	Belag (alt.Abdichtung in Nassräumen)
7,0 cm	Heizestrich
3,0 cm	Trittschalldämmung EPS T 650
5,0 cm	Schüttung
18,0 cm	Stahlbetondecke
7,5 cm	Wärmedämmung A2 z.B.: Tektalan A2 E-31 oder gleichwertig
42,5 cm	gesamt

FB02B Decke über EG - Wohnraum über STH - abgeh.DE

2,0 cm	Belag (alt.Abdichtung in Nassräumen)
7,0 cm	Heizestrich
3,0 cm	Trittschalldämmung EPS T 650
5,0 cm	Schüttung
18,0/20,0 cm	Stahlbetondecke
19,0 cm	Installationsebene mit Luftraum und 8cm Mineralwolle Wärmedämmung
1,25 cm	Gipskartonfeuerschutzplatten
55,0-57,0 cm	gesamt

FB02C Decke über EG - Wohnraum über Eingangsbereich

2,0 cm	Belag (alt.Abdichtung in Nassräumen)
7,0 cm	Heizestrich
3,0 cm	Trittschalldämmung EPS T 650
5,0 cm	Schüttung
18,0 cm	Stahlbetondecke
12,0 cm	Wärmedämmung EPS F plus
0,40 cm	Kunstharzputz armiert
47,5 cm	gesamt

AW01 Außenwand Faserzementplatten

1,0 cm	Faserzementplatten
4,0 cm	Lattung, Hinterlüftung Winddichtbahn, diffusionsoffen
14,0 cm	Holztragkonstruktion 5/14, Abstand 70cm, dazwischen Mineralwolle 0,038 W/mK
20,0 cm	Hochlochiegel, min. 1108 kg/m3, z.B.: Wienerberger Porotherm 20-40 Objekt N+F oder gleichwertig
1,0 cm	Innenputz
40,0 cm	gesamt

AW02 Außenwand Trapezblech Alu

5,0 cm	Trapezblech Alu, Hinterlüftung Winddichtbahn, diffusionsoffen
14,0 cm	Holztragkonstruktion 5/14, Abstand 70cm, dazwischen Mineralwolle 0,038 W/mK
20,0 cm	Hochlochiegel, min. 1108 kg/m3, z.B.: Wienerberger Porotherm 20-40 Objekt N+F oder gleichwertig
1,0 cm	Innenputz
40,0 cm	gesamt

AW03 Außenwand im Eingangsbereich

0,40 cm	Kunstharzputz armiert
10,0 cm	Wärmedämmung EPS F
20,0 cm	Hochlochiegel, min. 1108 kg/m3, z.B.: Wienerberger Porotherm 20-40 Objekt N+F oder gleichwertig
1,0 cm	Innenputz
31,5 cm	gesamt

AW01s Außenwand - Sockelbereiche

0,4 cm	Kunstharzputz, armiert
10,0 cm	Wärmedämmung XPS
1,0 cm	Zementmörtel
20,0 cm	Macuphon 20
1,0 cm	Innenputz
32,5 cm	gesamt

IW01 Wohnungstrennwand, Stb + GK-VS

1,25 cm	Gipskartonplatten
5,0 cm	Metallsteher Profile CW 50, dazwischen 5,0cm Mineralwolle
20,0 cm	Stahlbeton, Elektroinstallationen Spachtelung
26,3 cm	gesamt

IW01s Wand zw. Wohnung und Stiegenhaus, Stb+VSS

1,25 cm	Gipskartonplatten
5,0 cm	Metallsteher Profile CW 50, dazwischen 5,0cm Mineralwolle
20,0 cm	Stahlbeton, Elektroinstallationen Spachtelung
26,3 cm	gesamt

IW01e Trennwand zw. Wohnung u.Einlagerungsr., Stb+VSS

1,25 cm	Gipskartonplatten (wohnraumseitig) Dampfbremse
5,0 cm	Metallsteher Profile CW 50, dazwischen 5,0cm Mineralwolle
20,0 cm	Stahlbeton Spachtelung
26,3 cm	gesamt

IW02 Wand zw. Wohnung und Stiegenhaus, Ziegel+VSS

	Putz, Spachtelung
20,0 cm	Hochlochiegel, min. 1108 kg/m3, z.B.: Wienerberger Porotherm 20-40 Objekt N+F oder gleichwertig, keine Elektroinstallationen
5,0 cm	Metallsteher Profile CW 50, dazwischen 5,0cm Mineralwolle
1,25 cm	Gipskartonfeuerschutzplatten, gangseitig
26,3 cm	gesamt

IW03 Trennwand wohnungsintern

0,5 cm	Innenputz
20,0 cm	Hochlochziegel
0,5 cm	Innenputz
21,0 cm	gesamt

IW04 Innenwand 15cm wohnungsintern

2,5 cm	Gipskartonfeuerschutzplatten 2x12,5mm (imprägniert in Nassräumen)
10,0 cm	Metallsteher Profile CW 100, dazwischen 10,0cm Mineralwolle
2,5 cm	Gipskartonfeuerschutzplatten 2x12,5mm (imprägniert in Nassräumen)
15,0 cm	gesamt

IW05 Innenwand 12,5cm wohnungsintern

1,25 cm	Gipskartonfeuerschutzplatten 12,5mm (imprägniert in Nassräumen)
10,0 cm	Metallsteher Profile CW 100, dazwischen 10,0cm Mineralwolle
1,25 cm	Gipskartonfeuerschutzplatten 12,5mm (imprägniert in Nassräumen)
12,5 cm	gesamt

S01 Schachtwand (geschoßweise Brandschott)

	Schacht mit Mineralwolle dicht ausstopfen
1,25 cm	Gipskartonplatten

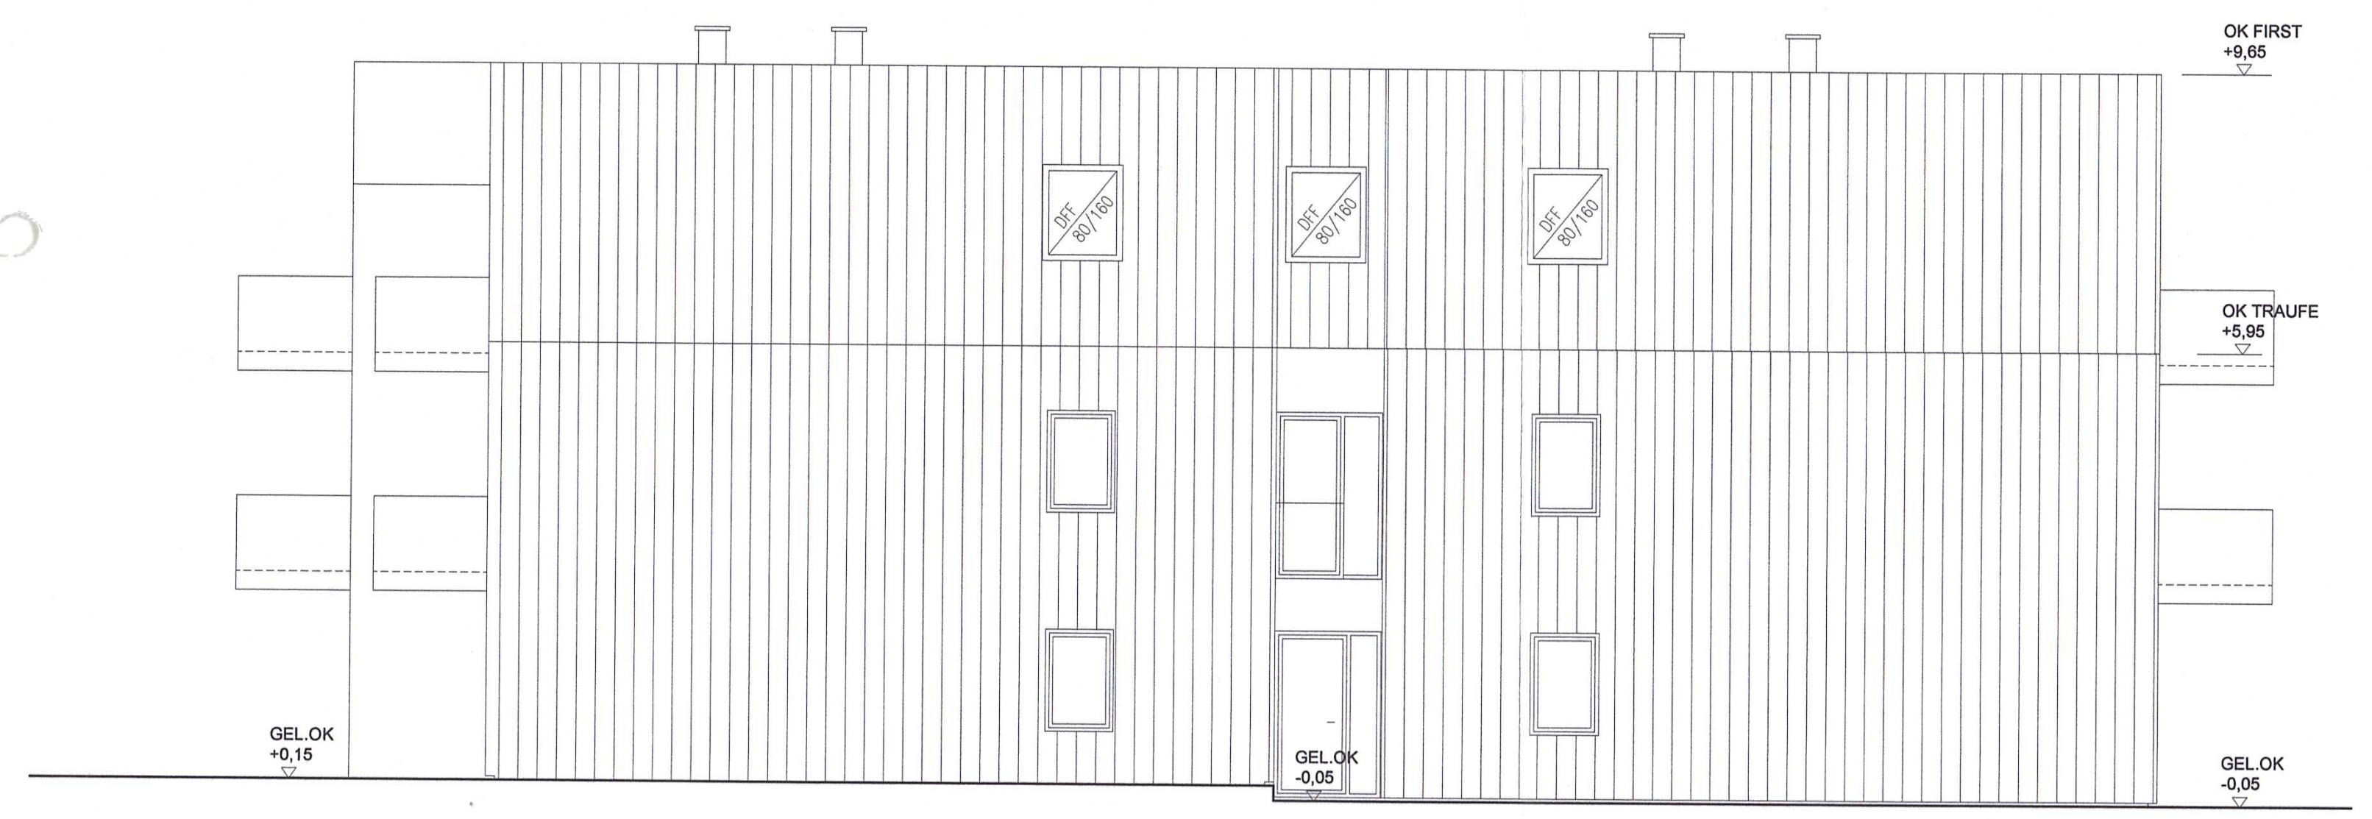

ANSICHT SÜD 1:100

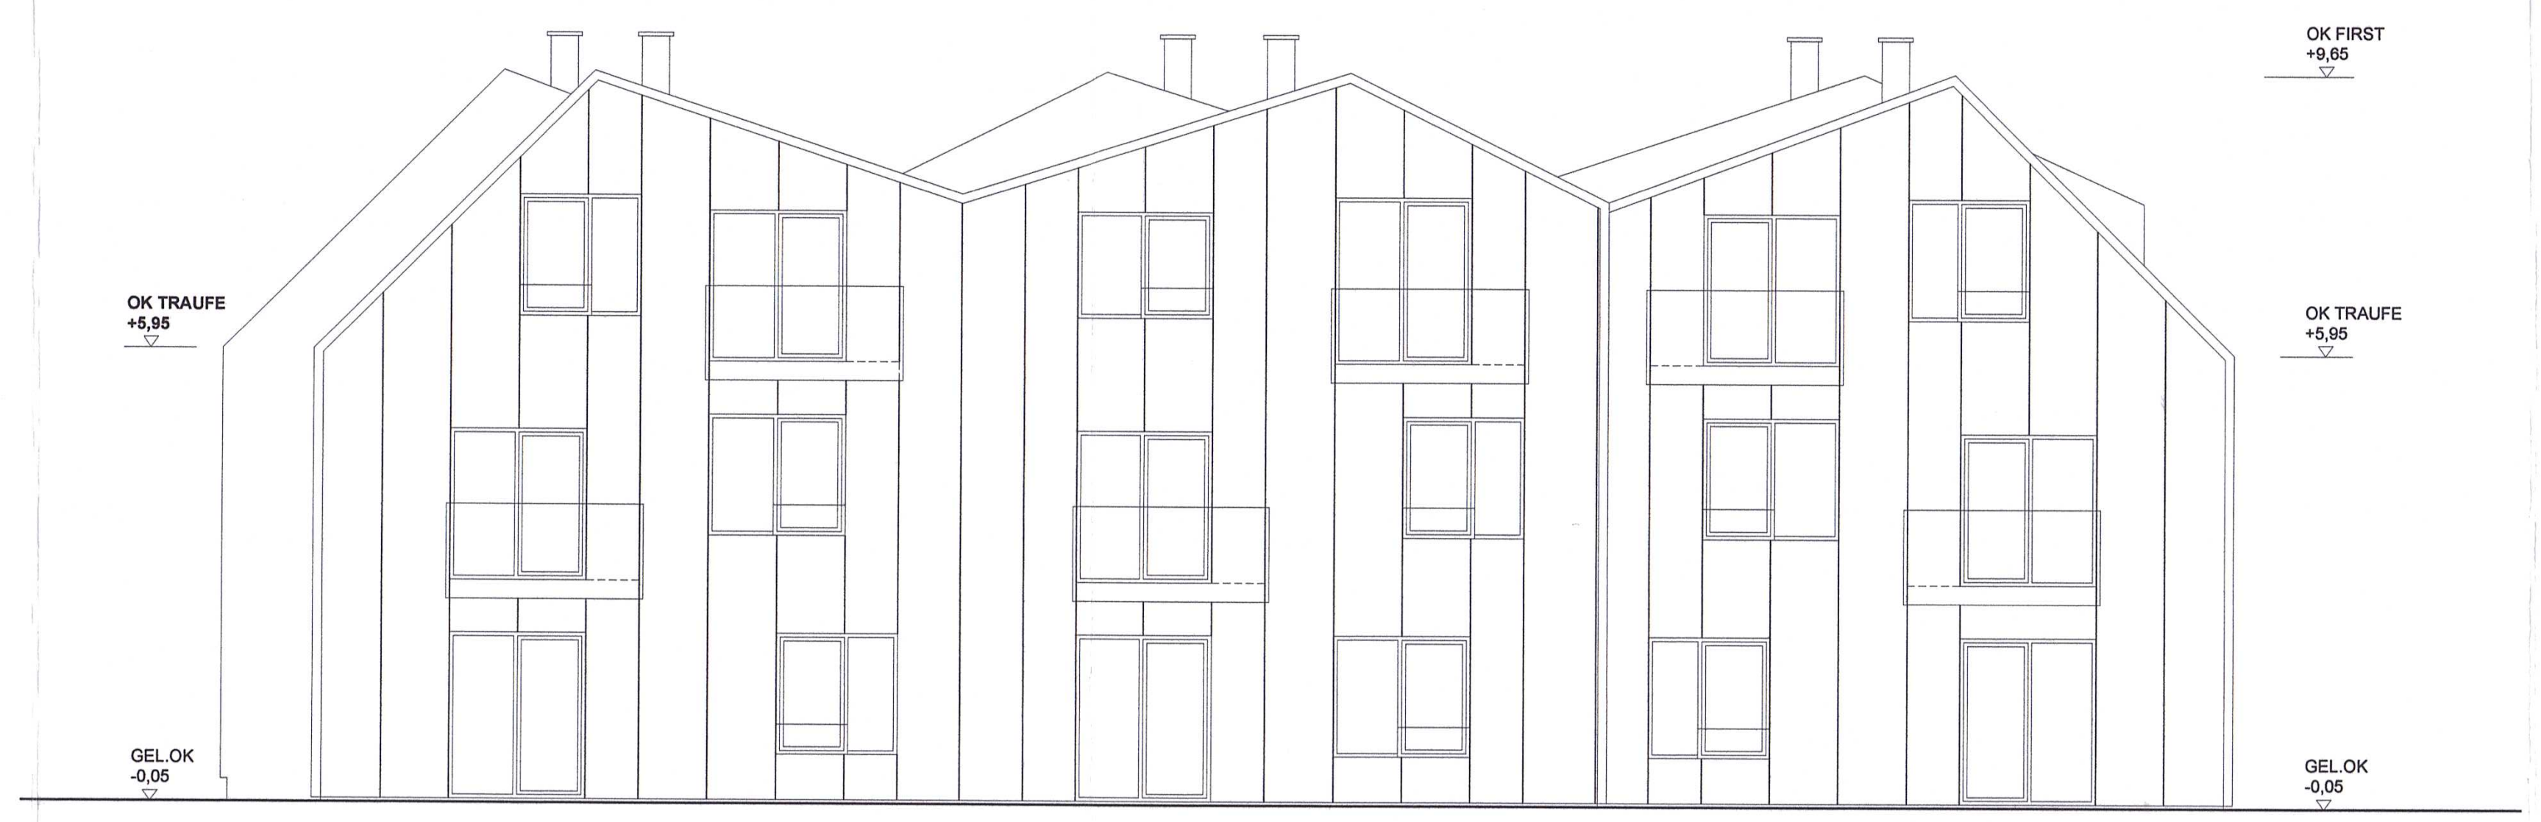

ANSICHT OST 1:100

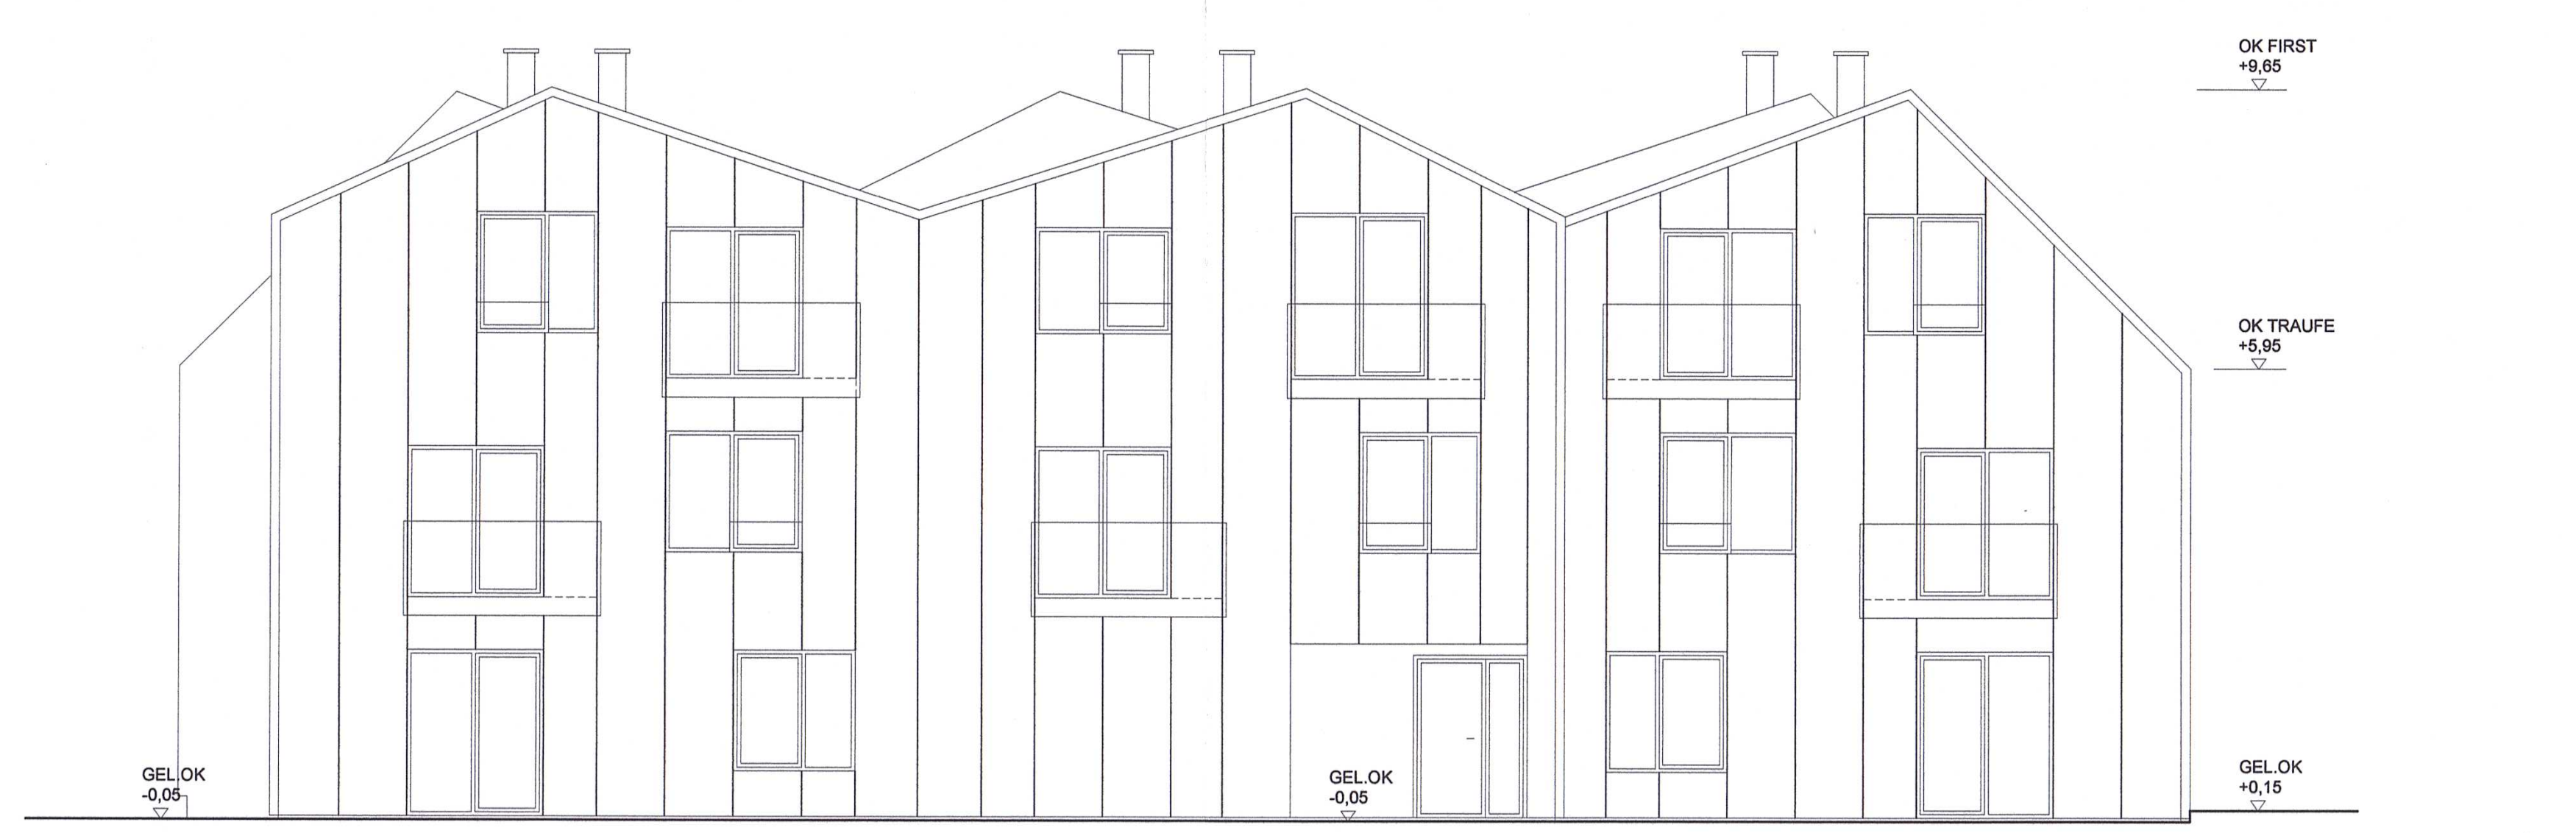

ANSICHT WEST 1:100

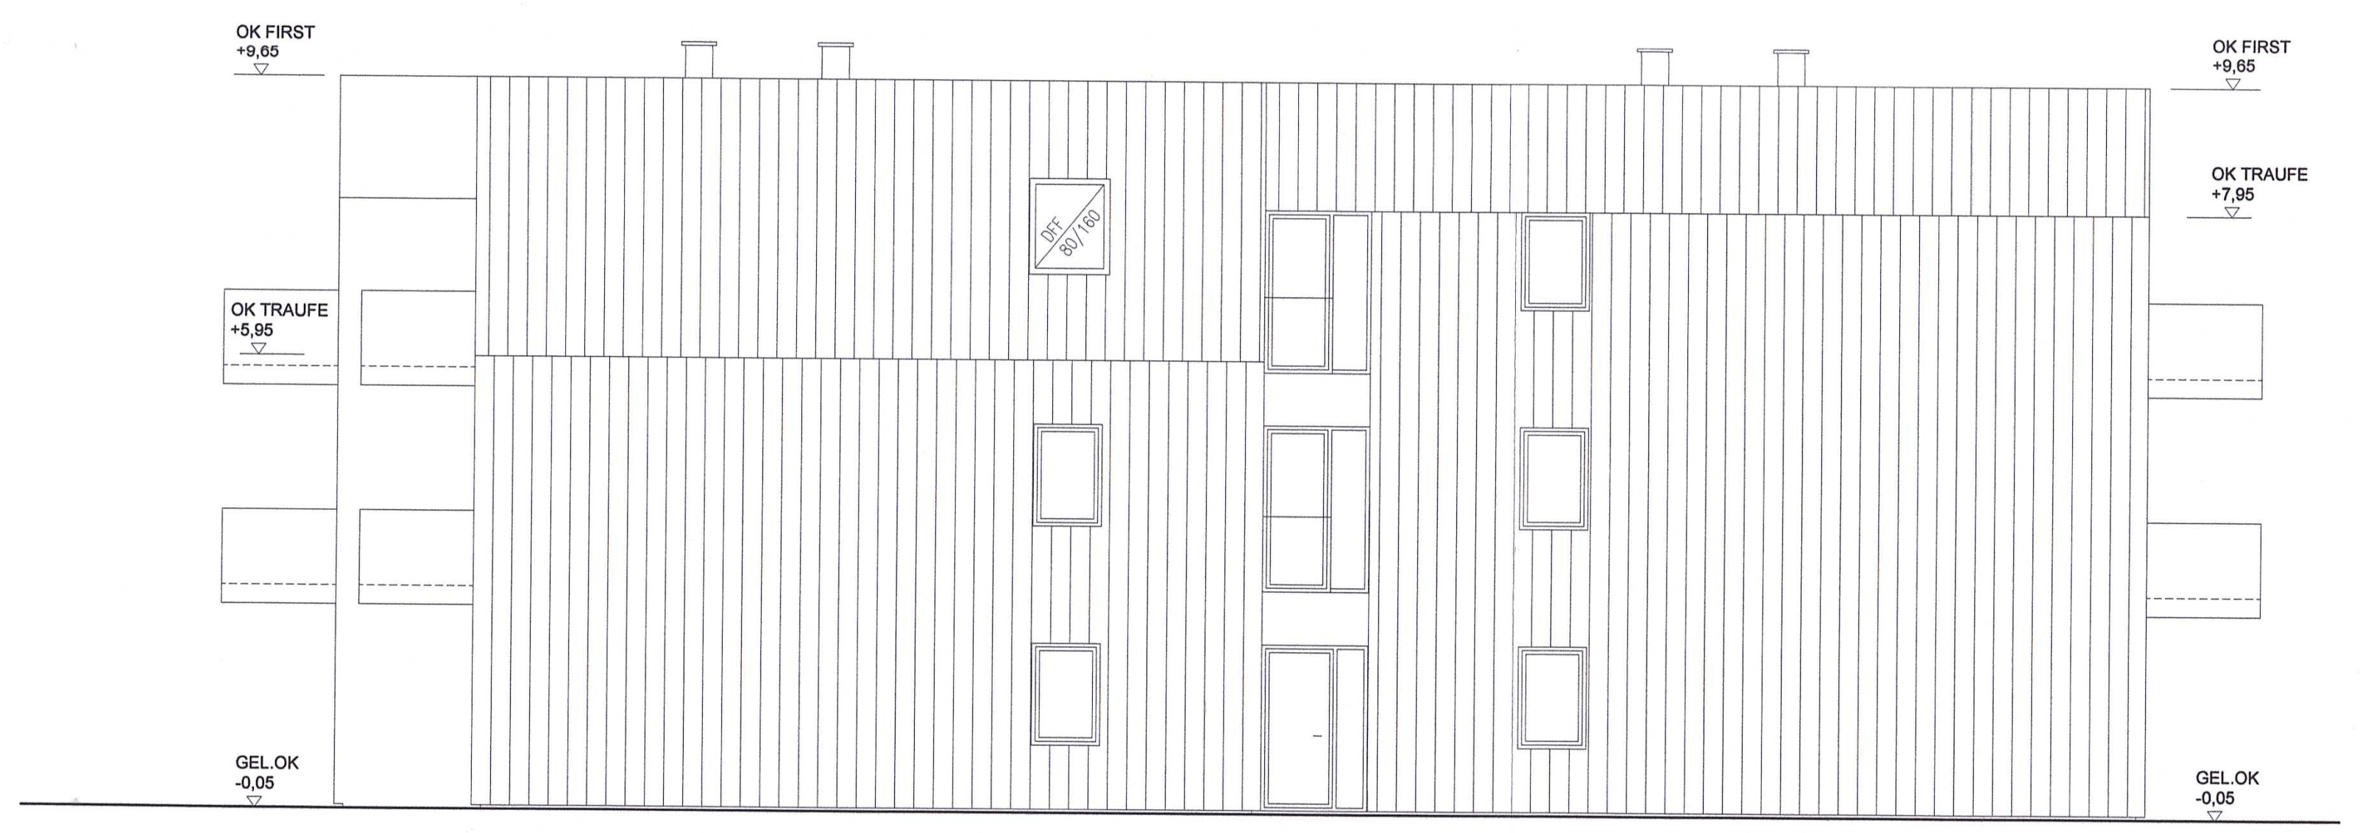

ANSICHT NORD 1:100

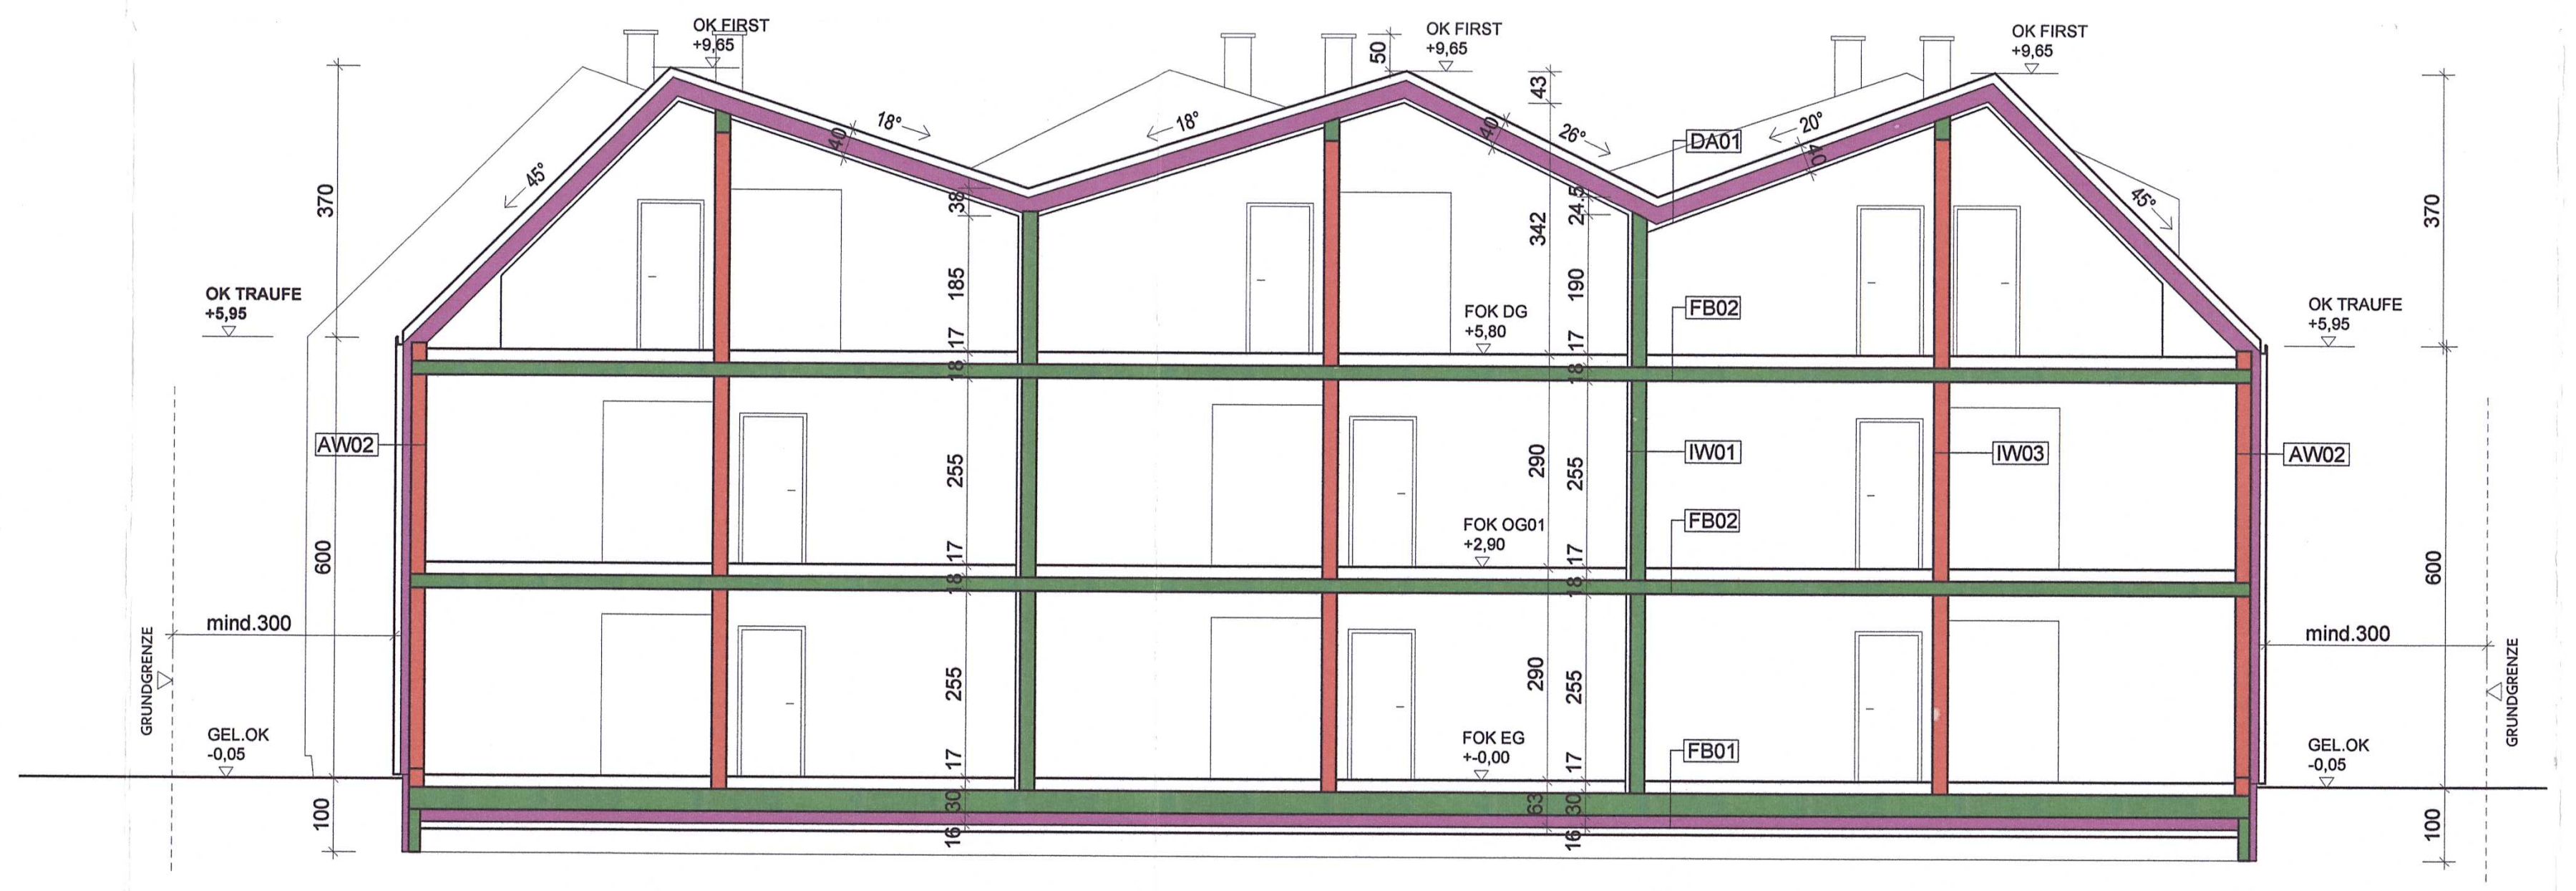

SCHNITT B-B 1:100

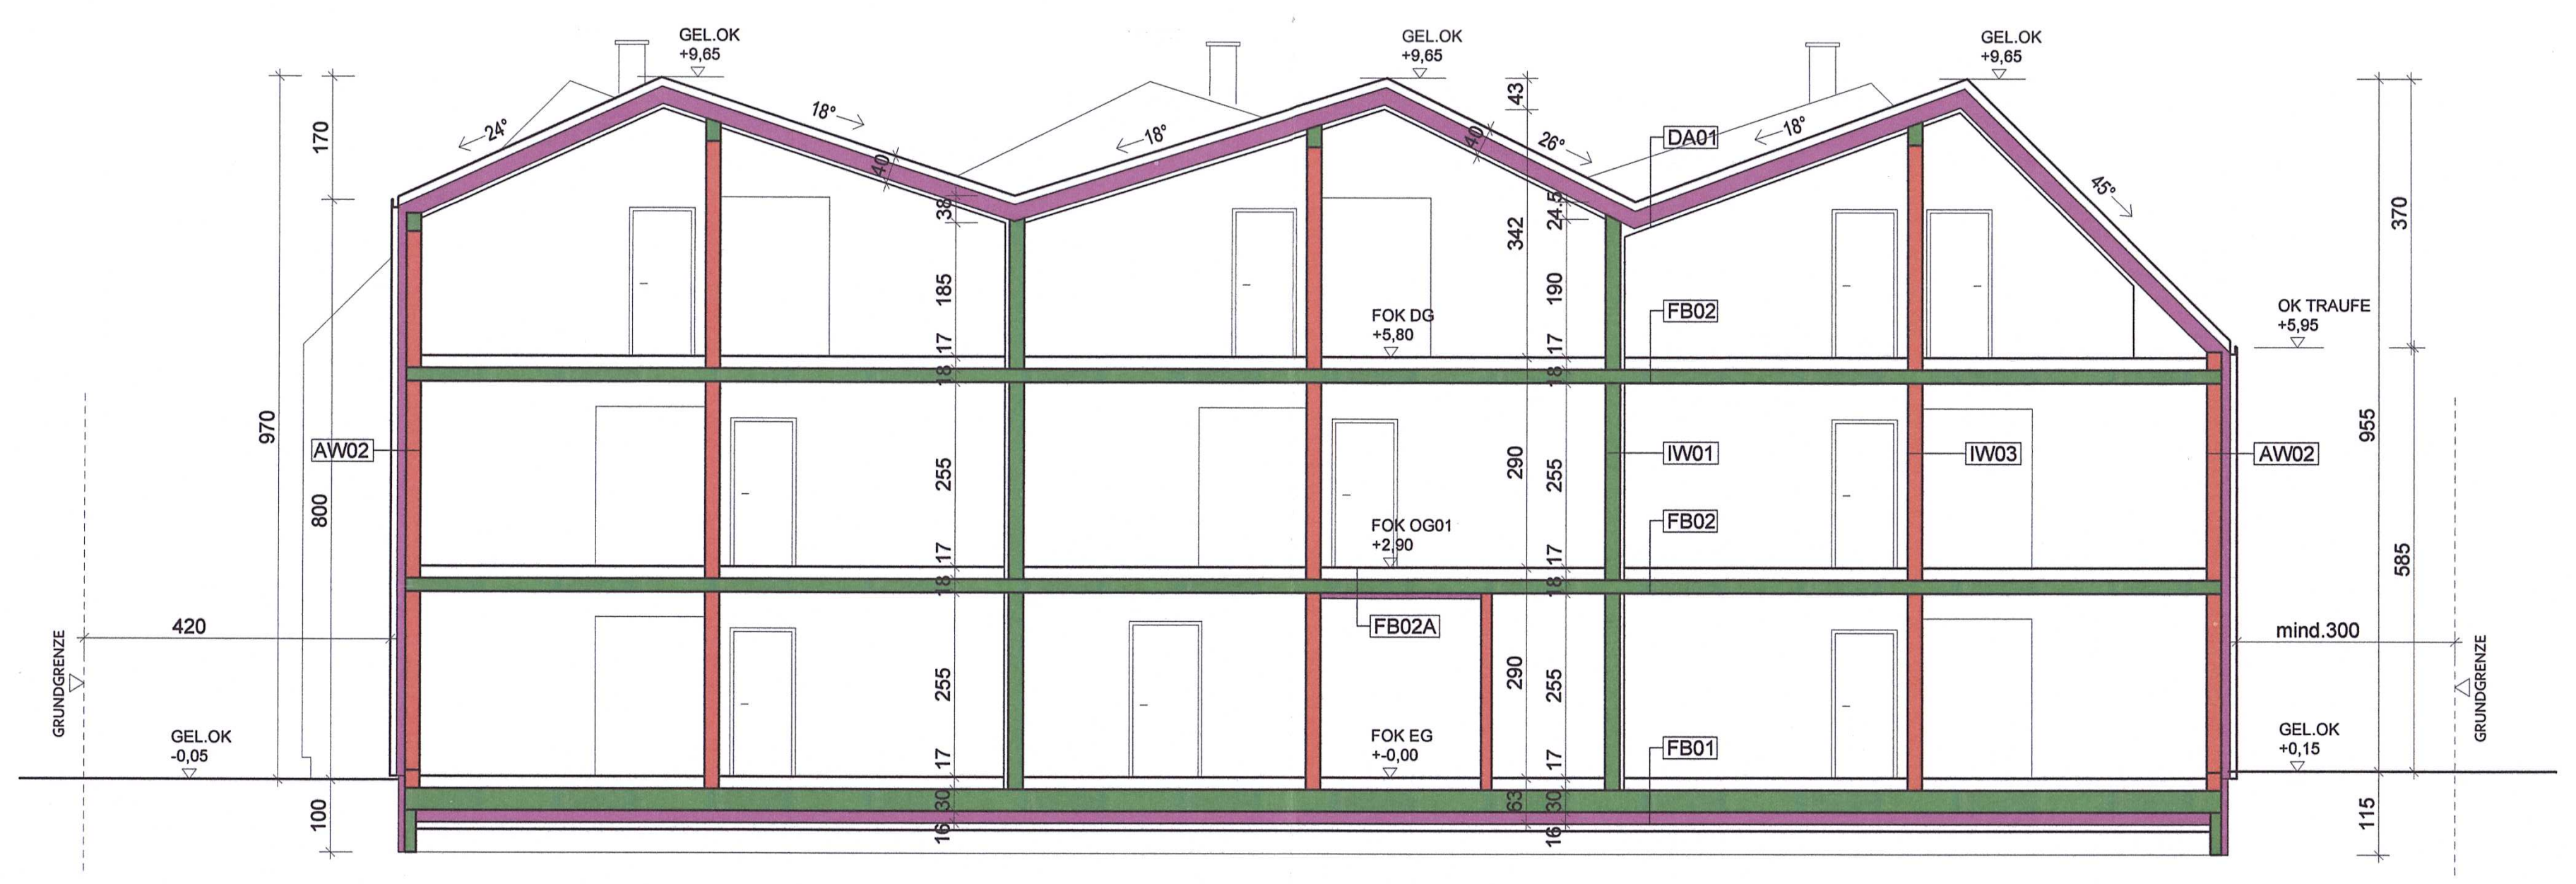

SCHNITT A-A 1:100

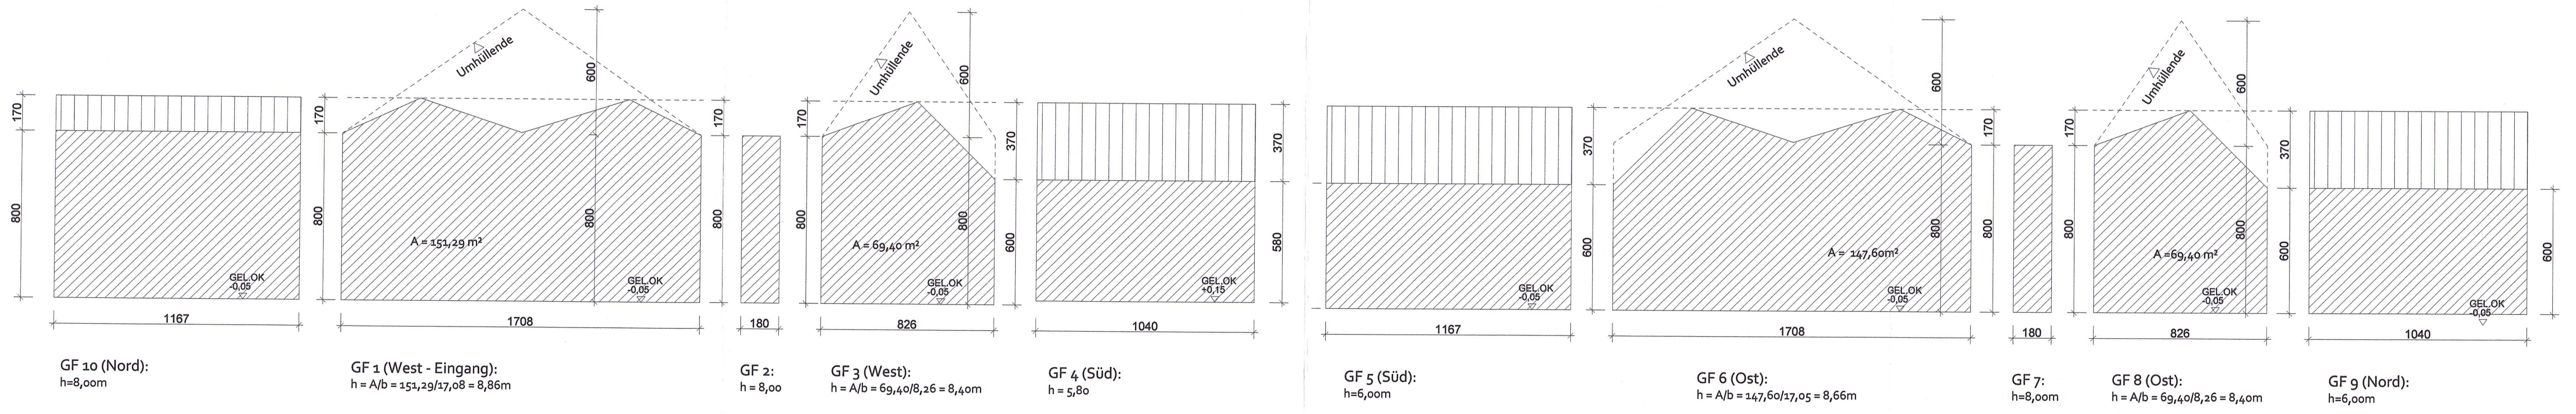

FASSADENABWICKLUNG 1:200

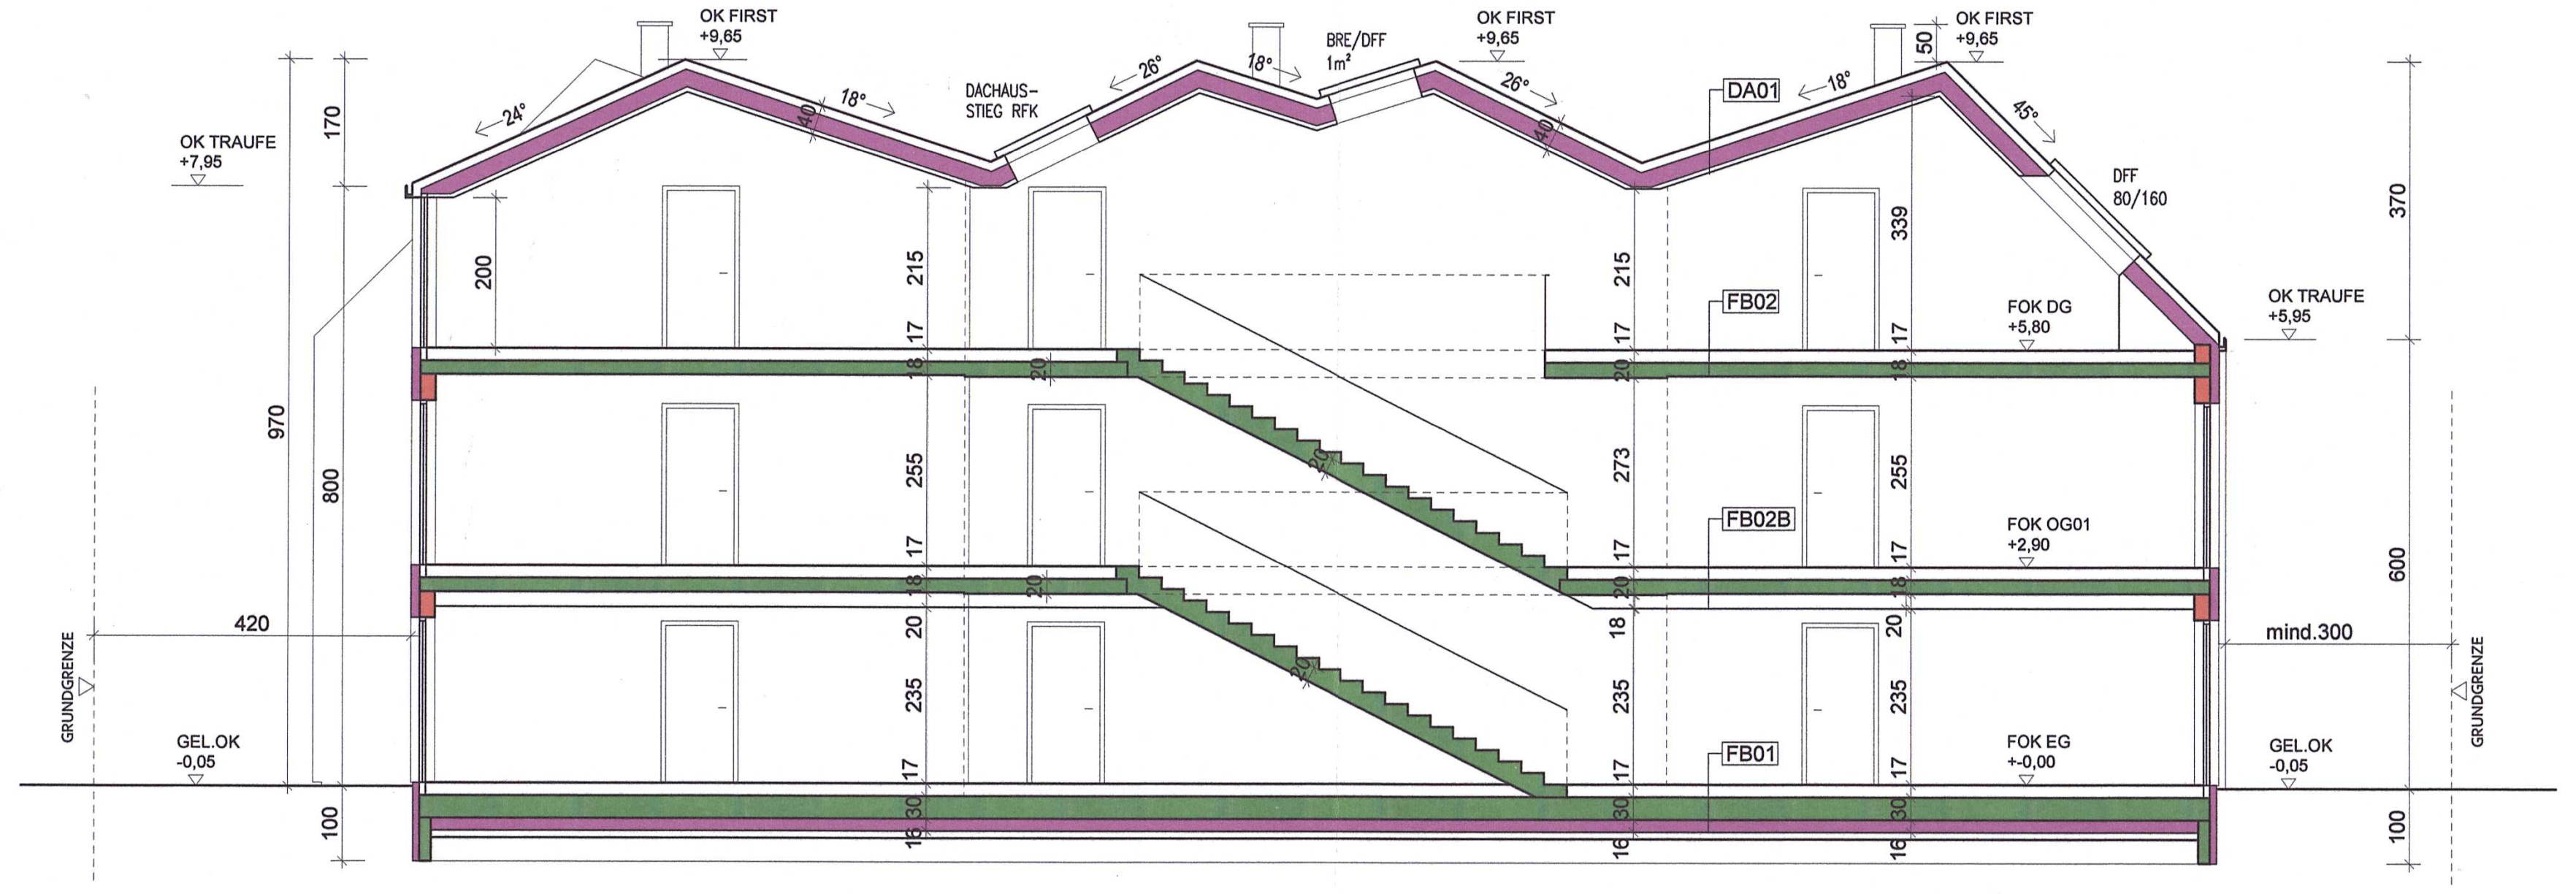

SCHNITT C-C 1:100

ABKÜRZUNGEN:

AL	Abluft	KT	Kehrtüre	RFK	Rauchfangkehrer	UK	Unterkante
AR	Abwasserrohr	LÜ	mech.Lüftung	RH	Raumhöhe	ÜL	Überlüftung
BA	Bodenablauf	FIX	Fixverglasung	RAR	Regenrohr	UZ	Unterzug
DA	Dunstabzug	NK	Notkamin	RM	Rauchmelder	VSG	Verbund-Sicherheitsglas
Gel.	Gelände	OK	Oberkante	RSK	Regensinkkasten	WM	Waschmaschine
KS	Kanalsohle	OL	Oberlichte	RS	Rauchsensor	ZUL	Zuluft
				TR	Wäschetrockner		

LEGENDE:

Bestand	⬜	Ziegel	🟥	Wärmedämmung	🟪
Neu	🟥	(Stahl-)Beton	🟩	Trockenbau	🟧
Abbruch	🟨				

GEMEINDE EINGELANGT BA am:
05. JULI 2017

EINREICHPLAN

f. die Errichtung eines Mehrfamilienhauses mit 14 Wohnungen
in der WALDGASSE 21, 2542 KOTTINGBRUNN

Gst.: 555/23, EZ 4060, KG: 04016 Kottingbrunn

BAUWERBER, GRUNDEIGENTÜMER:	BEHÖRDE:
Hr. Gazmen Qupi Heuweg 20 2751 Steinabrückel	Handschriftliche Änderungen am 15. September 2017
MARKTGEMEINDE KOTTINGBRUNN BAUAMT Bundesgebühr: € 7,80 unter Zahl: BAU-28-2017 am 17. Okt. 2017 vorgeschrieben / entrichtet.	Ist der Verhandlung am 26.09.2017 vorgelegen. Kottingbrunn, am 17.10.2017 Der (Für den) Bürgermeister:
Hierauf bezieht sich der Bescheid vom 17.10.2017 Zl. BAU-28-2017 Kottingbrunn, am 17.10.2017 Der (Für den) Bürgermeister:	
PLANVERFASSER:	**BAUFÜHRER:**
Arch.DI Marc Wohlschak Schönbrunnersraße 14A/4-5 1050 Wien tel.: 0699 18053440 email: mail@wohlschak.at	

	Dat	Mst	Plangr	Inhalt	Plannummer
A B C D	EINREICHUNG 30.06.2017	1:200 1:100	1250/600	ANSICHTEN SCHNITTE	KOT-EPL-02