




DACHDRAUFSICHT 1:100

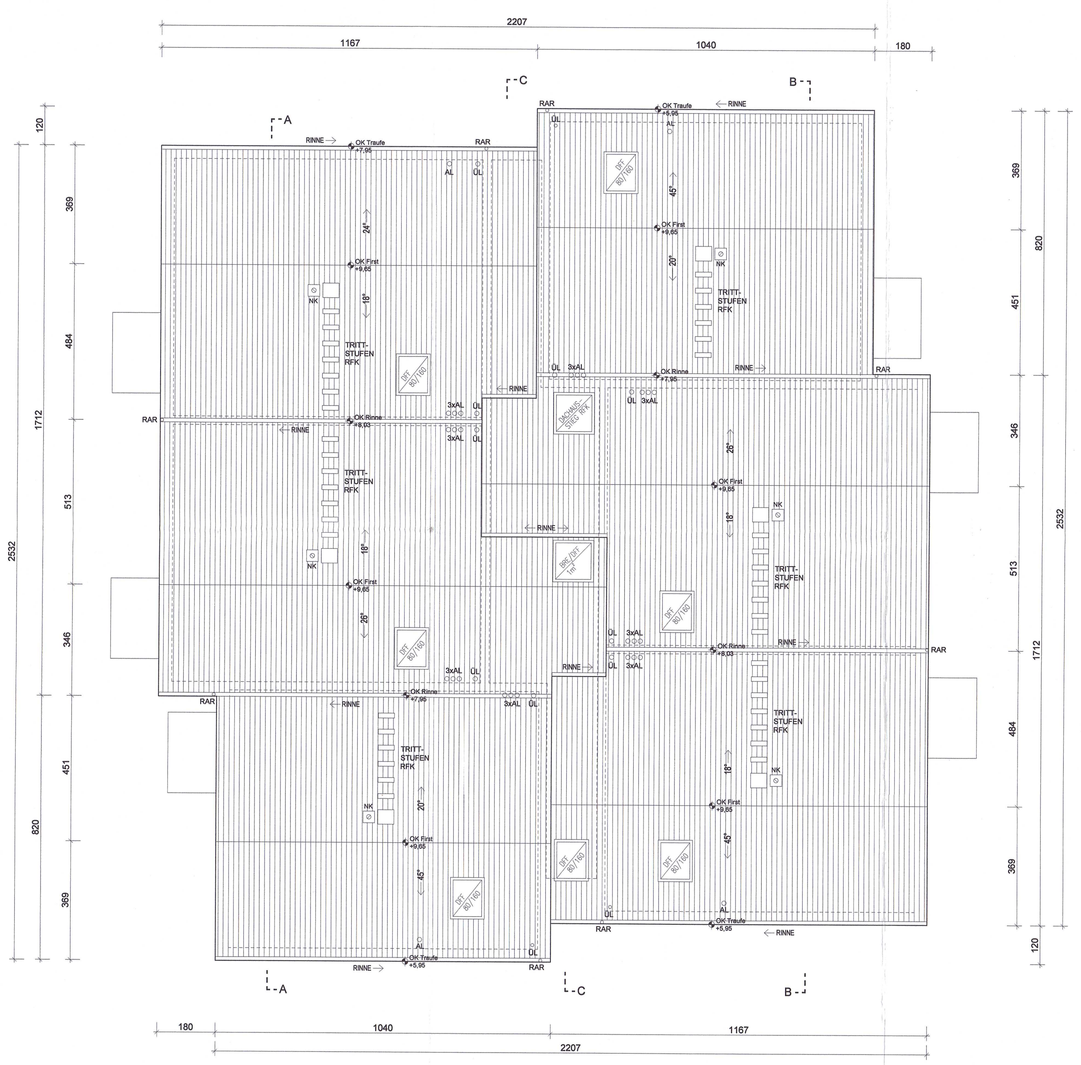

1.OBERGESCHOSS 1:100

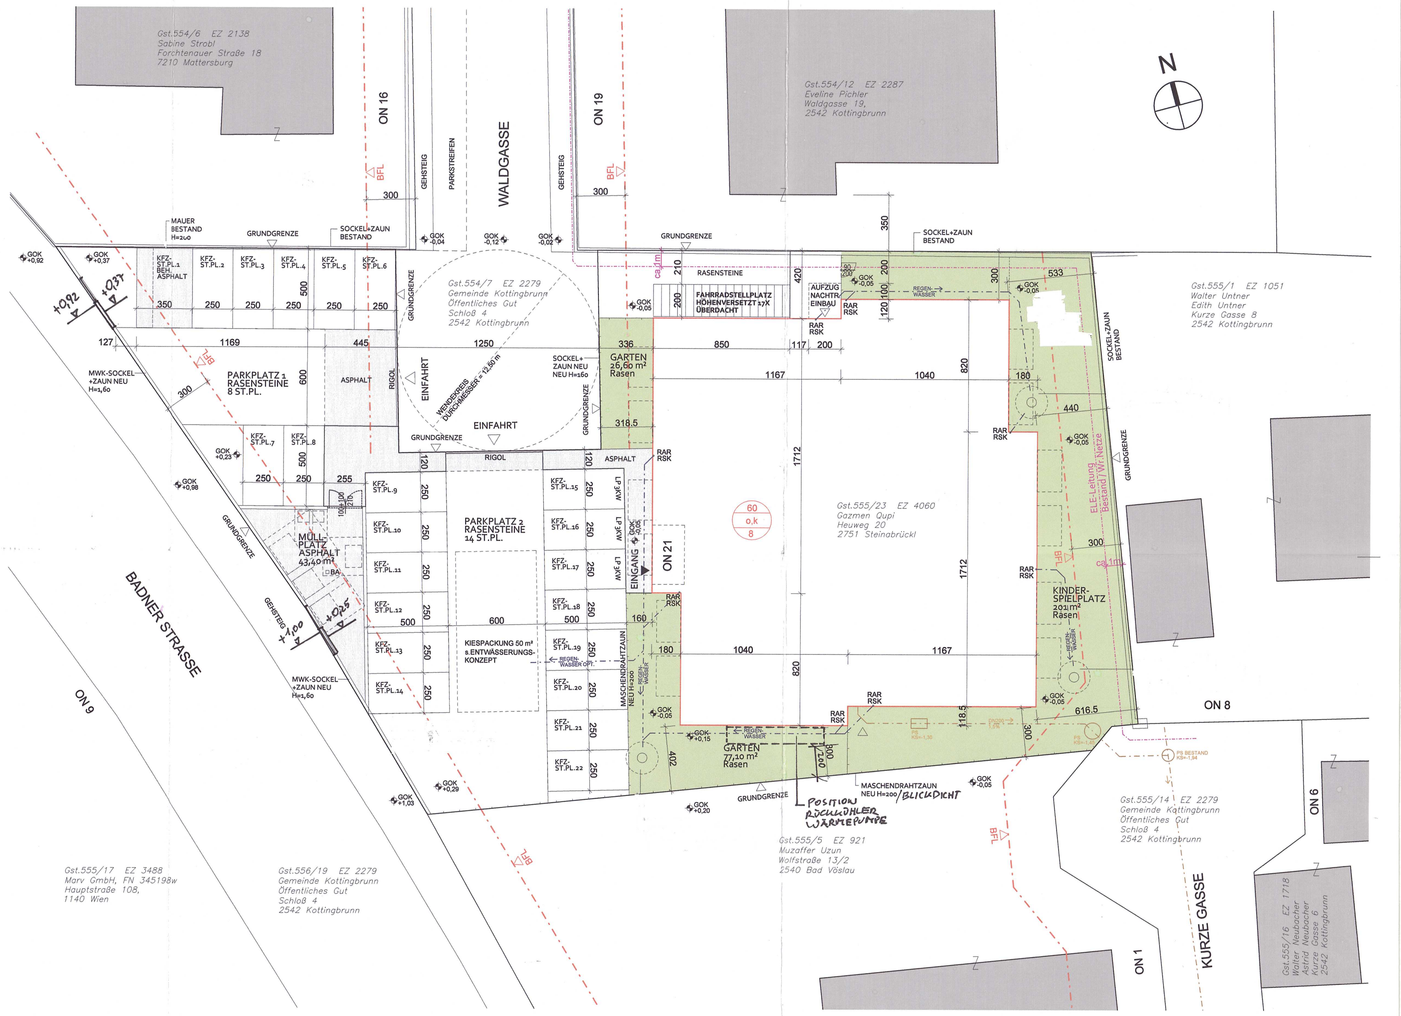

LAGEPLAN 1:200

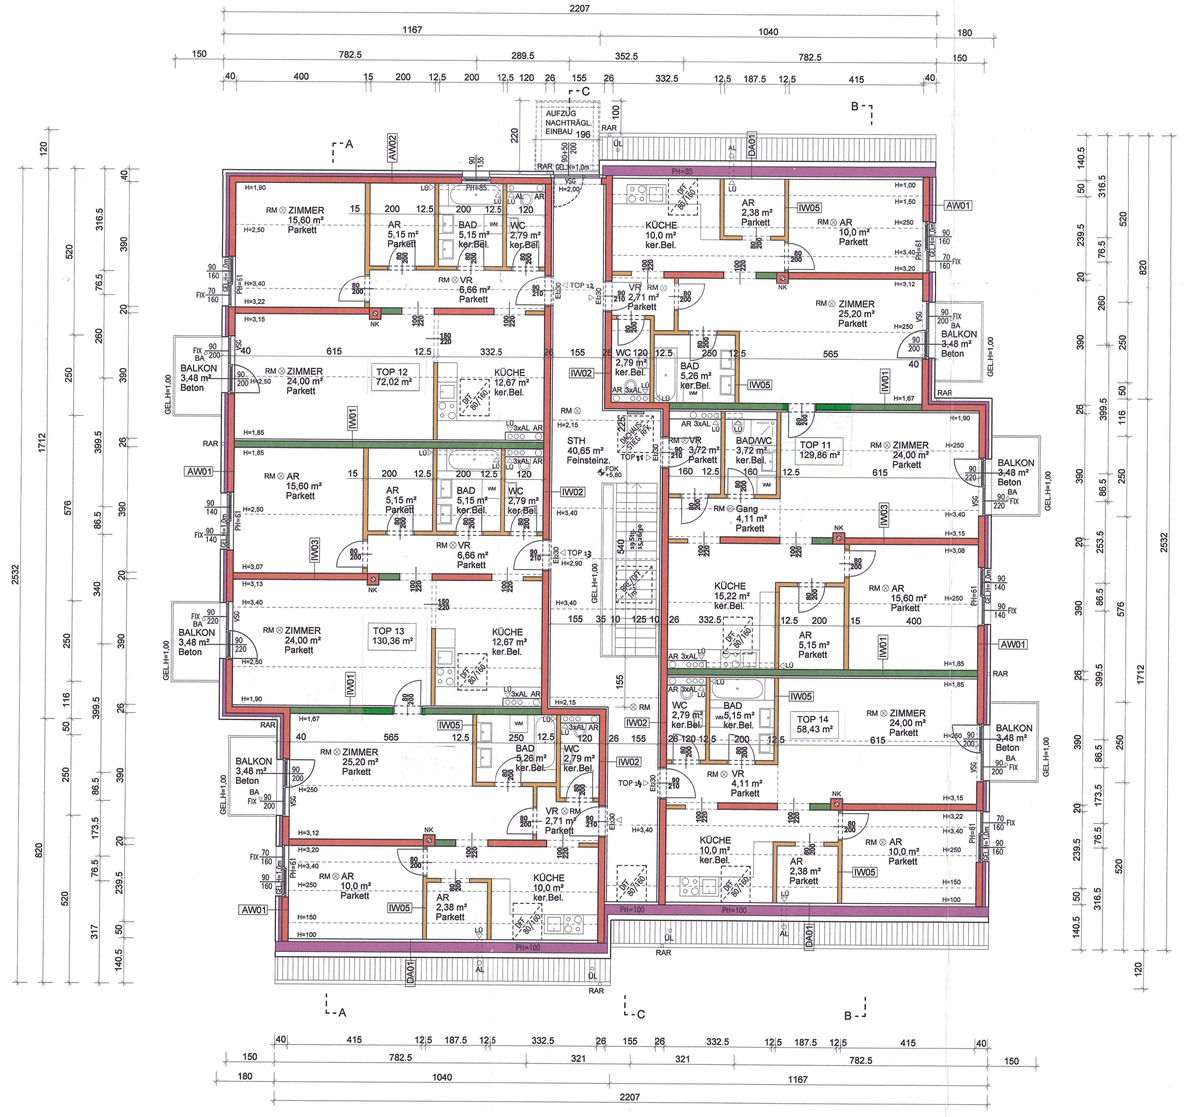

DACHGESCHOSS 1:100



ERDGESCHOSS 1:100

ABKÜRZUNGEN:

AL	Ablauf	LÜ	mech.Lüftung	RFK	Rauchfangkehrer	UK	Unterkante
AR	Abwasserrohr	NK	Notkamin	RH	Raumhöhe	ÜL	Überlüftung
BA	Bodenablauf	OK	Oberkante	RWA	Regenrohr	UZ	Unterzug
DA	Dunstabzug	OL	Oberlichte	RM	Rauchmelder	VSG	Verbund-Sicherheitsglas
Gel.	Geländе	PT	Putztüre	RSK	Regenwasserkasten	WM	Waschmaschine
KS	Kanalschohle			RS	Rauchsensor	ZUL	Zuluft
LP 3KW	Möglichkeit Ladepunkt 3KW			TR	Wäschetrockner		

LEGENDE:

Bestand	Ziegel	Wärmedämmung	
Neu	(Stahl-)Beton	Trockenbau	
Abbruch			

BAUBESCHREIBUNG:

BEZUGSHÖHE:
FFOK EG +/-0.00 = +256,45 ü. Adria

WIDMUNG:
Flächenwidmung: BK, 60 | o,k | 8 / Bauland Kerngebiet, 60% Bebauungsdichte, offene, gekuppelte Bauweise, Gebäudehöhe max.8m

BEBAUBARKEIT:
Grundstücksfläche: 1636 m² (lt. Aufmaß Geometer)
Max. bebaubare Fläche 60% (1636 m² x 0,6): 981,60 m²
Bebaute Fläche Neubau: 575,50 m² (2x11,67x17,12+2x10,40x8,20+0,53x10,12)
Bebaute Fläche gesamt: 575,50 m²(35%) < 981,60 m²

GEBÄUDEKLASSE: GK 3
3 Geschoße, Fluchtniveau: 5,85 m, BGFl. ges.: 1.719 m²

WOHNNUTZFLÄCHE / BALKONE:

		WHG	Balkon
EG:	Top1	71,52 m²	
	Top2	72,02 m²	
	Top3	72,02 m²	
	Top4	72,02 m²	
	Top5	72,02 m²	
1.OG:	Top6	143,54 m²	6,96 m²
	Top7	72,02 m²	3,48 m²
	Top8	72,02 m²	3,48 m²
	Top9	72,02 m²	3,48 m²
	Top10	72,02 m²	3,48 m²
DG:	Top11	129,86 m²	6,96 m²
	Top12	72,02 m²	3,48 m²
	Top13	130,36 m²	6,96 m²
	Top14	58,43 m²	3,48 m²
NFL ges.:		1.181,89 m²	41,76 m²

STELLPLATZVERPFLICHTUNG / FAHRRADABSTELLPLATZ / KINDERSPIELPLATZ:
Wohnungen Neu: 14
Stellplatzverpflichtg. ges.: -> 24 St.pl. (1½x1,5)
Stellplätze neu: 22 St.pl.

Fahrradabstellplätze: -> 1¼ St.pl. Fahrrad (1 St.pl./WGH)

Kinderspielplatz: 201m² > 185m² (150 + 7x5)

FENSTER / BESCHATTUNG:
Fenster: 2-Scheibenverglasung Uw=1,1W/m2K g=0,67
Alle raumhohen Fenster und alle Dachflächenfenster verfügen über einen außenliegenden Sonnenschutz

HAUSTECHNIK:
~~Grundwasserwärmepumpe mit Fußbodenheizung, kombinierte Warmwasserrufbereitung~~
LUFT/WASSER-WÄRMEPUMPE MIT ERZEUGUNG DER HEIZENERGIE

SONSTIGES:
-Alle Abwässer werden in den öffentlichen Kanal eingeleitet. Das Regenwasser wird auf Eigengrund versickert.
-Jede Wohnung hat einen Anschluss zu einem Notkamin (Kamin für Mehrfachbelegung zB.: Schiedl SIK DN18)
-Jede Wohnung verfügt über einen Waschmaschinenanschluss und Aufstellungsort für einen Wäschetrockner
-Die Belichtung ist gemäß OIB-Richtlinie 3 – Hygiene, Gesundheit und Umweltschutz, Punkt 9 gegeben.
-Alle Fluchtwege und Aufenthaltsräume verfügen über Rauchwarnmelder gemäß OIB-Richtline 2 Punkt 3.11
-Die im baupyhsikalischen Nachweis angegebenen Aufbauten und Angaben stimmen mit jenen auf dem Einreichplan,
insbesondere hinsichtlich der Dicke sowie des Materials bzw. der Type der Baustoffe überein.
-Alle innenliegenden Sanitärräume werden mechanisch entlüftet

GEMEINDE
EINGELANGT BA am:
05. Okt. 2017

EINREICHPLAN

f. die Errichtung eines Mehrfamilienhauses mit 1½ Wohnungen in der WALDGASSE 21, 2542 KOTTINGBRUNN

Gst.: 555/23, EZ 4060, KG: 04016 Kottingbrunn

BAUWERBER, GRUNDEIGENTÜMER:	BEHÖRDE:
Hr. Gazmen Qupi Heuweg 20 2751 Steinabrückel	Handschriftliche Änderungen am 15. September 2017 MARKTGEMEINDE KOTTINGBRUNN BAUAMT Bundesgebühr: € 7,30 unter Zahl: BAU-28-2017 am 17 Okt. 2017 vorgeschrieben / entrichtet Hiermit bezieht sich der Bescheid vom 13.10.2017 ZAHL: BAU-28-2017 Kottingbrunn, am 17.10.2017 Ist der Verhandlung am 26.09.2017 vorgelegen. Kottingbrunn, am 13.10.2017 (Für den) Bürgermeister: (Für den) Bürgermeister:
PLANVERFASSER:	BAUFÜHRER:
Arch.DI Marc Wohlschlager Schönbrunnerstraße 28A 1050 Wien tel.: 0699 18013466 email: mail@wohlschlager.at	

ABCD	Dat	Mst	Plangr	Inhalt	Plannummer
	EINREICHUNG 30.06.2017	1:200 1:100	1250/800	LAGEPLAN GRUNDRISSE	KOT-EPL-01