AW 01 a	ZIEGELWAND BESTAND ALTBAU EG
2,50 cm	Kalkzementputz genetzt und gespachtelt, In Anschlussbereichen mit Feuchtigkeitsabdichtung / Hochzug
60,00 cm	Bestehendes Ziegelmauerwerk 25,00 - 55,00 cm
1,50 cm	Bestehender Innenputz
64,00 cm	**BAUTEIL GESAMT**

AW 01 b	ZIEGELWAND BESTAND ALTBAU 1.OG
2,50 cm	Kalkzementputz genetzt und gespachtelt, In Anschlussbereichen mit Feuchtigkeitsabdichtung / Hochzug
45,00 cm	Bestehendes Ziegelmauerwerk 25,00 - 55,00 cm
1,50 cm	Bestehender Innenputz
49,00 cm	**BAUTEIL GESAMT**

AW 02	ZIEGELWAND BESTAND ZUBAU
1,00 cm	Silikatputz genetzt und gespachtelt, In Anschlussbereichen mit Feuchtigkeitsabdichtung / Hochzug
10,00 cm	*EPS Wärmedämmung (XPS im Sockelbereich)*
0,80 cm	Klebespachtel
25,00 cm	Bestehendes Ziegelmauerwerk
1,50 cm	Bestehender Innenputz
38,30 cm	**BAUTEIL GESAMT**

AW 03	AUSSENWAND HOLZ-LEICHTBAU BLECH (GAUBE)
0,80 cm	Blech Zink, gefalzt auf Strukturgewebe
2,40 cm	Vollholzschalung
5,00 cm	Konterlattung / Hinterlüftung mit Nageldichtband
0,10 cm	Diffusionsoffene UV-beständige Winddichtbahn lt. Bauphysik allseitig und alle Durchdringungen eingebunden
6,00 cm	Holzfaserdämmplatte
18,00 cm	Konstruktionsholz lt. Statik, fungizid behandelt dazw. Dämmung lt. Bauphysik
2,20 cm	OSB Platte, allseits luftdicht verklebt
1,50 cm	1 x 1,5 GKF-Platte **EI30**
5,00 cm	UK / Lattung dazw. Mineralwolle - Installationsebene
1,25 cm	1 x 1,25 cm GKB-Platte (GKBi in Nassräumen)
42,25 cm	**BAUTEIL GESAMT**

IW 01 a	INNENWAND ZIEGEL TRAGEND BESTAND
2,50 cm	Bestehender Innenputz
55,00 cm	Bestehendes Ziegelmauerwerk
2,50 cm	Bestehender Innenputz
60,00 cm	**BAUTEIL GESAMT**

IW 01 b	INNENWAND ZIEGEL TRAGEND BESTAND
2,50 cm	Bestehender Innenputz
45,00 cm	Bestehendes Ziegelmauerwerk
2,50 cm	Bestehender Innenputz
50,00 cm	**BAUTEIL GESAMT**

IW 01 c	INNENWAND ZIEGEL TRAGEND BESTAND
2,50 cm	Bestehender Innenputz
30,00 cm	Bestehendes Ziegelmauerwerk
2,50 cm	Bestehender Innenputz
35,00 cm	**BAUTEIL GESAMT**

IW 01 d	INNENWAND ZIEGEL TRAGEND BESTAND
2,50 cm	Bestehender Innenputz
15,00 cm	Bestehendes Ziegelmauerwerk
2,50 cm	Bestehender Innenputz
20,00 cm	**BAUTEIL GESAMT**

IW 02 a	INNENWAND HLZ-Mauerwerk
2,50 cm	Innenputz
20,00 cm	Hochlochziegel - Mauerwerk
2,50 cm	Innenputz
25,00 cm	**BAUTEIL GESAMT**

IW 02 b	INNENWAND HLZ-Mauerwerk
2,50 cm	Innenputz
20,00 cm	Hochlochziegel - Mauerwerk
2,50 cm	Innenputz
1,00 cm	Luftraum (Abstand)
5,00 cm	C-Profil dazw. Mineralwolle
2,50 cm	2 x 1,25 cm GKB-Platte (GKBi in Nassräumen)
33,50 cm	**BAUTEIL GESAMT**

IW 03	INNENWAND GKB 10,0 BESTAND
1,25 cm	Bestehende GKB - Platte
7,50 cm	Bestehende Unterkonstruktion
1,25 cm	Bestehende GKB - Platte
10,00 cm	**BAUTEIL GESAMT**

IW 04	INNENWAND TROCKENBAU DOPPELT BEPLANKT
2,50 cm	2 x 1,25 cm GKB-Platte (GKBi in Nassräumen)
7,50 cm	C-Profil dazw. Mineralwolle
2,50 cm	2 x 1,25 cm GKB-Platte (GKBi in Nassräumen)
12,50 cm	**BAUTEIL GESAMT**

IW 05	WOHNUNGSTRENNWAND TROCKENBAU
2,50 cm	2 x 1,25 cm GKF-Platte
	Dampfbremse allseits luftdicht verklebt
7,50 cm	C-Profil dazw. Mineralwolle
1,25 cm	1 x 1,25 cm GKF- Platte
0,25cm	Luftraum (Abstand)
7,50 cm	C-Profil dazw. Mineralwolle
2,50 cm	2 x 1,25 cm GKB-Platte (GKBi in Nassräumen)
21,50 cm	**BAUTEIL GESAMT**

VS 01	VORSATZSCHALE TROCKENBAU
1,00 cm	Luftraum (Abstand)
5,00 cm	C-Profil dazw. Mineralwolle
1,25 cm	1 x 1,25 cm GKB-Platte (GKBi in Nassräumen)
7,25 cm	**BAUTEIL GESAMT**

VS 02	VORSATZSCHALE TROCKENBAU NASSRAUM
1,00 cm	Luftraum (Abstand)
7,50 cm	C-Profil dazw. Mineralwolle
2,50 cm	2 x 1,25 cm GKB-Platte (GKBi in Nassräumen)
11,00 cm	**BAUTEIL GESAMT**

VS 03	VORSATZSCHALE TROCKENBAU WC
4,00 cm	Luftraum (Abstand)
15,00 cm	C-Profil dazw. Mineralwolle
2,50 cm	2 x 1,25 cm GKB-Platte (GKBi in Nassräumen)
21,50 cm	**BAUTEIL GESAMT**

DE 01	FUSSBODEN ERDBERÜHRT ALTBAU BESTAND
2,00 cm	Bodenbelag (Parkett / Fliese)
5,00 cm	Estrich (Zement)
	PE - Folie
3,00 cm	TDP EPS-T Trittschalldämmplatte
5,00 cm	Schüttung gebunden
	Dampfsperre
10,00 cm	EPS - T
1,00 cm	Bituminöse Bauwerksabdichtung
15,00 cm	Bestehende Betondecke
	Bestehende PE-Folie
30,00 cm	Bestehende Rollierung
71,10 cm	**BAUTEIL GESAMT**

DE 02	DECKE ÜBER EG ALTBAU BESTAND FBA NEU
1,50 cm	Bodenbelag (Parkett / Fliese)
5,00 cm	Zementestrich, inkl. Randdämmstreifen 1cm PE-Folie seitlich hochgezogen bis Estrich OK
3,00 cm	Trittschalldämmplatten lt. Bauphysik
4,50 cm	EPS - Schüttung zementgebunden
	PE-Folie
2,50 cm	Holzschalung
25,00 cm	Holzträme dazw. Luftraum
2,50 cm	Sparschalung
2,50 cm	Schilfmatten als Putzträger
1,50 cm	Innenputz
9,00 cm	*Unterkonstruktion abgeh. Decke*
1,25 cm	*GKB - Platte*
58,25 cm	**BAUTEIL GESAMT**

DE 03 a	DECKE ÜBER 1.OG ALTBAU BESTAND / FBA NEU
1,50 cm	Bodenbelag (Parkett / Fliese)
7,00 cm	Zementestrich mit FBH, inkl. Randdämmstreifen 1cm PE-Folie seitlich hochgezogen bis Estrich OK
3,00 cm	Trittschalldämmplatten lt. Bauphysik
5,00 cm	EPS - Schüttung zementgebunden
7,00 cm	Verbundbeton
	PE-Folie
2,40 cm	Vollholzschalung
20,00 cm	Bestehende Holztramdecke (dazw. 10cm MW)
2,50 cm	Sparschalung
	Dampfbremse
10,00 cm	Metallunterkonstruktion / Installationsebene (dazw. MW)
1,25 cm	GKB - Platte
59,55 cm	**BAUTEIL GESAMT**

DE 03 b	DECKE ÜBER 1.OG ALTBAU DACHTERRASSE
2,00 cm	Steinplattenbelag, rutsch- und witterungsfest
11,50 cm	Stelzlager - Höhenausgleich (7-16 cm)
1,50 cm	Regupol Sound & Drain
1,00 cm	2- lagige bit. Flachdachabdichtung samt Hochzüge erste Lage selbstklebend
7,50 cm	Gefälledämmung im Mittel 7,50 cm lt. Bauphysik (3-12cm)
8,00 cm	Grunddämmung EPS lt. Bauphysik
0,50 cm	Bitum. Dampfsperre lt. Bauphysik
7,00 cm	Verbundbeton
	PE-Folie
2,40 cm	Vollholzschalung
20,00 cm	Bestehende Holztramdecke (dazw. 10cm MW)
2,40 cm	Sparschalung
	Dampfbremse
10,00 cm	Metallunterkonstruktion / Installationsebene (dazw. MW)
1,25 cm	GKB - Platte
75,05 cm	**BAUTEIL GESAMT**

DE 04	FUSSBODEN ERDBERÜHRT ZUBAU
1,50 cm	Bodenbelag (Parkett / Fliese)
7,00 cm	Zementestrich mit FBH, inkl. Randdämmstreifen 1cm PE-Folie seitlich hochgezogen bis Estrich OK
3,00 cm	Trittschalldämmplatten lt. Bauphysik
3,00 cm	EPS - Schüttung zementgebunden
0,50 cm	Bituminöse Bauwerksabdichtung
30,00 cm	Bestehende Betondecke
20,00 cm	Bestehende XPS - Dämmung
30,00 cm	Bestehende Rollierung
95,00 cm	**BAUTEIL GESAMT**

DE 05	DECKE ÜBER EG + 1.OG ZUBAU
1,50 cm	Bodenbelag (Parkett / Fliese)
7,00 cm	Zementestrich mit FBH, inkl. Randdämmstreifen 1cm PE-Folie seitlich hochgezogen bis Estrich OK
3,00 cm	Trittschalldämmplatten lt. Bauphysik
3,50 cm	EPS - Schüttung zementgebunden
20,00 cm	Bestehende Betondecke
0,50 cm	Bestehende Spachtelung
35,50 cm	**BAUTEIL GESAMT**

DE 06	DECKE PODEST STIEGENHAUS
1,50 cm	Fliesenbelag, rutsch- und witterungsfest
25,00 cm	Stahlbetondecke / Stahlbetonstiege
26,50 cm	**BAUTEIL GESAMT**

DE 07	BALKON STAHLKONSTR. THERMISCH ENTKOPPELT
2,00 cm	Steinbelag, rutsch- und witterungsfest
8,00 cm	Stelzlager - Höhenausgleich
0,80 cm	Gummigranulatplatte mit Trittschallfunktion
0,50 cm	Bituminöse Abdichtung 2-lagig, erste Lage selbstklebend
0,50 cm	Stahlblech lt. Statik, OK im Gefälle 2%
20,00 cm	Konstruktion aus Stahlträgern lt. Statik, Untersicht verkleidet mit MAX Exterior
32,30 cm	**BAUTEIL GESAMT**

DE 08	FUSSBODEN AUSSENBEREICH PFLASTER
7,00 cm	Pflaster / Rasengitterstein
3,00 cm	Splittbett
25,00 cm	Mechanisch stabilisierte Tragschicht (Kies,Schotter)
35,00 cm	**BAUTEIL GESAMT**

DA 01	DACHAUFBAU ALTBAU ZIEGELDECKUNG
3,00 cm	Keramischer Dachziegel
3,00 cm	Lattung 30/50 mm
5,00 cm	Konterlattung 50/50 mit Nageldichtband - Hinterlüftung
0,20 cm	Diffussionsoffene Dachauflegebahn - erhöhte Regensicherheit, sd- Wert lt. Bauphysik
2,40 cm	Vollholzschalung
24,00 cm	Holzsparren lt. Statik dazw. Mineralwolle lt. Bauphysik
0,10 cm	Dampfbremse allseits verklebt
2,40 cm	Sparschalung
1,50 cm	1x 1,50 cm GKF-Platte **(EI30)**
41,60 cm	**BAUTEIL GESAMT**

DA 02	DACHAUFBAU ALTBAU BLECHDECKUNG (GAUBE)
0,80 cm	Blechdeckung auf Strukturmatte
2,40 cm	Vollholzschalung
8,00 cm	Konterlattung 80/50 mit Nageldichtband - Hinterlüftung
0,20 cm	Diffussionsoffene Dachauflegebahn - erhöhte Regensicherheit, sd- Wert lt. Bauphysik
2,40 cm	Vollholzschalung
24,00 cm	Holzsparren lt. Statik dazw. Mineralwolle lt. Bauphysik
0,10 cm	Dampfbremse allseits verklebt
2,40 cm	Sparschalung
1,50 cm	1 x 1,50 cm GKF-Platte **(EI30)**
41,80 cm	**BAUTEIL GESAMT**

DA 03	DACHAUFBAU ZUBAU ZIEGELDECKUNG
3,00 cm	Keramischer Dachziegel
3,00 cm	Lattung 30/50 mm
5,00 cm	Konterlattung 50/50 mit Nageldichtband - Hinterlüftung
0,20 cm	Diffussionsoffene Dachauflegebahn - erhöhte Regensicherheit, sd- Wert lt. Bauphysik
2,40 cm	Vollholzschalung
24,00 cm	Holzsparren lt. Statik dazw. Mineralwolle lt. Bauphysik
0,10 cm	Dampfbremse allseits verklebt
2,40 cm	Sparschalung
1,50 cm	1x 1,50 cm GKF-Platte **(EI30)**
41,60 cm	**BAUTEIL GESAMT**

DA 04	DACHAUFBAU ZUBAU BLECHDECKUNG
0,80 cm	Zinkblech auf Strukturmatte
2,40 cm	Vollholzschalung
8,00 cm	Konterlattung 80/50 mit Nageldichtband - Hinterlüftung
0,20 cm	Diffussionsoffene Dachauflegebahn - erhöhte Regensicherheit, sd- Wert lt. Bauphysik
2,40 cm	Vollholzschalung
24,00 cm	Holzsparren lt. Statik dazw. Mineralwolle lt. Bauphysik
0,10 cm	Dampfbremse allseits verklebt
2,40 cm	Sparschalung
1,50 cm	1 x 1,50 cm GKF-Platte **(EI30)**
5,00 cm	UK / Lattung dazw. Mineralwolle - Installationsebene
1,25 cm	1 x 1,25 cm GKB-Platte (GKBi in Nassräumen)
47,05 cm	**BAUTEIL GESAMT**

DA 05	DACHAUFBAU STIEGENHAUS ZIEGELDECKUNG
3,00 cm	Keramischer Dachziegel
3,00 cm	Lattung 30/50 mm
5,00 cm	Konterlattung 50/50 mit Nageldichtband - Hinterlüftung
0,20 cm	Diffussionsoffene Dachauflegebahn - erhöhte Regensicherheit, sd- Wert lt. Bauphysik
2,40 cm	Vollholzschalung auf Sicht / Dreischichtplatte
16,00 cm	Holzsparren lt. Statik
2,10 cm	OSB - Platte
3,00 cm	2 x 1,50cm GKF-Platte **(EI60)**
40,60 cm	**BAUTEIL GESAMT**

DA 06	DACHAUFBAU STIEGENHAUS BLECHDECKUNG
0,80 cm	Zinkblech auf Strukturmatte
2,40 cm	Vollholzschalung
8,00 cm	Konterlattung 80/50 mit Nageldichtband - Hinterlüftung
0,20 cm	Diffussionsoffene Dachauflegebahn - erhöhte Regensicherheit, sd- Wert lt. Bauphysik
2,40 cm	Vollholzschalung
16,00 cm	Holzsparren lt. Statik
2,10 cm	OSB-Platte
3,00 cm	2 x 1,50cm GKF-Platte **(EI60)**
36,80 cm	**BAUTEIL GESAMT**

AUFBAUTEN M1:100

GRUNDLAGE & HÖHENBEZUG:

±0.00 = + 257,47 über Adria
Der Bestand wurde basierend auf Geometerangaben vom Ingenieurbüro für Vermessungswesen Manfred Haslbauer dargestellt (Plandatum: 08.11.2024).

BEZUGSNIVEAU:
Das Beszugsniveau ist in **violetter Farbe** dargestellt. Das Bezugsniveau bezieht sich zum einen auf die Beilage zur Einreichung aus dem Bauakt zum Nachweis der Gebäudehöhe vom 26.02.2016 - Die Unterkante der Gebäudefront wird durch das Bezugsniveau gebildet - dementsprechend wurden diese Höhen als Bezugsniveau an den Gebäudefronten angesetzt.
Des Weiteren bezieht sich das Bezugsniveau auf die Höhenkoten des Lageplans der Einreichung, welche als Abbruch dargestellt wurden, da das Bezugsniveau das Niveau vor Geländeveränderung darstellt.
Achtung: Der Höhenbezug von ±0,00 = 257,28 ü.A. der vorangegangenen Einreichung entspricht nicht dem Höhenbezug ±0,00 = 257,47 ü.A. der vorliegenden Einreichung. Dementsprechend ist der Wert zum Projektursprung nicht ident (±0,00 alte Einreichplanung = -0,19 aktuelle Einreichplanung).

ALLGEMEIN:
→ Bauweise: Bestehende Massivbauweise / Altbau Tramdecken / Zubau Stahlbetondecken / Innenwände Leichtbau
→ Die Fassade des Altbaus wird saniert und orientiert sich farblich an der historischen Erscheinung des Objekts.
→ Die Faschen und Zierelemente des Albaus bleiben erhalten.
→ Das Vollwärmeschutzsystem des Zubaus wird erneuert.
→ Kinderspielplatzausgleichsabgabe wurde im Jahr 2018 vorgeschrieben und bereits bezahlt.
→ Der Kinderwagenabstellraum befindet sich im Erdgeschoss.
→ Brieffachanlagen befinden sich im Hauseingangsbereich.
→ Gemäß NÖ BO 2014 §66a besteht keine Verpflichtung zur Errichtung einer Photovoltaikanlage.

HAUSTECHNISCHE ANGABEN:
→ Elektroversorgung: Anschluss an das öffentliche Stromnetz
→ Heizung / Warmwasser: 2 Wärmepumpen NEU
→ Historischer Altbau: EG + 1. OG - Beheizung durch Radiatoren; DG - Fußbodenheizung
→ Zubau (hinterer Gebäudeteil): Fußbodenheizung, elektrische Handtuchheizkörper in den Bädern
→ In allen Wohnungen wird ein Anschluss für eine Waschmaschine vorgesehen. Wegen Platzmangel im Sanitärraumen wird in barrierefrei anpassbaren Wohneinheiten ein zweiter Anschluss in der Küche vorgesehen.
→ Das Gebäude wird mit einer gebäudeinternen physischen Infrastruktur und Glasfaserverkabelung ausgestattet.

BRANDSCHUTZ:
WOHNGEBÄUDE, GEBÄUDEKLASSE: GK3 lt OIB RL 2023
3 oberirdische Geschoße / 0 unterirdische Geschoße / Fluchtniveau weniger als 7m

→ Gemäß NÖ BTV 2014 Anlage 2 (OIB2) Pkt. 3.1.1 ist keine Unterteilung in mehrere Brandabschnitte erforderlich.
→ Die allgemeinen Anforderungen an das Brandverhalten gemäß NÖ BTV 2014 Anlage 2 (OIB2) Tabelle 1a werden eingehalten.
→ Die allgemeinen Anforderungen an den Feuerwiderstand von Bauteilen gemäß NÖ BTV 2014 Anlage 2 (OIB2) Tabelle 1b werden eingehalten.
→ Die Anforderungen an Treppenhäuser im Verlauf des einzigen Fluchtweges gemäß NÖ BTV 2014 Anlage 2 (OIB2) Punkt 5.1.1 b) werden eingehalten (Tabelle 2a).
→ Gemäß NÖ BTV 2014 Anlage 2 (OIB2) Tabelle 6 ist keine Sicherheitsbeleuchtung erforderlich.
→ Der Fluchtweg führt über das zentrale, offene Stiegenhaus, Fluchtweglänge < 40m.
→ Aufgrund der Tatsache, dass das Stiegenhaus offen ausgeführt wird besteht gemäß dem Grundsatz des gleichwertigen Abweichens keine Notwendigkeit zur Installation eines Rauch- und Wärmeabzuges am höchsten Punkt des Stiegenhauses.
→ Die neu hergestellten Treppenläufe und Podeste des Stiegenhauses werden in A2 und so ausgeführt, dass im Brandfall keine Beeinträchtigung durch Flammeneinwirkung und gefahrenbringende Strahlungswärme zu erwarten ist.
→ Sofern Schächte, Kanäle, Leitungen und sonstige Einbauten in Wänden bzw. Decken liegen oder diese durchdringen, ist entweder durch Abschottung oder Ummantelung sichergestellt, dass die Feuerwiderstandsklasse dieser Bauteile nicht beeinträchtigt wird.
→ Alle Aufenthaltsräume sowie alle Gänge über die eine Fluchtweg führt, sind mit Rauchwarnmeldern (batteriebetrieben) ausgestattet (in den Wohnküchen nicht unmittelbar im Kochbereich).
→ Alle neu hergestellten Eingangstüren, welche vom Stiegenhaus in Wohneinheiten oder Gänge des Gebäudes führen werden gemäß NÖ BTV 2014 Anlage 2 (OIB2) Tabelle 2a in EI² 30-C bzw. E 30-C ausgeführt.
→ Balkone werden in R30 oder A2 ausgeführt.

HYGIENE, GESUNDHEIT UND UMWELTSCHUTZ:
→ Trinkwasser: Bestehender Anschluss an das öffentliche Versorgungsnetz.
→ Abwasser: Bestehender Kanalanschluss an den öffentlichen Schmutzwasserkanal.
→ Alle Niederschlagswässer werden gemäß Entwässerungskonzept in einem Retentionsbecken gesammelt und in den Hörmbach eingeleitet. Die Einleitung der Niederschlagswässer in den Hörmbach ist ein eigenständiges wasserrechtliches Projekt, welches derzeit bei der Bezirkshauptmannschaft zur Prüfung aufliegt.
→ Die Entwässerung der Dachflächen erfolgt über Hängerinnen und Regenabfallrohre.
→ Die Entwässerung der Balkone erfolgt über Rinnen und Regenabfallrohre.
→ Kanalleitungen PVC bzw. Guss in kg, mind. 2% Gefälle
→ Putzschächte und Putzstücke gem. Ö-NORM ausgeführt.
→ Die Müllsammlung erfolgt über die Abfallsammelstelle im vorderen Bauwich.
→ Sämtliche Aufenthaltsräume werden natürlich belüftet (Fensterlüftung). Sanitärräume, die über kein Fenster verfügen werden mechanisch entlüftet. Sonstige innenliegende Räume werden entsprechend ihrem Verwendungszweck be- und entlüftet.
→ Alle Aufenthaltsräume verfügen über ausreichende Lichteintrittsflächen, sowie eine freie Sicht von mind. 2m und zumindest in einem Aufenthaltsraum pro Wohneinheit über eine freie waagrechte Sicht von mind. 6m in 1,20m Höhe.
→ In sämtlichen Nassräumen wird eine Kunststoffabdichtung unter Fliesenbelägen mit 15cm Wandhochzug ausgeführt.
→ Das Grundstück befindet sich im Radonvorsorgegebiet, kein Radonschutzgebiet. Es werden entsprechende Maßnahmen getroffen um den Eintrag von Radon aus dem Untergrund in das Gebäude zu verhindern.
→ Es werden gemäß NÖ BTV 2014 Anlage 3 (OIB 3) Pkt. 8.2.3 keine Baumaterialien verwendet deren Aktivitätskonzentrationsindex I überschreiten oder welche in Anhang B angeführt sind.

NUTZUNGSSICHERHEIT und BARRIEREFREIHEIT:

→ Geländer / Absturzsicherungen mind. 1,02 m hoch. Abstände von vertikalen Stäben max. 12cm.
→ Geländer / Absturzsicherungen werden Feuerverzinkt und korrosionsbeständig ausgeführt.
→ Alle Glasgeländer und bodentiefen Verglasungen mit Absturzgefahr werden in VSG ausgeführt, vertikale Verglasungen mit Durchsturzgefahr in ESG. Dachflächenfenster werden in VSG ausgeführt.
→ Es werden bei allen neu errichteten und neu eingedeckten, geneigten Dächern gemäß NÖ BTV 2014 Anlage 4 (OIB4) Pkt. 5.2 geeignete Maßnahmen gegen das Abrutschen von Schnee und Eis getroffen.
→ Der Blitzschutz wird an der Fassade gemäß Ö-Norm ausgeführt.
→ Sämtliche Treppen werden beidseitig mit Handläufen ausgestattet.
→ Gemäß NÖ BO 2014 §46 sind drei Wohnungen barrierefrei anpassbar auszuführen. Dementsprechend werden die drei Wohneinheiten im Erdgeschoß barrierefrei anpassbar ausgeführt.
→ Sämtliche öffentlich zugängliche Bereiche, wie Einstellraum und Abfallsammelstellebleiben bleiben unverändert und sind barrierefrei zugänglich.

BAUPHYSIK:
→ Für sämtliche Bauteile, welche von der Einreichung betroffen sind werden die Bestimmungen zum Schallschutz gemäß Anlage 5 zur NÖ BTV 2014 eingehalten.
→ Das neue Treppenhaus wird thermisch und schalltechnisch entkoppelt von den bestehenden Baukörpern ausgeführt.
→ Die im Einreichplan angegebenen Aufbauten und Angaben sind mit jenen im bauphysikalischen Nachweis identisch; insbesondere hinsichtlich der Dicke sowie des Materials bzw. der Type der Baustoffe.
→ Balkone werden thermisch getrennt ausgeführt.

EINREICHUNG gemäß NÖ BTV 2014 inkl. Anhänge (OIB-Richtlinien in der Fassung 2023)

BESCHREIBUNG

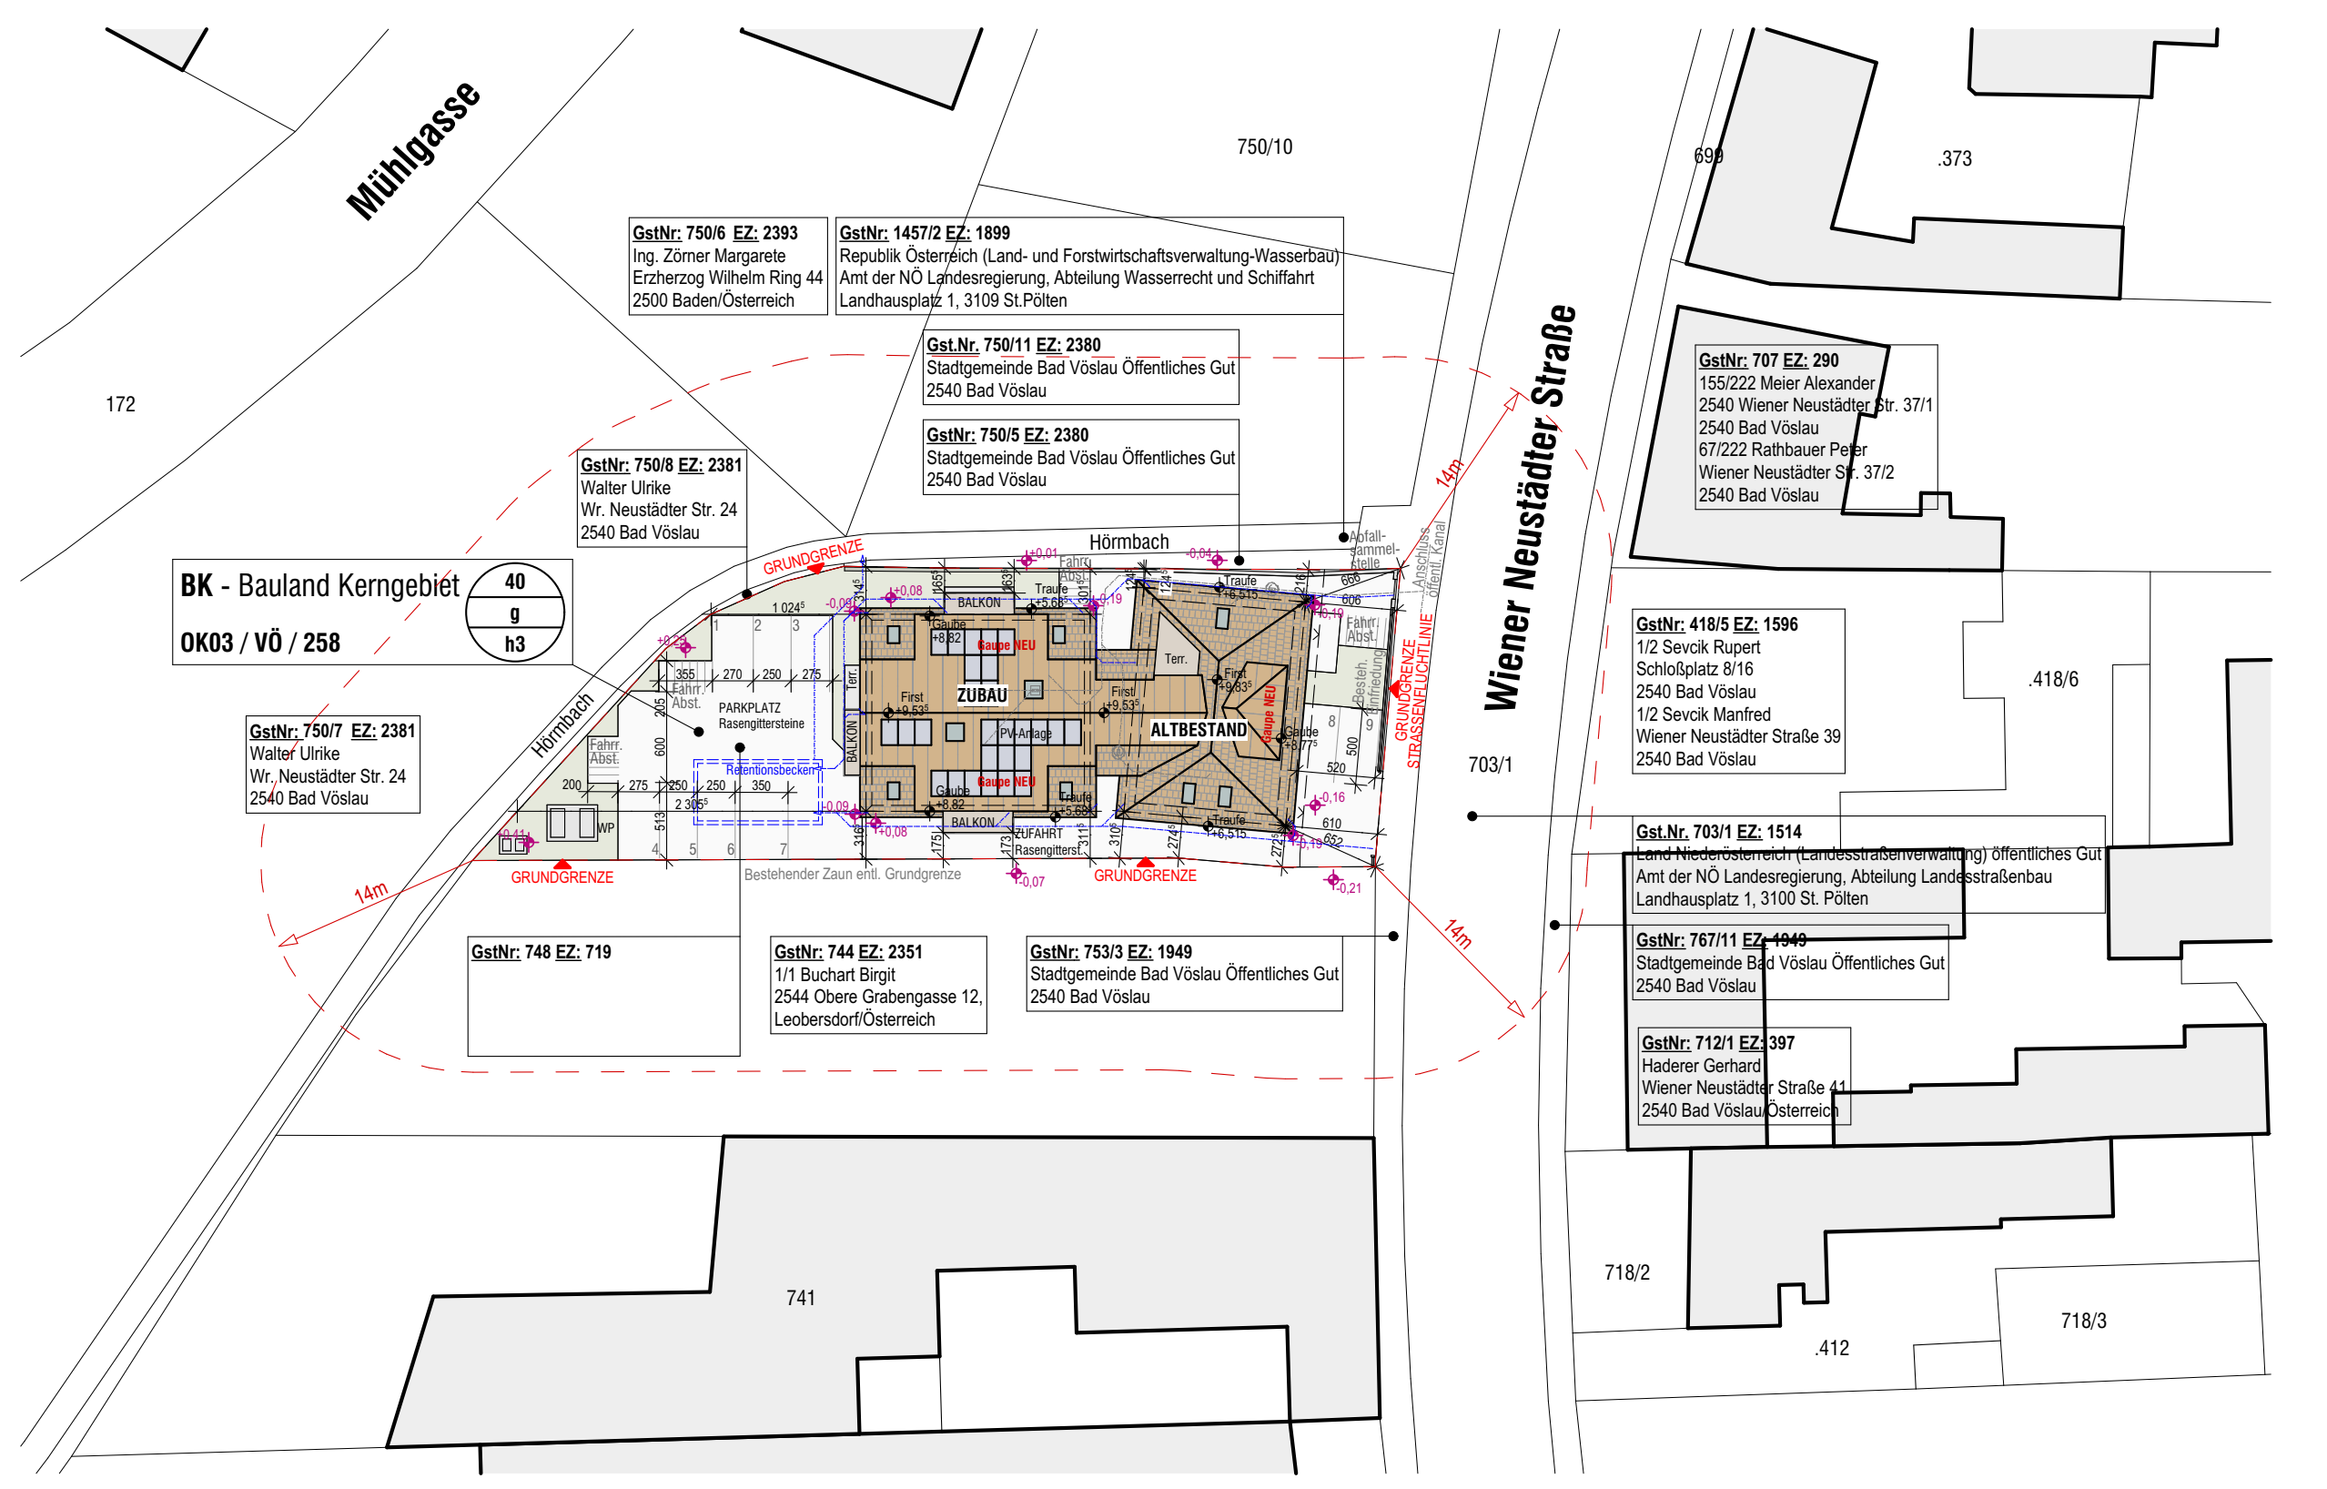

LAGEPLAN M1:500

NUTZFLÄCHEN / **AUSSENFLÄCHEN**

Nutzflächen	VR1	VR2	Gang	AR	WC1	WC2	Bad 1	Bad 2	Bad/WC	Woh./Ess.	Wohnküche	Wohnküche	Zimmer 1	Zimmer 2	Zimmer 3	NF GESAMT	Garten	Balkon/Terr.	Außenflächen Gesamt
EG																			
TOP 1	3,68 m²	4,81 m²	5,43 m²		2,33 m²	2,02 m²	3,88 m²	6,28 m²			18,55 m²	18,78 m²	10,04 m²	10,81 m²	18,59 m²	**105,20 m²**	18,28 m²	9,14 m²	**27,42 m²**
TOP 2	8,83 m²								5,42 m²		19,20 m²		10,08 m²	10,77 m²		**54,30 m²**	33,66 m²	6,82 m²	**40,48 m²**
TOP 3				8,70 m²					5,42 m²		20,91 m²		10,64 m²			**45,67 m²**	25,74 m²	8,70 m²	**34,44 m²**
1. OG																			
TOP 4	3,42 m²				2,58 m²		3,64 m²				21,17 m²		12,20 m²	10,34 m²		**53,35 m²**			**0,00 m²**
TOP 5	5,43 m²				1,98 m²		6,82 m²				21,17 m²		11,93 m²	10,41 m²		**57,74 m²**			**0,00 m²**
TOP 6	5,60 m²			9,34 m²					5,08 m²		24,65 m²					**44,67 m²**		6,44 m²	**6,44 m²**
TOP 7	7,82 m²								5,40 m²		19,24 m²		10,08 m²	10,73 m²		**53,27 m²**		6,02 m²	**6,02 m²**
TOP 8				8,08 m²					5,56 m²		21,10 m²		10,06 m²			**44,80 m²**		6,44 m²	**6,44 m²**
DG																			
TOP 9	8,38 m²			7,98 m²	1,71 m²		4,96 m²				31,70 m²		10,52 m²			**65,25 m²**		9,83 m²	**9,83 m²**
TOP 10				2,39 m²					4,25 m²		24,08 m²		10,83 m²			**41,55 m²**		6,44 m²	**6,44 m²**
TOP 11	5,39 m²			2,30 m²					3,88 m²		26,35 m²		12,65 m²			**50,57 m²**		6,02 m²	**6,02 m²**
TOP 12				2,08 m²					4,06 m²		19,03 m²		11,17 m²			**36,34 m²**		6,44 m²	**6,44 m²**
SUMME GESAMTE NUTZFLÄCHE																**652,71 m²**			**149,97 m²**

Allgemeinflächen	Gang	KIWA	Techn.Nische	Einlagerr.	Haustechnik	Gang 2	Gesamt	Stiegenhaus	Podest	Gesamt
EG Straßentrakt	18,33 m²	5,27 m²	1,15 m²	18,78 m²	9,76 m²		**53,29 m²**	5,28 m²		**5,28 m²**
1.Obergeschoß	7,91 m²					5,52 m²	**13,43 m²**	5,28 m²	3,63 m²	**8,91 m²**
Dachgeschoß	9,78 m²						**9,78 m²**	5,28 m²	3,63 m²	**8,91 m²**
SUMME ALLGEMEIN FLÄCHEN							**76,50 m²**			**23,10 m²**
SUMME NUTZFLÄCHE + ALLGEMEINFLÄCHEN							**729,21 m²**			**173,07 m²**

STATISTISCHE ANGANBEN:

GRUNDSTÜCKSFLÄCHE:	**988 m²**
ÜBERBAUTE FLÄCHE:	**445,88 m²**
BEBAUTE FLÄCHE:	**369,81 m²**
BEBAUUNGSDICHTE:	**37,43 %**
BRUTTOVOLUMEN:	**3.432,29 m³**
GRUNDRISSFLÄCHE:	**1.059,93 m²**
GESCHOSSFLÄCHENZAHL:	**1,073**
NUTZFLÄCHEN:	**729,21 m²**

KFZ - STELLPLATZBERECHNUNG:

Es wurde bereits bei der letzten Einreichung für **8 KFZ-Abstellplätze** die **Ausgleichsabgabe** entrichtet.
Laut Bebauungsvorschriften sind folgende Anzahl an KFZ-Stellplätze pro Wohneinheit zu errichten:
Wohnungen bis 64,99m² NGF:1,3 Stellplätze
Wohnungen ab 65,00m² bis 84,99m² NGF:1,5 Stellplätze
Wohnungen ab 85,00m² bis 64,99m² NGF:2,0 Stellplätze

Aufstellung:

TOP 1	105,20 m²	2,0 Stellplätze
TOP 2	54,30 m²	1,3 Stellplätze
TOP 3	45,67 m²	1,3 Stellplätze
TOP 4	53,35 m²	1,3 Stellplätze
TOP 5	57,74 m²	1,3 Stellplätze
TOP 6	44,67 m²	1,3 Stellplätze
TOP 7	53,27 m²	1,3 Stellplätze
TOP 8	44,80 m²	1,3 Stellplätze
TOP 9	65,25 m²	1,5 Stellplätze
TOP 10	41,55 m²	1,3 Stellplätze
TOP 11	50,57 m²	1,3 Stellplätze
TOP 12	36,34 m²	1,3 Stellplätze
GESAMT		**16,5 Stellplätze**

Anzahl der zu errichtenden Stellplätze:
17 (erf. Stellplätze) - **8** (entr. Ausgleichsabg.) **=** **9** KFZ Stellplätze

Es müssen gemäß der Stellplatzberechnung mindestens 9 KFZ-Stellplätze auf Eigengrund hergestellt werden.

Es wird gemäß §64 Abs. 6 NÖ BO 2014 mind. ein PKW-Stellplatz mit einem Ladepunkt ausgestattet sowie für mindestens 50% aller PKW-Stellplätze Vorbereitungsmaßnahmen für eine spätere Errichtung von Ladepunkten vorgesehen.

ABSTELLANLAGEN FÜR FAHRRÄDER:

Es ist gemäß NÖ BO 2014 §65 Abs.4 für jede Wohnung mindestens 2 Fahrradabstellplätze vorzusehen.

12 Wohnungen > **24 Stellplätze**

Die Stellplätze sind 2,00m lang und 0,50m breit (bei höhenversetzter Aufstellung) auszuführen.
Aufgrund der begrenzten Platzverhältnisse auf dem Grundstück, werden die Stellplätze insgesamt auf 4 Abstellanlagen aufgeteilt.

Abstellanlage 1 > 6 Stellplätze (vorderer Bauwich)
Abstellanlage 2 > 5 Stellplätze (Zugangsbereich)
Abstellanlage 3 > 7 Stellplätze (Parkplatz)
Abstellanalge 4 > 6 Stellplätze (Parkplatz)
GESAMT **24 Stellpätze**

Gemäß NÖ BTV 2014 §14 Abs. 5 müssen Abstellanlagen ab 10 Stellplätzen überdacht ausgeführt werden.
Aufgrund der Tatsache, dass keine der vier Abstellanlagen diese Anzahl erreicht, werden die Fahrradabstellanlagen im Sinne der Vermeidung einer "Verhüttelung" des Grundstücks, sowie des allgemeinen Erscheinungsbildes der Wohnhausanlage im Bereich der historischen Schutzzone nicht überdacht ausgeführt.

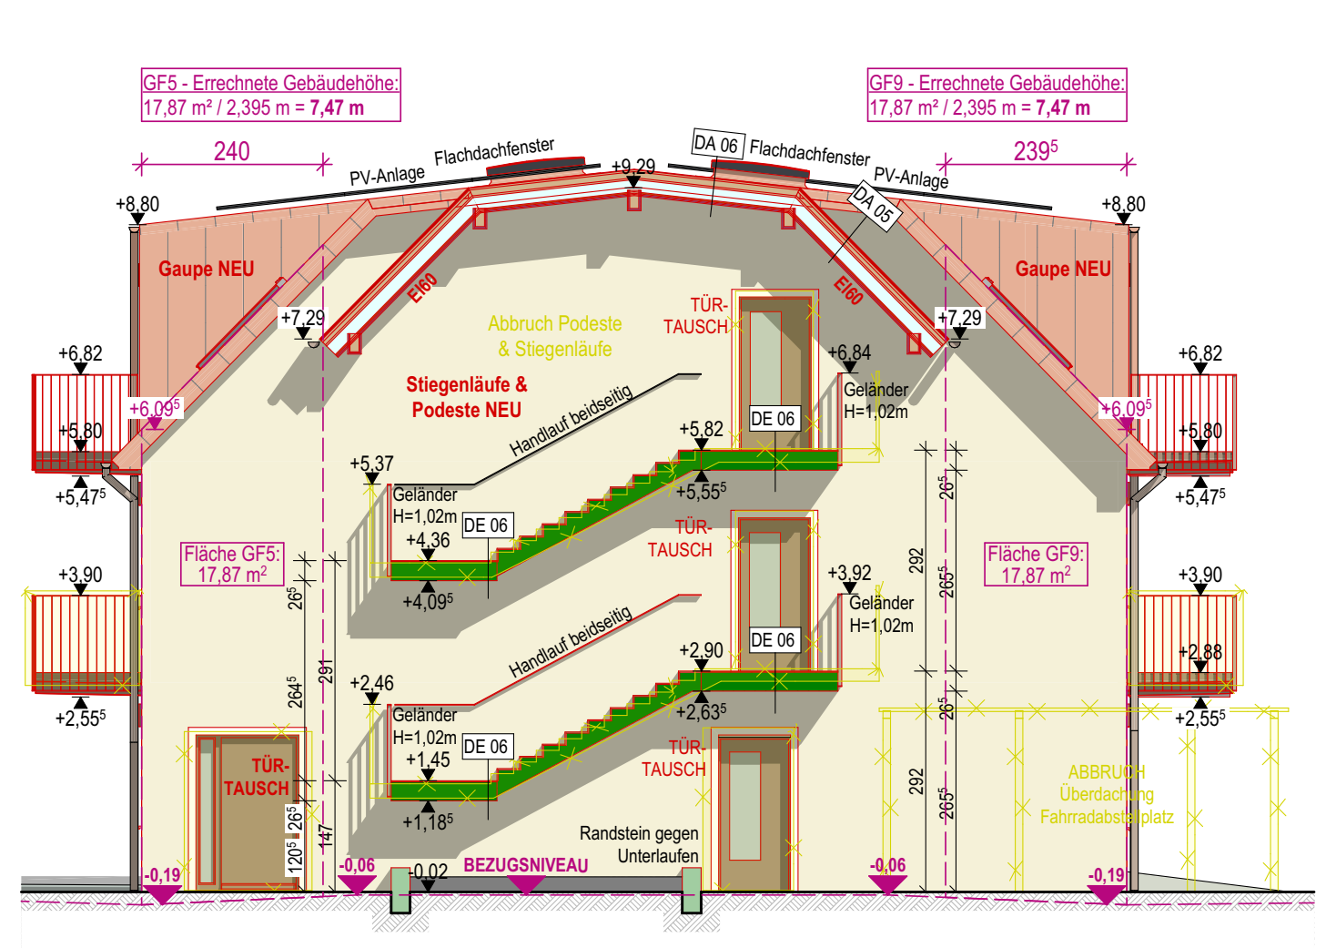

SCHNITT G-G // OSTANSICHT ZUBAU VON STIEGENHAUS M1:100

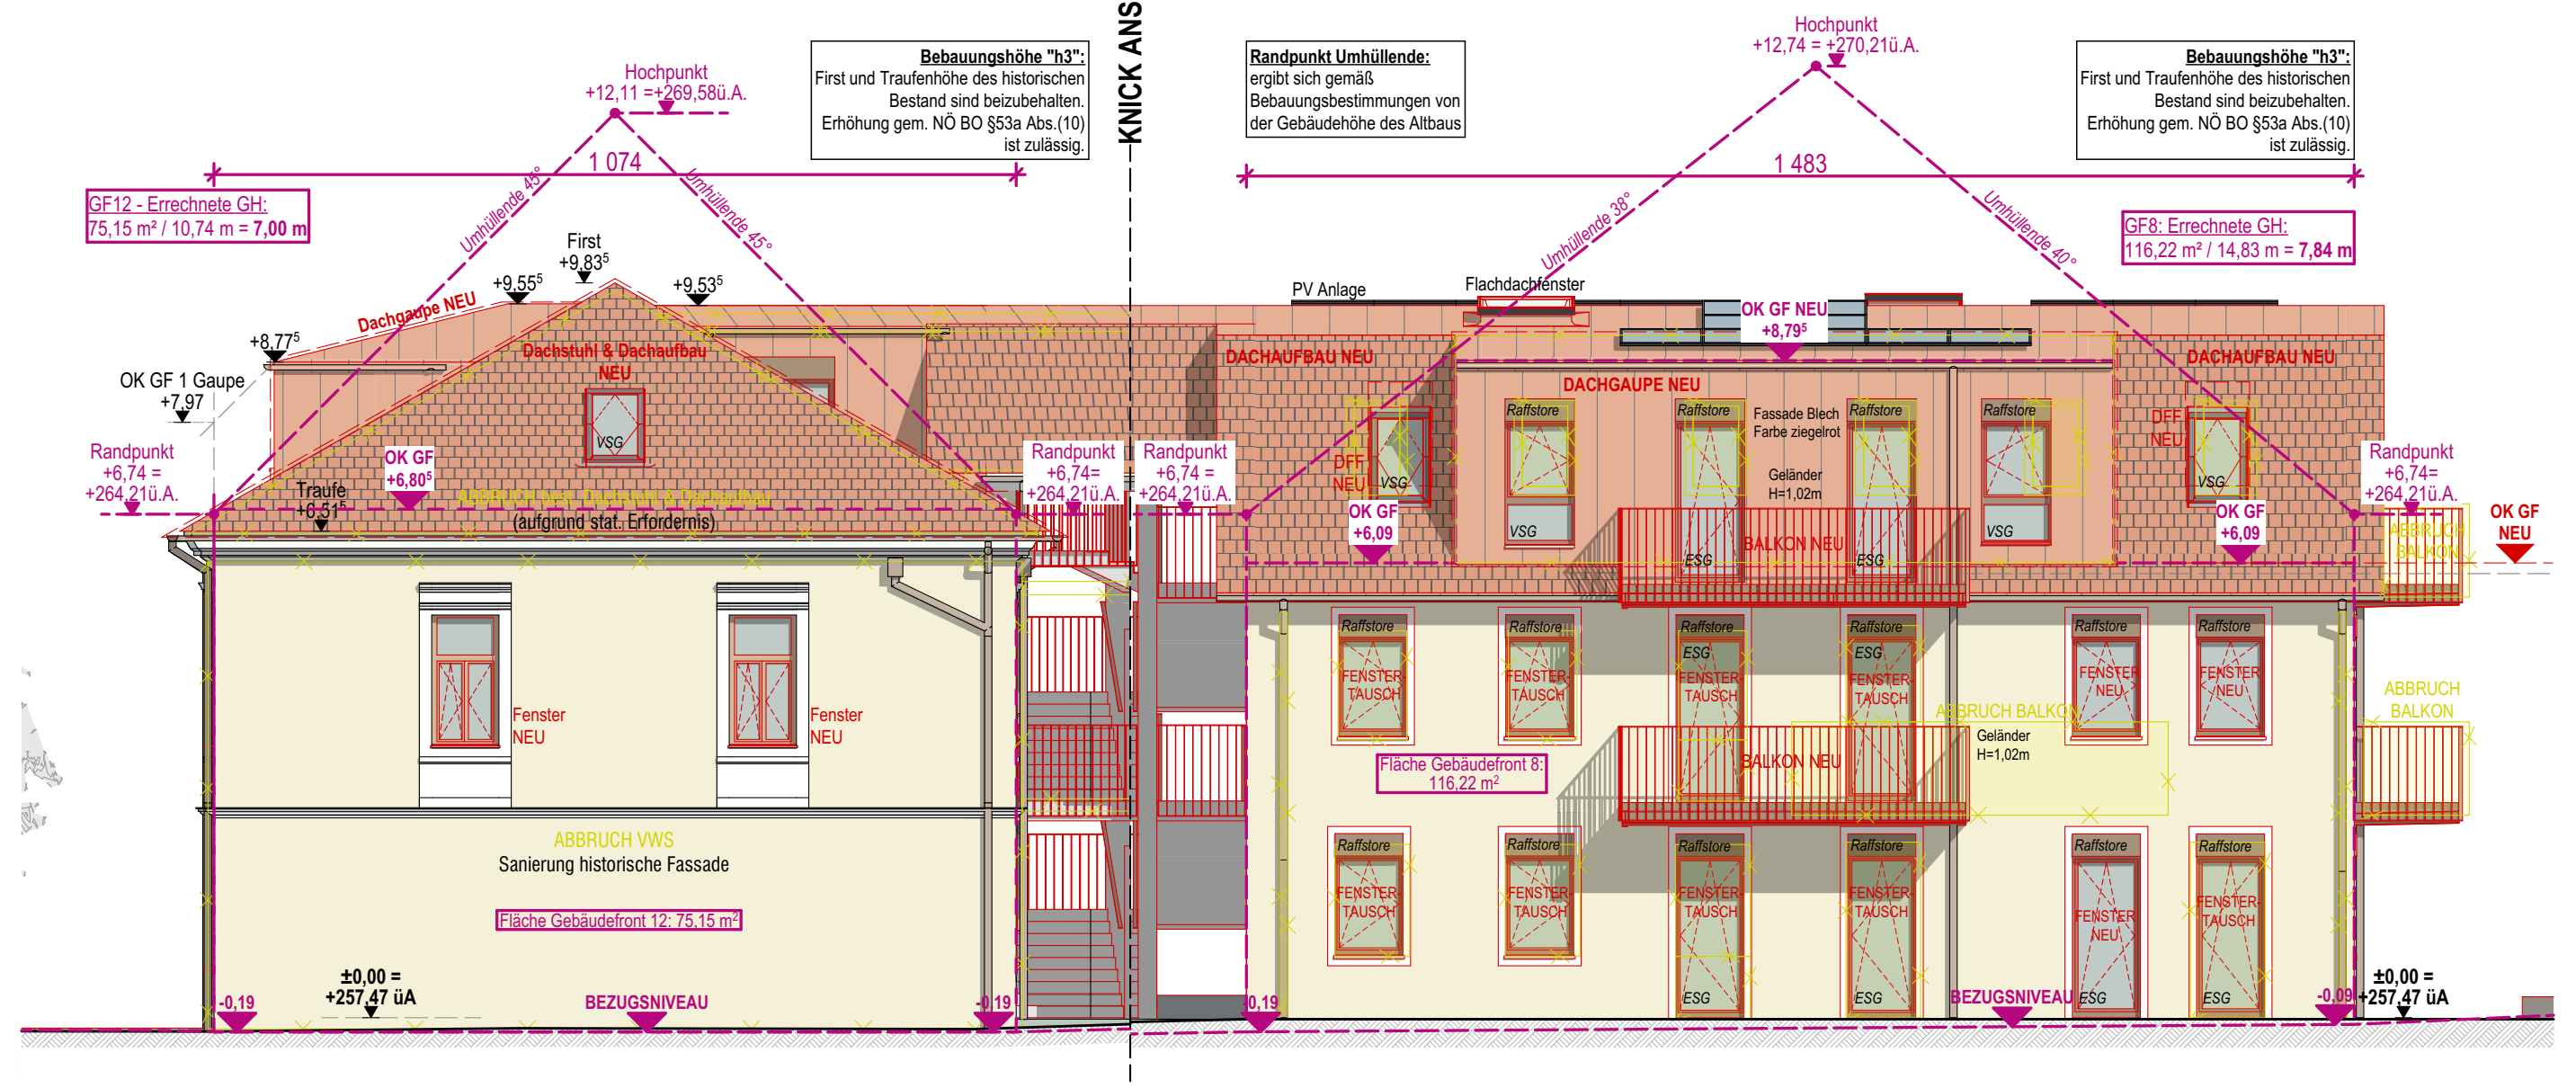
Hochpunkt
+12,74 = +270,21ü.A.
1 483
Bebauungshöhe "h3":
First und Traufenhöhe des historischen Bestand sind beizubehalten. Erhöhung gem. NÖ BO §53a Abs.(10) ist zulässig.
KNICK ANSICHT
Sanierung historische Fassade
BEZUGSNIVEAU

NORDANSICHT M1:100

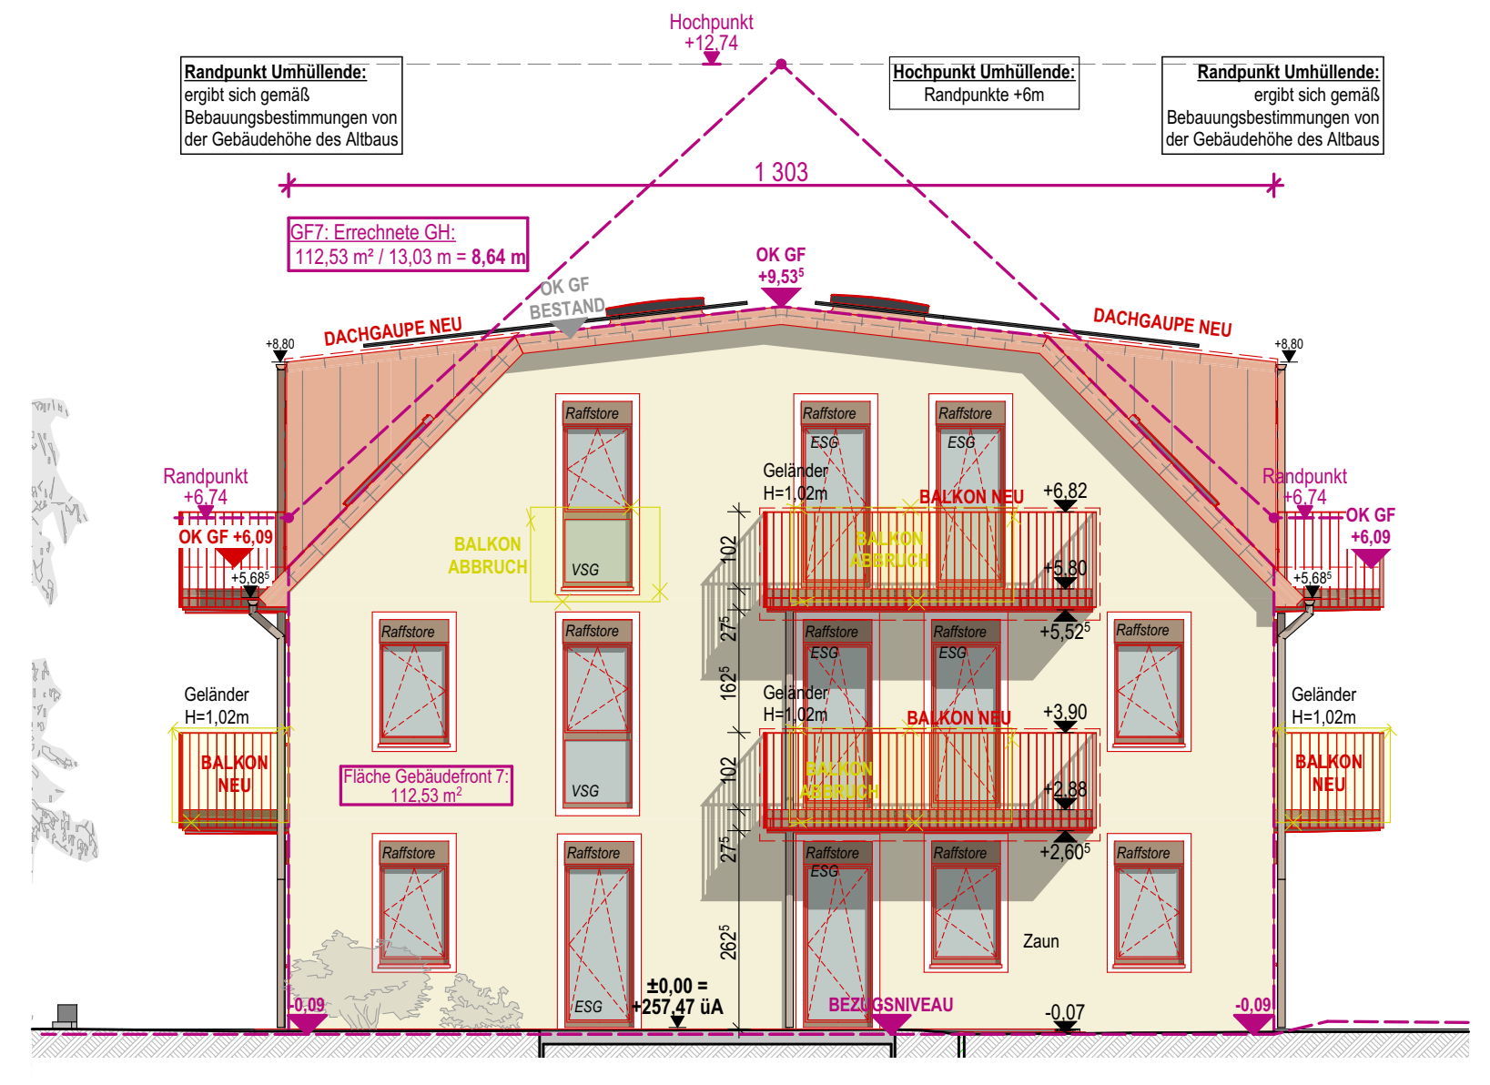

WESTANSICHT M1:100

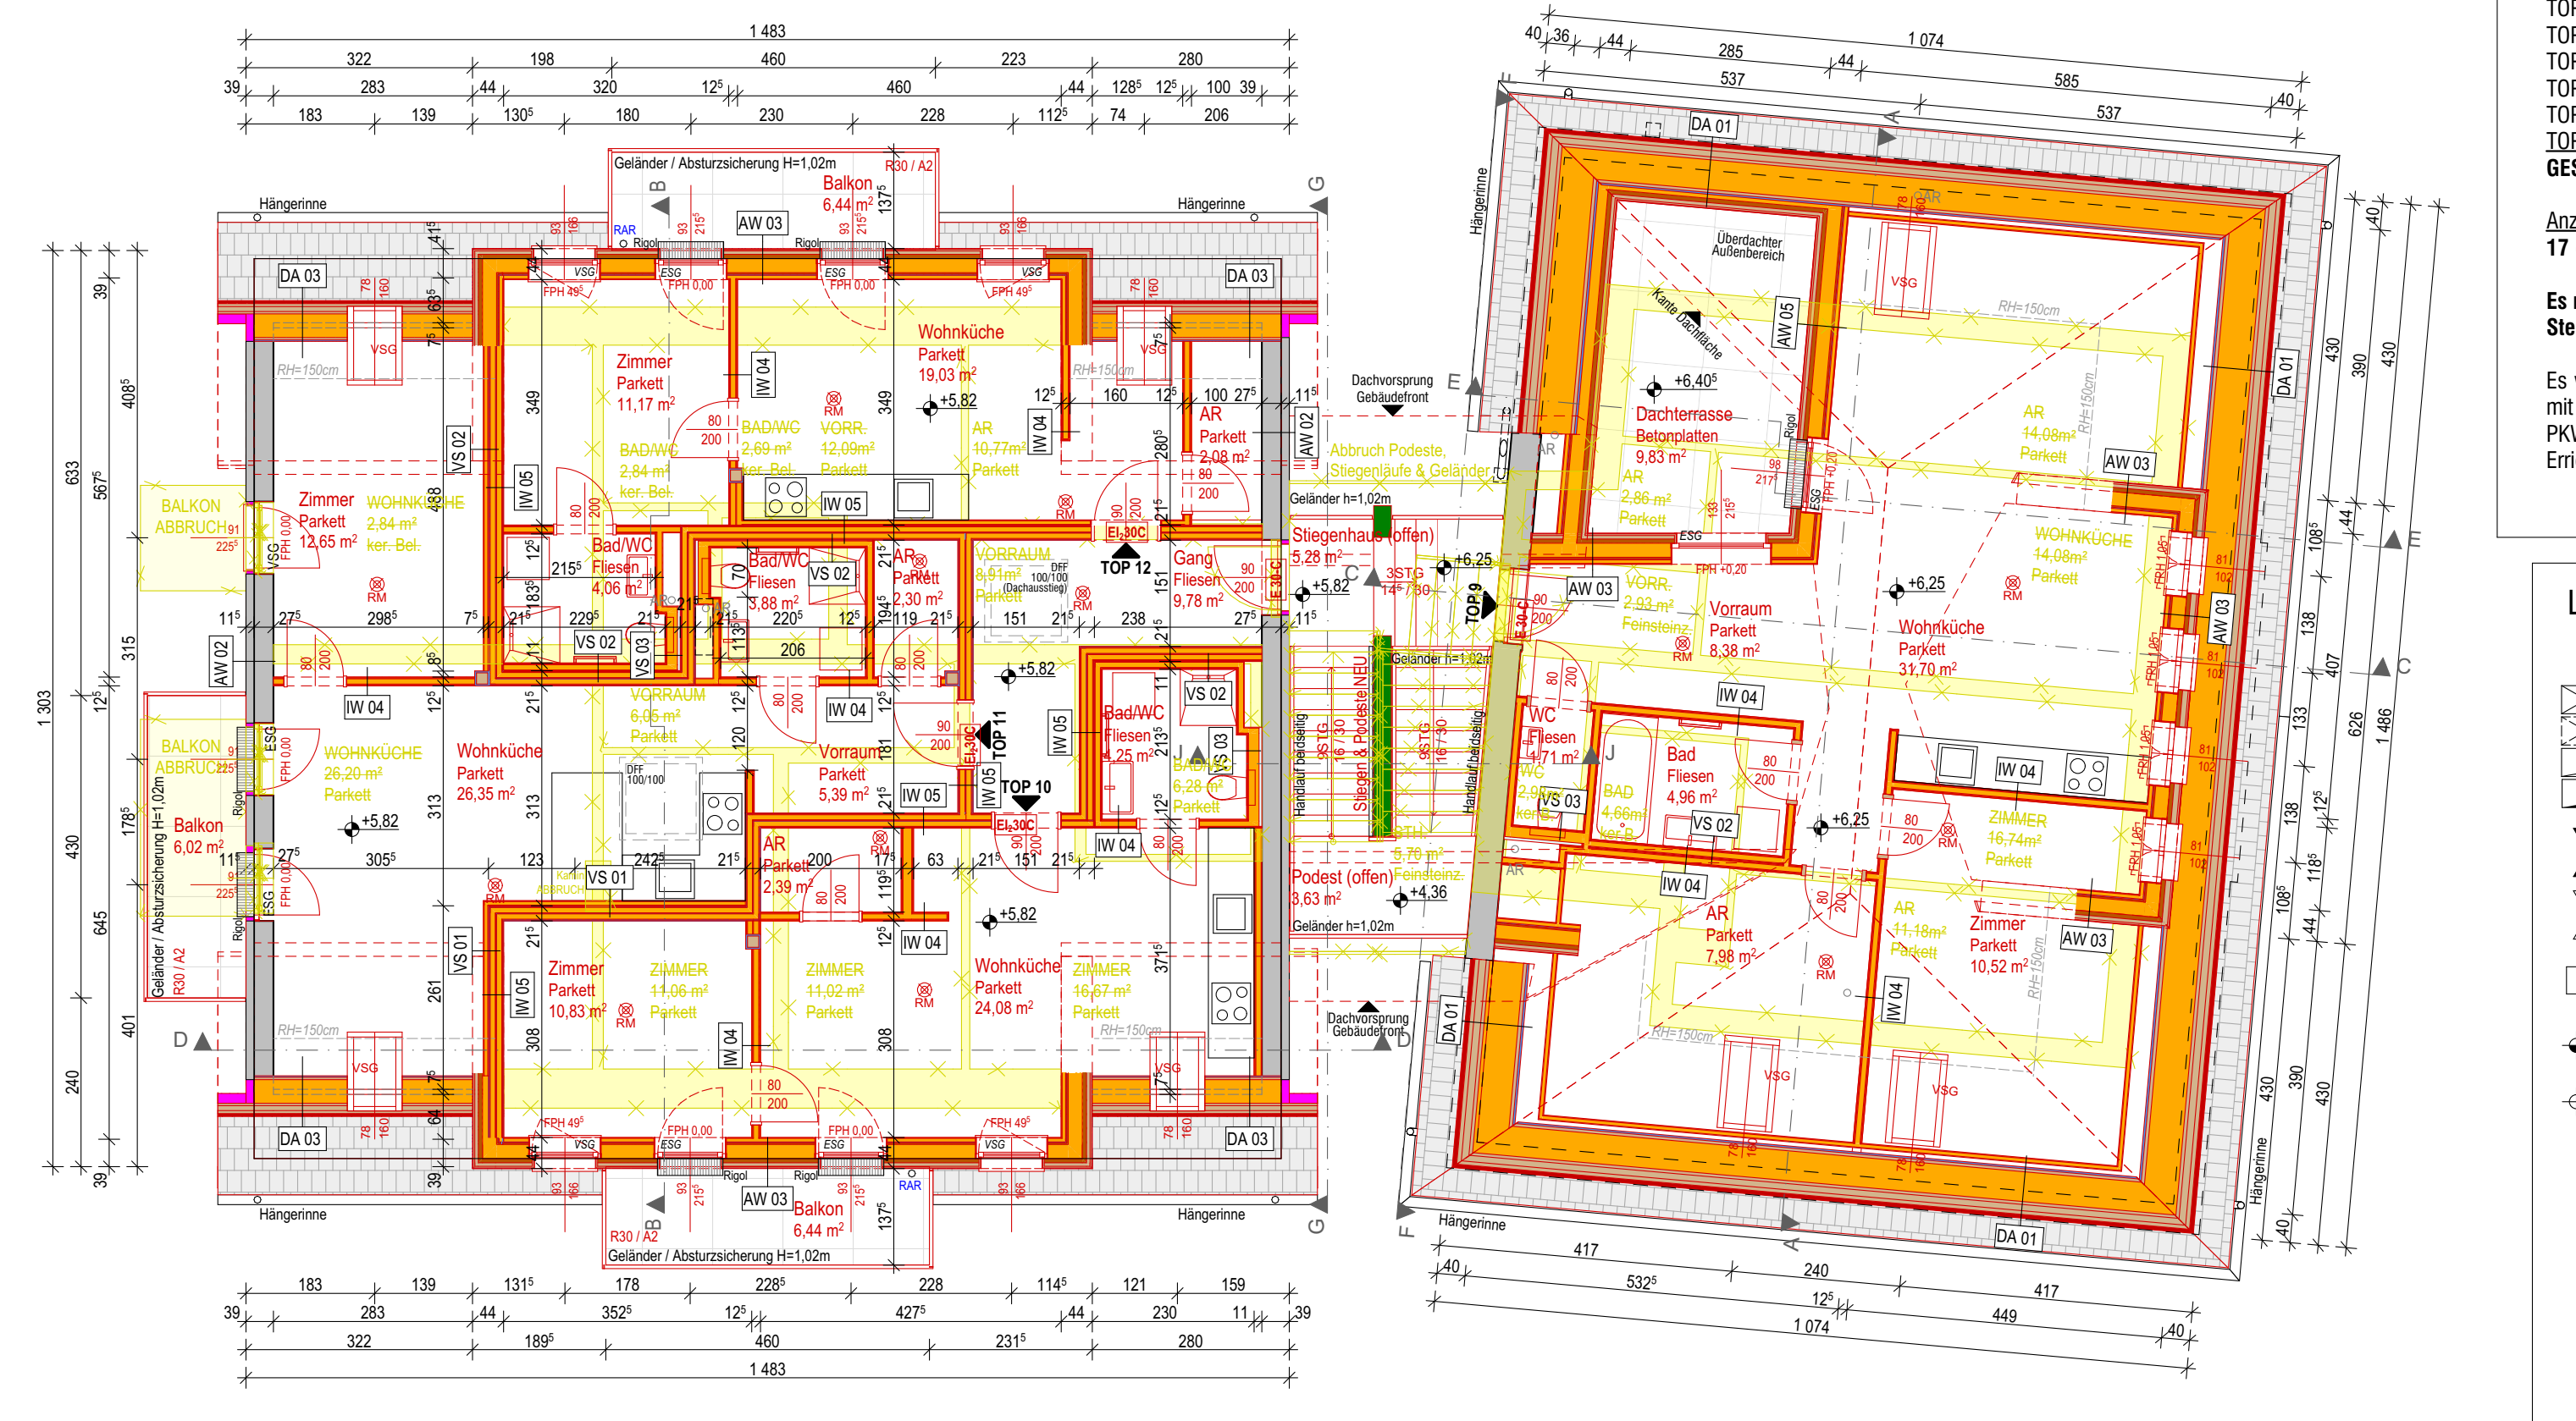

DACHGESCHOSS M1:100

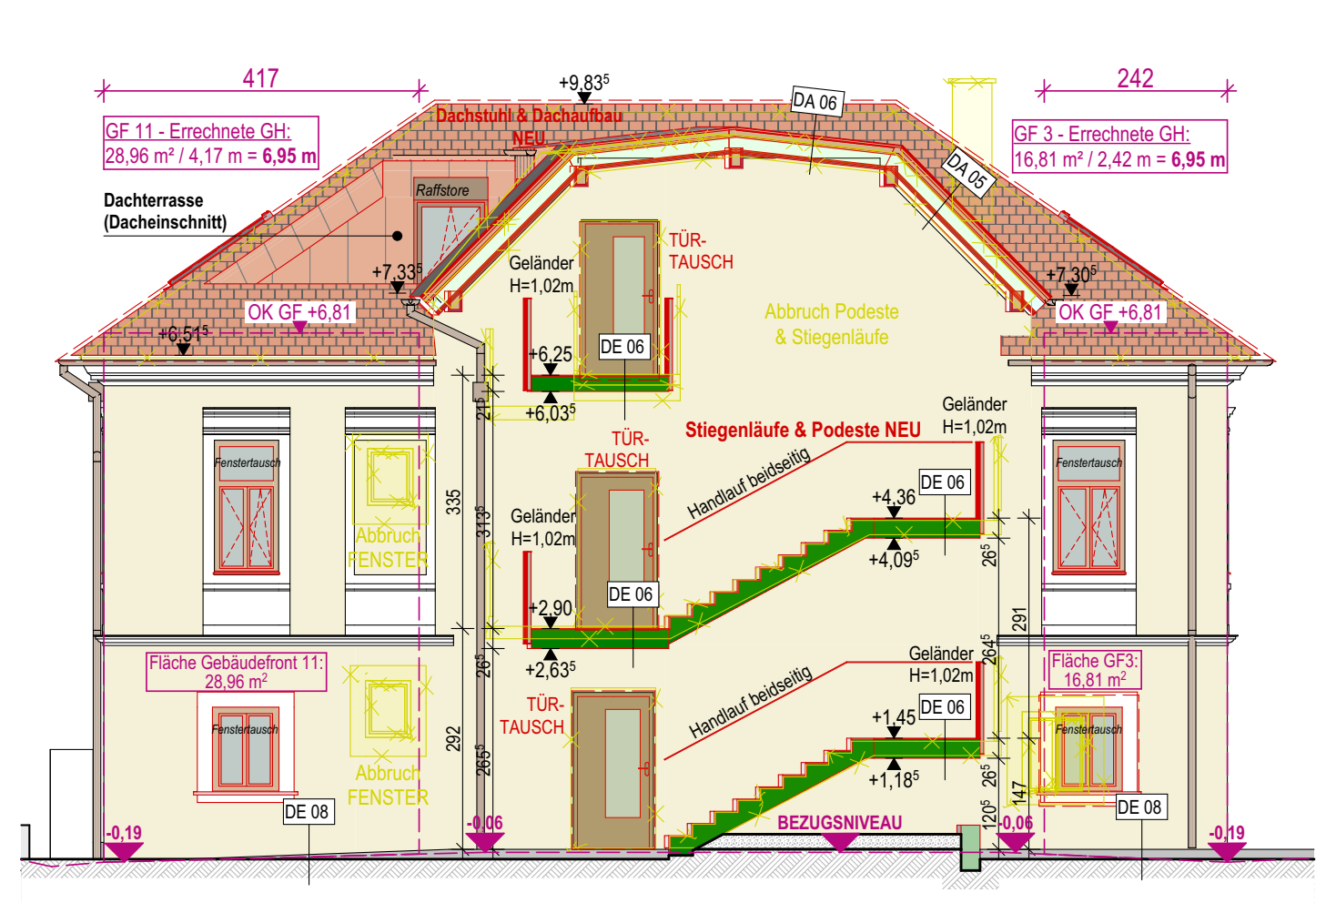

SCHNITT F-F // WESTANSICHT ALTBAU VON STIEGENHAUS M1:100

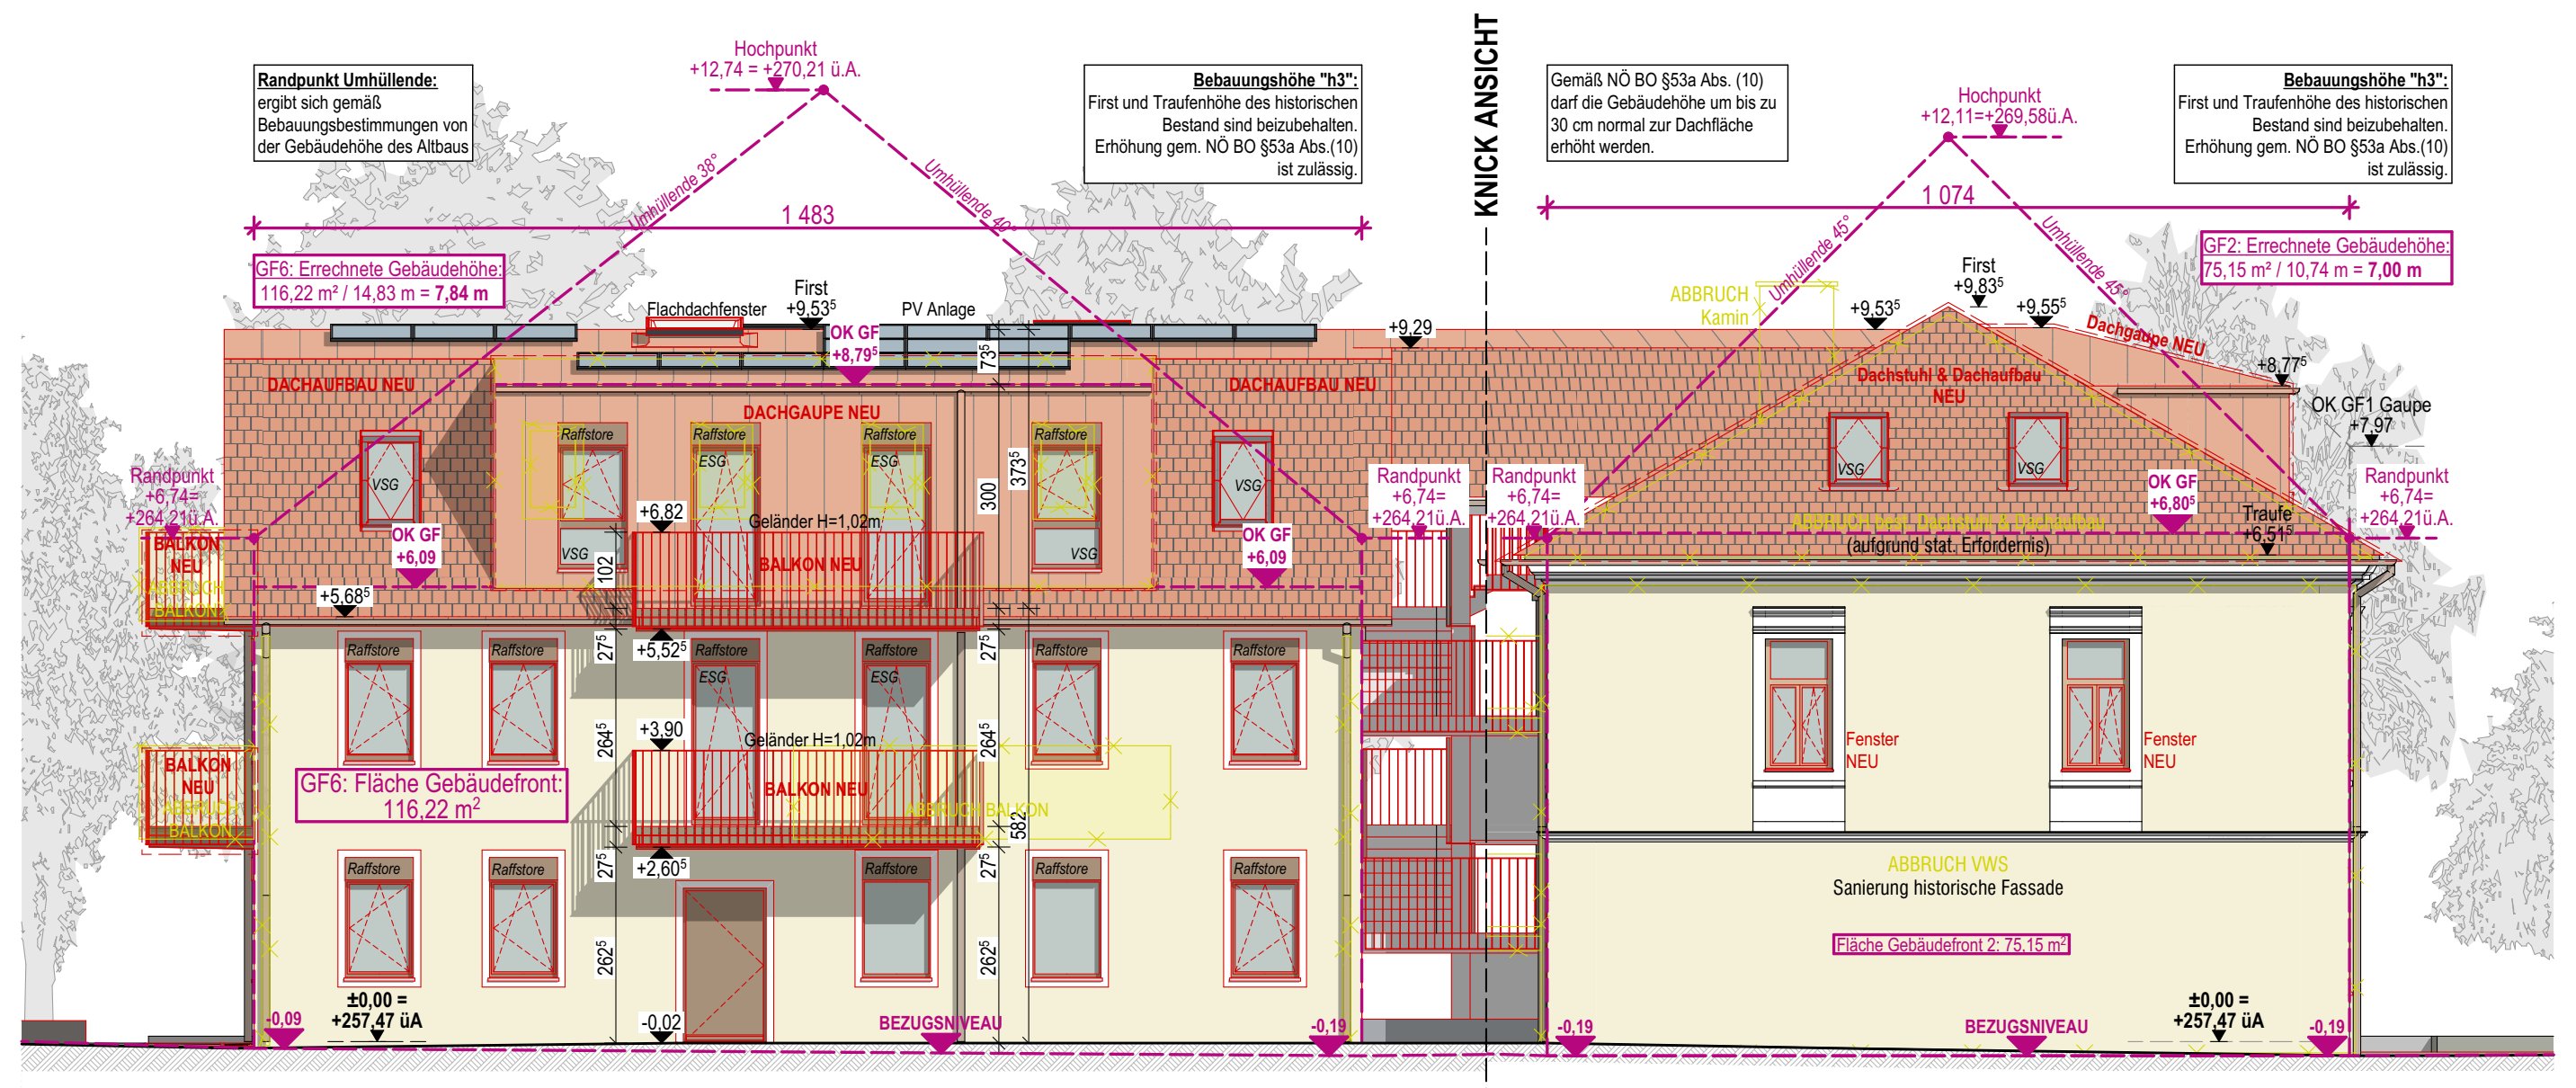
Hochpunkt
+12,11 =+269,58ü.A.
1 074
1 483
Bebauungshöhe "h3":
First und Traufenhöhe des historischen Bestand sind beizubehalten. Erhöhung gem. NÖ BO §53a Abs.(10) ist zulässig.
KNICK ANSICHT
Randpunkt Umhüllende:
ergibt sich gemäß Bebauungsbestimmungen von der Gebäudehöhe des Altbaus
Sanierung historische Fassade
BEZUGSNIVEAU

SÜDANSICHT M1:100

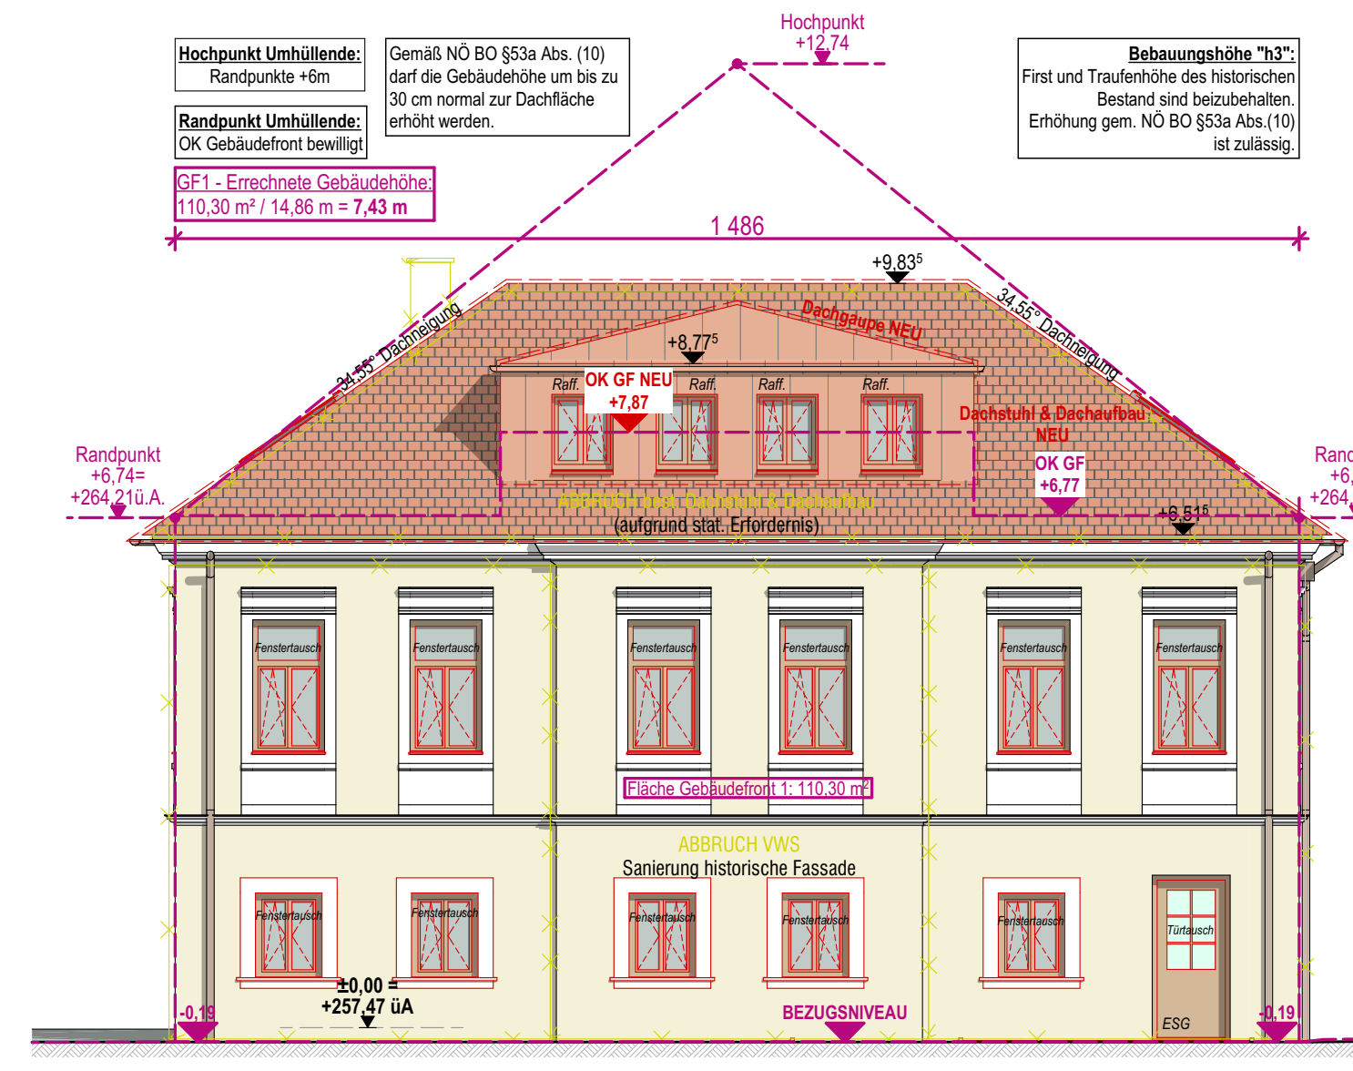

OSTANSICHT M1:100

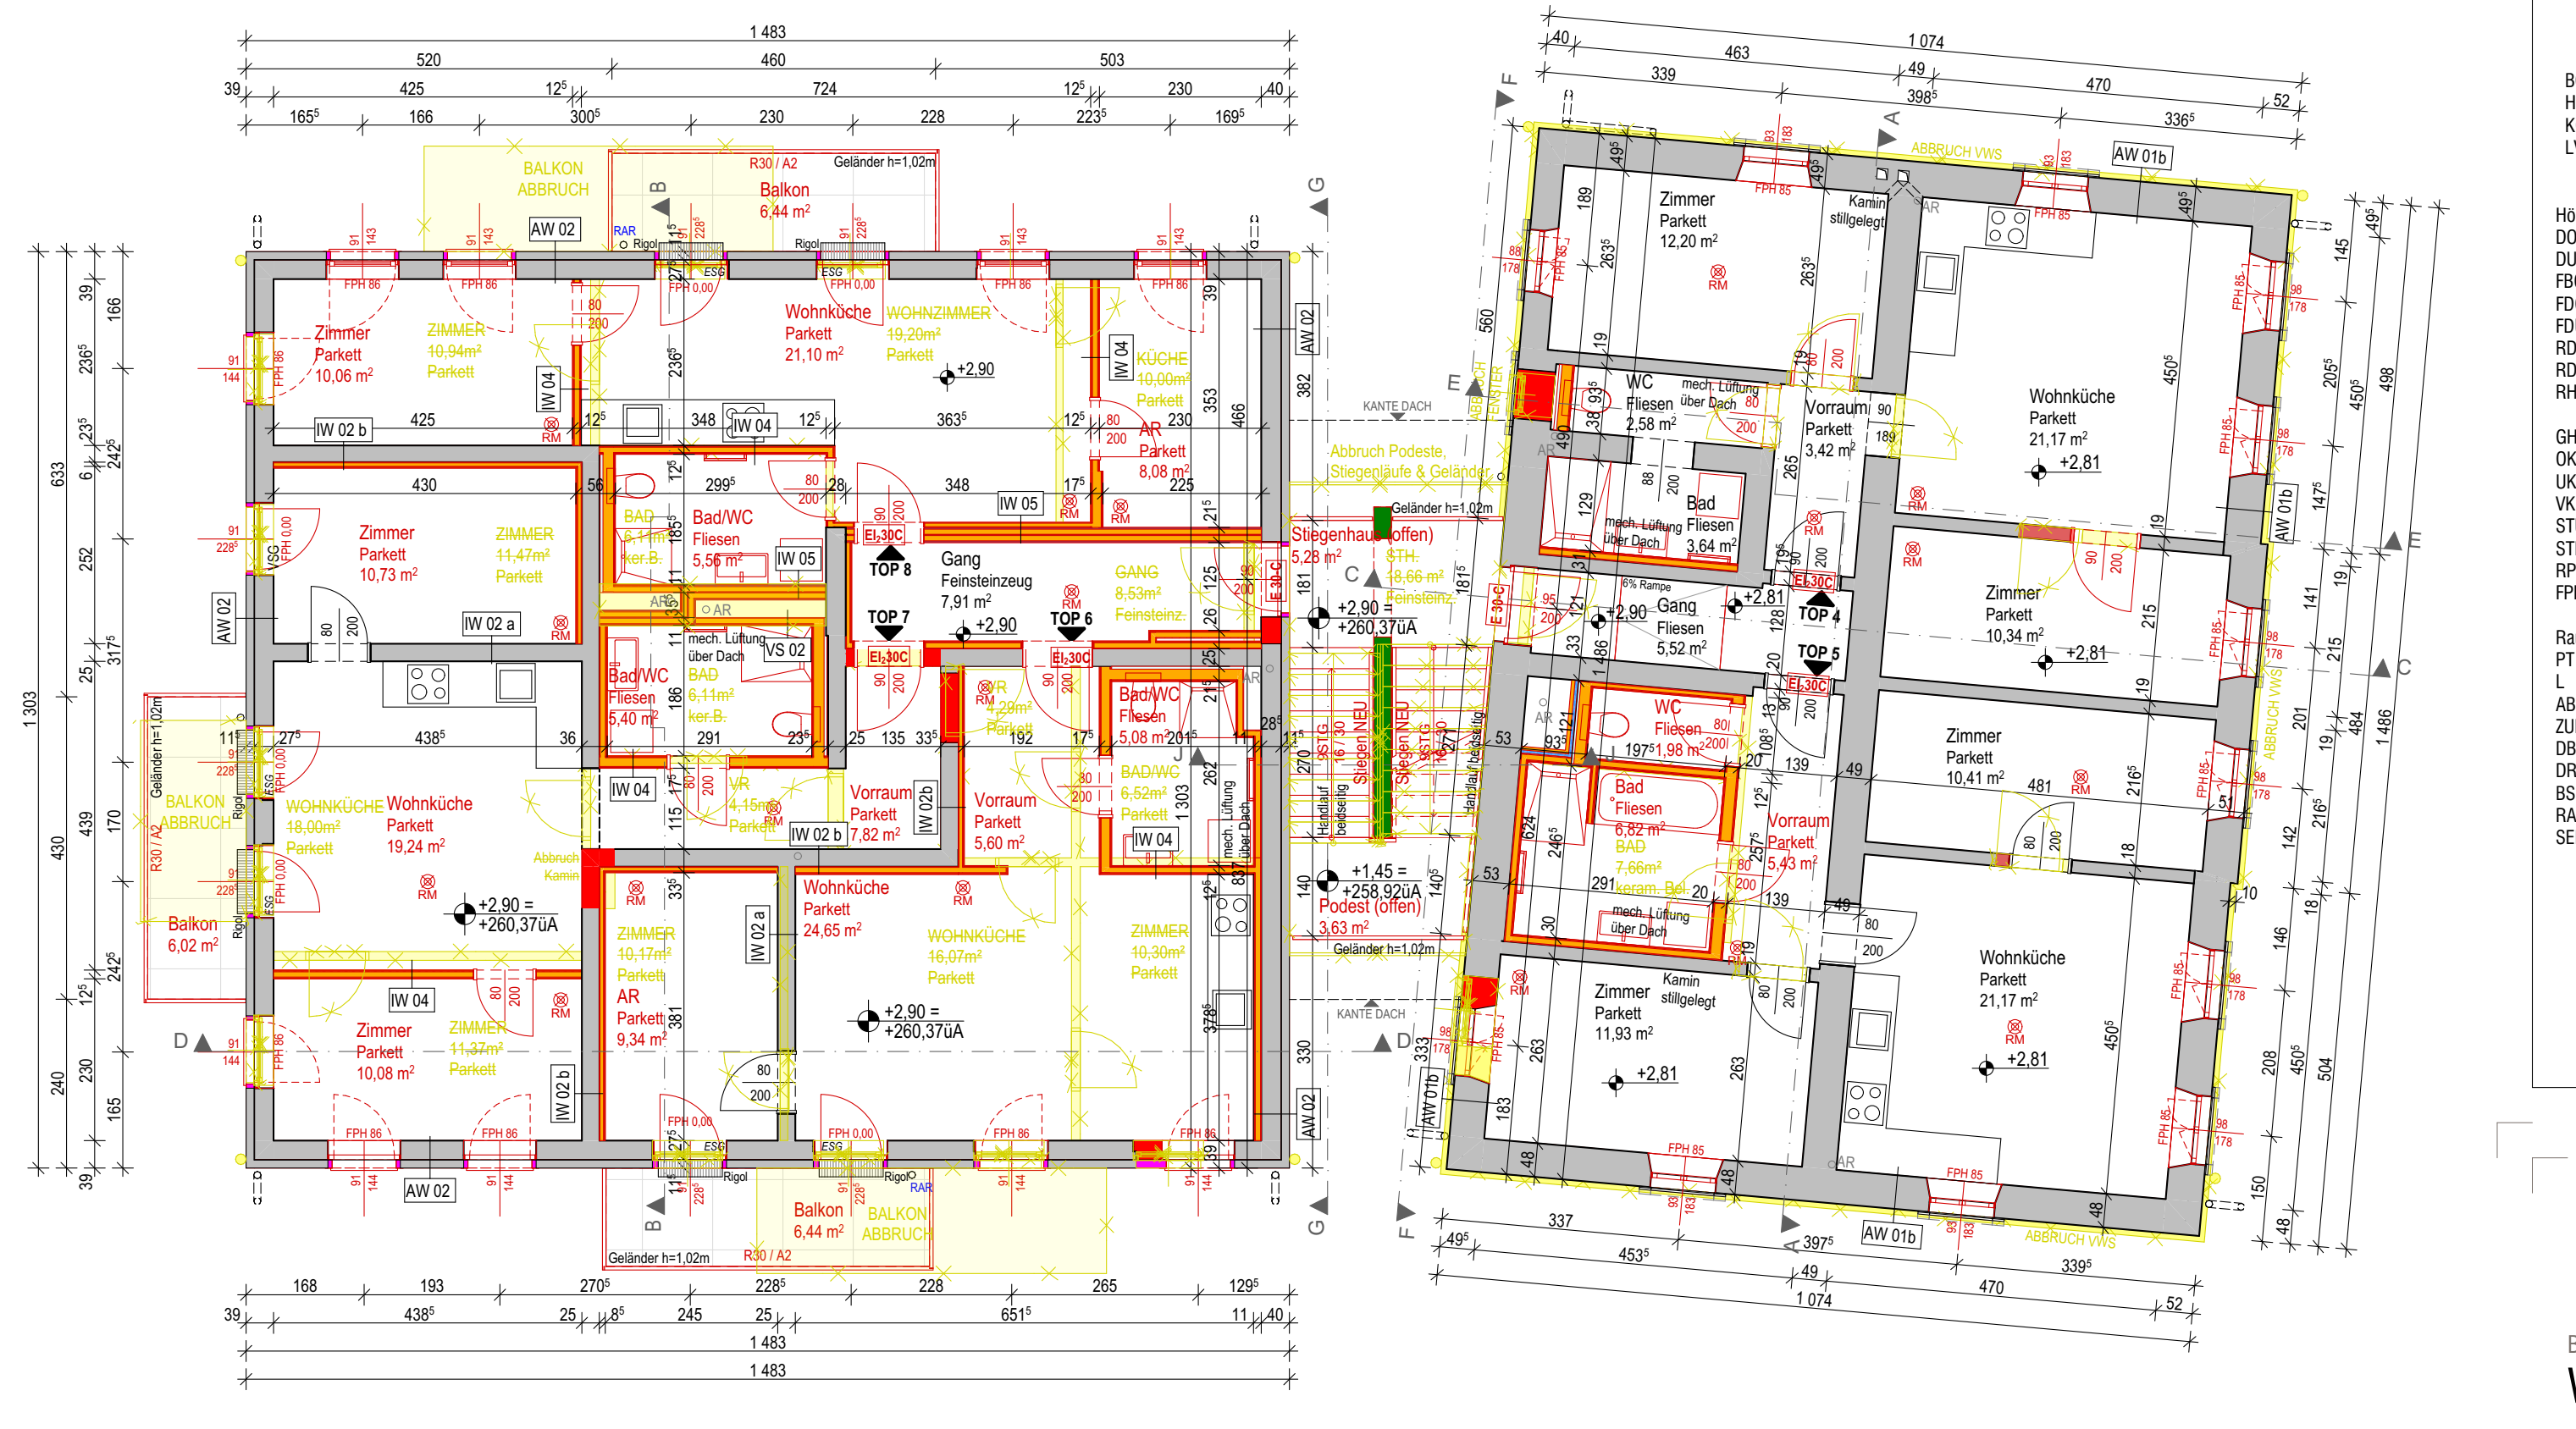

1. OBERGESCHOSS M1:100

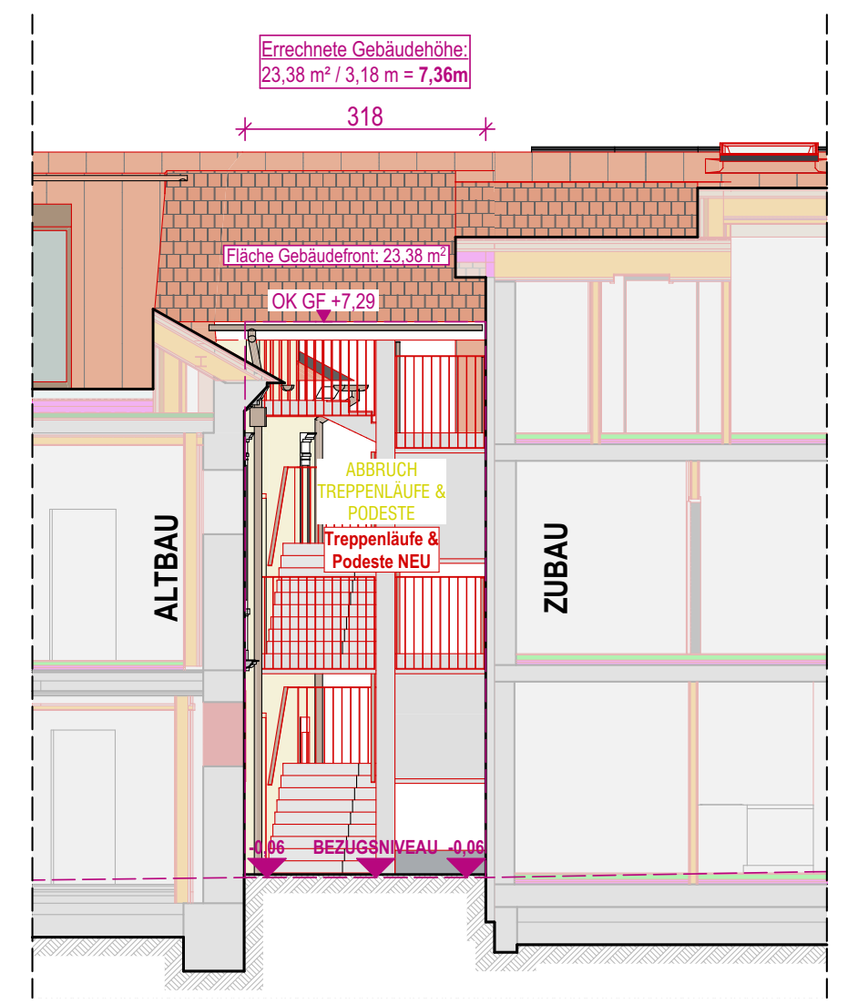

ANSICHT NORD STIEGENHAUS M1:100

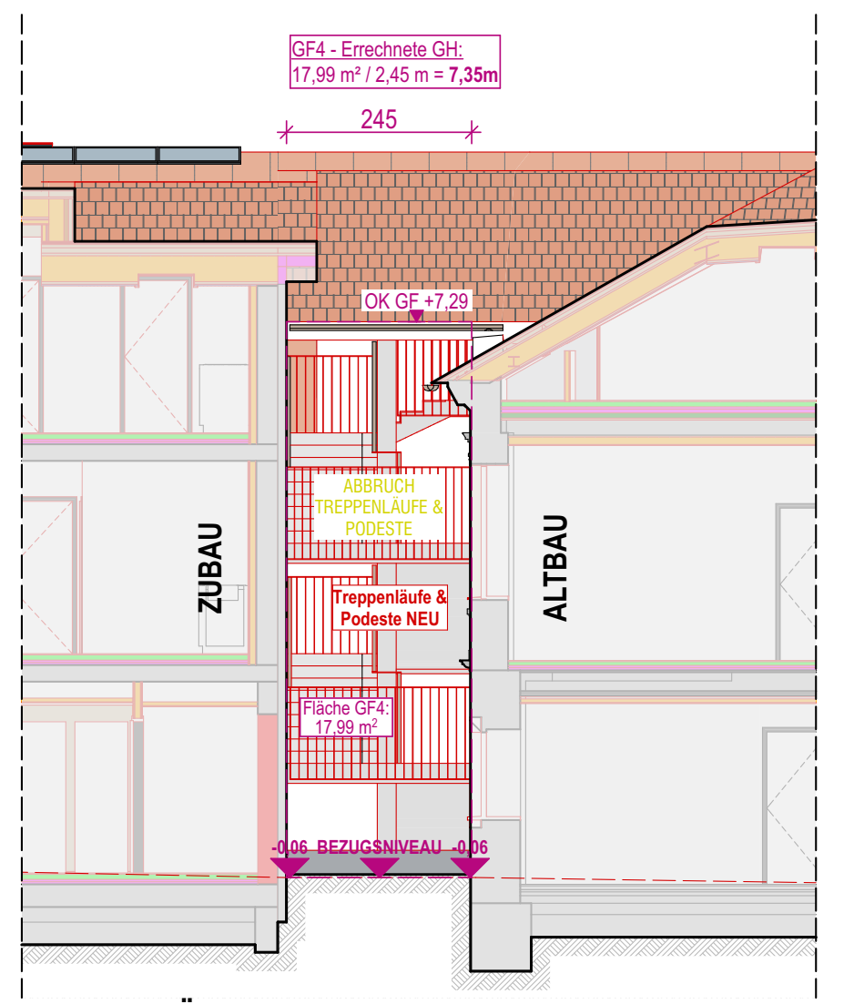

ANSICHT SÜD STIEGENHAUS M1:100

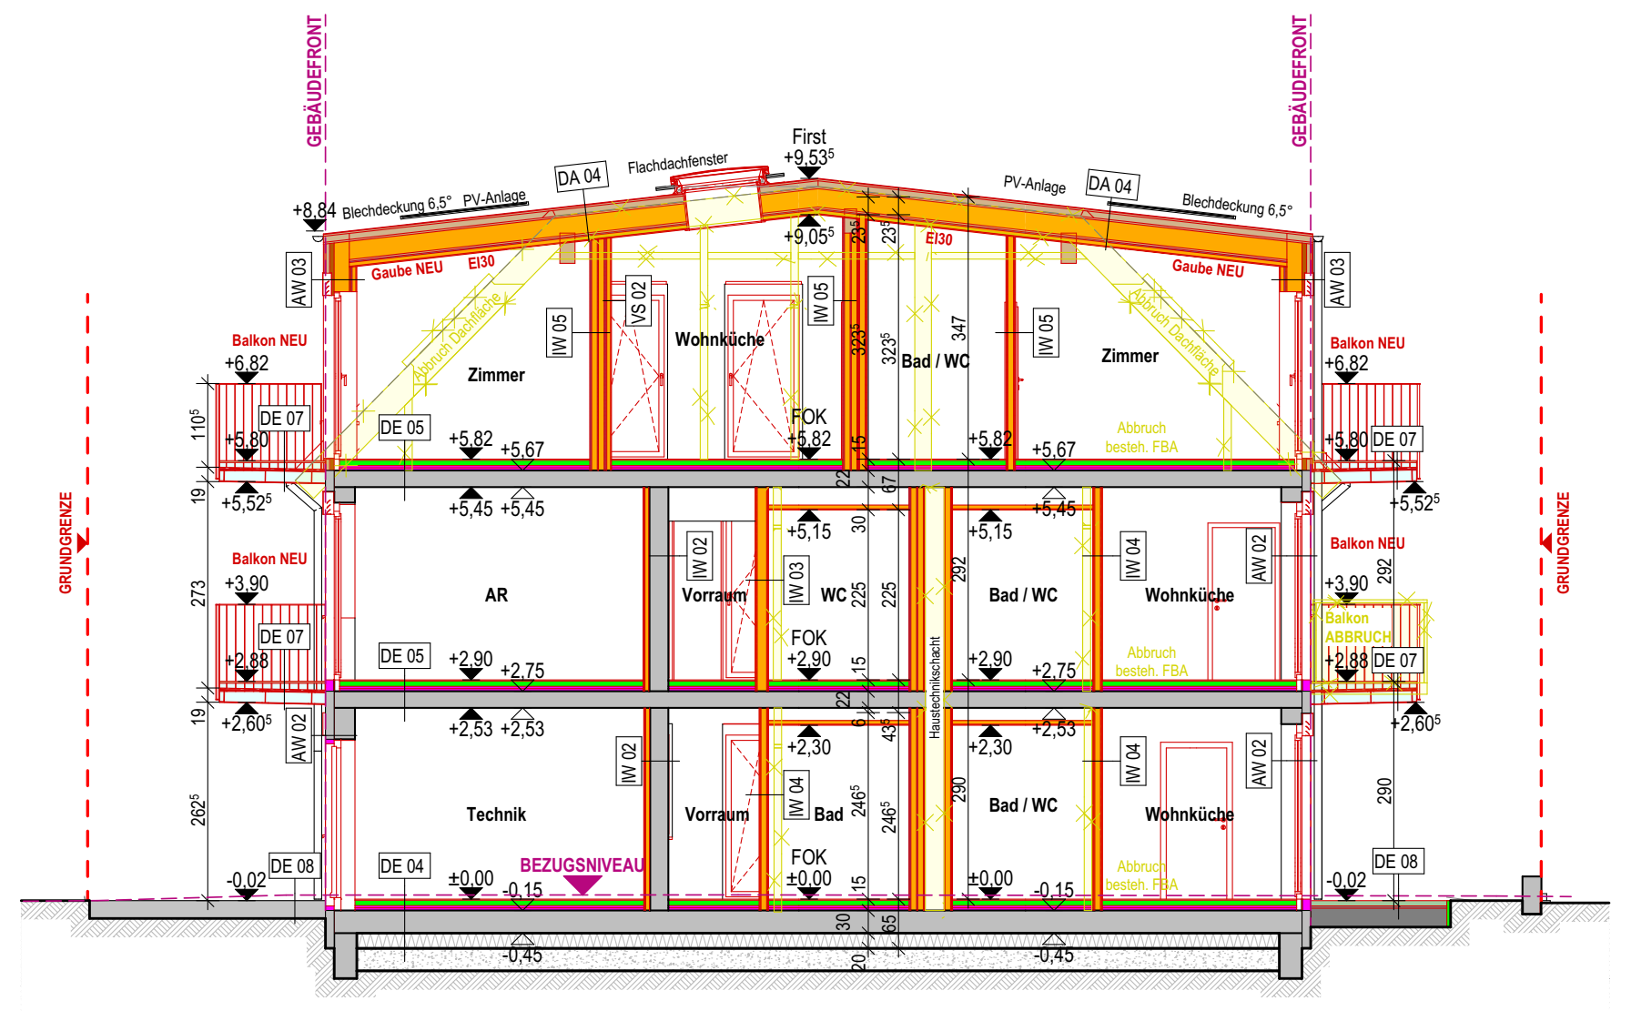

SCHNITT B-B M1:100

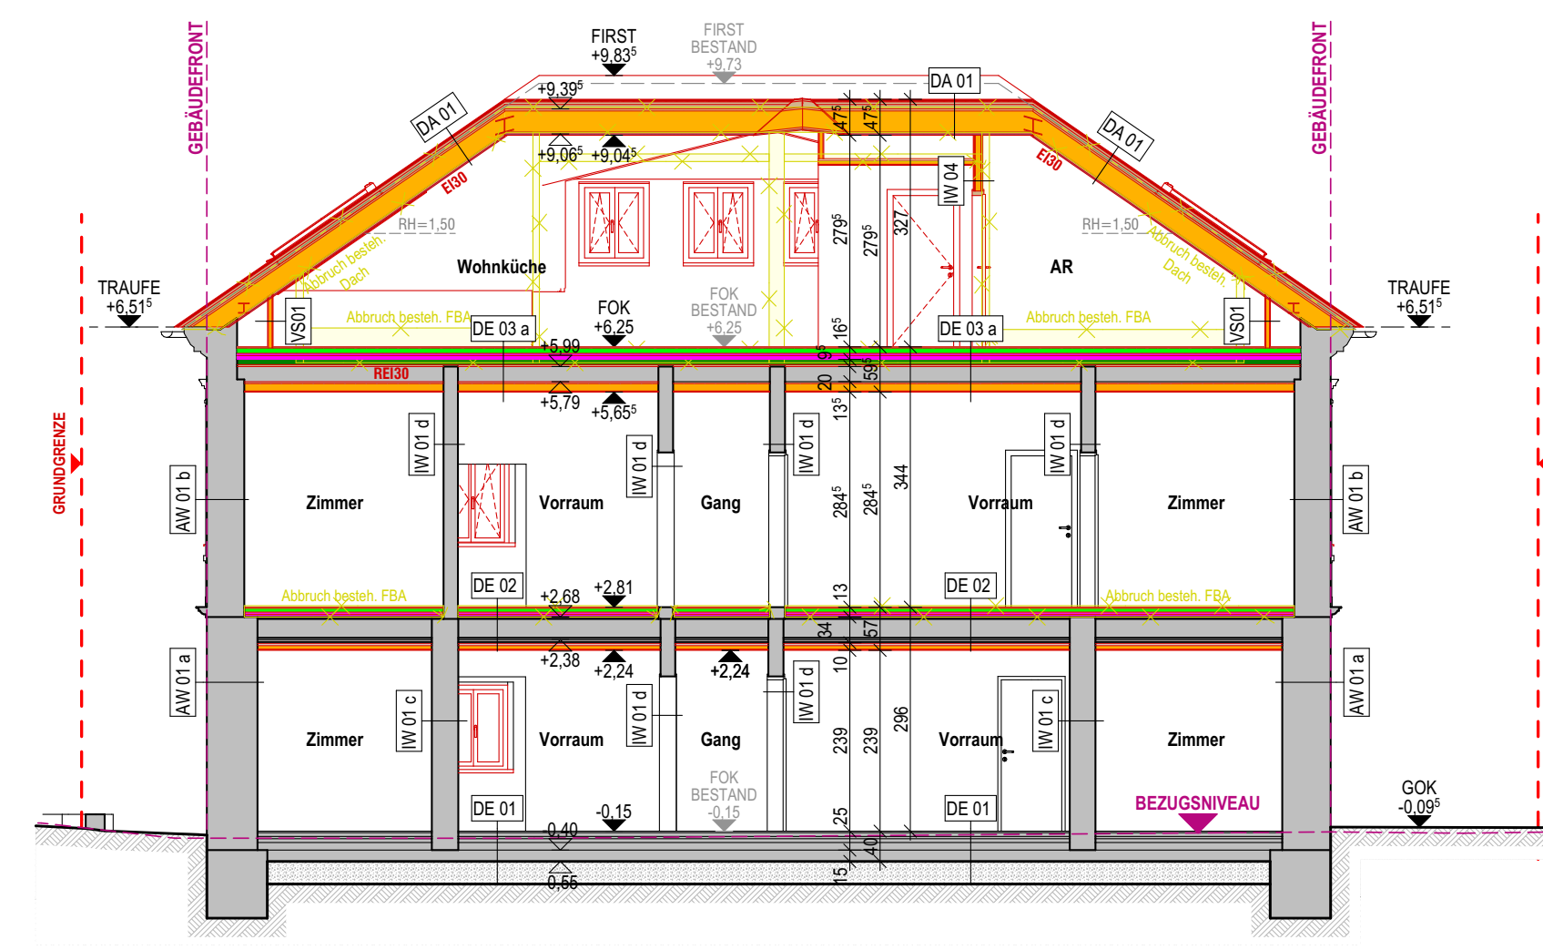

SCHNITT A-A M1:100

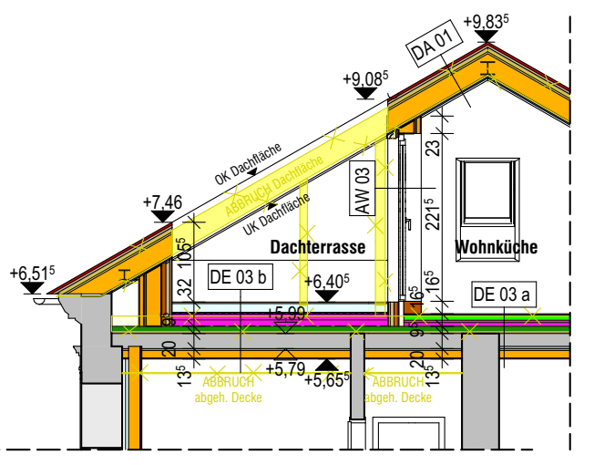

SCHNITT E-E M1:100

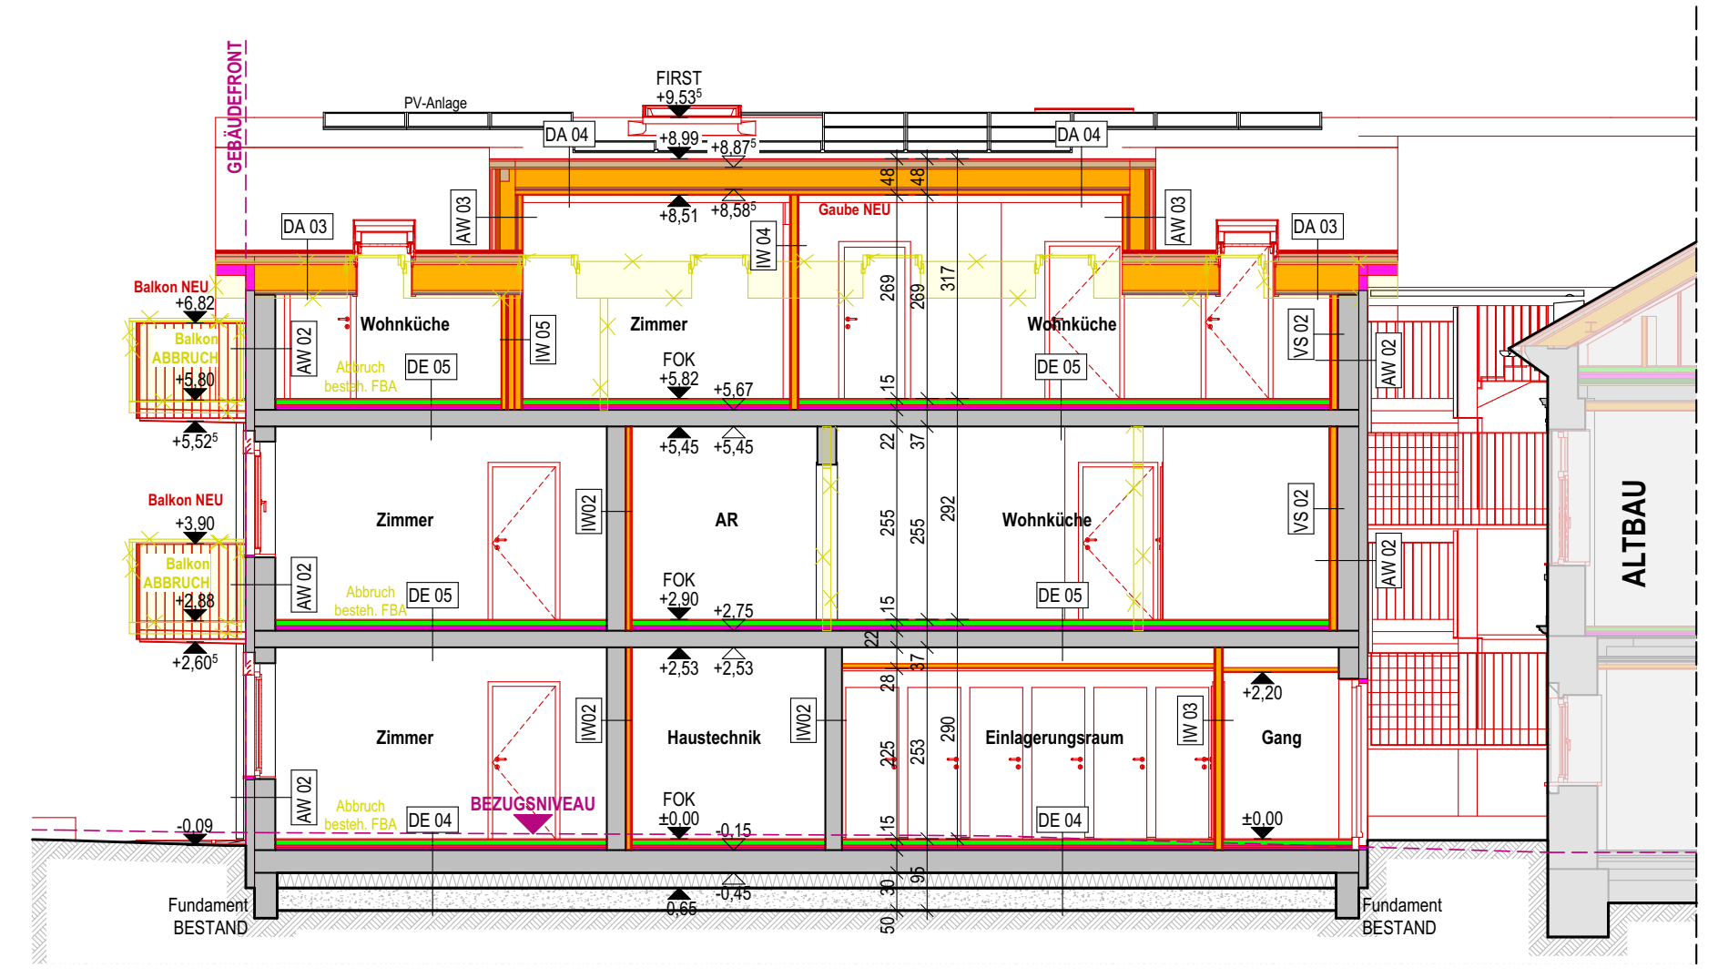

SCHNITT D-D M1:100

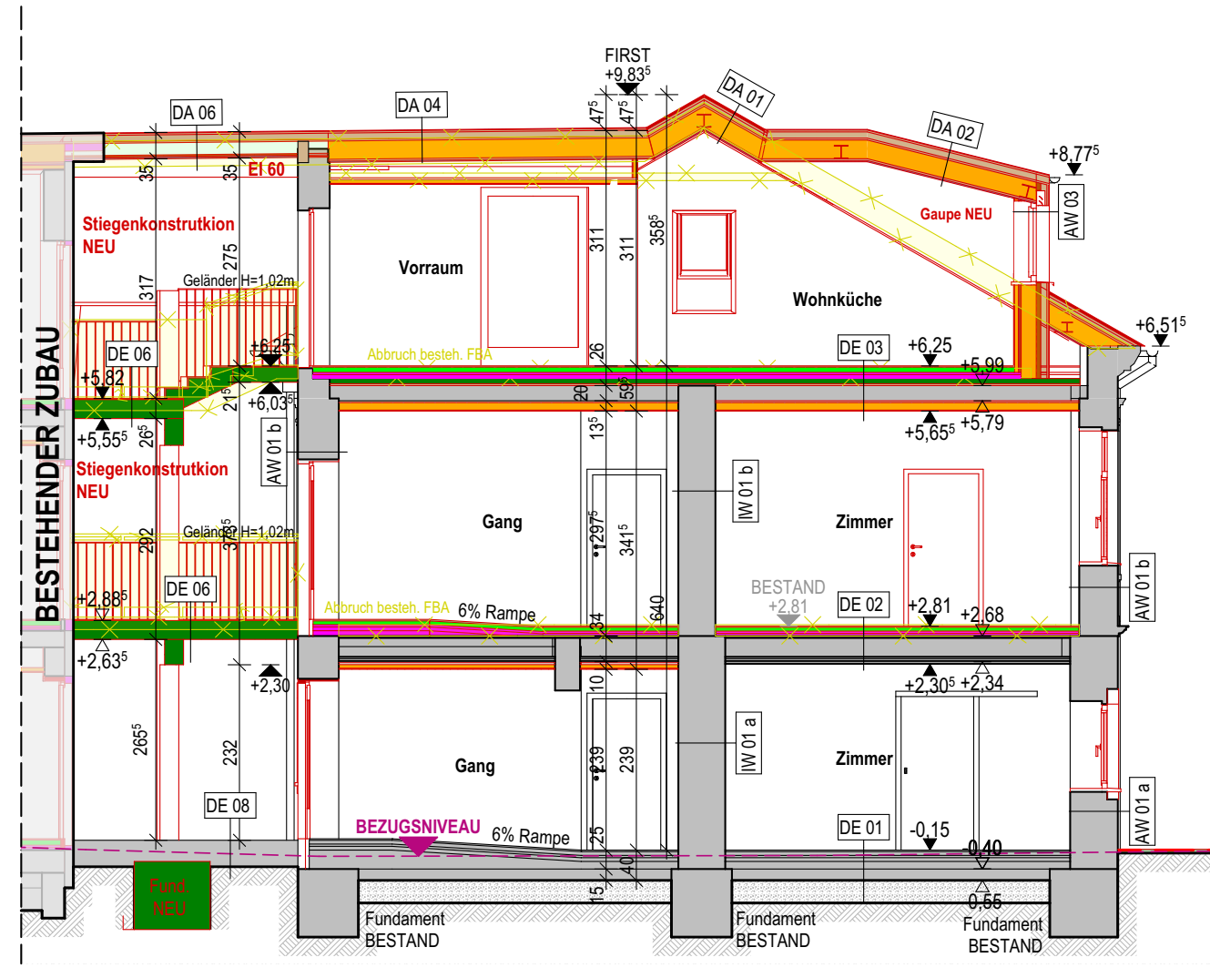

SCHNITT C-C M1:100

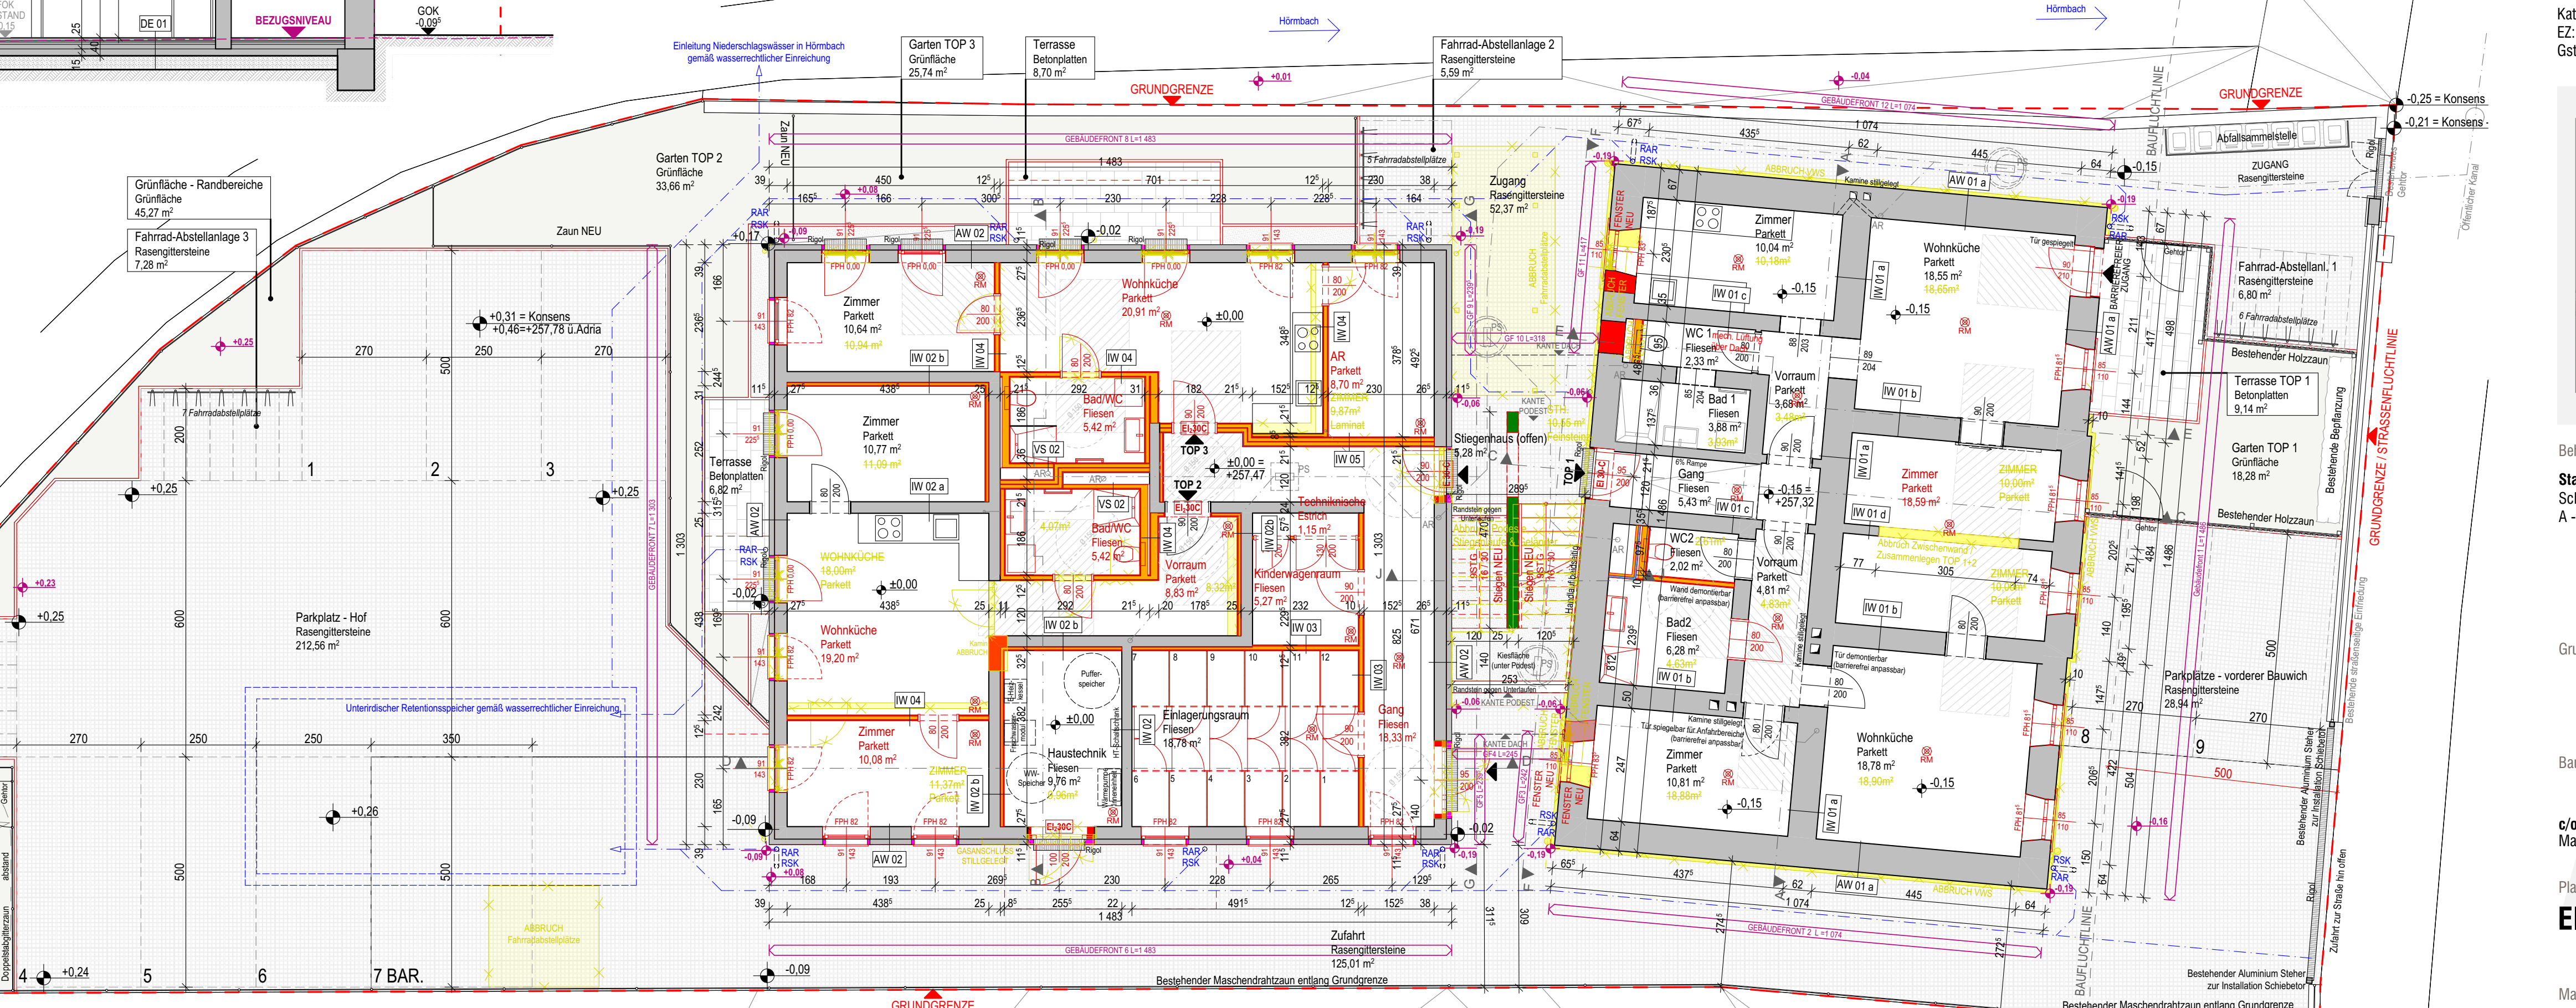

ERDGESCHOSS M1:100

LEGENDE

- Wanddurchbruch
- Deckendurchbruch
- Bodenschlitz
- Bodendurchbruch
- ▼ OK Fertigbau
- ▲ UK Fertigbau
- ▽ OK Rohbau
- △ UK Rohbau
- ± 0,00 Höhenangabe einer waagrechten Fläche
- ±0,00 Höhenangabe eines Punktes in einem Bauwerk - Fertigmaß
- ±0,00 Höhenangabe eines Punktes in einem Bauwerk - Rohbaumaß

- Bestand
- Abbruch
- unbewehrter Beton
- bewehrter Beton
- Mauerwerk
- Stahl (allgemein)
- Holz (allgemein)
- Dämmstoff (hart)
- Dämmstoff (weich)
- Dichtstoff (allgemein)
- Glas
- Gipskarton GKF (Brandschutz)
- Gipskarton GKB - im Nassraum GKBi
- Grünfläche
- Erdmaterial (allgemein)

- Medien
- Fernwärme
- Gas
- Strom
- Heizung
- Regenwasser
- Schmutzwasser
- Wasser
- Grundgrenze
- Baufluchtlinie
- Baulinie
- Widmungsgrenze

BGF	Bruttogesamtfläche
HNF / NNF	Haupt- Nebennutzfläche
KG	Kochgelegenheit
LV	Leerverohrung

Höhenbezugs- und Maßangaben

DOK	Deckenoberkante
DUK	Deckenunterkante
FBOK	Fußbodenoberkante
FDOK	Fundamentoberkante
FDUK	Fundamentunterkante
RDOK	Deckenoberkante
RDUK	Deckenunterkante
RH	lichte Raumhöhe
GH	Geschoßhöhe
OK	Oberkante
UK	Unterkante
VK	Vorderkante
STUK	Sturzunterkante (Rohbaumaß)
STH	Sturzhöhe gemessen von STUK bis DUK (Rohbaumaß)
RPH	Rohbauparapethöhe
FPH	fertige Parapethöhe (FBOK bis OK Fensterbank Innen)

Rauch-, Abgas- und Luftfänge, Schächte

PT	Putztürchen
L	Lüftungsschacht
ABL	Abluft
ZUL	Zuluft
DBA	Druckbelüftungsanlage
DRE	Druckregeleinheit
BSK	Brandsschutzklappe
RAE	Rauchabzugseinrichtung lt. OIB 2
SEL	Schachtentlüftung

Öffnungen und deren Abschlüsse

WD	Wanddurchbruch
DD	Deckendurchbruch
FBD	Fußbodendurchbruch
FDD	Fundamentdurchbruch
WS	Wandschlitz
WA	Wandaussparung
DA	Deckenaussparung
FBA	Fußbodenaussparung
DF	Drehflügel
DKF	Drehkippflügel
KF	Kippflügel
SF	Schiebeflügel
SWF	Schwingflügel
WF	Wendeflügel
HT	Hebetüre
HST	Hebeschiebetüre
DL	Durchgangslichte
OL	Oberlichte
FIX	Fixverglasung
GGT	Ganzglastüre
VSG	Verbund-Sicherheitsglas
ESG	Einscheiben-Sicherheitsglas

Drehflügel
Drehkippflügel
Kippflügel
Fenstertüre

EI2 30-C-, EI2 60-C-und EI2 90-C
Feuerschutztüren mit Angabe der Feuerwiderstandsklasse
(gemäß ÖNORM B 3850 und ÖNORM B 3807)

GT	gasdichte Türe
DT	Drucktüre
S 200	Rauchabschluss
C	Selbstschließend
FLS	Freilaufschließer
el.TÖ	elektrischer Türöffner

EINREICHPLAN

PARIE **A B C**

Bauvorhaben
WNEU30
2540 Bad Vöslau, Wiener Neustädter Straße 30

Katastralgemeinde 04035 Vöslau
EZ: 719
GstNr.: 748

Übersicht

Flächenwidmungsplan

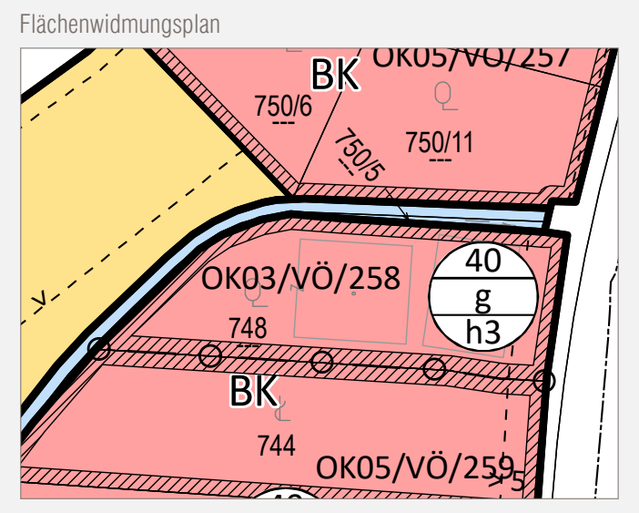

Behörde
Stadtgemeinde Bad Vöslau
Schloßplatz 1
A - 2540 Bad Vöslau

Grundeigentümer

Bauwerber / Auftraggeber

c/o BS Real 360 GmbH
Marokkanergasse 22, A - 1030 Wien

ARTMÜLLER ARCHITEKTEN
ZIVILTECHNIKER GMBH
Stolberggasse 34|26 A-1050 Wien
t [+43] 01 . 581 40 83 f [+43] 01. 581 40 83 99 office@artmueller.eu

Planinhalt
EINREICHPLAN

Maßstab	Gez	Datum	Plannr.	Index
1:100, 1:500	ML	21-10-2026	WNEU30_40_01	

Erstellt, am 22.10.2026