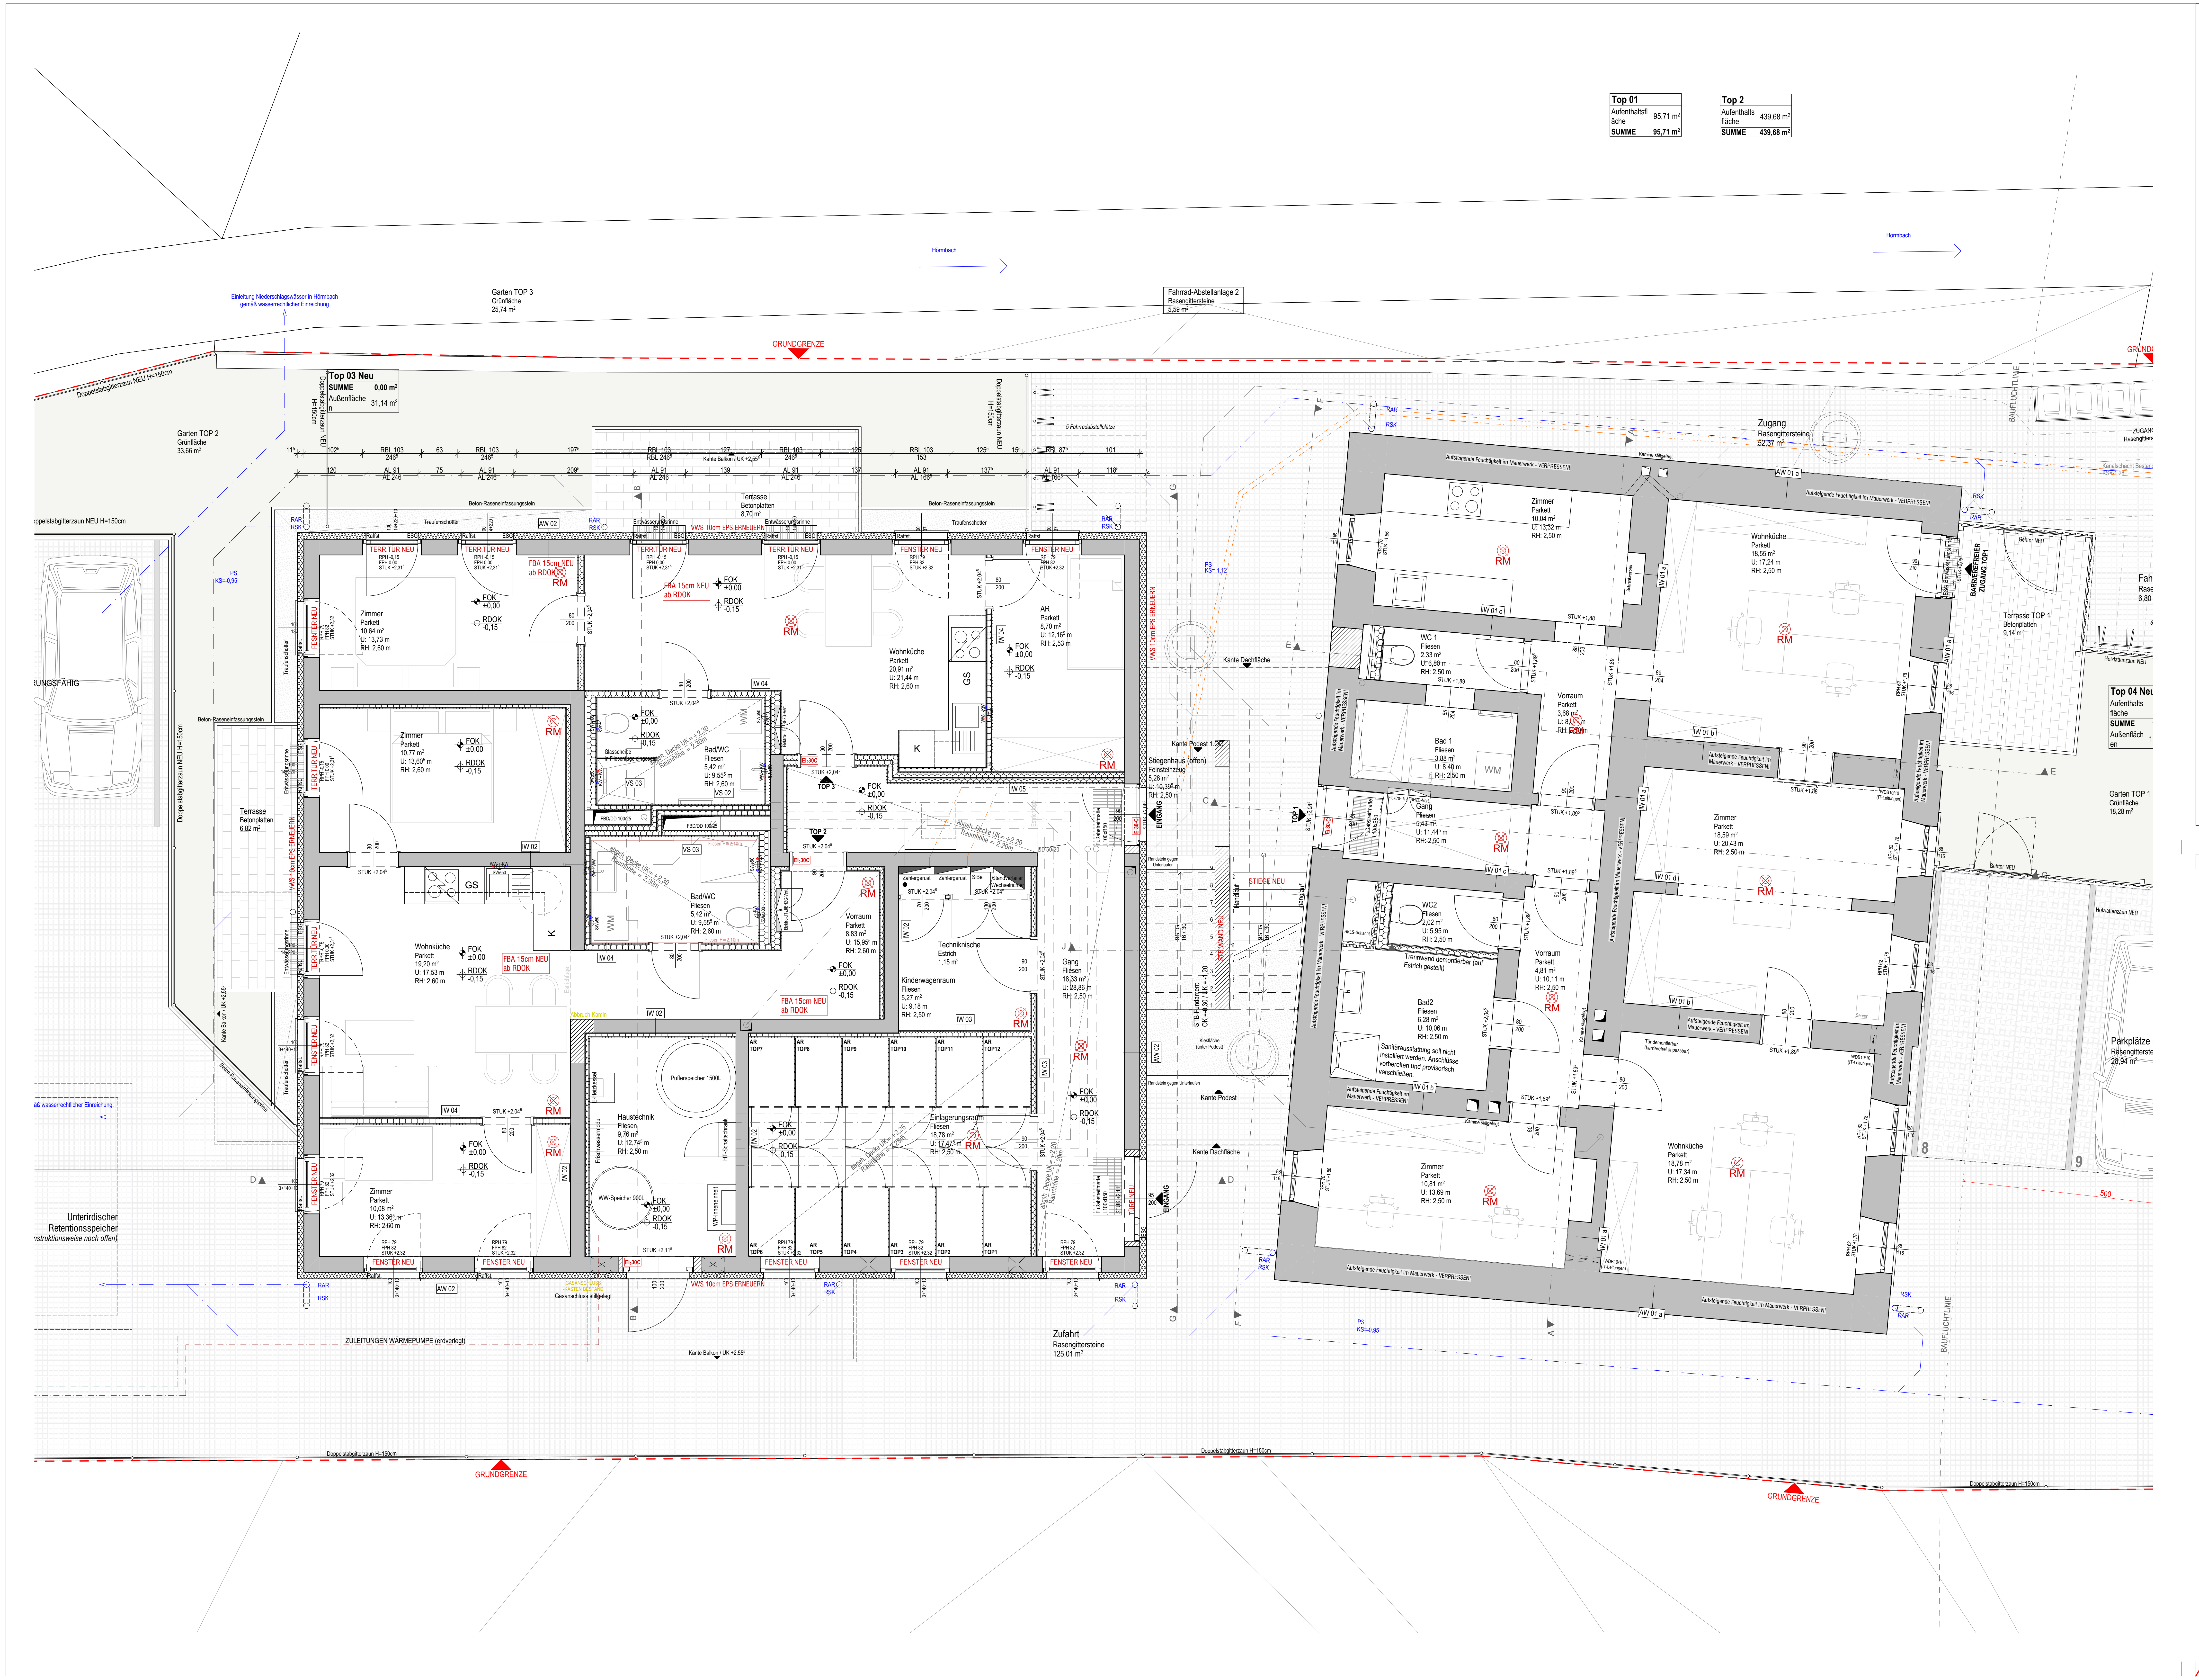
Hörnbach
Einleitung Niederschlagswässer in Hörnbach gemäß wasserrechtlicher Einreichung
Garten TOP 3 Grünfläche 25,74 m²
Fahrrad-Abstellanlage 2 Rasengittersteine 5,59 m²
GRUNDGRENZE
Doppelstabgitterzaun NEU H=150cm
Garten TOP 2 Grünfläche 33,66 m²
Terrasse Betonplatten 8,70 m²
Terrasse Betonplatten 6,82 m²
Zimmer Parkett 10,64 m² U: 13,73 m RH: 2,60 m
Wohnküche Parkett 20,91 m² U: 21,44 m RH: 2,60 m
AR Parkett 8,70 m² U: 12,16 m RH: 2,53 m
Zimmer Parkett 10,77 m² U: 13,60 m RH: 2,60 m
Bad/WC Fliesen 5,42 m² U: 9,55 m RH: 2,60 m
Wohnküche Parkett 19,20 m² U: 17,53 m RH: 2,60 m
Vorraum Parkett 8,83 m² U: 15,95 m RH: 2,60 m
Techniknische Estrich 1,15 m²
Kinderwagenraum Fliesen 5,27 m² U: 9,18 m RH: 2,50 m
Gang Fliesen 18,33 m² U: 28,86 m RH: 2,50 m
Haustechnik Fliesen 9,76 m² U: 12,74 m RH: 2,50 m
Einlagerungsraum Fliesen 18,78 m² U: 17,47 m RH: 2,50 m
Pufferspeicher 1500L
WW-Speicher 900L
Zimmer Parkett 10,08 m² U: 13,36 m RH: 2,60 m
Stiegenhaus (offen) Feinsteinzeug 5,28 m² U: 10,30 m RH: 2,50 m
STIEGE NEU
EINGANG
Zugang Rasengittersteine 52,37 m²
Zimmer Parkett 10,04 m² U: 13,32 m RH: 2,50 m
Wohnküche Parkett 18,55 m² U: 17,24 m RH: 2,50 m
WC 1 Fliesen 2,33 m² U: 6,80 m RH: 2,50 m
Vorraum Parkett 3,68 m²
Bad 1 Fliesen 3,88 m² U: 8,40 m RH: 2,50 m
Gang Fliesen 5,43 m² U: 11,44 m RH: 2,50 m
Gang Parkett 18,59 m² U: 20,43 m RH: 2,50 m
WC2 Fliesen 2,02 m² U: 5,95 m RH: 2,50 m
Vorraum Parkett 4,81 m² U: 10,11 m RH: 2,50 m
Bad2 Fliesen 6,28 m² U: 10,06 m RH: 2,50 m
Trennwand demontierbar (auf Estrich gestellt)
Sanitärausstattung soll nicht installiert werden. Anschlüsse vorbereiten und provisorisch verschließen.
Zimmer Parkett 10,81 m² U: 13,69 m RH: 2,50 m
Wohnküche Parkett 18,78 m² U: 17,34 m RH: 2,50 m
Aufsteigende Feuchtigkeit im Mauerwerk - VERPRESSEN!
BARRIEREFREIER ZUGANG TOP1
Terrasse TOP 1 Betonplatten 9,14 m²
Garten TOP 1 Grünfläche 18,28 m²
Parkplätze Rasengittersteine 28,94 m²
Unterirdischer Retentionsspeicher (konstruktionsweise noch offen)
Zufahrt Rasengittersteine 125,01 m²
ZULEITUNGEN WÄRMEPUMPE (erdverlegt)
Kante Balkon / UK +2,55
Kante Dachfläche
Kante Podest
BAUFLUCHTLINIE
TERR.TÜR NEU
FENSTER NEU
FBA 15cm NEU ab RDOK
WWS 10cm EPS ERNEUERN
RM
TOP 1
TOP 2
Top 03 Neu SUMME 0,00 m² Außenfläche 31,14 m²
Top 04 Neu

Top 01	
Aufenthaltsfläche	95,71 m²
SUMME	**95,71 m²**

Top 2	
Aufenthaltsfläche	439,68 m²
SUMME	**439,68 m²**

LEGENDE

☒	Wanddurchbruch
	Deckendurchbruch
	Bodenschlitz
	Bodendurchbruch
▼	OK Fertigbau
▲	UK Fertigbau
▽	OK Rohbau
△	UK Rohbau
± 0,00	Höhenangabe einer waagrechten Fläche
±0,00	Höhenangabe eines Punktes in einem Bauwerk - Fertigmaß
±0,00	Höhenangabe eines Punktes in einem Bauwerk - Rohbaumaß
BGF	Bruttogesamtfläche
HNF / NNF	Haupt- Nebennutzfläche

▨	Mauerwerk (wärmedämmend)
▨	Mauerwerk (nicht wärmedämmend)
▨	unbewehrter Beton
▨	bewehrter Beton
▦	Betonfertigteil
▤	Stein
▨	Stahl (allgemein)
▨	Holz (allgemein)
▨	Holzwerkstoffe
▩	Dämmstoff (hart)
▩	Dämmstoff (weich)
▩	Kunststoff (allgemein)
▚	Dichtstoff (allgemein)
▥	Gips (Gipskartonplatte)
▥	Gipskartonplatte Brandschutz
☐	Erdmaterial (allgemein)
⬛	Bestand
🟨	Abbruch
🟥	Neubau

—	Medien
—	Fernwärme
—	Gas
—	Strom
—	Heizung
—	Regenwasser
—	Schmutzwasser
—	Wasser
—	Blech
- - -	Abdichtung
- - -	Folie
- - -	Dampfsperre, -bremse

Höhenbezugs- und Maßangaben

DOK	Deckenoberkante
DOS	Deckenoberseite
DUK	Deckenunterkante
DUS	Deckenunterseite
DUF	Deckenunterkante (fertige Untersicht)
FBOK	Fußbodenoberkante
OFF	Oberfläche des fertigen Fußbodens
FDOK	Fundamentoberkante
FDOS	Fundamentoberseite
FDUK	Fundamentunterkante
FDUS	Fundamentunterseite
RH	lichte Raumhöhe
GH	Geschoßhöhe
OK	Oberkante
OS	Oberseite
UK	Unterkante
US	Unterseite
STUK	Sturzunterkante (Rohbaumaß)
STH	Sturzhöhe gemessen von STUK bis DUK (Rohbaumaß)
RPH	Rohbauparapethöhe
FPH	fertige Parapethöhe (FBOK bis OK Fensterbank Innen)

Rauch-, Abgas- und Luftfänge, Schächte

L	Lüftungsschacht
PT	Putztürchen
PS	Putzstück
KT	Kehrtürchen
ABL	Abluft
ZUL	Zuluft
DBA	Druckbelüftungsanlage
DES	Druckentlastungsschacht
BÖ	Belüftungsöffnung
ÜÖ	Überströmöffnung
AÖ	Abströmöffnung mit Überdruckentlastungsorgan
BSK	Brandsschutzklappe
FBHV	Fussbodenheizungsverteiler
E-Verteiler	Elektroverteiler

Öffnungen und deren Abschlüsse

WD	Wanddurchbruch
DD	Deckendurchbruch
FBD	Fußbodendurchbruch
FDD	Fundamentdurchbruch
WS	Wandschlitz
WA	Wandaussparung
DA	Deckenaussparung
FBA	Fußbodenaussparung
RBL	Rohbaulichte
AL	Architekturlichte
STL	Stocklichte
GL	Glaslichte
STAM	Stockaußenmaß
DL	Durchgangslichte
GGT	Ganzglastüre
MGT	Metallgittertür
HT	Hebetüre
HST	Hebeschiebetüre
T	Türe
AT	Allgemeintüre
ET	Eingangstüre
WET	Wohnungseingangstür
IT	Innentür
DF	Drehflügel
DKF	Drehkippflügel
SF	Schiebe-Fenster
SWF	Schwingflügel
WF	Wendeflügel
K	Kippfenster
OL	Oberlichte
DF	Dachfächenfenster
PFR	Pfostenriegelkonstruktion
FE	Fenster
FT	Fenstertüre
R	Rechtsöffnend
L	Linksöffnend
FIX	Fixverglasung
VSG	Verbund-Sicherheitsglas
ESG	Einscheiben-Sicherheitsglas

Drehflügel
Drehkippflügel
Kippflügel
Fenstertüre

EI2 30-C-, EI2 60-C-und EI2 90-C
Feuerschutztüren mit Angabe der Feuerwiderstandsklasse
(gemäß ÖNORM B 3850 und ÖNORM B 3807)

GT	gasdichte Türe
DT	Drucktüre
S 200	Rauchabschluss
S 200	Rauchabschluss
C	Selbstschließend
FLS	Freilaufschließer
LVfTÖ	Lehrverrohrung für Türöffner
elTÖ	elektrischer Türöffner

AUSFÜHRUNG

POLIERPLAN

Bauvorhaben
WNEU30

2540 Bad Vöslau, Wiener Neustädter Straße 30

XXX

Katastralgemeinde 04035 Vöslau
EZ: 719
GstNr.: 748

Diese Zeichnung bzw. Ausarbeitung sowie deren Daten auf Datenträgern sind geistiges Eigentum des Erstellers Arch. Artmüller Georg. Jede Benützung, Veröffentlichung,Vervielfältigung jeglicher Art oder Weitergabe an Dritte bedarf der schriftlichen Zustimmung durch Architekt Artmüller.

Durch die Übernahme dieses Planes akzeptiert die ausführende Firma bzw. Person die darauf dargestellten Anordnungen. Geschriebene Planmaße auf dieser Zeichnunghaben Vorrang gegenüber gezeichneten Dimensionen. Der Auftragnehmer verpflichtet sich **vor** Arbeitsbeginn alle Maße und Bedingungen im Zusammenhang mit seinerArbeit auf der Baustelle verantwortlich zu überprüfen.

Abweichungen gegenüber dargestellten oder schriftlich vereinbarten Anordnungen müssen Architekt Artmüller und der Bauleitung unverzüglich schriftlich mitgeteiltwerden. Vor Arbeitsbeginn sind dem Architekten gültige Werkzeichnungen zur Genehmigung vorzulegen.

NATURMASSE SIND ZU NEHMEN, KOTEN ZU PRÜFEN

Index	Datum	Bearbeiter	Änderung

Index	Änderung	Datum

VORABZUG
22. 10. 2026

Grundeigentümer

Bauwerber / Auftraggeber

ARTMÜLLER ARCHITEKTEN
ZIVILTECHNIKER GMBH
Stolberggasse 34|26 A-1050 Wien
t [+43] 01 . 581 40 83 f [+43] 01. 581 40 83 99 office@artmueller.eu

Planinhalt
Erdgeschoss

Maßstab	Gez	Datum	Plannr.	Index
1:50	ML	22-10-2026	WNEU30_50_01	VORABZUG

Erstellt, am 11.11.2026

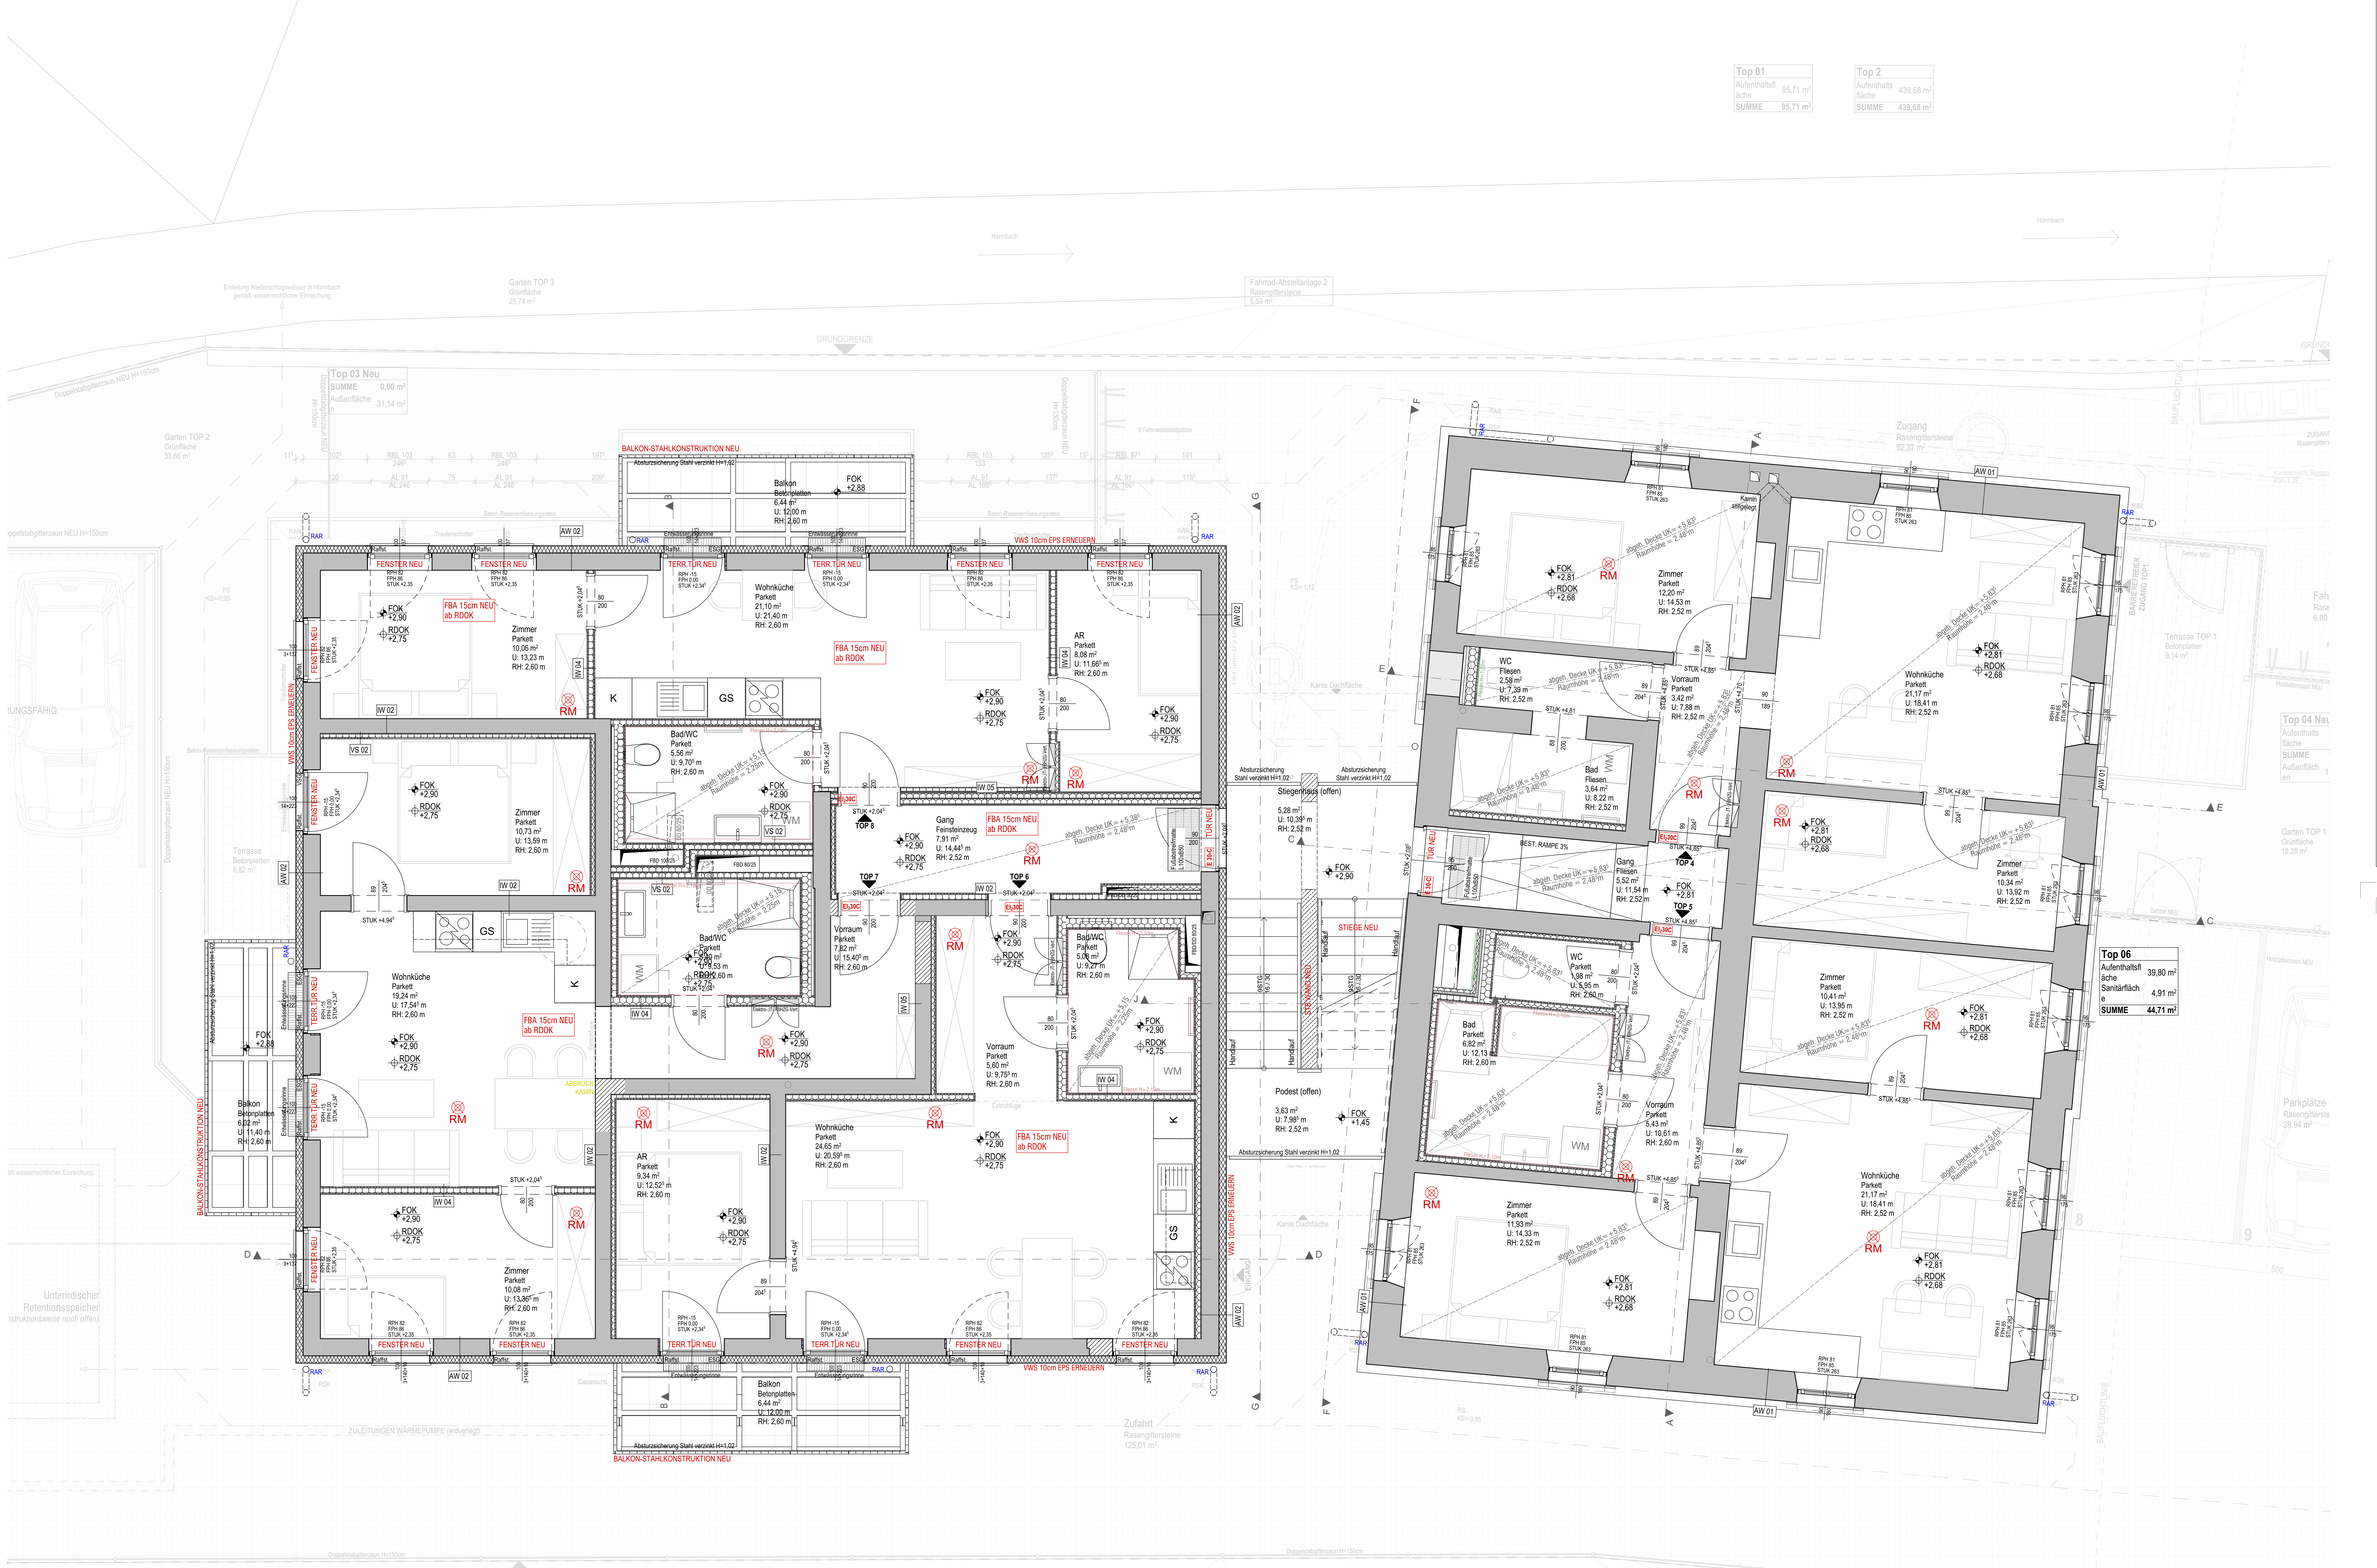
Top 01
Top 2
Top 03 Neu
Top 04 Neu
Garten TOP 2
Garten TOP 3
Fahrrad-Abstellanlage 2
GRUNDGRENZE
BALKON-STAHLKONSTRUKTION NEU
Absturzsicherung Stahl verzinkt H=1,02
Balkon
Betonplatten
6,44 m²
U: 12,00 m
RH: 2,60 m
FOK +2,88
FENSTER NEU
TERR.TÜR NEU
VWS 10cm EPS ERNEUERN
Zimmer
Parkett
10,06 m²
U: 13,23 m
RH: 2,60 m
FBA 15cm NEU ab RDOK
Wohnküche
Parkett
21,10 m²
U: 21,40 m
RH: 2,60 m
AR
Parkett
8,08 m²
U: 11,66⁵ m
RH: 2,60 m
Zimmer
Parkett
10,73 m²
U: 13,59 m
RH: 2,60 m
Bad/WC
Parkett
5,56 m²
U: 9,70⁵ m
RH: 2,60 m
Gang
Feinsteinzeug
7,91 m²
U: 14,44⁵ m
RH: 2,52 m
TOP 8
TOP 7
TOP 6
Wohnküche
Parkett
19,24 m²
U: 17,54⁵ m
RH: 2,60 m
Bad/WC
Vorraum
Parkett
7,82 m²
U: 15,40⁵ m
RH: 2,60 m
Bad/WC
Parkett
5,08 m²
U: 9,27 m
RH: 2,60 m
Vorraum
Parkett
5,60 m²
U: 9,75⁵ m
RH: 2,60 m
Balkon
Betonplatten
6,02 m²
U: 11,40 m
RH: 2,60 m
Terrasse
Betonplatten
6,82 m²
ABBRUCH KAMIN
AR
Parkett
9,34 m²
U: 12,52⁵ m
RH: 2,60 m
Wohnküche
Parkett
24,65 m²
U: 20,59⁵ m
RH: 2,60 m
Zimmer
Parkett
10,08 m²
U: 13,36⁵ m
RH: 2,60 m
Balkon
Betonplatten
6,44 m²
U: 12,00 m
RH: 2,60 m
ZULEITUNGEN WÄRMEPUMPE (erdverlegt)
Zufahrt
Rasengittersteine
125,01 m²
Stiegenhaus (offen)
STIEGE NEU
Podest (offen)
Zugang
Rasengittersteine
52,37 m²
Zimmer
Parkett
12,20 m²
U: 14,53 m
RH: 2,52 m
Kamin stillgelegt
WC
Fliesen
2,58 m²
U: 7,39 m
RH: 2,52 m
Vorraum
Parkett
3,42 m²
U: 7,88 m
RH: 2,52 m
Wohnküche
Parkett
21,17 m²
U: 18,41 m
RH: 2,52 m
Bad
Fliesen
3,64 m²
U: 8,22 m
RH: 2,52 m
Gang
Fliesen
5,52 m²
U: 11,54 m
RH: 2,52 m
BEST. RAMPE 3%
TOP 4
TOP 5
Zimmer
Parkett
10,34 m²
U: 13,92 m
RH: 2,52 m
WC
Parkett
1,98 m²
U: 5,95 m
RH: 2,60 m
Bad
Parkett
6,82 m²
U: 12,13 m
RH: 2,60 m
Vorraum
Parkett
5,43 m²
U: 10,61 m
RH: 2,60 m
Zimmer
Parkett
10,41 m²
U: 13,95 m
RH: 2,52 m
Zimmer
Parkett
11,93 m²
U: 14,33 m
RH: 2,52 m
Wohnküche
Parkett
21,17 m²
U: 18,41 m
RH: 2,52 m
Terrasse TOP 1
Betonplatten
9,14 m²
BARRIEREFREIER ZUGANG TOP1
Top 06
Aufenthaltsfläche 39,80 m²
Sanitärfläche 4,91 m²
SUMME 44,71 m²
Parkplätze
Rasengittersteine
BAUFLUCHTLINIE

LEGENDE

⊠	Wanddurchbruch
	Deckendurchbruch
	Bodenschlitz
	Bodendurchbruch
▼	OK Fertigbau
▲	UK Fertigbau
▽	OK Rohbau
△	UK Rohbau
± 0,00	Höhenangabe einer waagrechten Fläche
±0,00	Höhenangabe eines Punktes in einem Bauwerk - Fertigmaß
±0,00	Höhenangabe eines Punktes in einem Bauwerk - Rohbaumaß
BGF	Bruttogesamtfläche
HNF / NNF	Haupt- Nebennutzfläche

▨	Mauerwerk (wärmedämmend)
▨	Mauerwerk (nicht wärmedämmend)
▨	unbewehrter Beton
▨	bewehrter Beton
▦	Betonfertigteil
▤	Stein
▨	Stahl (allgemein)
▨	Holz (allgemein)
▨	Holzwerkstoffe
▩	Dämmstoff (hart)
▩	Dämmstoff (weich)
▩	Kunststoff (allgemein)
▚	Dichtstoff (allgemein)
▥	Gips (Gipskartonplatte)
▥	Gipskartonplatte Brandschutz
☐	Erdmaterial (allgemein)
⬜	Bestand
🟨	Abbruch
🟥	Neubau

—	Medien
—	Fernwärme
—	Gas
—	Strom
—	Heizung
—	Regenwasser
—	Schmutzwasser
—	Wasser
—	Blech
- - -	Abdichtung
- - -	Folie
– – –	Dampfsperre, -bremse

Höhenbezugs- und Maßangaben

DOK	Deckenoberkante
DOS	Deckenoberseite
DUK	Deckenunterkante
DUS	Deckenunterseite
DUF	Deckenunterkante (fertige Untersicht)
FBOK	Fußbodenoberkante
OFF	Oberfläche des fertigen Fußbodens
FDOK	Fundamentoberkante
FDOS	Fundamentoberseite
FDUK	Fundamentunterkante
FDUS	Fundamentunterseite
RH	lichte Raumhöhe
GH	Geschoßhöhe
OK	Oberkante
OS	Oberseite
UK	Unterkante
US	Unterseite
STUK	Sturzunterkante (Rohbaumaß)
STH	Sturzhöhe gemessen von STUK bis DUK (Rohbaumaß)
RPH	Rohbauparapethöhe
FPH	fertige Parapethöhe (FBOK bis OK Fensterbank Innen)

Rauch-, Abgas- und Luftfänge, Schächte

L	Lüftungsschacht
PT	Putztürchen
PS	Putzstück
KT	Kehrtürchen
ABL	Abluft
ZUL	Zuluft
DBA	Druckbelüftungsanlage
DES	Druckentlastungsschacht
BÖ	Belüftungsöffnung
ÜÖ	Überströmöffnung
AÖ	Abströmöffnung mit Überdruckentlastungsorgan
BSK	Brandsschutzklappe
FBHV	Fussbodenheizungsverteiler
E-Verteiler	Elektroverteiler

Öffnungen und deren Abschlüsse

WD	Wanddurchbruch
DD	Deckendurchbruch
FBD	Fußbodendurchbruch
FDD	Fundamentdurchbruch
WS	Wandschlitz
WA	Wandaussparung
DA	Deckenaussparung
FBA	Fußbodenaussparung
RBL	Rohbaulichte
AL	Architekturlichte
STL	Stocklichte
GL	Glaslichte
STAM	Stockaußenmaß
DL	Durchgangslichte
GGT	Ganzglastüre
MGT	Metallgittertür
HT	Hebetüre
HST	Hebeschiebetüre
T	Türe
AT	Allgemeintüre
ET	Eingangstüre
WET	Wohnungseingangstür
IT	Innentür
DF	Drehflügel
DKF	Drehkippflügel
SF	Schiebe-Fenster
SWF	Schwingflügel
WF	Wendeflügel
K	Kippfenster
OL	Oberlichte
DF	Dachfächenfenster
PFR	Pfostenriegelkonstruktion
FE	Fenster
FT	Fenstertüre
R	Rechtsöffnend
L	Linksöffnend
FIX	Fixverglasung
VSG	Verbund-Sicherheitsglas
ESG	Einscheiben-Sicherheitsglas

Drehflügel
Drehkippflügel
Kippflügel
Fenstertüre

EI2 30-C-, EI2 60-C-und EI2 90-C
Feuerschutztüren mit Angabe der Feuerwiderstandsklasse
(gemäß ÖNORM B 3850 und ÖNORM B 3807)

GT	gasdichte Türe
DT	Drucktüre
S 200	Rauchabschluss
S 200	Rauchabschluss
C	Selbstschließend
FLS	Freilaufschließer
LVfTÖ	Lehrverrohrung für Türöffner
elTÖ	elektrischer Türöffner

AUSFÜHRUNG

POLIERPLAN

Bauvorhaben
WNEU30
2540 Bad Vöslau, Wiener Neustädter Straße 30

XXX

Katastralgemeinde 04035 Vöslau
EZ: 719
GstNr.: 748

Diese Zeichnung bzw. Ausarbeitung sowie deren Daten auf Datenträgern sind geistiges Eigentum des Erstellers Arch. Artmüller Georg. Jede Benützung, Veröffentlichung,Vervielfältigung jeglicher Art oder Weitergabe an Dritte bedarf der schriftlichen Zustimmung durch Architekt Artmüller.

Durch die Übernahme dieses Planes akzeptiert die ausführende Firma bzw. Person die darauf dargestellten Anordnungen. Geschriebene Planmaße auf dieser Zeichnunghaben Vorrang gegenüber gezeichneten Dimensionen. Der Auftragnehmer verpflichtet sich **vor** Arbeitsbeginn alle Maße und Bedingungen im Zusammenhang mit seinerArbeit auf der Baustelle verantwortlich zu überprüfen.

Abweichungen gegenüber dargestellten oder schriftlich vereinbarten Anordnungen müssen Architekt Artmüller und der Bauleitung unverzüglich schriftlich mitgeteiltwerden. Vor Arbeitsbeginn sind dem Architekten gültige Werkzeichnungen zur Genehmigung vorzulegen.

NATURMASSE SIND ZU NEHMEN, KOTEN ZU PRÜFEN

Index	Datum	Bearbeiter	Änderung

Index	Änderung	Datum

VORABZUG
22.10.2026

Grundeigentümer

Bauwerber / Auftraggeber

ARTMÜLLER ARCHITEKTEN
ZIVILTECHNIKER GMBH
Stolberggasse 34|26 A-1050 Wien
t [+43] 01 . 581 40 83 f [+43] 01. 581 40 83 99 office@artmueller.eu

Planinhalt
1. Obergeschoß

Maßstab	Gez	Datum	Plannr.	Index
1:50	ML	22-10-2026	WNEU30_50_02	VORABZUG

Erstellt, am 11.11.2026

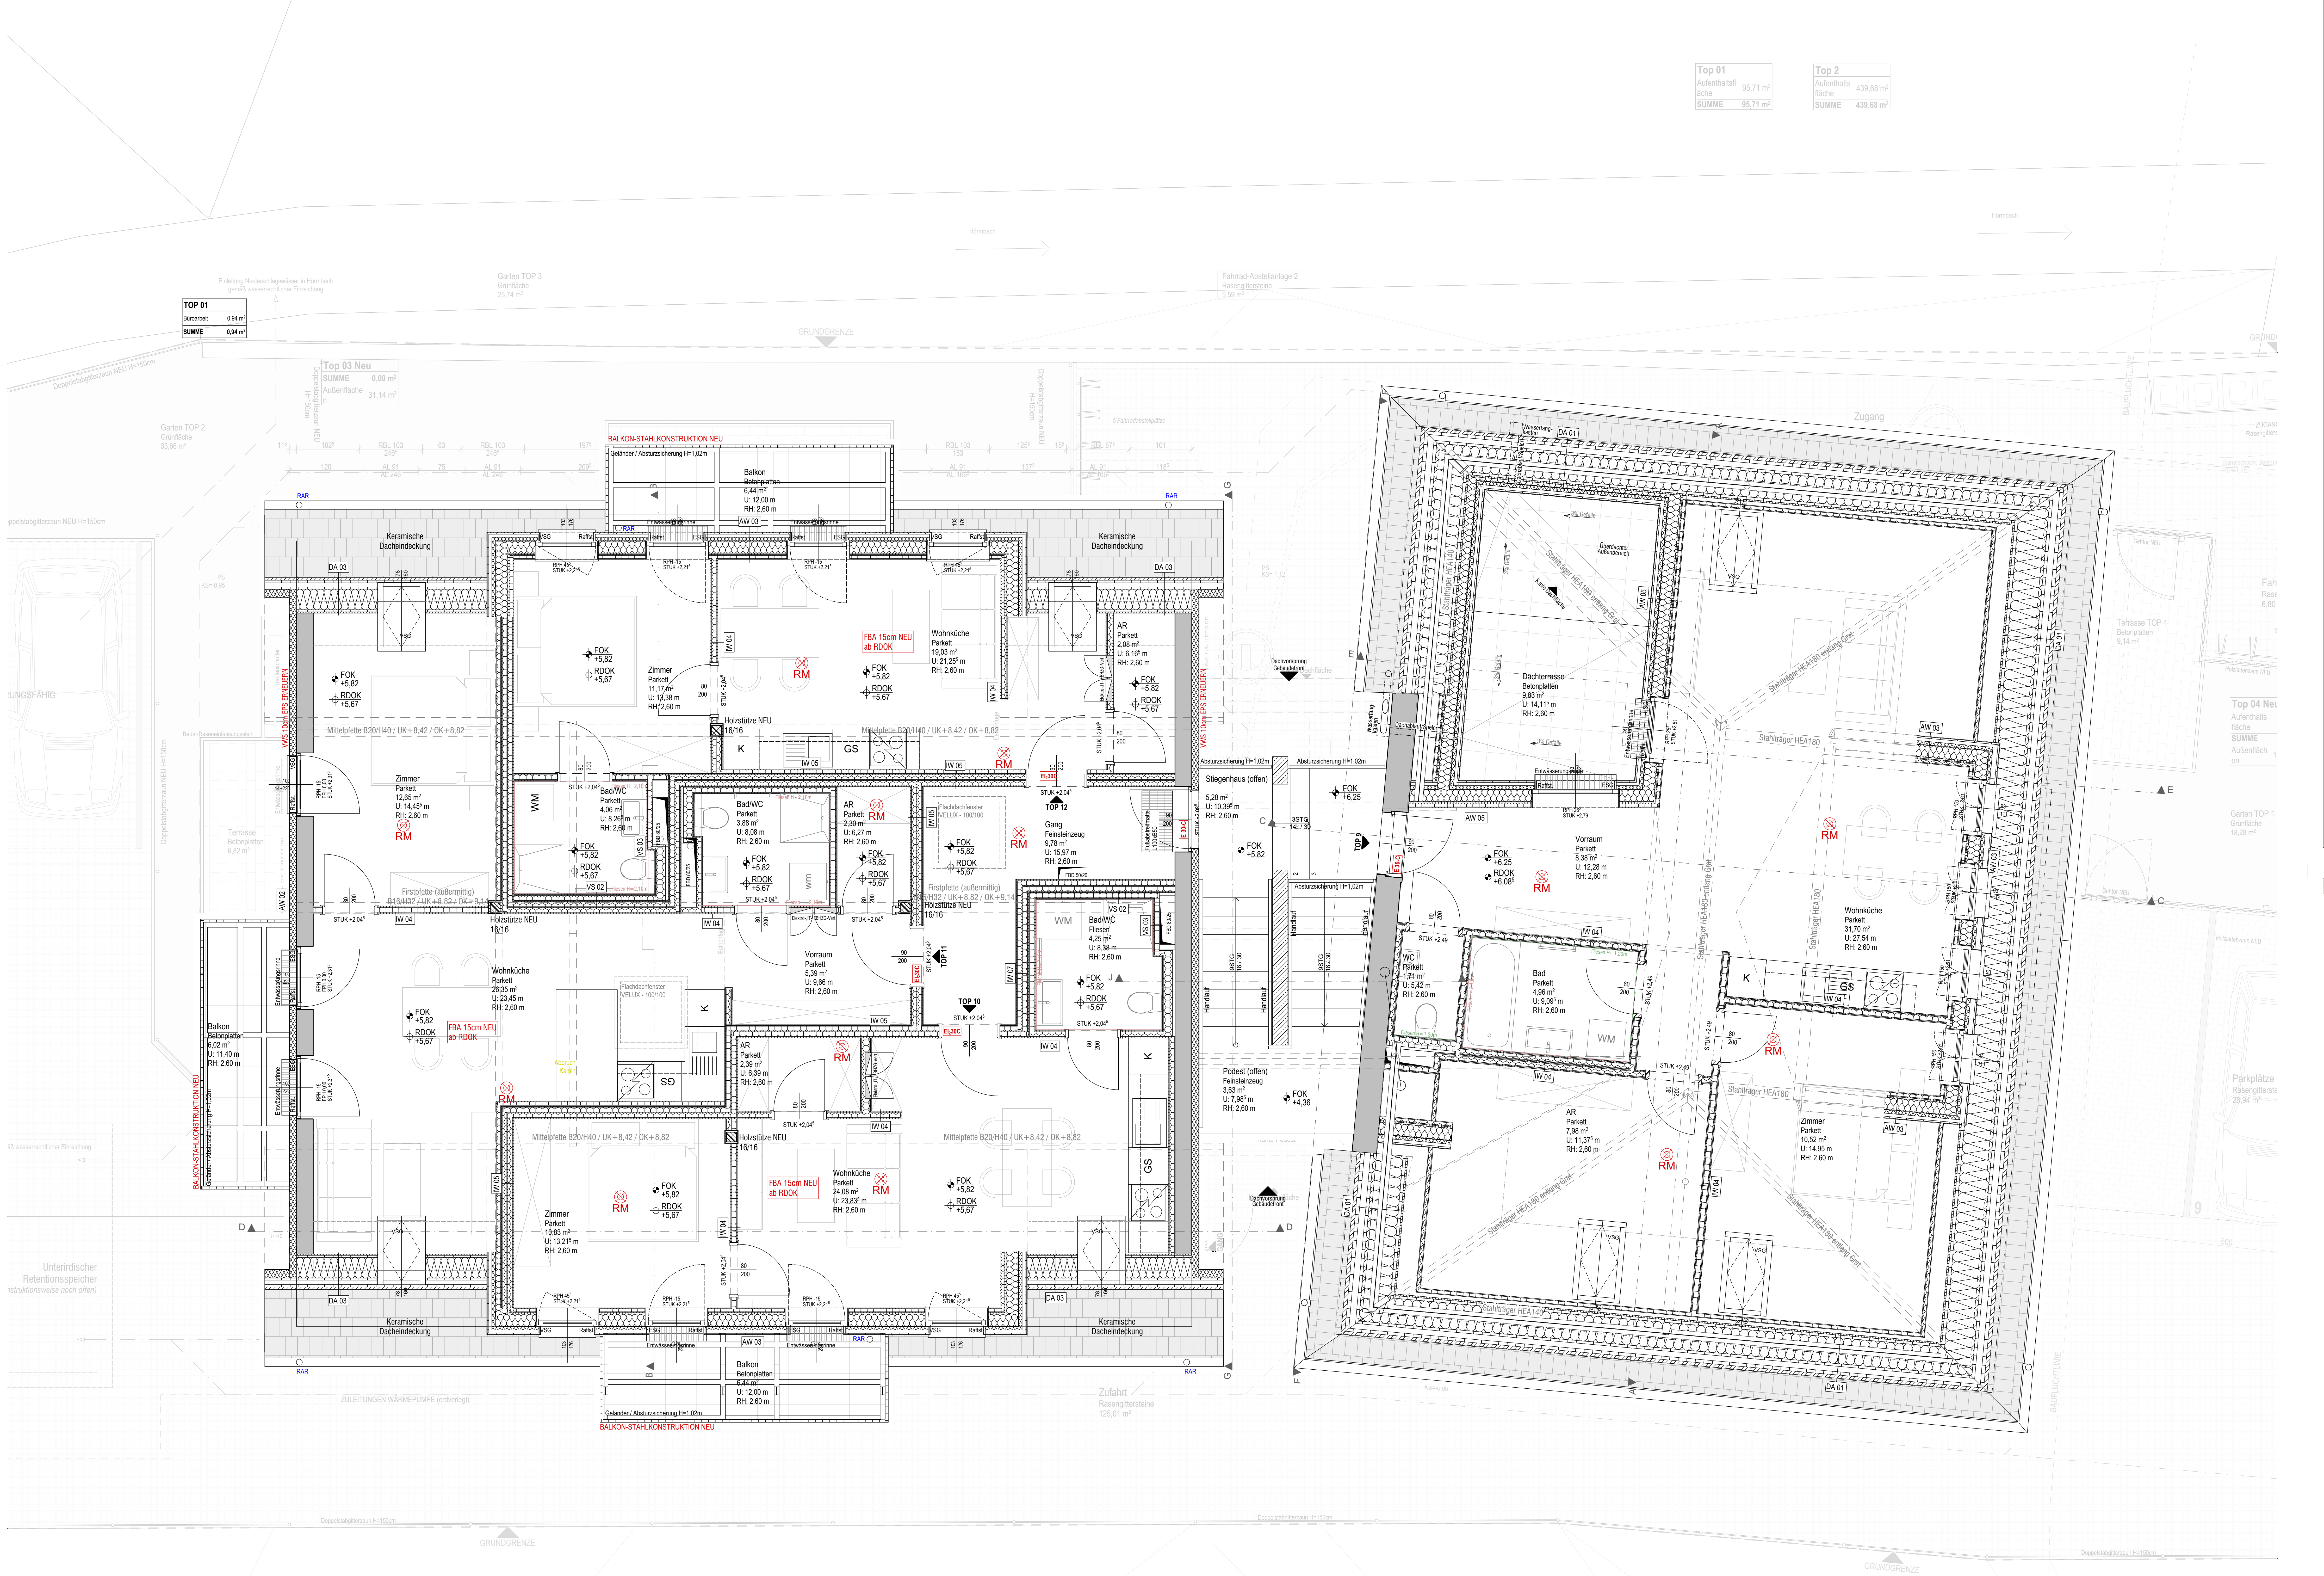
TOP 01
Büroarbeit 0,94 m²
SUMME 0,94 m²
Top 03 Neu
SUMME 0,00 m²
Außenfläche 31,14 m²
Top 01
SUMME 95,71 m²
Top 2
SUMME 439,69 m²
Garten TOP 2
Garten TOP 3
Fahrrad-Abstellanlage 2
5 Fahrradabstellplätze
GRUNDGRENZE
Zugang
BALKON-STAHLKONSTRUKTION NEU
Geländer / Absturzsicherung H=1,02m
Balkon
Betonplatten
6,44 m²
U: 12,00 m
RH: 2,60 m
Keramische Dacheindeckung
DA 03
RAR
Zimmer
Parkett
12,65 m²
U: 14,45⁵ m
RH: 2,60 m
Zimmer
Parkett
11,17 m²
U: 13,38 m
RH: 2,60 m
Wohnküche
Parkett
19,03 m²
U: 21,25⁵ m
RH: 2,60 m
FBA 15cm NEU ab RDOK
AR
Parkett
2,08 m²
U: 6,16⁵ m
RH: 2,60 m
FOK +5,82
RDOK +5,67
RM
VWS 10cm EPS ERNEUERN
Mittelpfette B20/H40 / UK+8,42 / OK+8,82
Firstpfette (außermittig) B16/H32 / UK+8,82 / OK+9,14
Holzstütze NEU 16/16
Bad/WC
Parkett
4,06 m²
U: 8,26⁵ m
RH: 2,60 m
Bad/WC
Parkett
3,88 m²
U: 8,08 m
RH: 2,60 m
AR
Parkett
2,30 m²
U: 6,27 m
RH: 2,60 m
Flachdachfenster VELUX - 100/100
Gang
Feinsteinzeug
9,78 m²
U: 15,97 m
RH: 2,60 m
TOP 12
TOP 11
TOP 10
TOP 9
Stiegenhaus (offen)
5,28 m²
U: 10,39⁵ m
RH: 2,60 m
Absturzsicherung H=1,02m
Terrasse
Betonplatten
6,82 m²
Balkon
Betonplatten
6,02 m²
U: 11,40 m
RH: 2,60 m
BALKON-STAHLKONSTRUKTION NEU
Wohnküche
Parkett
26,35 m²
U: 23,45 m
RH: 2,60 m
Abbruch Kamin
Vorraum
Parkett
5,39 m²
U: 9,66 m
RH: 2,60 m
Bad/WC
Fliesen
4,25 m²
U: 8,38 m
RH: 2,60 m
AR
Parkett
2,39 m²
U: 6,39 m
RH: 2,60 m
Zimmer
Parkett
10,83 m²
U: 13,21⁵ m
RH: 2,60 m
Wohnküche
Parkett
24,08 m²
U: 23,83⁵ m
RH: 2,60 m
Podest (offen)
Feinsteinzeug
3,63 m²
U: 7,98⁵ m
RH: 2,60 m
FOK +4,36
Dachvorsprung Gebäudefront
ZULEITUNGEN WÄRMEPUMPE (erdverlegt)
Zufahrt
Rasengittersteine
125,01 m²
Dachterrasse
Betonplatten
9,83 m²
U: 14,11⁵ m
RH: 2,60 m
Überdachter Außenbereich
Stahlträger HEA180 entlang Grat
Stahlträger HEA140
Stahlträger HEA180
Vorraum
Parkett
8,38 m²
U: 12,28 m
RH: 2,60 m
FOK +6,25
RDOK +6,08⁵
Wohnküche
Parkett
31,70 m²
U: 27,54 m
RH: 2,60 m
WC
Parkett
1,71 m²
U: 5,42 m
RH: 2,60 m
Bad
Parkett
4,96 m²
U: 9,09⁵ m
RH: 2,60 m
AR
Parkett
7,98 m²
U: 11,37⁵ m
RH: 2,60 m
Zimmer
Parkett
10,52 m²
U: 14,95 m
RH: 2,60 m
Terrasse TOP 1
Betonplatten
9,14 m²
BAUFLUCHTLINIE
Doppelstabgitterzaun H=150cm
Unterirdischer Retentionsspeicher

LEGENDE

☒	Wanddurchbruch
⬚	Deckendurchbruch
◺	Bodenschlitz
◢	Bodendurchbruch
▼	OK Fertigbau
▲	UK Fertigbau
▽	OK Rohbau
△	UK Rohbau
± 0,00	Höhenangabe einer waagrechten Fläche
±0,00	Höhenangabe eines Punktes in einem Bauwerk - Fertigmaß
±0,00	Höhenangabe eines Punktes in einem Bauwerk - Rohbaumaß
BGF	Bruttogesamtfläche
HNF / NNF	Haupt- Nebennutzfläche

▨	Mauerwerk (wärmedämmend)
▨	Mauerwerk (nicht wärmedämmend)
▨	unbewehrter Beton
▨	bewehrter Beton
▦	Betonfertigteil
▤	Stein
▨	Stahl (allgemein)
▨	Holz (allgemein)
▨	Holzwerkstoffe
▩	Dämmstoff (hart)
▩	Dämmstoff (weich)
▩	Kunststoff (allgemein)
▚	Dichtstoff (allgemein)
▥	Gips (Gipskartonplatte)
▥	Gipskartonplatte Brandschutz
☐	Erdmaterial (allgemein)
■	Bestand
🟨	Abbruch
🟥	Neubau

—	Medien
—	Fernwärme
—	Gas
—	Strom
—	Heizung
—	Regenwasser
—	Schmutzwasser
—	Wasser
—	Blech
- - -	Abdichtung
- - -	Folie
- - -	Dampfsperre, -bremse

Höhenbezugs- und Maßangaben

DOK	Deckenoberkante
DOS	Deckenoberseite
DUK	Deckenunterkante
DUS	Deckenunterseite
DUF	Deckenunterkante (fertige Untersicht)
FBOK	Fußbodenoberkante
OFF	Oberfläche des fertigen Fußbodens
FDOK	Fundamentoberkante
FDOS	Fundamentoberseite
FDUK	Fundamentunterkante
FDUS	Fundamentunterseite
RH	lichte Raumhöhe
GH	Geschoßhöhe
OK	Oberkante
OS	Oberseite
UK	Unterkante
US	Unterseite
STUK	Sturzunterkante (Rohbaumaß)
STH	Sturzhöhe gemessen von STUK bis DUK (Rohbaumaß)
RPH	Rohbauparapethöhe
FPH	fertige Parapethöhe (FBOK bis OK Fensterbank Innen)

Rauch-, Abgas- und Luftfänge, Schächte

L	Lüftungsschacht
PT	Putztürchen
PS	Putzstück
KT	Kehrtürchen
ABL	Abluft
ZUL	Zuluft
DBA	Druckbelüftungsanlage
DES	Druckentlastungsschacht
BÖ	Belüftungsöffnung
ÜÖ	Überströmöffnung
AÖ	Abströmöffnung mit Überdruckentlastungsorgan
BSK	Brandsschutzklappe
FBHV	Fussbodenheizungsverteiler
E-Verteiler	Elektroverteiler

Öffnungen und deren Abschlüsse

WD	Wanddurchbruch
DD	Deckendurchbruch
FBD	Fußbodendurchbruch
FDD	Fundamentdurchbruch
WS	Wandschlitz
WA	Wandaussparung
DA	Deckenaussparung
FBA	Fußbodenaussparung
RBL	Rohbaulichte
AL	Architekturlichte
STL	Stocklichte
GL	Glaslichte
STAM	Stockaußenmaß
DL	Durchgangslichte
GGT	Ganzglastüre
MGT	Metallgittertür
HT	Hebetüre
HST	Hebeschiebetüre
T	Türe
AT	Allgemeintüre
ET	Eingangstüre
WET	Wohnungseingangstür
IT	Innentür
DF	Drehflügel
DKF	Drehkippflügel
SF	Schiebe-Fenster
SWF	Schwingflügel
WF	Wendeflügel
K	Kippfenster
OL	Oberlichte
DF	Dachfächenfenster
PFR	Pfostenriegelkonstruktion
FE	Fenster
FT	Fenstertüre
R	Rechtsöffnend
L	Linksöffnend
FIX	Fixverglasung
VSG	Verbund-Sicherheitsglas
ESG	Einscheiben-Sicherheitsglas

Drehflügel
Drehkippflügel
Kippflügel
Fenstertüre

EI2 30-C-, EI2 60-C-und EI2 90-C
Feuerschutztüren mit Angabe der Feuerwiderstandsklasse
(gemäß ÖNORM B 3850 und ÖNORM B 3807)

GT	gasdichte Türe
DT	Drucktüre
S 200	Rauchabschluss
S 200	Rauchabschluss
C	Selbstschließend
FLS	Freilaufschließer
LVfTÖ	Lehrverrohrung für Türöffner
elTÖ	elektrischer Türöffner

AUSFÜHRUNG

POLIERPLAN

Bauvorhaben
WNEU30

2540 Bad Vöslau, Wiener Neustädter Straße 30

XXX

Katastralgemeinde 04035 Vöslau
EZ: 719
GstNr.: 748

Diese Zeichnung bzw. Ausarbeitung sowie deren Daten auf Datenträgern sind geistiges Eigentum des Erstellers Arch. Artmüller Georg. Jede Benützung, Veröffentlichung,Vervielfältigung jeglicher Art oder Weitergabe an Dritte bedarf der schriftlichen Zustimmung durch Architekt Artmüller.

Durch die Übernahme dieses Planes akzeptiert die ausführende Firma bzw. Person die darauf dargestellten Anordnungen. Geschriebene Planmaße auf dieser Zeichnunghaben Vorrang gegenüber gezeichneten Dimensionen. Der Auftragnehmer verpflichtet sich **vor** Arbeitsbeginn alle Maße und Bedingungen im Zusammenhang mit seinerArbeit auf der Baustelle verantwortlich zu überprüfen.

Abweichungen gegenüber dargestellten oder schriftlich vereinbarten Anordnungen müssen Architekt Artmüller und der Bauleitung unverzüglich schriftlich mitgeteiltwerden. Vor Arbeitsbeginn sind dem Architekten gültige Werkzeichnungen zur Genehmigung vorzulegen.

NATURMASSE SIND ZU NEHMEN, KOTEN ZU PRÜFEN

Index	Datum	Bearbeiter	Änderung

Index	Änderung	Datum

VORABZUG
22. 10. 2026

Grundeigentümer

Bauwerber / Auftraggeber

ARTMÜLLER ARCHITEKTEN
ZIVILTECHNIKER GMBH
Stolberggasse 34|26 A-1050 Wien
t [+43] 01 . 581 40 83 f [+43] 01. 581 40 83 99 office@artmueller.eu

Planinhalt
Dachgeschoß

Maßstab	Gez	Datum	Plannr.	Index
1:50	ML	22-10-2026	WNEU30_50_03	VORABZUG

Erstellt, am 11.11.2026

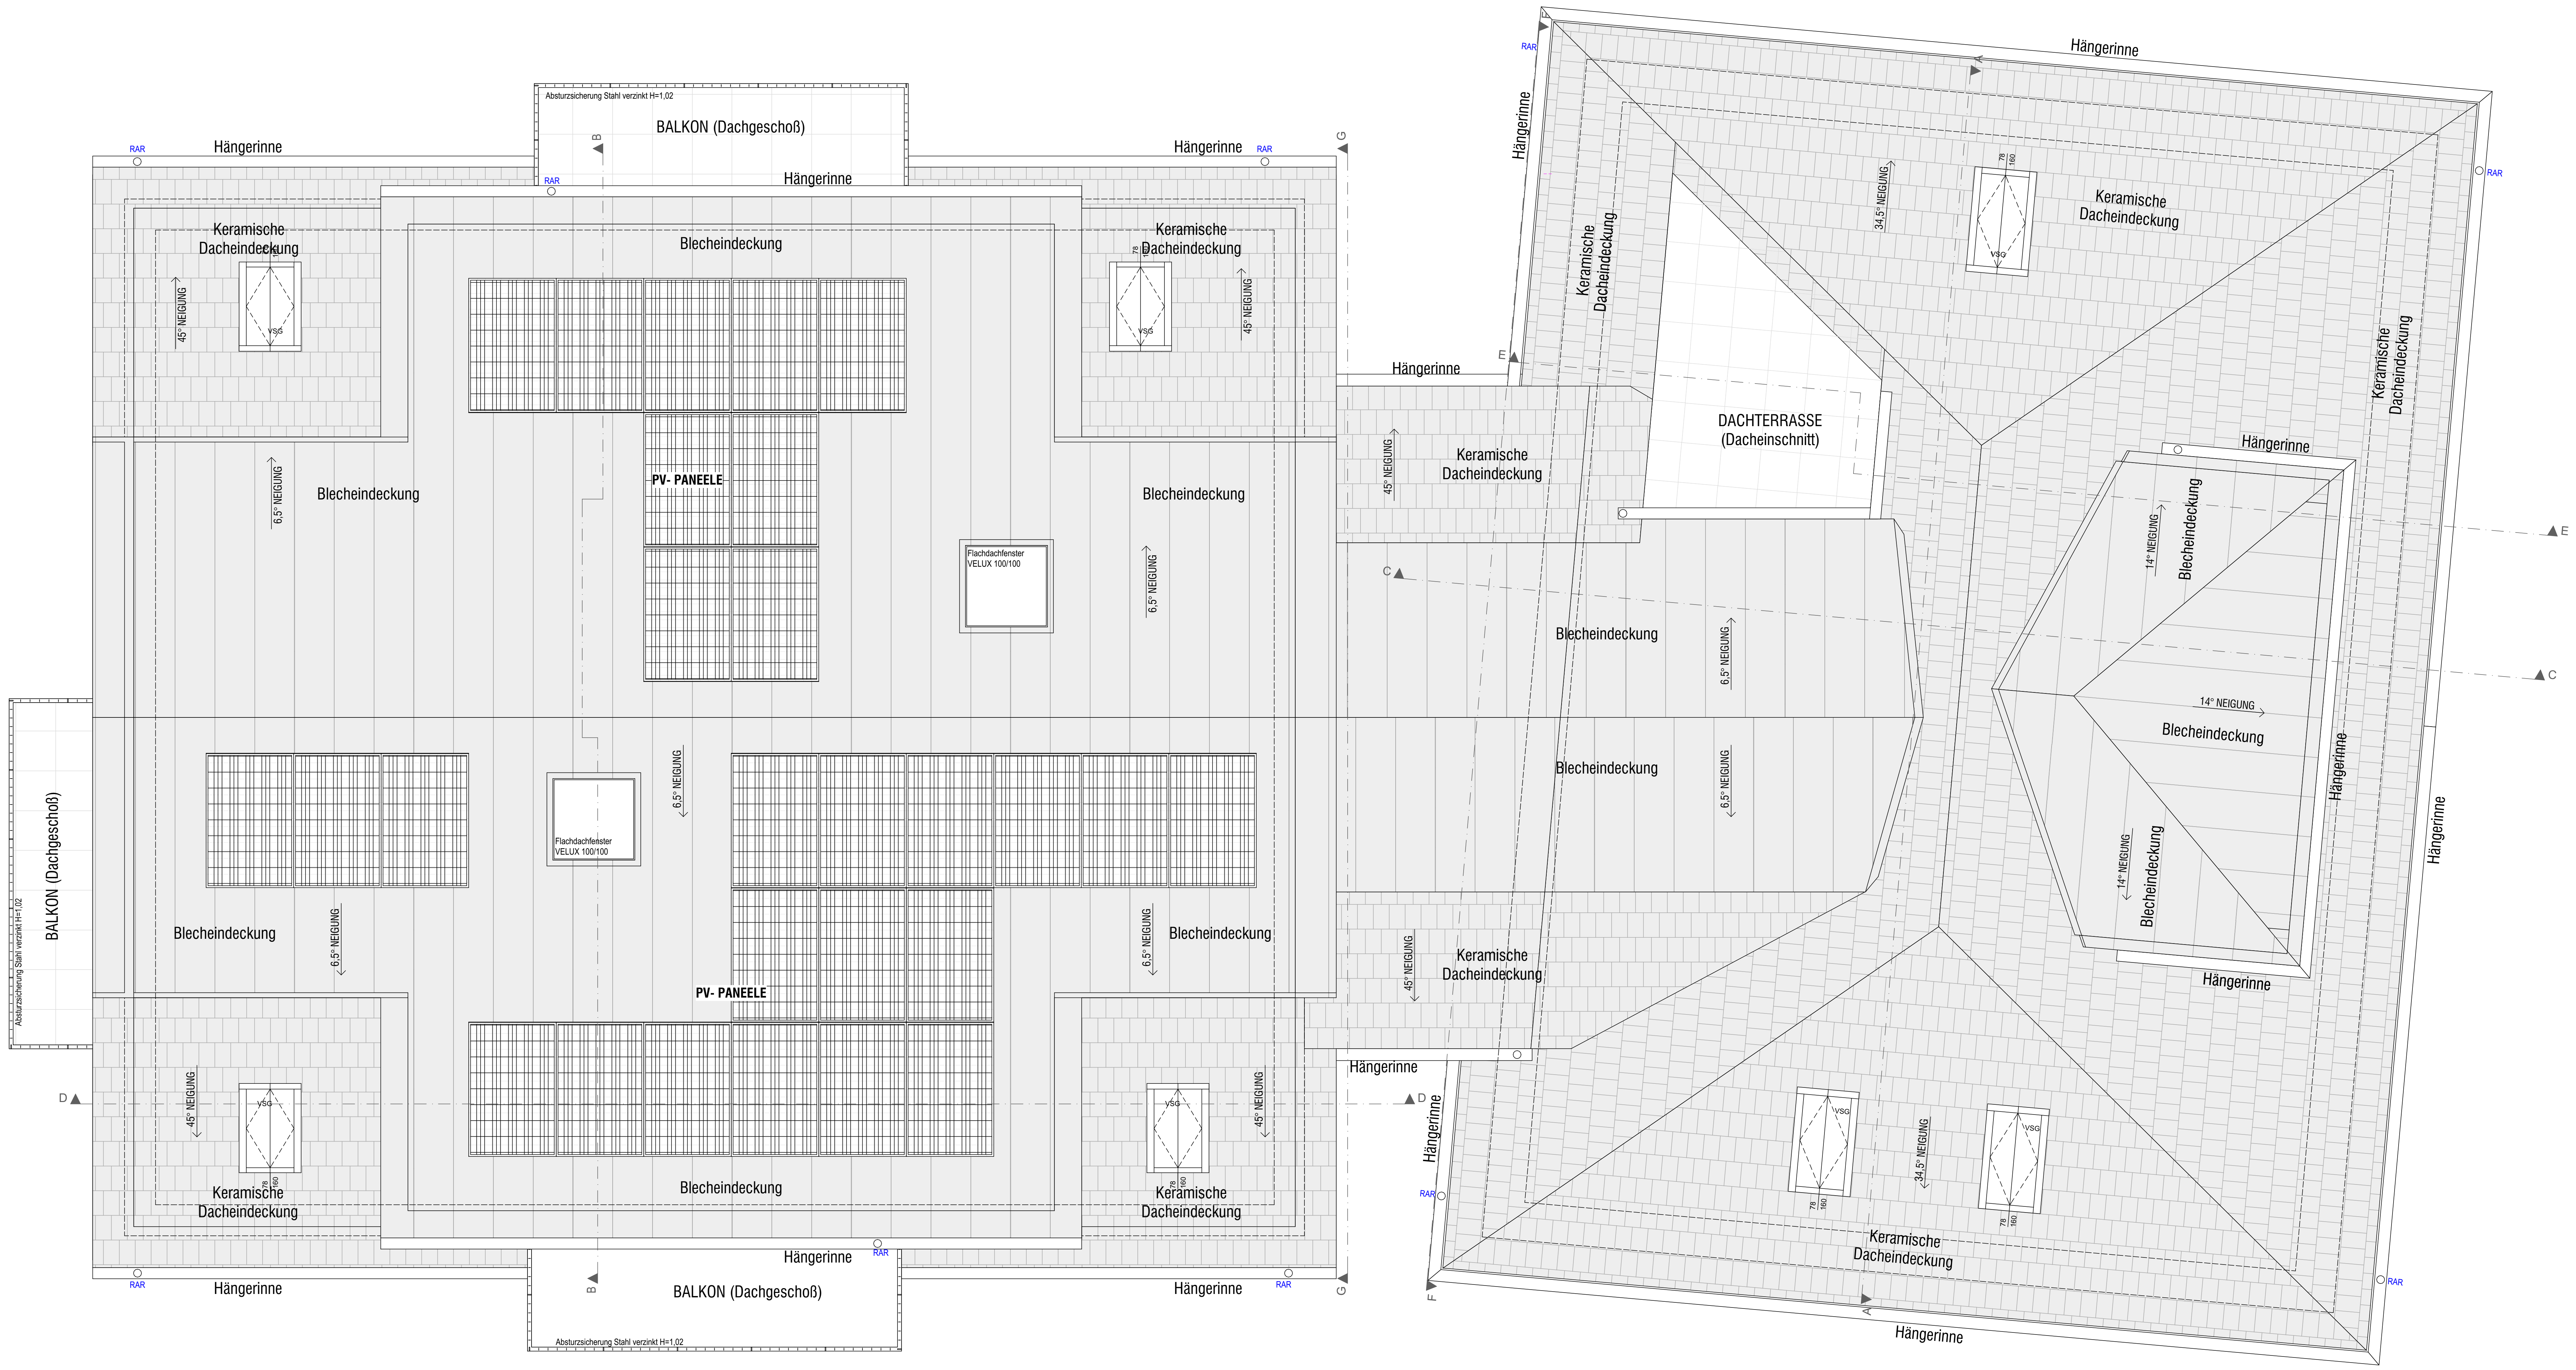
BALKON (Dachgeschoß)
Absturzsicherung Stahl verzinkt H=1,02
Hängerinne
RAR
Keramische Dacheindeckung
Blecheindeckung
PV- PANEELE
45° NEIGUNG
6,5° NEIGUNG
Flachdachfenster VELUX 100/100
VSG
BALKON (Dachgeschoß)
Absturzsicherung Stahl verzinkt H=1,02
DACHTERRASSE (Dacheinschnitt)
34,5° NEIGUNG
14° NEIGUNG
A
B
C
D
E
F
G

LEGENDE

☒	Wanddurchbruch
⬚	Deckendurchbruch
▭	Bodenschlitz
◪	Bodendurchbruch
▼	OK Fertigbau
▲	UK Fertigbau
▽	OK Rohbau
△	UK Rohbau
± 0,00	Höhenangabe einer waagrechten Fläche
±0,00	Höhenangabe eines Punktes in einem Bauwerk - Fertigmaß
±0,00	Höhenangabe eines Punktes in einem Bauwerk - Rohbaumaß

BGF	Bruttogesamtfläche
HNF / NNF	Haupt- Nebennutzfläche

▨	Mauerwerk (wärmedämmend)
▨	Mauerwerk (nicht wärmedämmend)
▨	unbewehrter Beton
▨	bewehrter Beton
▦	Betonfertigteil
▤	Stein
▨	Stahl (allgemein)
▨	Holz (allgemein)
▨	Holzwerkstoffe
▩	Dämmstoff (hart)
▩	Dämmstoff (weich)
▩	Kunststoff (allgemein)
▚	Dichtstoff (allgemein)
▥	Gips (Gipskartonplatte)
▥	Gipskartonplatte Brandschutz
□	Erdmaterial (allgemein)
■	Bestand
🟨	Abbruch
🟥	Neubau

—	Medien
—	Fernwärme
—	Gas
—	Strom
—	Heizung
—	Regenwasser
—	Schmutzwasser
—	Wasser
—	Blech
- - -	Abdichtung
- - -	Folie
– – –	Dampfsperre, -bremse

Höhenbezugs- und Maßangaben

DOK	Deckenoberkante
DOS	Deckenoberseite
DUK	Deckenunterkante
DUS	Deckenunterseite
DUF	Deckenunterkante (fertige Untersicht)
FBOK	Fußbodenoberkante
OFF	Oberfläche des fertigen Fußbodens
FDOK	Fundamentoberkante
FDOS	Fundamentoberseite
FDUK	Fundamentunterkante
FDUS	Fundamentunterseite
RH	lichte Raumhöhe
GH	Geschoßhöhe
OK	Oberkante
OS	Oberseite
UK	Unterkante
US	Unterseite
STUK	Sturzunterkante (Rohbaumaß)
STH	Sturzhöhe gemessen von STUK bis DUK (Rohbaumaß)
RPH	Rohbauparapethöhe
FPH	fertige Parapethöhe (FBOK bis OK Fensterbank Innen)

Rauch-, Abgas- und Luftfänge, Schächte

L	Lüftungsschacht
PT	Putztürchen
PS	Putzstück
KT	Kehrtürchen
ABL	Abluft
ZUL	Zuluft
DBA	Druckbelüftungsanlage
DES	Druckentlastungsschacht
BÖ	Belüftungsöffnung
ÜÖ	Überströmöffnung
AÖ	Abströmöffnung mit Überdruckentlastungsorgan
BSK	Brandsschutzklappe
FBHV	Fussbodenheizungsverteiler
E-Verteiler	Elektroverteiler

Öffnungen und deren Abschlüsse

WD	Wanddurchbruch
DD	Deckendurchbruch
FBD	Fußbodendurchbruch
FDD	Fundamentdurchbruch
WS	Wandschlitz
WA	Wandaussparung
DA	Deckenaussparung
FBA	Fußbodenaussparung
RBL	Rohbaulichte
AL	Architekturlichte
STL	Stocklichte
GL	Glaslichte
STAM	Stockaußenmaß
DL	Durchgangslichte
GGT	Ganzglastüre
MGT	Metallgittertür
HT	Hebetüre
HST	Hebeschiebetüre
T	Türe
AT	Allgemeintüre
ET	Eingangstüre
WET	Wohnungseingangstür
IT	Innentür
DF	Drehflügel
DKF	Drehkippflügel
SF	Schiebe-Fenster
SWF	Schwingflügel
WF	Wendeflügel
K	Kippfenster
OL	Oberlichte
DF	Dachfächenfenster
PFR	Pfostenriegelkonstruktion
FE	Fenster
FT	Fenstertüre
R	Rechtsöffnend
L	Linksöffnend
FIX	Fixverglasung
VSG	Verbund-Sicherheitsglas
ESG	Einscheiben-Sicherheitsglas

Drehflügel
Drehkippflügel
Kippflügel
Fenstertüre

EI2 30-C-, EI2 60-C-und EI2 90-C
Feuerschutztüren mit Angabe der Feuerwiderstandsklasse
(gemäß ÖNORM B 3850 und ÖNORM B 3807)

GT	gasdichte Türe
DT	Drucktüre
S 200	Rauchabschluss
S 200	Rauchabschluss
C	Selbstschließend
FLS	Freilaufschließer
LVfTÖ	Lehrverrohrung für Türöffner
elTÖ	elektrischer Türöffner

AUSFÜHRUNG

POLIERPLAN

Bauvorhaben
WNEU30

2540 Bad Vöslau, Wiener Neustädter Straße 30

XXX

Katastralgemeinde 04035 Vöslau
EZ: 719
GstNr.: 748

Diese Zeichnung bzw. Ausarbeitung sowie deren Daten auf Datenträgern sind geistiges Eigentum des Erstellers Arch. Artmüller Georg. Jede Benützung, Veröffentlichung,Vervielfältigung jeglicher Art oder Weitergabe an Dritte bedarf der schriftlichen Zustimmung durch Architekt Artmüller.

Durch die Übernahme dieses Planes akzeptiert die ausführende Firma bzw. Person die darauf dargestellten Anordnungen. Geschriebene Planmaße auf dieser Zeichnunghaben Vorrang gegenüber gezeichneten Dimensionen. Der Auftragnehmer verpflichtet sich **vor** Arbeitsbeginn alle Maße und Bedingungen im Zusammenhang mit seinerArbeit auf der Baustelle verantwortlich zu überprüfen.

Abweichungen gegenüber dargestellten oder schriftlich vereinbarten Anordnungen müssen Architekt Artmüller und der Bauleitung unverzüglich schriftlich mitgeteiltwerden. Vor Arbeitsbeginn sind dem Architekten gültige Werkzeichnungen zur Genehmigung vorzulegen.

NATURMASSE SIND ZU NEHMEN, KOTEN ZU PRÜFEN

Index	Datum	Bearbeiter	Änderung

Index	Änderung	Datum

VORABZUG
22. 10. 2026

Grundeigentümer

Bauwerber / Auftraggeber

ARTMÜLLER ARCHITEKTEN
ZIVILTECHNIKER GMBH
Stolberggasse 34|26 A-1050 Wien
t [+43] 01 . 581 40 83 f [+43] 01. 581 40 83 99 office@artmueller.eu

Planinhalt
Dachdraufsicht

Maßstab	Gez	Datum	Plannr.	Index
1:50	ML	22-10-2026	WNEU30_50_04	VORABZUG

Erstellt, am 11.11.2026

Top 1
Aufenthaltsfläche 47,50 m²
SUMME 47,50 m²
Top 2
Aufenthaltsfläche 52,11 m²
SUMME 52,11 m²
Top 01
Aufenthaltsfläche 95,71 m²
SUMME 95,71 m²
Top 2
Aufenthaltsfläche 439,68 m²
SUMME 439,68 m²
Top 03 Neu
SUMME 0,00 m²
Außenflächen 31,14 m²
Top 04 Neu
Aufenthaltsfläche 17,40 m²
SUMME 17,40 m²
Außenflächen 113,24 m²
Fahrrad-Abstellanlage 3
Grünfläche
Rasengittersteine
45,27 m²
7,28 m²
Garten TOP 2
Grünfläche
33,66 m²
Einleitung Niederschlagswässer in Hörmbach gemäß wasserrechtlicher Einreichung
Doppelstabgitterzaun NEU H=150cm
Beton-Raseneinfassungsstein
7 Fahrradabstellplätze
3 KFZ - STELLPLÄTZE
BETONSTEINPFLASTER - VERSICKERUNGSFÄHIG
1
2
3
Parkplatz - Hof
Rasengittersteine
212,56 m²
Terrasse
Betonplatten
6,82 m²
Hörmbach
GRUNDGRENZE
Fahrrad-Abstellanlage 4
Rasengittersteine
6,35 m²
6 Fahrradabstellplätze
ZULEITUNGEN WÄRMEPUMPE (erdverlegt)
2 STK Luft/Wasser Wärmepumpen Außeneinheit
B1900 x L940 x H1570 [mm]
Gewicht (ohne Wasser, mit Kältemittel): 550 [kg]
auf 3 Stk. STB Streifenfundamente
Schotterkoffer
Kies
8,02 m²
Außeneinheit WP auf STB Fundam.
Schotterkoffer
Kies
2,16 m²
2 STK. Pumpenmodule
B420 x L800 x H550 [mm]
Gewicht 40 [kg]
Waschbetonplatte im Kiesbett
Gehtor
Sicherheitsabstand WP 1,5m
Unterirdischer Retentionsspeicher gemäß wasserrechtlicher Einreichung.
PARKPLÄTZE
BETONSTEINPFLASTER
(versickerungsfähig)
Unterirdischer Retentionsspeicher
(Ausführung/Konstruktionsweise noch offen)
4
5
6
7 - BARRIEREFREI
Fahrrad-Abstellanlage 2
Rasengittersteine
5,59 m²
Zugang
Rasengittersteine
Zufahrt
Rasengittersteine
Zimmer
Parkett
Wohnküche
Bad/WC
Vorraum
Technikraum
Kinderwagenraum
Haustechnik
Einlagerungsraum
Stiegenhaus
Gang
Fliesen
TERR.TÜR NEU
FENSTER NEU
VWS 10cm EPS ERNEUERN
Hausanschluss Elektro
Fahrrad-Abstellanl. 1
Rasengittersteine
6,80 m²
6 Fahrradabstellplätze
Terrasse TOP 1
Betonplatten
9,14 m²
Holzlattenzaun NEU
Gehtor NEU
Garten TOP 1
Grünfläche
18,28 m²
HECKE NEU
GRUNDGRENZE / STRASSENFLUCHTLINIE
Parkplätze - vorderer Bauwich
Rasengittersteine
28,94 m²
9
500
Bestehender Aluminiumzaun auf Betonsockel
Bestehende straßenseitige Einfriedung
Bestehender Aluminium Steher zur Installation Schiebetor
Entwässerungsrinne

LEGENDE

- ⊠ Wanddurchbruch
- ▭ Deckendurchbruch
- ▭ Bodenschlitz
- ◢ Bodendurchbruch
- ▼ OK Fertigbau
- ▲ UK Fertigbau
- ▽ OK Rohbau
- △ UK Rohbau
- ± 0,00 Höhenangabe einer waagrechten Fläche
- ±0,00 Höhenangabe eines Punktes in einem Bauwerk - Fertigmaß
- ±0,00 Höhenangabe eines Punktes in einem Bauwerk - Rohbaumaß

BGF	Bruttogesamtfläche
HNF / NNF	Haupt- Nebennutzfläche

- ▨ Mauerwerk (wärmedämmend)
- ▨ Mauerwerk (nicht wärmedämmend)
- ▨ unbewehrter Beton
- ▨ bewehrter Beton
- ▦ Betonfertigteil
- ▤ Stein
- ▨ Stahl (allgemein)
- ▨ Holz (allgemein)
- ▨ Holzwerkstoffe
- ▩ Dämmstoff (hart)
- ▩ Dämmstoff (weich)
- ▩ Kunststoff (allgemein)
- ▚ Dichtstoff (allgemein)
- ▥ Gips (Gipskartonplatte)
- ▥ Gipskartonplatte Brandschutz
- ☐ Erdmaterial (allgemein)
- ⬜ Bestand
- 🟨 Abbruch
- 🟥 Neubau

- — Medien
- — Fernwärme
- — Gas
- — Strom
- — Heizung
- — Regenwasser
- — Schmutzwasser
- — Wasser
- — Blech
- - - Abdichtung
- - - Folie
- - - Dampfsperre, -bremse

Höhenbezugs- und Maßangaben

DOK	Deckenoberkante
DOS	Deckenoberseite
DUK	Deckenunterkante
DUS	Deckenunterseite
DUF	Deckenunterkante (fertige Untersicht)
FBOK	Fußbodenoberkante
OFF	Oberfläche des fertigen Fußbodens
FDOK	Fundamentoberkante
FDOS	Fundamentoberseite
FDUK	Fundamentunterkante
FDUS	Fundamentunterseite
RH	lichte Raumhöhe
GH	Geschoßhöhe
OK	Oberkante
OS	Oberseite
UK	Unterkante
US	Unterseite
STUK	Sturzunterkante (Rohbaumaß)
STH	Sturzhöhe gemessen von STUK bis DUK (Rohbaumaß)
RPH	Rohbauparapethöhe
FPH	fertige Parapethöhe (FBOK bis OK Fensterbank Innen)

Rauch-, Abgas- und Luftfänge, Schächte

L	Lüftungsschacht
PT	Putztürchen
PS	Putzstück
KT	Kehrtürchen
ABL	Abluft
ZUL	Zuluft
DBA	Druckbelüftungsanlage
DES	Druckentlastungsschacht
BÖ	Belüftungsöffnung
ÜÖ	Überströmöffnung
AÖ	Abströmöffnung mit Überdruckentlastungsorgan
BSK	Brandsschutzklappe
FBHV	Fussbodenheizungsverteiler
E-Verteiler	Elektroverteiler

Öffnungen und deren Abschlüsse

WD	Wanddurchbruch
DD	Deckendurchbruch
FBD	Fußbodendurchbruch
FDD	Fundamentdurchbruch
WS	Wandschlitz
WA	Wandaussparung
DA	Deckenaussparung
FBA	Fußbodenaussparung
RBL	Rohbaulichte
AL	Architekturlichte
STL	Stocklichte
GL	Glaslichte
STAM	Stockaußenmaß
DL	Durchgangslichte
GGT	Ganzglastüre
MGT	Metallgittertür
HT	Hebetüre
HST	Hebeschiebetüre
T	Türe
AT	Allgemeintüre
ET	Eingangstüre
WET	Wohnungseingangstür
IT	Innentür
DF	Drehflügel
DKF	Drehkippflügel
SF	Schiebe-Fenster
SWF	Schwingflügel
WF	Wendeflügel
K	Kippfenster
OL	Oberlichte
DF	Dachflächenfenster
PFR	Pfostenriegelkonstruktion
FE	Fenster
FT	Fenstertüre
R	Rechtsöffnend
L	Linksöffnend
FIX	Fixverglasung
VSG	Verbund-Sicherheitsglas
ESG	Einscheiben-Sicherheitsglas

Drehflügel
Drehkippflügel
Kippflügel
Fenstertüre

EI2 30-C-, EI2 60-C-und EI2 90-C
Feuerschutztüren mit Angabe der Feuerwiderstandsklasse
(gemäß ÖNORM B 3850 und ÖNORM B 3807)

GT	gasdichte Türe
DT	Drucktüre
S 200	Rauchabschluss
S 200	Rauchabschluss
C	Selbstschließend
FLS	Freilaufschließer
LVfTÖ	Lehrverrohrung für Türöffner
elTÖ	elektrischer Türöffner

AUSFÜHRUNG

POLIERPLAN

Bauvorhaben
WNEU30
2540 Bad Vöslau, Wiener Neustädter Straße 30

XXX

Katastralgemeinde 04035 Vöslau
EZ: 719
GstNr.: 748

Diese Zeichnung bzw. Ausarbeitung sowie deren Daten auf Datenträgern sind geistiges Eigentum des Erstellers Arch. Artmüller Georg. Jede Benützung, Veröffentlichung,Vervielfältigung jeglicher Art oder Weitergabe an Dritte bedarf der schriftlichen Zustimmung durch Architekt Artmüller.

Durch die Übernahme dieses Planes akzeptiert die ausführende Firma bzw. Person die darauf dargestellten Anordnungen. Geschriebene Planmaße auf dieser Zeichnunghaben Vorrang gegenüber gezeichneten Dimensionen. Der Auftragnehmer verpflichtet sich **vor** Arbeitsbeginn alle Maße und Bedingungen im Zusammenhang mit seinerArbeit auf der Baustelle verantwortlich zu überprüfen.

Abweichungen gegenüber dargestellten oder schriftlich vereinbarten Anordnungen müssen Architekt Artmüller und der Bauleitung unverzüglich schriftlich mitgeteiltwerden. Vor Arbeitsbeginn sind dem Architekten gültige Werkzeichnungen zur Genehmigung vorzulegen.

NATURMASSE SIND ZU NEHMEN, KOTEN ZU PRÜFEN

Index	Datum	Bearbeiter	Änderung

Index	Änderung	Datum

Grundeigentümer

Bauwerber / Auftraggeber

ARTMÜLLER ARCHITEKTEN
ZIVILTECHNIKER GMBH
Stolberggasse 34|26 A-1050 Wien
t [+43] 01 . 581 40 83 f [+43] 01. 581 40 83 99 office@artmueller.eu

Planinhalt
Aussenanlagen

Maßstab	Gez	Datum	Plannr.	Index
1:50	ML	22-10-2026	WNEU30_50_05	VORABZUG

Erstellt, am 11.11.2026

VORABZUG
22. 10. 2026

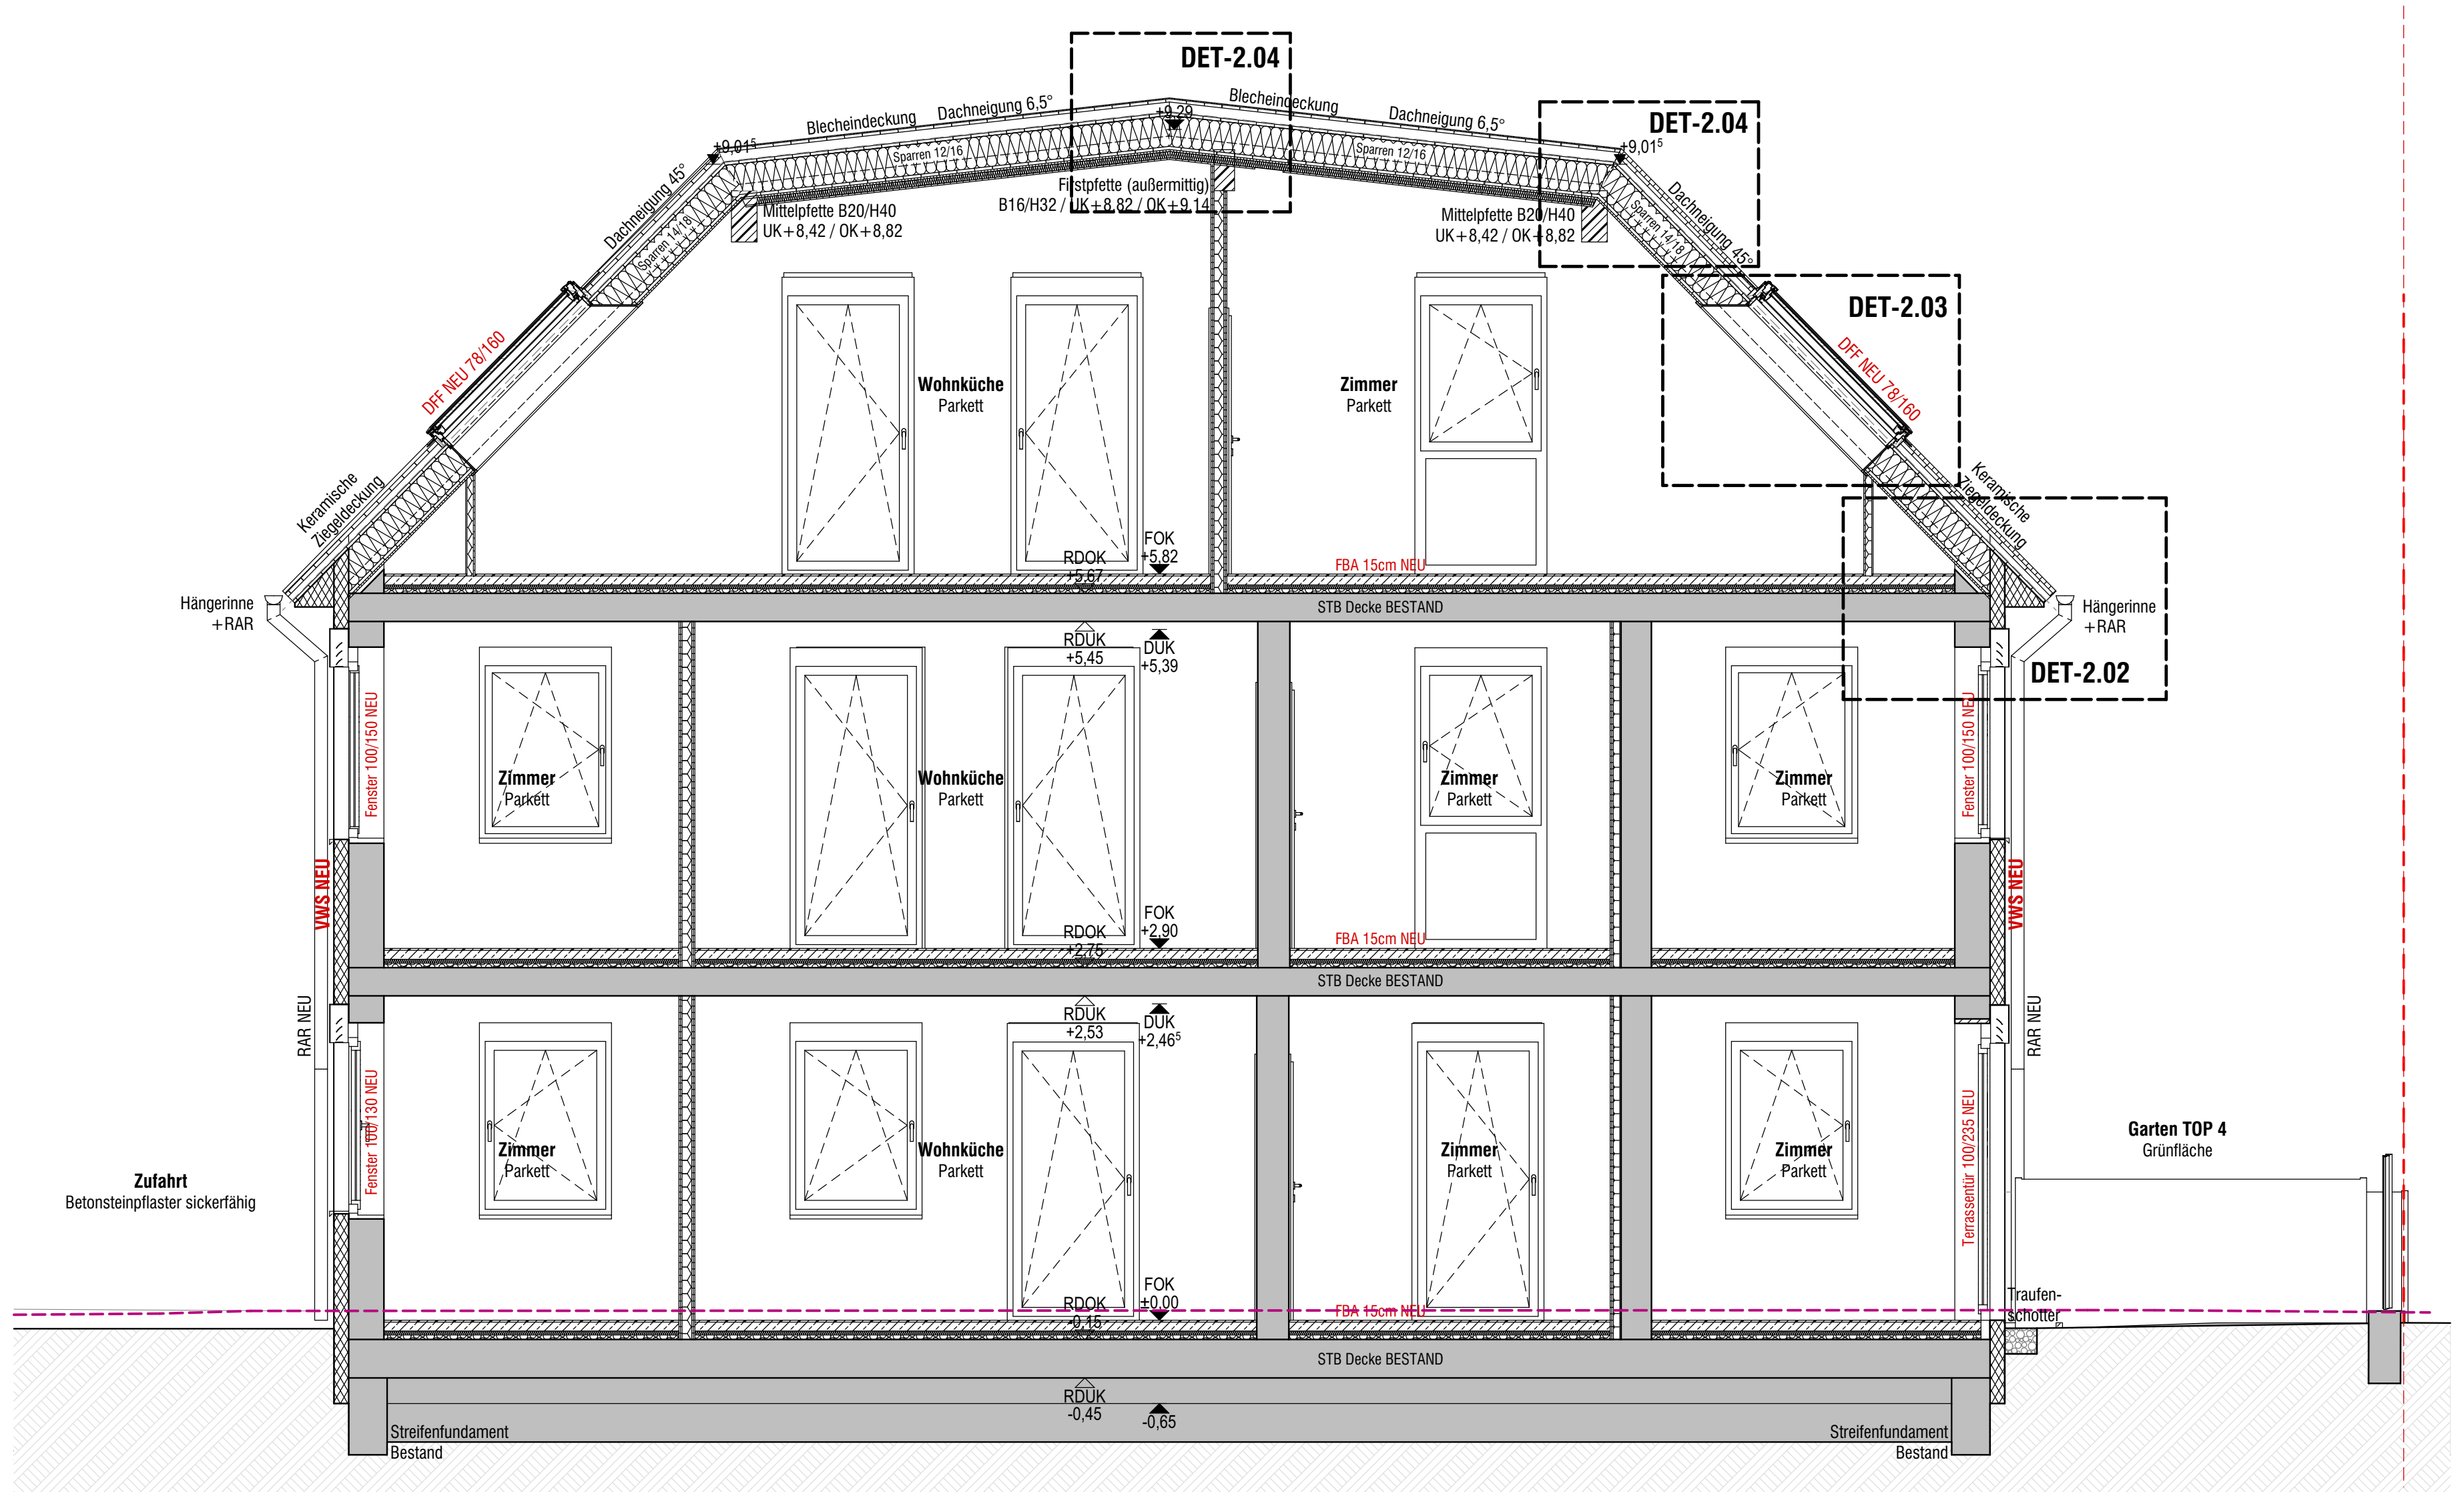
DET-2.04
DET-2.04
DET-2.03
DET-2.02
Wohnküche
Parkett
Zimmer
Parkett
Blecheindeckung
Dachneigung 6,5°
Dachneigung 45°
Mittelpfette B20/H40
UK+8,42 / OK+8,82
Hängerinne
+RAR
FBA 15cm NEU
STB Decke BESTAND
Garten TOP 4
Grünfläche
Zufahrt
Betonsteinpflaster sickerfähig
Streifenfundament
Bestand
FOK
ROK
DUK

Schnitt H-H | 1:50

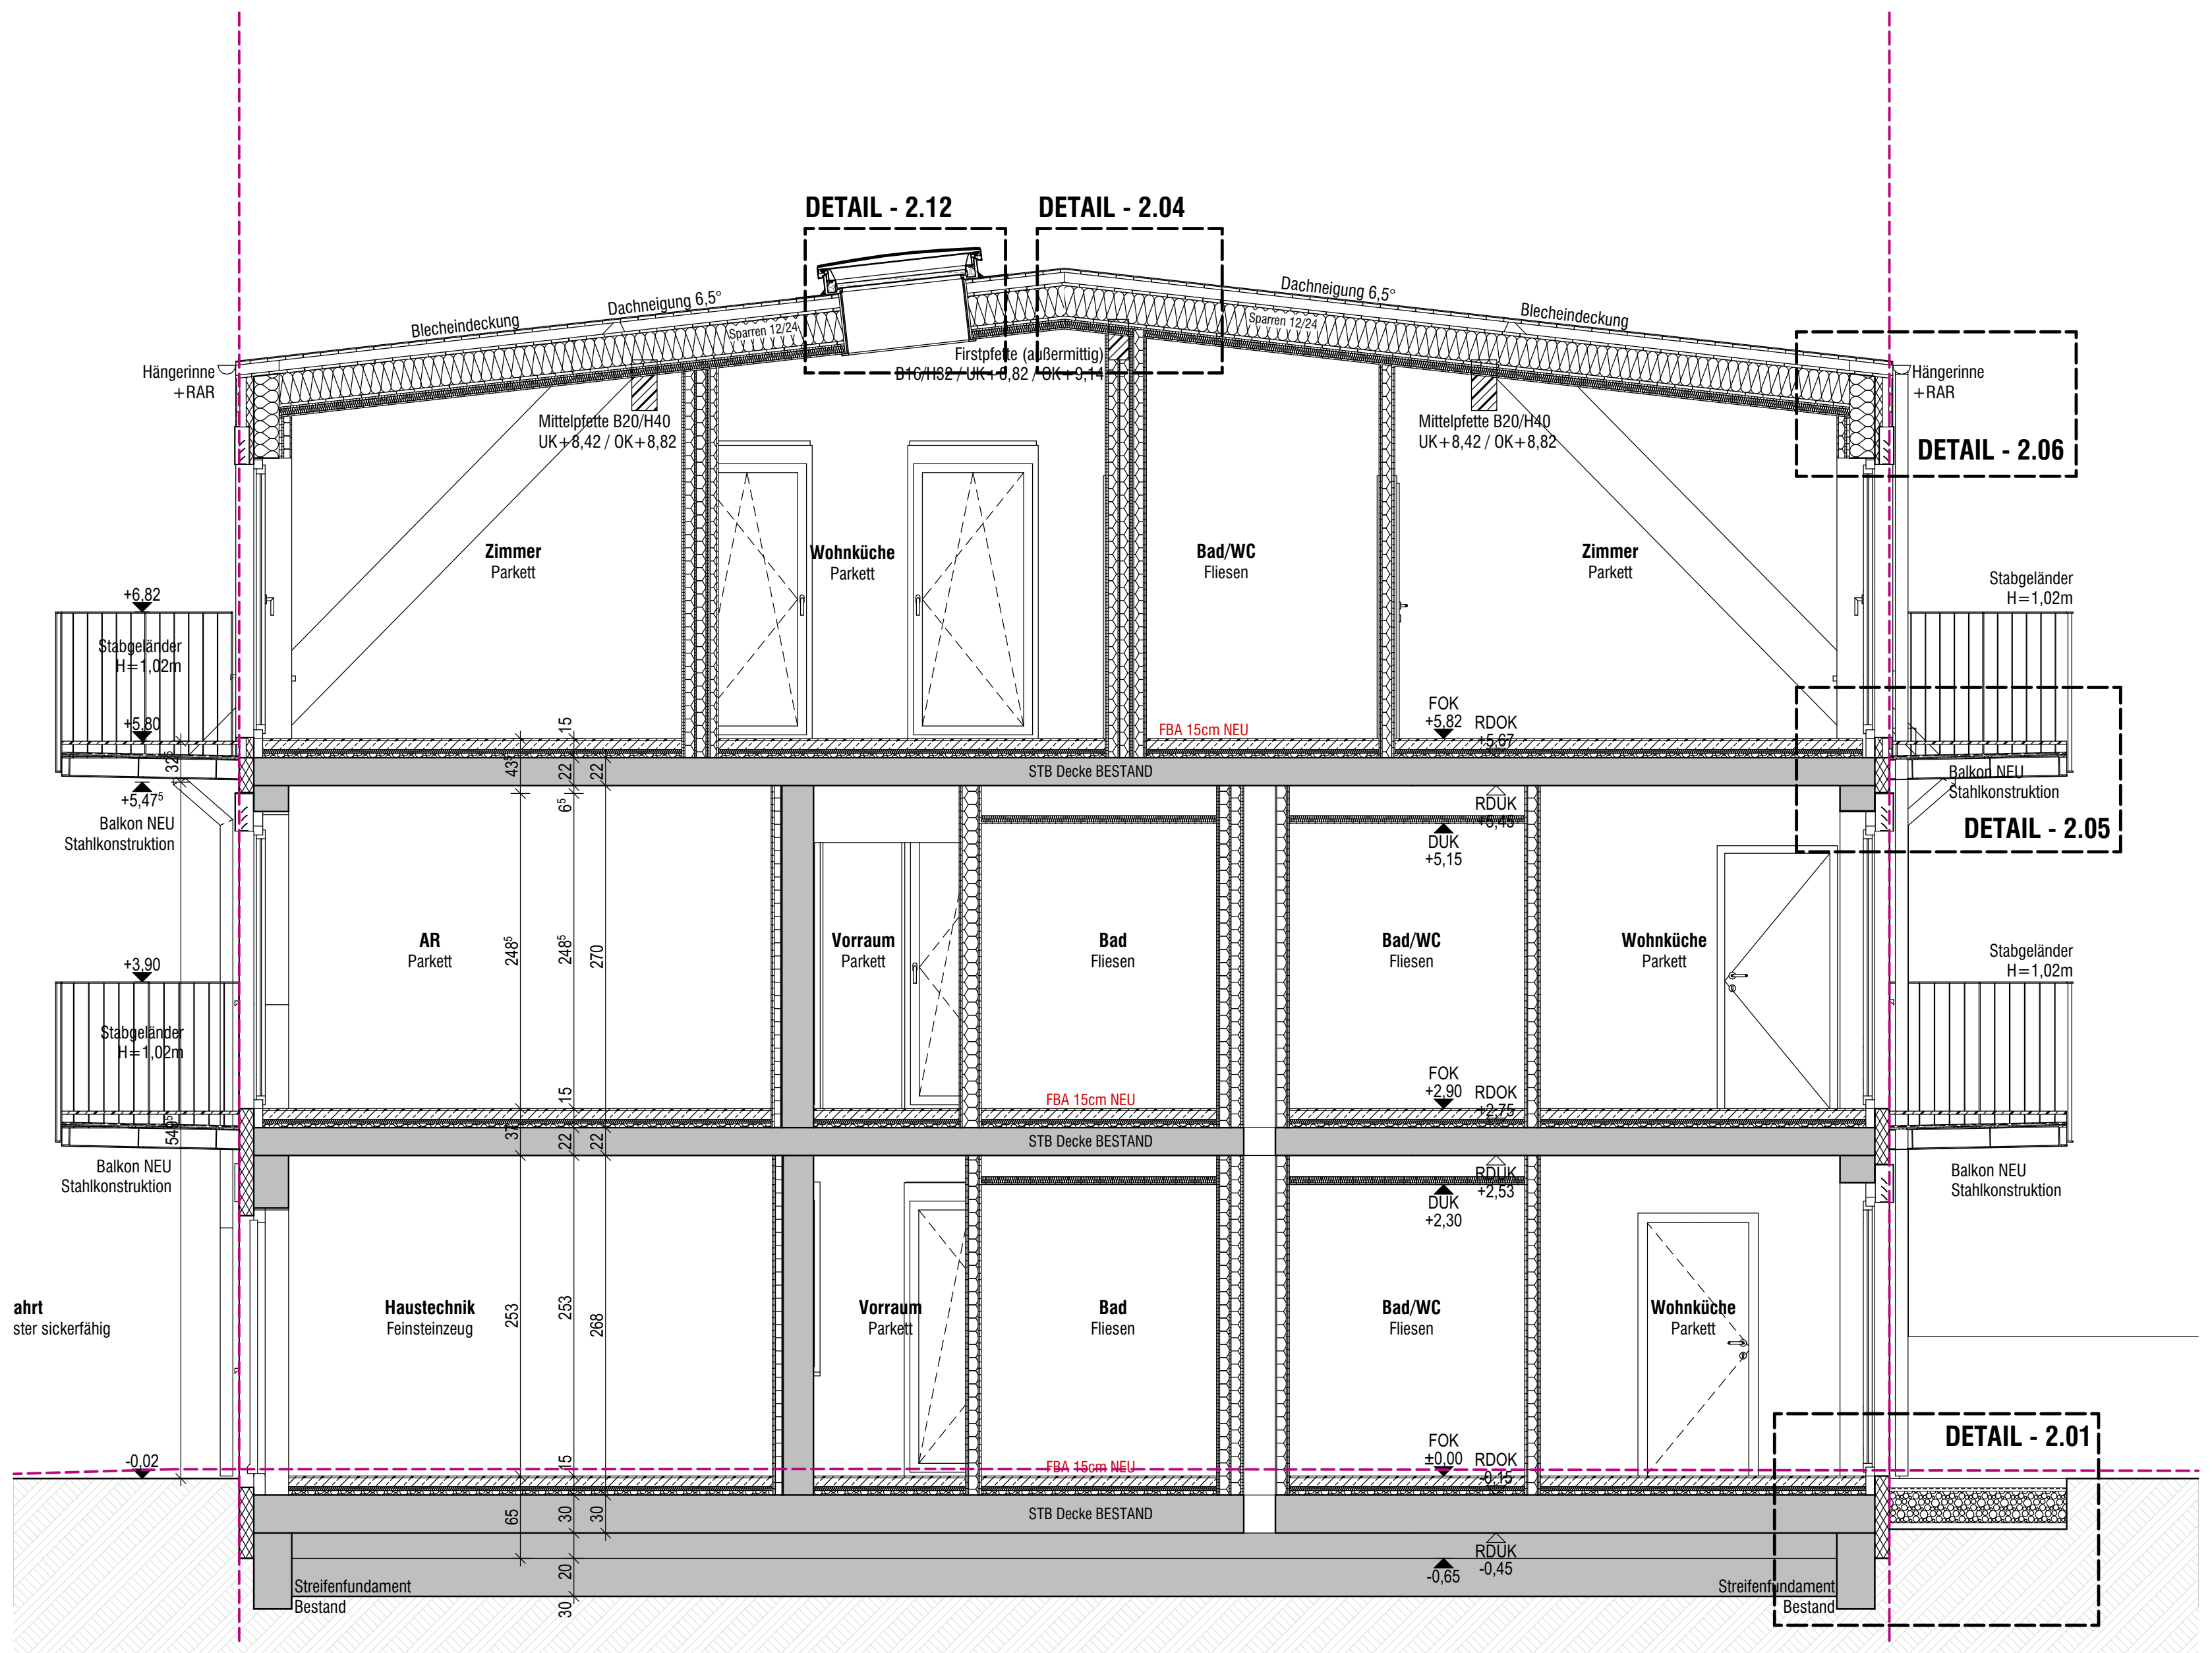
DETAIL - 2.12
DETAIL - 2.04
DETAIL - 2.06
DETAIL - 2.05
DETAIL - 2.01
Blecheindeckung
Dachneigung 6,5°
Hängerinne
+RAR
Zimmer
Parkett
Wohnküche
Parkett
Bad/WC
Fliesen
AR
Parkett
Vorraum
Parkett
Bad
Fliesen
Haustechnik
Feinsteinzeug
Stabgeländer
H=1,02m
Balkon NEU
Stahlkonstruktion
FBA 15cm NEU
STB Decke BESTAND
Streifenfundament
Bestand

Schnitt B-B | 1:50

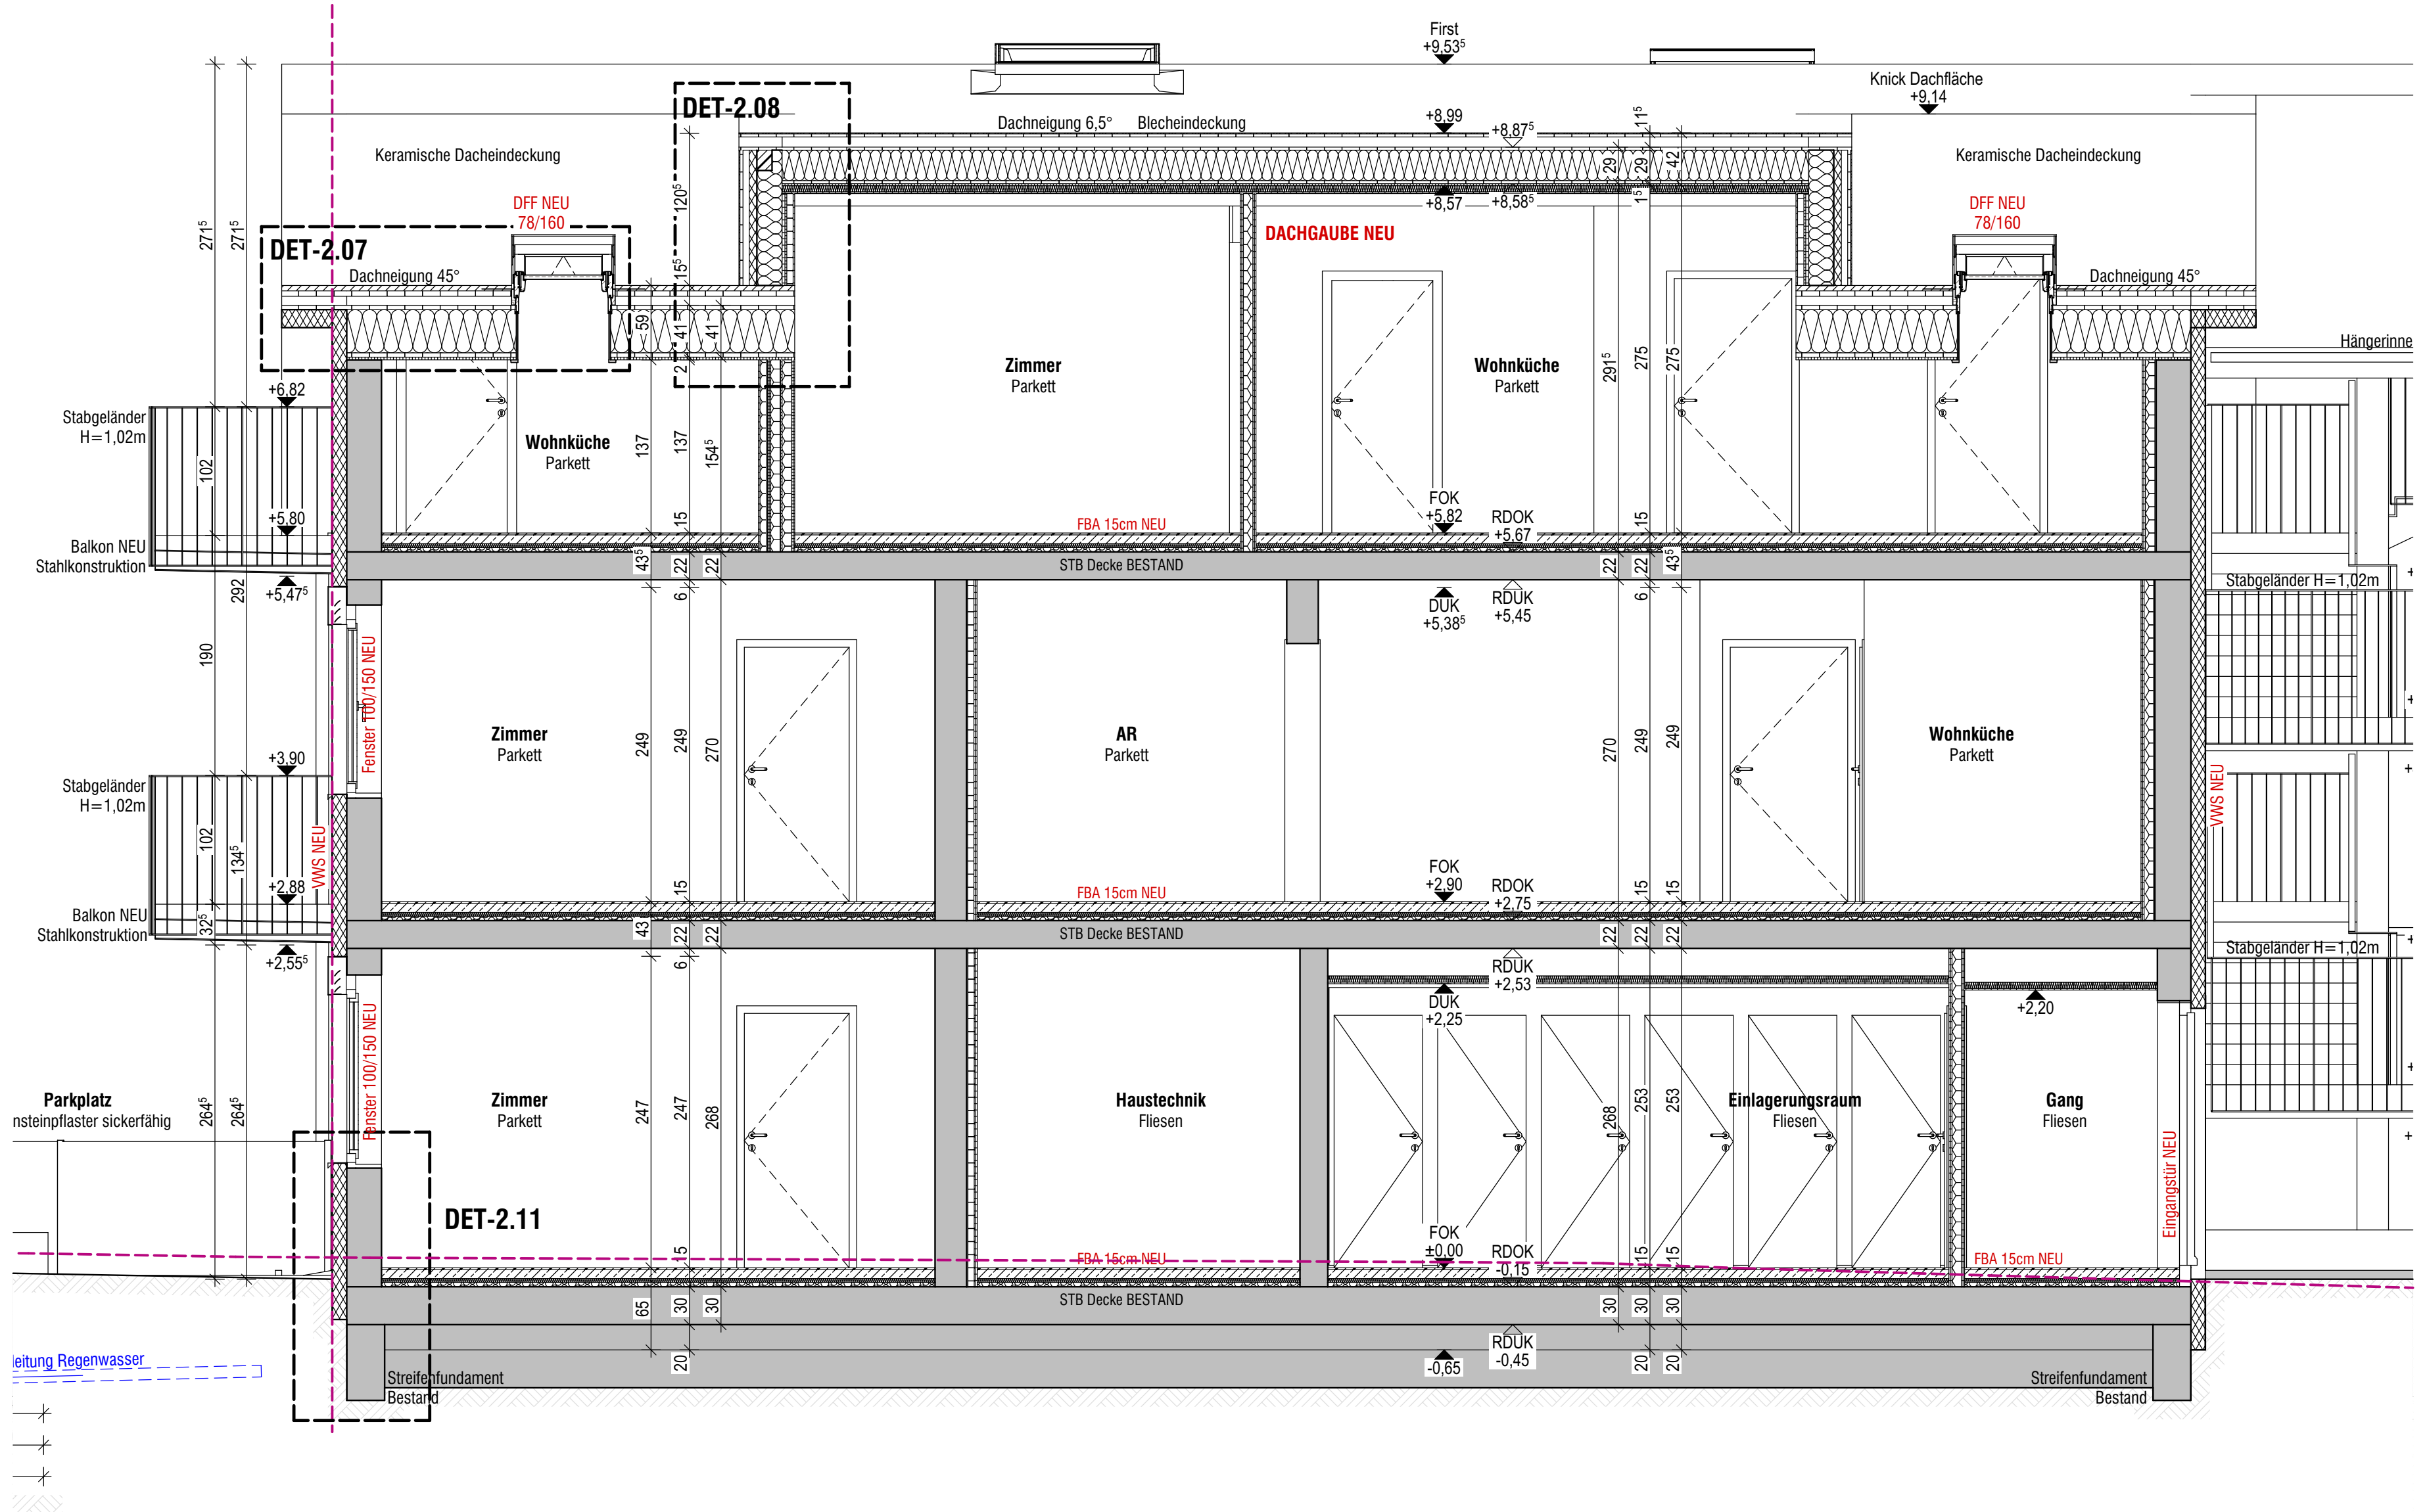
DET-2.08
DET-2.07
DET-2.11
First
Dachneigung 6,5°
Blecheindeckung
Keramische Dacheindeckung
DFF NEU
78/160
DACHGAUBE NEU
Dachneigung 45°
Knick Dachfläche
Hängerinne
Zimmer
Parkett
Wohnküche
Parkett
AR
Parkett
Haustechnik
Fliesen
Einlagerungsraum
Fliesen
Gang
Fliesen
Stabgeländer
H=1,02m
Balkon NEU
Stahlkonstruktion
Parkplatz
Betonsteinpflaster sickerfähig
FBA 15cm NEU
STB Decke BESTAND
Streifenfundament
Bestand

SchnittD-D | 1:50

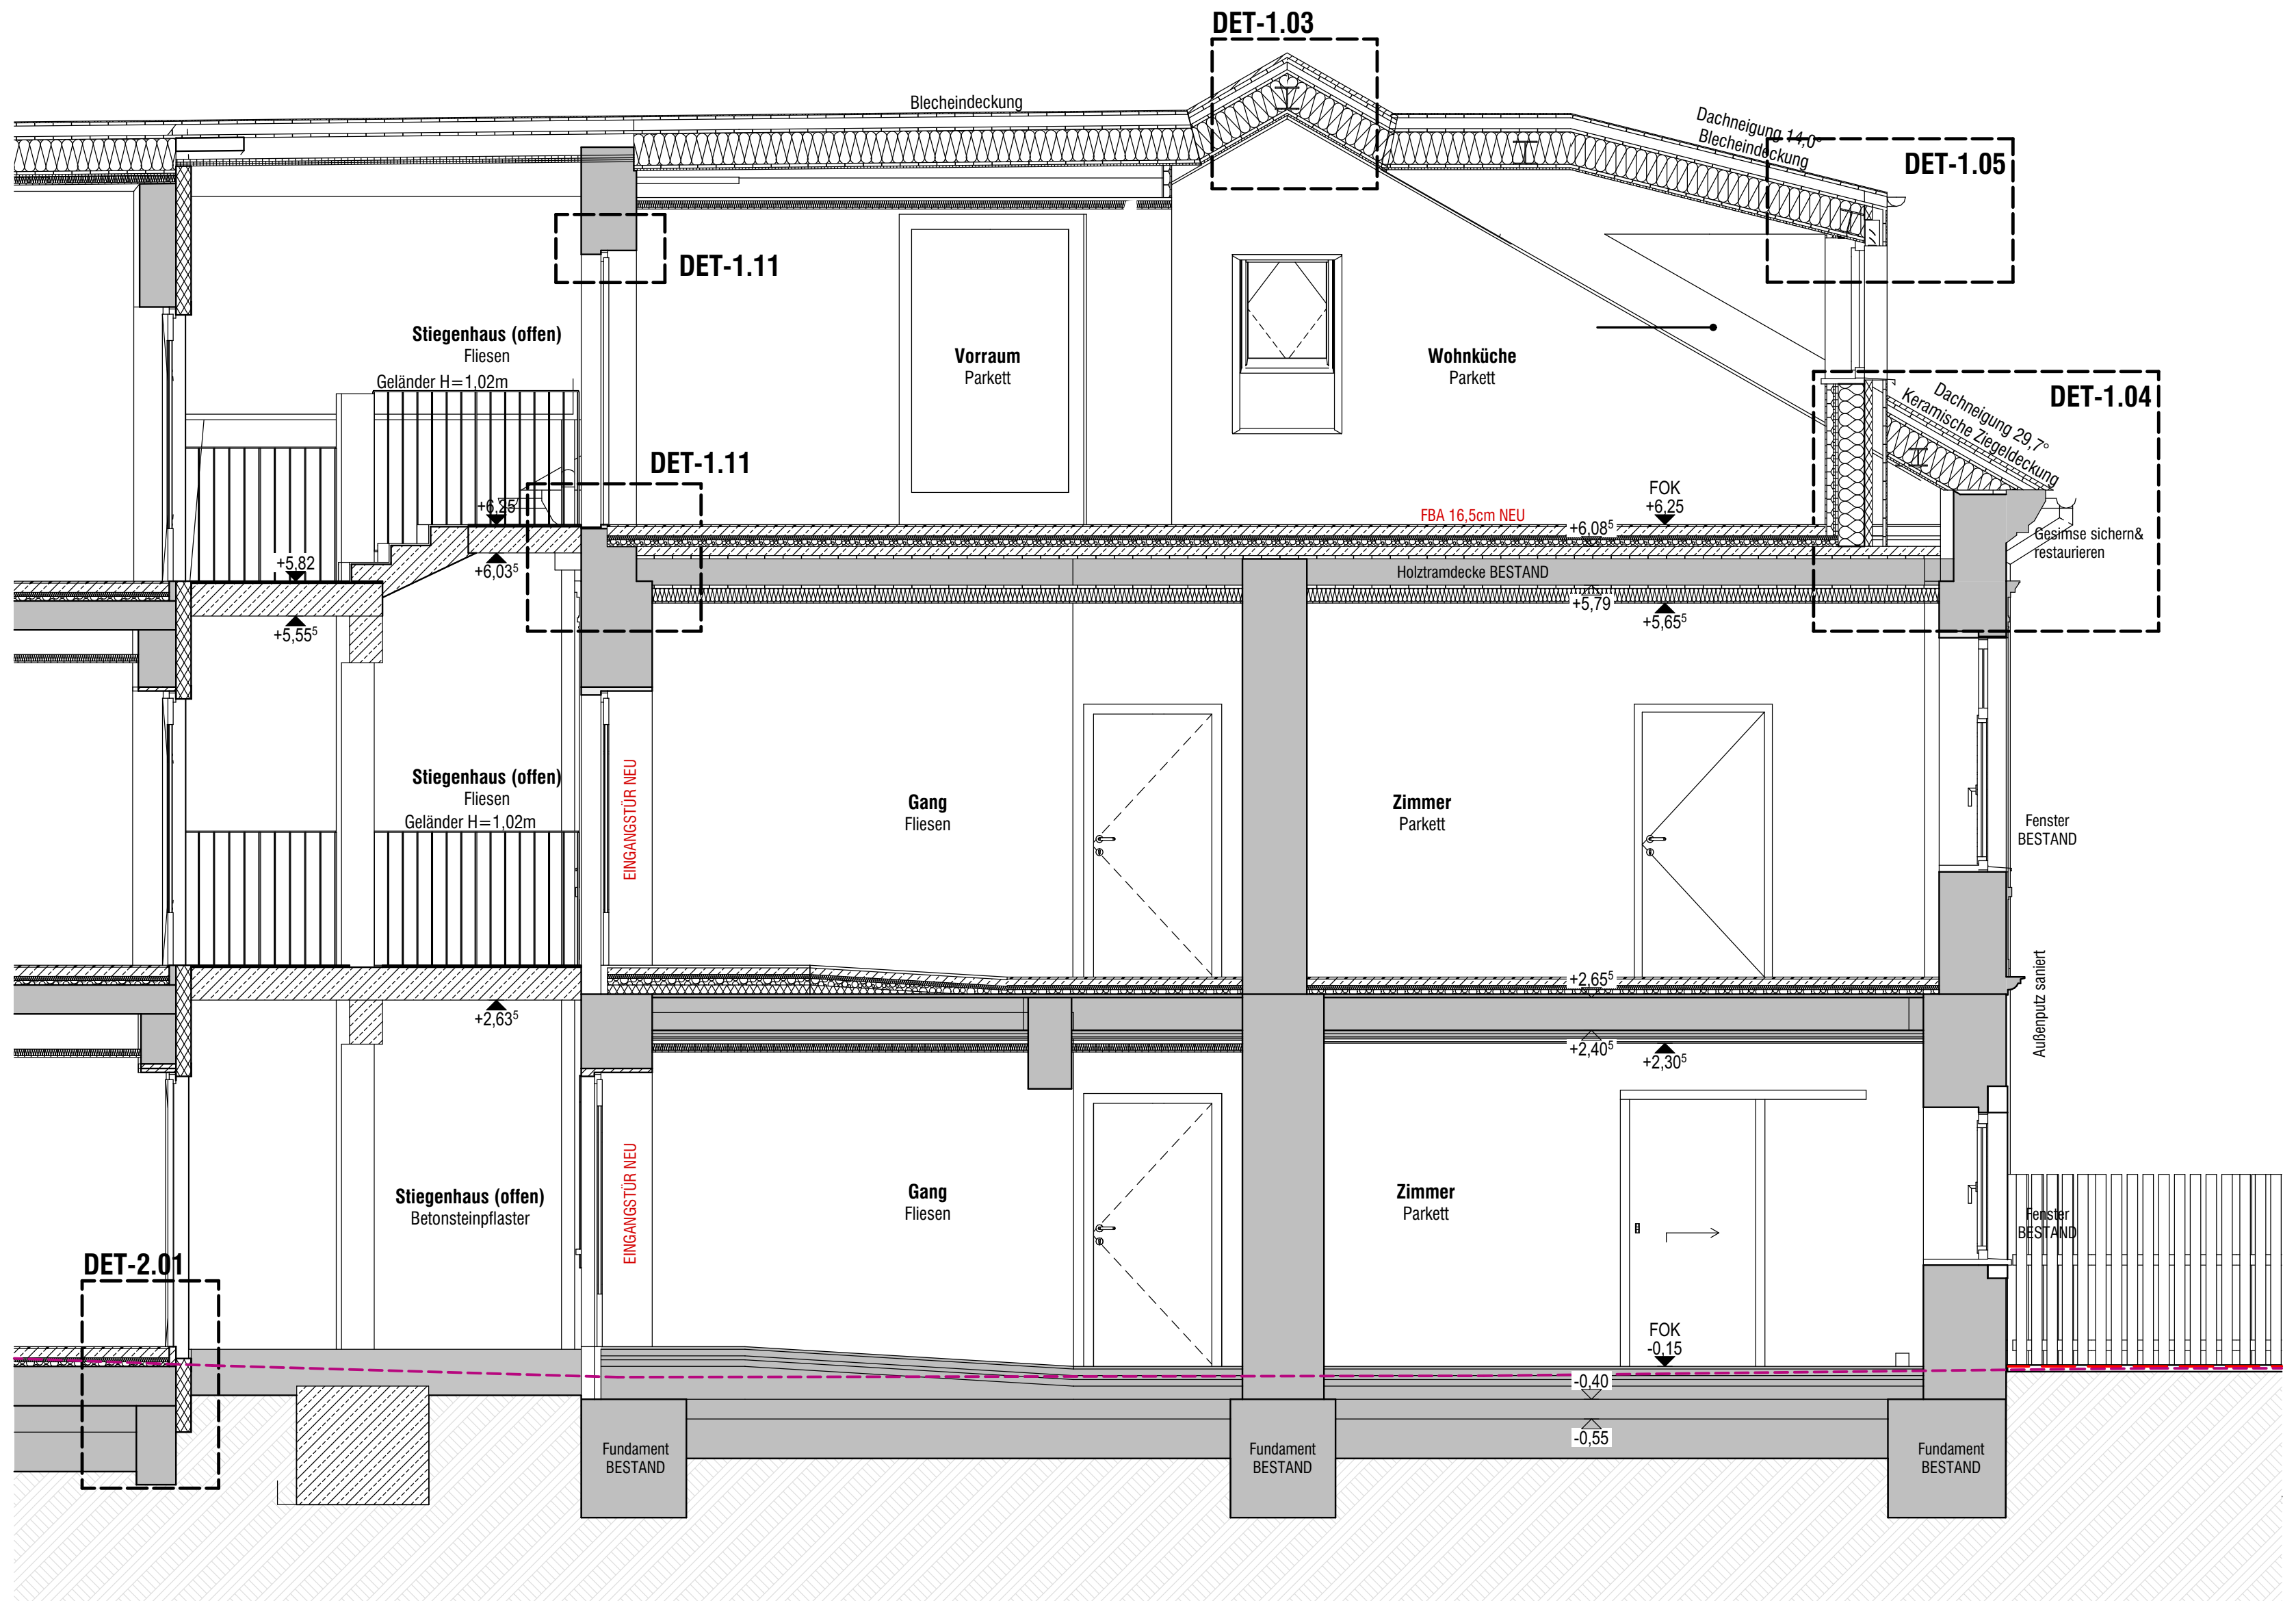
DET-1.03
DET-1.05
DET-1.04
DET-1.11
DET-1.11
DET-2.01
Blecheindeckung
Stiegenhaus (offen)
Fliesen
Geländer H=1,02m
Stiegenhaus (offen)
Betonsteinpflaster
Vorraum
Parkett
Wohnküche
Parkett
Gang
Fliesen
Zimmer
Parkett
FBA 16,5cm NEU
Holztramdecke BESTAND
Fenster
BESTAND
Fundament
BESTAND

Schnitt C-C | 1:50

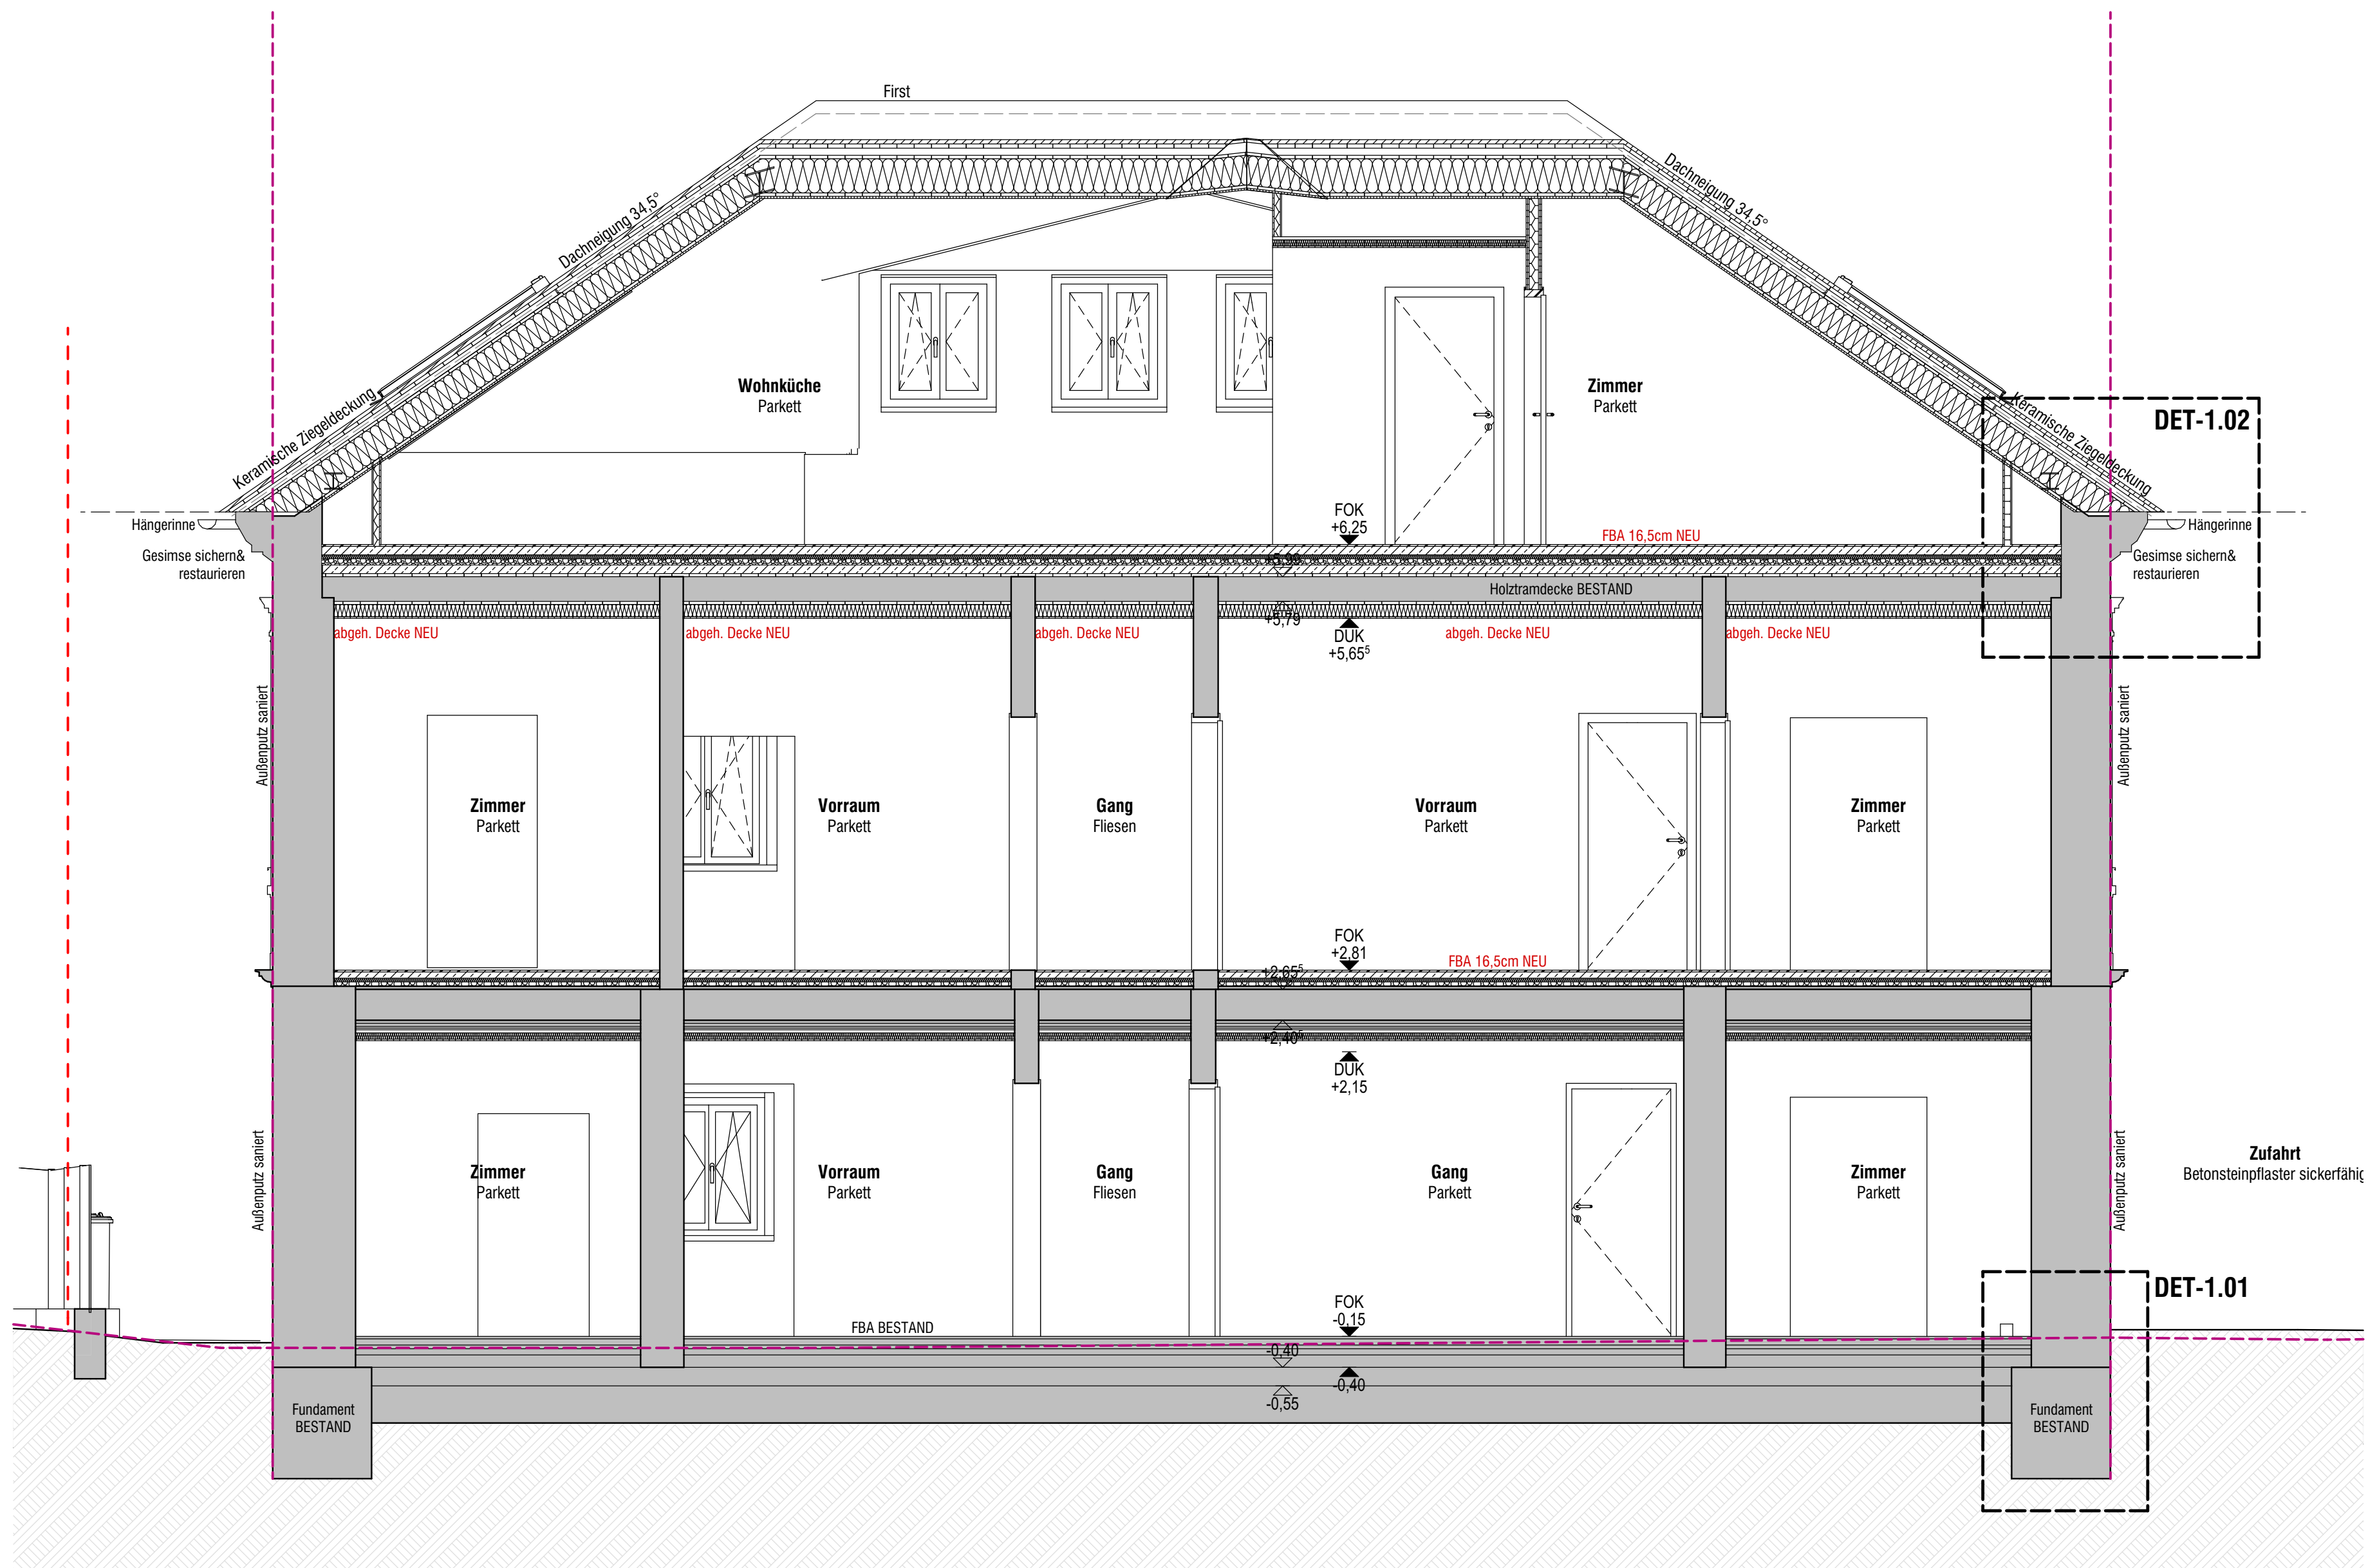
DET-1.02
DET-1.01
First
Dachneigung 34,5°
Wohnküche
Parkett
Zimmer
Parkett
Vorraum
Parkett
Gang
Fliesen
Hängerinne
Gesimse sichern& restaurieren
FBA 16,5cm NEU
Holztramdecke BESTAND
abgeh. Decke NEU
FBA BESTAND
Zufahrt
Betonsteinpflaster sickerfähig
Fundament
BESTAND

Schnitt A-A | 1:50

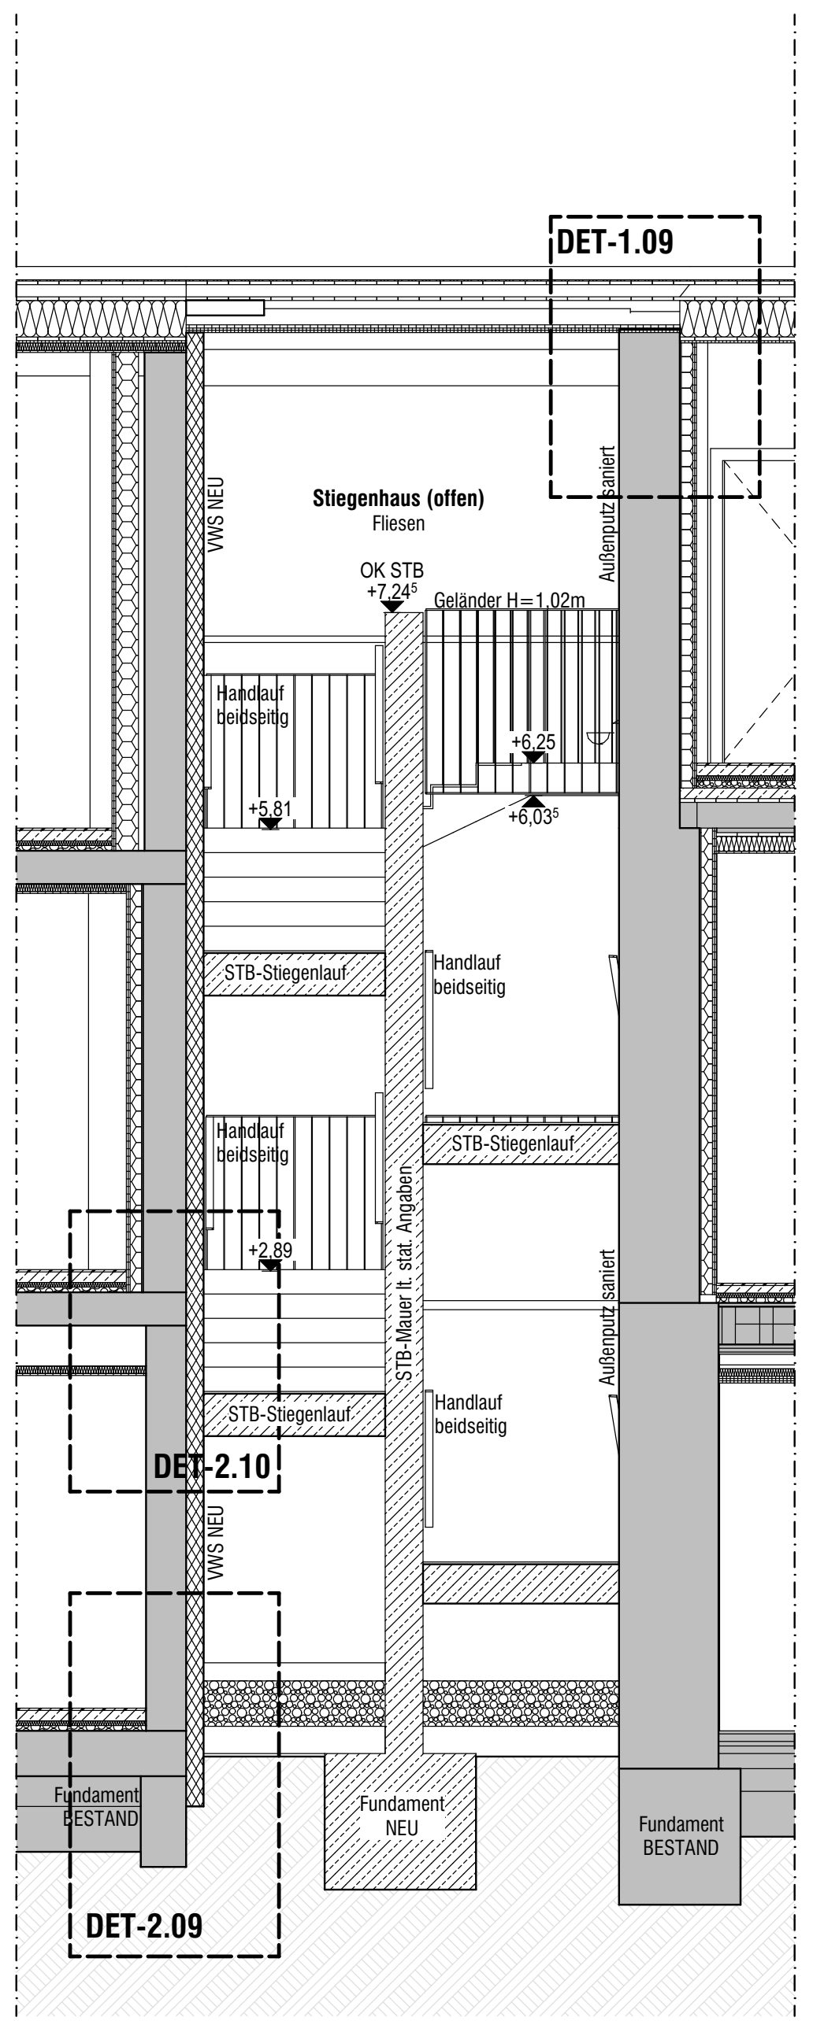
DET-1.09
DET-2.10
DET-2.09
Stiegenhaus (offen)
Fliesen
Geländer H=1,02m
Handlauf beidseitig
STB-Stiegenlauf
Fundament
BESTAND
Fundament
NEU

Schnitt J-J | 1:50

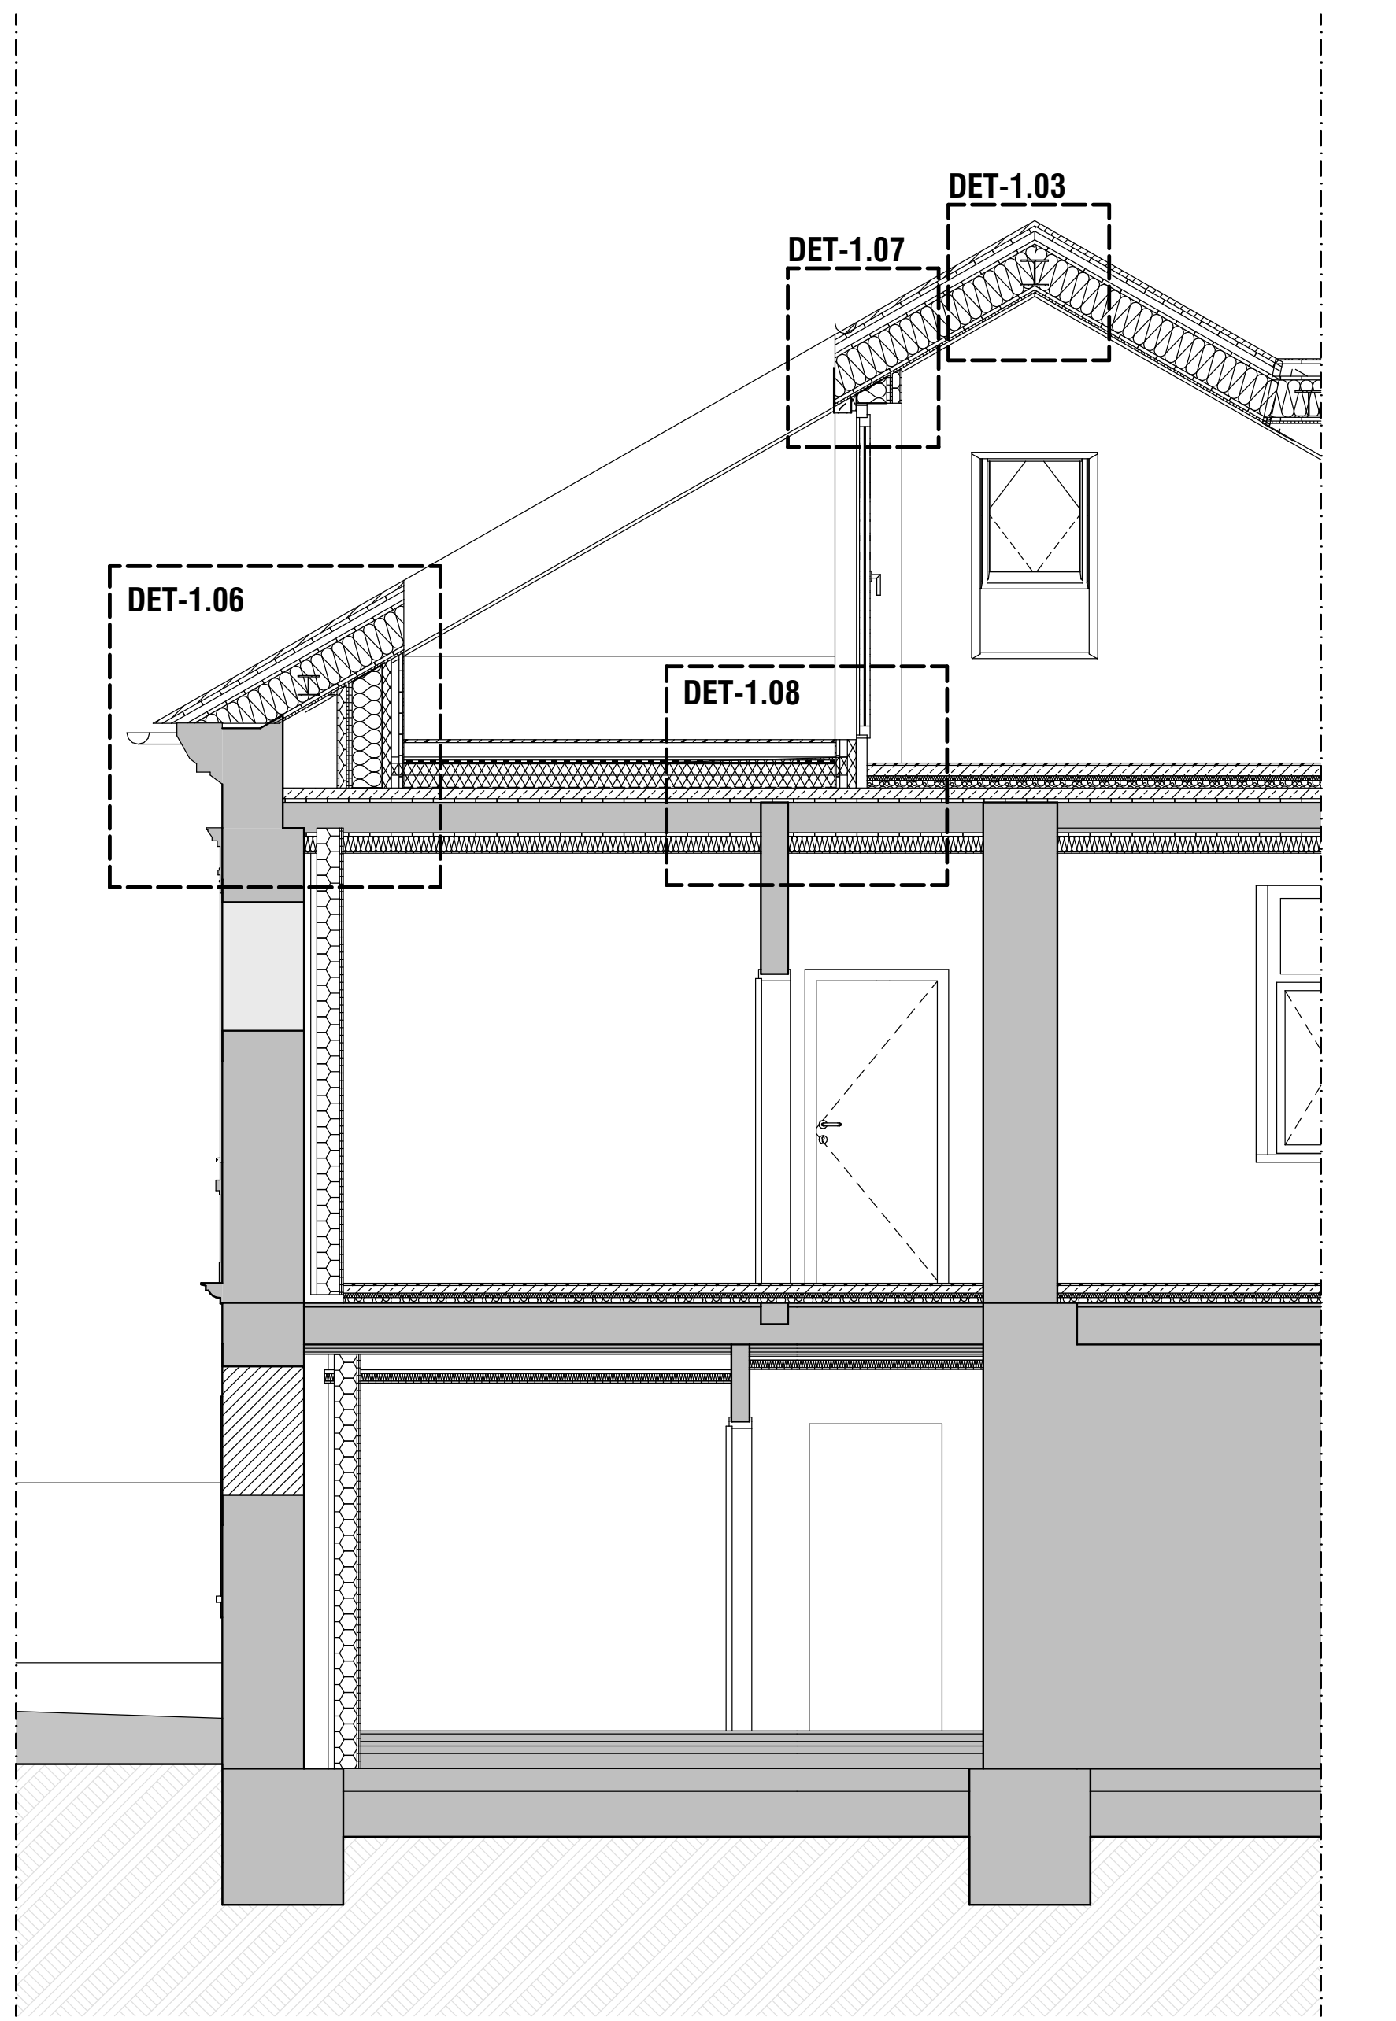
DET-1.03
DET-1.07
DET-1.06
DET-1.08

Schnitt E-E | 1:50

LEGENDE

⊠	Wanddurchbruch
⬚	Deckendurchbruch
◺	Bodenschlitz
◢	Bodendurchbruch
▼	OK Fertigbau
▲	UK Fertigbau
▽	OK Rohbau
△	UK Rohbau
± 0,00	Höhenangabe einer waagrechten Fläche
±0,00	Höhenangabe eines Punktes in einem Bauwerk - Fertigmaß
±0,00	Höhenangabe eines Punktes in einem Bauwerk - Rohbaumaß
BGF	Bruttogesamtfläche
HNF / NNF	Haupt- Nebennutzfläche

▨	Mauerwerk (wärmedämmend)
▨	Mauerwerk (nicht wärmedämmend)
▨	unbewehrter Beton
▨	bewehrter Beton
▦	Betonfertigteil
▤	Stein
▨	Stahl (allgemein)
▨	Holz (allgemein)
▨	Holzwerkstoffe
▩	Dämmstoff (hart)
▩	Dämmstoff (weich)
▩	Kunststoff (allgemein)
▚	Dichtstoff (allgemein)
▥	Gips (Gipskartonplatte)
▥	Gipskartonplatte Brandschutz
☐	Erdmaterial (allgemein)
■	Bestand
🟨	Abbruch
🟥	Neubau

—	Medien
—	Fernwärme
—	Gas
—	Strom
—	Heizung
—	Regenwasser
—	Schmutzwasser
—	Wasser
—	Blech
- - -	Abdichtung
- - -	Folie
- - -	Dampfsperre, -bremse

Höhenbezugs- und Maßangaben

DOK	Deckenoberkante
DOS	Deckenoberseite
DUK	Deckenunterkante
DUS	Deckenunterseite
DUF	Deckenunterkante (fertige Untersicht)
FBOK	Fußbodenoberkante
OFF	Oberfläche des fertigen Fußbodens
FDOK	Fundamentoberkante
FDOS	Fundamentoberseite
FDUK	Fundamentunterkante
FDUS	Fundamentunterseite
RH	lichte Raumhöhe
GH	Geschoßhöhe
OK	Oberkante
OS	Oberseite
UK	Unterkante
US	Unterseite
STUK	Sturzunterkante (Rohbaumaß)
STH	Sturzhöhe gemessen von STUK bis DUK (Rohbaumaß)
RPH	Rohbauparapethöhe
FPH	fertige Parapethöhe (FBOK bis OK Fensterbank Innen)

Rauch-, Abgas- und Luftfänge, Schächte

L	Lüftungsschacht
PT	Putztürchen
PS	Putzstück
KT	Kehrtürchen
ABL	Abluft
ZUL	Zuluft
DBA	Druckbelüftungsanlage
DES	Druckentlastungsschacht
BÖ	Belüftungsöffnung
ÜÖ	Überströmöffnung
AÖ	Abströmöffnung mit Überdruckentlastungsorgan
BSK	Brandsschutzklappe
FBHV	Fussbodenheizungsverteiler
E-Verteiler	Elektroverteiler

Öffnungen und deren Abschlüsse

WD	Wanddurchbruch
DD	Deckendurchbruch
FBD	Fußbodendurchbruch
FDD	Fundamentdurchbruch
WS	Wandschlitz
WA	Wandaussparung
DA	Deckenaussparung
FBA	Fußbodenaussparung
RBL	Rohbaulichte
AL	Architekturlichte
STL	Stocklichte
GL	Glaslichte
STAM	Stockaußenmaß
DL	Durchgangslichte
GGT	Ganzglastüre
MGT	Metallgittertür
HT	Hebetüre
HST	Hebeschiebetüre
T	Türe
AT	Allgemeintüre
ET	Eingangstüre
WET	Wohnungseingangstür
IT	Innentür
DF	Drehflügel
DKF	Drehkippflügel
SF	Schiebe-Fenster
SWF	Schwingflügel
WF	Wendeflügel
K	Kippfenster
OL	Oberlichte
DF	Dachflächenfenster
PFR	Pfostenriegelkonstruktion
FE	Fenster
FT	Fenstertüre
R	Rechtsöffnend
L	Linksöffnend
FIX	Fixverglasung
VSG	Verbund-Sicherheitsglas
ESG	Einscheiben-Sicherheitsglas

Drehflügel
Drehkippflügel
Kippflügel
Fenstertüre

EI2 30-C-, EI2 60-C-und EI2 90-C
Feuerschutztüren mit Angabe der Feuerwiderstandsklasse
(gemäß ÖNORM B 3850 und ÖNORM B 3807)

GT	gasdichte Türe
DT	Drucktüre
S 200	Rauchabschluss
S 200	Rauchabschluss
C	Selbstschließend
FLS	Freilaufschließer
LVfTÖ	Lehrverrohrung für Türöffner
elTÖ	elektrischer Türöffner

AUSFÜHRUNG

POLIERPLAN

Bauvorhaben
WNEU30

2540 Bad Vöslau, Wiener Neustädter Straße 30

XXX

Katastralgemeinde 04035 Vöslau
EZ: 719
GstNr.: 748

Diese Zeichnung bzw. Ausarbeitung sowie deren Daten auf Datenträgern sind geistiges Eigentum des Erstellers Arch. Artmüller Georg. Jede Benützung, Veröffentlichung,Vervielfältigung jeglicher Art oder Weitergabe an Dritte bedarf der schriftlichen Zustimmung durch Architekt Artmüller.

Durch die Übernahme dieses Planes akzeptiert die ausführende Firma bzw. Person die darauf dargestellten Anordnungen. Geschriebene Planmaße auf dieser Zeichnunghaben Vorrang gegenüber gezeichneten Dimensionen. Der Auftragnehmer verpflichtet sich **vor** Arbeitsbeginn alle Maße und Bedingungen im Zusammenhang mit seinerArbeit auf der Baustelle verantwortlich zu überprüfen.

Abweichungen gegenüber dargestellten oder schriftlich vereinbarten Anordnungen müssen Architekt Artmüller und der Bauleitung unverzüglich schriftlich mitgeteiltwerden. Vor Arbeitsbeginn sind dem Architekten gültige Werkzeichnungen zur Genehmigung vorzulegen.

NATURMASSE SIND ZU NEHMEN, KOTEN ZU PRÜFEN

Index	Datum	Bearbeiter	Änderung	

Index	Änderung	Datum

Grundeigentümer

Bauwerber / Auftraggeber

ARTMÜLLER ARCHITEKTEN
ZIVILTECHNIKER GMBH
Stolberggasse 34|26 A-1050 Wien
t [+43] 01 . 581 40 83 f [+43] 01. 581 40 83 99 office@artmueller.eu

Planinhalt
Schnitte

Maßstab	Gez	Datum	Plannr.	Index
1:50	ML	22-10-2026	WNEU30_50_06	VORABZUG

Erstellt, am 11.11.2026

VORABZUG
22. 10. 2026

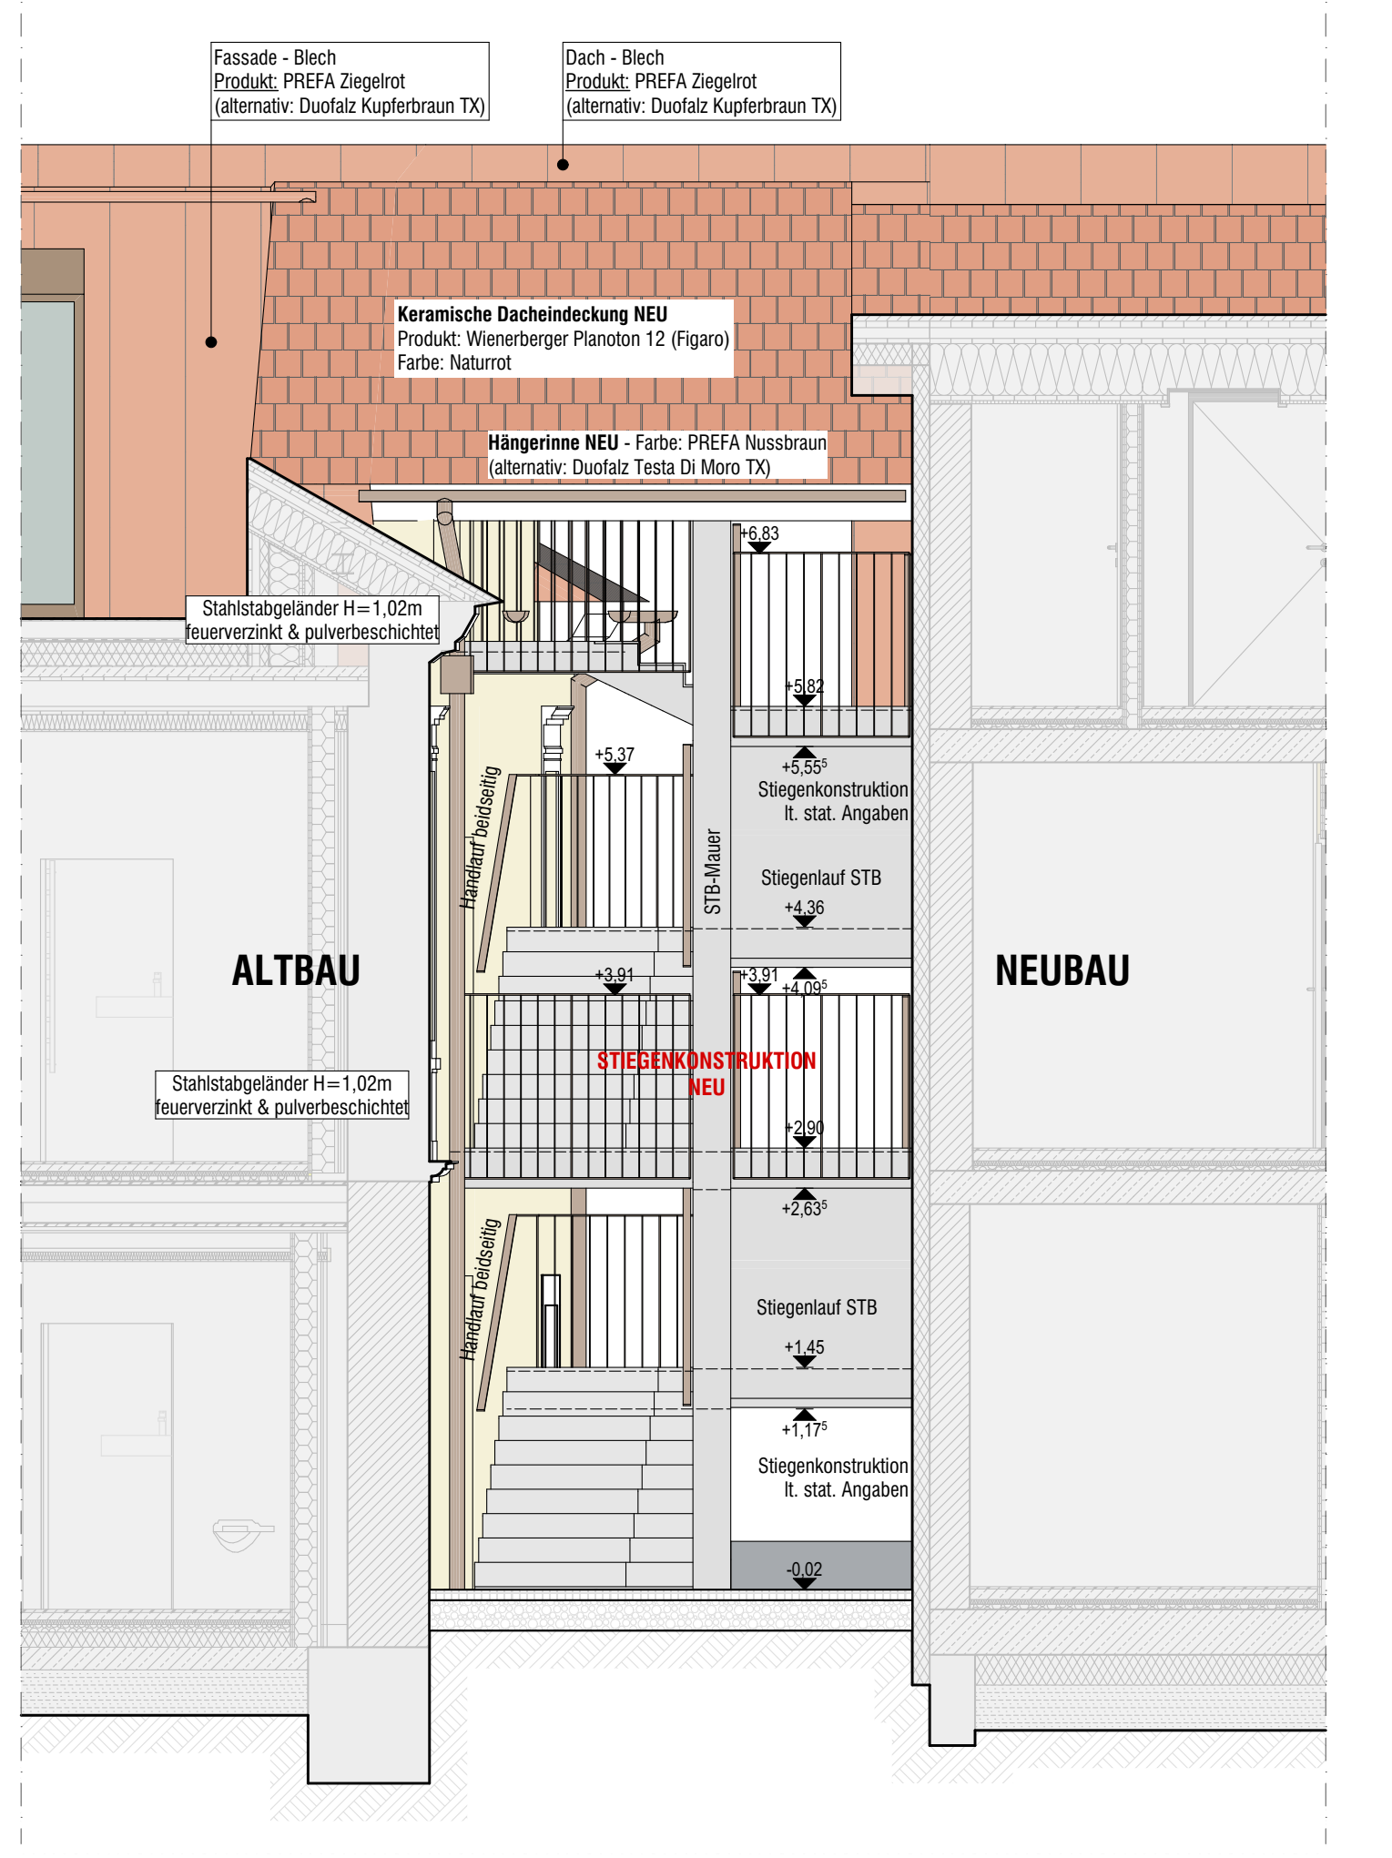
Fassade - Blech
Produkt: PREFA Ziegelrot
(alternativ: Duofalz Kupferbraun TX)
Dach - Blech
Produkt: PREFA Ziegelrot
(alternativ: Duofalz Kupferbraun TX)
Keramische Dacheindeckung NEU
Produkt: Wienerberger Planoton 12 (Figaro)
Farbe: Naturrot
Hängerinne NEU - Farbe: PREFA Nussbraun
(alternativ: Duofalz Testa Di Moro TX)
Stahlstabgeländer H=1,02m
feuerverzinkt & pulverbeschichtet
+6,83
+5,82
+5,37
+5,55
Stiegenkonstruktion
lt. stat. Angaben
Stiegenlauf STB
STB-Mauer
Handlauf beidseitig
+4,36
+3,91
+4,09
ALTBAU
NEUBAU
STIEGENKONSTRUKTION NEU
+2,90
+2,63
+1,45
+1,17
-0,02

NORDANSICHT Stiegenhaus | 1:50

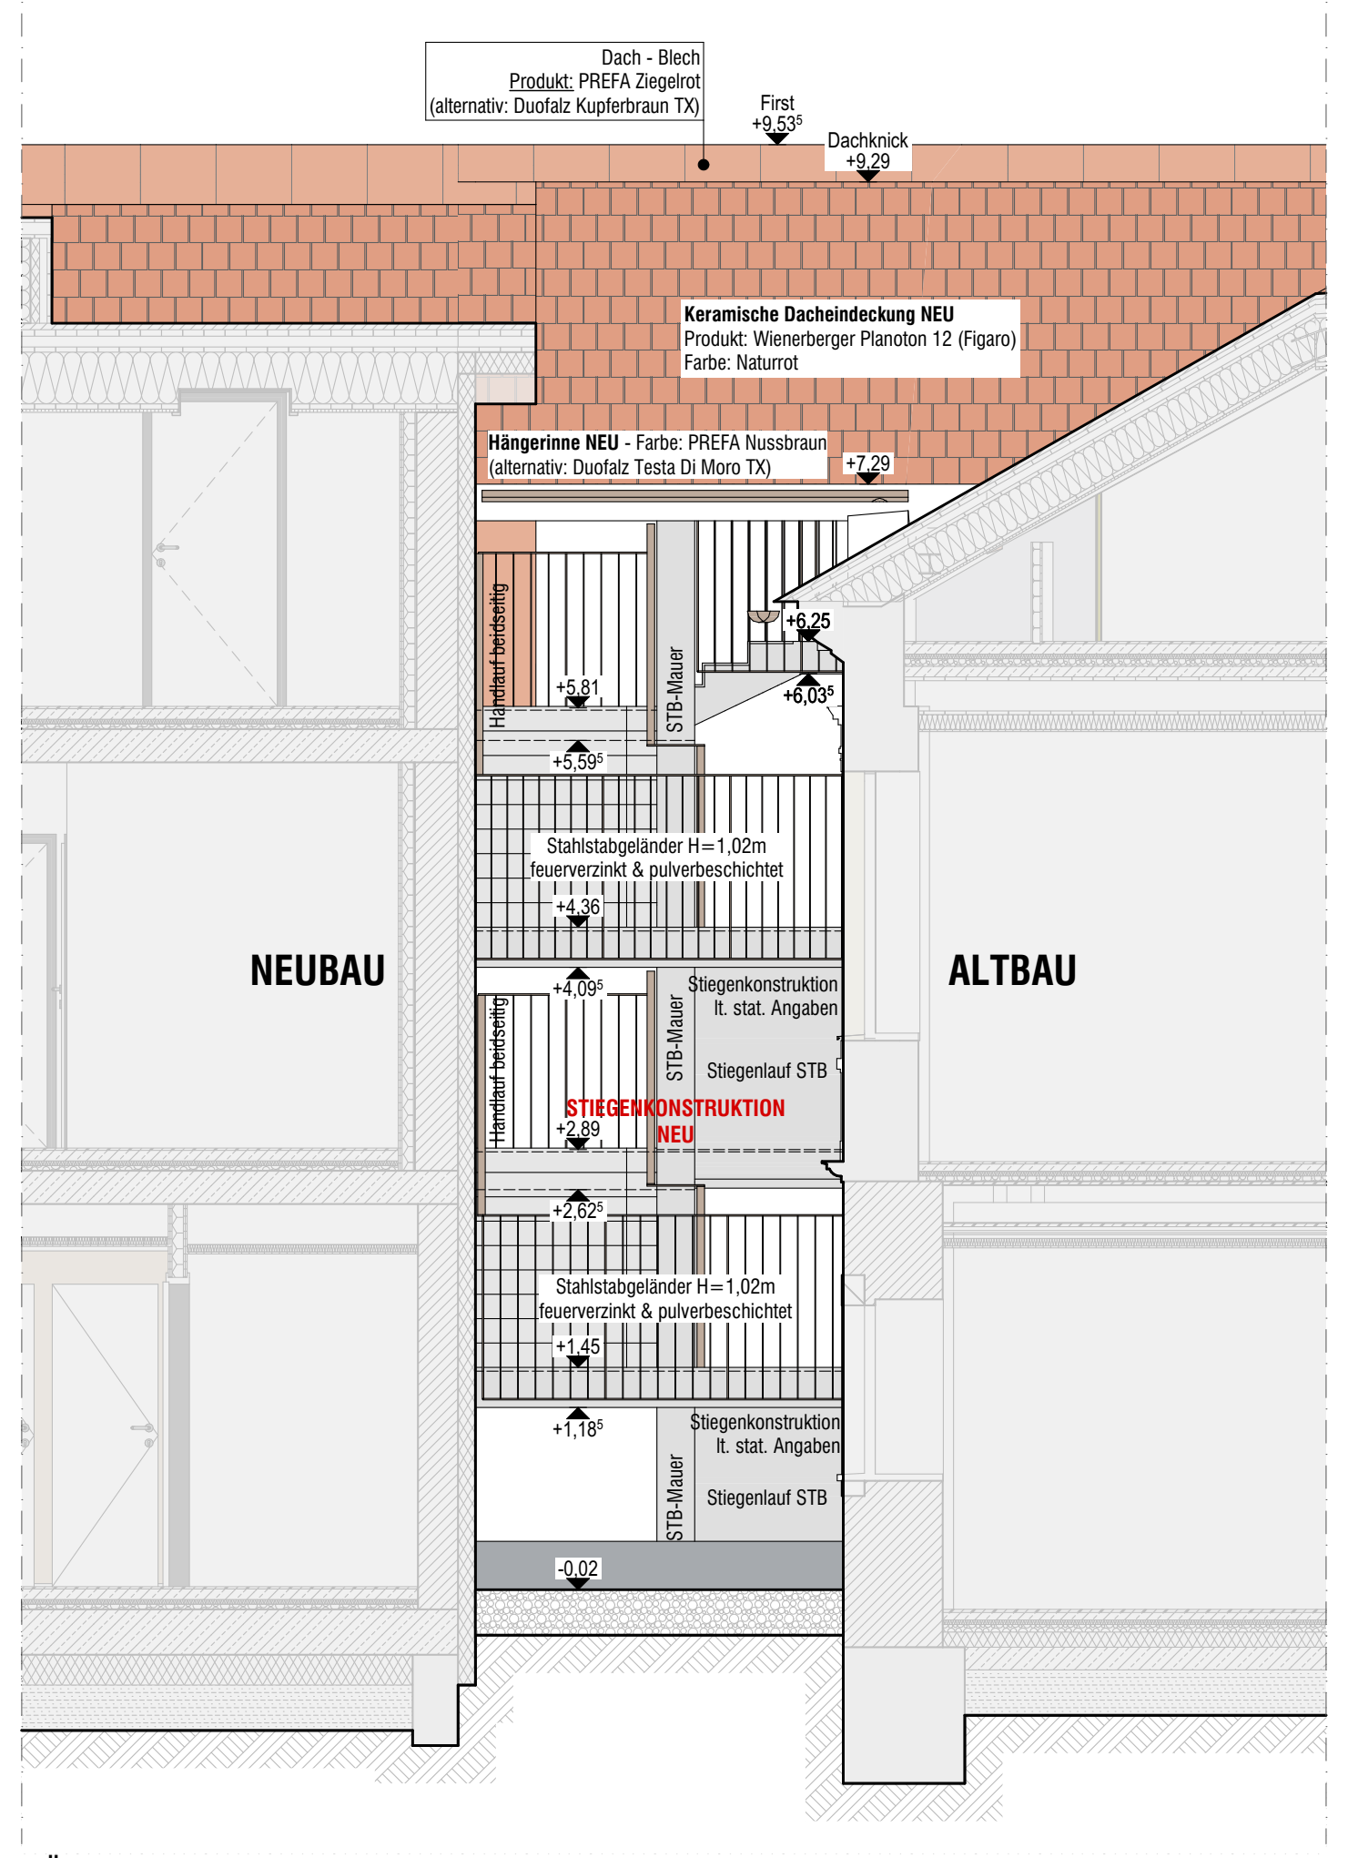
Dach - Blech
Produkt: PREFA Ziegelrot
(alternativ: Duofalz Kupferbraun TX)
First
+9,53
Dachknick
+9,29
Keramische Dacheindeckung NEU
Produkt: Wienerberger Planoton 12 (Figaro)
Farbe: Naturrot
Hängerinne NEU - Farbe: PREFA Nussbraun
(alternativ: Duofalz Testa Di Moro TX)
+7,29
+6,25
+6,03
Handlauf beidseitig
STB-Mauer
+5,81
+5,59
Stahlstabgeländer H=1,02m
feuerverzinkt & pulverbeschichtet
+4,36
+4,09
NEUBAU
ALTBAU
Stiegenkonstruktion
lt. stat. Angaben
Stiegenlauf STB
STIEGENKONSTRUKTION NEU
+2,89
+2,62
+1,45
+1,18
-0,02

SÜDANSICHT Stiegenhaus | 1:50

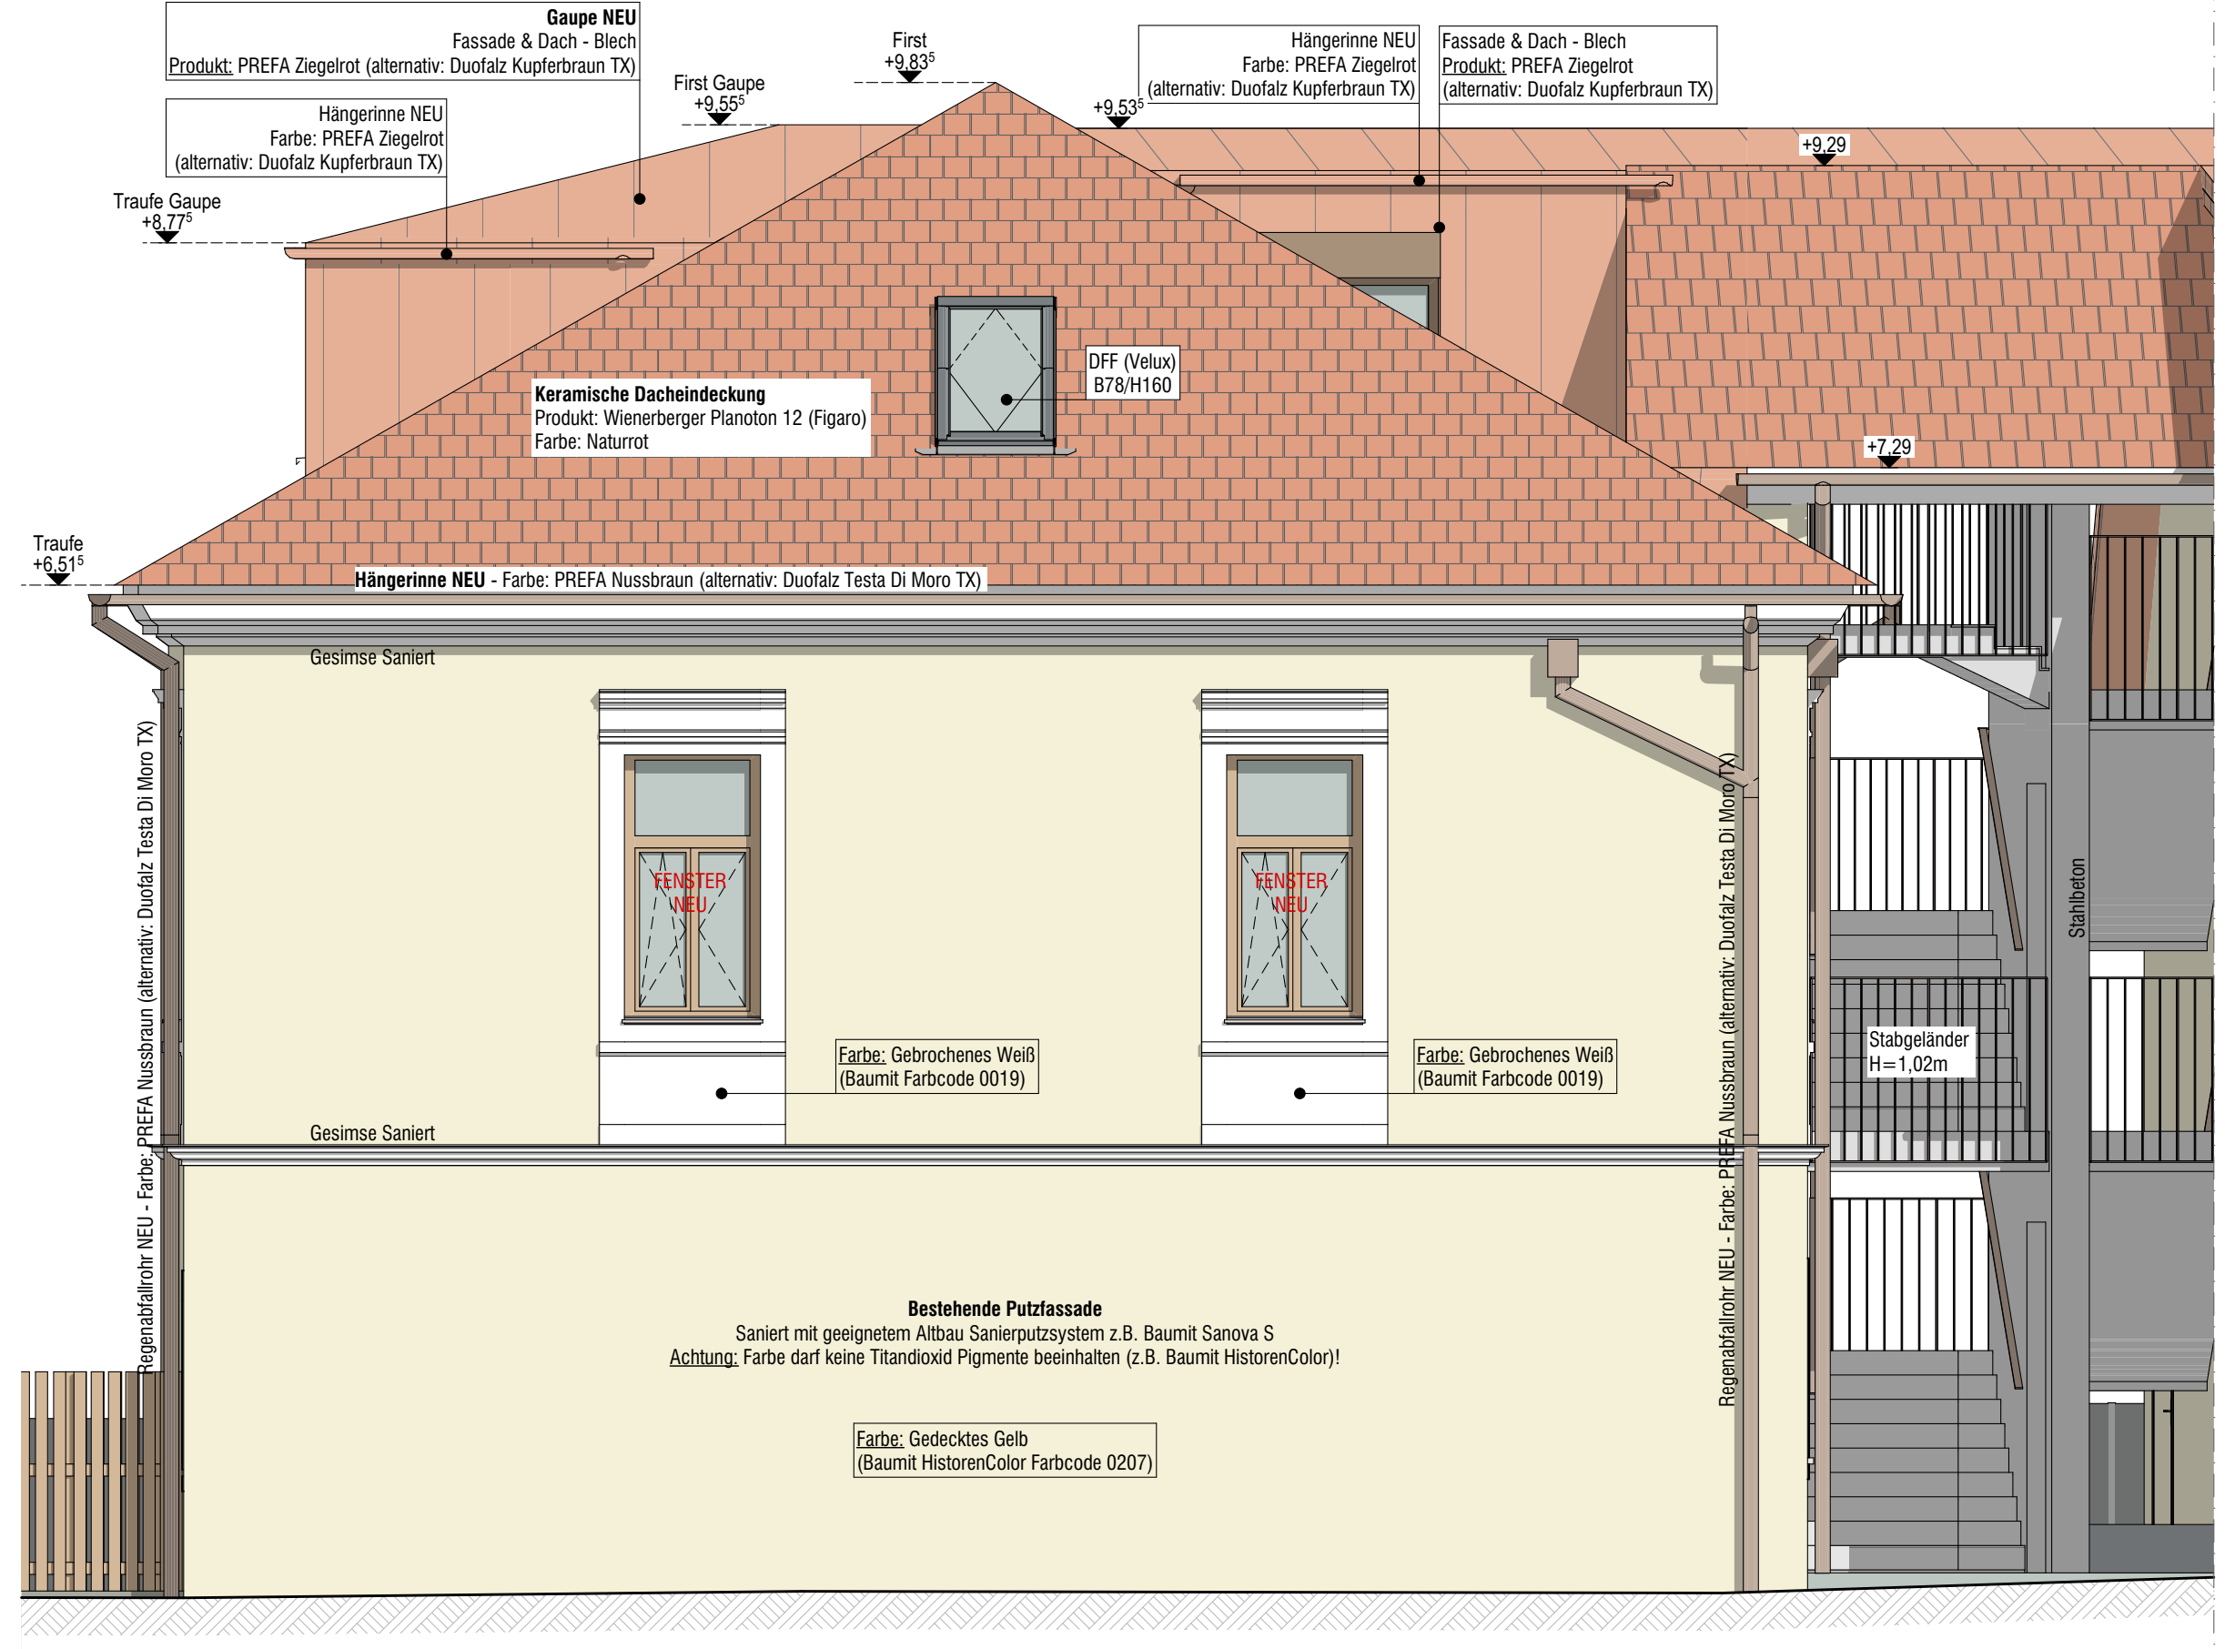
Gaupe NEU
Fassade & Dach - Blech
Produkt: PREFA Ziegelrot (alternativ: Duofalz Kupferbraun TX)
Hängerinne NEU
Farbe: PREFA Ziegelrot
(alternativ: Duofalz Kupferbraun TX)
Traufe Gaupe
+8,77
First Gaupe
+9,55
First
+9,83
+9,53
Fassade & Dach - Blech
Produkt: PREFA Ziegelrot
(alternativ: Duofalz Kupferbraun TX)
+9,29
Keramische Dacheindeckung
Produkt: Wienerberger Planoton 12 (Figaro)
Farbe: Naturrot
DFF (Velux)
B78/H160
+7,29
Traufe
+6,51
Hängerinne NEU - Farbe: PREFA Nussbraun (alternativ: Duofalz Testa Di Moro TX)
Gesimse Saniert
Regenabfallrohr NEU - Farbe: PREFA Nussbraun (alternativ: Duofalz Testa Di Moro TX)
FENSTER NEU
Farbe: Gebrochenes Weiß
(Baumit Farbcode 0019)
Stahlbeton
Stabgeländer
H=1,02m
Bestehende Putzfassade
Saniert mit geeignetem Altbau Sanierputzsystem z.B. Baumit Sanova S
Achtung: Farbe darf keine Titandioxid Pigmente beinhalten (z.B. Baumit HistorenColor)!
Farbe: Gedecktes Gelb
(Baumit HistorenColor Farbcode 0207)

NORDANSICHT Altbau | 1:50

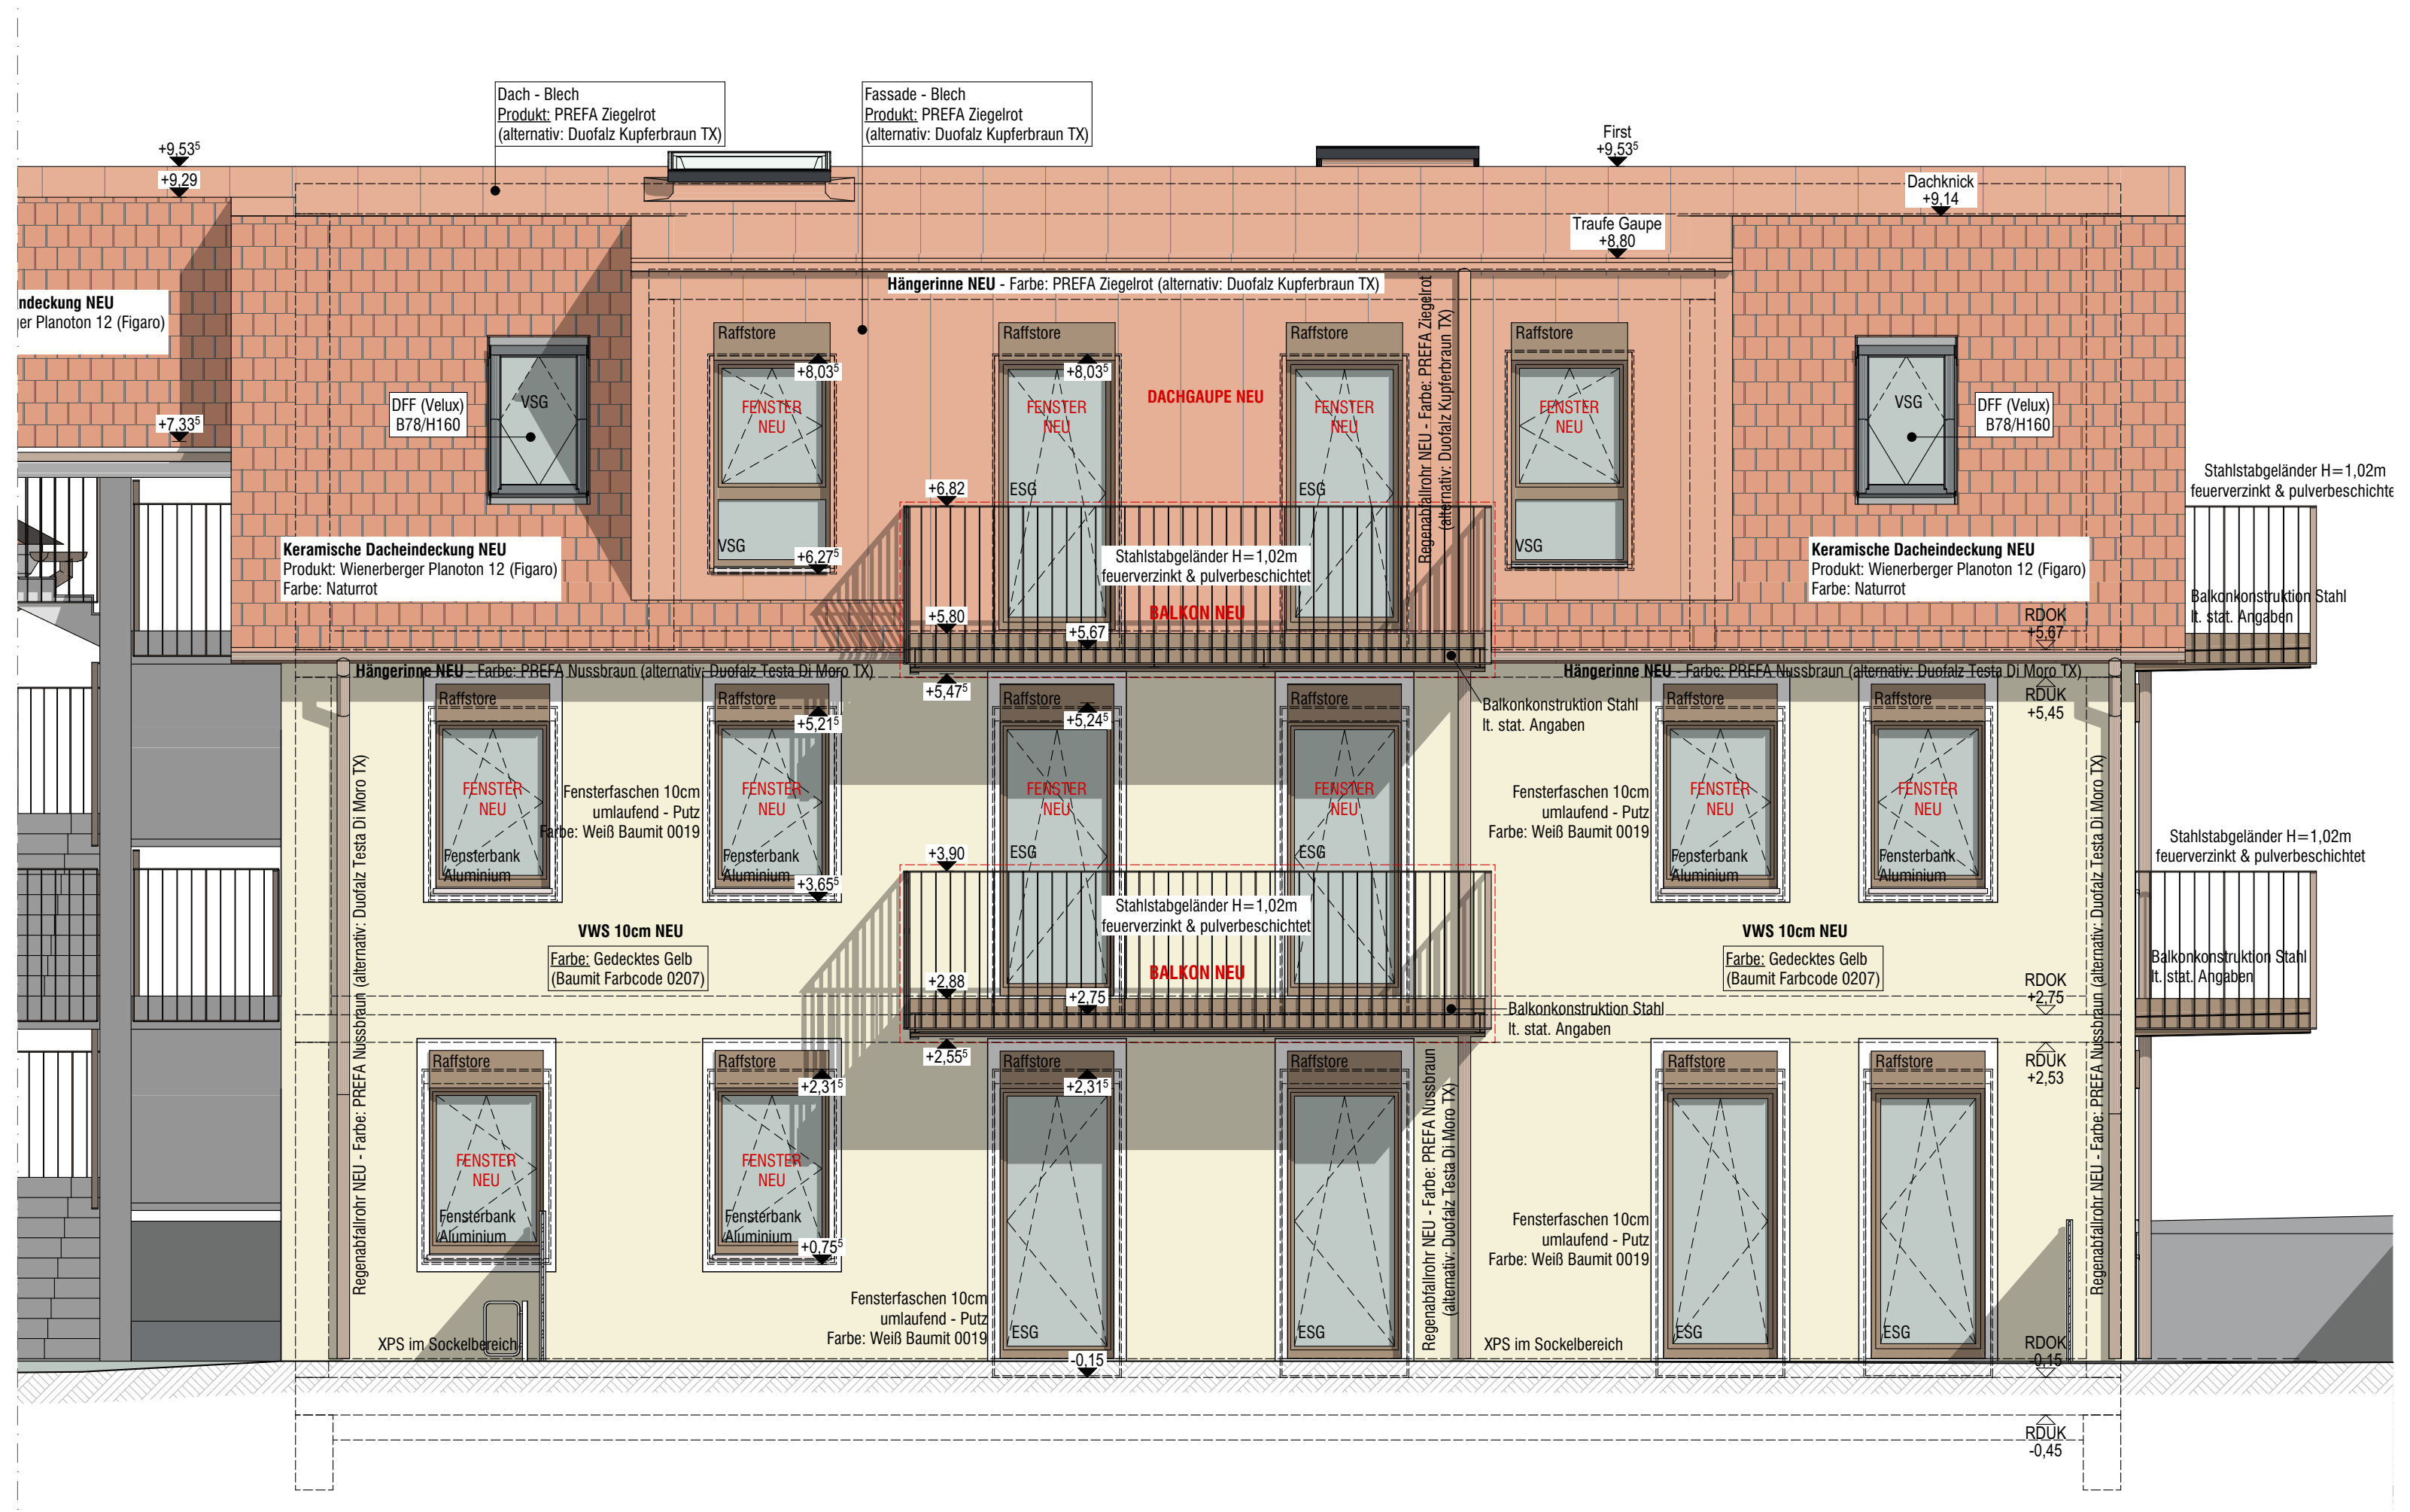
Dach - Blech
Produkt: PREFA Ziegelrot
(alternativ: Duofalz Kupferbraun TX)
Fassade - Blech
Produkt: PREFA Ziegelrot
(alternativ: Duofalz Kupferbraun TX)
+9,53
+9,29
First
Dachknick
+9,14
Traufe Gaupe
+8,80
Hängerinne NEU - Farbe: PREFA Ziegelrot (alternativ: Duofalz Kupferbraun TX)
Keramische Dacheindeckung NEU
Produkt: Wienerberger Planoton 12 (Figaro)
Farbe: Naturrot
+7,33
DFF (Velux)
B78/H160
VSG
Raffstore
FENSTER NEU
DACHGAUPE NEU
ESG
+8,03
+6,27
+6,82
+5,80
+5,67
Stahlstabgeländer H=1,02m
feuerverzinkt & pulverbeschichtet
BALKON NEU
Regenabfallrohr NEU - Farbe: PREFA Ziegelrot (alternativ: Duofalz Kupferbraun TX)
Balkonkonstruktion Stahl
lt. stat. Angaben
RDOK
+5,67
Hängerinne NEU - Farbe: PREFA Nussbraun (alternativ: Duofalz Testa Di Moro TX)
RDUK
+5,45
+5,47
+5,21
+5,24
Fensterfaschen 10cm
umlaufend - Putz
Farbe: Weiß Baumit 0019
Fensterbank
Aluminium
+3,65
+3,90
VWS 10cm NEU
Farbe: Gedecktes Gelb
(Baumit Farbcode 0207)
+2,88
+2,75
+2,55
RDOK
+2,75
RDUK
+2,53
+2,31
+0,75
Regenabfallrohr NEU - Farbe: PREFA Nussbraun (alternativ: Duofalz Testa Di Moro TX)
XPS im Sockelbereich
-0,15
RDOK
-0,15
RDUK
-0,45

NORDANSICHT Neubau | 1:50

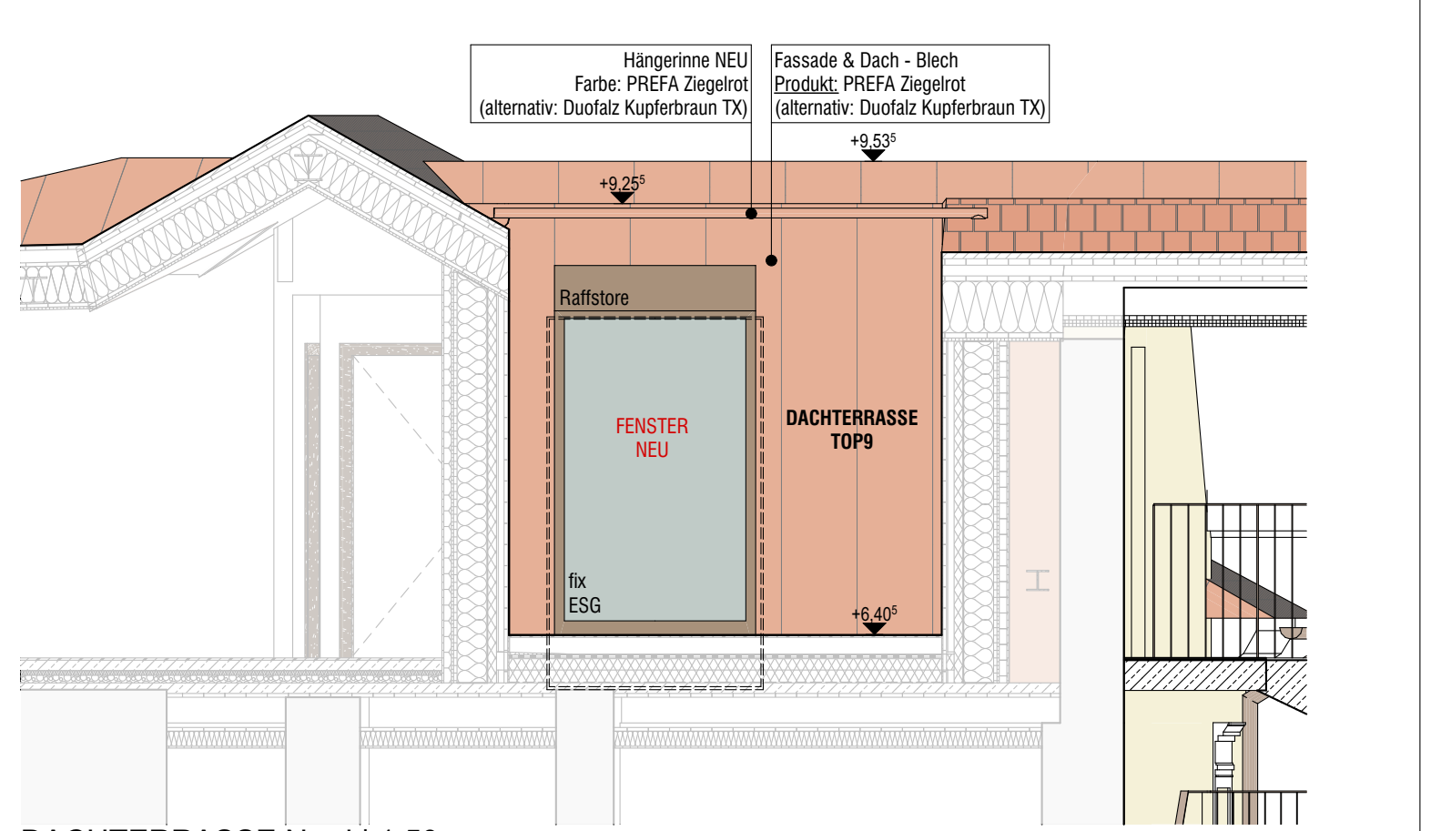
Hängerinne NEU
Farbe: PREFA Ziegelrot
(alternativ: Duofalz Kupferbraun TX)
Fassade & Dach - Blech
Produkt: PREFA Ziegelrot
(alternativ: Duofalz Kupferbraun TX)
+9,53
+9,25
Raffstore
FENSTER NEU
DACHTERRASSE TOP9
fix
ESG
+6,40

DACHTERRASSE Nord | 1:50

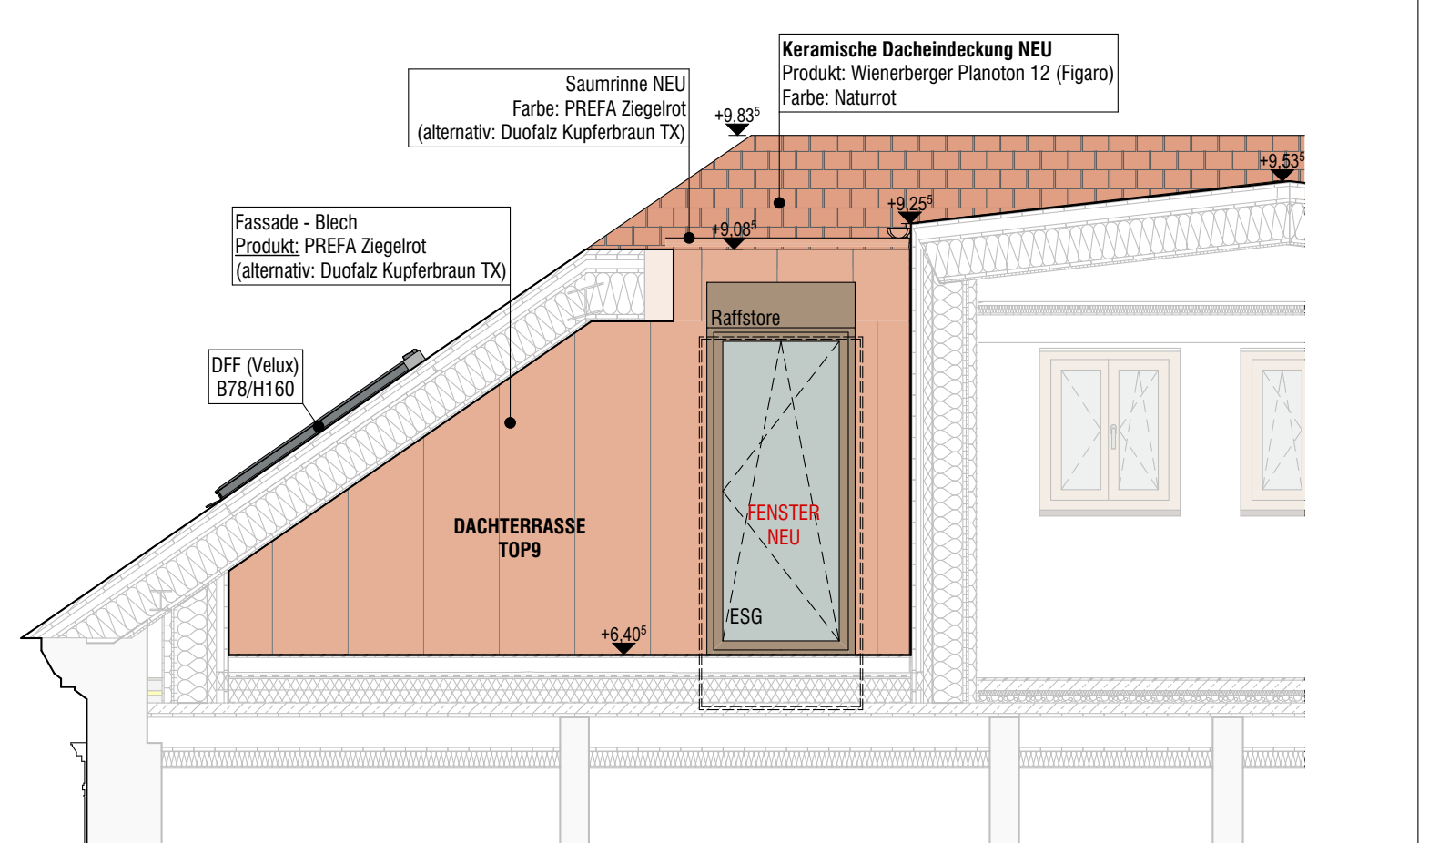
Keramische Dacheindeckung NEU
Produkt: Wienerberger Planoton 12 (Figaro)
Farbe: Naturrot
Saumrinne NEU
Farbe: PREFA Ziegelrot
(alternativ: Duofalz Kupferbraun TX)
+9,83
+9,53
+9,25
+9,08
Fassade - Blech
Produkt: PREFA Ziegelrot
(alternativ: Duofalz Kupferbraun TX)
DFF (Velux)
B78/H160
Raffstore
DACHTERRASSE TOP9
FENSTER NEU
ESG
+6,40

DACHTERRASSE West | 1:50

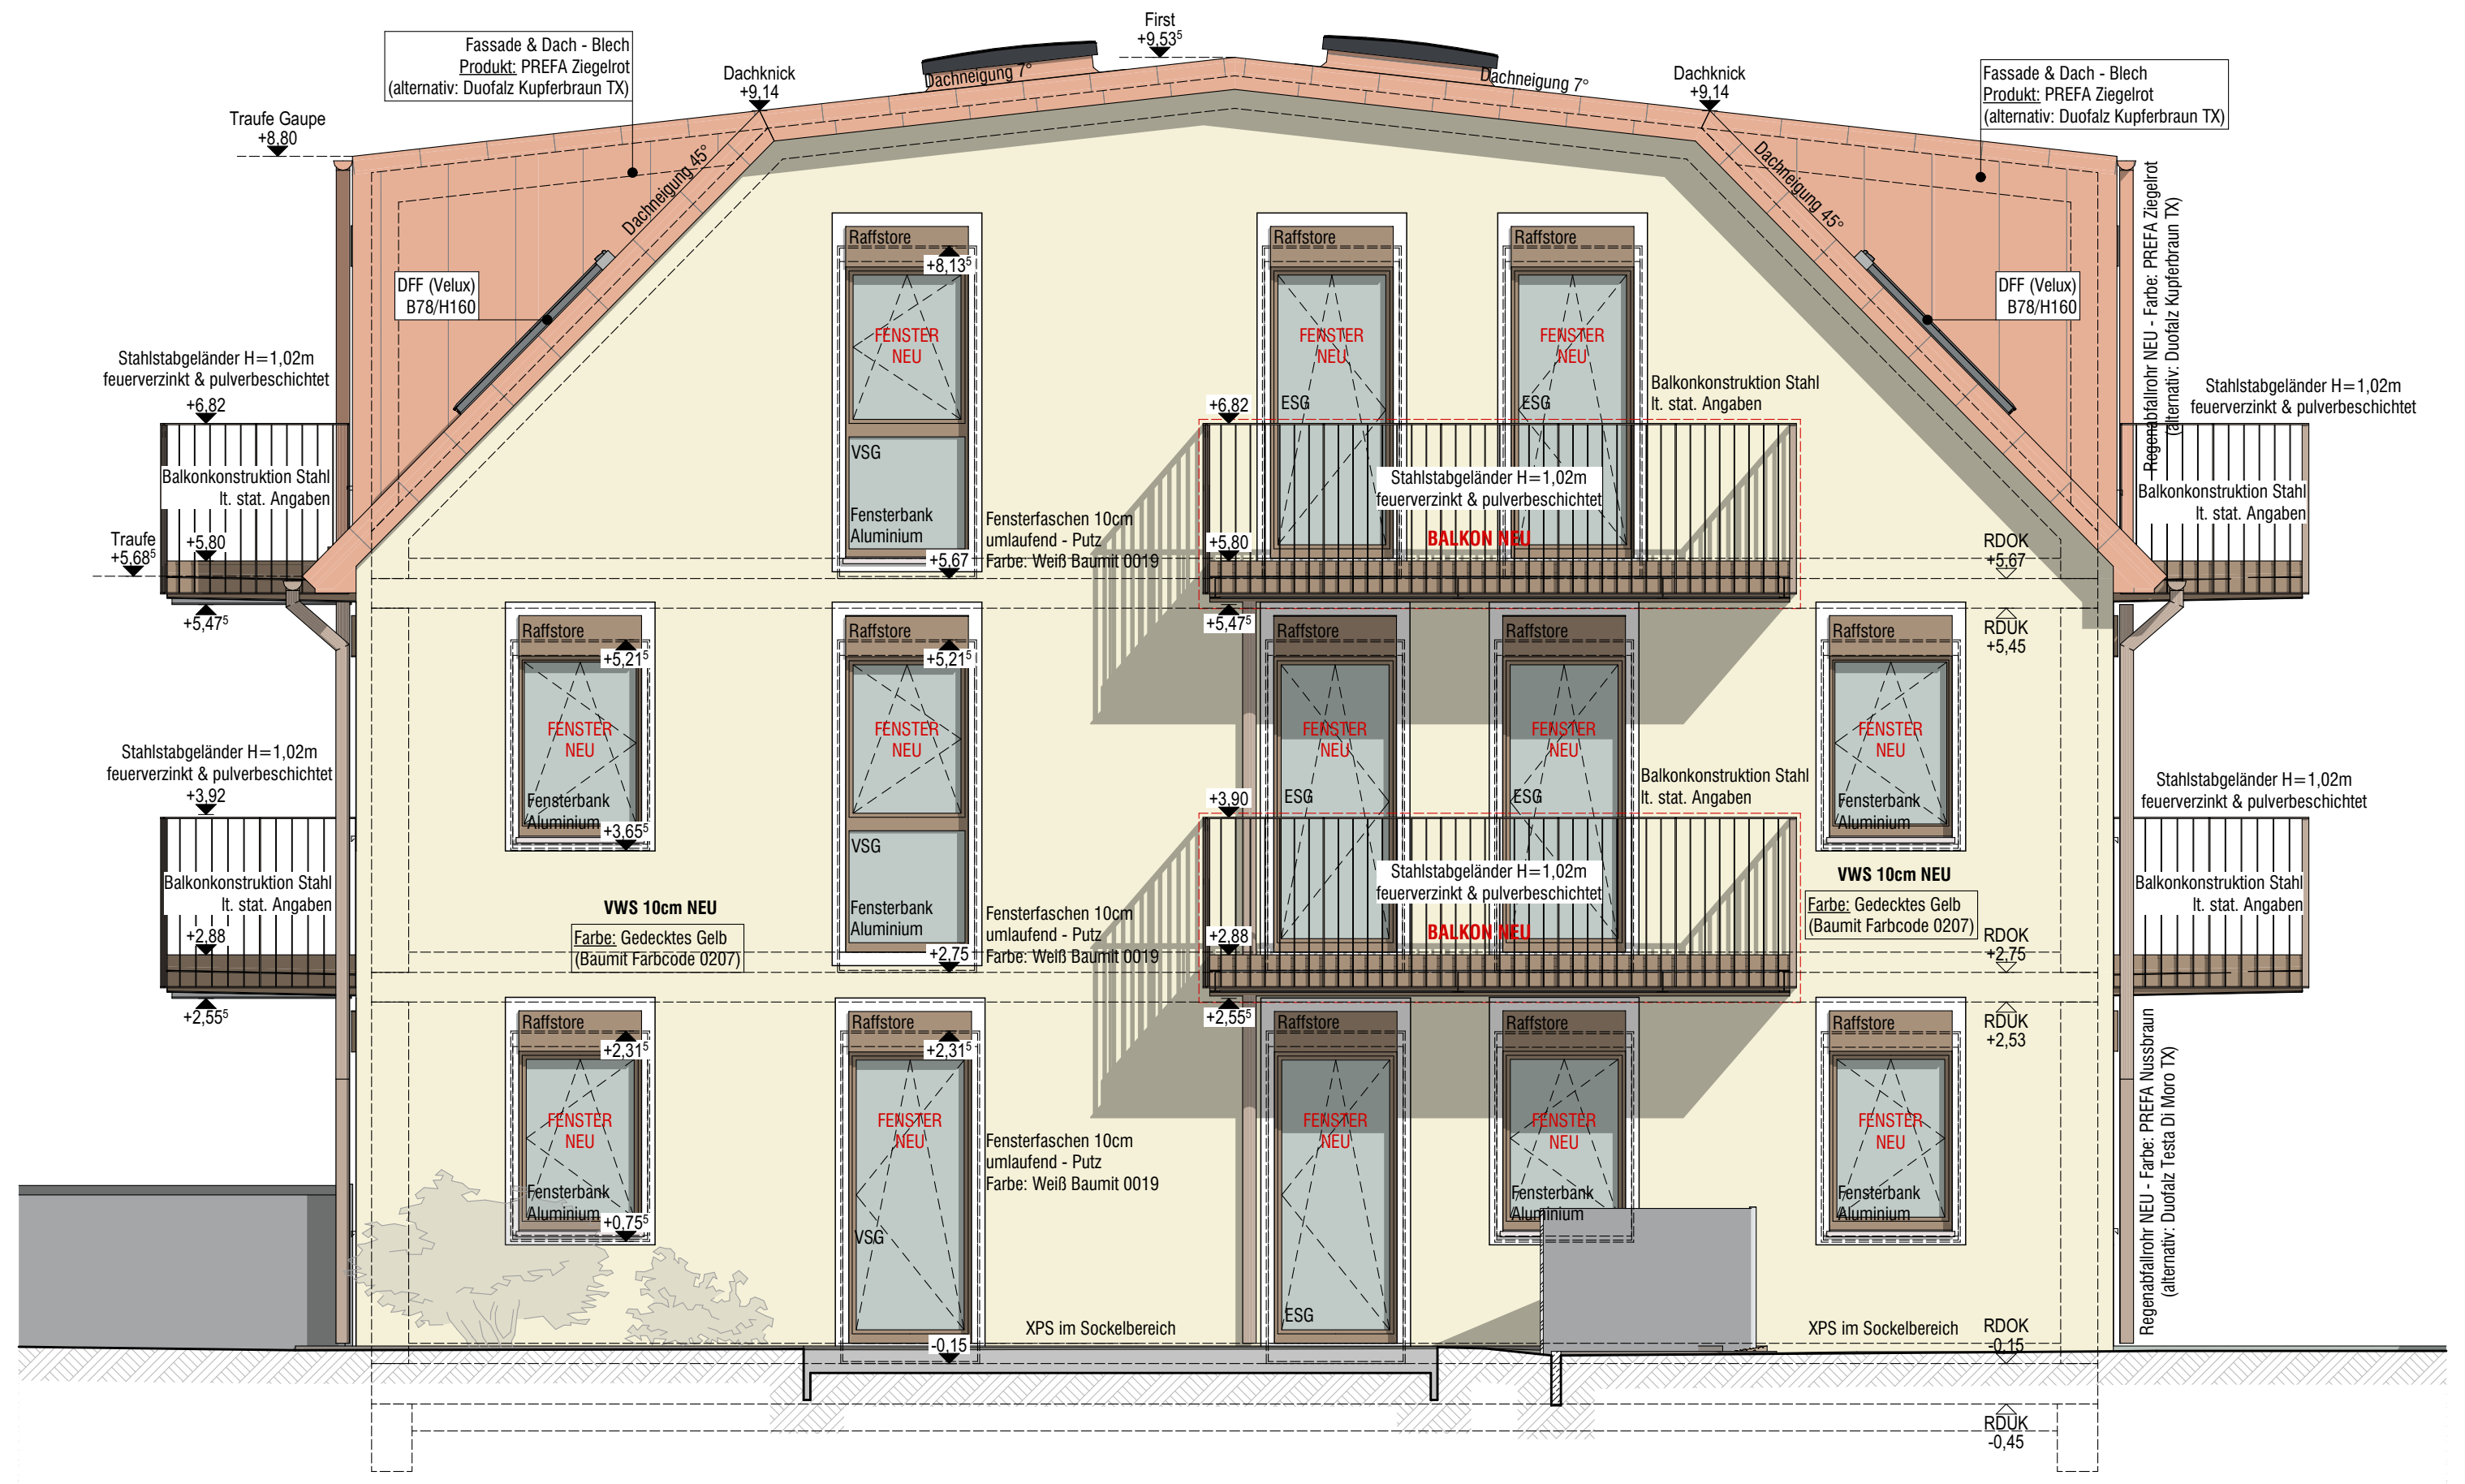
Fassade & Dach - Blech
Produkt: PREFA Ziegelrot
(alternativ: Duofalz Kupferbraun TX)
First
+9,53
Dachknick
+9,14
Dachneigung 7°
Dachneigung 45°
Traufe Gaupe
+8,80
DFF (Velux)
B78/H160
Raffstore
FENSTER NEU
VSG
ESG
Fensterbank
Aluminium
Stahlstabgeländer H=1,02m
feuerverzinkt & pulverbeschichtet
Balkonkonstruktion Stahl
lt. stat. Angaben
Traufe
+5,68
+8,13
+6,82
+5,80
+5,67
+5,47
+5,21
+3,92
+3,90
+3,65
+2,88
+2,75
+2,55
+2,31
+0,75
BALKON NEU
Fensterfaschen 10cm
umlaufend - Putz
Farbe: Weiß Baumit 0019
VWS 10cm NEU
Farbe: Gedecktes Gelb
(Baumit Farbcode 0207)
RDOK
+5,67
RDUK
+5,45
RDOK
+2,75
RDUK
+2,53
XPS im Sockelbereich
-0,15
RDOK
-0,15
RDUK
-0,45
Regenabfallrohr NEU - Farbe: PREFA Ziegelrot (alternativ: Duofalz Kupferbraun TX)
Regenabfallrohr NEU - Farbe: PREFA Nussbraun (alternativ: Duofalz Testa Di Moro TX)

WESTANSICHT Neubau | 1:50

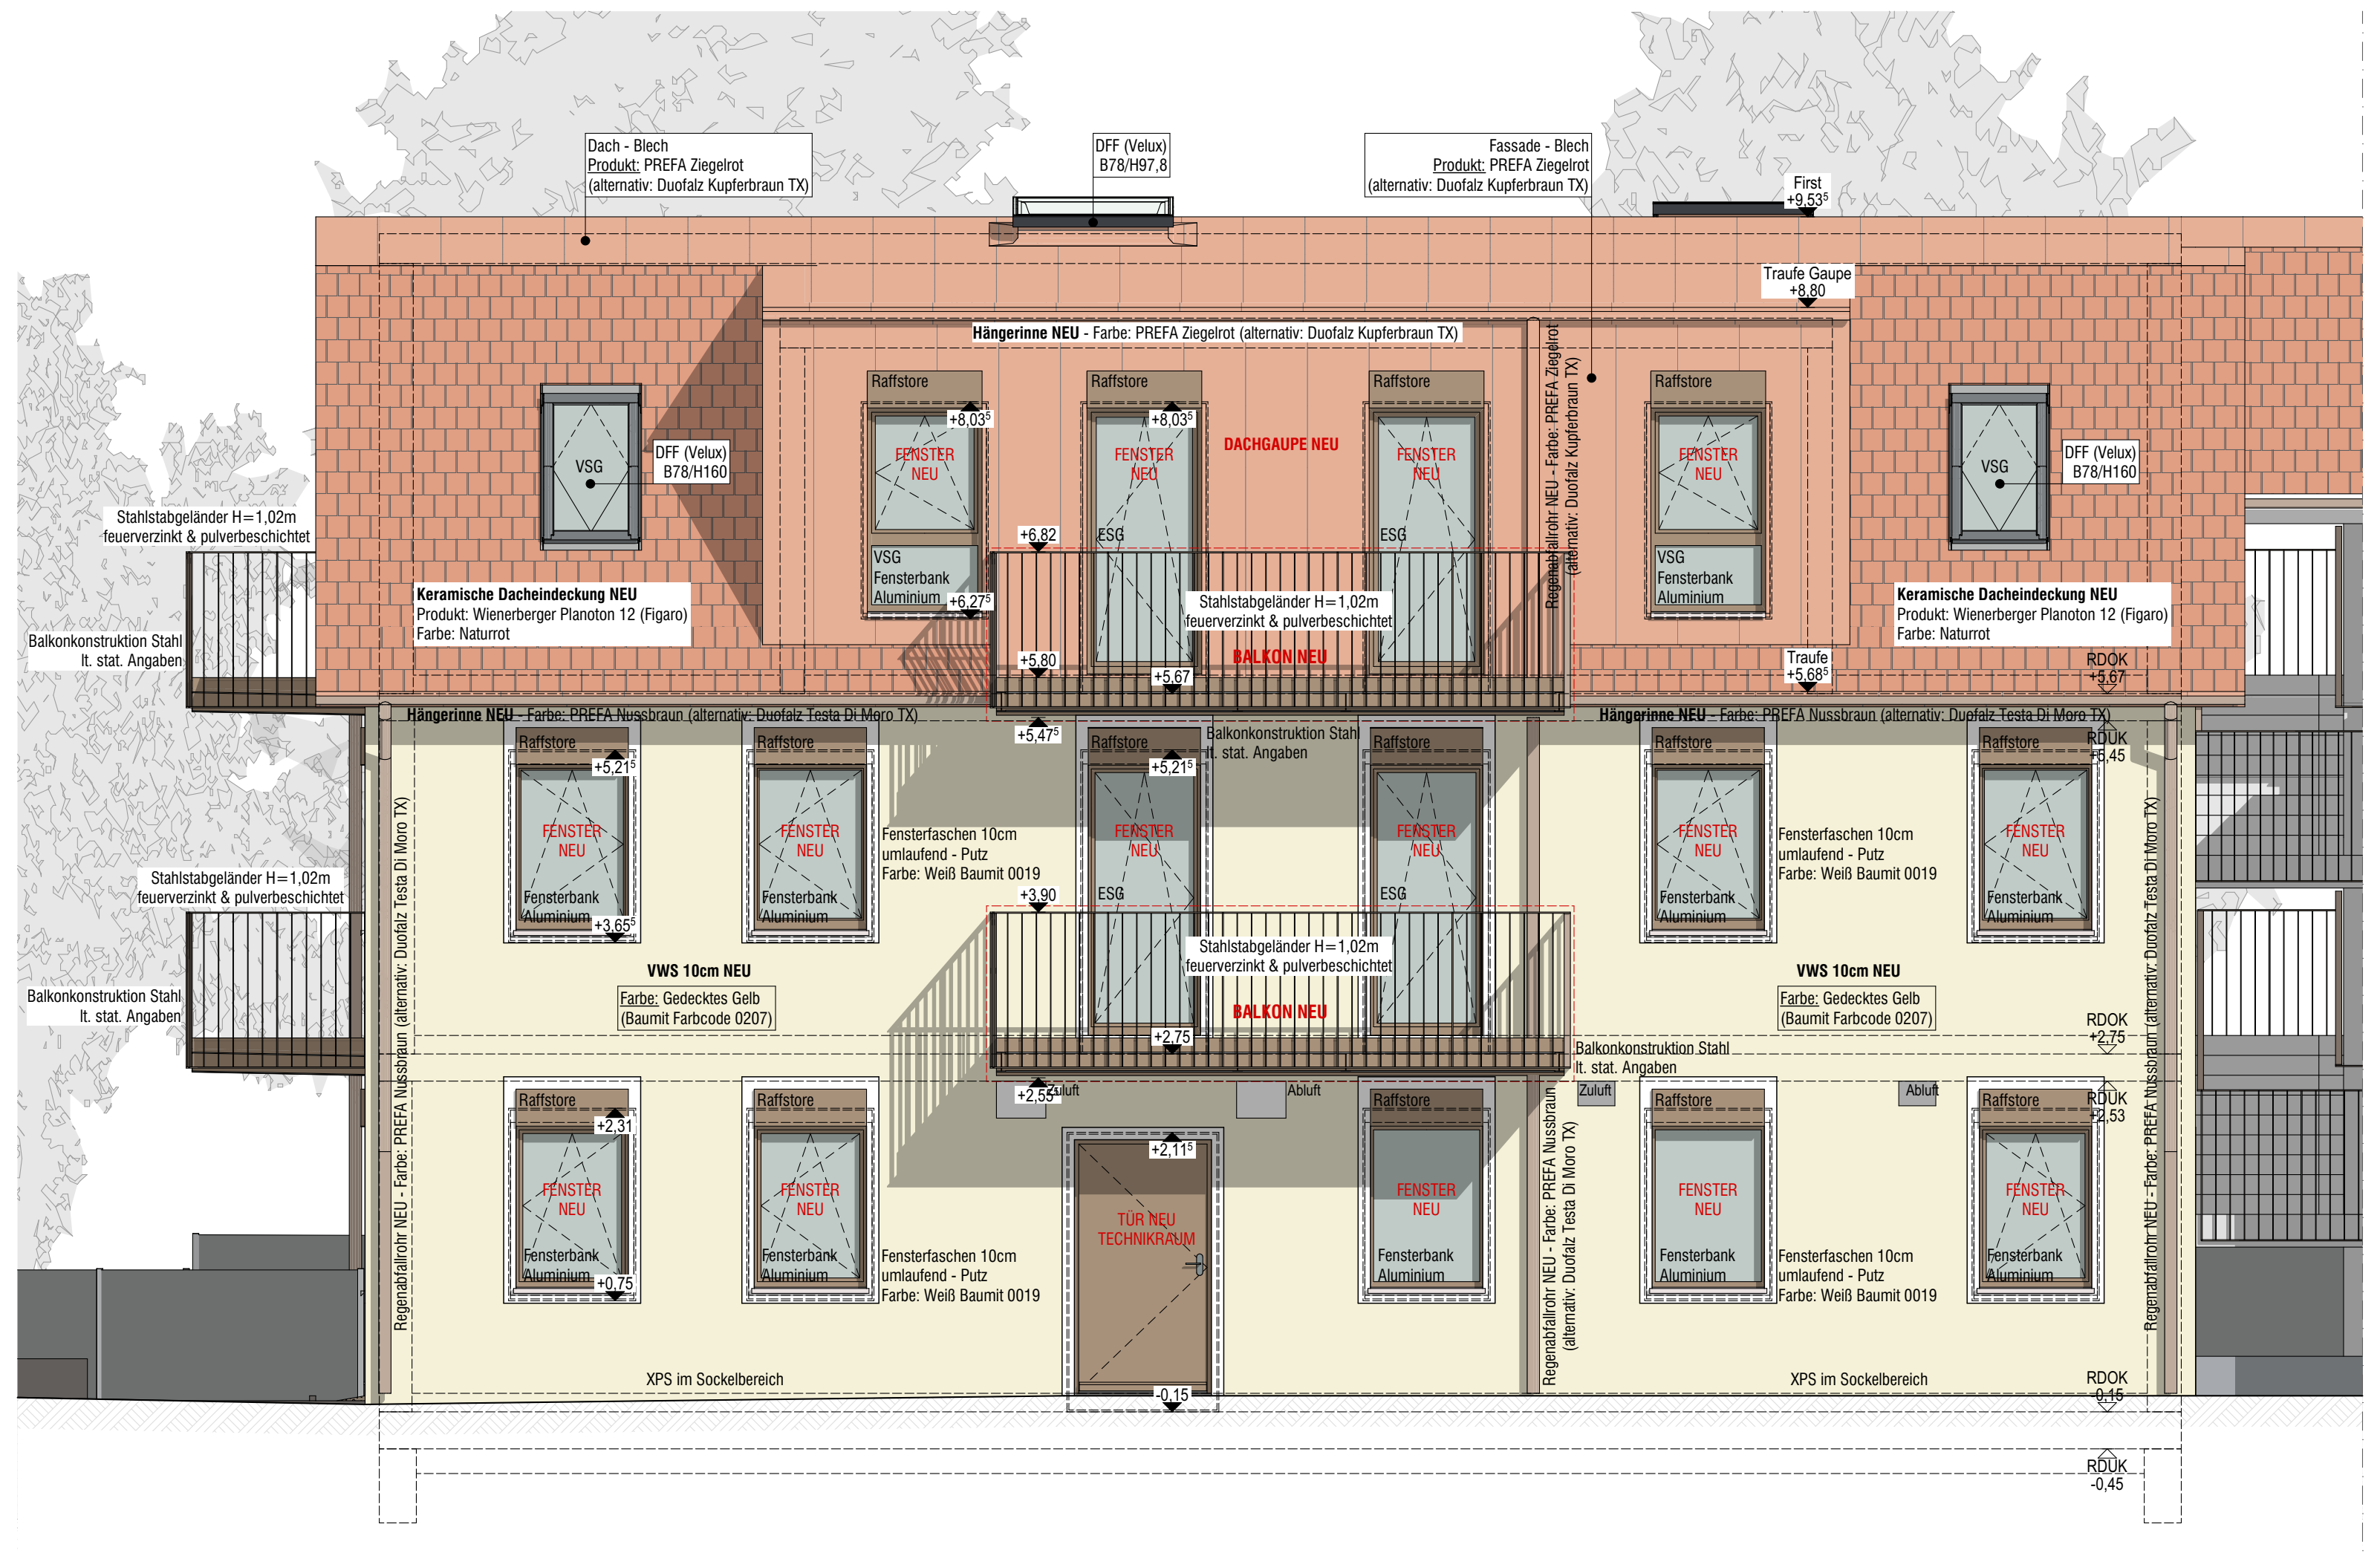
Dach - Blech
Produkt: PREFA Ziegelrot
(alternativ: Duofalz Kupferbraun TX)
DFF (Velux)
B78/H97,8
Fassade - Blech
Produkt: PREFA Ziegelrot
(alternativ: Duofalz Kupferbraun TX)
First
+9,53
Traufe Gaupe
+8,80
Hängerinne NEU - Farbe: PREFA Ziegelrot (alternativ: Duofalz Kupferbraun TX)
Raffstore
FENSTER NEU
DACHGAUPE NEU
VSG
ESG
DFF (Velux)
B78/H160
Fensterbank
Aluminium
+8,03
+6,82
+6,27
+5,80
+5,67
Stahlstabgeländer H=1,02m
feuerverzinkt & pulverbeschichtet
BALKON NEU
Keramische Dacheindeckung NEU
Produkt: Wienerberger Planoton 12 (Figaro)
Farbe: Naturrot
Balkonkonstruktion Stahl
lt. stat. Angaben
Traufe
+5,68
RDOK
+5,67
Hängerinne NEU - Farbe: PREFA Nussbraun (alternativ: Duofalz Testa Di Moro TX)
RDUK
+5,45
+5,47
+5,21
Fensterfaschen 10cm
umlaufend - Putz
Farbe: Weiß Baumit 0019
+3,90
+3,65
VWS 10cm NEU
Farbe: Gedecktes Gelb
(Baumit Farbcode 0207)
RDOK
+2,75
+2,55
Zuluft
Abluft
RDUK
+2,53
+2,31
+2,11
TÜR NEU
TECHNIKRAUM
+0,75
XPS im Sockelbereich
-0,15
RDOK
-0,15
RDUK
-0,45
Regenabfallrohr NEU - Farbe: PREFA Nussbraun (alternativ: Duofalz Testa Di Moro TX)
Regenabfallrohr NEU - Farbe: PREFA Ziegelrot (alternativ: Duofalz Kupferbraun TX)

SÜDANSICHT Neubau | 1:50

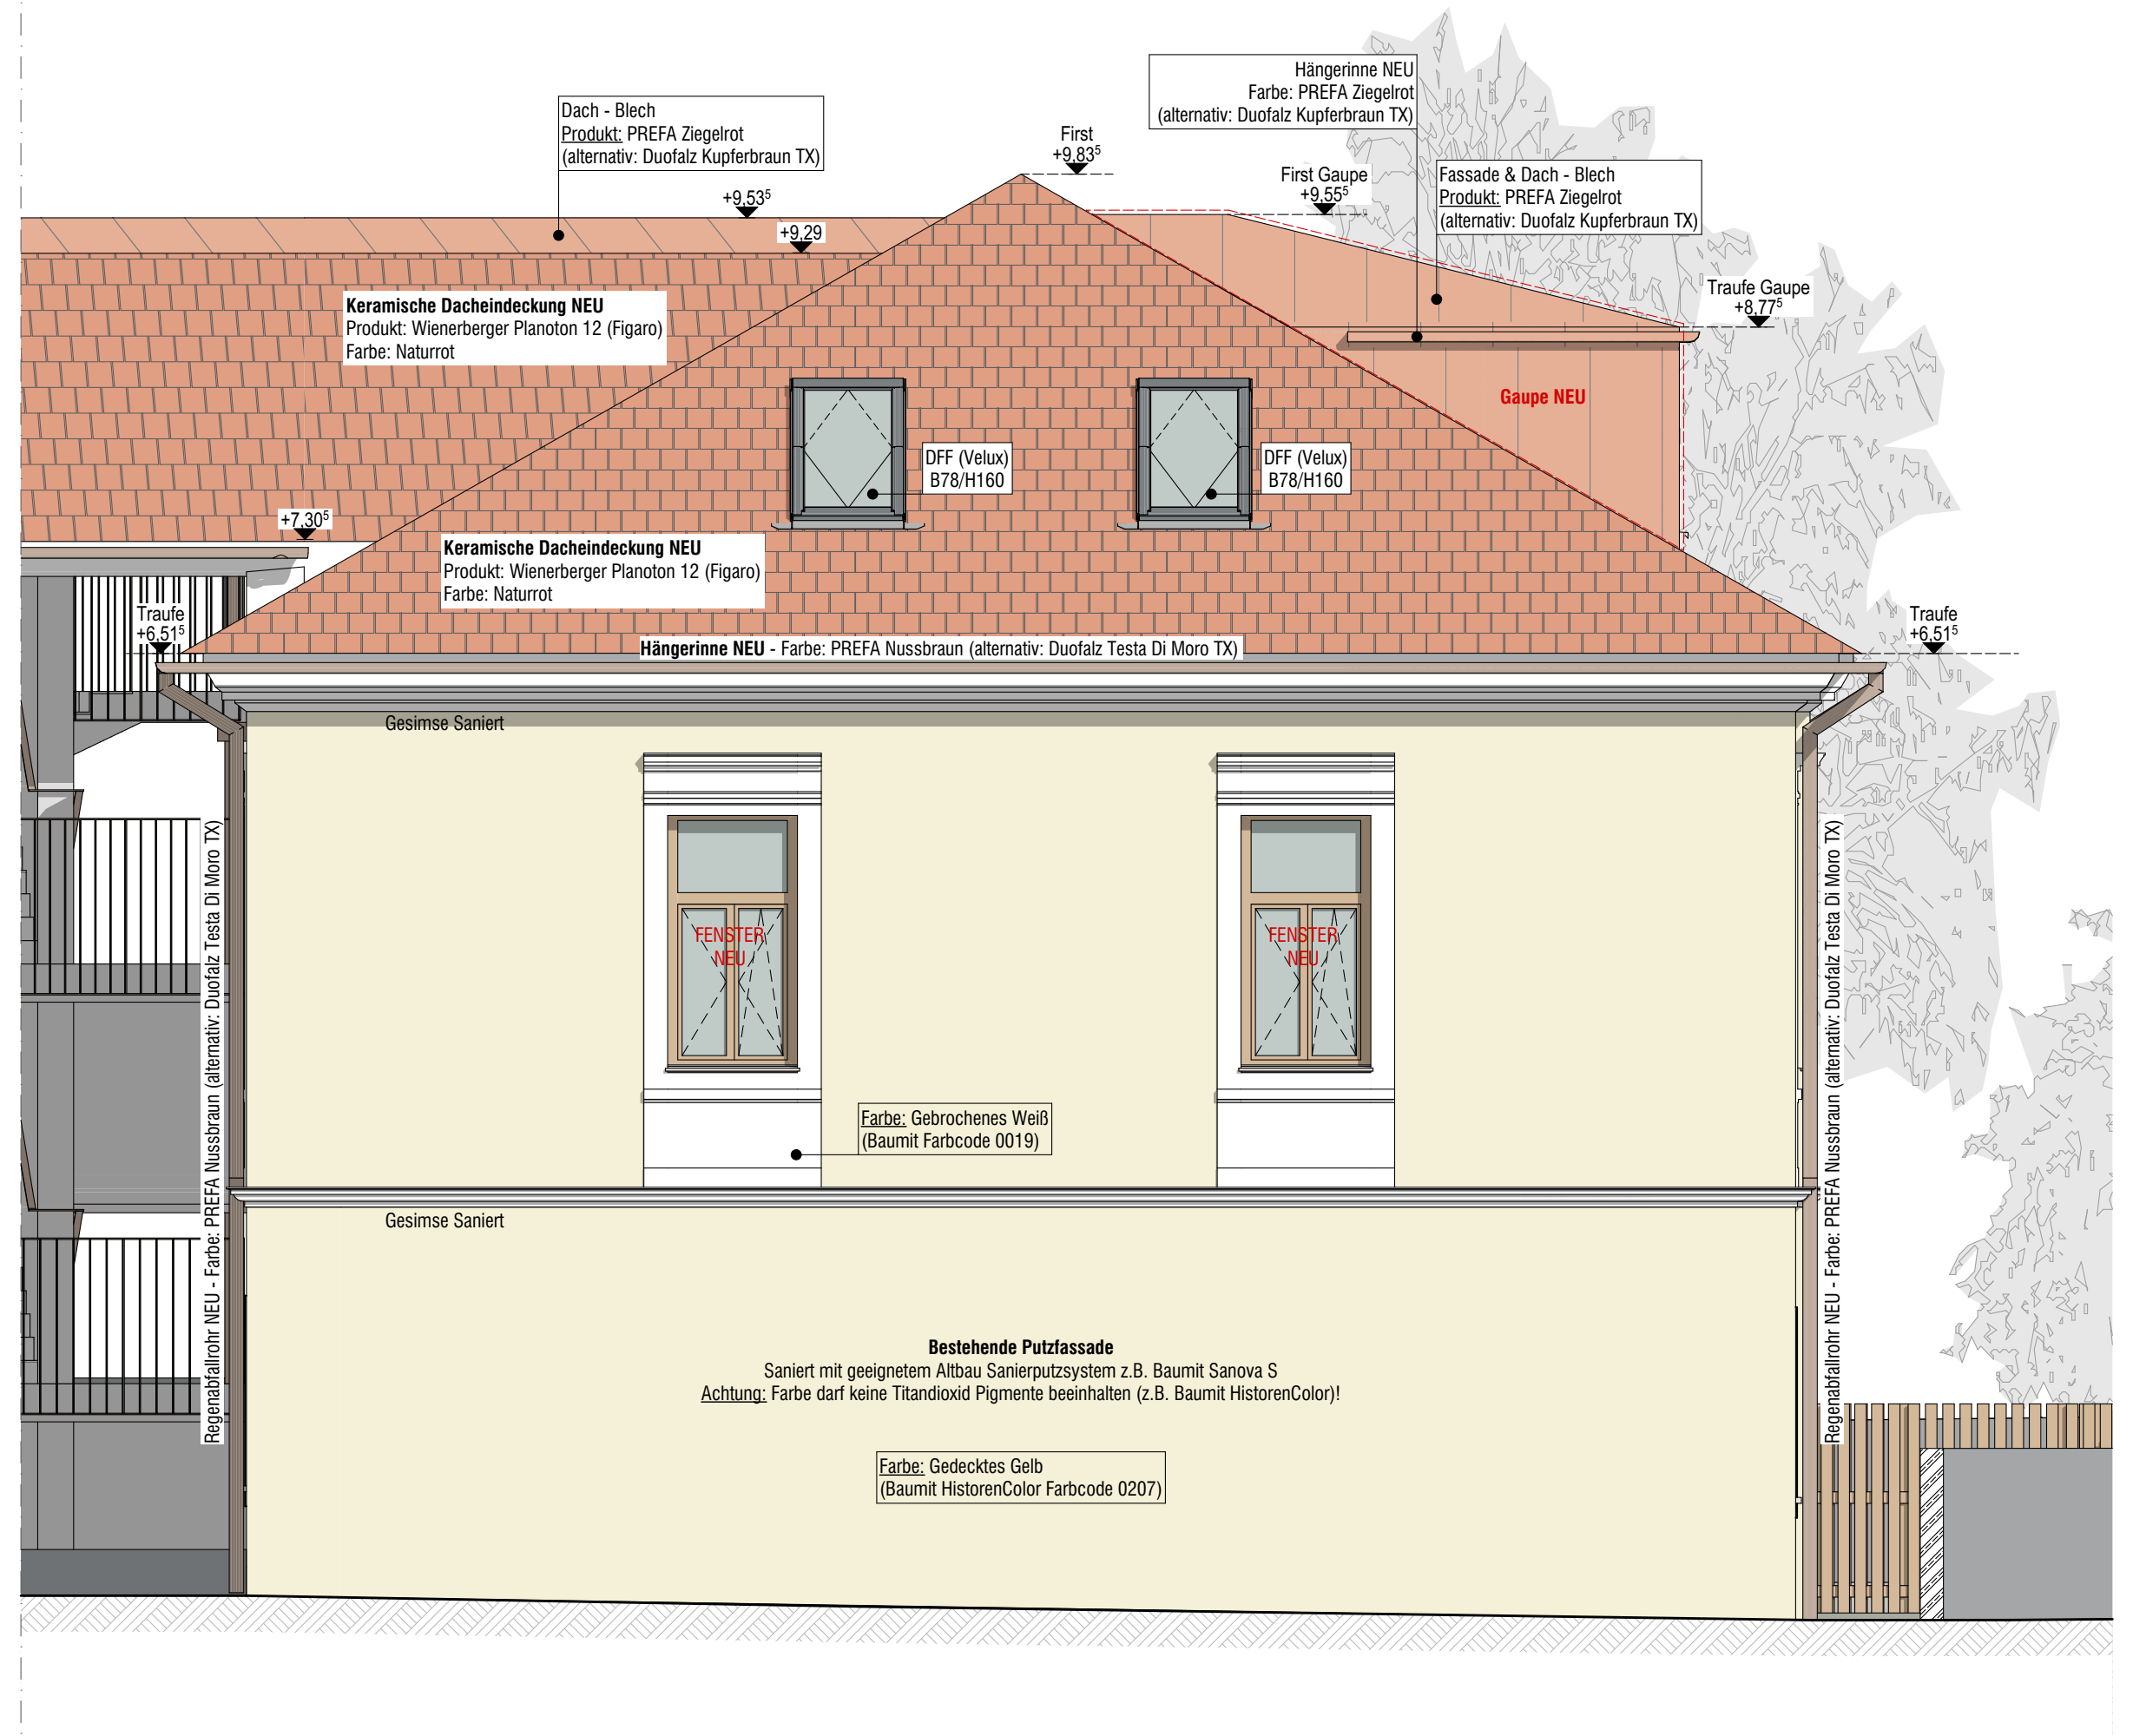
Dach - Blech
Produkt: PREFA Ziegelrot
(alternativ: Duofalz Kupferbraun TX)
Hängerinne NEU
Farbe: PREFA Ziegelrot
(alternativ: Duofalz Kupferbraun TX)
First
+9,83
First Gaupe
+9,55
Fassade & Dach - Blech
Produkt: PREFA Ziegelrot
(alternativ: Duofalz Kupferbraun TX)
+9,53
+9,29
Traufe Gaupe
+8,77
Keramische Dacheindeckung NEU
Produkt: Wienerberger Planoton 12 (Figaro)
Farbe: Naturrot
Gaupe NEU
DFF (Velux)
B78/H160
+7,30
Traufe
+6,51
Hängerinne NEU - Farbe: PREFA Nussbraun (alternativ: Duofalz Testa Di Moro TX)
Gesimse Saniert
FENSTER NEU
Farbe: Gebrochenes Weiß
(Baumit Farbcode 0019)
Regenabfallrohr NEU - Farbe: PREFA Nussbraun (alternativ: Duofalz Testa Di Moro TX)
Bestehende Putzfassade
Saniert mit geeignetem Altbau Sanierputzsystem z.B. Baumit Sanova S
Achtung: Farbe darf keine Titandioxid Pigmente beinhalten (z.B. Baumit HistorenColor)!
Farbe: Gedecktes Gelb
(Baumit HistorenColor Farbcode 0207)

SÜDANSICHT Altbau | 1:50

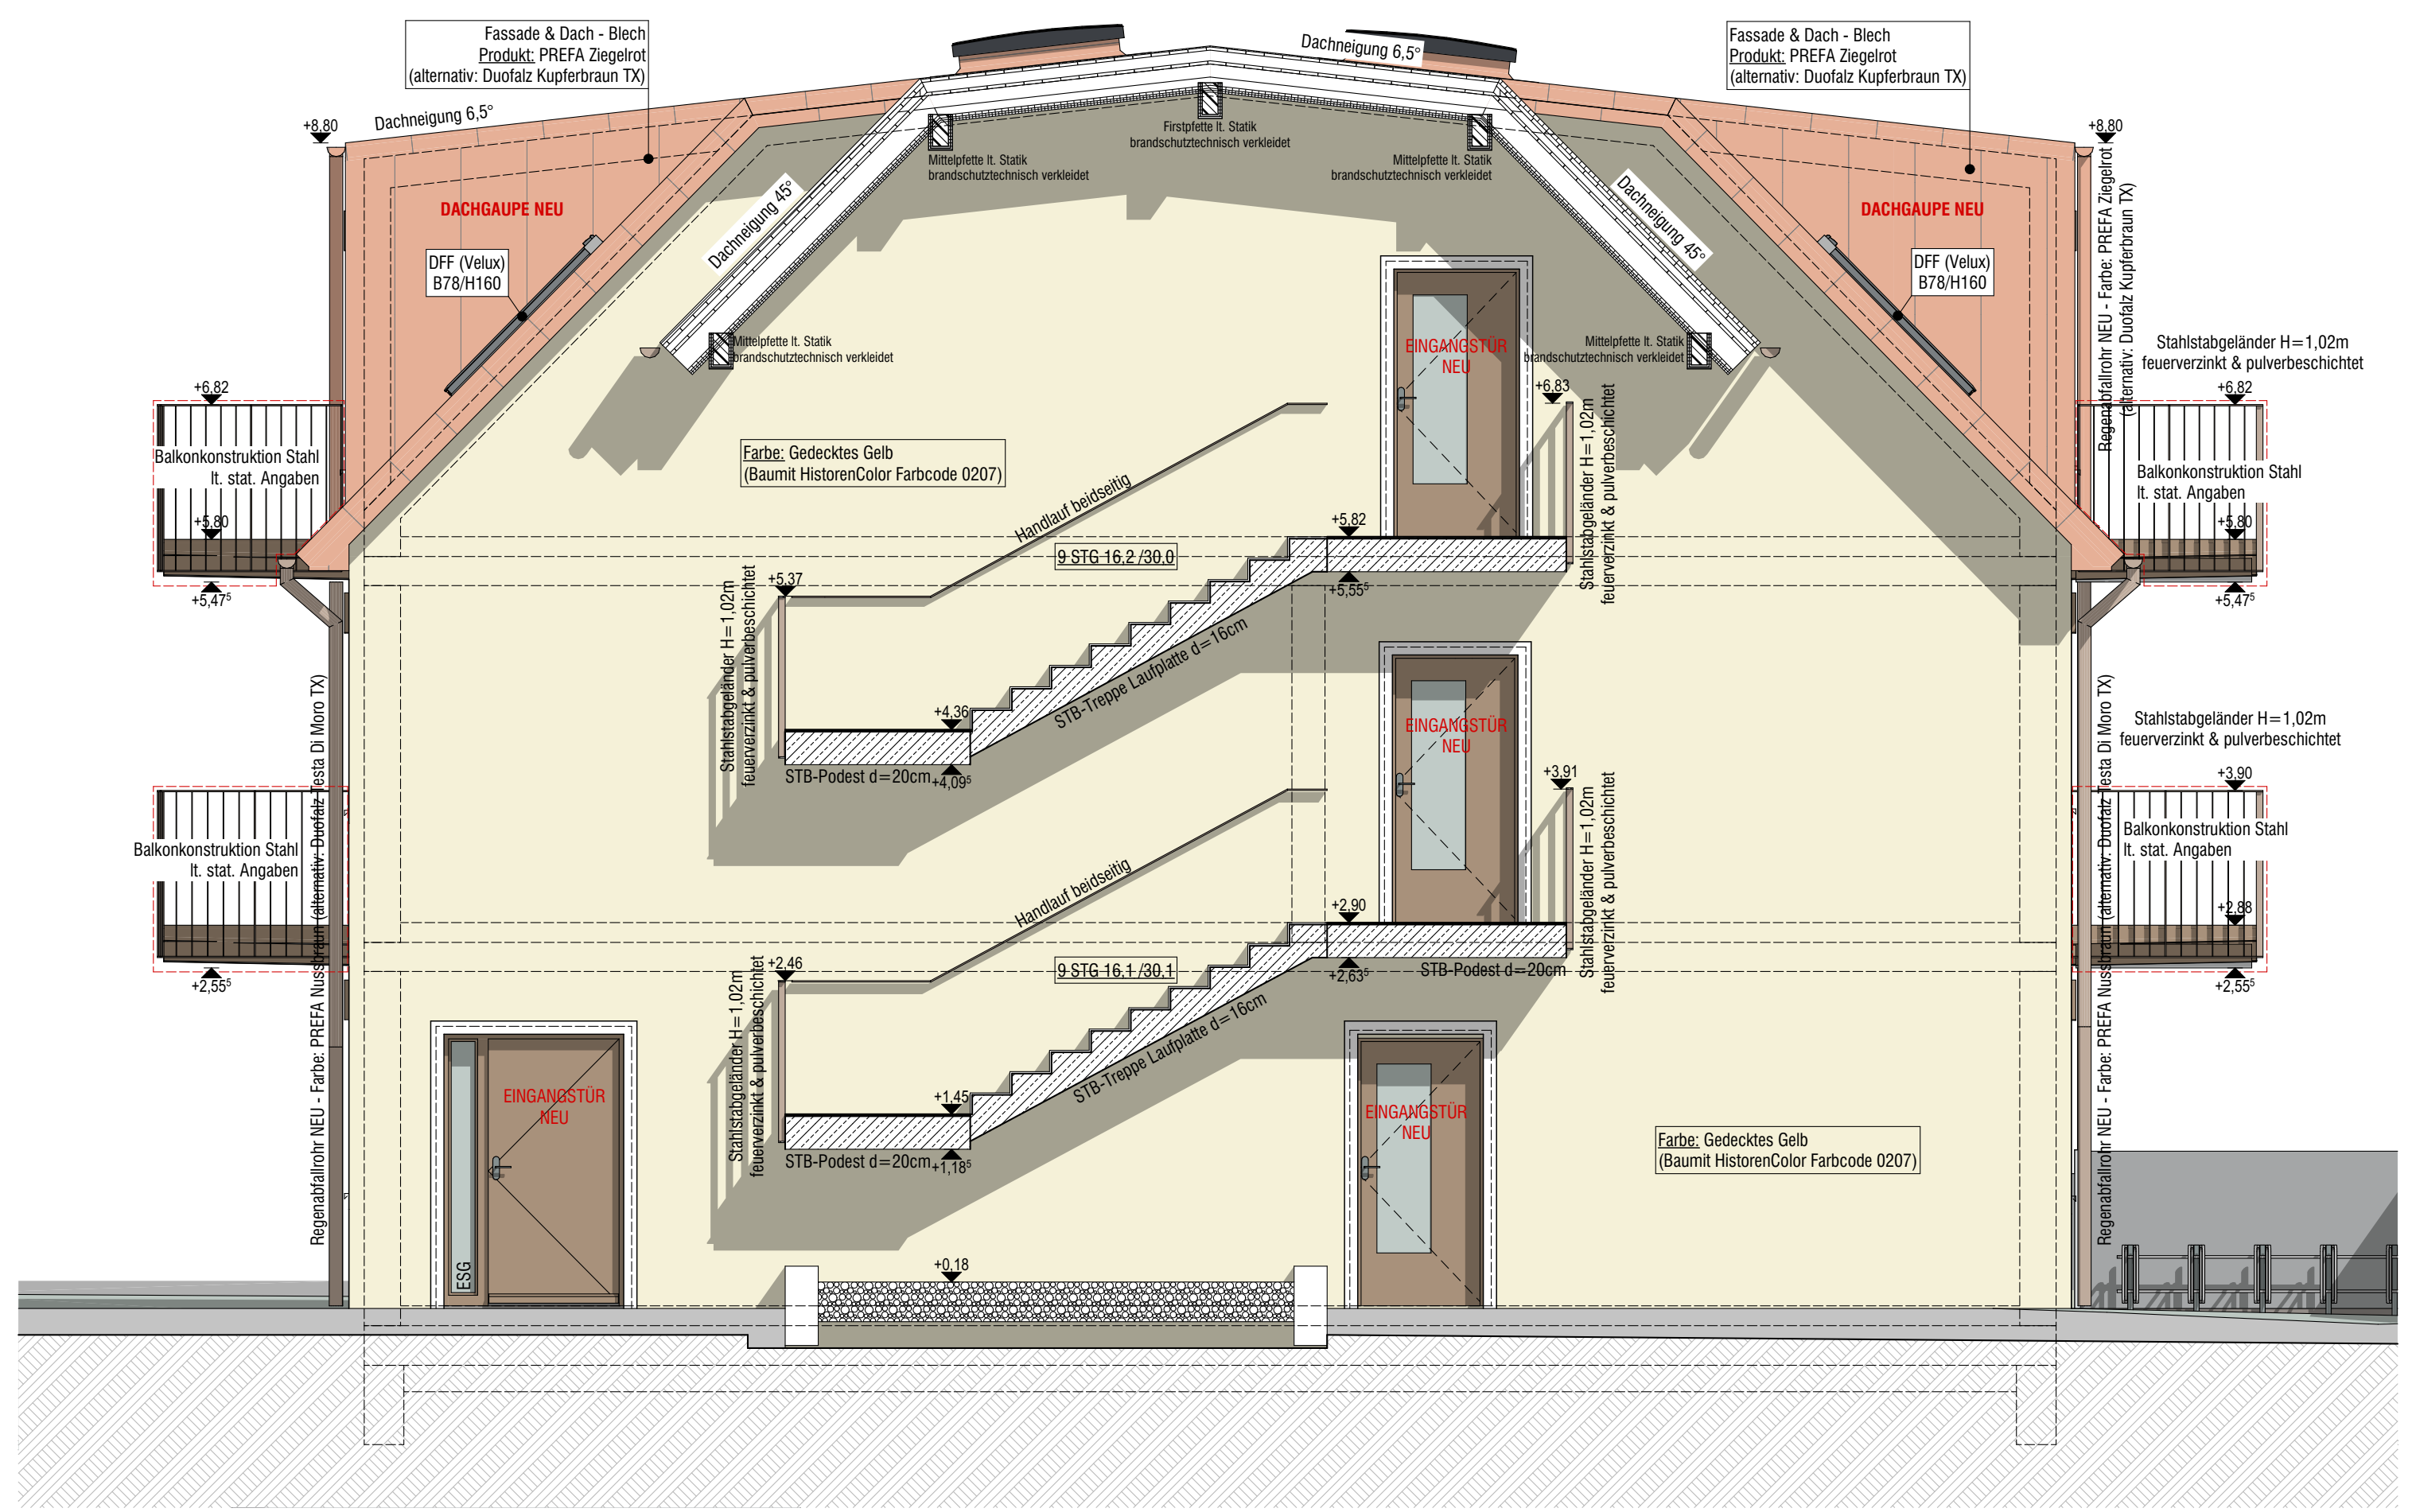
Fassade & Dach - Blech
Produkt: PREFA Ziegelrot
(alternativ: Duofalz Kupferbraun TX)
Dachneigung 6,5°
Dachneigung 45°
+8,80
Mittelpfette lt. Statik
brandschutztechnisch verkleidet
Firstpfette lt. Statik
brandschutztechnisch verkleidet
DACHGAUPE NEU
DFF (Velux)
B78/H160
EINGANGSTÜR NEU
Stahlstabgeländer H=1,02m
feuerverzinkt & pulverbeschichtet
Balkonkonstruktion Stahl
lt. stat. Angaben
Farbe: Gedecktes Gelb
(Baumit HistorenColor Farbcode 0207)
Handlauf beidseitig
9 STG 16,2 /30,0
9 STG 16,1 /30,1
STB-Treppe Laufplatte d=16cm
STB-Podest d=20cm
+6,83
+6,82
+5,82
+5,80
+5,55
+5,47
+5,37
+4,36
+4,09
+3,91
+3,90
+2,90
+2,88
+2,63
+2,55
+2,46
+1,45
+1,18
+0,18
ESG
Regenabfallrohr NEU - Farbe: PREFA Nussbraun (alternativ: Duofalz Testa Di Moro TX)
Regenabfallrohr NEU - Farbe: PREFA Ziegelrot (alternativ: Duofalz Kupferbraun TX)

OSTANSICHT Neubau | 1:50

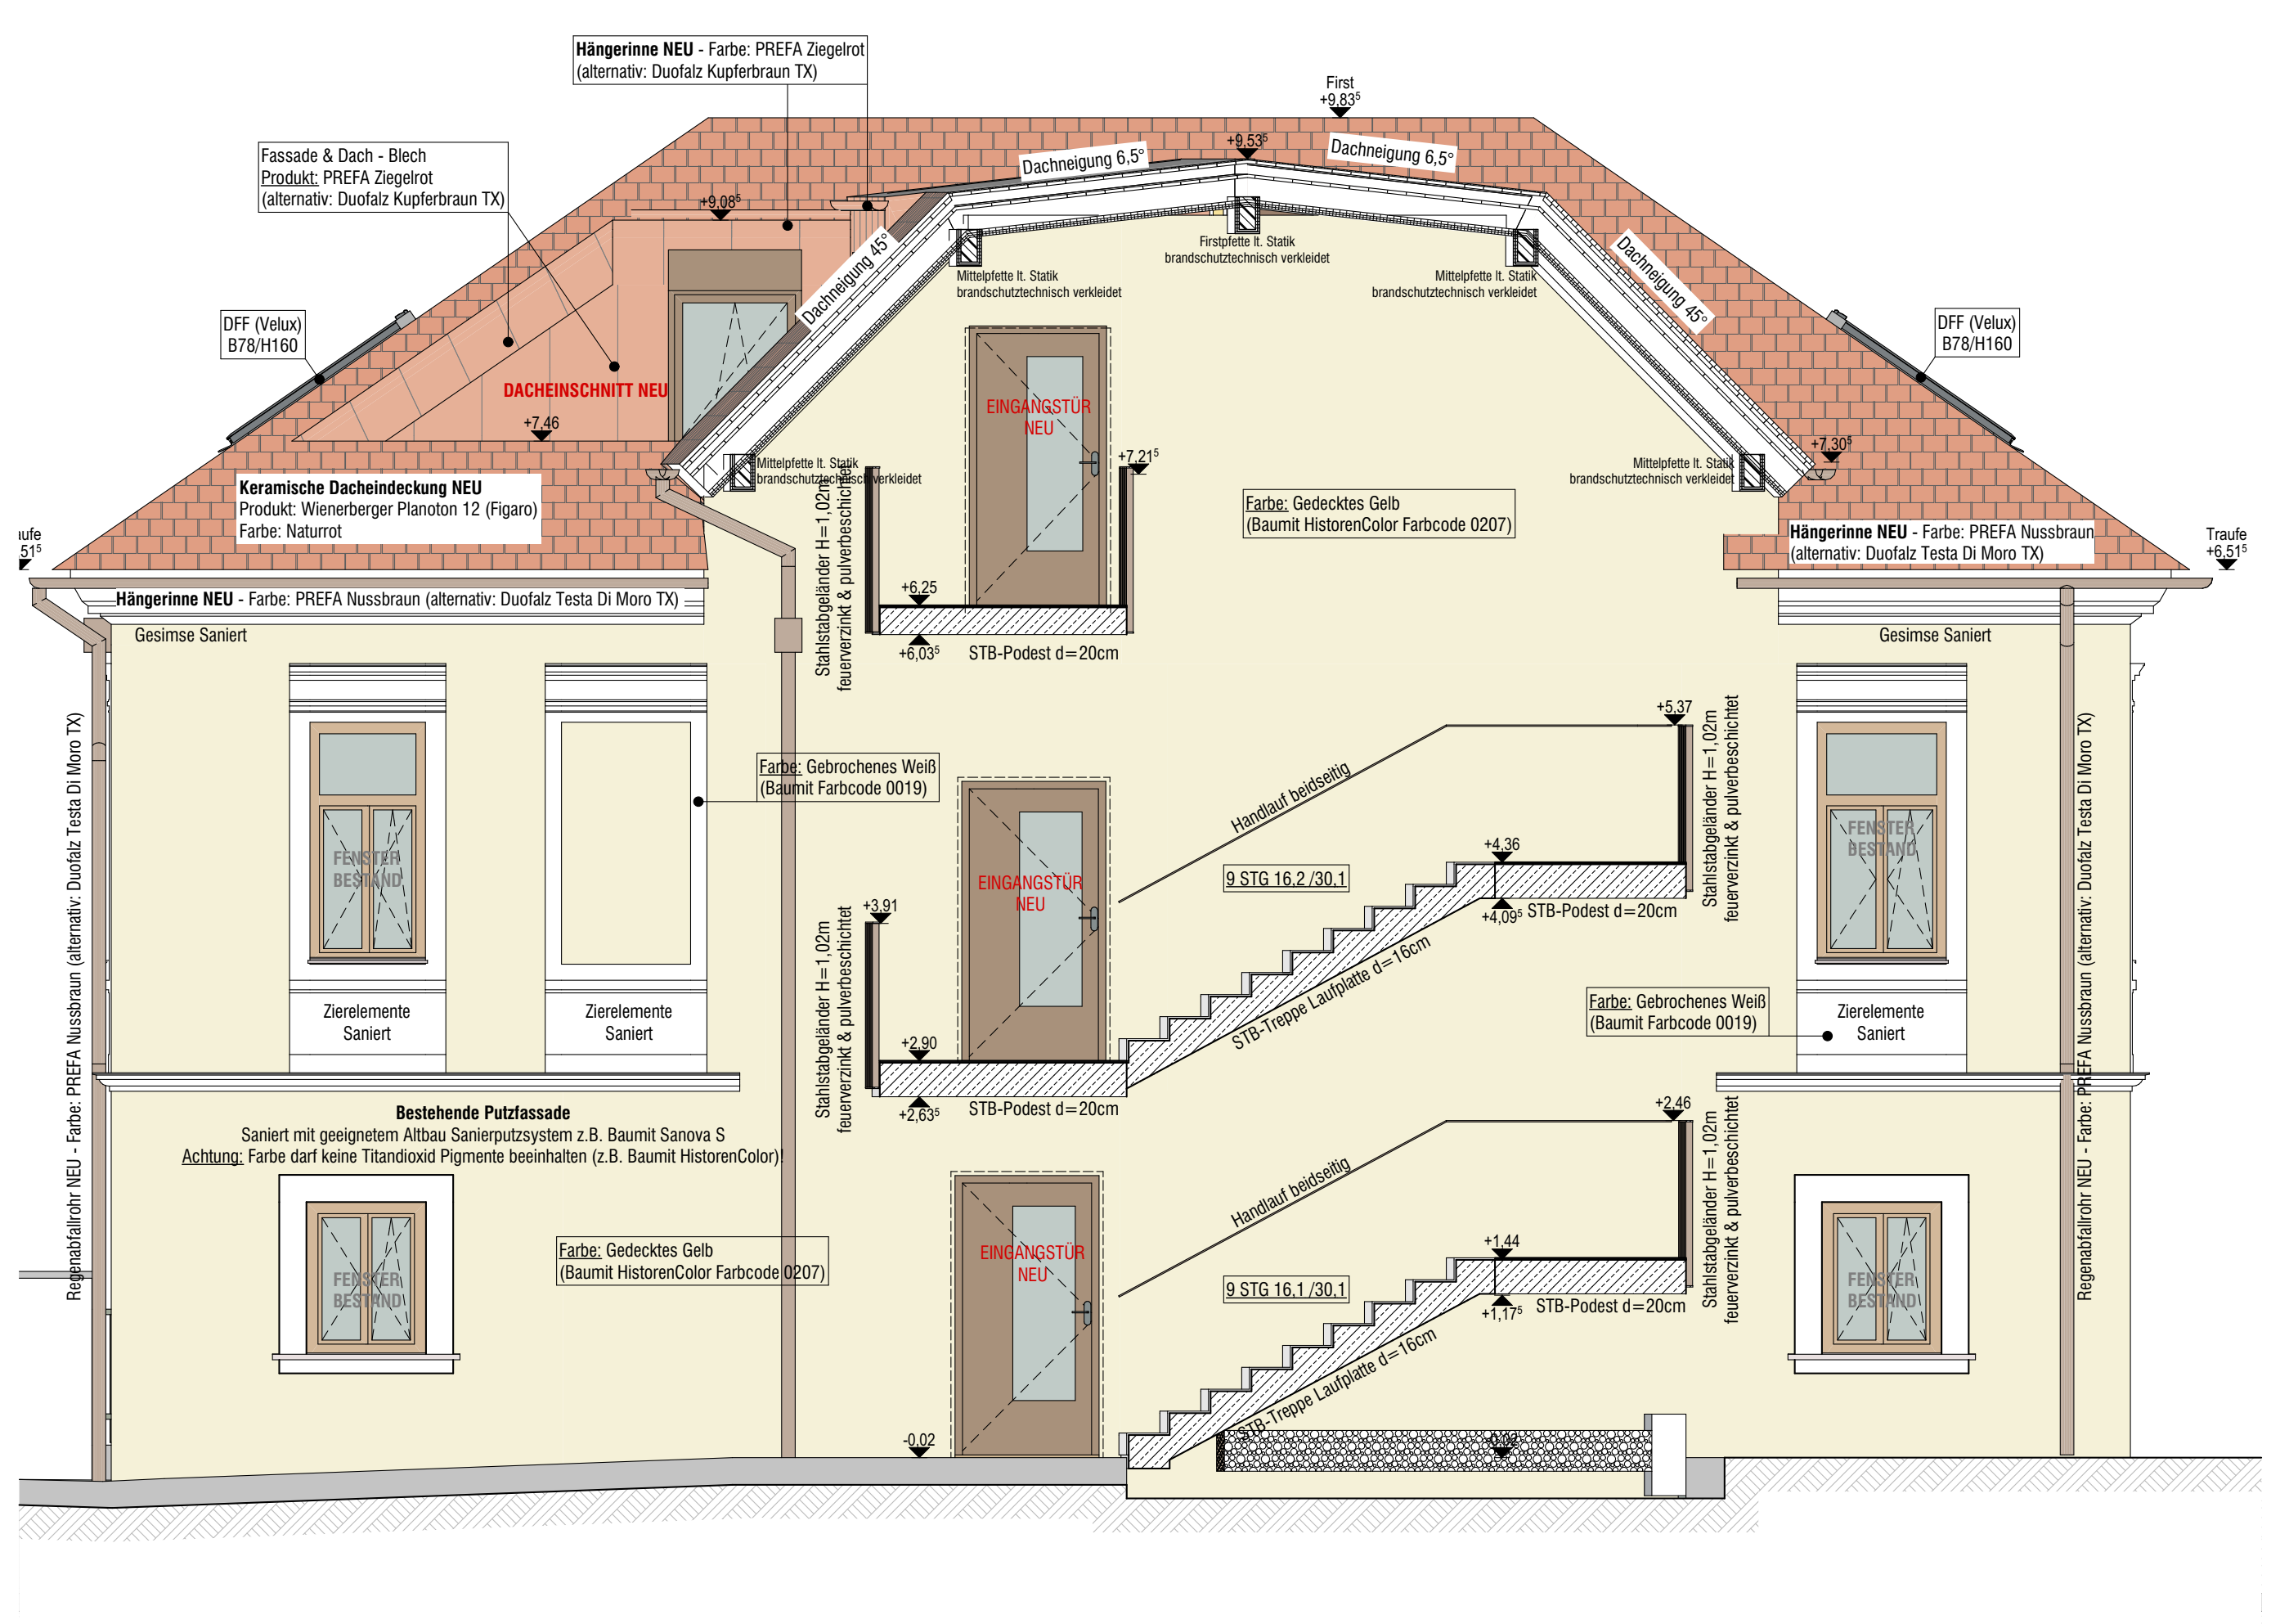
Hängerinne NEU - Farbe: PREFA Ziegelrot
(alternativ: Duofalz Kupferbraun TX)
Fassade & Dach - Blech
Produkt: PREFA Ziegelrot
(alternativ: Duofalz Kupferbraun TX)
First
+9,83
+9,53
+9,08
Dachneigung 6,5°
Dachneigung 45°
Firstpfette lt. Statik
brandschutztechnisch verkleidet
Mittelpfette lt. Statik
brandschutztechnisch verkleidet
DFF (Velux)
B78/H160
DACHEINSCHNITT NEU
+7,46
+7,30
Keramische Dacheindeckung NEU
Produkt: Wienerberger Planoton 12 (Figaro)
Farbe: Naturrot
EINGANGSTÜR NEU
+7,21
Farbe: Gedecktes Gelb
(Baumit HistorenColor Farbcode 0207)
Hängerinne NEU - Farbe: PREFA Nussbraun
(alternativ: Duofalz Testa Di Moro TX)
Traufe
+6,51
Gesimse Saniert
+6,25
+6,03
STB-Podest d=20cm
Stahlstabgeländer H=1,02m
feuerverzinkt & pulverbeschichtet
FENSTER BESTAND
Farbe: Gebrochenes Weiß
(Baumit Farbcode 0019)
Handlauf beidseitig
9 STG 16,2 /30,1
9 STG 16,1 /30,1
STB-Treppe Laufplatte d=16cm
+5,37
+4,36
+4,09
+3,91
+2,90
+2,63
+2,46
+1,44
+1,17
-0,02
Zierelemente
Saniert
Bestehende Putzfassade
Saniert mit geeignetem Altbau Sanierputzsystem z.B. Baumit Sanova S
Achtung: Farbe darf keine Titandioxid Pigmente beinhalten (z.B. Baumit HistorenColor)!
Regenabfallrohr NEU - Farbe: PREFA Nussbraun (alternativ: Duofalz Testa Di Moro TX)

WESTANSICHT Altbau | 1:50

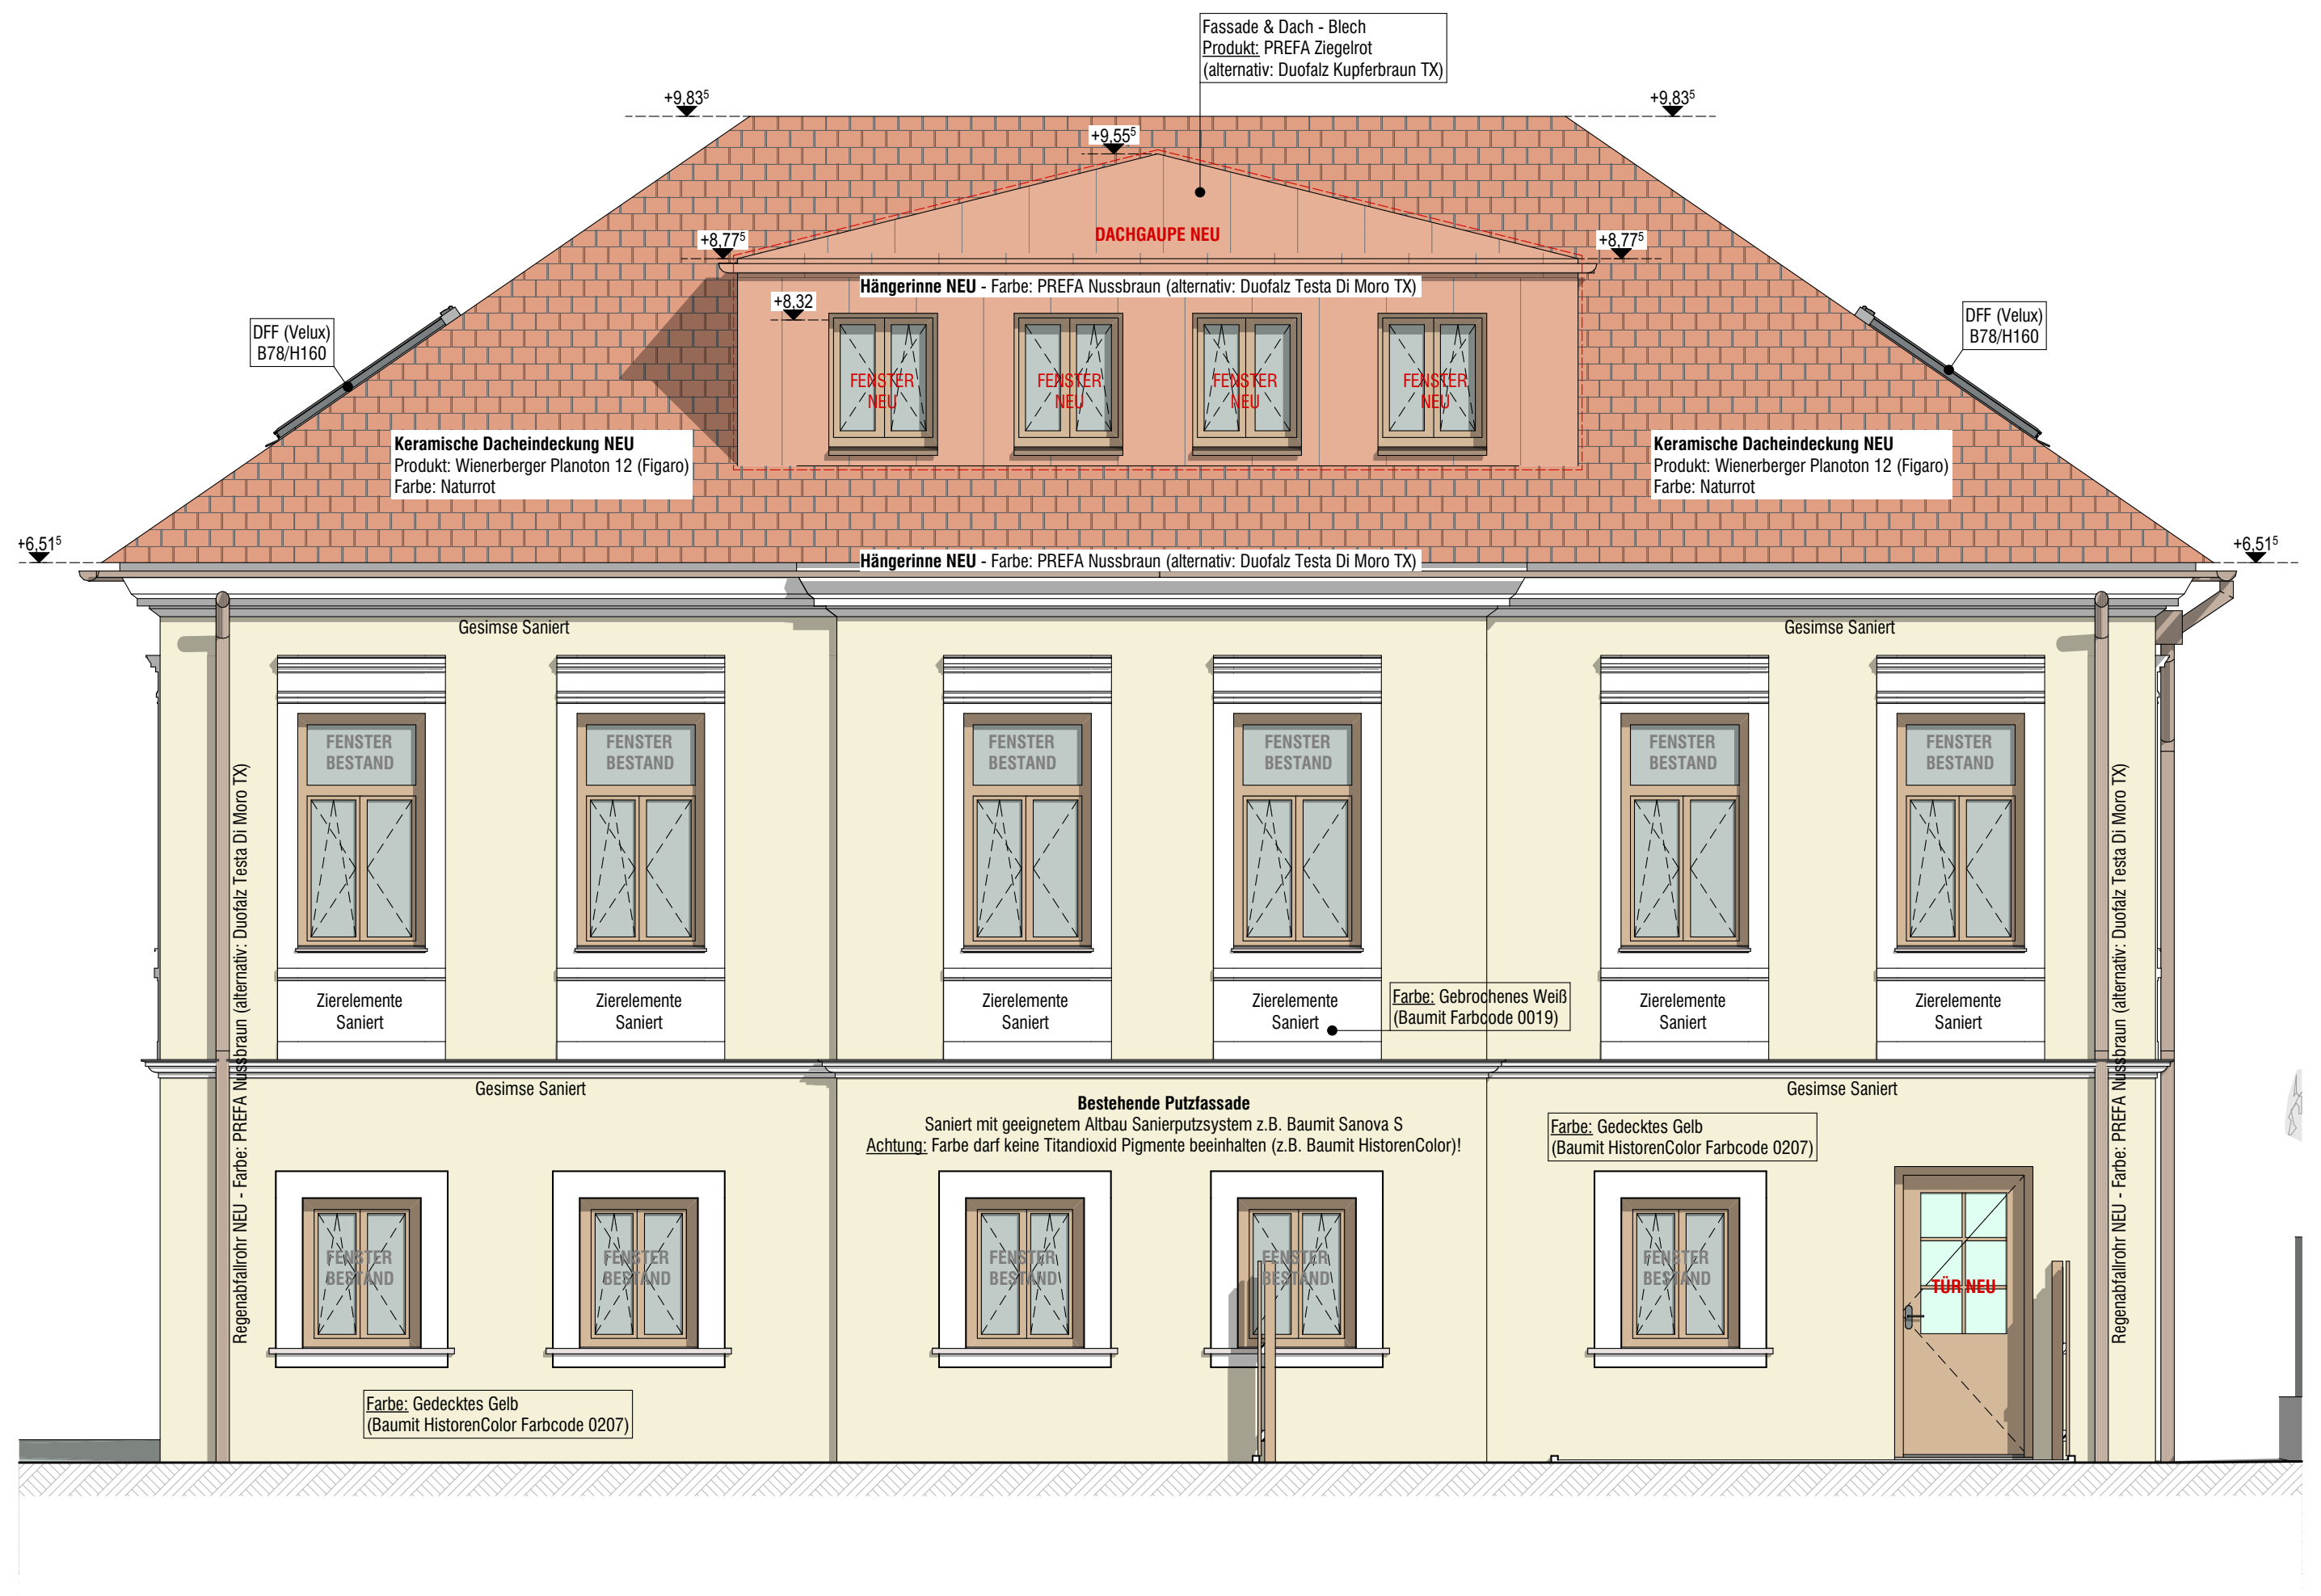
Fassade & Dach - Blech
Produkt: PREFA Ziegelrot
(alternativ: Duofalz Kupferbraun TX)
+9,83
+9,55
+8,77
+8,32
DACHGAUPE NEU
Hängerinne NEU - Farbe: PREFA Nussbraun (alternativ: Duofalz Testa Di Moro TX)
DFF (Velux)
B78/H160
FENSTER NEU
Keramische Dacheindeckung NEU
Produkt: Wienerberger Planoton 12 (Figaro)
Farbe: Naturrot
Traufe
+6,51
Gesimse Saniert
FENSTER BESTAND
Zierelemente
Saniert
Farbe: Gebrochenes Weiß
(Baumit Farbcode 0019)
Bestehende Putzfassade
Saniert mit geeignetem Altbau Sanierputzsystem z.B. Baumit Sanova S
Achtung: Farbe darf keine Titandioxid Pigmente beinhalten (z.B. Baumit HistorenColor)!
Farbe: Gedecktes Gelb
(Baumit HistorenColor Farbcode 0207)
TÜR NEU
Regenabfallrohr NEU - Farbe: PREFA Nussbraun (alternativ: Duofalz Testa Di Moro TX)

OSTANSICHT Altbau | 1:50

LEGENDE

☒	Wanddurchbruch
⬚	Deckendurchbruch
◺	Bodenschlitz
◢	Bodendurchbruch
▼	OK Fertigbau
▲	UK Fertigbau
▽	OK Rohbau
△	UK Rohbau
± 0,00	Höhenangabe einer waagrechten Fläche
±0,00	Höhenangabe eines Punktes in einem Bauwerk - Fertigmaß
±0,00	Höhenangabe eines Punktes in einem Bauwerk - Rohbaumaß
BGF	Bruttogesamtfläche
HNF / NNF	Haupt- Nebennutzfläche

▨	Mauerwerk (wärmedämmend)
▨	Mauerwerk (nicht wärmedämmend)
▨	unbewehrter Beton
▨	bewehrter Beton
▦	Betonfertigteil
▨	Stein
▨	Stahl (allgemein)
▨	Holz (allgemein)
▨	Holzwerkstoffe
▨	Dämmstoff (hart)
▨	Dämmstoff (weich)
▨	Kunststoff (allgemein)
▨	Dichtstoff (allgemein)
▥	Gips (Gipskartonplatte)
▥	Gipskartonplatte Brandschutz
☐	Erdmaterial (allgemein)
■	Bestand
🟨	Abbruch
🟥	Neubau

—	Medien
—	Fernwärme
—	Gas
—	Strom
—	Heizung
—	Regenwasser
—	Schmutzwasser
—	Wasser
—	Blech
- - -	Abdichtung
- - -	Folie
– – –	Dampfsperre, -bremse

Höhenbezugs- und Maßangaben

DOK	Deckenoberkante
DOS	Deckenoberseite
DUK	Deckenunterkante
DUS	Deckenunterseite
DUF	Deckenunterkante (fertige Untersicht)
FBOK	Fußbodenoberkante
OFF	Oberfläche des fertigen Fußbodens
FDOK	Fundamentoberkante
FDOS	Fundamentoberseite
FDUK	Fundamentunterkante
FDUS	Fundamentunterseite
RH	lichte Raumhöhe
GH	Geschoßhöhe
OK	Oberkante
OS	Oberseite
UK	Unterkante
US	Unterseite
STUK	Sturzunterkante (Rohbaumaß)
STH	Sturzhöhe gemessen von STUK bis DUK (Rohbaumaß)
RPH	Rohbauparapethöhe
FPH	fertige Parapethöhe (FBOK bis OK Fensterbank Innen)

Rauch-, Abgas- und Luftfänge, Schächte

L	Lüftungsschacht
PT	Putztürchen
PS	Putzstück
KT	Kehrtürchen
ABL	Abluft
ZUL	Zuluft
DBA	Druckbelüftungsanlage
DES	Druckentlastungsschacht
BÖ	Belüftungsöffnung
ÜÖ	Überströmöffnung
AÖ	Abströmöffnung mit Überdruckentlastungsorgan
BSK	Brandsschutzklappe
FBHV	Fussbodenheizungsverteiler
E-Verteiler	Elektroverteiler

Öffnungen und deren Abschlüsse

WD	Wanddurchbruch
DD	Deckendurchbruch
FBD	Fußbodendurchbruch
FDD	Fundamentdurchbruch
WS	Wandschlitz
WA	Wandaussparung
DA	Deckenaussparung
FBA	Fußbodenaussparung
RBL	Rohbaulichte
AL	Architekturlichte
STL	Stocklichte
GL	Glaslichte
STAM	Stockaußenmaß
DL	Durchgangslichte
GGT	Ganzglastüre
MGT	Metallgittertür
HT	Hebetüre
HST	Hebeschiebetüre
T	Türe
AT	Allgemeintüre
ET	Eingangstüre
WET	Wohnungseingangstür
IT	Innentür
DF	Drehflügel
DKF	Drehkippflügel
SF	Schiebe-Fenster
SWF	Schwingflügel
WF	Wendeflügel
K	Kippfenster
OL	Oberlichte
DF	Dachflächenfenster
PFR	Pfostenriegelkonstruktion
FE	Fenster
FT	Fenstertüre
R	Rechtsöffnend
L	Linksöffnend
FIX	Fixverglasung
VSG	Verbund-Sicherheitsglas
ESG	Einscheiben-Sicherheitsglas

Drehflügel
Drehkippflügel
Kippflügel
Fenstertüre

EI2 30-C-, EI2 60-C-und EI2 90-C
Feuerschutztüren mit Angabe der Feuerwiderstandsklasse
(gemäß ÖNORM B 3850 und ÖNORM B 3807)

GT	gasdichte Türe
DT	Drucktüre
S 200	Rauchabschluss
S 200	Rauchabschluss
C	Selbstschließend
FLS	Freilaufschließer
LVfTÖ	Lehrverrohrung für Türöffner
elTÖ	elektrischer Türöffner

AUSFÜHRUNG

POLIERPLAN

Bauvorhaben
WNEU30

2540 Bad Vöslau, Wiener Neustädter Straße 30

XXX

Katastralgemeinde 04035 Vöslau
EZ: 719
GstNr.: 748

Diese Zeichnung bzw. Ausarbeitung sowie deren Daten auf Datenträgern sind geistiges Eigentum des Erstellers Arch. Artmüller Georg. Jede Benützung, Veröffentlichung,Vervielfältigung jeglicher Art oder Weitergabe an Dritte bedarf der schriftlichen Zustimmung durch Architekt Artmüller.

Durch die Übernahme dieses Planes akzeptiert die ausführende Firma bzw. Person die darauf dargestellten Anordnungen. Geschriebene Planmaße auf dieser Zeichnunghaben Vorrang gegenüber gezeichneten Dimensionen. Der Auftragnehmer verpflichtet sich **vor** Arbeitsbeginn alle Maße und Bedingungen im Zusammenhang mit seinerArbeit auf der Baustelle verantwortlich zu überprüfen.

Abweichungen gegenüber dargestellten oder schriftlich vereinbarten Anordnungen müssen Architekt Artmüller und der Bauleitung unverzüglich schriftlich mitgeteiltwerden. Vor Arbeitsbeginn sind dem Architekten gültige Werkzeichnungen zur Genehmigung vorzulegen.

NATURMASSE SIND ZU NEHMEN, KOTEN ZU PRÜFEN

Index	Datum	Bearbeiter	Änderung

VORABZUG
22. 10. 2026

Index	Änderung	Datum

Grundeigentümer

Bauwerber / Auftraggeber

ARTMÜLLER ARCHITEKTEN
ZIVILTECHNIKER GMBH
Stolberggasse 34|26 A-1050 Wien
t [+43] 01 . 581 40 83 f [+43] 01. 581 40 83 99 office@artmueller.eu

Planinhalt
Ansichten

Maßstab	Gez	Datum	Plannr.	Index
1:50	ML	22-10-2026	WNEU30_50_07	VORABZUG

Erstellt, am 11.11.2026