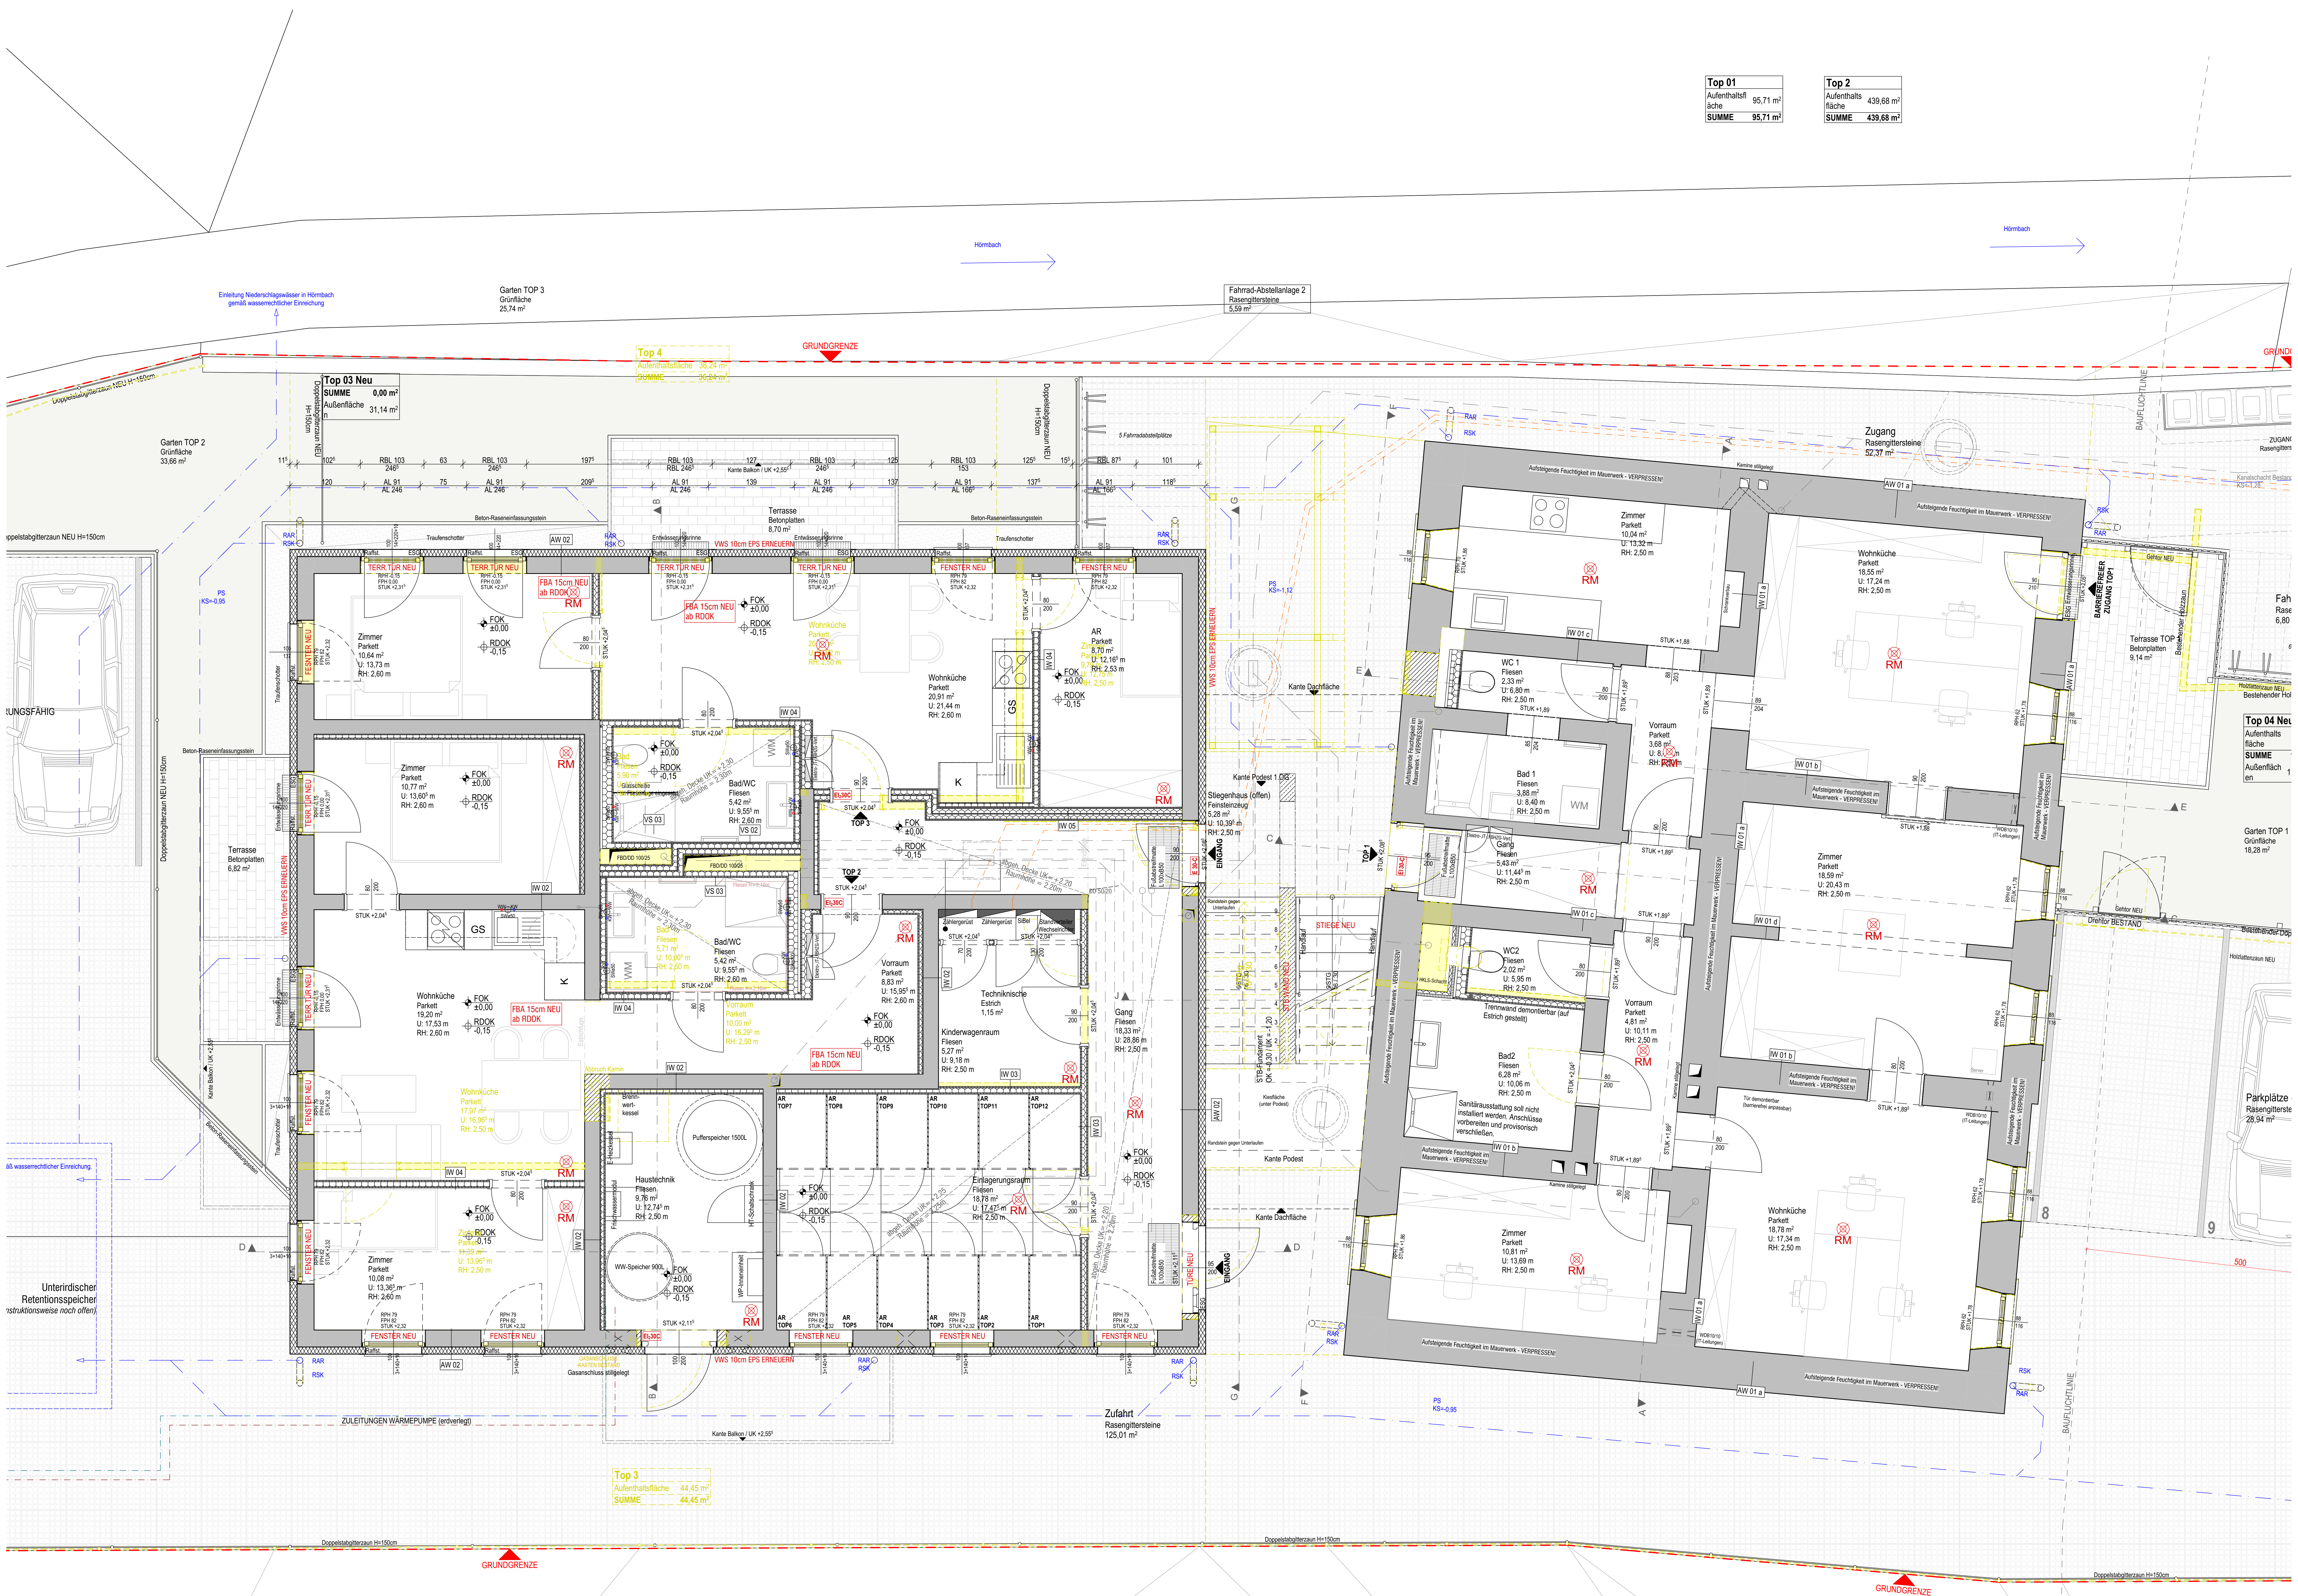
Hörmbach
Einleitung Niederschlagswässer in Hörmbach gemäß wasserrechtlicher Einreichung
Garten TOP 3 Grünfläche 25,74 m²
Fahrrad-Abstellanlage 2 Rasengittersteine 5,59 m²
GRUNDGRENZE
Top 4
Top 03 Neu
Garten TOP 2 Grünfläche 33,66 m²
Terrasse Betonplatten 8,70 m²
Zugang Rasengittersteine 52,37 m²
Zimmer Parkett 10,64 m²
Wohnküche Parkett 20,91 m²
AR Parkett 8,70 m²
Bad/WC Fliesen 5,42 m²
Zimmer Parkett 10,77 m²
Wohnküche Parkett 19,20 m²
Vorraum Parkett 8,83 m²
Bad/WC Fliesen 5,42 m²
Technikschacht Estrich 1,15 m²
Kinderwagenraum Fliesen 5,27 m²
Gang Fliesen 18,33 m²
Haustechnik Fliesen 9,76 m²
Einlagerungsraum Fliesen 18,78 m²
Zimmer Parkett 10,08 m²
Pufferspeicher 1500L
WW-Speicher 900L
Stiegenhaus (offen) Feinsteinzeug 5,28 m²
Terrasse Betonplatten 6,82 m²
Unterirdischer Retentionsspeicher (Konstruktionsweise noch offen)
Zimmer Parkett 10,04 m²
Wohnküche Parkett 18,55 m²
WC 1 Fliesen 2,33 m²
Vorraum Parkett 3,68 m²
Bad 1 Fliesen 3,88 m²
Gang Fliesen 5,43 m²
WC2 Fliesen 2,02 m²
Vorraum Parkett 4,81 m²
Bad2 Fliesen 6,28 m²
Zimmer Parkett 18,59 m²
Zimmer Parkett 10,81 m²
Wohnküche Parkett 18,78 m²
Terrasse TOP 1 Betonplatten 9,14 m²
Garten TOP 1 Grünfläche 18,28 m²
Parkplätze Rasengittersteine 28,94 m²
Zufahrt Rasengittersteine 125,01 m²
Top 3 Aufenthaltsfläche 44,45 m² SUMME 44,45 m²
ZULEITUNGEN WÄRMEPUMPE (erdverlegt)
Doppelstabgitterzaun H=150cm
GRUNDGRENZE

Top 01	
Aufenthaltsfläche	95,71 m²
SUMME	**95,71 m²**

Top 2	
Aufenthaltsfläche	439,68 m²
SUMME	**439,68 m²**

LEGENDE

☒	Wanddurchbruch
▭	Deckendurchbruch
▭	Bodenschlitz
◢	Bodendurchbruch
▼	OK Fertigbau
▲	UK Fertigbau
▽	OK Rohbau
△	UK Rohbau
± 0,00	Höhenangabe einer waagrechten Fläche
±0,00	Höhenangabe eines Punktes in einem Bauwerk - Fertigmaß
±0,00	Höhenangabe eines Punktes in einem Bauwerk - Rohbaumaß

BGF	Bruttogesamtfläche
HNF / NNF	Haupt- Nebennutzfläche

▨	Mauerwerk (wärmedämmend)
▨	Mauerwerk (nicht wärmedämmend)
▨	unbewehrter Beton
▨	bewehrter Beton
▦	Betonfertigteil
▤	Stein
▨	Stahl (allgemein)
▨	Holz (allgemein)
▨	Holzwerkstoffe
▩	Dämmstoff (hart)
▩	Dämmstoff (weich)
▩	Kunststoff (allgemein)
▚	Dichtstoff (allgemein)
▥	Gips (Gipskartonplatte)
▥	Gipskartonplatte Brandschutz
☐	Erdmaterial (allgemein)
■	Bestand
🟨	Abbruch
🟥	Neubau

—	Medien
—	Fernwärme
—	Gas
—	Strom
—	Heizung
—	Regenwasser
—	Schmutzwasser
—	Wasser
—	Blech
- - -	Abdichtung
- - -	Folie
- - -	Dampfsperre, -bremse

Höhenbezugs- und Maßangaben

DOK	Deckenoberkante
DOS	Deckenoberseite
DUK	Deckenunterkante
DUS	Deckenunterseite
DUF	Deckenunterkante (fertige Untersicht)
FBOK	Fußbodenoberkante
OFF	Oberfläche des fertigen Fußbodens
FDOK	Fundamentoberkante
FDOS	Fundamentoberseite
FDUK	Fundamentunterkante
FDUS	Fundamentunterseite
RH	lichte Raumhöhe
GH	Geschoßhöhe
OK	Oberkante
OS	Oberseite
UK	Unterkante
US	Unterseite
STUK	Sturzunterkante (Rohbaumaß)
STH	Sturzhöhe gemessen von STUK bis DUK (Rohbaumaß)
RPH	Rohbauparapethöhe
FPH	fertige Parapethöhe (FBOK bis OK Fensterbank Innen)

Rauch-, Abgas- und Luftfänge, Schächte

L	Lüftungsschacht
PT	Putztürchen
PS	Putzstück
KT	Kehrtürchen
ABL	Abluft
ZUL	Zuluft
DBA	Druckbelüftungsanlage
DES	Druckentlastungsschacht
BÖ	Belüftungsöffnung
ÜÖ	Überströmöffnung
AÖ	Abströmöffnung mit Überdruckentlastungsorgan
BSK	Brandsschutzklappe
FBHV	Fussbodenheizungsverteiler
E-Verteiler	Elektroverteiler

Öffnungen und deren Abschlüsse

WD	Wanddurchbruch
DD	Deckendurchbruch
FBD	Fußbodendurchbruch
FDD	Fundamentdurchbruch
WS	Wandschlitz
WA	Wandaussparung
DA	Deckenaussparung
FBA	Fußbodenaussparung
RBL	Rohbaulichte
AL	Architekturlichte
STL	Stocklichte
GL	Glaslichte
STAM	Stockaußenmaß
DL	Durchgangslichte
GGT	Ganzglastüre
MGT	Metallgittertür
HT	Hebetüre
HST	Hebeschiebetüre
T	Türe
AT	Allgemeintüre
ET	Eingangstüre
WET	Wohnungseingangstür
IT	Innentür
DF	Drehflügel
DKF	Drehkippflügel
SF	Schiebe-Fenster
SWF	Schwingflügel
WF	Wendeflügel
K	Kippfenster
OL	Oberlichte
DF	Dachfächenfenster
PFR	Pfostenriegelkonstruktion
FE	Fenster
FT	Fenstertüre
R	Rechtsöffnend
L	Linksöffnend
FIX	Fixverglasung
VSG	Verbund-Sicherheitsglas
ESG	Einscheiben-Sicherheitsglas

Drehflügel
Drehkippflügel
Kippflügel
Fenstertüre

EI2 30-C-, EI2 60-C-und EI2 90-C
Feuerschutztüren mit Angabe der Feuerwiderstandsklasse
(gemäß ÖNORM B 3850 und ÖNORM B 3807)

GT	gasdichte Türe
DT	Drucktüre
S 200	Rauchabschluss
S 200	Rauchabschluss
C	Selbstschließend
FLS	Freilaufschließer
LVfTÖ	Lehrverrohrung für Türöffner
elTÖ	elektrischer Türöffner

AUSFÜHRUNG POLIERPL. ABBRUCH

Bauvorhaben
WNEU30
2540 Bad Vöslau, Wiener Neustädter Straße 30

XXX

Katastralgemeinde 04035 Vöslau
EZ: 719
GstNr.: 748

Diese Zeichnung bzw. Ausarbeitung sowie deren Daten auf Datenträgern sind geistiges Eigentum des Erstellers Arch. Artmüller Georg. Jede Benützung, Veröffentlichung,Vervielfältigung jeglicher Art oder Weitergabe an Dritte bedarf der schriftlichen Zustimmung durch Architekt Artmüller.

Durch die Übernahme dieses Planes akzeptiert die ausführende Firma bzw. Person die darauf dargestellten Anordnungen. Geschriebene Planmaße auf dieser Zeichnunghaben Vorrang gegenüber gezeichneten Dimensionen. Der Auftragnehmer verpflichtet sich **vor** Arbeitsbeginn alle Maße und Bedingungen im Zusammenhang mit seinerArbeit auf der Baustelle verantwortlich zu überprüfen.

Abweichungen gegenüber dargestellten oder schriftlich vereinbarten Anordnungen müssen Architekt Artmüller und der Bauleitung unverzüglich schriftlich mitgeteiltwerden. Vor Arbeitsbeginn sind dem Architekten gültige Werkzeichnungen zur Genehmigung vorzulegen.

NATURMASSE SIND ZU NEHMEN, KOTEN ZU PRÜFEN

Index	Datum	Bearbeiter	Änderung

Index	Änderung	Datum

Grundeigentümer

Bauwerber / Auftraggeber

ARTMÜLLER ARCHITEKTEN
ZIVILTECHNIKER GMBH
Stolberggasse 34|26 A-1050 Wien
t [+43] 01 . 581 40 83 f [+43] 01. 581 40 83 99 office@artmueller.eu

Planinhalt
Erdgeschoss

Maßstab	Gez	Datum	Plannr.	Index
1:50	ML	02-11-2026	WNEU30_51_01	

Erstellt, am 11.11.2026

Top 9	
Aufenthaltsfläche	46,38 m²
Außenflächen	7,47 m²
SUMME	**53,85 m²**

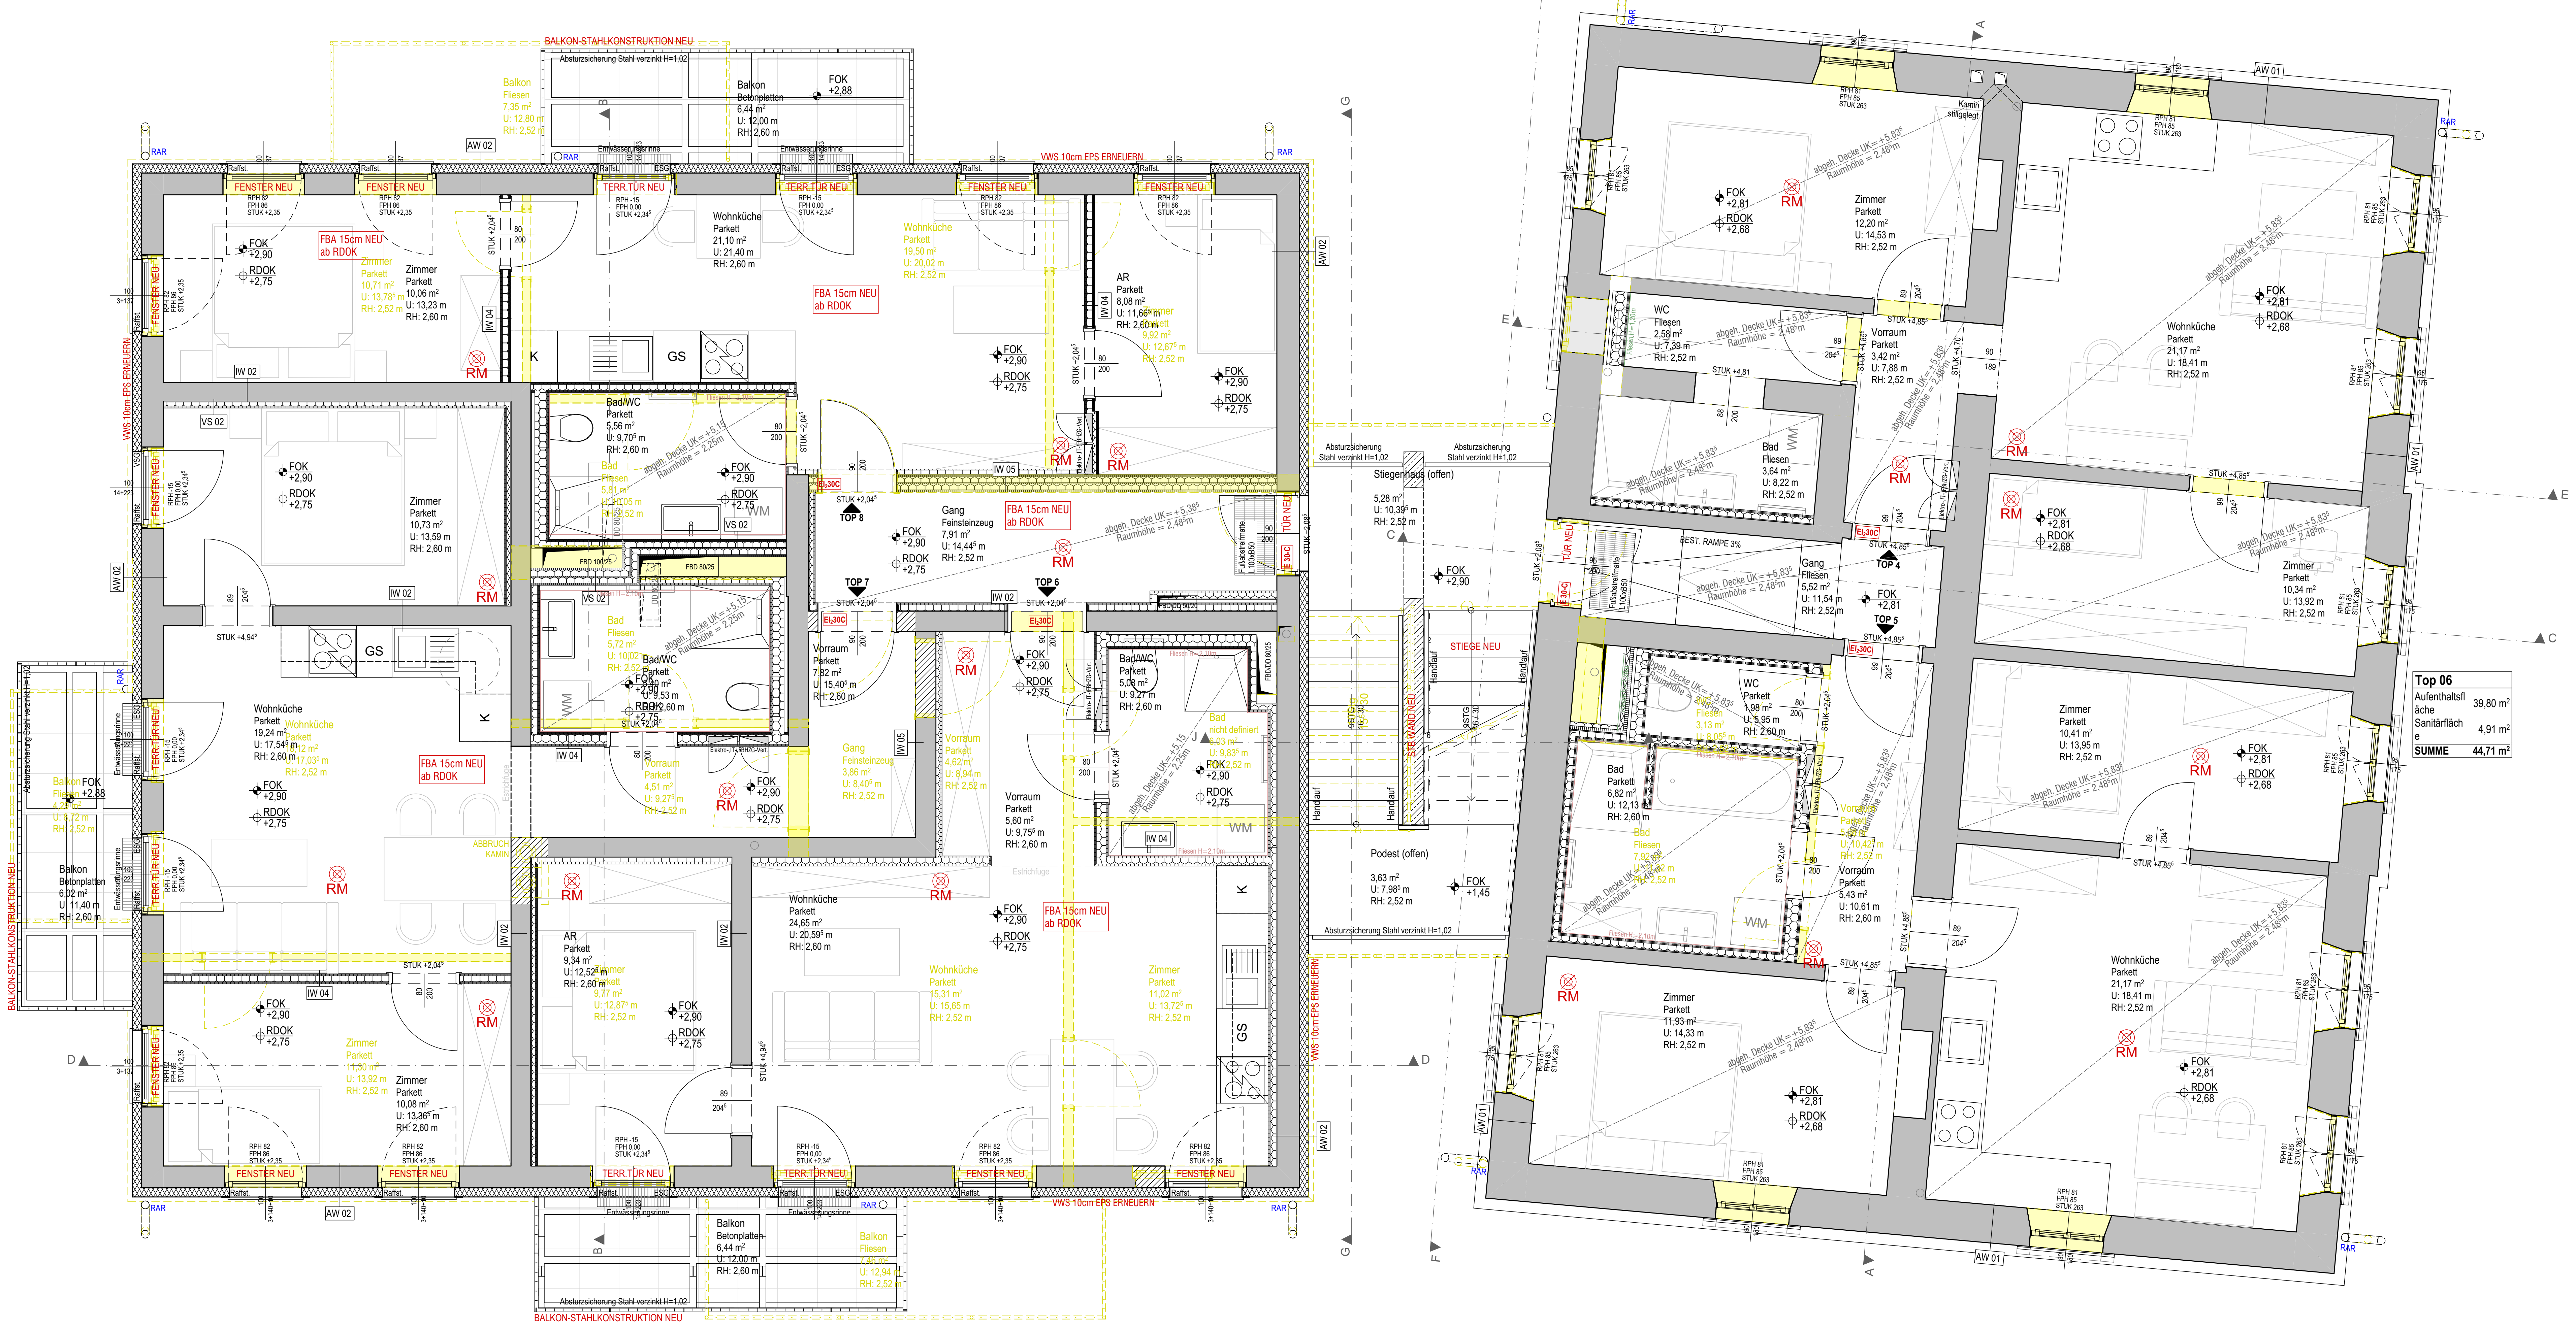

Top 06	
Aufenthaltsfläche	39,80 m²
Sanitärfläche	4,91 m²
SUMME	**44,71 m²**

Top 6	
Aufenthaltsfläche	16,13 m²
SUMME	**16,13 m²**

Top 7	
Aufenthaltsfläche	47,08 m²
Außenflächen	7,52 m²
SUMME	**54,60 m²**

LEGENDE

- ⊠ Wanddurchbruch
- Deckendurchbruch
- Bodenschlitz
- Bodendurchbruch
- ▼ OK Fertigbau
- ▲ UK Fertigbau
- ▽ OK Rohbau
- △ UK Rohbau
- ± 0,00 Höhenangabe einer waagrechten Fläche
- ±0,00 Höhenangabe eines Punktes in einem Bauwerk - Fertigmaß
- ±0,00 Höhenangabe eines Punktes in einem Bauwerk - Rohbaumaß

BGF	Bruttogesamtfläche
HNF / NNF	Haupt- Nebennutzfläche

- ▨ Mauerwerk (wärmedämmend)
- ▨ Mauerwerk (nicht wärmedämmend)
- ▨ unbewehrter Beton
- ▨ bewehrter Beton
- ▦ Betonfertigteil
- ▤ Stein
- ▨ Stahl (allgemein)
- ▨ Holz (allgemein)
- ▨ Holzwerkstoffe
- ▩ Dämmstoff (hart)
- ▩ Dämmstoff (weich)
- ▩ Kunststoff (allgemein)
- ▚ Dichtstoff (allgemein)
- ▥ Gips (Gipskartonplatte)
- ▥ Gipskartonplatte Brandschutz
- □ Erdmaterial (allgemein)
- ■ Bestand
- 🟨 Abbruch
- 🟥 Neubau

- Medien
- Fernwärme
- Gas
- Strom
- Heizung
- Regenwasser
- Schmutzwasser
- Wasser

- Blech
- Abdichtung
- Folie
- Dampfsperre, -bremse

Höhenbezugs- und Maßangaben

DOK	Deckenoberkante
DOS	Deckenoberseite
DUK	Deckenunterkante
DUS	Deckenunterseite
DUF	Deckenunterkante (fertige Untersicht)
FBOK	Fußbodenoberkante
OFF	Oberfläche des fertigen Fußbodens
FDOK	Fundamentoberkante
FDOS	Fundamentoberseite
FDUK	Fundamentunterkante
FDUS	Fundamentunterseite
RH	lichte Raumhöhe
GH	Geschoßhöhe
OK	Oberkante
OS	Oberseite
UK	Unterkante
US	Unterseite
STUK	Sturzunterkante (Rohbaumaß)
STH	Sturzhöhe gemessen von STUK bis DUK (Rohbaumaß)
RPH	Rohbauparapethöhe
FPH	fertige Parapethöhe (FBOK bis OK Fensterbank Innen)

Rauch-, Abgas- und Luftfänge, Schächte

L	Lüftungsschacht
PT	Putztürchen
PS	Putzstück
KT	Kehrtürchen
ABL	Abluft
ZUL	Zuluft
DBA	Druckbelüftungsanlage
DES	Druckentlastungsschacht
BÖ	Belüftungsöffnung
ÜÖ	Überströmöffnung
AÖ	Abströmöffnung mit Überdruckentlastungsorgan
BSK	Brandsschutzklappe
FBHV	Fussbodenheizungsverteiler
E-Verteiler	Elektroverteiler

Öffnungen und deren Abschlüsse

WD	Wanddurchbruch
DD	Deckendurchbruch
FBD	Fußbodendurchbruch
FDD	Fundamentdurchbruch
WS	Wandschlitz
WA	Wandaussparung
DA	Deckenaussparung
FBA	Fußbodenaussparung
RBL	Rohbaulichte
AL	Architekturlichte
STL	Stocklichte
GL	Glaslichte
STAM	Stockaußenmaß
DL	Durchgangslichte
GGT	Ganzglastüre
MGT	Metallgittertür
HT	Hebetüre
HST	Hebeschiebetüre
T	Türe
AT	Allgemeintüre
ET	Eingangstüre
WET	Wohnungseingangstür
IT	Innentür
DF	Drehflügel
DKF	Drehkippflügel
SF	Schiebe-Fenster
SWF	Schwingflügel
WF	Wendeflügel
K	Kippfenster
OL	Oberlichte
DF	Dachfächenfenster
PFR	Pfostenriegelkonstruktion
FE	Fenster
FT	Fenstertüre
R	Rechtsöffnend
L	Linksöffnend
FIX	Fixverglasung
VSG	Verbund-Sicherheitsglas
ESG	Einscheiben-Sicherheitsglas

- Drehflügel
- Drehkippflügel
- Kippflügel
- Fenstertüre

EI2 30-C-, EI2 60-C-und EI2 90-C
Feuerschutztüren mit Angabe der Feuerwiderstandsklasse
(gemäß ÖNORM B 3850 und ÖNORM B 3807)

GT	gasdichte Türe
DT	Drucktüre
S 200	Rauchabschluss
S 200	Rauchabschluss
C	Selbstschließend
FLS	Freilaufschließer
LVfTÖ	Lehrverrohrung für Türöffner
elTÖ	elektrischer Türöffner

AUSFÜHRUNG POLIERPL. ABBRUCH

Bauvorhaben

WNEU30

2540 Bad Vöslau, Wiener Neustädter Straße 30

XXX

Katastralgemeinde 04035 Vöslau
EZ: 719
GstNr.: 748

Durch die Übernahme dieses Planes akzeptiert die ausführende Firma bzw. Person die darauf dargestellten Anordnungen. Geschriebene Planmaße auf dieser Zeichnunghaben Vorrang gegenüber gezeichneten Dimensionen. Der Auftragnehmer verpflichtet sich **vor** Arbeitsbeginn alle Maße und Bedingungen im Zusammenhang mit seinerArbeit auf der Baustelle verantwortlich zu überprüfen.

Abweichungen gegenüber dargestellten oder schriftlich vereinbarten Anordnungen müssen Architekt Artmüller und der Bauleitung unverzüglich schriftlich mitgeteiltwerden. Vor Arbeitsbeginn sind dem Architekten gültige Werkzeichnungen zur Genehmigung vorzulegen.

NATURMASSE SIND ZU NEHMEN, KOTEN ZU PRÜFEN

Index	Datum	Bearbeiter	Änderung

Index	Änderung	Datum

Grundeigentümer

Bauwerber / Auftraggeber

ARTMÜLLER ARCHITEKTEN
ZIVILTECHNIKER GMBH
Stolberggasse 34|26 A-1050 Wien
t [+43] 01 . 581 40 83 f [+43] 01. 581 40 83 99 office@artmueller.eu

Planinhalt

1.Obergeschoß

Maßstab	Gez	Datum	Plannr.	Index
1:50	ML	02-11-2026	WNEU30_51_02	

Erstellt, am 11.11.2026

TOP 01	
Büroarbeit	0,94 m²
SUMME	**0,94 m²**

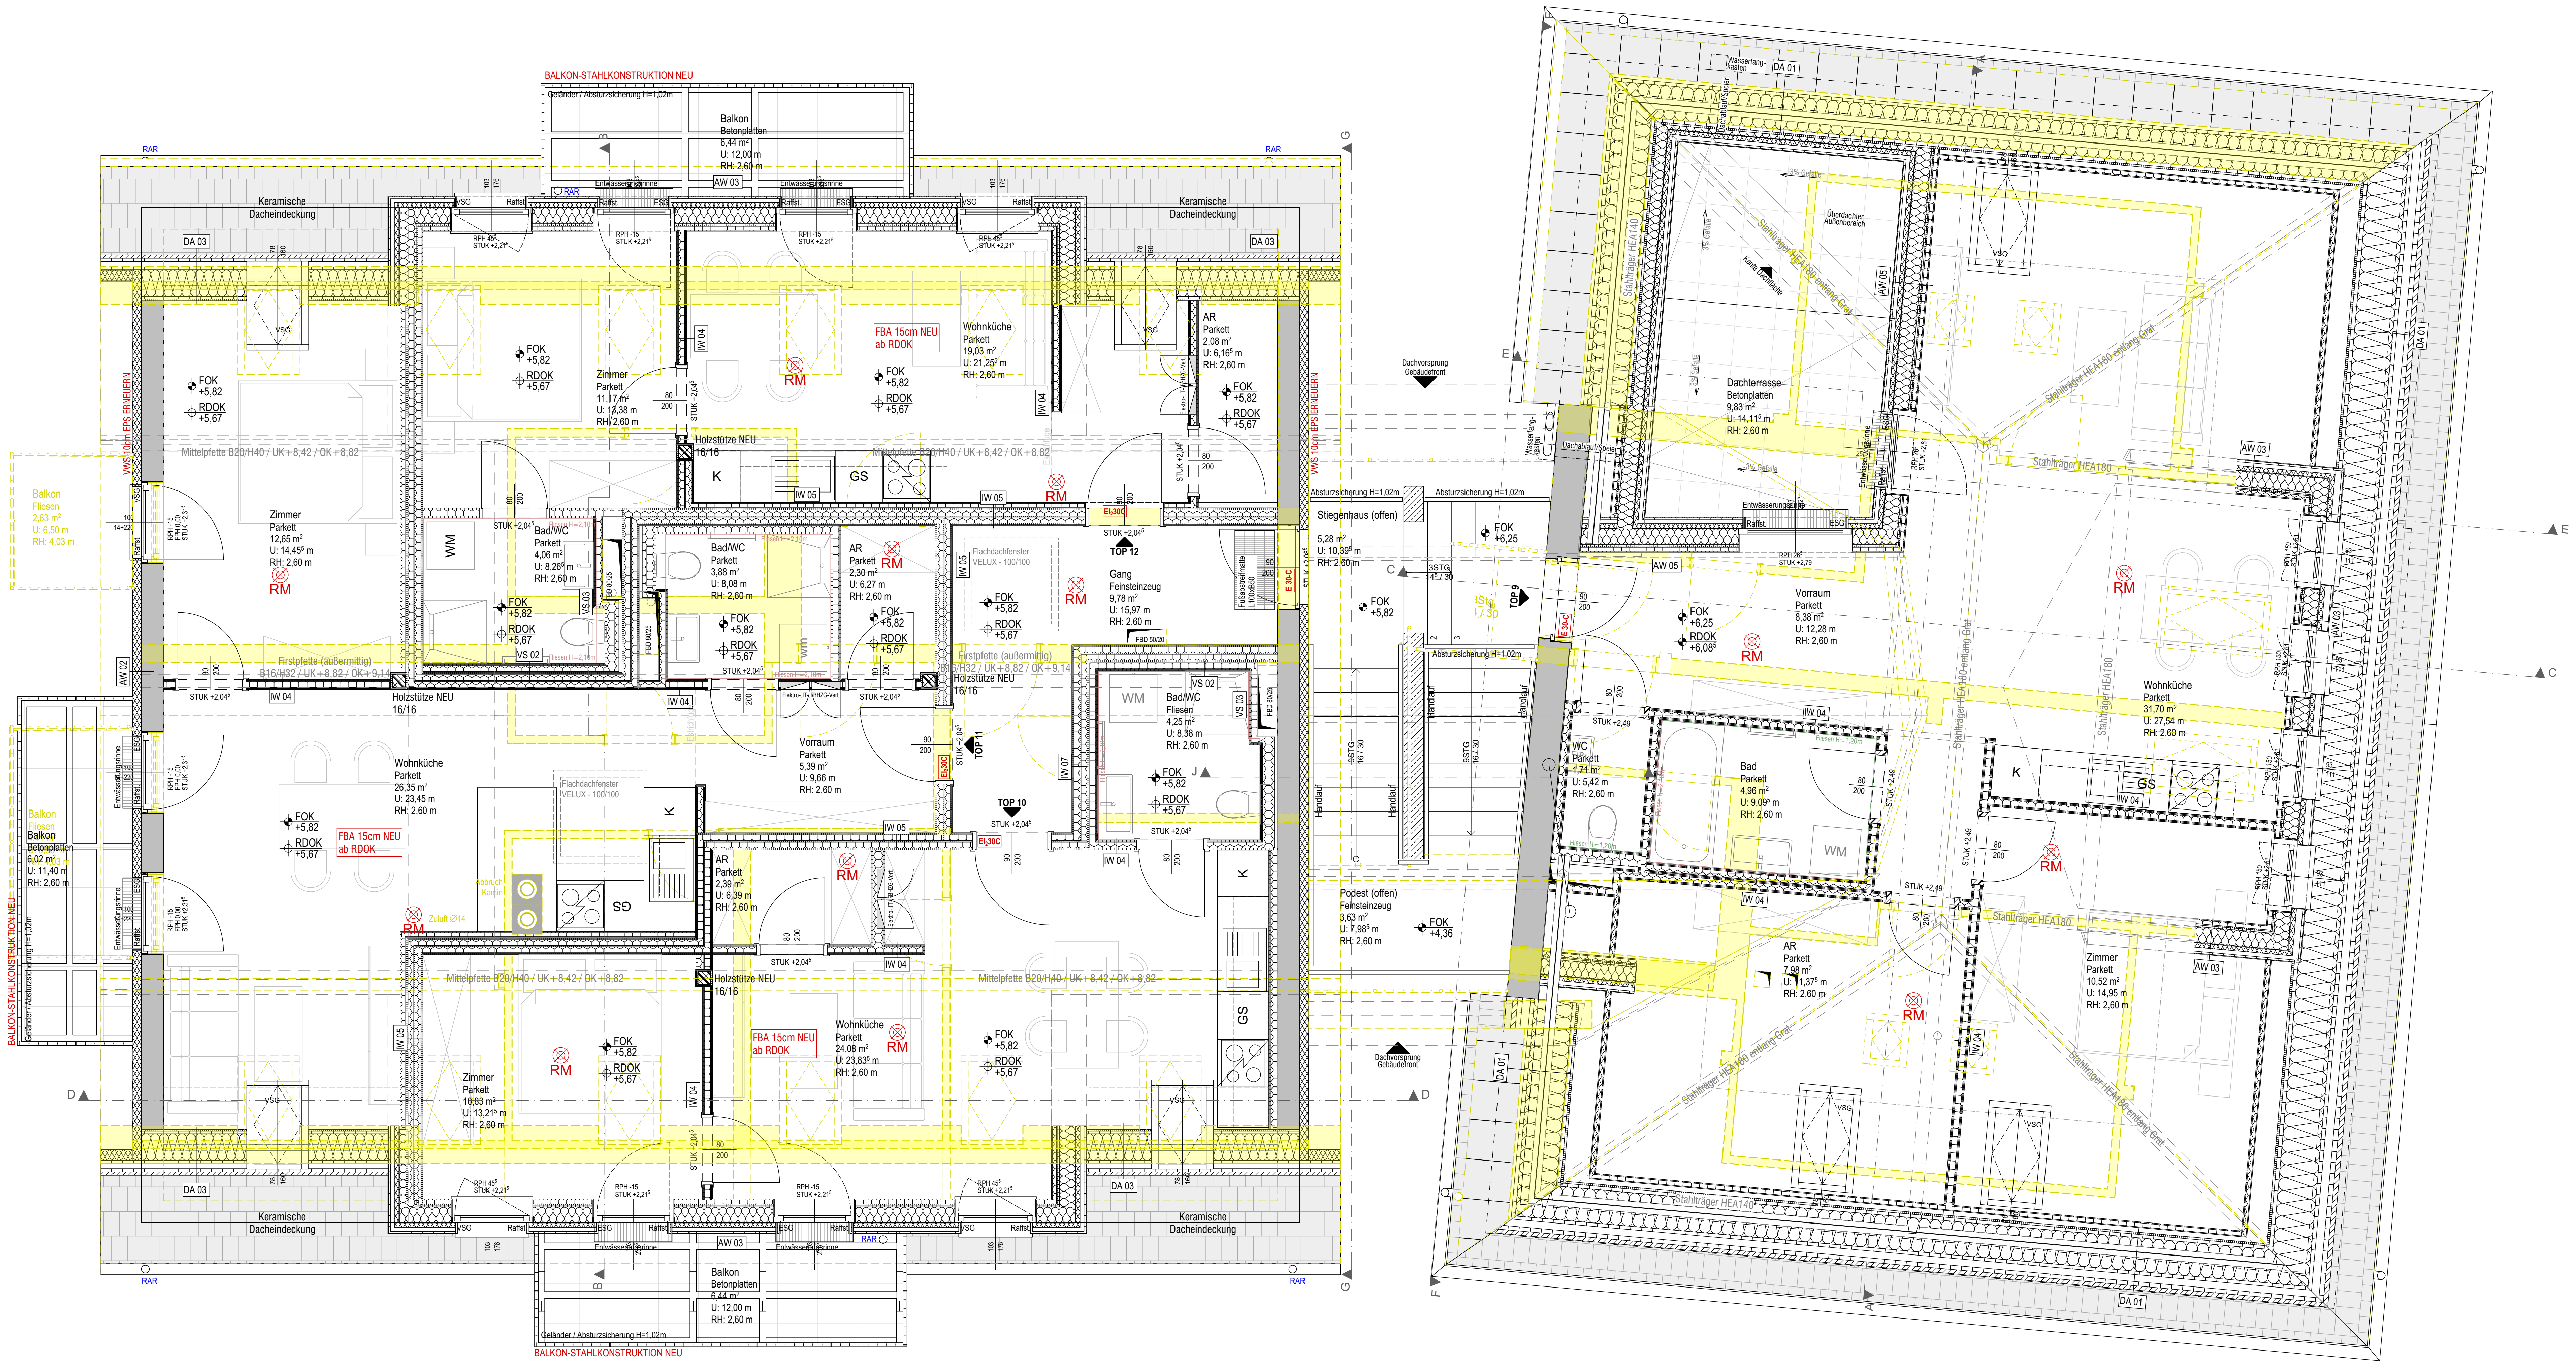

Top 10	
Aufenthaltsfläch	
SUMME	

Top 11	
Aufenthaltsfläche	35,
SUMME	**35,**

Top 12	
Aufenthaltsfläche	42,75 m²
SUMME	**42,75 m²**

LEGENDE

- ⊠ Wanddurchbruch
- ⬚ Deckendurchbruch
- ◿ Bodenschlitz
- ◢ Bodendurchbruch
- ▼ OK Fertigbau
- ▲ UK Fertigbau
- ▽ OK Rohbau
- △ UK Rohbau
- ± 0,00 Höhenangabe einer waagrechten Fläche
- ⊕ ±0,00 Höhenangabe eines Punktes in einem Bauwerk - Fertigmaß
- ⊕ ±0,00 Höhenangabe eines Punktes in einem Bauwerk - Rohbaumaß

BGF	Bruttogesamtfläche
HNF / NNF	Haupt- Nebennutzfläche

- ▨ Mauerwerk (wärmedämmend)
- ▨ Mauerwerk (nicht wärmedämmend)
- ▨ unbewehrter Beton
- ▨ bewehrter Beton
- ▦ Betonfertigteil
- ▤ Stein
- ▨ Stahl (allgemein)
- ▨ Holz (allgemein)
- ▨ Holzwerkstoffe
- ▩ Dämmstoff (hart)
- ▩ Dämmstoff (weich)
- ▩ Kunststoff (allgemein)
- ▚ Dichtstoff (allgemein)
- ▥ Gips (Gipskartonplatte)
- ▥ Gipskartonplatte Brandschutz
- ☐ Erdmaterial (allgemein)
- ■ Bestand
- 🟨 Abbruch
- 🟥 Neubau

- — Medien
- — Fernwärme
- — Gas
- — Strom
- — Heizung
- — Regenwasser
- — Schmutzwasser
- — Wasser
- — Blech
- - - Abdichtung
- - - Folie
- - - Dampfsperre, -bremse

Höhenbezugs- und Maßangaben

DOK	Deckenoberkante
DOS	Deckenoberseite
DUK	Deckenunterkante
DUS	Deckenunterseite
DUF	Deckenunterkante (fertige Untersicht)
FBOK	Fußbodenoberkante
OFF	Oberfläche des fertigen Fußbodens
FDOK	Fundamentoberkante
FDOS	Fundamentoberseite
FDUK	Fundamentunterkante
FDUS	Fundamentunterseite
RH	lichte Raumhöhe
GH	Geschoßhöhe
OK	Oberkante
OS	Oberseite
UK	Unterkante
US	Unterseite
STUK	Sturzunterkante (Rohbaumaß)
STH	Sturzhöhe gemessen von STUK bis DUK (Rohbaumaß)
RPH	Rohbauparapethöhe
FPH	fertige Parapethöhe (FBOK bis OK Fensterbank Innen)

Rauch-, Abgas- und Luftfänge, Schächte

L	Lüftungsschacht
PT	Putztürchen
PS	Putzstück
KT	Kehrtürchen
ABL	Abluft
ZUL	Zuluft
DBA	Druckbelüftungsanlage
DES	Druckentlastungsschacht
BÖ	Belüftungsöffnung
ÜÖ	Überströmöffnung
AÖ	Abströmöffnung mit Überdruckentlastungsorgan
BSK	Brandsschutzklappe
FBHV	Fussbodenheizungsverteiler
E-Verteiler	Elektroverteiler

Öffnungen und deren Abschlüsse

WD	Wanddurchbruch
DD	Deckendurchbruch
FBD	Fußbodendurchbruch
FDD	Fundamentdurchbruch
WS	Wandschlitz
WA	Wandaussparung
DA	Deckenaussparung
FBA	Fußbodenaussparung
RBL	Rohbaulichte
AL	Architekturlichte
STL	Stocklichte
GL	Glaslichte
STAM	Stockaußenmaß
DL	Durchgangslichte
GGT	Ganzglastüre
MGT	Metallgittertür
HT	Hebetüre
HST	Hebeschiebetüre
T	Türe
AT	Allgemeintüre
ET	Eingangstüre
WET	Wohnungseingangstür
IT	Innentür
DF	Drehflügel
DKF	Drehkippflügel
SF	Schiebe-Fenster
SWF	Schwingflügel
WF	Wendeflügel
K	Kippfenster
OL	Oberlichte
DF	Dachfächenfenster
PFR	Pfostenriegelkonstruktion
FE	Fenster
FT	Fenstertüre
R	Rechtsöffnend
L	Linksöffnend
FIX	Fixverglasung
VSG	Verbund-Sicherheitsglas
ESG	Einscheiben-Sicherheitsglas

- Drehflügel
- Drehkippflügel
- Kippflügel
- Fenstertüre

EI2 30-C-, EI2 60-C-und EI2 90-C
Feuerschutztüren mit Angabe der Feuerwiderstandsklasse
(gemäß ÖNORM B 3850 und ÖNORM B 3807)

GT	gasdichte Türe
DT	Drucktüre
S 200	Rauchabschluss
S 200	Rauchabschluss
C	Selbstschließend
FLS	Freilaufschließer
LVfTÖ	Lehrverrohrung für Türöffner
elTÖ	elektrischer Türöffner

AUSFÜHRUNG POLIERPL. ABBRUCH

Bauvorhaben

WNEU30

2540 Bad Vöslau, Wiener Neustädter Straße 30

XXX

Katastralgemeinde 04035 Vöslau
EZ: 719
GstNr.: 748

Diese Zeichnung bzw. Ausarbeitung sowie deren Daten auf Datenträgern sind geistiges Eigentum des Erstellers Arch. Artmüller Georg. Jede Benützung, Veröffentlichung,Vervielfältigung jeglicher Art oder Weitergabe an Dritte bedarf der schriftlichen Zustimmung durch Architekt Artmüller.

Durch die Übernahme dieses Planes akzeptiert die ausführende Firma bzw. Person die darauf dargestellten Anordnungen. Geschriebene Planmaße auf dieser Zeichnunghaben Vorrang gegenüber gezeichneten Dimensionen. Der Auftragnehmer verpflichtet sich **vor** Arbeitsbeginn alle Maße und Bedingungen im Zusammenhang mit seinerArbeit auf der Baustelle verantwortlich zu überprüfen.

Abweichungen gegenüber dargestellten oder schriftlich vereinbarten Anordnungen müssen Architekt Artmüller und der Bauleitung unverzüglich schriftlich mitgeteiltwerden. Vor Arbeitsbeginn sind dem Architekten gültige Werkzeichnungen zur Genehmigung vorzulegen.

NATURMASSE SIND ZU NEHMEN, KOTEN ZU PRÜFEN

Index	Datum	Bearbeiter	Änderung

Index	Änderung	Datum

Grundeigentümer

Bauwerber / Auftraggeber

ARTMÜLLER ARCHITEKTEN
ZIVILTECHNIKER GMBH
Stolberggasse 34|26 A-1050 Wien
t [+43] 01 . 581 40 83 f [+43] 01. 581 40 83 99 office@artmueller.eu

Planinhalt

Dachgeschoß

Maßstab	Gez	Datum	Plannr.	Index
1:50	ML	02-11-2026	WNEU30_51_03	

Erstellt, am 11.11.2026

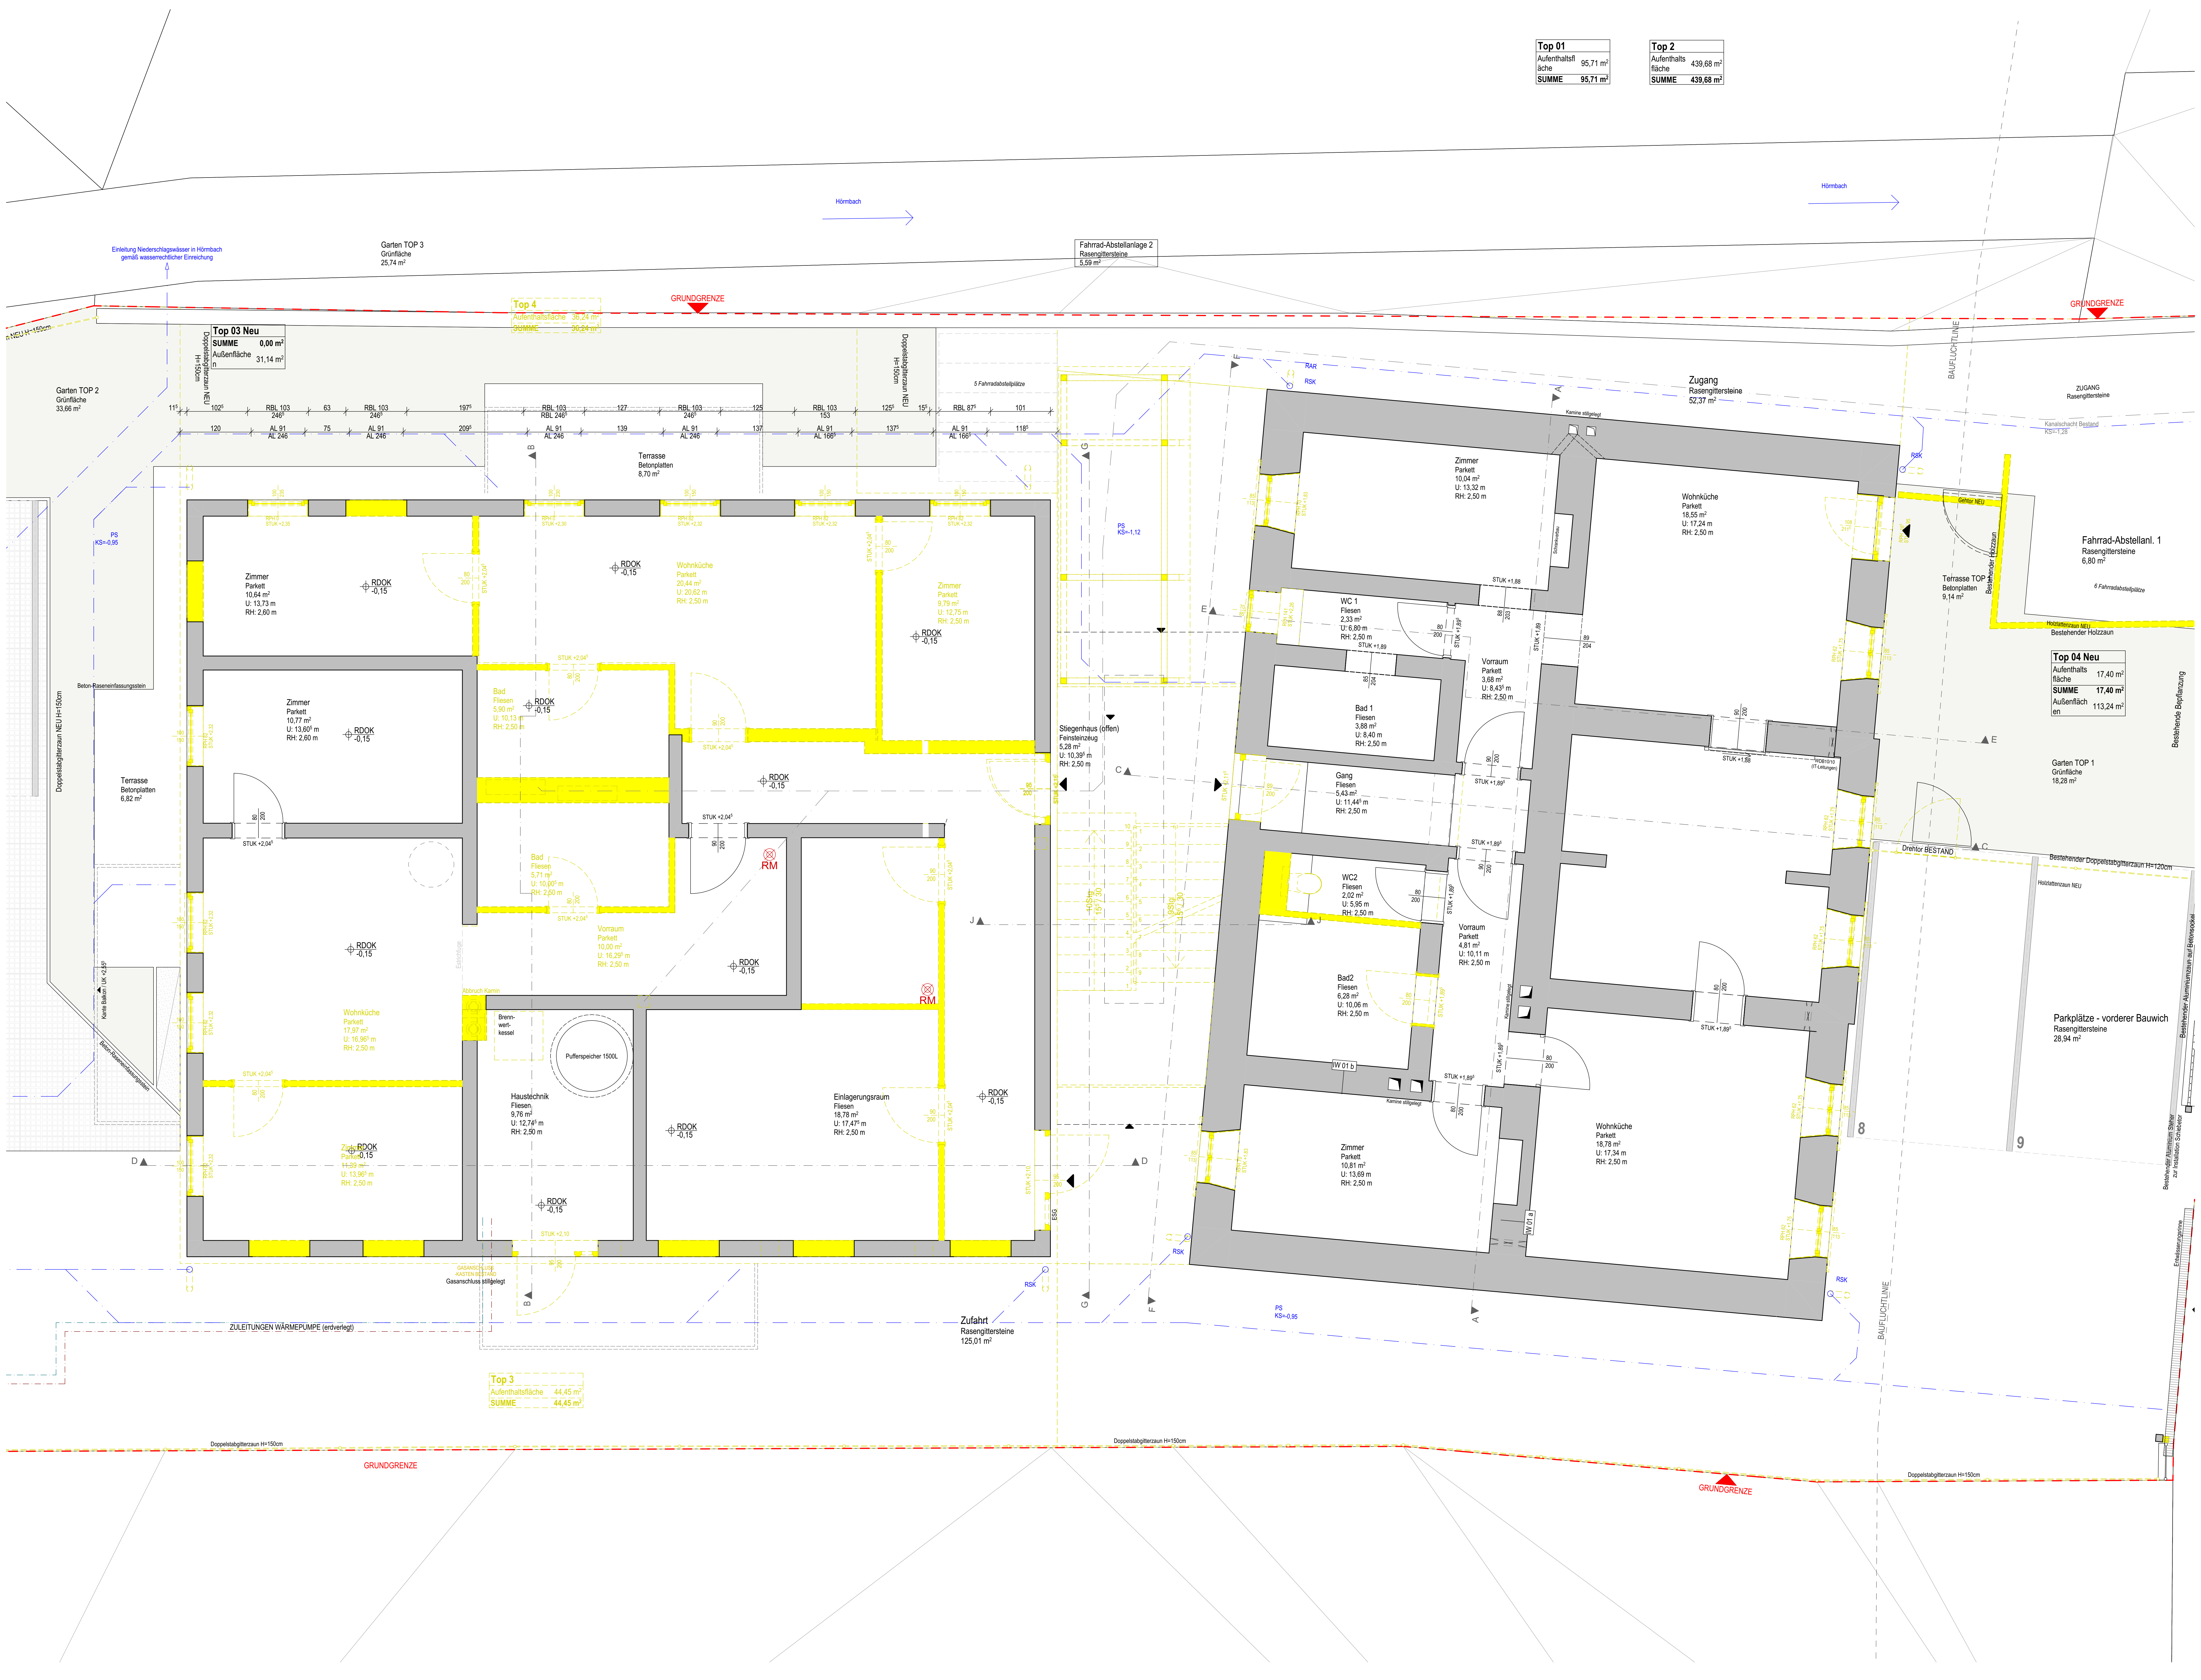

LEGENDE

☒	Wanddurchbruch
⬚	Deckendurchbruch
◺	Bodenschlitz
◢	Bodendurchbruch
▼	OK Fertigbau
▲	UK Fertigbau
▽	OK Rohbau
△	UK Rohbau
± 0,00	Höhenangabe einer waagrechten Fläche
±0,00	Höhenangabe eines Punktes in einem Bauwerk - Fertigmaß
±0,00	Höhenangabe eines Punktes in einem Bauwerk - Rohbaumaß
BGF	Bruttogesamtfläche
HNF / NNF	Haupt- Nebennutzfläche

▨	Mauerwerk (wärmedämmend)
▨	Mauerwerk (nicht wärmedämmend)
▨	unbewehrter Beton
▨	bewehrter Beton
▦	Betonfertigteil
▤	Stein
▨	Stahl (allgemein)
▨	Holz (allgemein)
▨	Holzwerkstoffe
▩	Dämmstoff (hart)
▩	Dämmstoff (weich)
▩	Kunststoff (allgemein)
▚	Dichtstoff (allgemein)
▥	Gips (Gipskartonplatte)
▥	Gipskartonplatte Brandschutz
☐	Erdmaterial (allgemein)
■	Bestand
🟨	Abbruch
🟥	Neubau

—	Medien
—	Fernwärme
—	Gas
—	Strom
—	Heizung
—	Regenwasser
—	Schmutzwasser
—	Wasser
—	Blech
- - -	Abdichtung
- - -	Folie
- - -	Dampfsperre, -bremse

Höhenbezugs- und Maßangaben

DOK	Deckenoberkante
DOS	Deckenoberseite
DUK	Deckenunterkante
DUS	Deckenunterseite
DUF	Deckenunterkante (fertige Untersicht)
FBOK	Fußbodenoberkante
OFF	Oberfläche des fertigen Fußbodens
FDOK	Fundamentoberkante
FDOS	Fundamentoberseite
FDUK	Fundamentunterkante
FDUS	Fundamentunterseite
RH	lichte Raumhöhe
GH	Geschoßhöhe
OK	Oberkante
OS	Oberseite
UK	Unterkante
US	Unterseite
STUK	Sturzunterkante (Rohbaumaß)
STH	Sturzhöhe gemessen von STUK bis DUK (Rohbaumaß)
RPH	Rohbauparapethöhe
FPH	fertige Parapethöhe (FBOK bis OK Fensterbank Innen)

Rauch-, Abgas- und Luftfänge, Schächte

L	Lüftungsschacht
PT	Putztürchen
PS	Putzstück
KT	Kehrtürchen
ABL	Abluft
ZUL	Zuluft
DBA	Druckbelüftungsanlage
DES	Druckentlastungsschacht
BÖ	Belüftungsöffnung
ÜÖ	Überströmöffnung
AÖ	Abströmöffnung mit Überdruckentlastungsorgan
BSK	Brandsschutzklappe
FBHV	Fussbodenheizungsverteiler
E-Verteiler	Elektroverteiler

Öffnungen und deren Abschlüsse

WD	Wanddurchbruch
DD	Deckendurchbruch
FBD	Fußbodendurchbruch
FDD	Fundamentdurchbruch
WS	Wandschlitz
WA	Wandaussparung
DA	Deckenaussparung
FBA	Fußbodenaussparung
RBL	Rohbaulichte
AL	Architekturlichte
STL	Stocklichte
GL	Glaslichte
STAM	Stockaußenmaß
DL	Durchgangslichte
GGT	Ganzglastüre
MGT	Metallgittertür
HT	Hebetüre
HST	Hebeschiebetüre
T	Türe
AT	Allgemeintüre
ET	Eingangstüre
WET	Wohnungseingangstür
IT	Innentür
DF	Drehflügel
DKF	Drehkippflügel
SF	Schiebe-Fenster
SWF	Schwingflügel
WF	Wendeflügel
K	Kippfenster
OL	Oberlichte
DF	Dachfächenfenster
PFR	Pfostenriegelkonstruktion
FE	Fenster
FT	Fenstertüre
R	Rechtsöffnend
L	Linksöffnend
FIX	Fixverglasung
VSG	Verbund-Sicherheitsglas
ESG	Einscheiben-Sicherheitsglas

Drehflügel
Drehkippflügel
Kippflügel
Fenstertüre

EI2 30-C-, EI2 60-C-und EI2 90-C
Feuerschutztüren mit Angabe der Feuerwiderstandsklasse
(gemäß ÖNORM B 3850 und ÖNORM B 3807)

GT	gasdichte Türe
DT	Drucktüre
S 200	Rauchabschluss
S 200	Rauchabschluss
C	Selbstschließend
FLS	Freilaufschließer
LVfTÖ	Lehrverrohrung für Türöffner
elTÖ	elektrischer Türöffner

AUSFÜHRUNG POLIERPL. ABBRUCH

Bauvorhaben
WNEU30
2540 Bad Vöslau, Wiener Neustädter Straße 30

XXX

Katastralgemeinde 04035 Vöslau
EZ: 719
GstNr.: 748

Durch die Übernahme dieses Planes akzeptiert die ausführende Firma bzw. Person die darauf dargestellten Anordnungen. Geschriebene Planmaße auf dieser Zeichnunghaben Vorrang gegenüber gezeichneten Dimensionen. Der Auftragnehmer verpflichtet sich **vor** Arbeitsbeginn alle Maße und Bedingungen im Zusammenhang mit seinerArbeit auf der Baustelle verantwortlich zu überprüfen.

Abweichungen gegenüber dargestellten oder schriftlich vereinbarten Anordnungen müssen Architekt Artmüller und der Bauleitung unverzüglich schriftlich mitgeteiltwerden. Vor Arbeitsbeginn sind dem Architekten gültige Werkzeichnungen zur Genehmigung vorzulegen.

NATURMASSE SIND ZU NEHMEN, KOTEN ZU PRÜFEN

Index	Datum	Bearbeiter	Änderung

Index Änderung Datum

Grundeigentümer

Bauwerber / Auftraggeber

ARTMÜLLER ARCHITEKTEN
ZIVILTECHNIKER GMBH
Stolberggasse 34|26 A-1050 Wien
t [+43] 01 . 581 40 83 f [+43] 01. 581 40 83 99 office@artmueller.eu

Planinhalt
EG Abbruch Skizze

Maßstab	Gez	Datum	Plannr.	Index
1:50	ML	02-11-2026	WNEU30_51_04	

Erstellt, am 11.11.2026

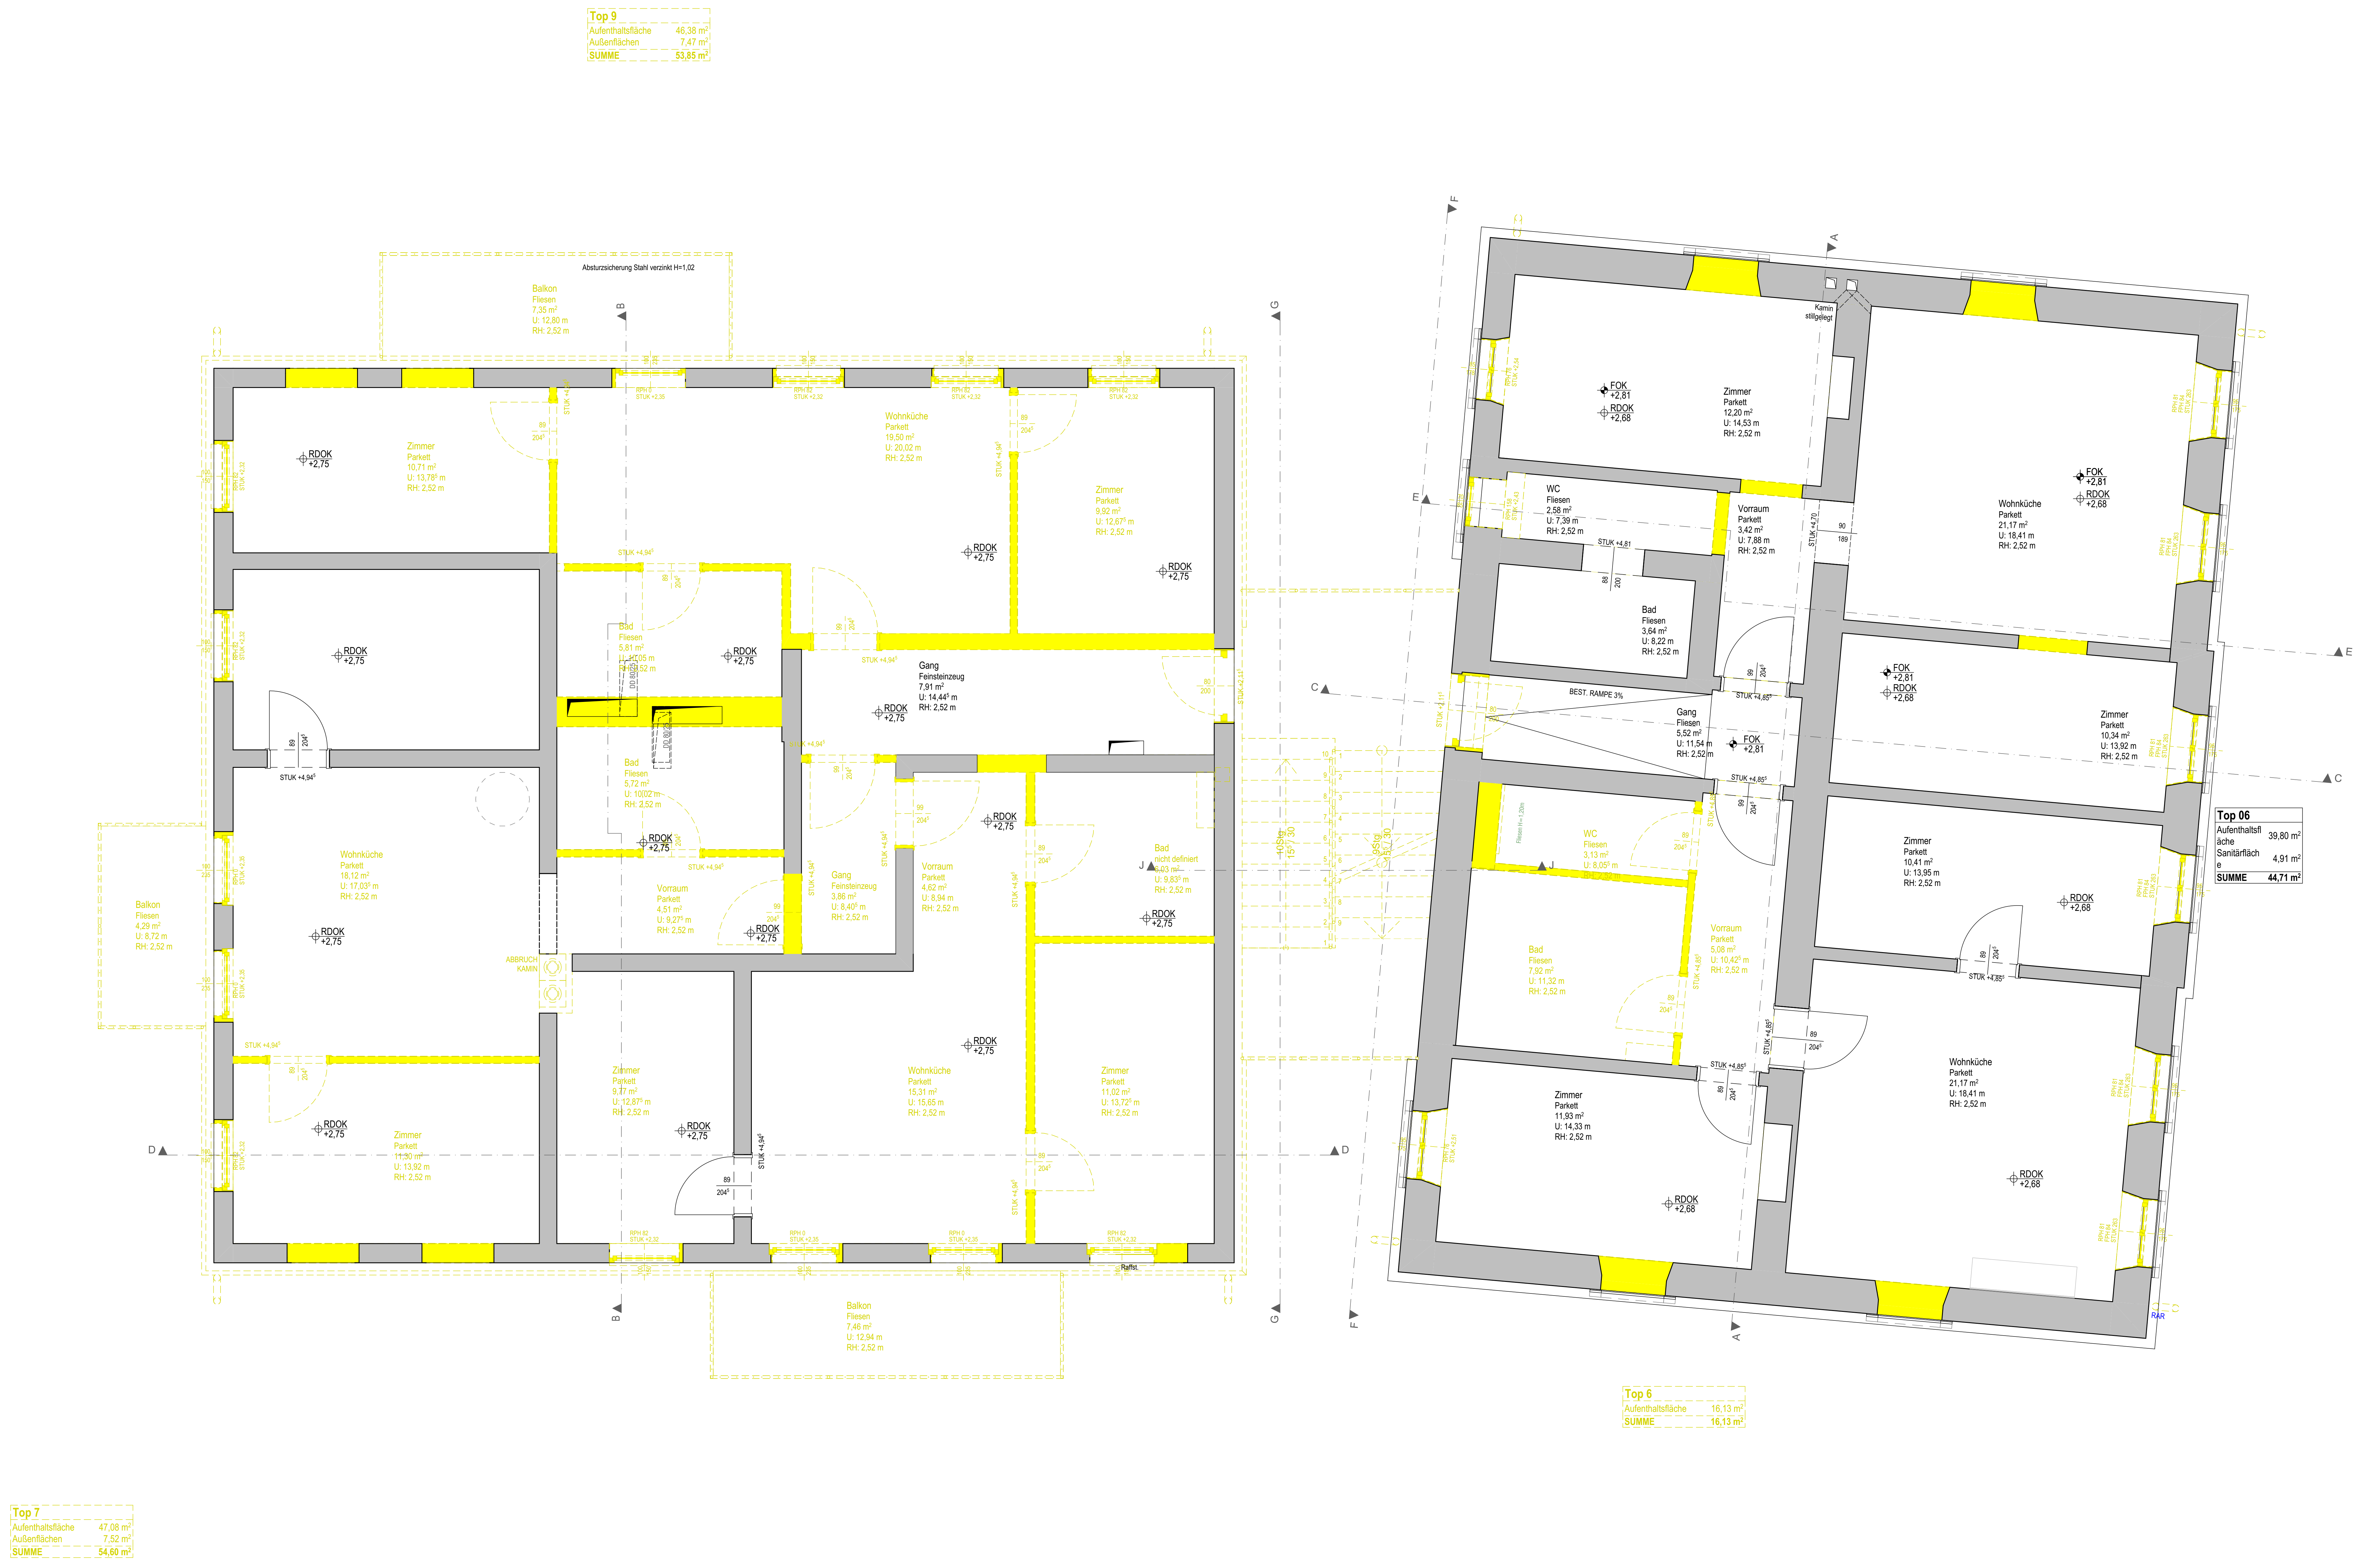

Top 9	
Aufenthaltsfläche	46,38 m²
Außenflächen	7,47 m²
SUMME	53,85 m²

Top 7	
Aufenthaltsfläche	47,08 m²
Außenflächen	7,52 m²
SUMME	54,60 m²

Top 6	
Aufenthaltsfläche	16,13 m²
SUMME	16,13 m²

Top 06	
Aufenthaltsfläche	39,80 m²
Sanitärfläche	4,91 m²
SUMME	44,71 m²

LEGENDE

- ⊠ Wanddurchbruch
- Deckendurchbruch
- Bodenschlitz
- Bodendurchbruch
- ▼ OK Fertigbau
- ▲ UK Fertigbau
- ▽ OK Rohbau
- △ UK Rohbau
- ± 0,00 Höhenangabe einer waagrechten Fläche
- ±0,00 Höhenangabe eines Punktes in einem Bauwerk - Fertigmaß
- ±0,00 Höhenangabe eines Punktes in einem Bauwerk - Rohbaumaß

BGF	Bruttogesamtfläche
HNF / NNF	Haupt- Nebennutzfläche

- ▨ Mauerwerk (wärmedämmend)
- ▨ Mauerwerk (nicht wärmedämmend)
- ▨ unbewehrter Beton
- ▨ bewehrter Beton
- ▦ Betonfertigteil
- ▤ Stein
- ▨ Stahl (allgemein)
- ▨ Holz (allgemein)
- ▨ Holzwerkstoffe
- ▩ Dämmstoff (hart)
- ▩ Dämmstoff (weich)
- ▩ Kunststoff (allgemein)
- ▚ Dichtstoff (allgemein)
- ▥ Gips (Gipskartonplatte)
- ▥ Gipskartonplatte Brandschutz
- ☐ Erdmaterial (allgemein)
- ⬜ Bestand
- 🟨 Abbruch
- 🟥 Neubau

- Medien
- Fernwärme
- Gas
- Strom
- Heizung
- Regenwasser
- Schmutzwasser
- Wasser
- Blech
- Abdichtung
- Folie
- Dampfsperre, -bremse

Höhenbezugs- und Maßangaben

DOK	Deckenoberkante
DOS	Deckenoberseite
DUK	Deckenunterkante
DUS	Deckenunterseite
DUF	Deckenunterkante (fertige Untersicht)
FBOK	Fußbodenoberkante
OFF	Oberfläche des fertigen Fußbodens
FDOK	Fundamentoberkante
FDOS	Fundamentoberseite
FDUK	Fundamentunterkante
FDUS	Fundamentunterseite
RH	lichte Raumhöhe
GH	Geschoßhöhe
OK	Oberkante
OS	Oberseite
UK	Unterkante
US	Unterseite
STUK	Sturzunterkante (Rohbaumaß)
STH	Sturzhöhe gemessen von STUK bis DUK (Rohbaumaß)
RPH	Rohbauparapethöhe
FPH	fertige Parapethöhe (FBOK bis OK Fensterbank Innen)

Rauch-, Abgas- und Luftfänge, Schächte

L	Lüftungsschacht
PT	Putztürchen
PS	Putzstück
KT	Kehrtürchen
ABL	Abluft
ZUL	Zuluft
DBA	Druckbelüftungsanlage
DES	Druckentlastungsschacht
BÖ	Belüftungsöffnung
ÜÖ	Überströmöffnung
AÖ	Abströmöffnung mit Überdruckentlastungsorgan
BSK	Brandsschutzklappe
FBHV	Fussbodenheizungsverteiler
E-Verteiler	Elektroverteiler

Öffnungen und deren Abschlüsse

WD	Wanddurchbruch
DD	Deckendurchbruch
FBD	Fußbodendurchbruch
FDD	Fundamentdurchbruch
WS	Wandschlitz
WA	Wandaussparung
DA	Deckenaussparung
FBA	Fußbodenaussparung
RBL	Rohbaulichte
AL	Architekturlichte
STL	Stocklichte
GL	Glaslichte
STAM	Stockaußenmaß
DL	Durchgangslichte
GGT	Ganzglastüre
MGT	Metallgittertür
HT	Hebetüre
HST	Hebeschiebetüre
T	Türe
AT	Allgemeintüre
ET	Eingangstüre
WET	Wohnungseingangstür
IT	Innentür
DF	Drehflügel
DKF	Drehkippflügel
SF	Schiebe-Fenster
SWF	Schwingflügel
WF	Wendeflügel
K	Kippfenster
OL	Oberlichte
DF	Dachfächenfenster
PFR	Pfostenriegelkonstruktion
FE	Fenster
FT	Fenstertüre
R	Rechtsöffnend
L	Linksöffnend
FIX	Fixverglasung
VSG	Verbund-Sicherheitsglas
ESG	Einscheiben-Sicherheitsglas

- Drehflügel
- Drehkippflügel
- Kippflügel
- Fenstertüre

EI2 30-C-, EI2 60-C-und EI2 90-C
Feuerschutztüren mit Angabe der Feuerwiderstandsklasse
(gemäß ÖNORM B 3850 und ÖNORM B 3807)

GT	gasdichte Türe
DT	Drucktüre
S 200	Rauchabschluss
S 200	Rauchabschluss
C	Selbstschließend
FLS	Freilaufschließer
LVfTÖ	Lehrverrohrung für Türöffner
elTÖ	elektrischer Türöffner

AUSFÜHRUNG POLIERPL. ABBRUCH

Bauvorhaben
WNEU30
2540 Bad Vöslau, Wiener Neustädter Straße 30

XXX

Katastralgemeinde 04035 Vöslau
EZ: 719
GstNr.: 748

Durch die Übernahme dieses Planes akzeptiert die ausführende Firma bzw. Person die darauf dargestellten Anordnungen. Geschriebene Planmaße auf dieser Zeichnunghaben Vorrang gegenüber gezeichneten Dimensionen. Der Auftragnehmer verpflichtet sich **vor** Arbeitsbeginn alle Maße und Bedingungen im Zusammenhang mit seinerArbeit auf der Baustelle verantwortlich zu überprüfen.

Abweichungen gegenüber dargestellten oder schriftlich vereinbarten Anordnungen müssen Architekt Artmüller und der Bauleitung unverzüglich schriftlich mitgeteiltwerden. Vor Arbeitsbeginn sind dem Architekten gültige Werkzeichnungen zur Genehmigung vorzulegen.

NATURMASSE SIND ZU NEHMEN, KOTEN ZU PRÜFEN

Index	Datum	Bearbeiter	Änderung

Index	Änderung	Datum

Grundeigentümer

Bauwerber / Auftraggeber

ARTMÜLLER ARCHITEKTEN
ZIVILTECHNIKER GMBH
Stolberggasse 34|26 A-1050 Wien
t [+43] 01 . 581 40 83 f [+43] 01. 581 40 83 99 office@artmueller.eu

Planinhalt
OG Abbruch Skizze

Maßstab	Gez	Datum	Plannr.	Index
1:50	ML	02-11-2026	WNEU30_51_05	

Erstellt, am 11.11.2026

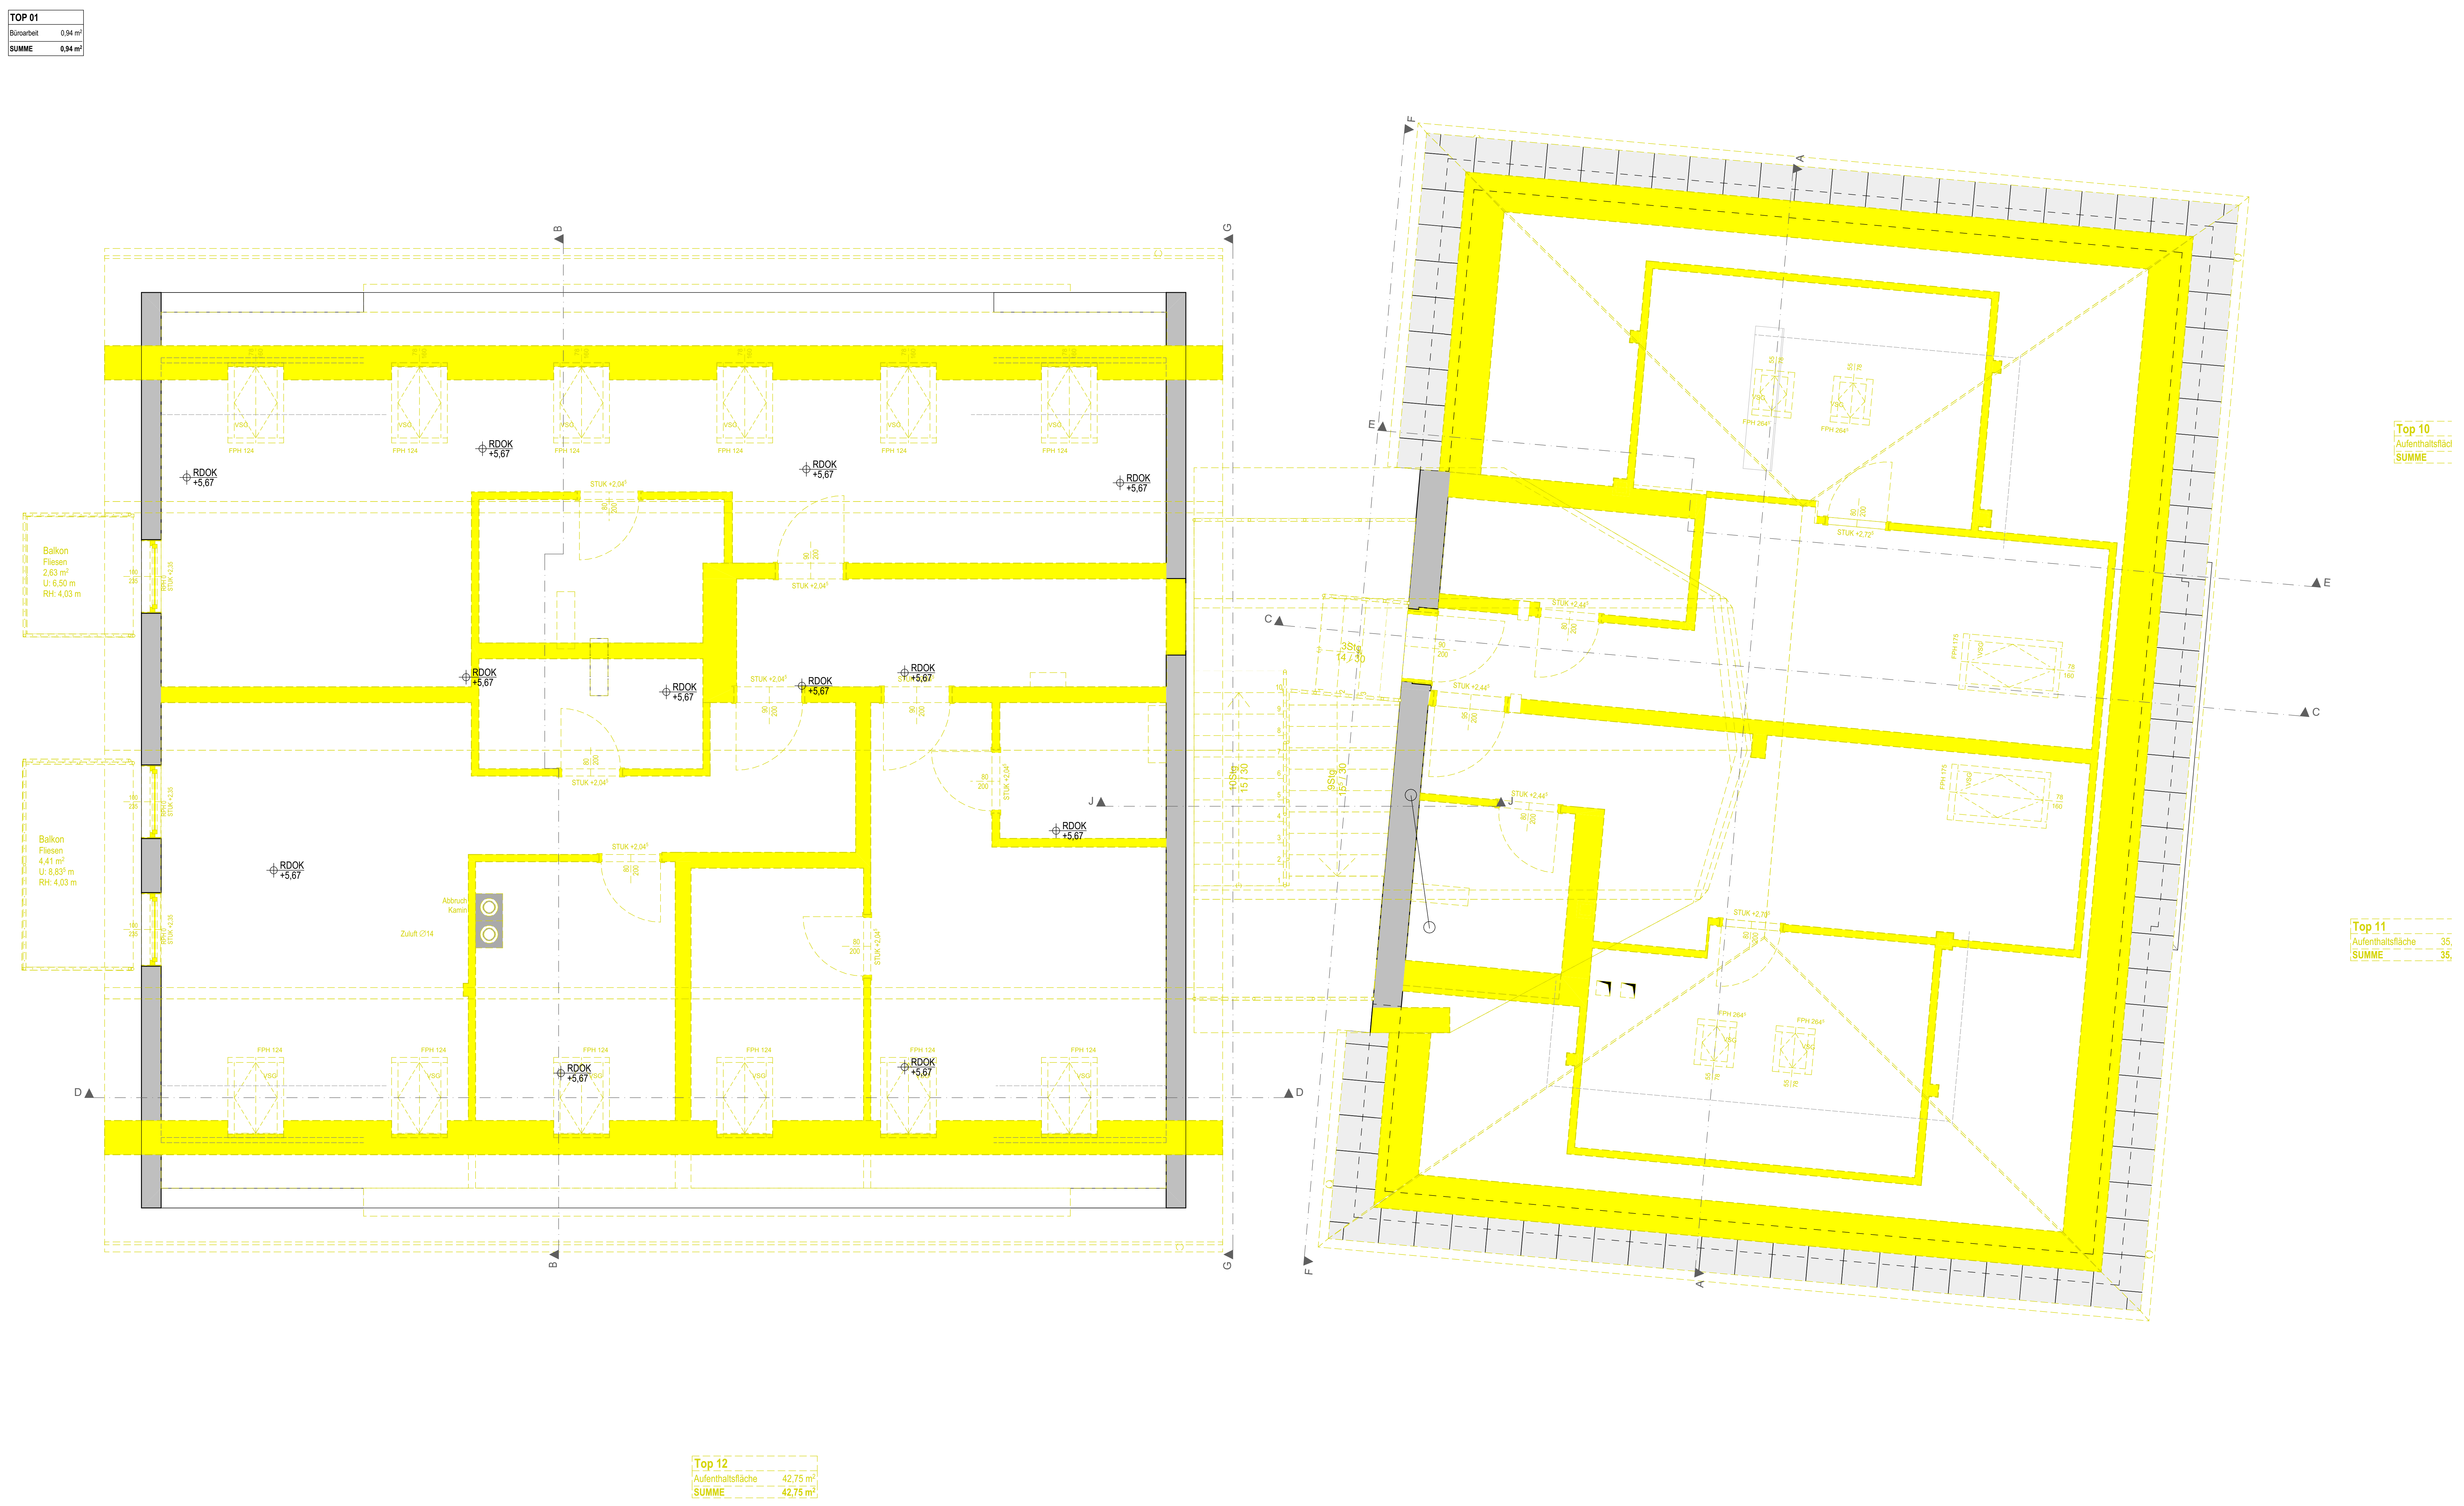

LEGENDE

⊠	Wanddurchbruch
⬚	Deckendurchbruch
◸	Bodenschlitz
◢	Bodendurchbruch
▼	OK Fertigbau
▲	UK Fertigbau
▽	OK Rohbau
△	UK Rohbau
± 0,00	Höhenangabe einer waagrechten Fläche
⊕ ±0,00	Höhenangabe eines Punktes in einem Bauwerk - Fertigmaß
⌖ ±0,00	Höhenangabe eines Punktes in einem Bauwerk - Rohbaumaß

BGF	Bruttogesamtfläche
HNF / NNF	Haupt- Nebennutzfläche

▨	Mauerwerk (wärmedämmend)
▨	Mauerwerk (nicht wärmedämmend)
▨	unbewehrter Beton
▨	bewehrter Beton
▦	Betonfertigteil
▤	Stein
▨	Stahl (allgemein)
▨	Holz (allgemein)
▨	Holzwerkstoffe
▩	Dämmstoff (hart)
▩	Dämmstoff (weich)
▩	Kunststoff (allgemein)
▚	Dichtstoff (allgemein)
▥	Gips (Gipskartonplatte)
▥	Gipskartonplatte Brandschutz
☐	Erdmaterial (allgemein)
⬛	Bestand
🟨	Abbruch
🟥	Neubau

—	Medien
—	Fernwärme
—	Gas
—	Strom
—	Heizung
—	Regenwasser
—	Schmutzwasser
—	Wasser
—	Blech
- - -	Abdichtung
- - -	Folie
– – –	Dampfsperre, -bremse

Höhenbezugs- und Maßangaben

DOK	Deckenoberkante
DOS	Deckenoberseite
DUK	Deckenunterkante
DUS	Deckenunterseite
DUF	Deckenunterkante (fertige Untersicht)
FBOK	Fußbodenoberkante
OFF	Oberfläche des fertigen Fußbodens
FDOK	Fundamentoberkante
FDOS	Fundamentoberseite
FDUK	Fundamentunterkante
FDUS	Fundamentunterseite
RH	lichte Raumhöhe
GH	Geschoßhöhe
OK	Oberkante
OS	Oberseite
UK	Unterkante
US	Unterseite
STUK	Sturzunterkante (Rohbaumaß)
STH	Sturzhöhe gemessen von STUK bis DUK (Rohbaumaß)
RPH	Rohbauparapethöhe
FPH	fertige Parapethöhe (FBOK bis OK Fensterbank Innen)

Rauch-, Abgas- und Luftfänge, Schächte

L	Lüftungsschacht
PT	Putztürchen
PS	Putzstück
KT	Kehrtürchen
ABL	Abluft
ZUL	Zuluft
DBA	Druckbelüftungsanlage
DES	Druckentlastungsschacht
BÖ	Belüftungsöffnung
ÜÖ	Überströmöffnung
AÖ	Abströmöffnung mit Überdruckentlastungsorgan
BSK	Brandsschutzklappe
FBHV	Fussbodenheizungsverteiler
E-Verteiler	Elektroverteiler

Öffnungen und deren Abschlüsse

WD	Wanddurchbruch
DD	Deckendurchbruch
FBD	Fußbodendurchbruch
FDD	Fundamentdurchbruch
WS	Wandschlitz
WA	Wandaussparung
DA	Deckenaussparung
FBA	Fußbodenaussparung
RBL	Rohbaulichte
AL	Architekturlichte
STL	Stocklichte
GL	Glaslichte
STAM	Stockaußenmaß
DL	Durchgangslichte
GGT	Ganzglastüre
MGT	Metallgittertür
HT	Hebetüre
HST	Hebeschiebetüre
T	Türe
AT	Allgemeintüre
ET	Eingangstüre
WET	Wohnungseingangstür
IT	Innentür
DF	Drehflügel
DKF	Drehkippflügel
SF	Schiebe-Fenster
SWF	Schwingflügel
WF	Wendeflügel
K	Kippfenster
OL	Oberlichte
DF	Dachfächenfenster
PFR	Pfostenriegelkonstruktion
FE	Fenster
FT	Fenstertüre
R	Rechtsöffnend
L	Linksöffnend
FIX	Fixverglasung
VSG	Verbund-Sicherheitsglas
ESG	Einscheiben-Sicherheitsglas

Drehflügel
Drehkippflügel
Kippflügel
Fenstertüre

EI2 30-C-, EI2 60-C-und EI2 90-C
Feuerschutztüren mit Angabe der Feuerwiderstandsklasse
(gemäß ÖNORM B 3850 und ÖNORM B 3807)

GT	gasdichte Türe
DT	Drucktüre
S 200	Rauchabschluss
S 200	Rauchabschluss
C	Selbstschließend
FLS	Freilaufschließer
LVfTÖ	Lehrverrohrung für Türöffner
elTÖ	elektrischer Türöffner

AUSFÜHRUNG POLIERPL. ABBRUCH

Bauvorhaben
WNEU30
2540 Bad Vöslau, Wiener Neustädter Straße 30

XXX

Katastralgemeinde 04035 Vöslau
EZ: 719
GstNr.: 748

Diese Zeichnung bzw. Ausarbeitung sowie deren Daten auf Datenträgern sind geistiges Eigentum des Erstellers Arch. Artmüller Georg. Jede Benützung, Veröffentlichung,Vervielfältigung jeglicher Art oder Weitergabe an Dritte bedarf der schriftlichen Zustimmung durch Architekt Artmüller.

Durch die Übernahme dieses Planes akzeptiert die ausführende Firma bzw. Person die darauf dargestellten Anordnungen. Geschriebene Planmaße auf dieser Zeichnunghaben Vorrang gegenüber gezeichneten Dimensionen. Der Auftragnehmer verpflichtet sich **vor** Arbeitsbeginn alle Maße und Bedingungen im Zusammenhang mit seinerArbeit auf der Baustelle verantwortlich zu überprüfen.

Abweichungen gegenüber dargestellten oder schriftlich vereinbarten Anordnungen müssen Architekt Artmüller und der Bauleitung unverzüglich schriftlich mitgeteiltwerden. Vor Arbeitsbeginn sind dem Architekten gültige Werkzeichnungen zur Genehmigung vorzulegen.

NATURMASSE SIND ZU NEHMEN, KOTEN ZU PRÜFEN

Index	Datum	Bearbeiter	Änderung

Index	Änderung	Datum

Grundeigentümer

Bauwerber / Auftraggeber

ARTMÜLLER ARCHITEKTEN
ZIVILTECHNIKER GMBH
Stolberggasse 34|26 A-1050 Wien
t [+43] 01 . 581 40 83 f [+43] 01. 581 40 83 99 office@artmueller.eu

Planinhalt
DG Abbruch Skizze

Maßstab	Gez	Datum	Plannr.	Index
1:50	ML	02-11-2026	WNEU30_51_06	

Erstellt, am 11.11.2026